3 этаж

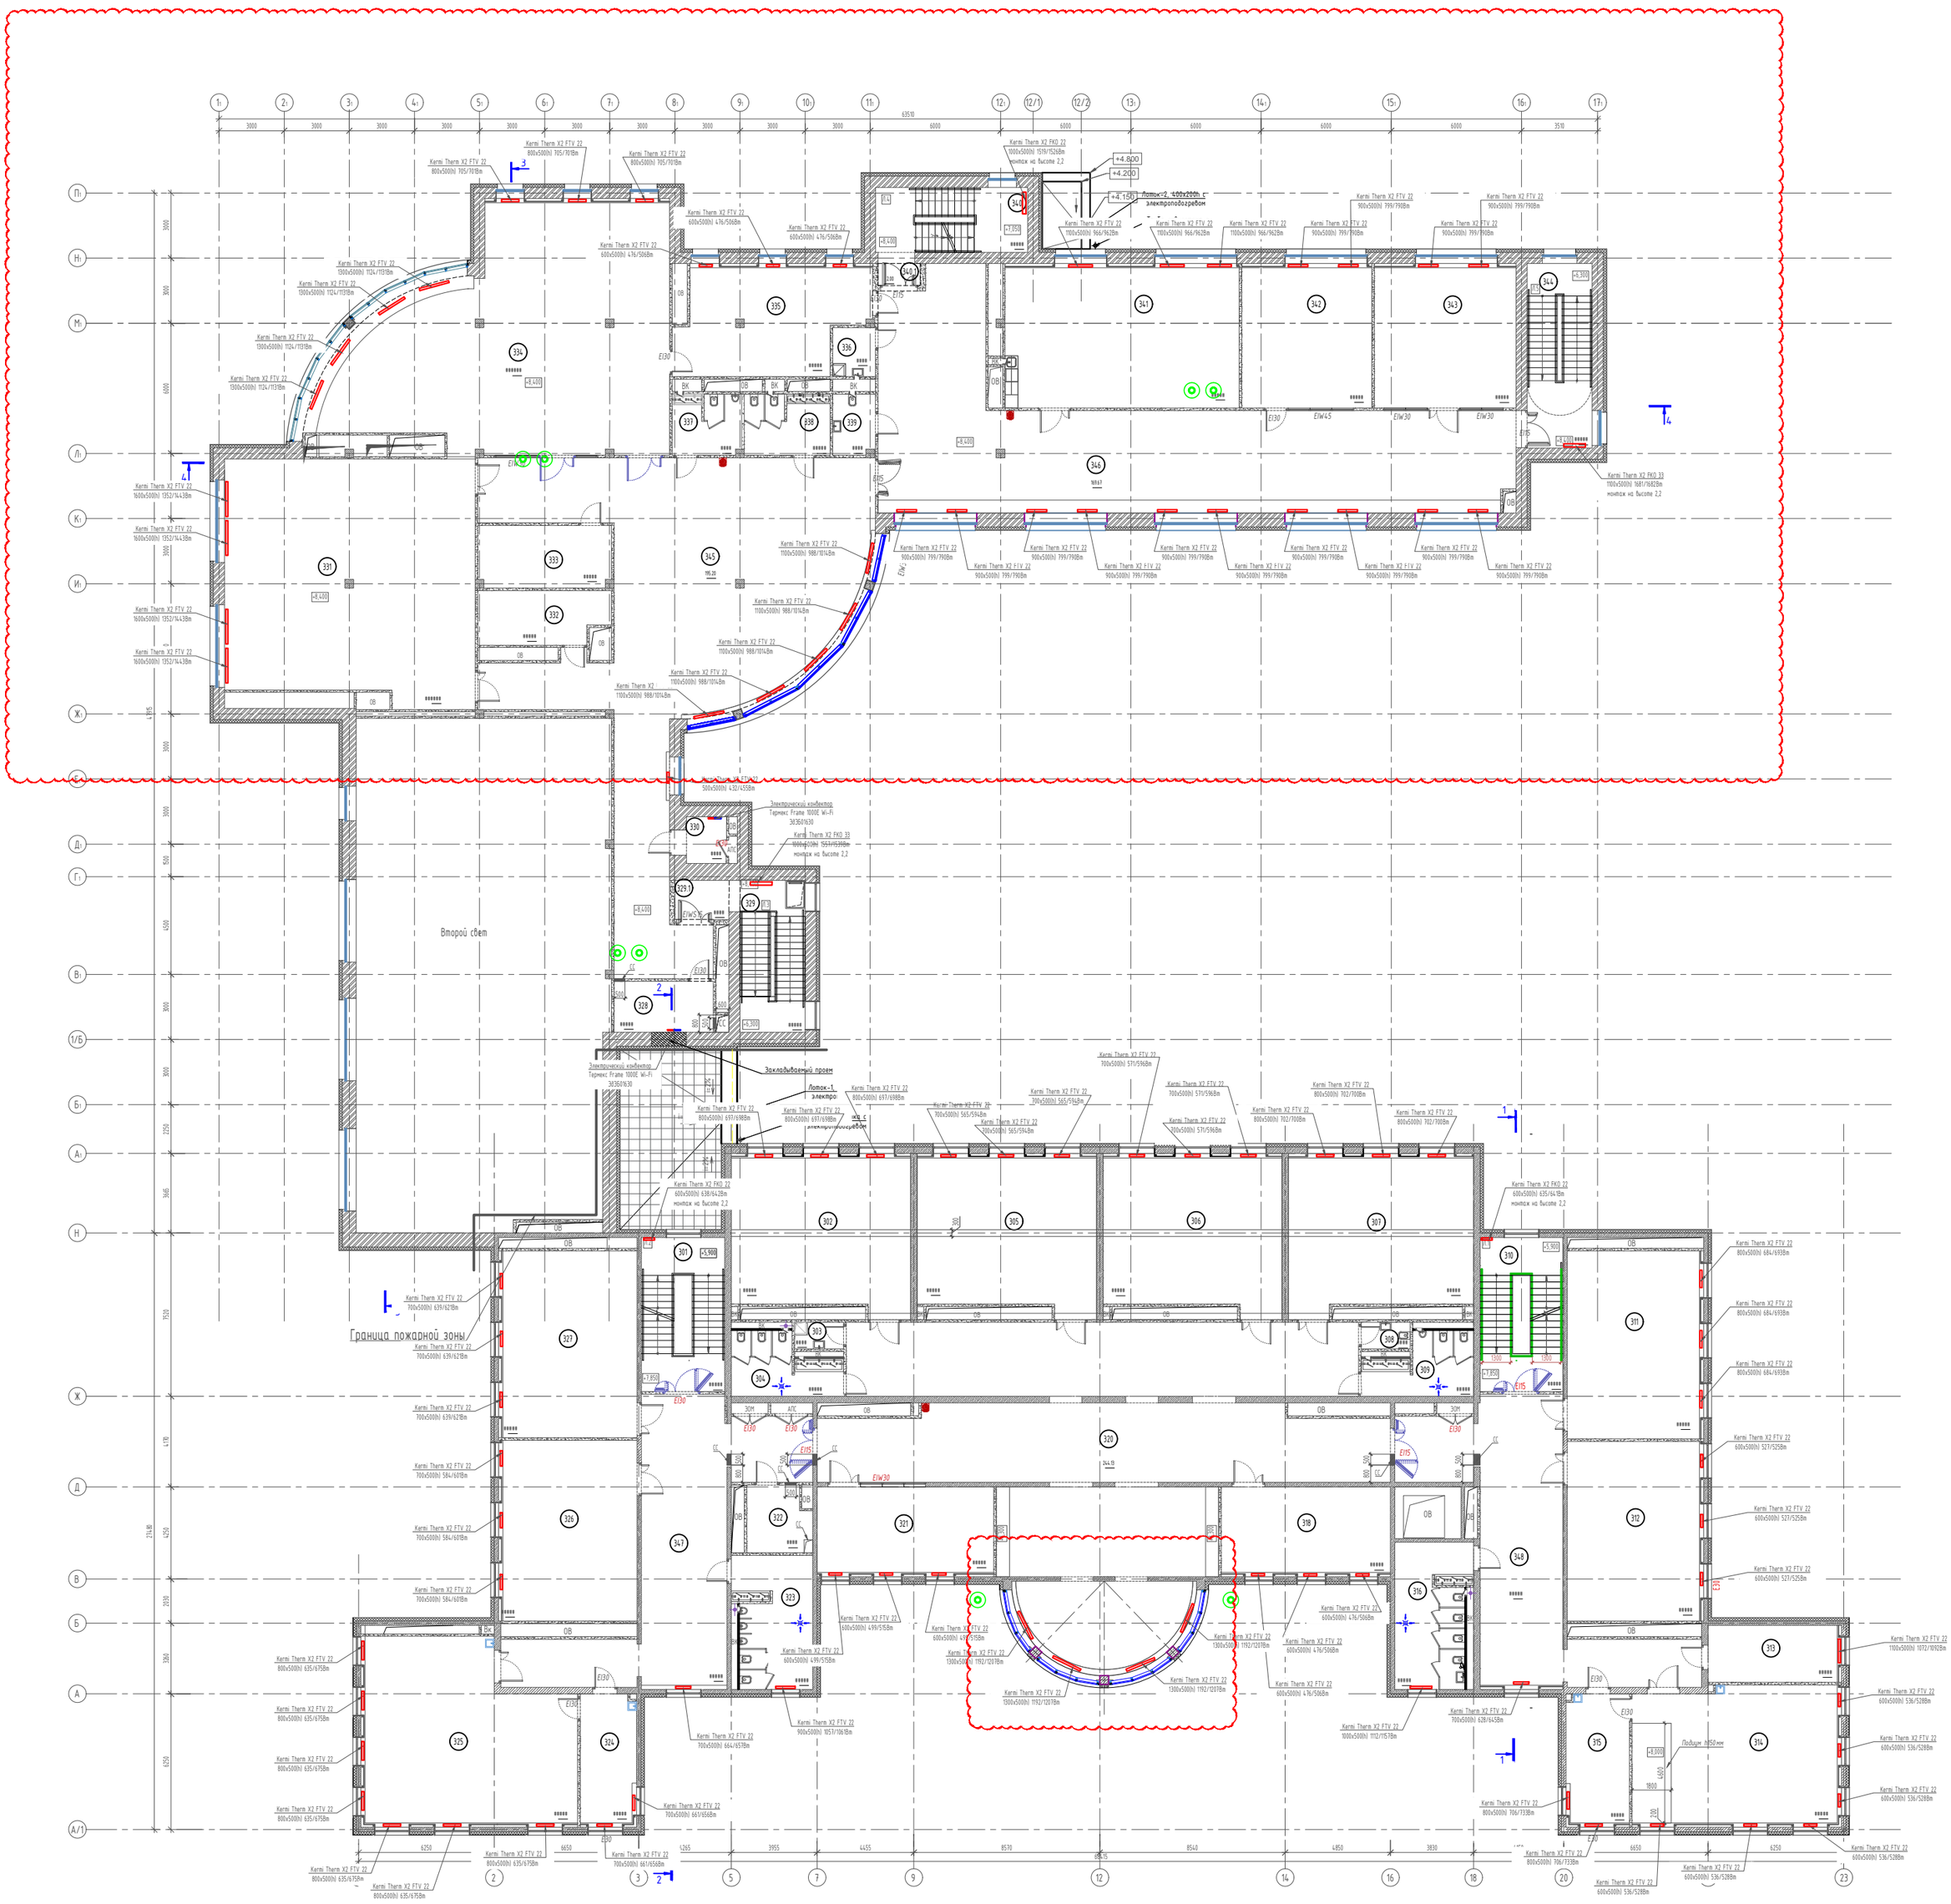
Второй свет
Граница пожарной зоны
Закладываемый проем
Лоток-1, электро
Лоток-2, 400х200h, с электропроводкой
Подиум h=50мм