




Парапет кирпичный

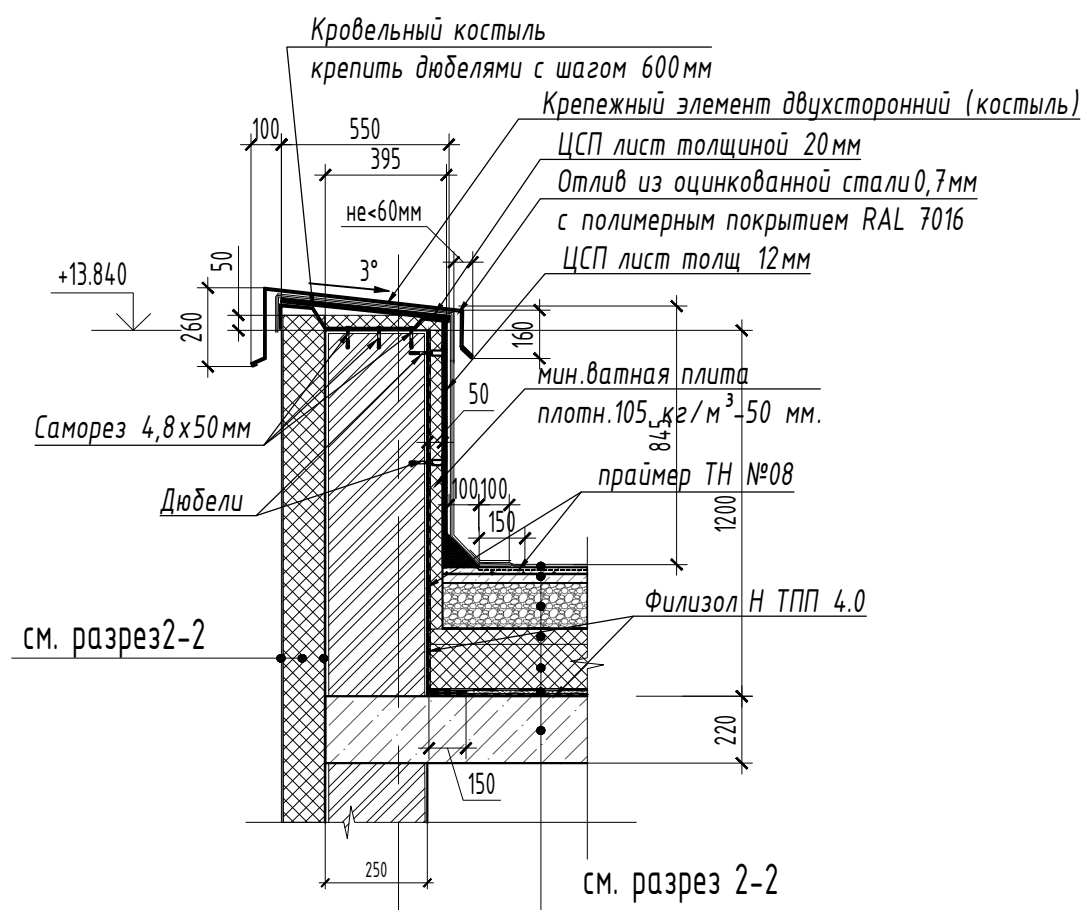


Устройство водоотведения через парапет кирпичный

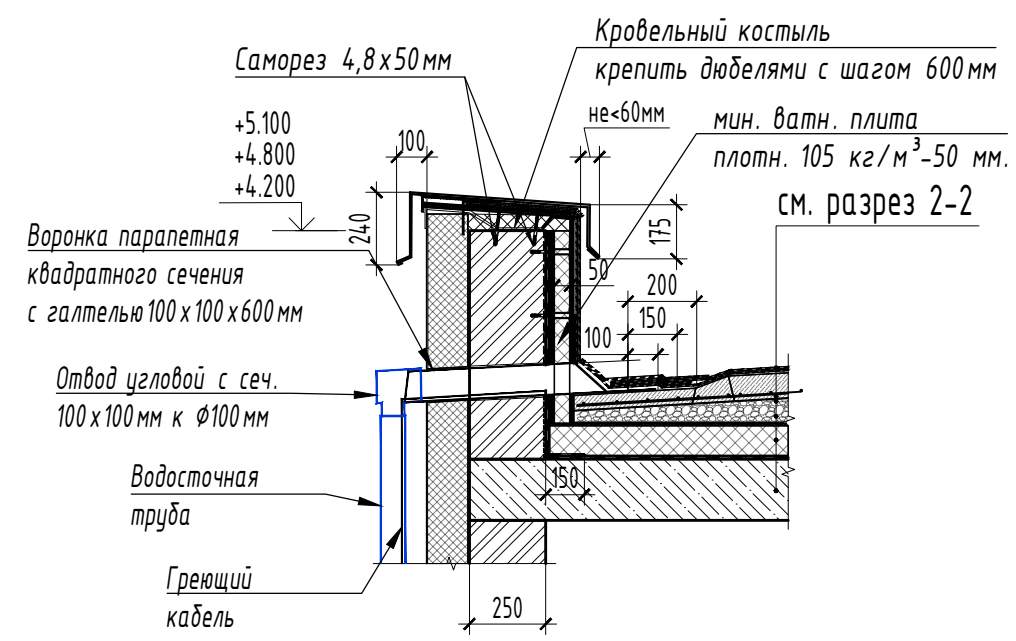


Парапет из железобетона

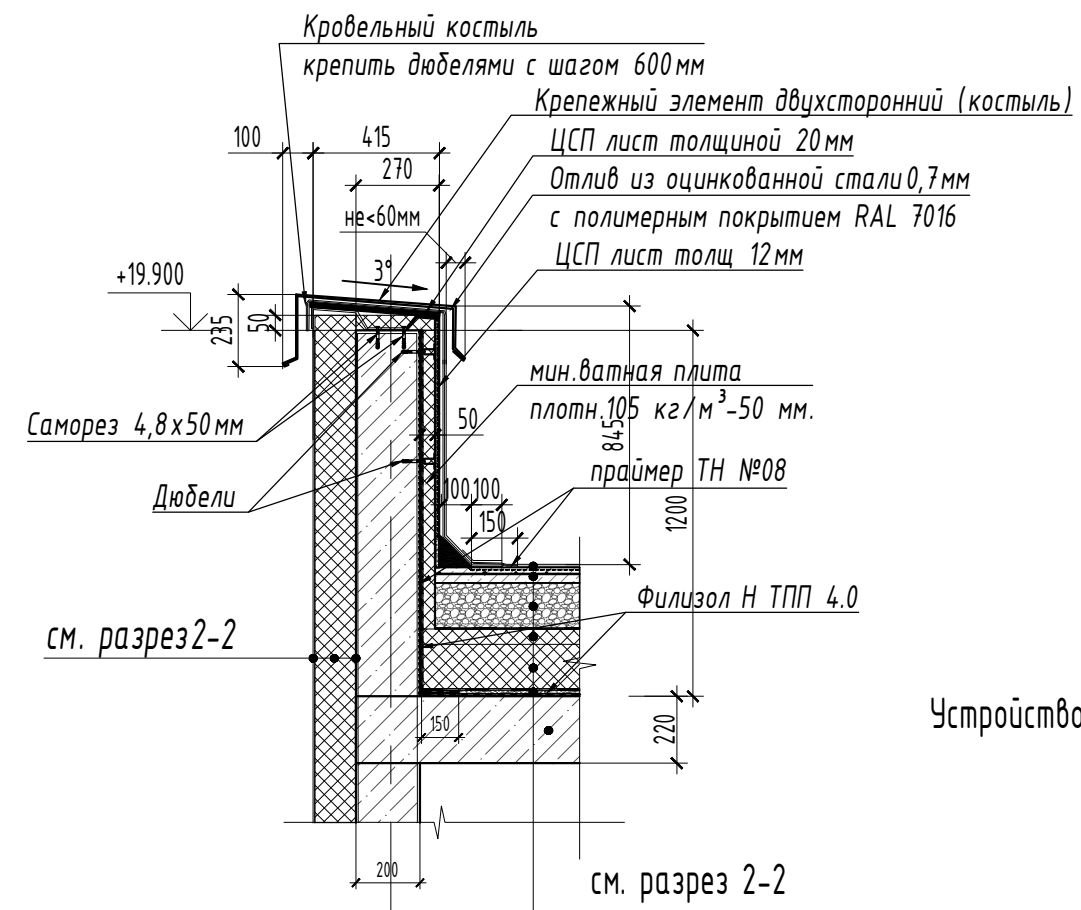

Устройство водоотведения через парапет железобетонный

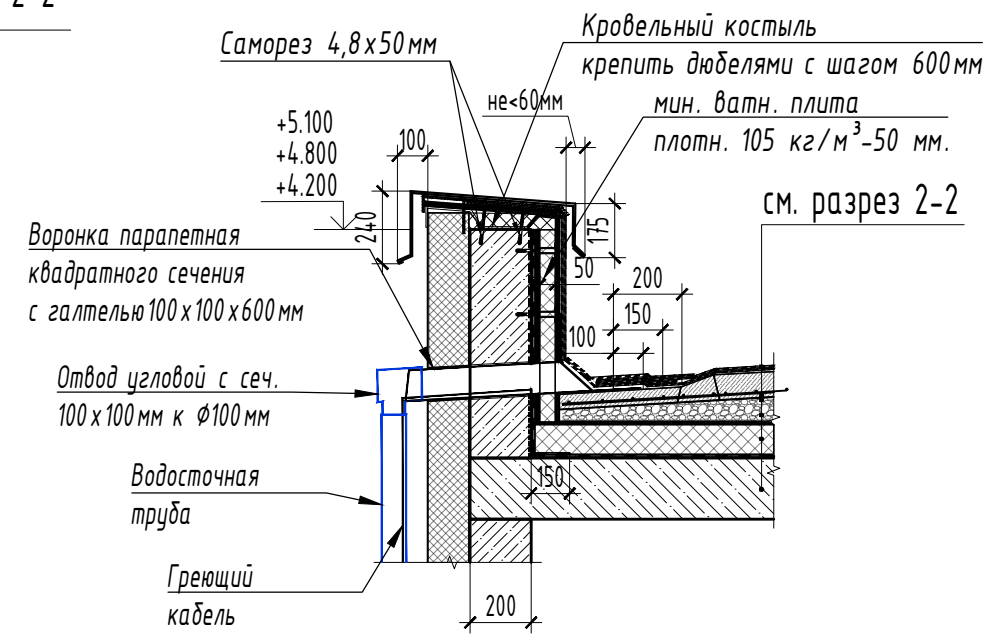

Козыль кровельный схема сгиба
М 1:25

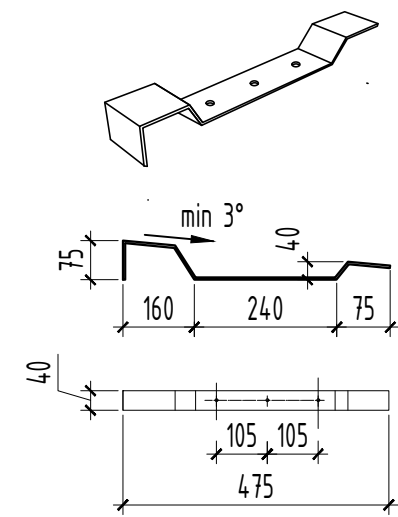

						16-25/Г-П-АР			
						Капитальный ремонт объекта "ГБОУ Школа № 429 "Соколиная гора", расположенного по адресу: г.Москва, ул. Соколиной горы 5-я, д.14			
Изм	Кол.уч	Лист	№ док	Подпись	Дата	Архитектурно-планировочные решения	Стадия	Лист	Листов
Разраб.		Барсуков			2026.07.01		Р		
Проверил.		Липавская			2026.07.01				
						Узлы устройства парапетов М 1:25		АЗУРИТ	
Н. контр.		Губарева			2026.07.01				
ГИП		Неменов			2026.07.01				