
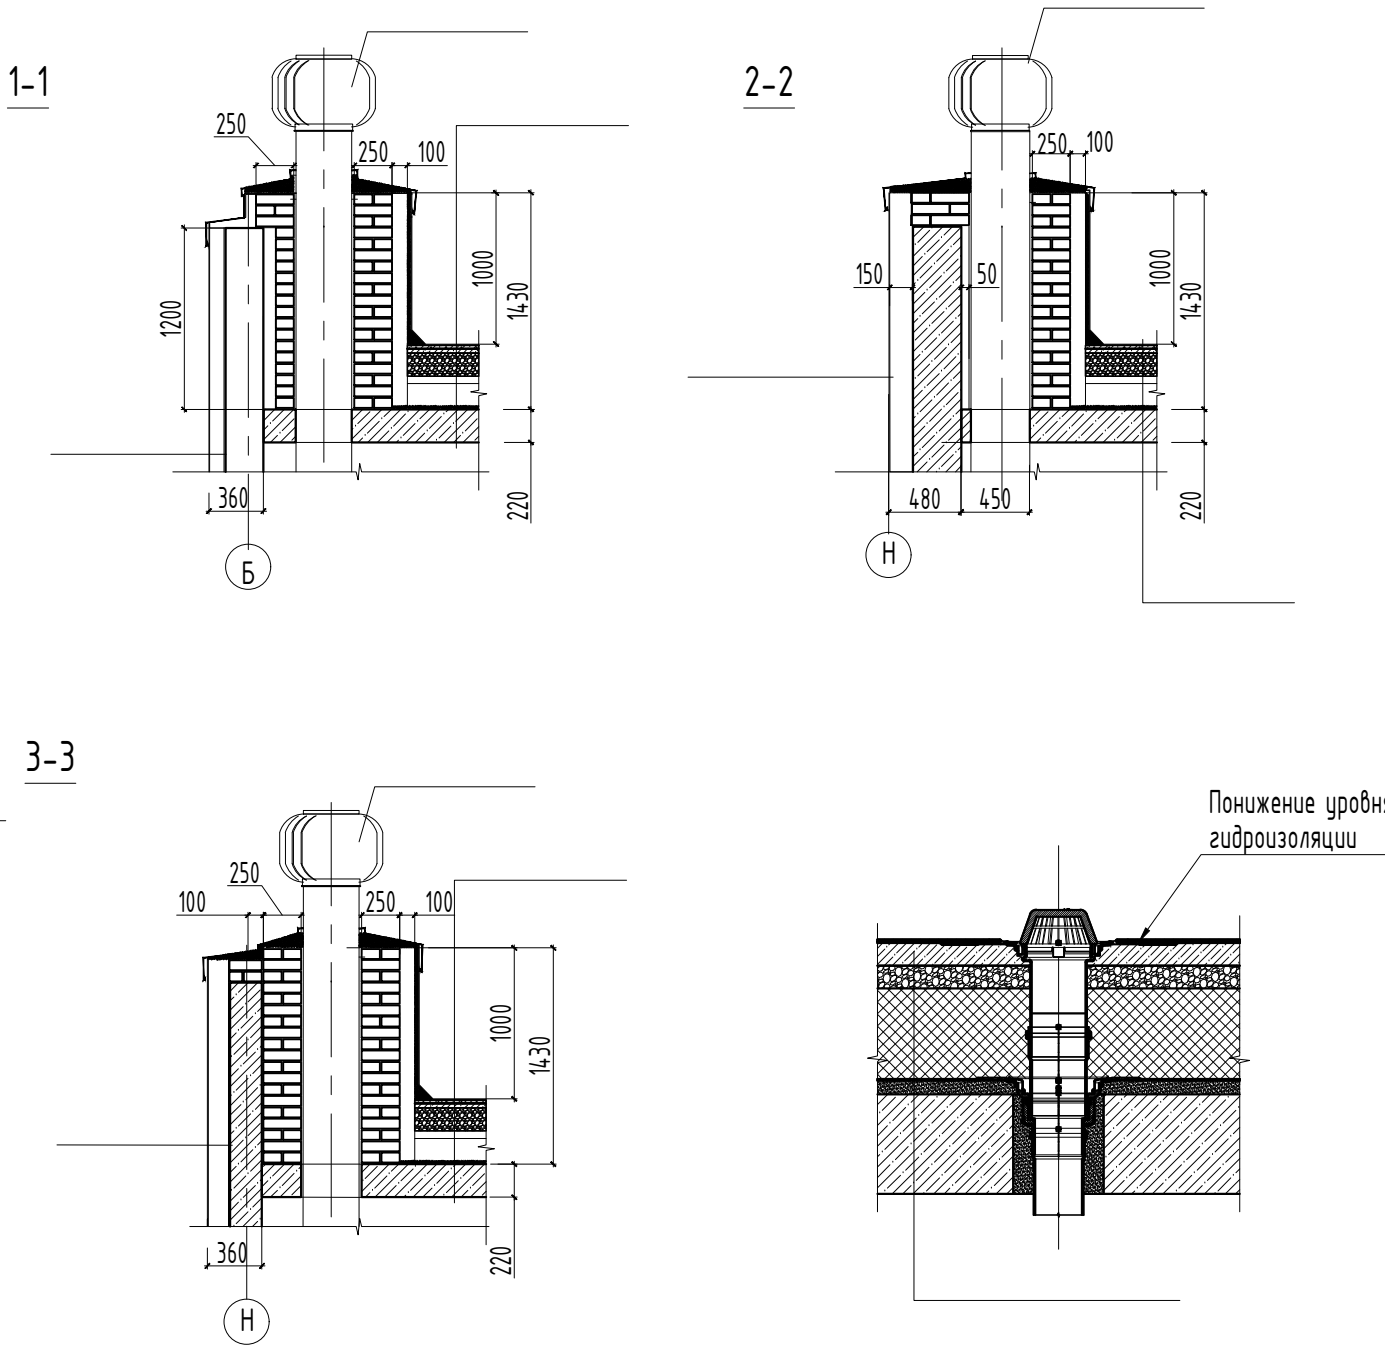


|             |              |
|-------------|--------------|
| Секции      | Всего: шт. N |
| Полы и окна |              |
| Мат. N пола |              |

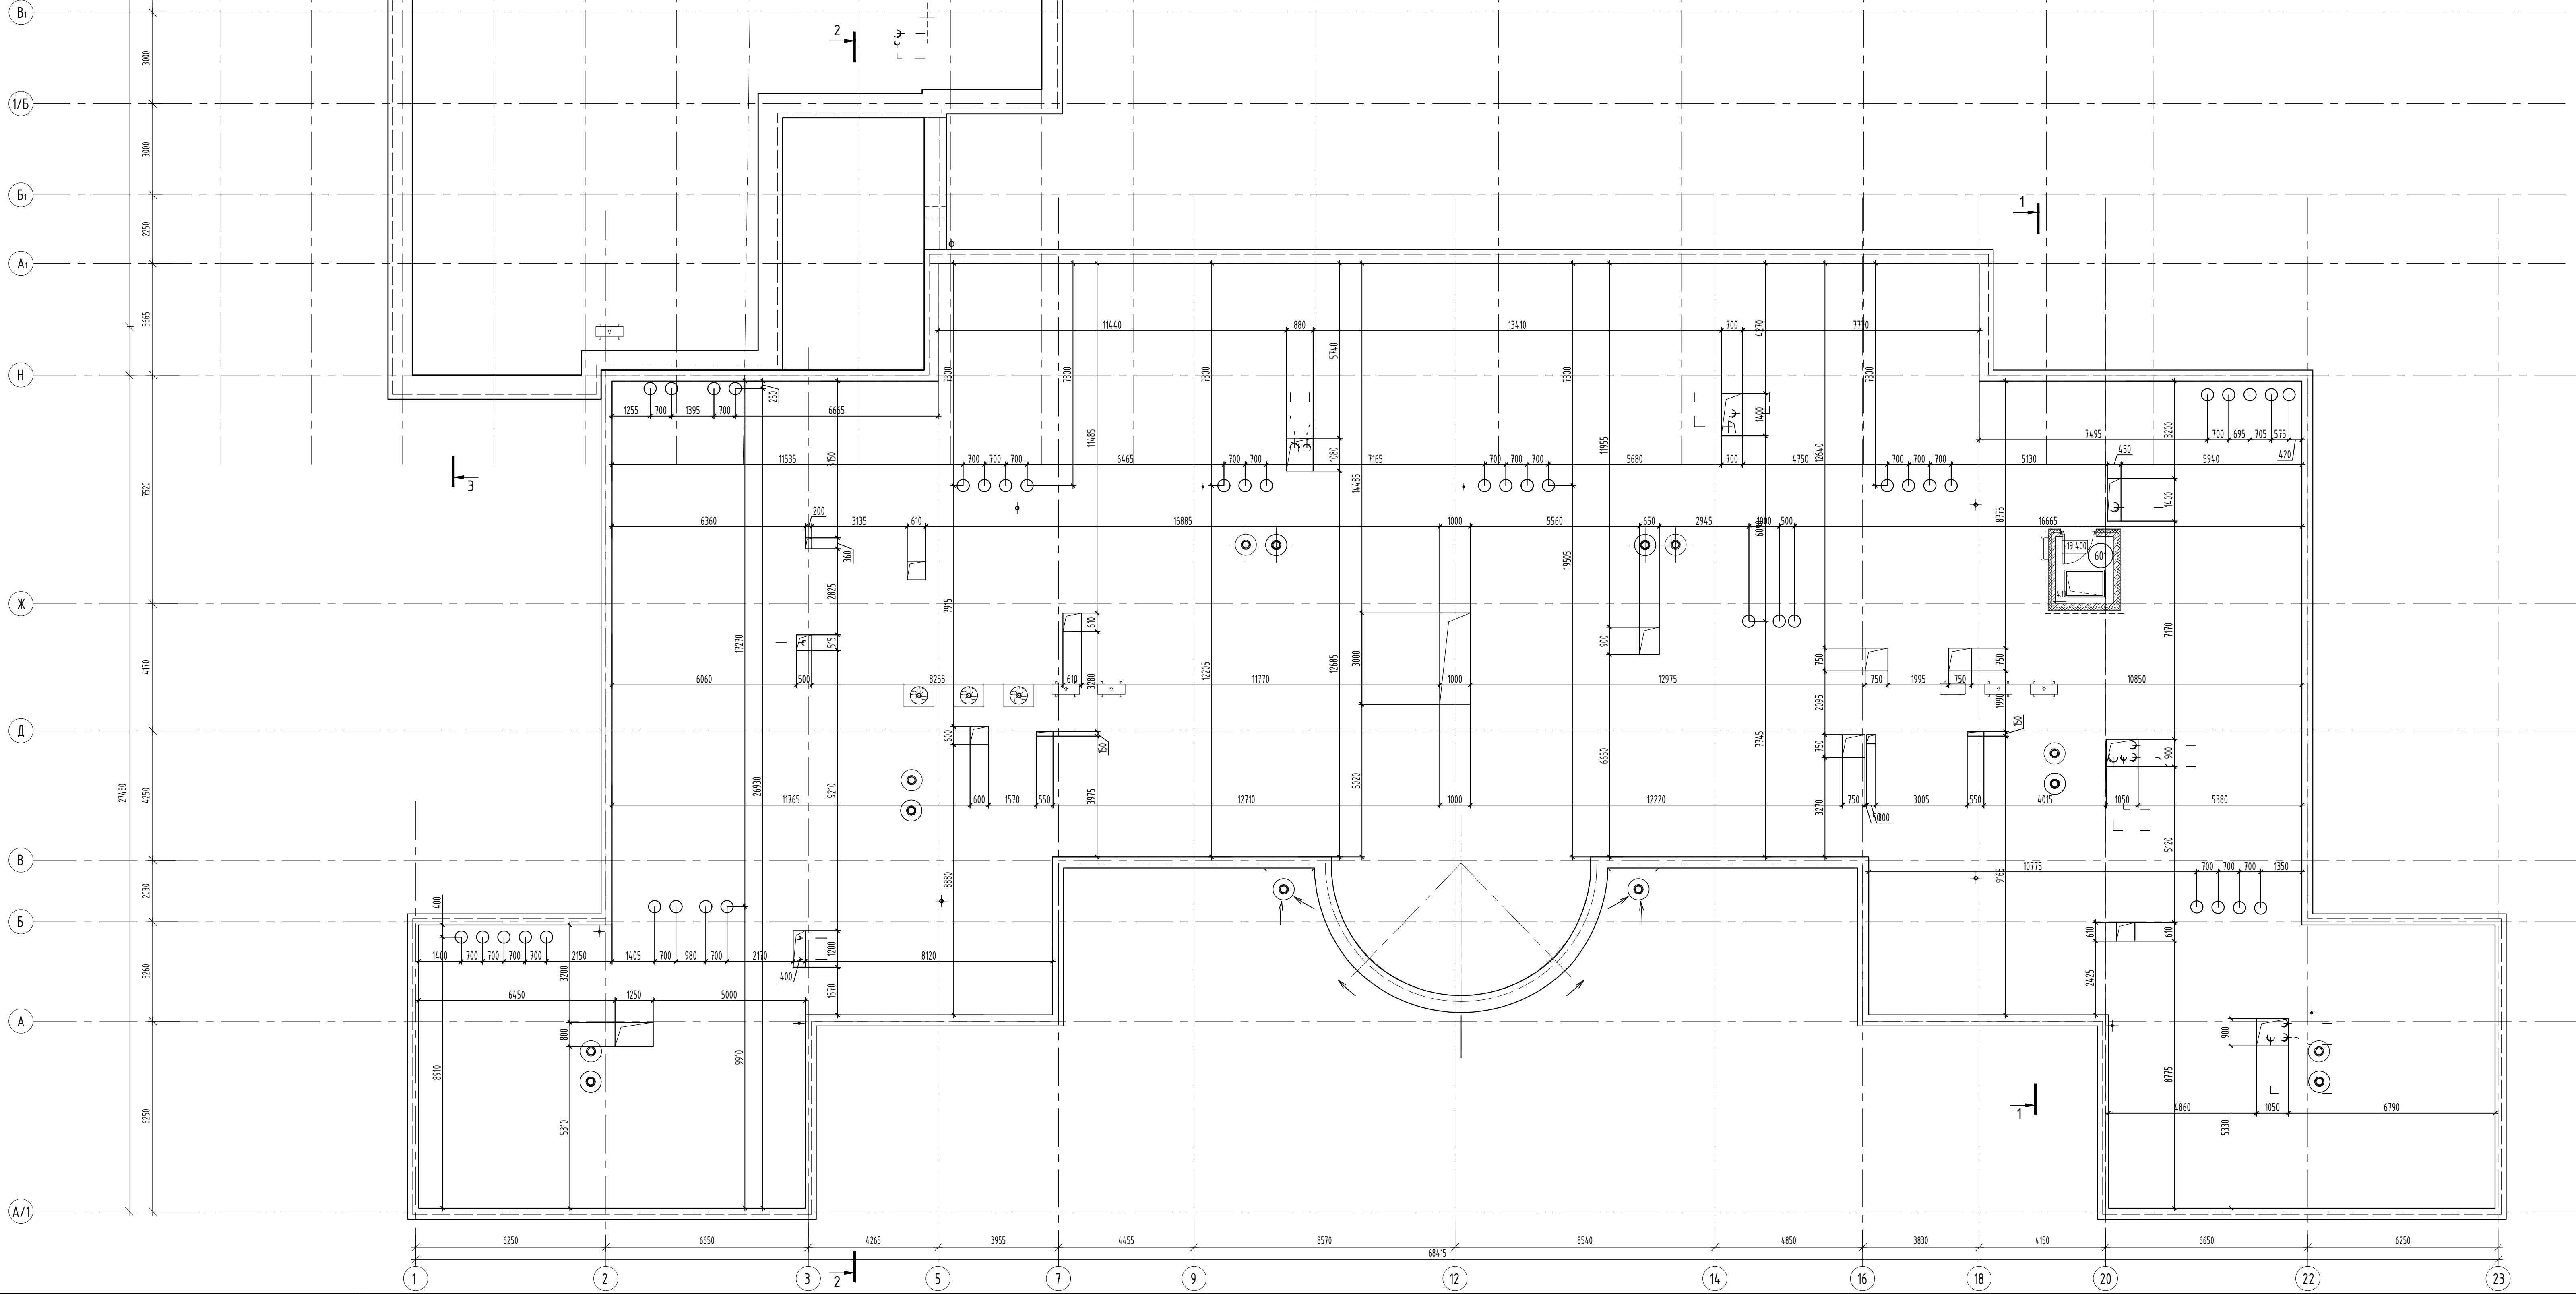

УСЛОВНЫЕ ОБОЗНАЧЕНИЯ

- Водосточная воронка (внутренний организованный водосток)
- Направление ската крыши к внутреннему организованному водостоку
- Бетонная тротуарная плитка 500x500x50 с покрытием против скольжения повышенной морозостойкости
- Маркировка огнестойкости заменяемых дверей, окон, перегородок
- Отметка уровня крыши
- Марка фановой трубы

- Возможность устройства проемов в несущих стенах будет уточняться в проекте. Размер и расположение вентиляционных шахт будет уточнен в проекте.
- Шахты предназначены для прокладки инженерных коммуникаций и стояков (ВК, СС, ЗОМ), оборудуются лючками для обслуживания.
- ★ категорирование по взрывопожарной опасности данных помещений выполнить на этапе проектирования.
- Марки ограждений смотреть альбом 16-25/Г-П-АР лист 61

|           |          |           |        |                                                                                       |            |   |                                                                                       |        |        |
|-----------|----------|-----------|--------|---------------------------------------------------------------------------------------|------------|---|---------------------------------------------------------------------------------------|--------|--------|
|           |          |           |        |                                                                                       |            | 16-25/Г-П-АР   |                                                                                       |        |        |
|           |          |           |        |                                                                                       |            | Капитальный ремонт объекта "ГБОУ Школа № 429 "Соколовая гора",<br>расположенного по адресу: г.Москва, ул. Соколовой горы 5-я, д.14 |                                                                                       |        |        |
| Изм.      | Кол.изм. | Лист      | № док. | Подпись                                                                               | Дата       | Архитектурно-планировочные решения                                                                                                 | Стадия                                                                                | Лист   | Листов |
| Разр.     |          | Липовская |        |  | 2026.07.07 |   | Р                                                                                     |        |        |
|           |          |           |        |                                                                                       |            |   |                                                                                       |        |        |
| Н. контр. | Губарева |           |        |  | 2026.07.07 | План кровли. М1:100   |  | АЗУРИТ |        |
| ГИП       | Маркова  |           |        |  | 2026.07.07 |   |                                                                                       |        |        |

±0,000=156.92

ФОРМАТ А0