


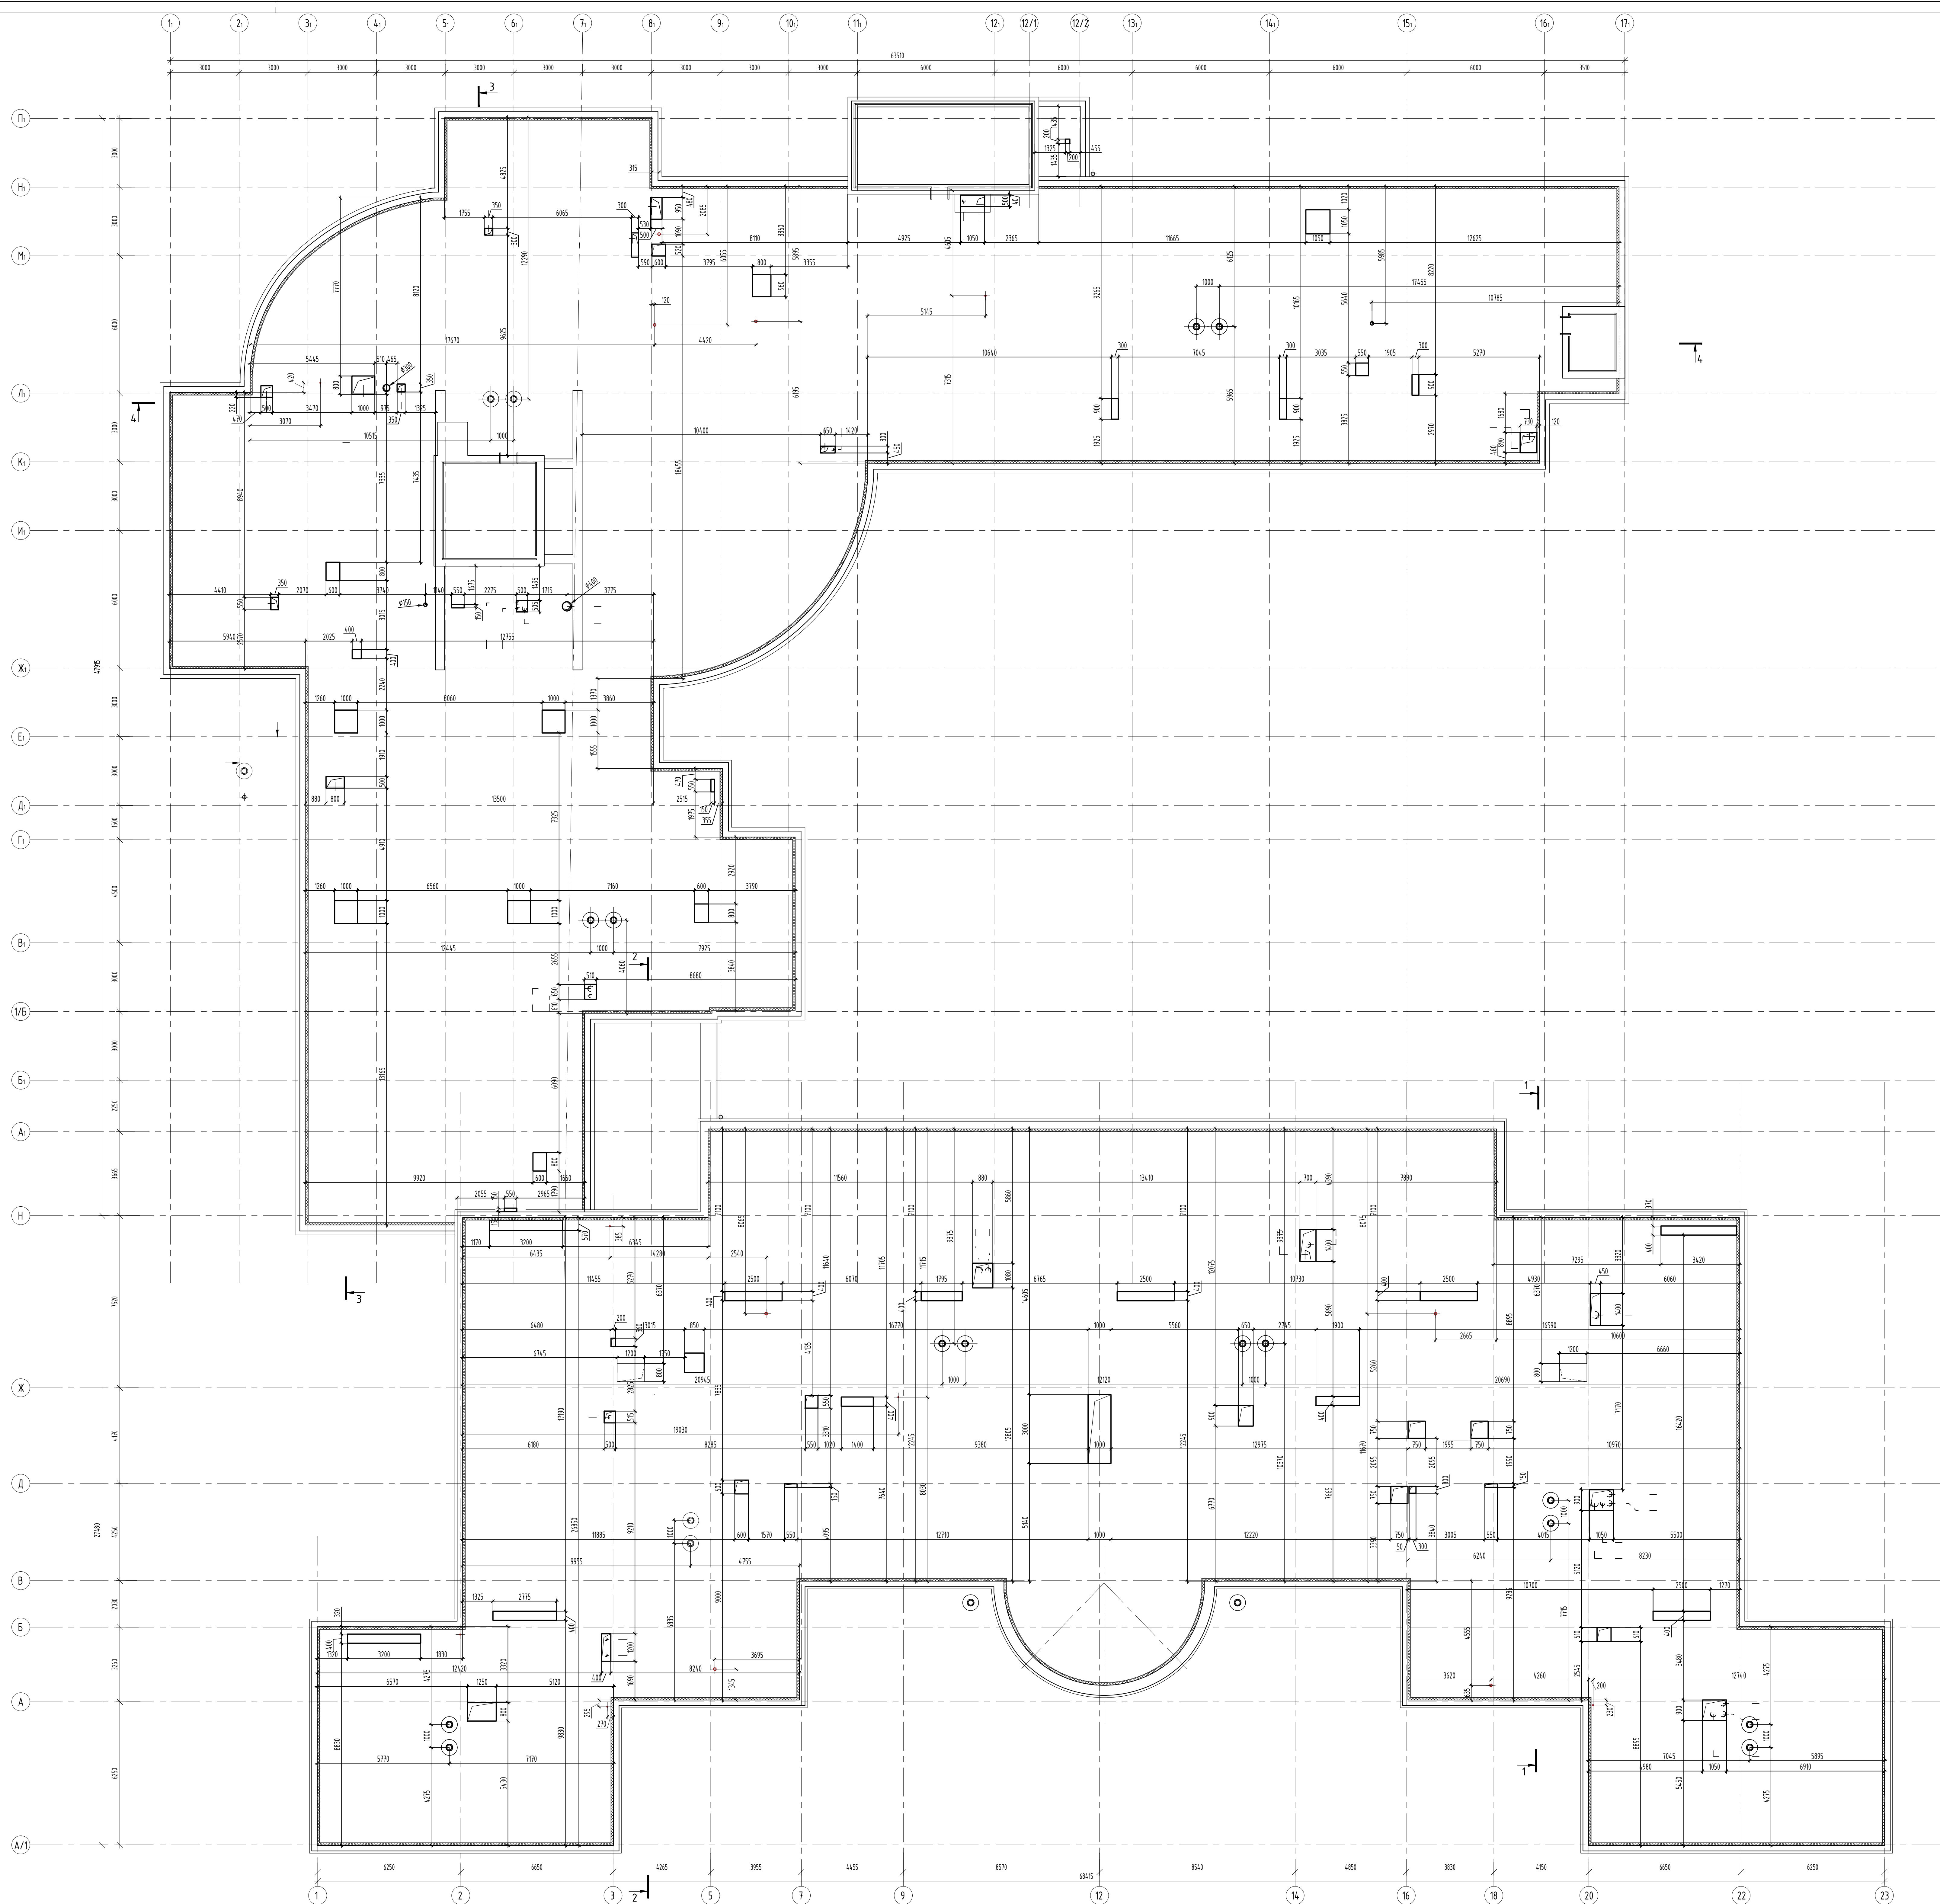


Экспликация помещений кровли

Номер помеще-ния	Наименование	Площадь м2	Кол. помеще-ния
601	Помещение выхода на кровлю	4.19	
602	Помещение выхода на кровлю	5.19	
	Всего	4.2	

УСЛОВНЫЕ ОБОЗНАЧЕНИЯ

- Водосточная воронка (внутренний организационный водосток)
- Направление ската кровли к внутреннему организованному водостоку
- Бетонная пропускная плита 500х500х50 с покрытием против скольжения повышенной морозостойкости
- Маркировка огнестойкости заменяемых дверей, окон, перегородок
- Отметка кровли
- Марка фановой трубы

1. Возможность устройства проемов в несущих стенах будет уточняться в проекте.
Размер и расположение вентиляционных шахт будет уточнен в проекте.
2. Шахты предназначены для прокладки инженерных коммуникаций и стоек (ВК, СС, ЗОМ), оборудуются лючками для обслуживания.
3. * категорирование по взрывопожарной опасности данных помещений выполнить на этапе проектирования.
4. Шахты ограждены смотреть альбом 16-25/Г-П-АР лист 61

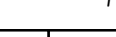					№-25/Г-П-АР		
					Капитальный ремонт объекта "БСФУ Школа № 429 "Скопаяная гора", расположенного по адресу: г.Москва, ул. Скопояной горы 5-я, д.14		
Изм.	Кол.ар.	Лист	№"Докум.	Подпись	Дата		
Разработ		Литовских			2020.07.05		
Архитектурно-планировочные решения						Станд.	Лист
							Листов
И.контр.	Губарева				2020.07.05		
Гит.	Морозов				2020.07.05		
Ллан кровли: М1100						 АЗУРИТ	