


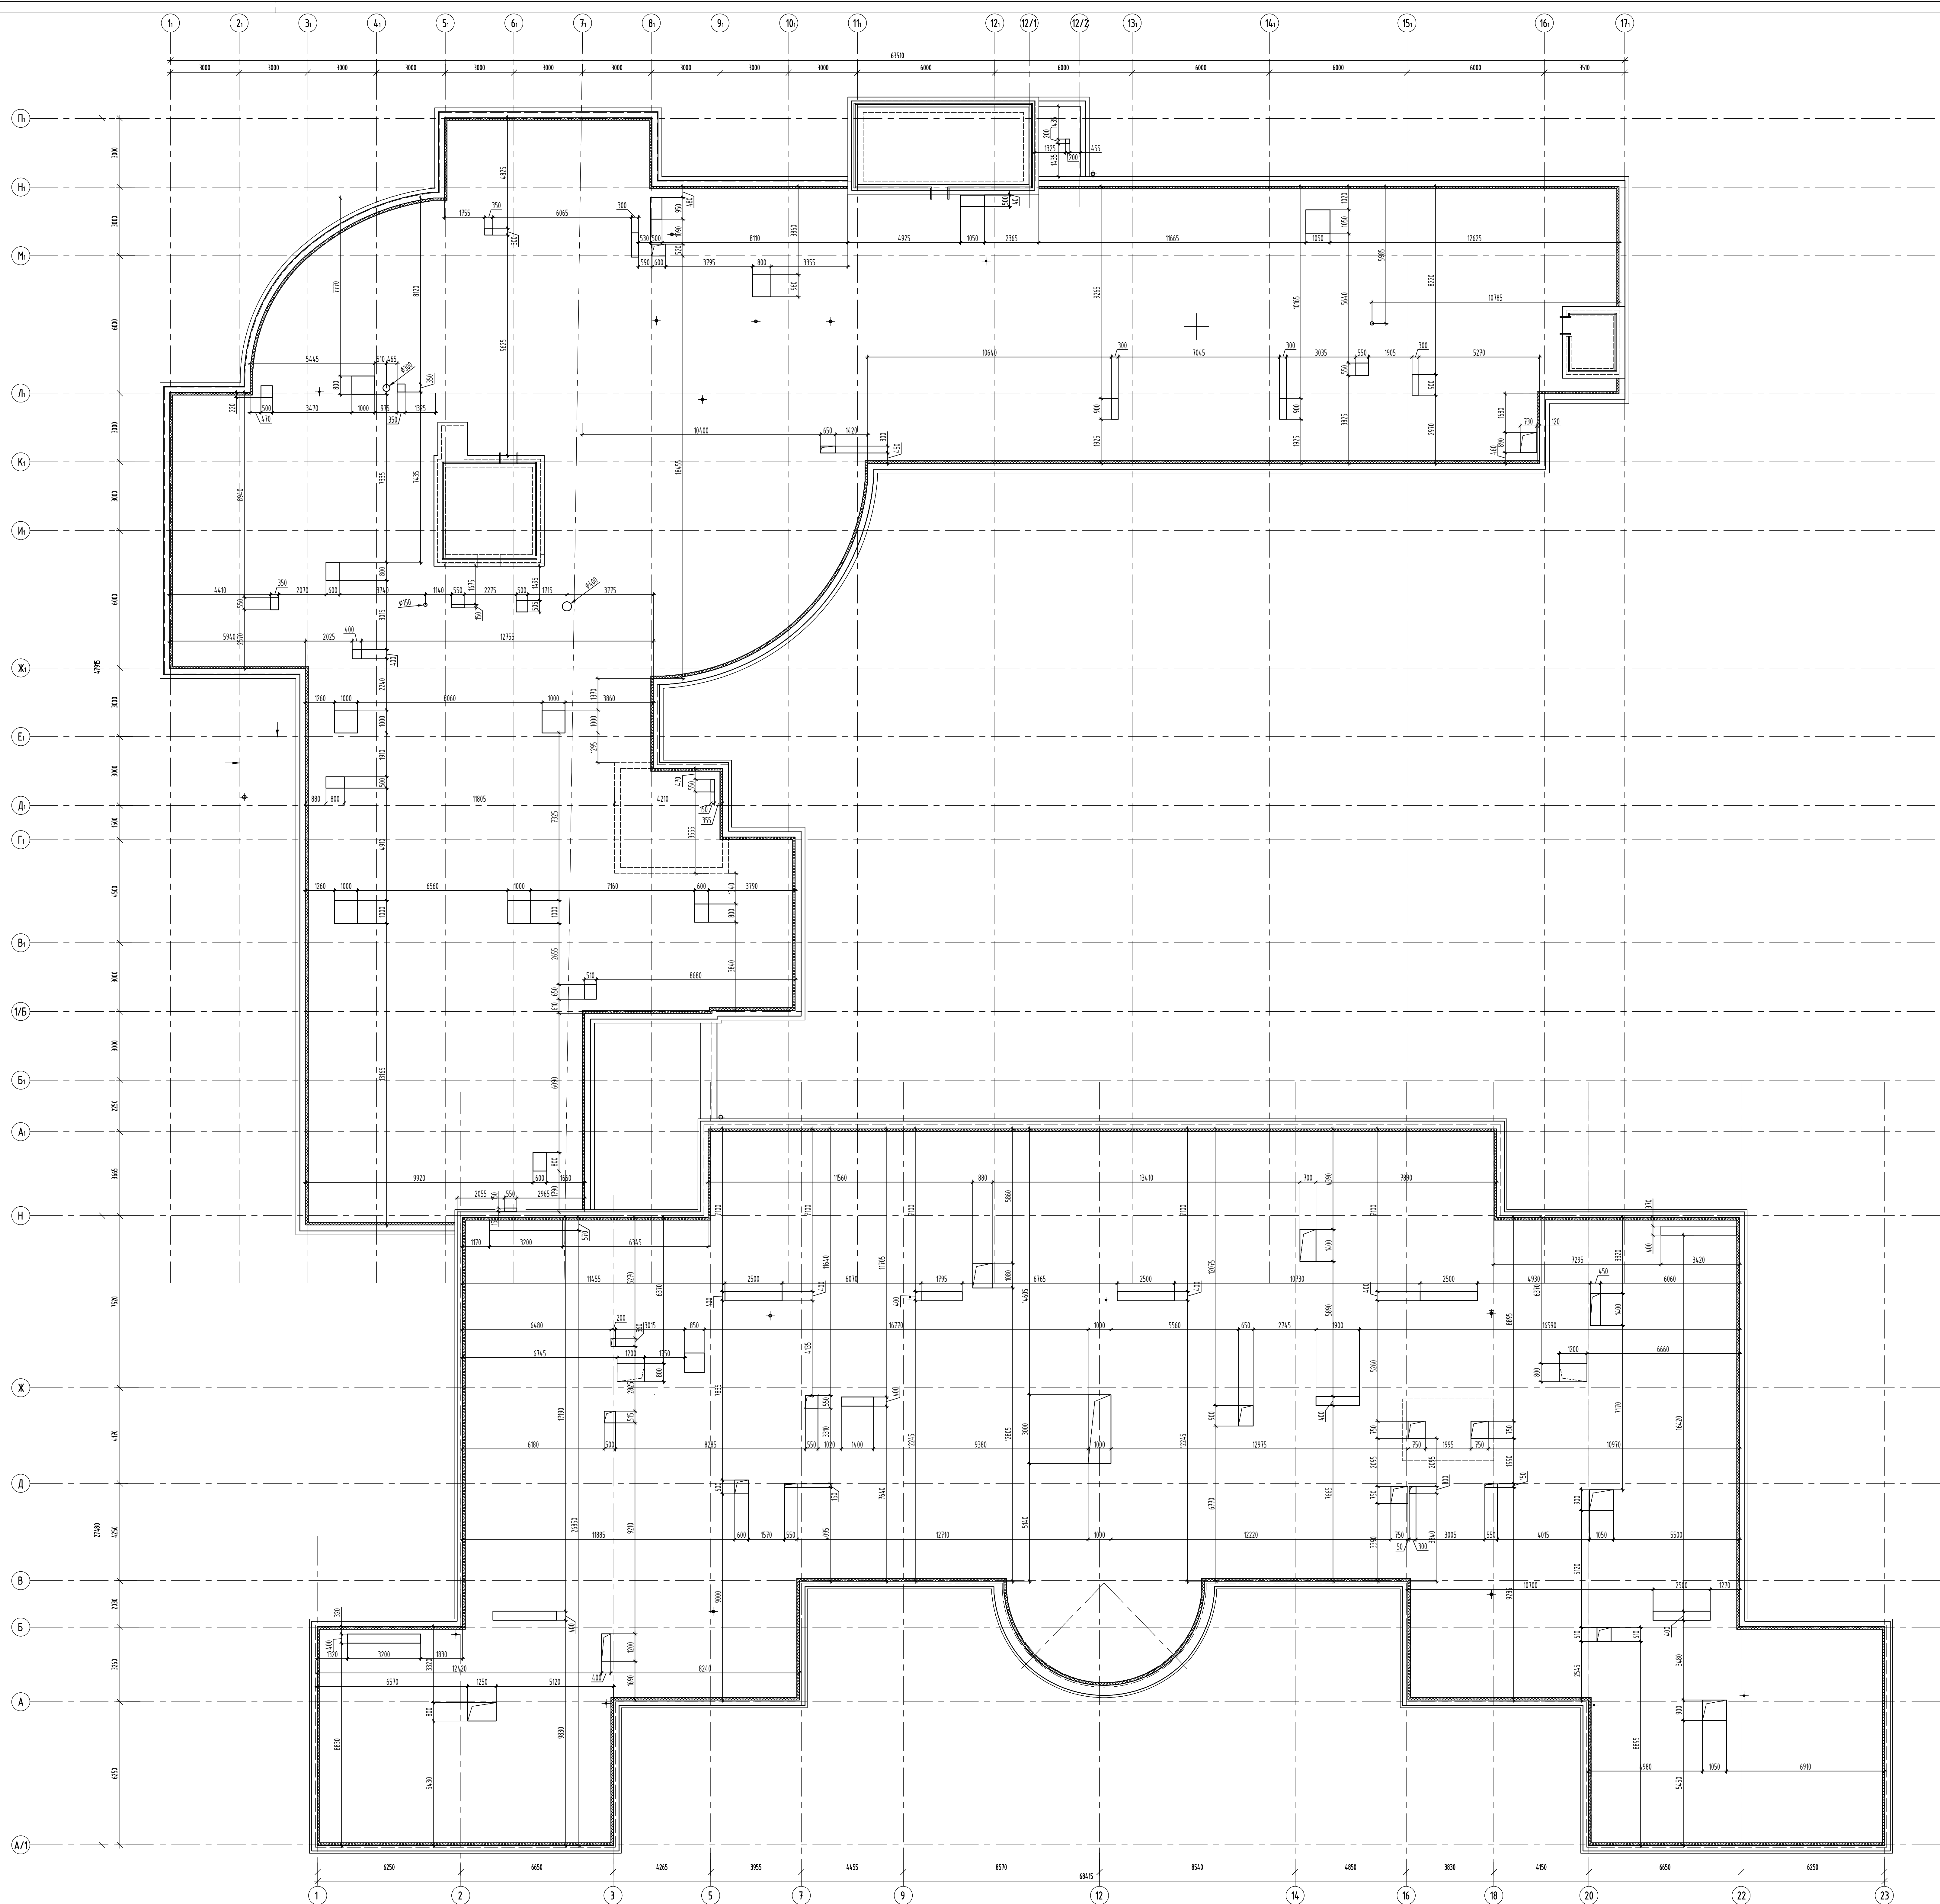

Номер помещения	Наименование	Площадь м2	Кат. помещ.ения
601	Помещение выхода на кровлю	4.19	
602	Помещение выхода на кровлю	5.19	
	Всего	4.2	

- Бетонная пропускная плитка 500х500х50 с покрытием против скольжения повышенной морозостойкости
- Маркировка огнестойкости заменяемых дверей, окон, перегородок
- Отметка уровня кровли
- Марка фановой пружины

1. Возможность устройства проемов в несущих стенах будет уточняться в проекте.
Размер и расположение вентиляционных шахт будет уточнен в проекте.
2. Шахты предназначены для прокладки инженерных коммуникаций и стоек (ВК, СС, ЗОМ), оборудуются люками для обслуживания.
3. * категорирование по взрывопожарной опасности данных помещений выполнить на этапе проектирования.
4. Шахты ограждены смотреть альбом 16-25/Г-1-АР лист 61

					№ 25/Г - П-АР		
					Капитальный ремонт объекта "БСШ Школа № 429 "Скопелская гора", расположенного по адресу: г. Москва, ул. Скопелской горы 5-а, д. 14		
Изм.	Кол. экз.	Листы	№ док.	Подпись	Дата		
Разработ		Листовских			2020.07.05		
Архитектурно-планировочные решения						Страница	Листы
						р	Листов
И. контр.	Губарева				2020.07.05	План кровли: М1100	
Гипот.	Григорьев				2020.07.05	 АЗУРИТ	