
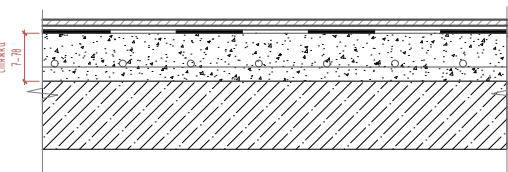
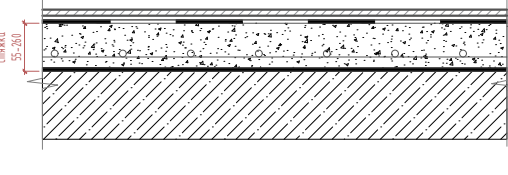
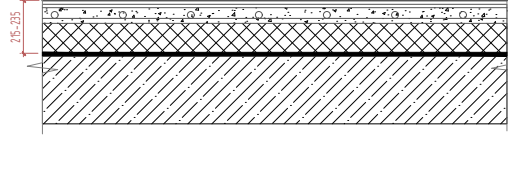
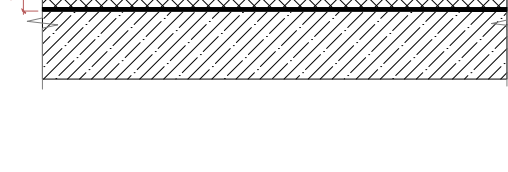
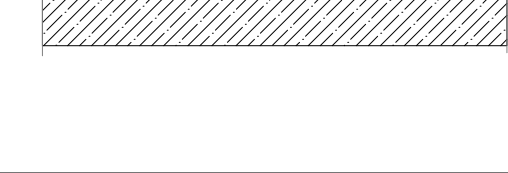
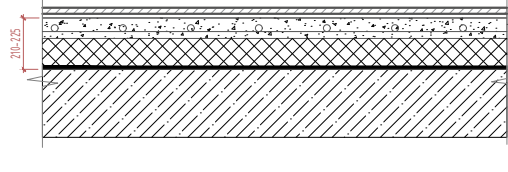
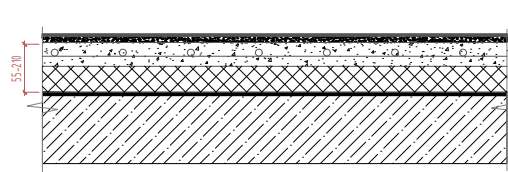
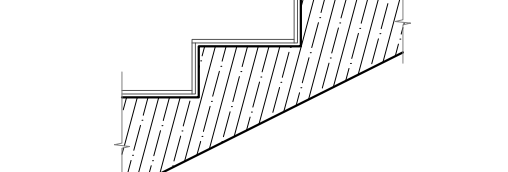
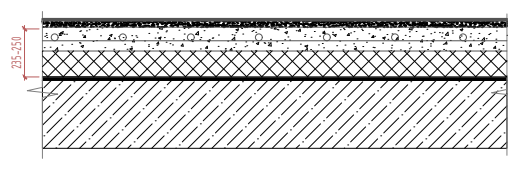
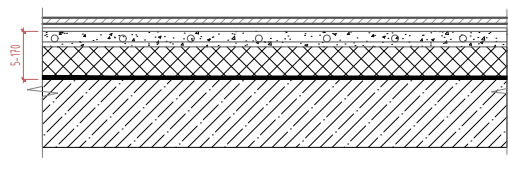
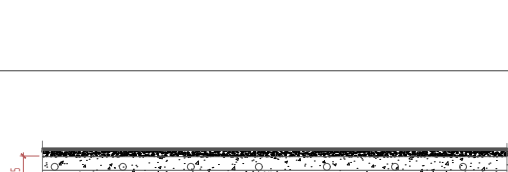
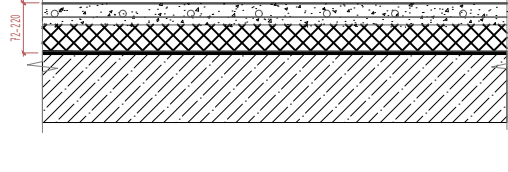
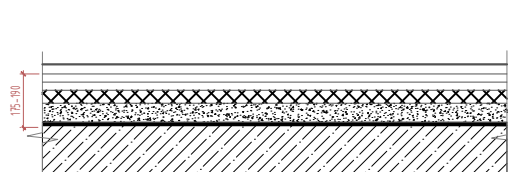
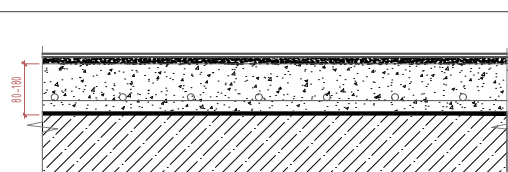


Сводная ведомость конструкций полов

Номер помещения	Марка помещения	Схема пола	Элементы пола и их толщина, мм	Площадь, м2						
				Подвал	1 этаж	2 этаж	3 этаж	4 этаж	Тех. этаж	Всего
102, 109, 110, 111, 107, 130, 132, 120, 131, 169, 171	Tun 1		1. Керамогранит крупноформатный матовый, цвет "под бетон" Kerama Marazzi Фондamenta пепельный светлый обрезной DL500720R (1195x600x9 мм) на клею (укладка со смещением на 1/2 по длинной стороне) -20 мм 2. Армированная цементно-песчаная стяжка М150, армированная сеткой #5BrIII шаг 100x100, 1800 кг/м3 -7-78 мм 3. Пленка полиэтиленовая 200 мкм - 5 мм 4. Звукоизоляция 5. Существующая ж/б плита	-	710,61	-	-	-		710,61
106, 112, 113, 125, 118, 119, 134, 134, 139, 140, 142, 156, 157, 160, 161, 164, 221, 214, 204, 203, 209, 208, 239, 240, 237, 238, 323, 316, 304, 303, 308, 309, 337, 338, 339, 423, 416, 409, 408, 403, 404	Tun 2		1. Керамогранит крупноформатный матовый, цвет "под бетон" Kerama Marazzi Фондamenta пепельный светлый серый обрезной DL600720R (600x600x9 мм) на клею -20 мм 2. Гидроизоляция 2 слоя с заведением на стены на 200 мм 3. Армированная цементно-песчаная стяжка М150, армированная сеткой #5BrIII шаг 100x100, 1800 кг/м3 -50 мм 4. Засыпка керамзитовым гравием (фракции 20-40 мм) по ГОСТ 32497-2013 против цементным молочком, марки П50-100 или звукоизоляционная плита Rockwool ФЛОР БАТТС на клею (Пропасть наклон уклон 55:30 мм) -6-210 мм 5. Пленка полиэтиленовая 200 мкм 6. Звукоизоляция 7. Существующая ж/б плита -5 мм	-	141,06	124,36	102,69	73,23	-	441,34
138, 1, 142, 2, 158, 159	Tun 3		1. Керамогранит крупноформатный матовый, цвет "под бетон" Kerama Marazzi Про Стоун серый светлый обрезной DD600320R (600x600x9 мм) на клею - 20 мм 2. Гидроизоляция 2 слоя (с заведением на стены на 200 мм) 3. Армированная цементно-песчаная стяжка М150, армированная сеткой #5BrIII шаг 100x100, 1800 кг/м3 -50 мм 4. Засыпка керамзитовым гравием (фракции 20-40 мм) по ГОСТ 32497-2013 против цементным молочком, марки П50-100 или звукоизоляционная плита Rockwool ФЛОР БАТТС на клею -165-185 мм 5. Гидроизоляция (с заведением на стены на 200 мм) 6. Существующая ж/б плита	-	17,50	-	-	-		
101, 171, 112, 1, 215, 229, 1, 333, 1	Tun 3.1		1. Керамогранит крупноформатный матовый, цвет "под бетон" Kerama Marazzi Про Стоун серый светлый обрезной DD600320R (600x600x9 мм) на клею - 20 мм 2. Армированная цементно-песчаная стяжка М150, армированная сеткой #5BrIII шаг 100x100, 1800 кг/м3 -50 мм 3. Засыпка керамзитовым гравием (фракции 20-40 мм) по ГОСТ 32497-2013 против цементным молочком, марки П50-100 или звукоизоляционная плита Rockwool ФЛОР БАТТС на клею -27-155 мм 4. Пленка полиэтиленовая 200 мкм 5. Звукоизоляция 6. Существующая ж/б плита	-	5,80	11,10	5,14			22,04
144, 145, 146, 143, 147, 1, 147, 148, 149, 152, 152, 1, 151, 150, 153	Tun 4		1. Керамогранит крупноформатный матовый, цвет "под бетон" Kerama Marazzi Фондamenta пепельный светлый обрезной DL600920R (600x600x9 мм) на клею - 20 мм 2. Гидроизоляция с заведением на стены на 200 мм 3. Армированная цементно-песчаная стяжка М150, армированная сеткой #5BrIII шаг 100x100, 1800 кг/м3 -50 мм 4. Засыпка керамзитовым гравием (фракции 20-40 мм) по ГОСТ 32497-2013 против цементным молочком, марки П50-100 или звукоизоляционная плита Rockwool ФЛОР БАТТС на клею -160-175 мм 5. Пленка полиэтиленовая 200 мкм 6. Звукоизоляция 7. Существующая ж/б плита - 5 мм	-	225,57	-	-	-	-	225,57
154	Tun 5		1. Керамогранит крупноформатный матовый, цвет "под бетон" Kerama Marazzi Фондamenta серый светлый обрезной DL500720R (1195x600x9 мм), укладка буквой "Г" на клею - 20 мм 2. Армированная цементно-песчаная стяжка М150, армированная сеткой #5BrIII шаг 100x100, 1800 кг/м3 -50 мм 3. Засыпка керамзитовым гравием (фракции 20-40 мм) по ГОСТ 32497-2013 против цементным молочком, марки П50-100 или звукоизоляционная плита Rockwool ФЛОР БАТТС на клею -160-175 мм 4. Пленка полиэтиленовая 200 мкм 5. Звукоизоляция 6. Существующая ж/б плита - 5 мм	-	6150	-	-	-	-	6150
	Tun 5		1. Керамогранит крупноформатный матовый, цвет "под бетон" Kerama Marazzi Фондamenta серый светлый обрезной DL500820R (1195x600x9 мм), укладка буквой "Г" на клею -20 мм 2. Армированная цементно-песчаная стяжка М150, армированная сеткой #5BrIII шаг 100x100, 1800 кг/м3 -50 мм 3. Засыпка керамзитовым гравием (фракции 20-40 мм) по ГОСТ 32497-2013 против цементным молочком, марки П50-100 или звукоизоляционная плита Rockwool ФЛОР БАТТС на клею -160-175 мм 4. Пленка полиэтиленовая 200 мкм 5. Звукоизоляция 6. Существующая ж/б плита - 5 мм	-	6150	-	-	-	-	6150
151, 110, 172, 163, 168, 201, 210, 229, 241, 242, 301, 310, 329, 340, 344, 401, 410, 427, 501, 502	Tun 6		1. Керамогранит крупноформатный матовый, цвет "под камень" Kerama Marazzi Про Лайнстоун серый светлый натуральный DD641020R (600x600x9 мм) на клею -20 мм 2. Армированная цементно-песчаная стяжка М150, армированная сеткой #5BrIII шаг 100x100, 1800 кг/м3 -50 мм 3. Засыпка керамзитовым гравием (фракции 20-40 мм) по ГОСТ 32497-2013 против цементным молочком, марки П50-100 или звукоизоляционная плита Rockwool ФЛОР БАТТС на клею -5-160 мм 4. Существующая ж/б плита	-	12100	72,00	72,00	43,00	29,00	337,00
151, 110, 172, 163, 168, 201, 210, 229, 241, 242, 301, 310, 329, 340, 344, 401, 410, 427, 501, 502	Tun 7		Проступь забальцованная: 1. Керамогранит матовый, цвет "под камень" Kerama Marazzi Про Лайнстоун серый светлый натуральный DD205320R-GR (600x300x9 мм) на клею - 20 мм 2. Существующая ж/б плита	7,0	66,0	66,0	66,0	66,0	20,0	291,00
	Tun 7		Подступенок: 1. Керамогранит матовый, цвет "под камень" Kerama Marazzi Про Лайнстоун серый светлый натуральный DD205320R-12 (600x145x9 мм) на клею - 20 мм 2. Существующая ж/б плита	8,6	32,00	32,00	32,00	32,00	9,0	145,60
155, 156	Tun 8		1. Линолеум - 2 мм 2. Нивелирующая масса - 10 мм 3. Армированная цементно-песчаная стяжка М150, армированная сеткой #5BrIII шаг 100x100, 1800 кг/м3 -50 мм 4. Засыпка керамзитовым гравием (фракции 20-40 мм) по ГОСТ 32497-2013 против цементным молочком, марки П50-100 или звукоизоляционная плита Rockwool ФЛОР БАТТС на клею -185-200 мм 5. Пленка полиэтиленовая 200 мкм 6. Звукоизоляция 7. Существующая ж/б плита - 5 мм	-	48,22	-	-	-	-	48,22
212, 213, 226, 227, 234, 236, 318, 318, 321, 325, 335, 343, 426, 421, 418, 411, 414	Tun 9		1. Кварц-виниловая плитка, цвет "серый бетон с отпечатками" (500x500x2,55 мм), тип укладки: "зиз-заг" - 2,55 мм 2. Нивелирующая масса - 10 мм 3. Армированная цементно-песчаная стяжка М150, армированная сеткой #5BrIII шаг 100x100, 1800 кг/м3 -50 мм 4. Засыпка керамзитовым гравием (фракции 20-40 мм) по ГОСТ 32497-2013 против цементным молочком, марки П50-100 или звукоизоляционная плита Rockwool ФЛОР БАТТС на клею -5-170 мм 5. Пленка полиэтиленовая 200 мкм 6. Звукоизоляция 7. Существующая ж/б плита - 5 мм	-	-	216,80	97,80	87,70		402,30
	Tun 9		1. Кварц-виниловая плитка, цвет "лиловый бетон" (500x500x2,55 мм), тип укладки: "зиз-заг" - 2,55 мм 2. Нивелирующая масса - 10 мм 3. Армированная цементно-песчаная стяжка М150, армированная сеткой #5BrIII шаг 100x100, 1800 кг/м3 -50 мм 4. Засыпка керамзитовым гравием (фракции 20-40 мм) по ГОСТ 32497-2013 против цементным молочком, марки П50-100 или звукоизоляционная плита Rockwool ФЛОР БАТТС на клею -5-170 мм 5. Пленка полиэтиленовая 200 мкм 6. Звукоизоляция 7. Существующая ж/б плита - 5 мм	-	-	216,80	97,80	87,70		402,30
104, 246, 413	Tun 10		1. Кварц-виниловая плитка, цвет "белый дуб" (1000x200x2,55 мм), раскладка со сдвигом на 1/2 - 2,55 мм 2. Нивелирующая масса - 10 мм 3. Армированная цементно-песчаная стяжка М150, армированная сеткой #5BrIII шаг 100x100, 1800 кг/м3 -50 мм 4. Засыпка керамзитовым гравием (фракции 20-40 мм) по ГОСТ 32497-2013 против цементным молочком, марки П50-100 или звукоизоляционная плита Rockwool ФЛОР БАТТС на клею -145-165 мм 5. Звукоизоляция 6. Существующая ж/б плита - 5 мм	-	25,52	19,20	-	16,43	-	61,15
	Tun 10		1. Кварц-виниловая плитка, цвет "натуральный бетон" (500x500x2,55 мм) -2,55 мм 2. Нивелирующая масса -10 мм 3. Армированная цементно-песчаная стяжка М150, армированная сеткой #5BrIII шаг 100x100, 1800 кг/м3 -50 мм 4. Засыпка керамзитовым гравием (фракции 20-40 мм) по ГОСТ 32497-2013 против цементным молочком, марки П50-100 или звукоизоляционная плита Rockwool ФЛОР БАТТС на клею -22-170 мм 5. Пленка полиэтиленовая 200 мкм 6. Звукоизоляция 7. Существующая ж/б плита -5 мм	-	448,59	1293,40	1051,56	885,19	-	3678,74
127, 128, 129, 117, 115, 114, 124, 123, 122, 133, 141, 142, 155, 162, 165, 228, 202, 205, 206, 207, 211, 216, 217, 218, 219, 220, 222, 223, 224, 225, 228, 230, 271, 232, 233, 243, 244, 245, 302, 305, 306, 307, 311, 312, 313, 315, 320, 324, 326, 327, 328, 330, 332, 333, 345, 346, 347, 348, 402, 405, 406, 407, 412, 413, 415, 419, 420, 422, 424, 425	Tun 11		1. Кварц-виниловая плитка, цвет "серый бетон с отпечатками" (500x500x2,55 мм), тип укладки: "зиз-заг" - 2,55 мм 2. Нивелирующая масса - 10 мм 3. Армированная цементно-песчаная стяжка М150, армированная сеткой #5BrIII шаг 100x100, 1800 кг/м3 -50 мм 4. Засыпка керамзитовым гравием (фракции 20-40 мм) по ГОСТ 32497-2013 против цементным молочком, марки П50-100 или звукоизоляционная плита Rockwool ФЛОР БАТТС на клею -5-170 мм 5. Пленка полиэтиленовая 200 мкм 6. Звукоизоляция 7. Существующая ж/б плита - 5 мм	-	448,59	1293,40	1051,56	885,19	-	3678,74
167, 331	Tun 12		1. Паркетная доска Парета дерева: дуб (2266x188x14 мм) 2. Фанера ФК 2 слоя (1525x125x12 мм) - 30 мм 3. Амортизирующий слой - профессиональные каучуковые амортизаторы "СПОРТ" на основе литой резины - 19 мм 4. Армированная цементно-песчаная стяжка М150, армированная сеткой #5BrIII шаг 100x100, 1800 кг/м3 -50 мм 5. Засыпка керамзитовым гравием (фракции 20-40 мм) по ГОСТ 32497-2013 против цементным молочком, марки П50-100 или звукоизоляционная плита Rockwool ФЛОР БАТТС на клею -125-140 мм 6. Пленка полиэтиленовая 200 мкм 7. Звукоизоляция 8. Существующая ж/б плита -5 мм	-	271,90	-	126,25	-	-	398,15
235, 341	Tun 13		1. Кадровое покрытие -5 мм 2. Нивелирующая масса -10 мм 3. Армированная цементно-песчаная стяжка М150, армированная сеткой #5BrIII шаг 100x100, 1800 кг/м3 -50 мм 4. Засыпка керамзитовым гравием (фракции 20-40 мм) по ГОСТ 32497-2013 против цементным молочком, марки П50-100 или звукоизоляционная плита Rockwool ФЛОР БАТТС на клею -10-110 мм 5. Пленка полиэтиленовая 200 мкм 6. Звукоизоляция 7. Существующая ж/б плита -5 мм	-	-	44,56	71,90	-	-	116,46

						16-25/Г-П-АР.ВОР		
						Капитальный ремонт объекта "ГБОУ Школа № 429 "Соколиная гора", расположенного по адресу: г.Москва, ул. Соколиной горы 5-я, д.14		
Изм.	Кол.чл.	Лист	№ док.	Подпись	Дата			
Разраб.		Липовская			2026.09.09			
Объемно-планировочные и архитектурные решения						Студия	Лист	Листов
						П	16	
Сводная ведомость конструкций полов Сводная ведомость плитусов.						 АЗУРИТ		
Н. контр.	Губарева				2026.09.09			
ГИП	Неменов				2026.09.09			
						ФОРМАТ А1		

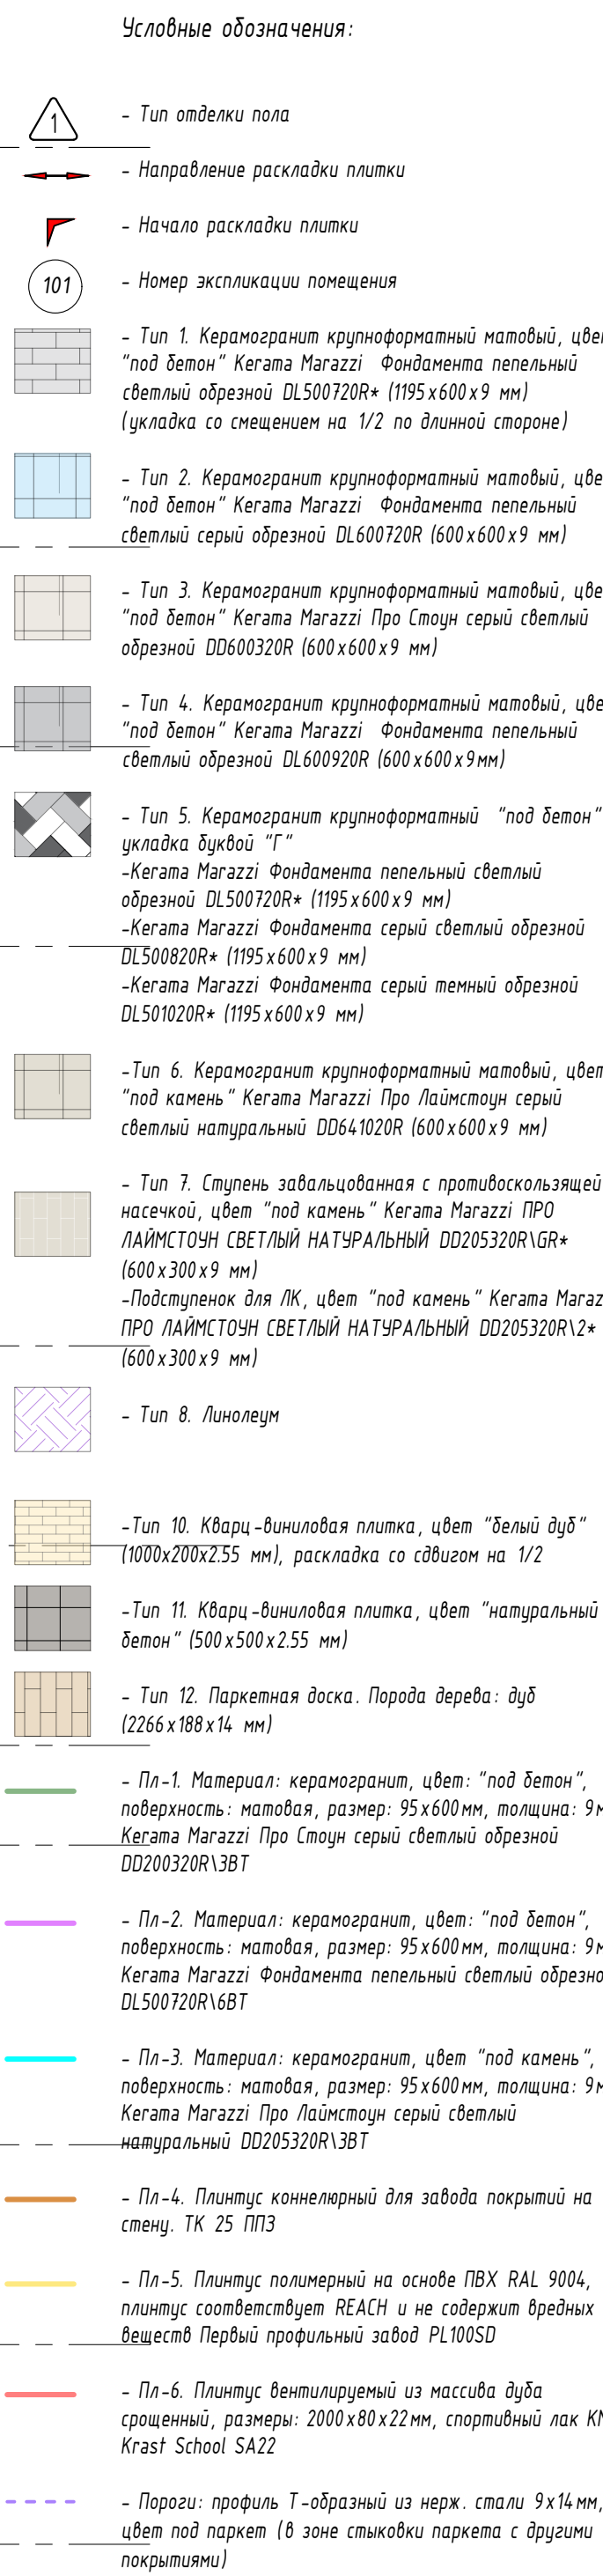

Номер помещения	Наименование	Площадь м2	Кол. помещений
101	Тамбур	35,02	
102	Коридор с рекреацией	271,54	
103	Санитар для МН	5,23	
104	Административный кабинет тип 1 (начальная школа)	25,91	
106	Санитар для девочек (начальная школа)	23,25	
107	Гардеробная для обучающихся (использов и старшая школа)	91,54	
108	Гардеробная для обучающихся (использов и старшая школа)	34,75	
109	Гардеробная для обучающихся (начальная школа)	16,62	
110	Лестничная клетка (ЛК)	24,50	
111	Коридор	71,54	
112	Санитар для мальчиков (начальная школа)	12,84	
113	Санитар для персонала	2,18	
114	Учебные кабинеты (начальная школа)	65,12	
115	Учебные кабинеты (начальная школа)	58,33	
117	Учебные кабинеты (начальная школа)	62,97	
118	ПМ	2,18	84
119	Санитар для девочек (начальная школа)	12,44	
120	Коридор с рекреацией (использов и старшая школа)	215,40	
122	Компьютерная (с диспетчерским пунктом)	93,03	
123	Гардеробная комната (для учителей)	9,86	
124	Помещение связи	9,47	84
125	Санитар для мальчиков (начальная школа)	21,23	
127	Учебные кабинеты (начальная школа)	57,26	
128	Учебные кабинеты (начальная школа)	53,71	
129	Учебные кабинеты (начальная школа)	58,81	
130	Коридор с рекреацией	117,57	
131	Лестничная клетка Тип И2	27,18	
132	Вестибюль	42,02	
133	Электрощитовая	16,24	83
Место для приготовления дезинфицирующих растворов и хранения уборочных инвентаря, предназначенных для помещений медицинских назначения			
134-1	Тупик медкабинета	7,36	84
135	Кабинет врача	27,00	
136	Процедурный (профилактический) кабинет	28,88	
137	Коридор	26,06	
138	Комната инструктора	12,03	
138-1	Санитар с душем	7,07	
139	ПМ	6,29	84
140	Санитар для персонала	3,77	
141	Помещение связи	11,87	83
142	Помещение для персонала	12,01	
142-1	Санитар для персонала	2,01	
142-2	Душевая	2,29	
143	ПМ	6,05	84
144	Помещение для временного хранения пищевых отходов	4,81	
145	Кладовая с вещами уборочной пары	6,92	84
146	Зеркальный шкаф	7,45	84
147	Коридор	28,66	
147-1	Помещение с холодильным оборудованием	26,18	83
148	Кладовая сухих продуктов	10,85	83
149	Дизельотопный шкаф	19,26	83
150	Горючий шкаф	35,15	83
151	Маточная для кухонной посуды	9,75	
152	Маточная для столовой посуды	34,18	
152-1	Предназначена	5,48	
153	Холодный шкаф	15,96	83
154	Обеденный зал	178,91	
155	Раздевальня для мальчиков	11,10	
156	Санитар для мальчиков	2,16	
157	Санитар для девочек	2,10	
158	Душевые для мальчиков	4,75	
159	Душевые для девочек	4,16	
160	Санитар для мальчиков	8,71	
161	Санитар для девочек	9,76	
162	Раздевальня для девочек	11,00	
163	Лестничная клетка (ЛК)	27,00	
164	Теплотехническое помещение	5,10	84
165	Сквиринка	21,35	83
166	ПМ	4,47	84
167	Циферблатный спортивный зал	270,82	
168	Лестничная клетка (ЛК)	25,50	
169	Коридор с рекреацией (использов и старшая школа)	281,24	
171	Тех. помещение	3,93	84
172	Лестничная клетка (ЛК)	21,00	
172-1	Тамбур	4,42	
173	Электрощитовая	16,36	83
Всего		2236,41	

					16-25/Г-П-АР ВОР		
					Капитальный ремонт объекта "БСОУ Школа № 429 "Светлая дзю", расположенного по адресу: г. Москва, ул. Сахаровский бу-ль-вар, д.14		
Имя	Фамилия	Адрес	№ док.	Подпись	Дата	Страница	Лист
Рязанов	Александр	Липовая		<i>[Подпись]</i>	2026.09.28	1	37
					Объемно-планировочные и архитектурные решения		
И. номер	Губернатор			<i>[Подпись]</i>	2026.09.28		
Гипс	Григорьев			<i>[Подпись]</i>	2026.09.28		
Листов всего 1-го этажа, М. 1100						 АЗУРИТ	