


Фрагмент плана подвала на отм. -2,850.
Укрытие. Маркировочный план

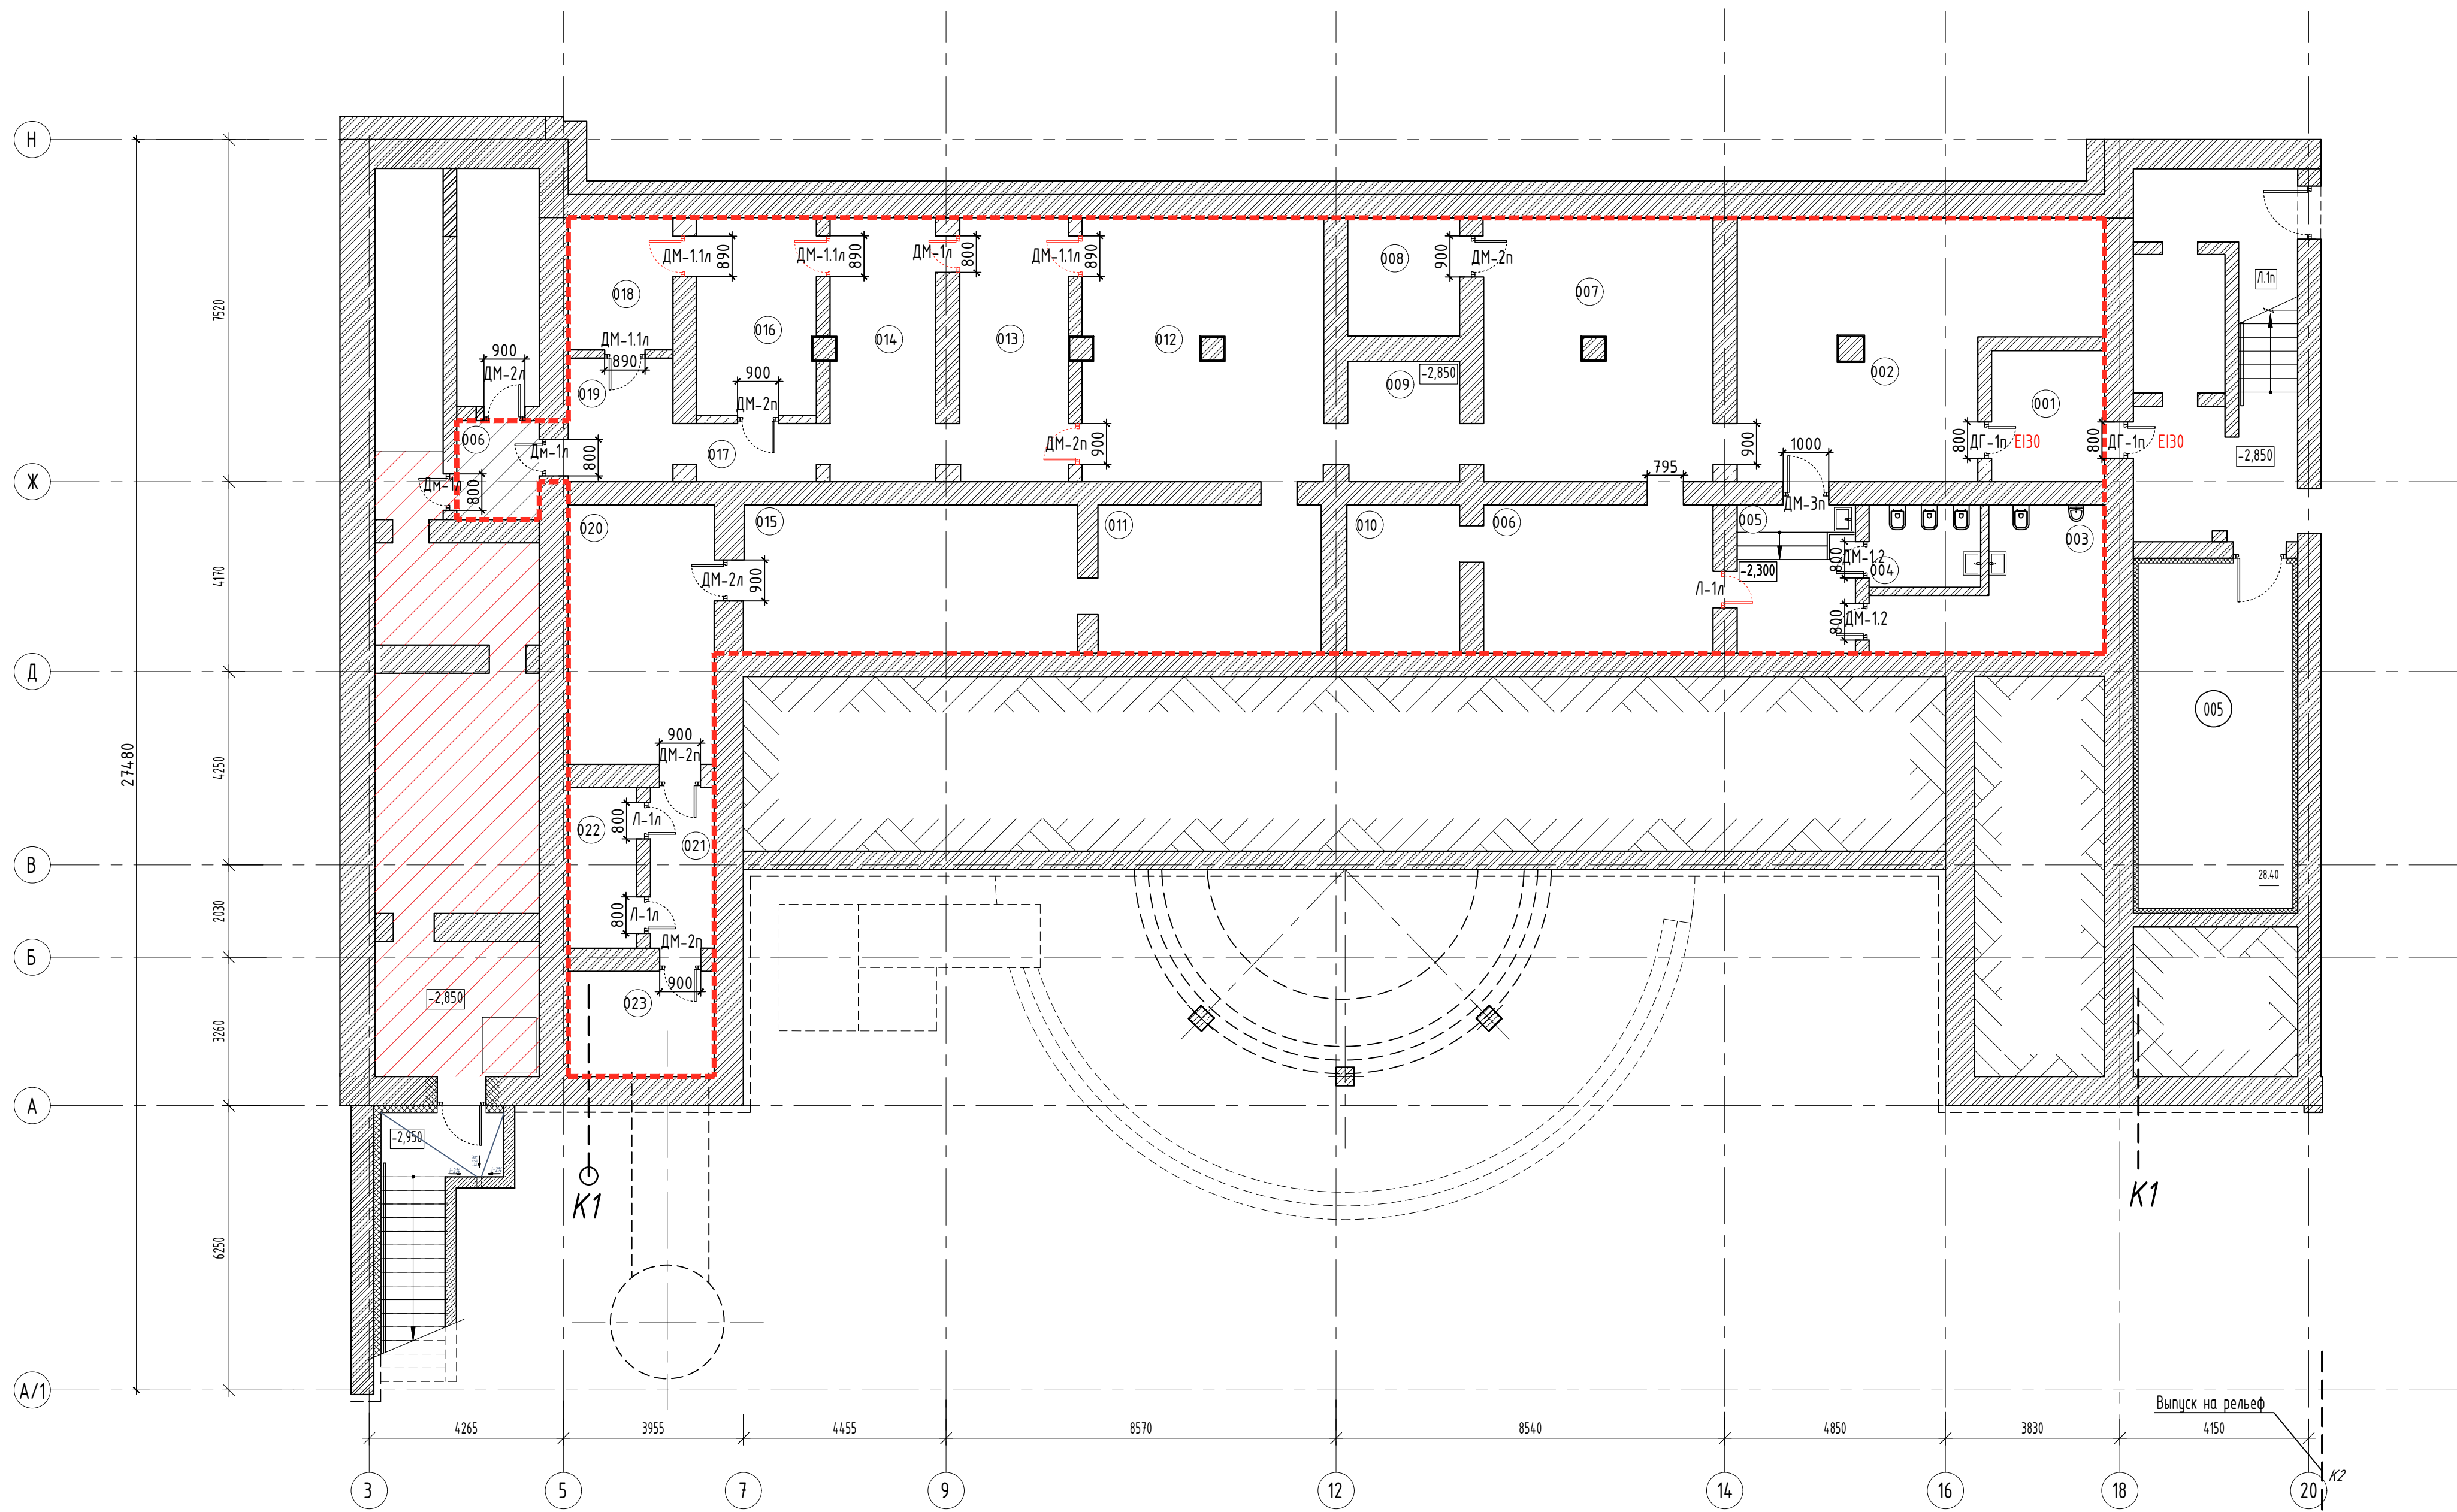

Номер помещения	Наименование	Площадь, м2	Кат. помещения
001	Помещение специальное	7.20	
002	Помещение специальное	38.50	
003	Санузел	10.70	
004	Санузел	5.20	
005	Коридор	8.50	
006	Помещение специальное	15.90	
007	Помещение специальное	26.70	
008	Помещение специальное	6.70	
009	Помещение специальное	7.20	
010	Помещение специальное	7.60	
011	Помещение специальное	15.90	
012	Помещение специальное	30.80	
013	Помещение специальное	12.80	
014	Помещение специальное	15.00	
015	Помещение специальное	24.00	
016	Помещение специальное	10.40	
017	Коридор	3.30	
018	Помещение специальное	7.90	
019	Коридор	5.80	
020	Помещение специальное	18.70	
021	Помещение специальное	4.90	
022	Помещение специальное	5.00	
023	Помещение специальное	7.50	
Всего		296.2	


УСЛОВНЫЕ ОБОЗНАЧЕНИЯ

- Существующие стены из полнотелого керамического кирпича
- Заменяемые монолитные Ж/Б стены
- Заменяемые перегородки из полнотелого кирпича 120мм, оштукатуренная
- Номер помещения по экспликации
- Маркировка огнестойкости заменяемых дверей
- Отметка уровня пола этажа
- Пути эвакуации
- Марки типов дверей


ПРИМЕЧАНИЕ:
1. За условную отметку ±0.000 принята отметка уровня чистого пола 1 этажа.

Спецификация заполнения внутренних проемов

№	Марка	Наименование изделия	Размер проема, мм		Кол-во, шт.	Площадь, м2	Примечание
			L	H			
1	ДГ-1н	Дверь одностворчатая глухая противопожарная	800	2100	2	2.3	Дверь стальная противопожарная, с механическим замком, с возможностью запирания изнутри помещения
3	ДМ-1л	Дверь одностворчатая глухая металлическая	800	2100	3	3	Дверь стальная
4	ДМ-1.1л		890	2100	4	4	
5	ДМ-1.2		800	2100	2	2	
6	ДМ-2л		900	2100	5	5	
6	ДМ-2л		900	2100	2	2	
7	ДМ-3л		1000	2100	1	1	
8	Л-1л	Ляк металлический	800	800	3	3	
Всего					22		

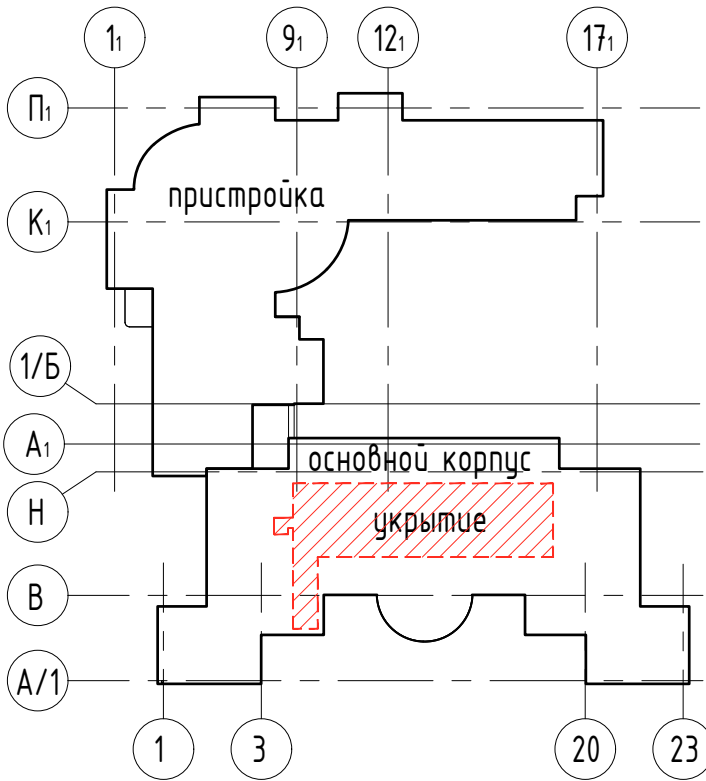

						16-25/Г-П-АР			
						Капитальный ремонт общеобразовательного учреждения (ГБОУ "Школа №429"), расположенного по адресу: г.Москва, 5-ая ул.Соколиной Горы, д.14			
Изм.	Кол.уч.	Лист	№*док	Подпись	Дата		Стация	Лист	Листов
Разраб.		Липовская			2025.08	Объемно-планировочные и архитектурные решения	П	70.1	
Н. контр.		Губарева Е.В.			2025.08	Фрагмент плана подвала на отм. -2,850 Укрытие. Маркировочный план дверей		АЗУРИТ	
ГИП		Неменов		2025.08					

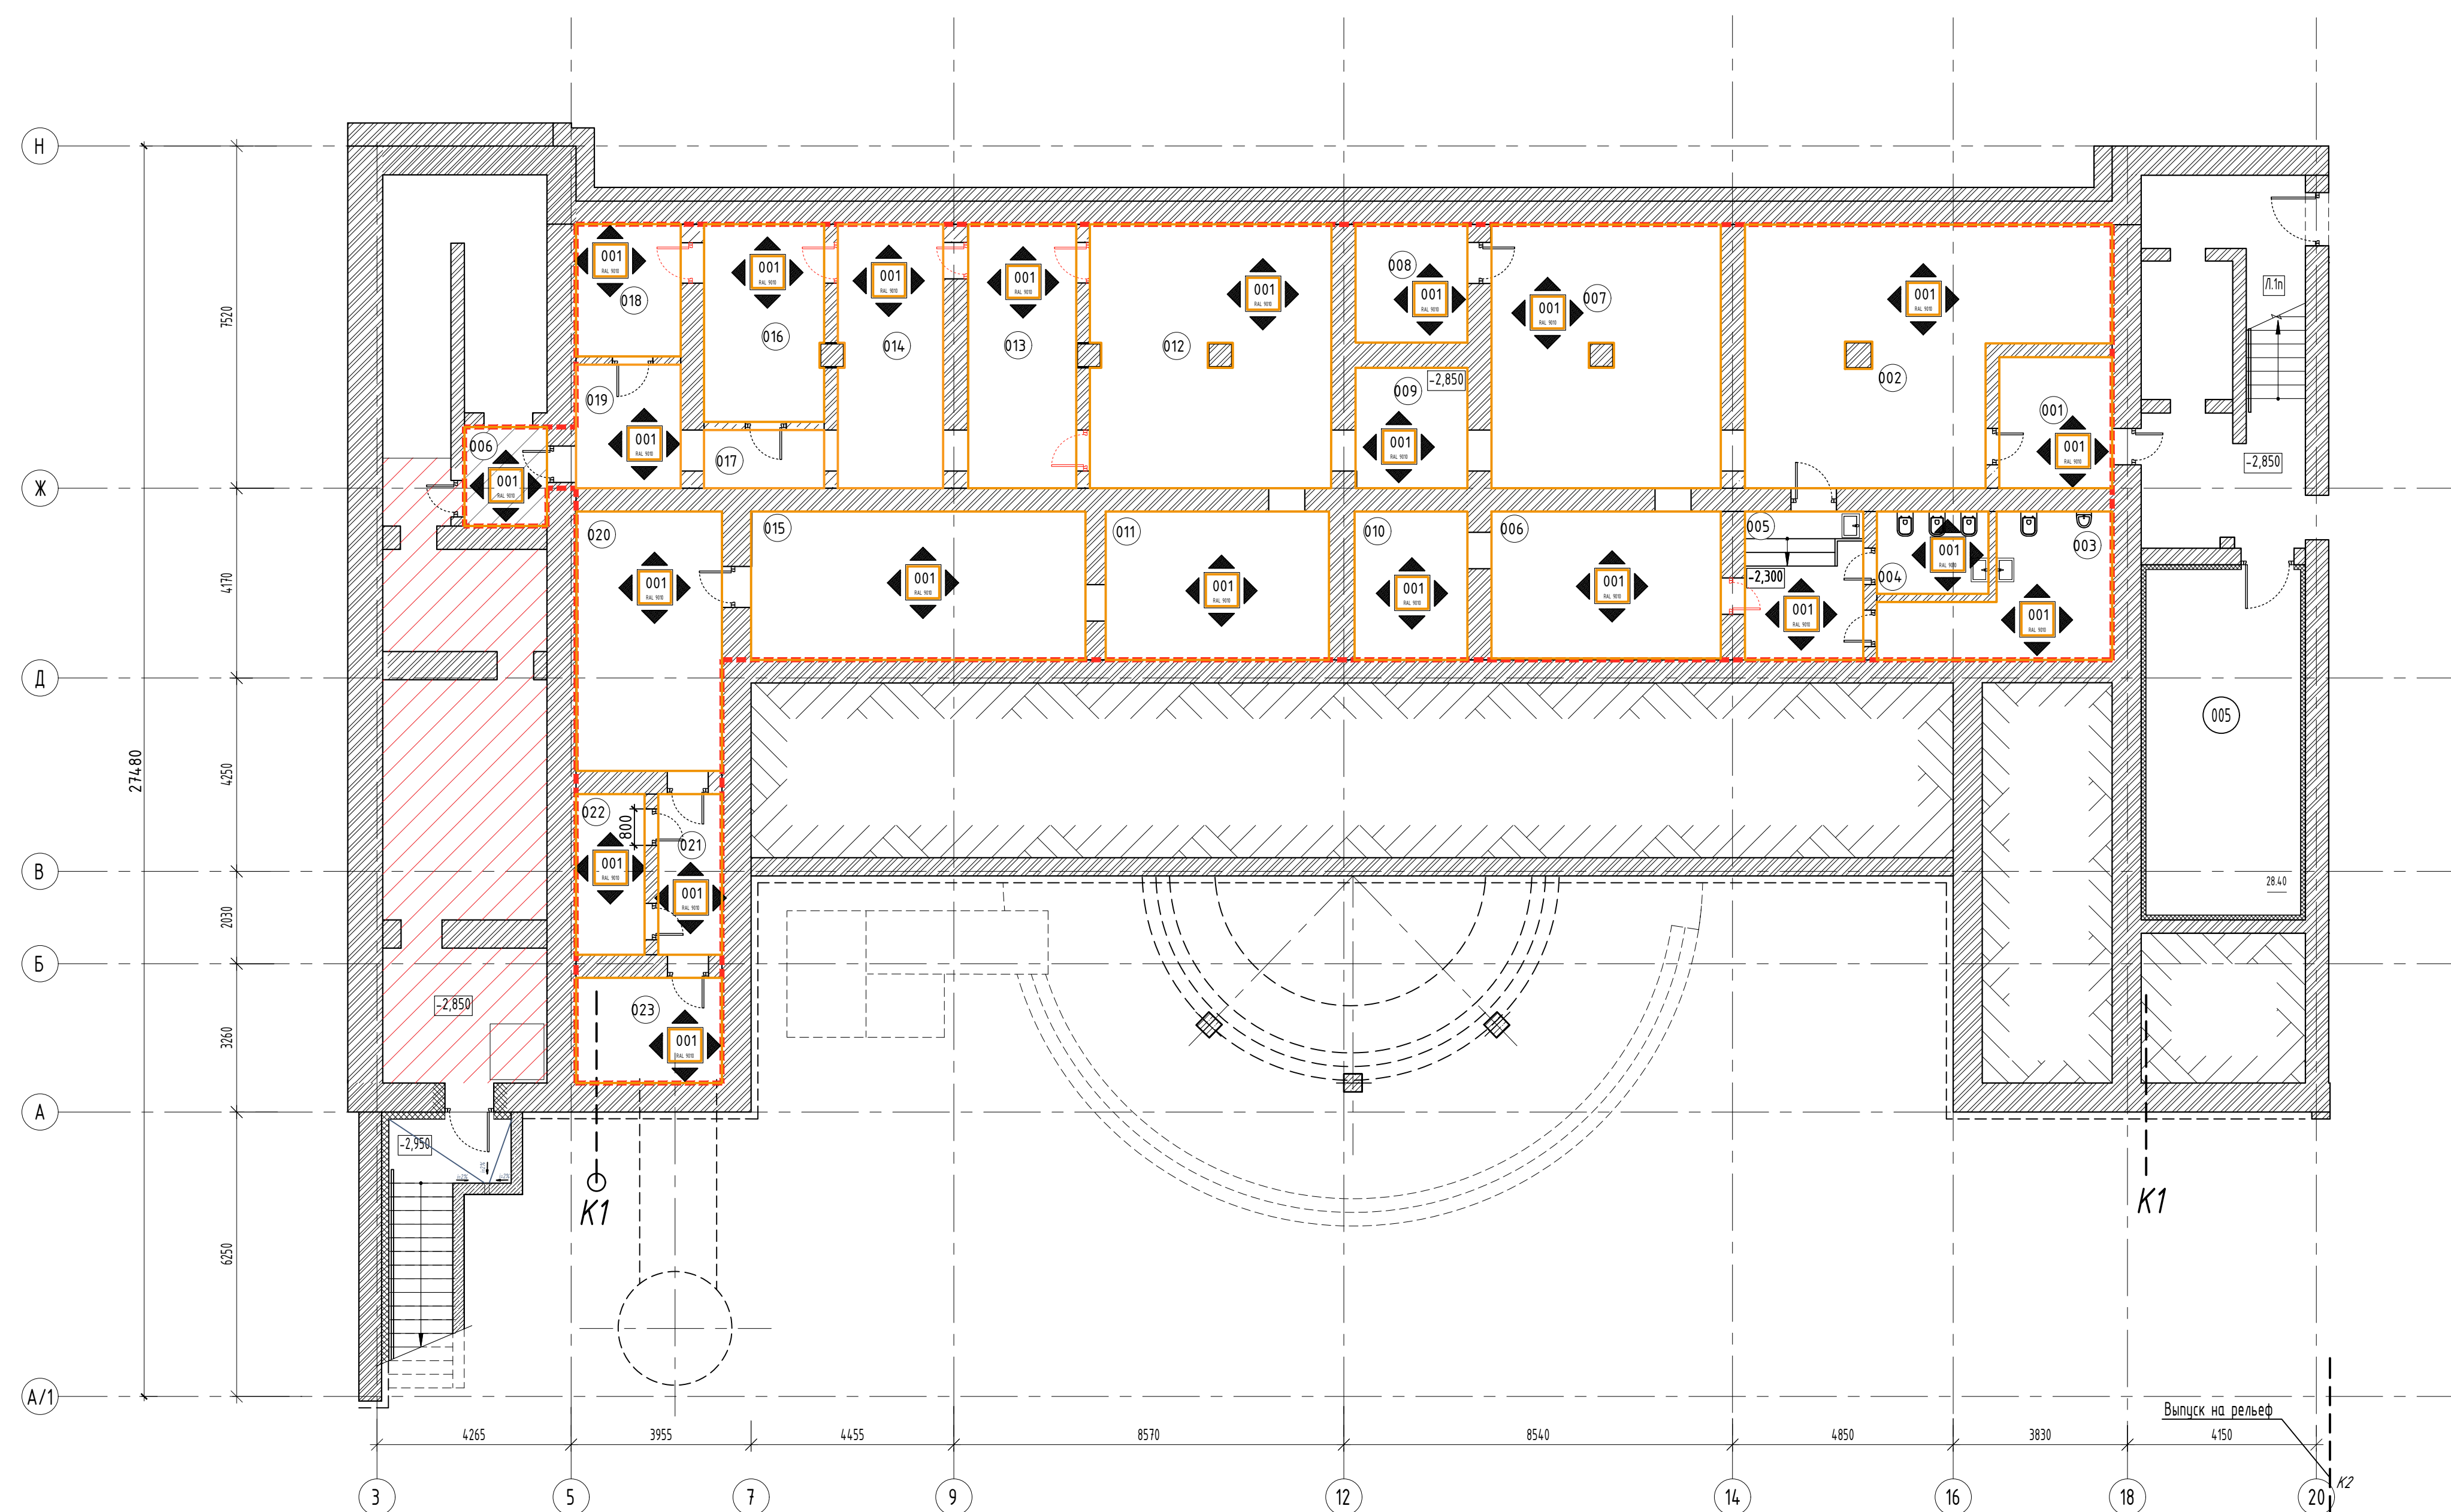



Номер помещения	Наименование	Площадь м2	Кат. помещения
001	Помещение специальное	7.20	
002	Помещение специальное	38.50	
003	Санузел	10.70	
004	Санузел	5.20	
005	Коридор	8.50	
006	Помещение специальное	15.90	
007	Помещение специальное	26.70	
008	Помещение специальное	6.70	
009	Помещение специальное	7.20	
010	Помещение специальное	7.60	
011	Помещение специальное	15.90	
012	Помещение специальное	30.80	
013	Помещение специальное	12.80	
014	Помещение специальное	15.00	
015	Помещение специальное	24.00	
016	Помещение специальное	10.40	
017	Коридор	3.30	
018	Помещение специальное	7.90	
019	Коридор	5.80	
020	Помещение специальное	18.70	
021	Помещение специальное	4.90	
022	Помещение специальное	5.00	
023	Помещение специальное	7.50	
	Всего	296.2	

Условные обозначения:


-  - Граница укрытия
-  - Номер помещения по экспликаци
-  - Тип 001. Простая окраска стен без подготовки и выравнивания поверхности

1. За условную отметку ± 0.000 принята отметка уровня чистого пола 1 этажа.

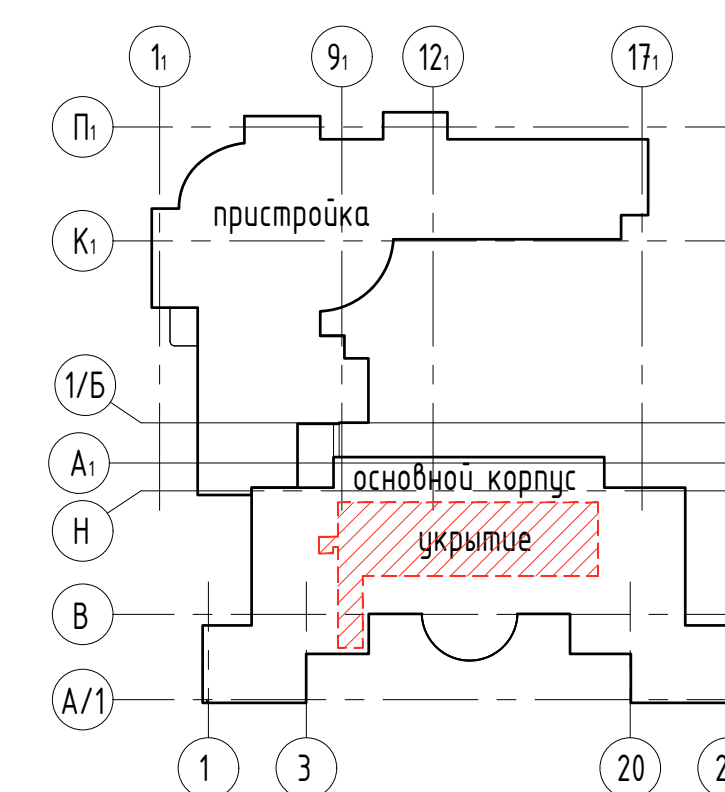

 						№-25/Г.-П.-АР					
						Капитальный ремонт общеобразовательного учреждения «ГБОУ "Школа №429", расположенного по адресу : г Москва, 5-ая ул Соколкиной Горы, д.14					
Изм	Кол.чл	Лист	N° док	Подпись	Дата	Объемно -планировочные и архитектурные решения			Стадия	Лист	Листов
Разраб.		Липавская			2026.08				П	70.2	
Н. контр.		Губарева Е.В.			2026.08	Фрагмент плана подвала на отн. -2,850 Высота, Отделка стен:				АЗУРИТ	
ГИП		Неменов		2026.08							

Фрагмент плана подвала на отм. -2,850.
Укрытие. Отделка пола

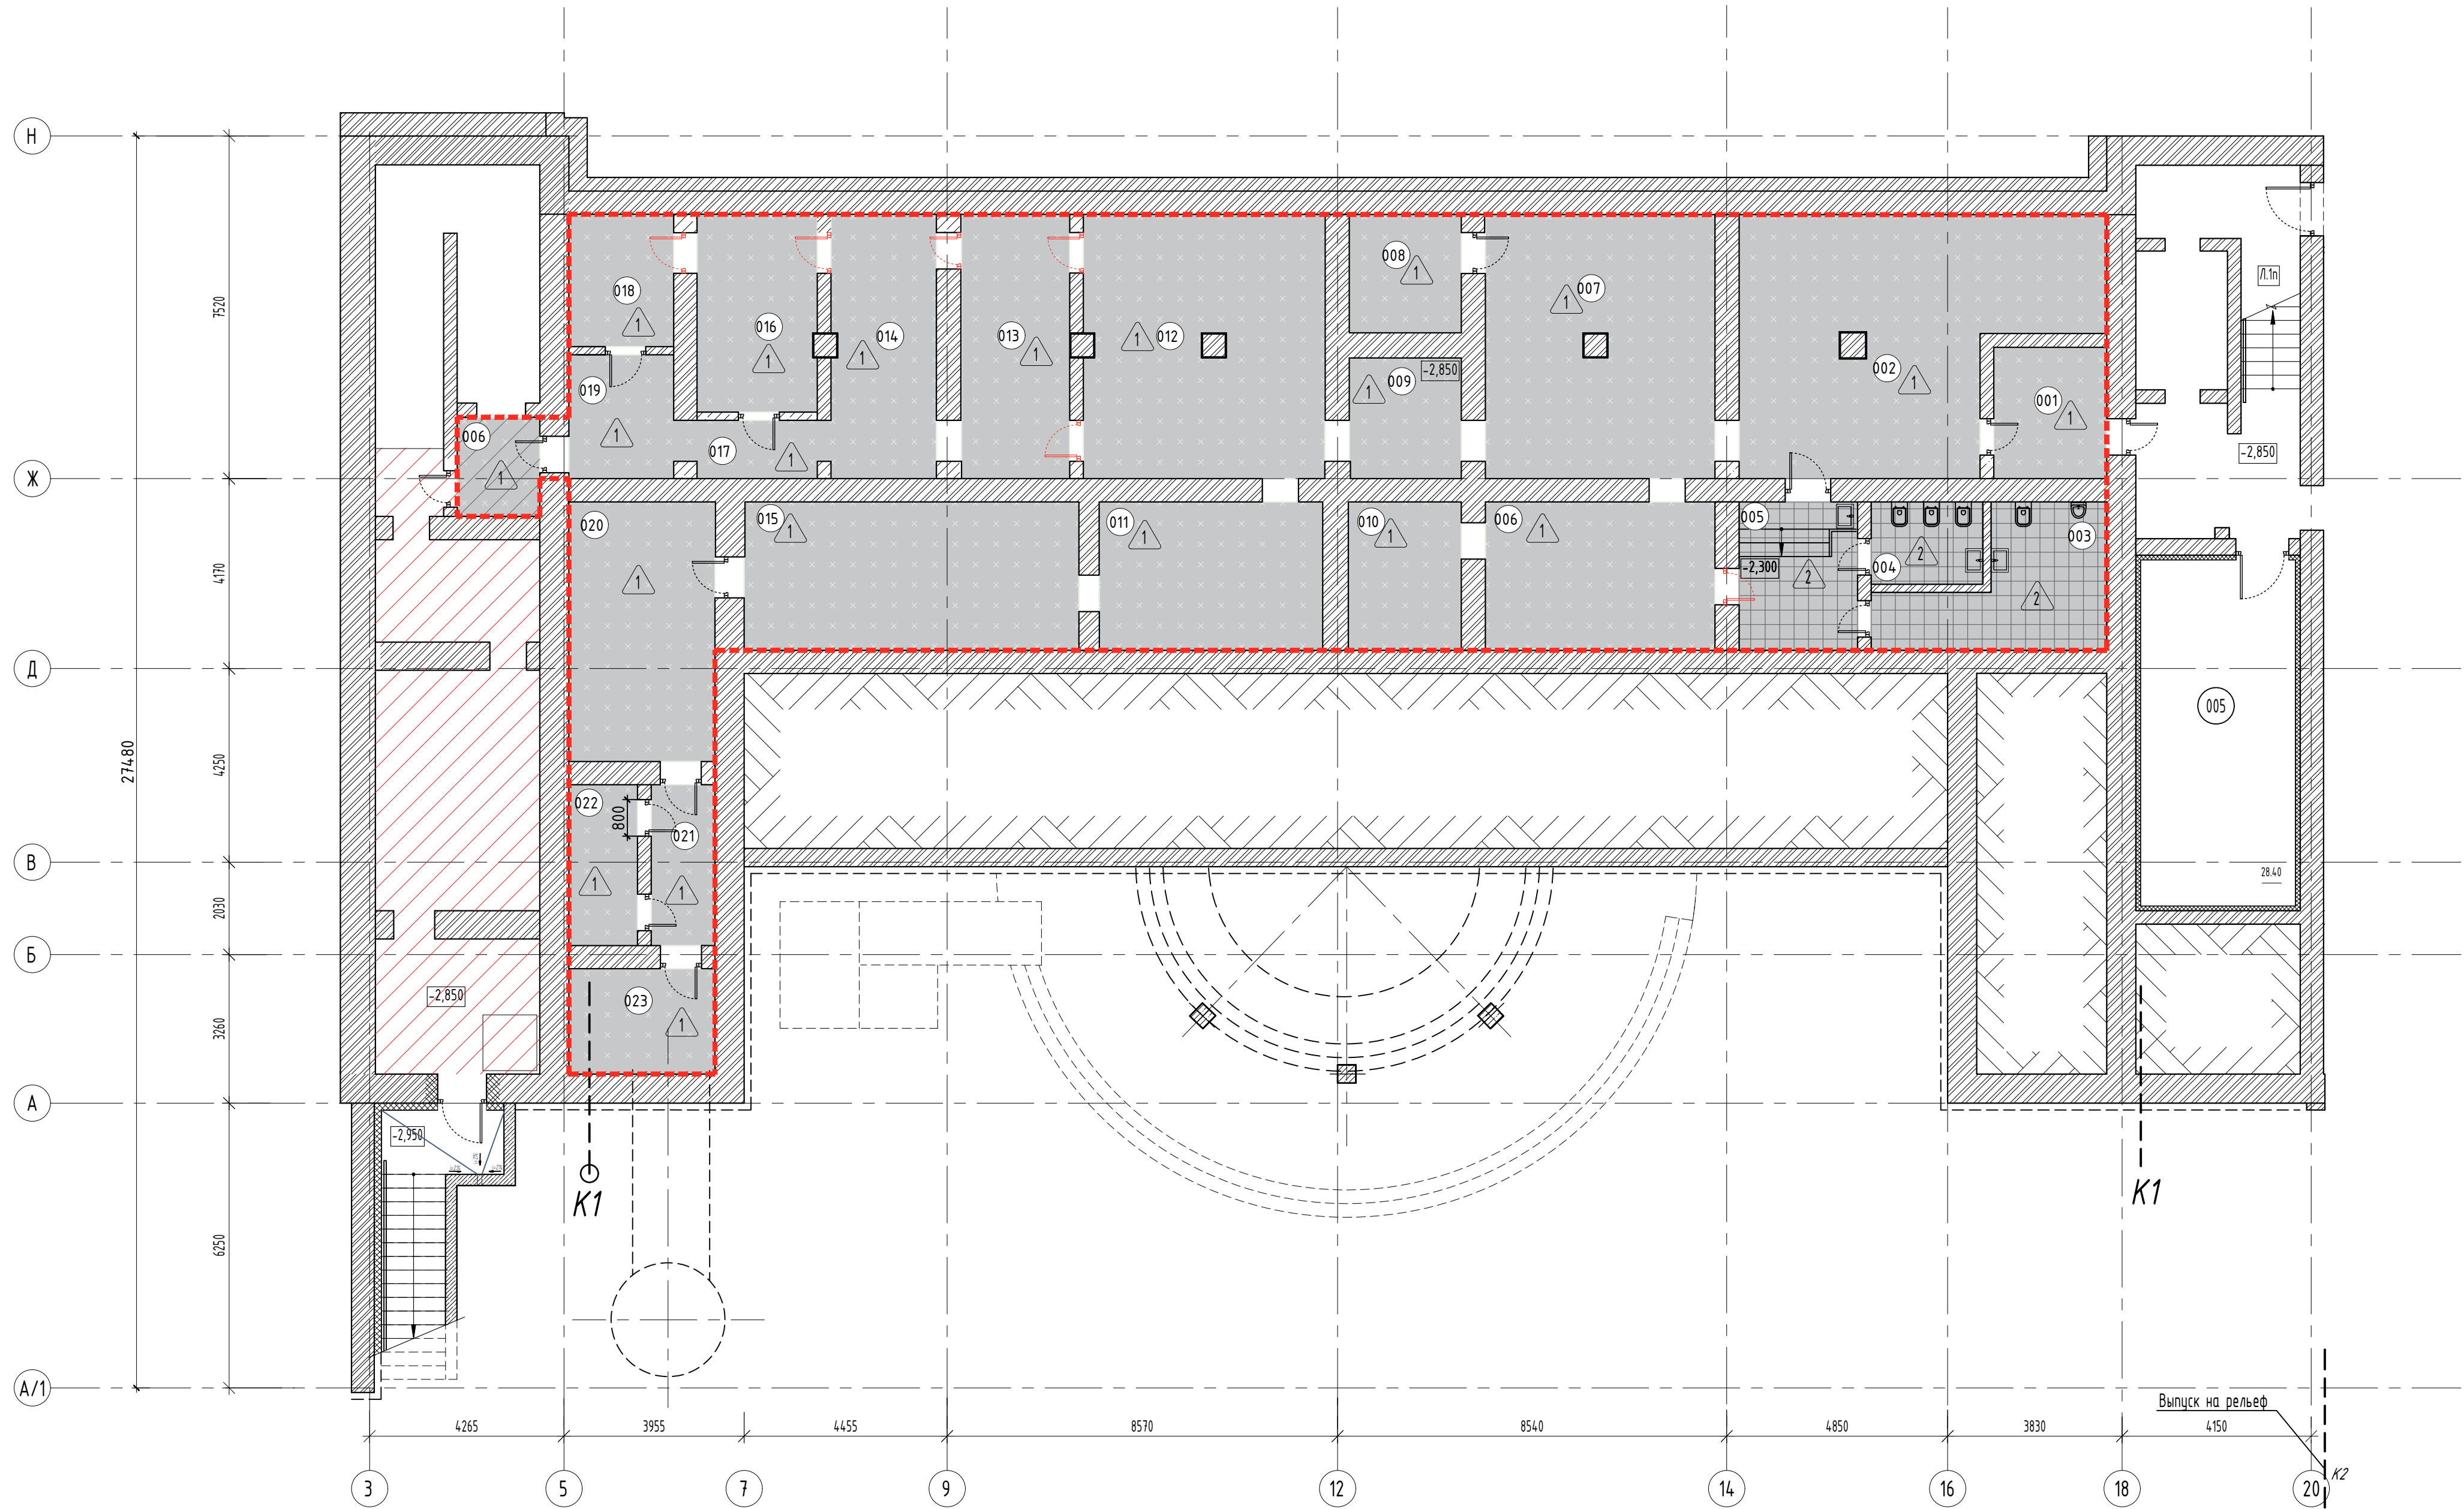


Номер помещения	Наименование	Площадь м2	Кат. помещения
001	Помещение специальное	7.20	
002	Помещение специальное	38.50	
003	Санузел	10.70	
004	Санузел	5.20	
005	Коридор	8.50	
006	Помещение специальное	15.90	
007	Помещение специальное	26.70	
008	Помещение специальное	6.70	
009	Помещение специальное	7.20	
010	Помещение специальное	7.60	
011	Помещение специальное	15.90	
012	Помещение специальное	30.80	
013	Помещение специальное	12.80	
014	Помещение специальное	15.00	
015	Помещение специальное	24.00	
016	Помещение специальное	10.40	
017	Коридор	3.30	
018	Помещение специальное	7.90	
019	Коридор	5.80	
020	Помещение специальное	18.70	
021	Помещение специальное	4.90	
022	Помещение специальное	5.00	
023	Помещение специальное	7.50	
Всего		296.2	

Условные обозначения:


- Граница укрытия
- Номер экспликации помещений
- Марка типа отделки пола
- Тип 1. Грунтование
- Тип 2. Керамогранит крупноформатный, цвет "под бетон" Кегата Magazzi Фундамент пепельный светлый обрезной DD600900R* (600x600x9 мм)

ПРИМЕЧАНИЕ:
1. За условную отметку ±0.000 принята отметка уровня чистого пола 1 этажа.

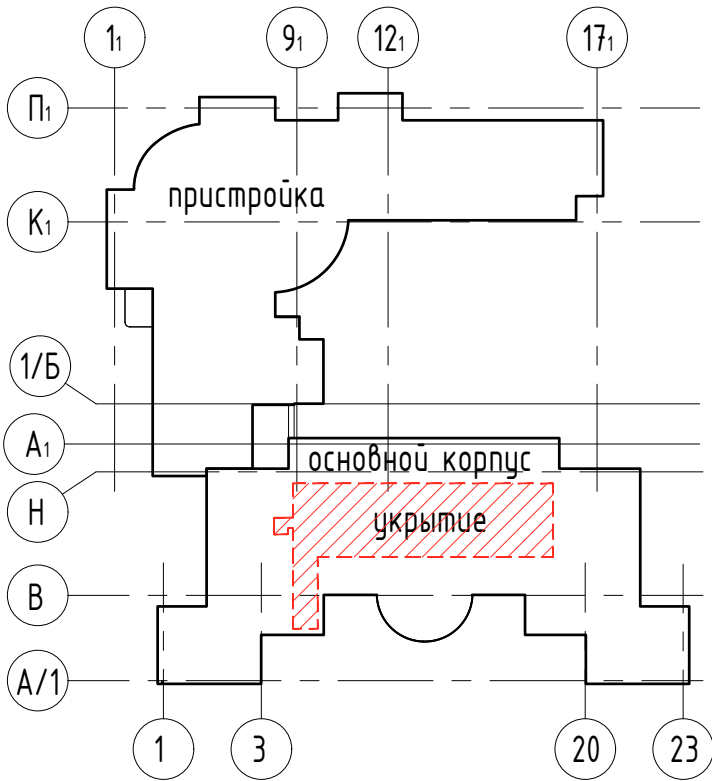

						16-25/Г-П-АР		
						Капитальный ремонт общеобразовательного учреждения (ГБОУ "Школа №429"), расположенного по адресу: г.Москва, 5-ая ул.Соколиной Горы, д.14		
						Объемно-планировочные и архитектурные решения		
						Стация	Лист	Листов
						П	70.3	
						Фрагмент плана подвала на отм. -2,850 Укрытие. Отделка пола		
						АЗУРИТ		
						ФОРМАТ 01		

Создано	
Внесены изменения	
Дата и дата	
Имя, И.И.И.	

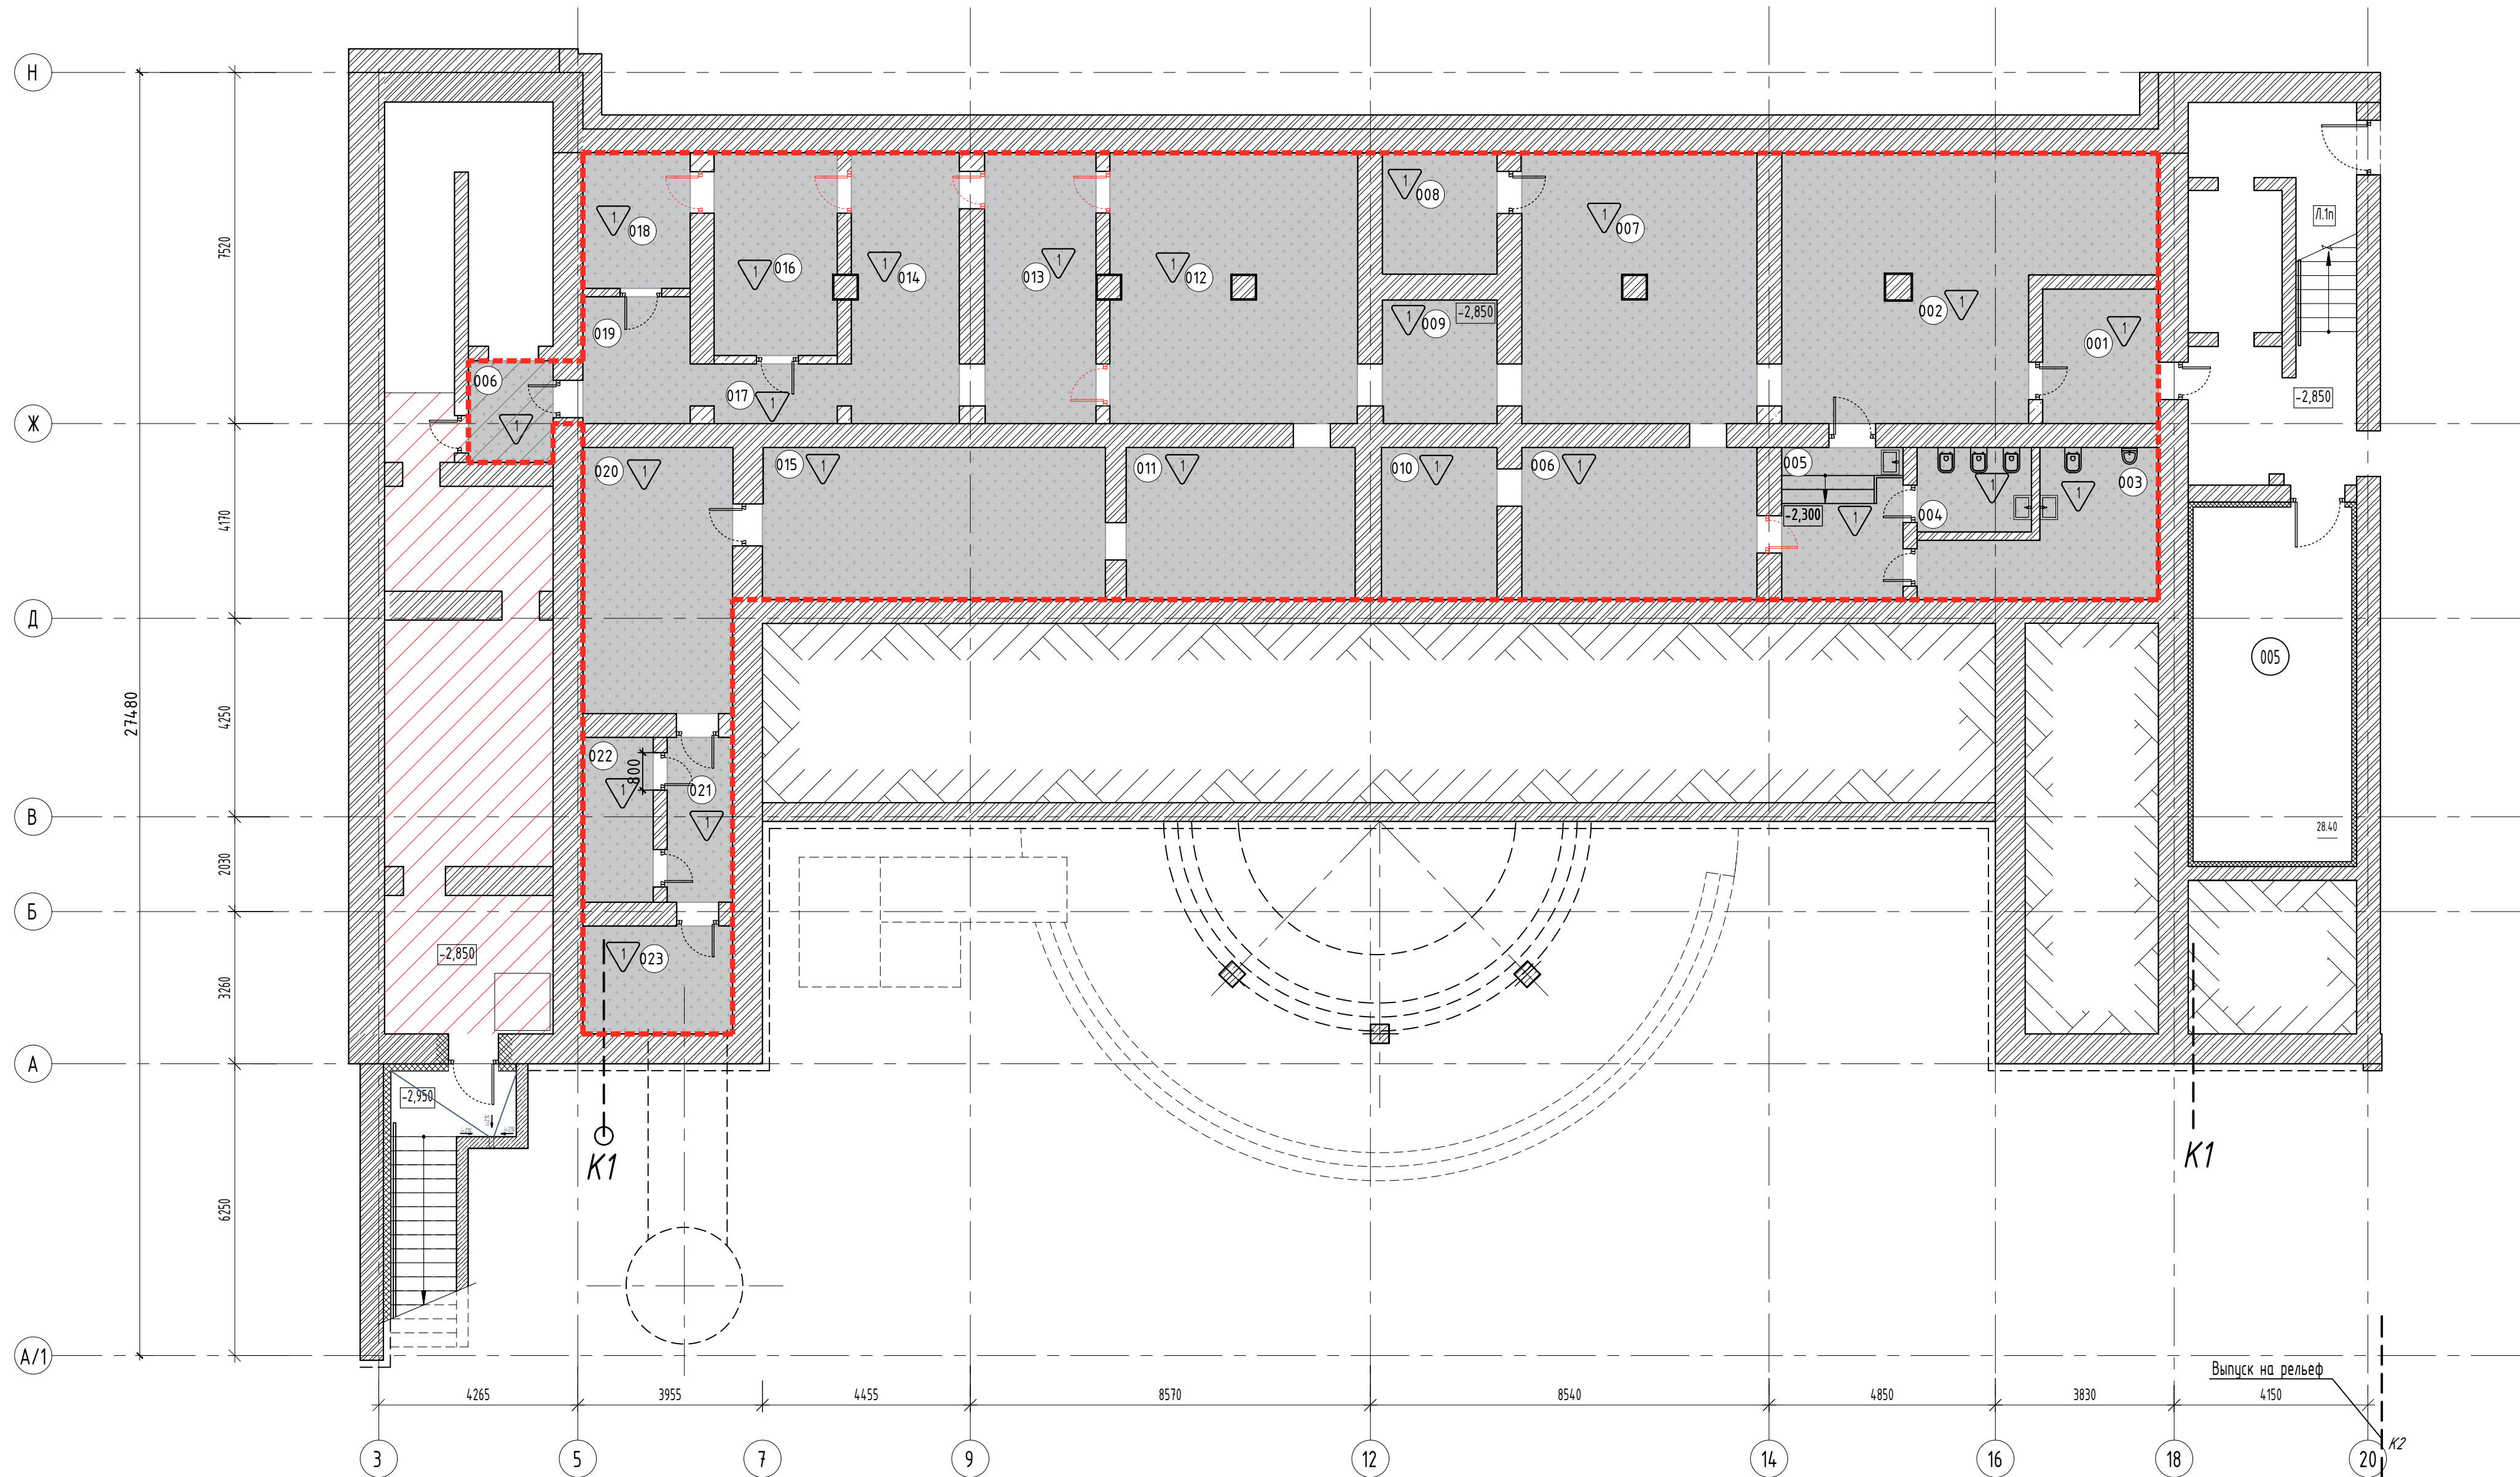

Номер поме- щения	Наименование	Площадь м2	Кат. поме- щени- я
001	Помещение специальное	7.20	
002	Помещение специальное	38.50	
003	Санузел	10.70	
004	Санузел	5.20	
005	Коридор	8.50	
006	Помещение специальное	15.90	
007	Помещение специальное	26.70	
008	Помещение специальное	6.70	
009	Помещение специальное	7.20	
010	Помещение специальное	7.60	
011	Помещение специальное	15.90	
012	Помещение специальное	30.80	
013	Помещение специальное	12.80	
014	Помещение специальное	15.00	
015	Помещение специальное	24.00	
016	Помещение специальное	10.40	
017	Коридор	3.30	
018	Помещение специальное	7.90	
019	Коридор	5.80	
020	Помещение специальное	18.70	
021	Помещение специальное	4.90	
022	Помещение специальное	5.00	
023	Помещение специальное	7.50	
Всего		296.2	

Ведомость отделки помещений укрытия


Номер поме- щения	Наименование	Потолок	Площадь м2	Пол	Площадь м2	Стены	Площадь м2	
001	Помещение специальное	1. Расчистка 2. Простая окраска в цвет RAL 9003	7.20	1. Расчистка 2. Грунтовка	7.20	1. Расчистка 2. Простая окраска в цвет RAL 9010	27.54	
002	Помещение специальное		38.50		38.50		77.01	
003	Санузел		10.70		10.70		43.10	
004	Санузел		5.20		5.20		21.93	
005	Коридор		8.50		8.50		30.09	
006	Помещение специальное		15.90		15.90		42.33	
007	Помещение специальное		26.70		26.70		55.40	
008	Помещение специальное		6.70		6.70		26.10	
009	Помещение специальное		7.20		7.20		26.27	
010	Помещение специальное		7.60		7.60		29.33	
011	Помещение специальное		15.90		15.90		41.82	
012	Помещение специальное		30.80		30.80		64.26	
013	Помещение специальное		12.80		12.80		41.82	
014	Помещение специальное		15.00		15.00		42.33	
015	Помещение специальное		24.00		24.00		54.40	
016	Помещение специальное		10.40		10.40		36.21	
017	Коридор		3.30		3.30		20.20	
018	Помещение специальное		7.90		7.90		26.78	
019	Коридор		5.80		5.80		25.76	
020	Помещение специальное		18.70		18.70		45.39	
021	Помещение специальное		4.90		4.90		25.25	
022	Помещение специальное		5.00		5.00		25.76	
023	Помещение специальное		7.50		7.50		28.31	
	Всего				296.2			296.2

*Предусмотреть обработку 10% сущ. стен и потолков укрытия противогрибковым средством

Условные обозначения:

- - - - - Граница укрытия
- 101 - Номер экспликации помещений
- ▽ - Марка типа отделки потолка
- - Тип 1. Простая окраска в цвет RAL 9003

ПРИМЕЧАНИЕ:
1. За условную отметку ±0.000 принята отметка уровня чистого пола 1 этажа.

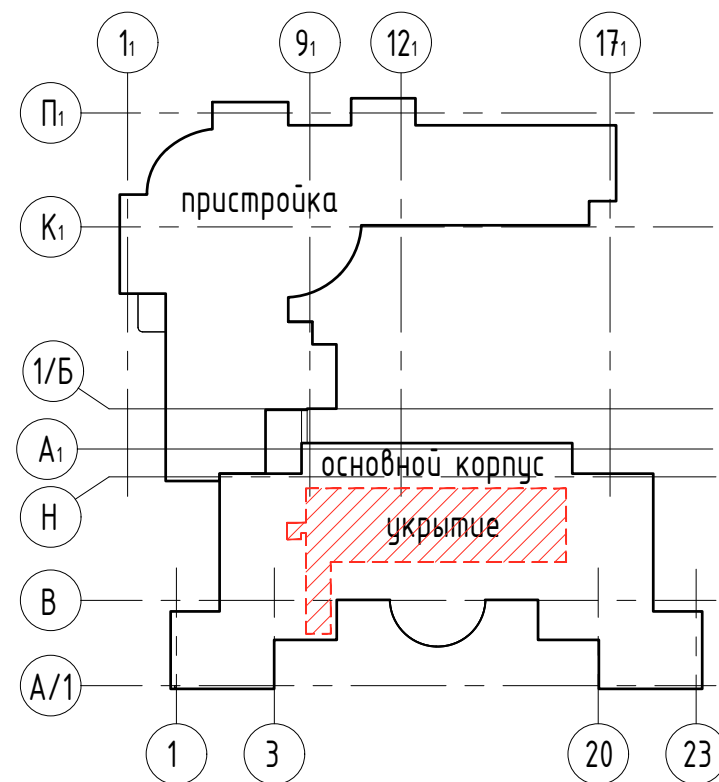

16-25/Г-П-АР					
Капитальный ремонт общеобразовательного учреждения (ГБОУ "Школа №429"), расположенного по адресу: г.Москва, 5-ая ул.Соколиной Горы, д.14					
Объемно-планировочные и архитектурные решения				Стация	Лист
				П	70.4
Фрагмент плана подвала на отм. -2,850 Укрытие. Отделка потолка. Ведомость отделки					
АЗУРИТ					
ФОРМАТ 01					