


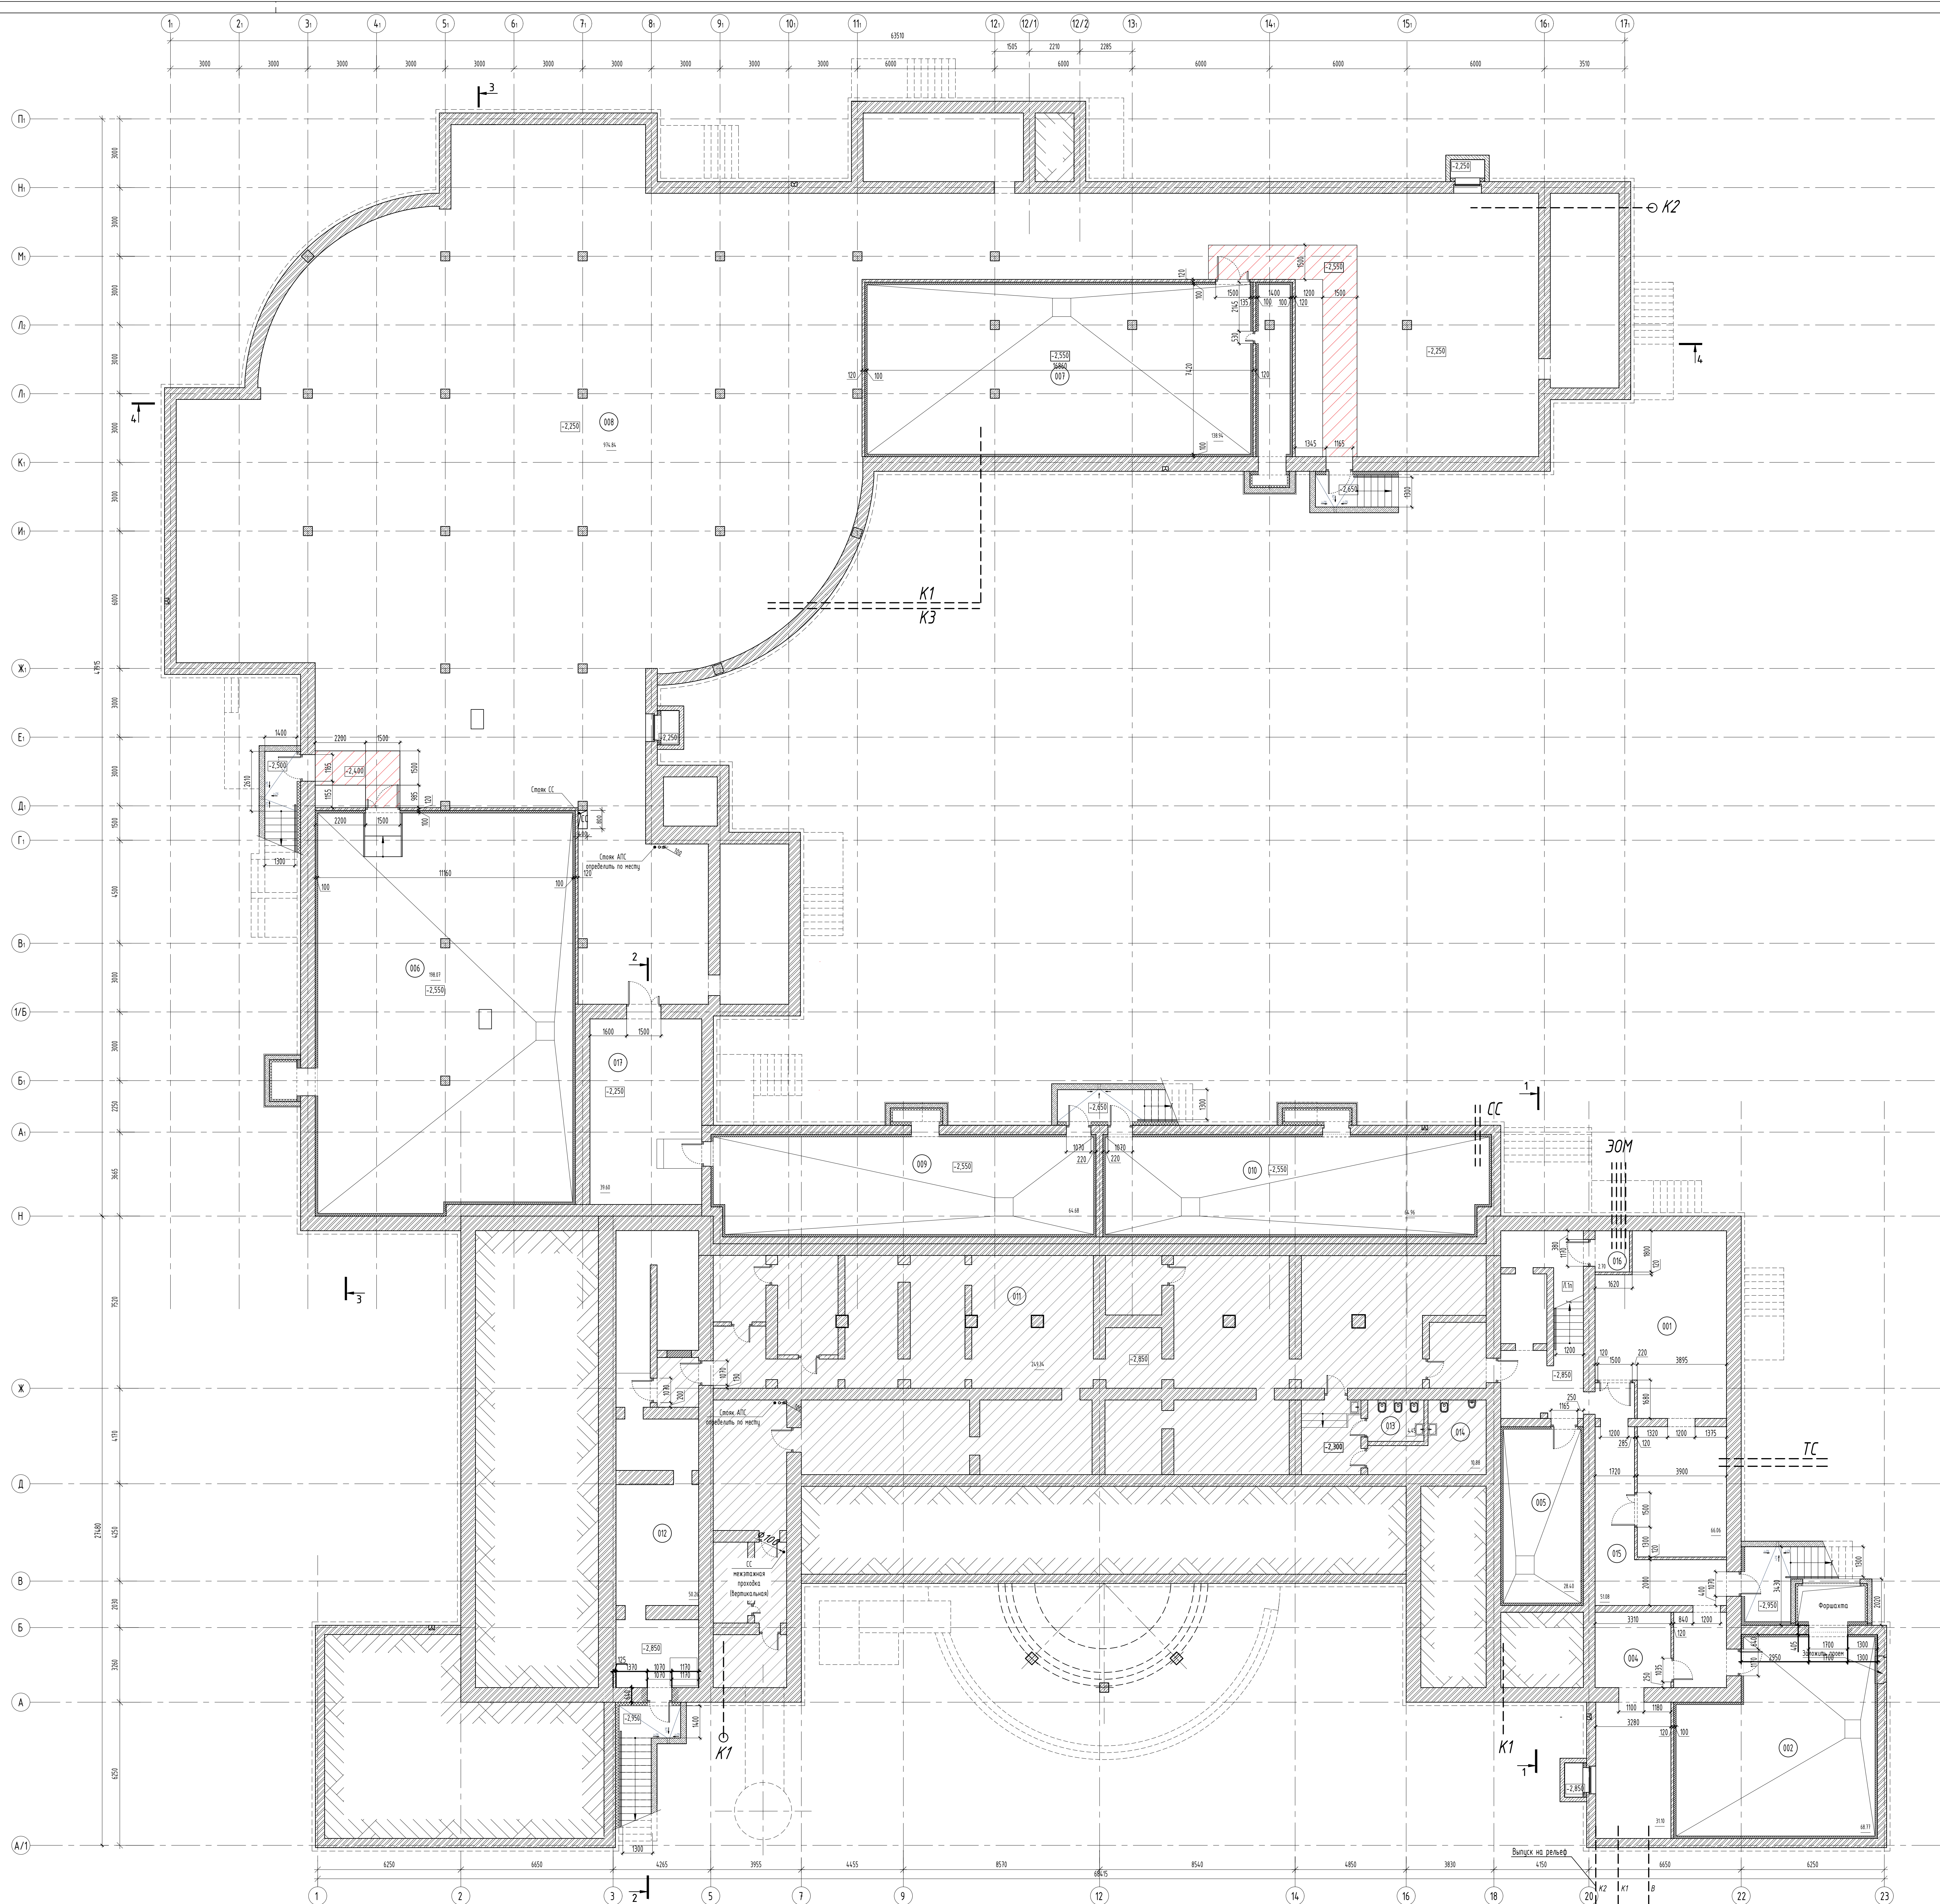


Экспликация помещений подвала			
Номер помещения	Наименование	Площадь м2	Кл. помещения
001	ИТП	66.06	д
002	Венткамера с формальде	71.26	Б3
004	Водяной узел и насосная	31.10	д
005	Венткамера	28.40	Б3
006	Венткамера	198.07	Б3
007	Венткамера	138.94	Б3
008	Техническое помещение для хранения инженерных коммуникаций	974.84	Б3
009	Венткамера	64.68	Б3
010	Венткамера	64.36	Б3
011	Защитное помещение гражданской обороны	2493.34	Б3
012	Коридор	50.95	
013	Санузел женский	10.88	
014	Санузел мужской	4.45	
015	Коридор	21.08	
016	Узел ввода электрических сетей	5.70	Б4
017	Коридор	39.60	
		Всего	2047.4

УСЛОВНЫЕ ОБОЗНАЧЕНИЯ

- Существующие стены из полнотелого кирпича
- Замена монолитных X/B стены
- Замена перегородки из полнотелого кирпича 120мм, оштукатуренная
- Номер помещения по эскизу
- Маркировка целостности замены дверей
- Отметка уровня пола знака
- Помещение ГО ЧС
- Пути эвакуации

1. Возможность устройства проемов в несущих стенах будет уточняться в проекте.
Газель и расположение вентиляционных шахт будет уточнен в проекте.
2. Шахты предназначение для прокладки инженерных коммуникаций и стоек (ВК, СС, ЗОМ), оборудуемые люками для обслуживания.
3. ★ категорирование по взрывопожарной опасности данных помещений выполнить на этапе проектирования.
4. Марки ограждений смотреть альбом 16-25/Г-П-АР лист 61

						16-25/17-П-АР		
						Капитальный ремонт объекта "БООУ Школа № 429 "Самойковой сора", расположенного по адресу: г.Москва, ул. Садовой Скорой 5-я, 8/16		
Изм.	Кол. экз.	Лист	№ док.	Подпись	Дата			
Разреш.		Листов		<i>[Подпись]</i>	2016.07.07			
						Станд.	Лист	Листов
							р	
						Архитектура-планировочные решения		
И.контр.		Губарева		<i>[Подпись]</i>	2016.07.07			
Гип.		Морозов		<i>[Подпись]</i>	2016.07.07			
						План подвала М1100		
						 AZURIT		

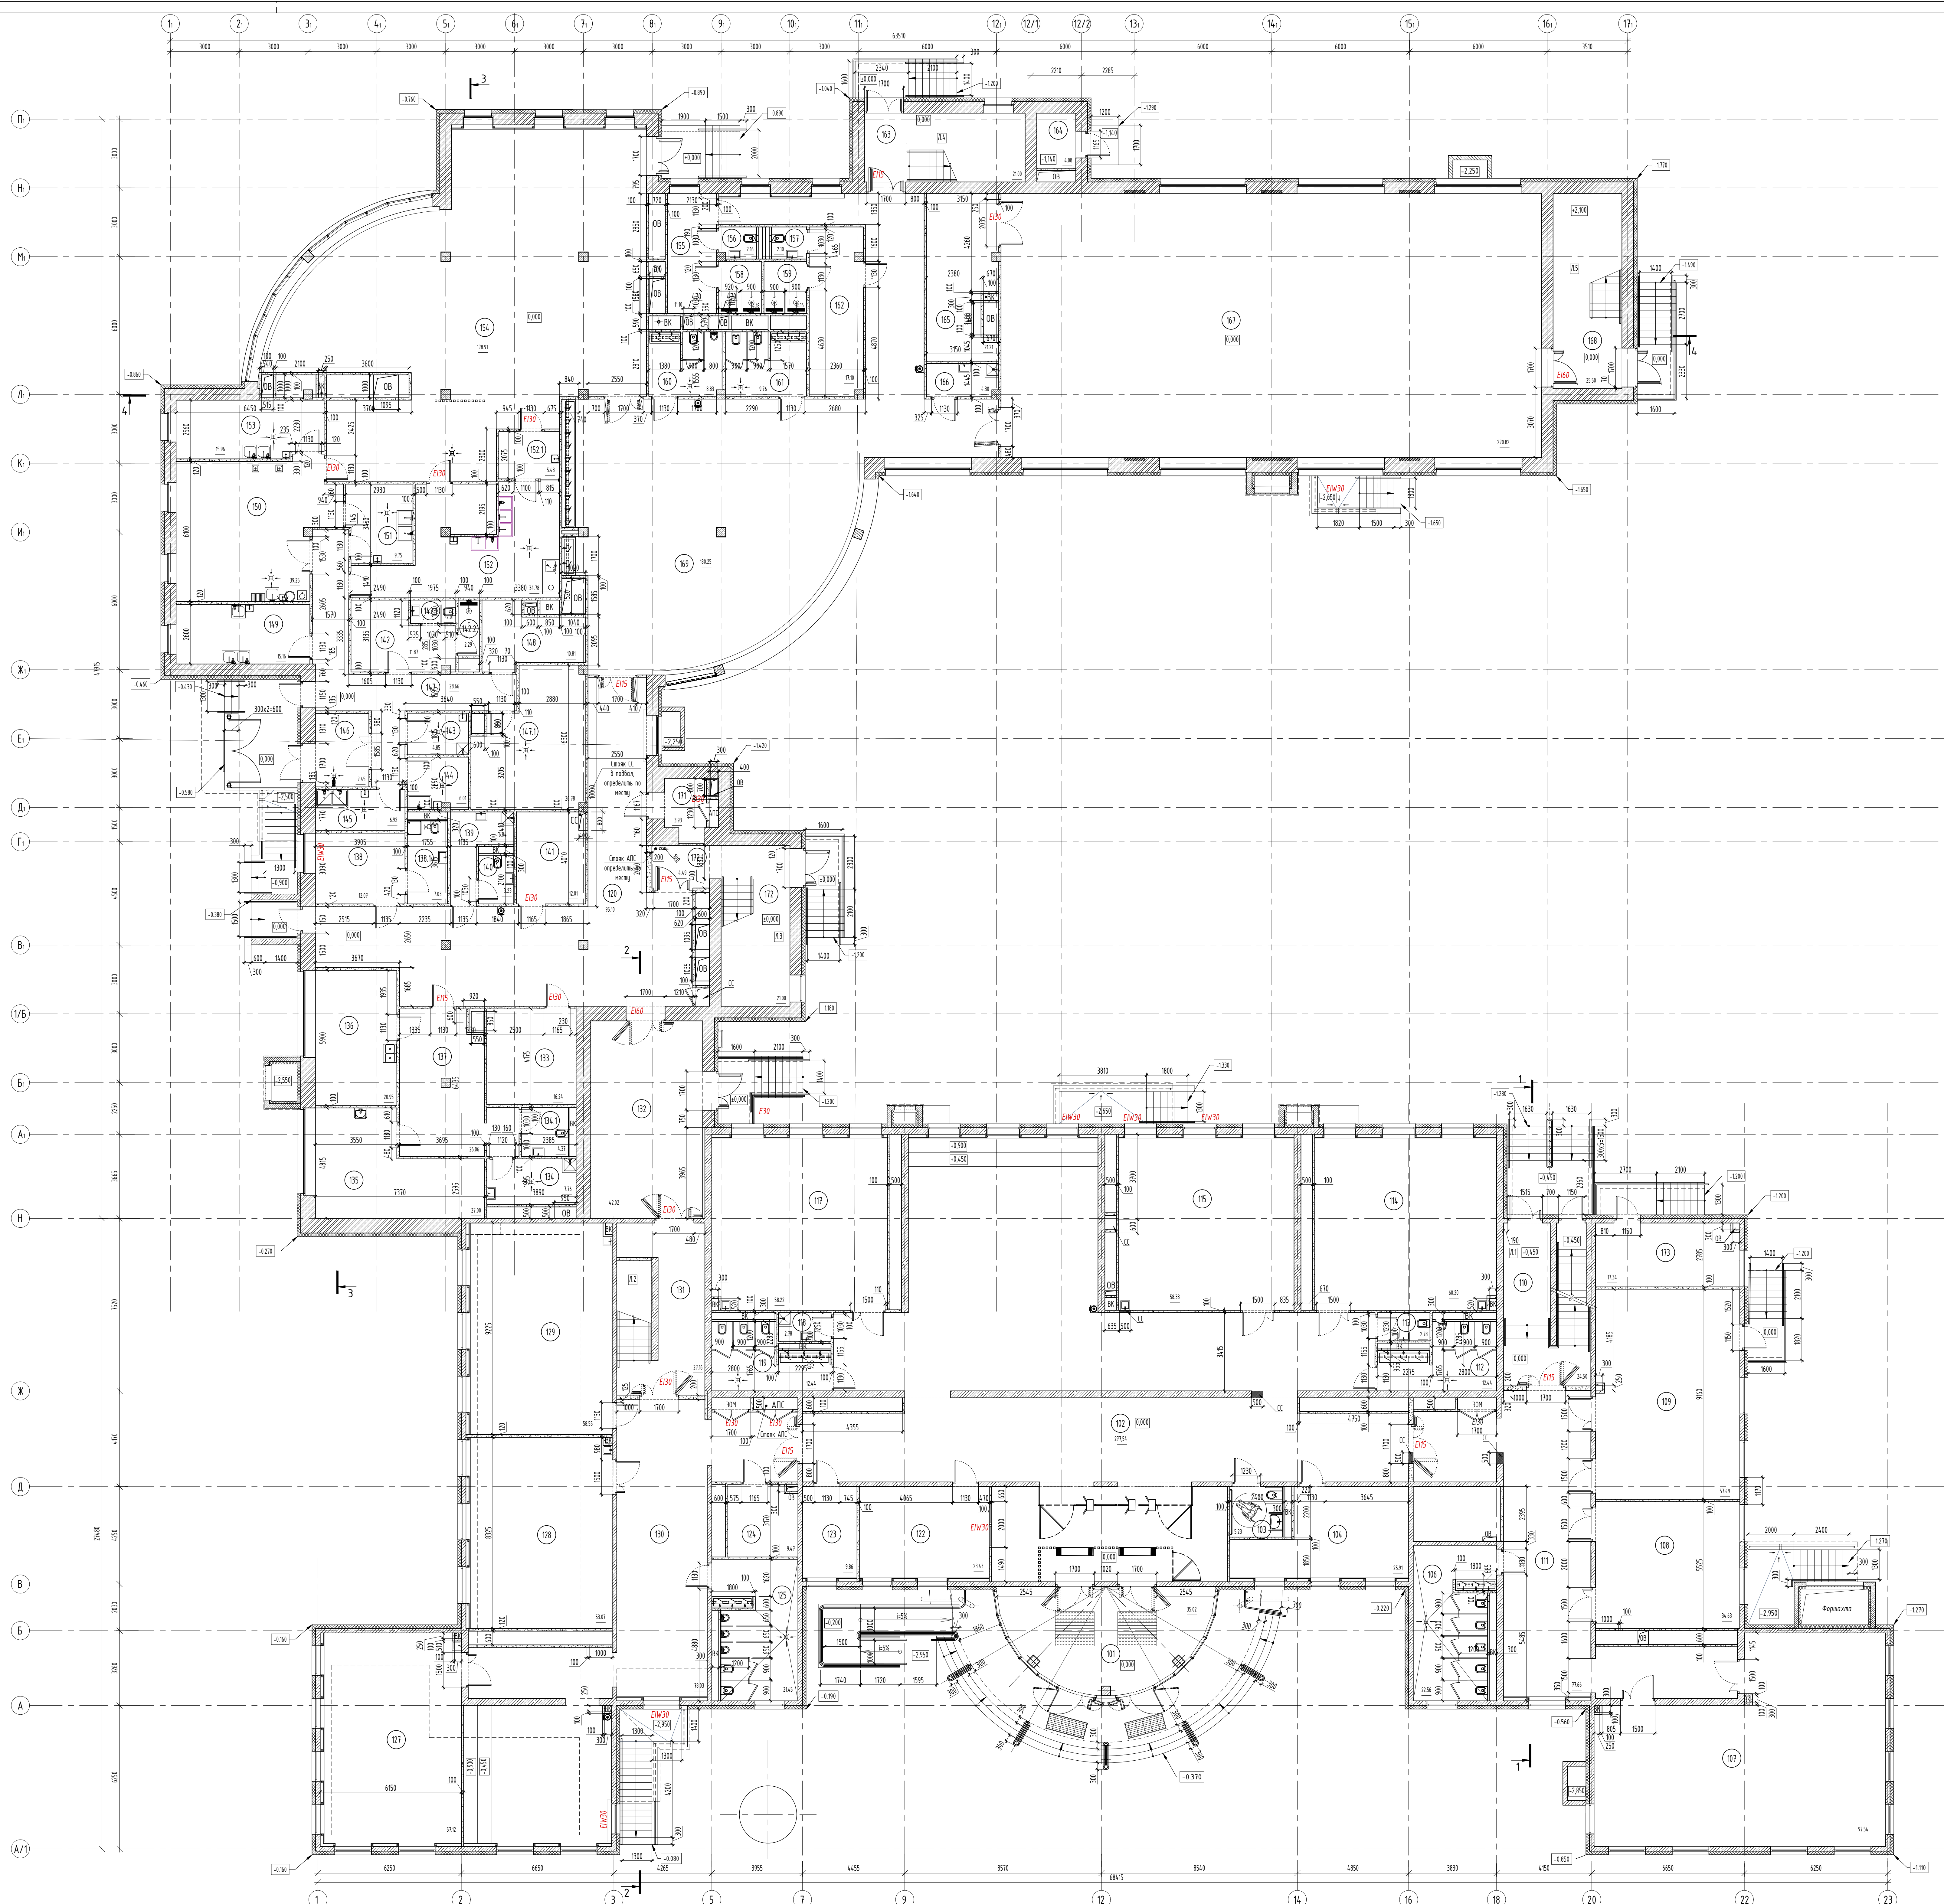


Поме- щения	Наименование	Площадь, м2	Кол- пomme- щения
101	Танцб.	35,02	
102	Коридор с рекреацией	271,54	
103	Санит. для МП	5,23	
104	Административный кабинет тип 1 (начальная школа)	25,91	
105	Санит. для девочек (начальная школа)	23,25	
107	Гардеробная для обучающихся (основная и старшая школа)	97,54	
108	Гардеробная для обучающихся (основная и старшая школа)	35,25	
109	Гардеробная для обучающихся (начальная школа)	51,49	
110	Лестничная клетка (ЛК)	24,50	
111	Коридор	71,66	
112	Санит. для мальчиков (начальная школа)	12,44	
113	Санит. для персонала	2,78	
114	Учебные кабинеты (начальная школа)	60,20	
115	Учебные кабинеты (начальная школа)	58,33	
117	Учебные кабинеты (начальная школа)	58,22	
118	ПСИ	2,78	84
119	Санит. для девочек (начальная школа)	12,44	
120	Коридор с рекреацией (основная и старшая школа)	95,10	
122	Комната охраны (с диспетчерским пунктом)	23,43	
123	Гардеробная комната (для учителей)	9,86	
124	Помещение связи	9,47	84
125	Санит. для мальчиков (начальная школа)	21,73	
127	Учебные кабинеты (начальная школа)	58,31	
128	Учебные кабинеты (начальная школа)	53,71	
129	Учебные кабинеты (начальная школа)	58,81	
130	Коридор с рекреацией	117,57	
131	Лестничная клетка Тип НЗ	27,18	
132	Вестибюль	42,02	
133	Электрощитовая	16,26	83
134	Место для приёма/выдачи дезинфекционных растворов и средств для обработки помещений, предназначенных для помещений медицинского назначения	7,74	84
134.1	Туалет男/белая	4,31	
135	Кабинет броси	21,00	
136	Процедурный (приёмный) кабинет	28,88	
137	Кабинет	12,06	
138	Комната инструктора	26,97	
138.1	Санит. с душем	7,93	
139	ПСИ	6,39	84
140	Санит. для персонала	3,27	
141	Помещение связи	12,01	
142	Помещение для персонала	11,87	83
142.1	Санит. для персонала	2,01	
142.2	Душевые	2,29	
143	ПСИ	4,85	84
144	Помещение для временного хранения вещей отбывающих	6,01	84
145	Кладовая с вещами отбывающих пары	6,92	84
146	Защитный щит	7,45	84
147	Коридор	28,66	
147.1	Помещение с холодильным оборудованием	26,78	83
148	Кладовая обуви/предметов	10,81	
149	Диспетчерский щит	15,16	83
150	Гарный щит	39,25	83
151	Менская для кройки пошива	9,75	Д
152	Менская для стирки пошива	34,18	Д
152.1	Предметная	5,48	83
153	Холодный щит	15,96	Д
154	Обеденный зал	118,91	
155	Раздевальня	176,10	
156	Санит.	2,76	
157	Санит.	2,10	
158	Душевые	4,15	
159	Душевые	4,15	
160	Санит. для мальчиков	8,71	
161	Санит. для девочек	9,76	
162	Раздевальня	21,10	
163	Лестничная клетка (ЛК)	11,00	
164	Техническое помещение	4,16	84
165	Сараи	21,21	83
166	ПСИ	4,30	84
167	Экспериментальный спортивный зал	270,82	
168	Лестничная клетка (ЛК)	25,50	
169	Коридор с рекреацией (основная и старшая школа)	281,24	
171	Тех. помещение	3,93	84
172	Лестничная клетка (ЛК)	21,00	
172.1	Танцб.	4,48	
173	Электрощитовая	17,34	83
Итого		2667,3	

	- Существующие молитовые х/б стенов
	- Замена перегородки из разовальных блоков 1625x25x100/350/85 по ГОСТ Р 19522-2022, пол на клею с армированием базальтовой сеткой, шт
	- Замена перегородки из разовальных блоков 1625x25x100/350/85 по ГОСТ Р 19522-2022, пол на клею с армированием базальтовой сеткой, шт
	- Замена перегородки из акриловых односторонних стенок толщиной 100мм
	- Замена перегородки из акриловых односторонних стенок толщиной 100мм
	- Замена остекленные перегородки
	- Замена перегородки синтетическая (пластиковая) с фактурой и неводонепроницаемой

- 201 - Номер помещения по экспликации
- 10,000 - Отметка уровня пола этажа
- E30/EI30/EIW30 - Маркировка огнестойкости заменяемых дверей, окон, перегородок;



1. Возможность устройства проемов в несущих стенах будет уточняться в проекте.
- Размер и расположение вентиляционных шахт будет уточнен в проекте.
2. Шахты предназначенные для прокладки инженерных коммуникаций и стоек ЛВК, СС, ЭОМ оборудуются лючками для обслуживания.
3. ★ категорирование по взрывопожарной опасности данных помещений выполнить на этапе проектирования.
4. Марки ограждений смотреть альбом 16-25/Г-П-АР лист 61

						№-25/Г - П-АР					
						Капитальный ремонт объекта "БООУ Школа № 429 "Солнечная гора", расположенного по адресу: г. Москва, ул. Солнечной горы 5-я, д.14					
Изм.	Кол.л.	Лист	№ док.	Подпись	Дата	Архитектурно-планировочные решения					
Разраб.		Литовская			08.07.18	Станд.	Лист	Листов	Р		
И. контрол.		Гударева			08.07.18	Лист 1 из 1, стр. 1 из 1					
						 АЗУРИТ					

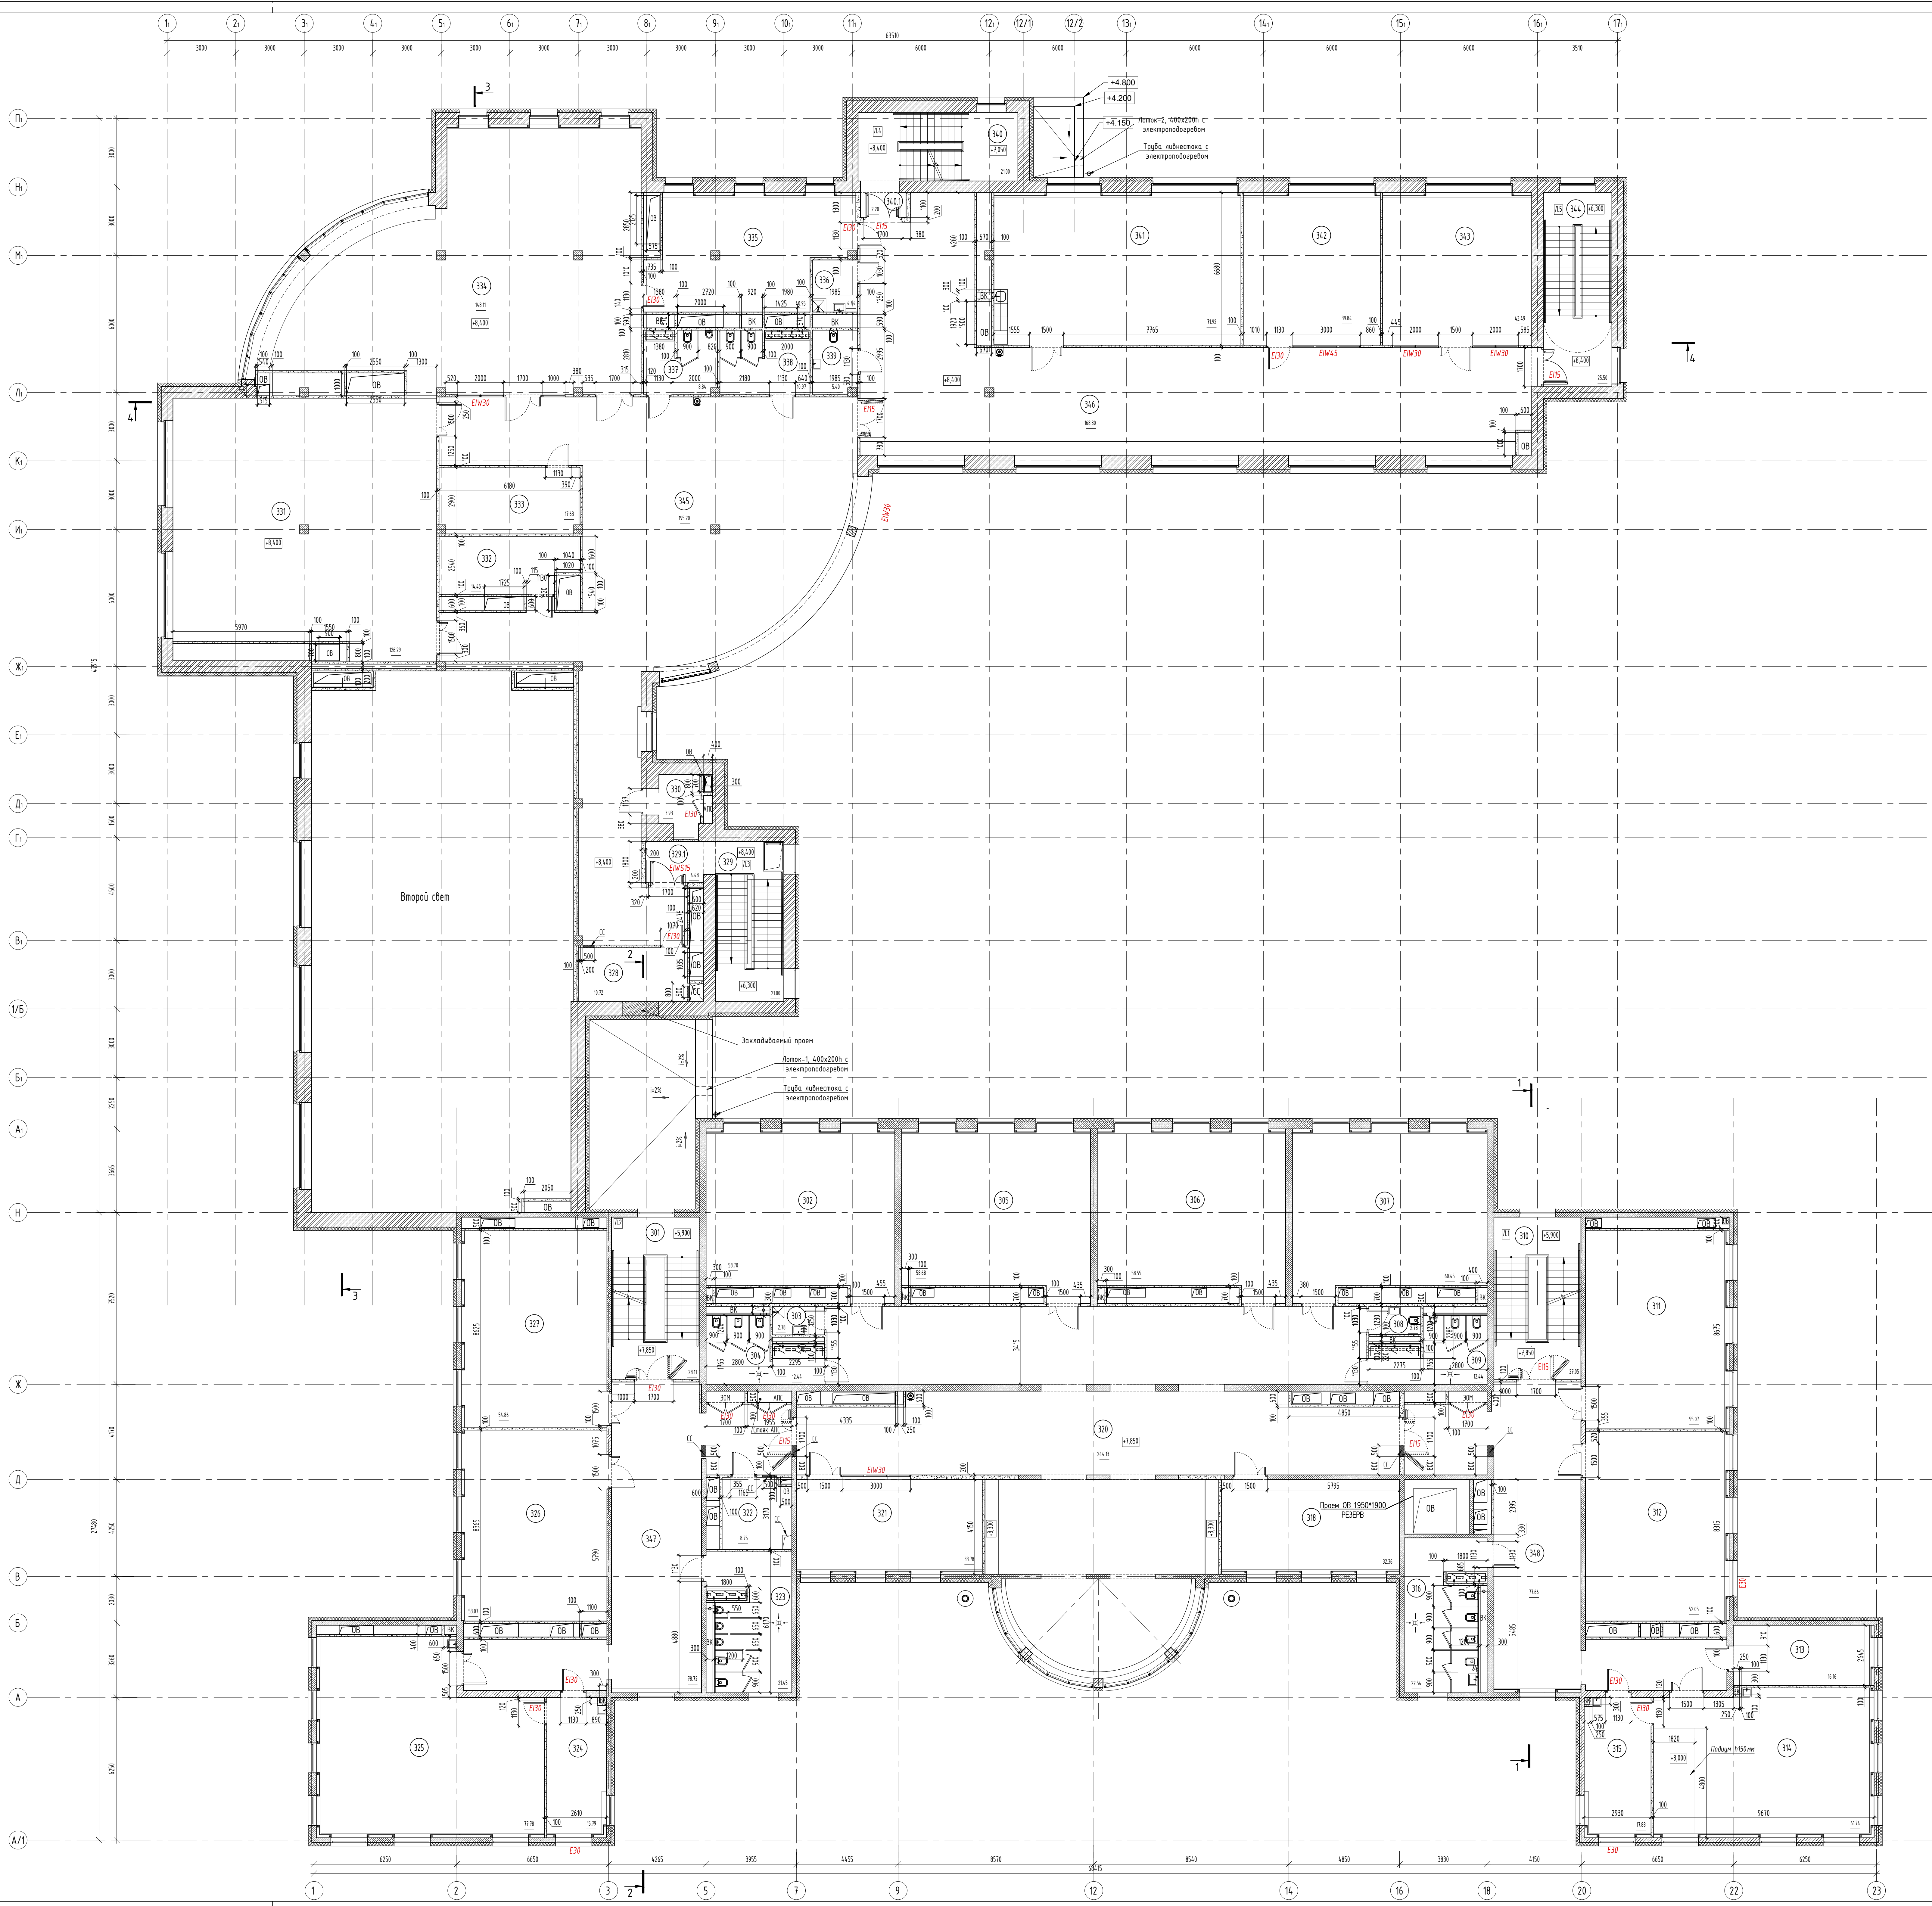


Экспликация помещений 3-20 этажа				
Номер помещения	Наименование	Площадь, м2	Кол. помещ.	всего
301	Лесничная клетка Тип И2	28,82		
302	Кабинет русского языка и литературы	58,70		
303	ПМ	2,78	84	
304	Специал. для девочек (основная и старшая школа)	12,44		
305	Кабинет русского языка и литературы	58,88		
306	Кабинет математики	58,55		
307	Кабинет математики	60,45		
308	Специал. для персонала	2,75		
309	Специал. для мальчиков (основная и старшая школа)	12,44		
310	Лесничная клетка (П1)	27,00		
311	Кабинет географии	55,07		
312	Универсальный учебный кабинет	56,05		
313	Кабинет для индивидуальных занятий, 6 кв. с компьютером-психологом	16,16		
314	Учебный кабинет для изучения естественных физика	61,06		
315	Лабортарная кабинета физики	18,02	83	
316	Специал. для девочек с компьютерной техникой (основная и старшая школа)	23,25		
317	подсобное помещение	6,66	84	
318	Кабинет иностранного языка (основная и старшая школа)	32,36		
320	Коридор / рекреация	244,13		
321	Кабинет иностранного языка (основная и старшая школа)	33,78		
322	Помещение связи	8,75	84	
323	Специал. для мальчиков (основная и старшая школа)	21,73		
324	Лабортарная кабинета биологии	15,93	83	
325	Учебный кабинет для изучения естественных: биология + ОБСР	71,98		
326	Универсальный учебный кабинет	53,07		
327	Кабинет истории тип 1	54,86		
328	Корсидор	10,72	83	
329	Лесничная клетка (П1)	21,00		
329.1	Тамбур	4,48		
330	Тех. помещение	3,33	84	
331	Универсальное помещение с возможностью организации лингвистического зала (рекреатория)	125,19		
332	Раздевальня	14,45		
333	Раздевальня	14,45		
334	Интегрированный информационный библиотечный центр с залом для индивидуальных занятий	152,15		
335	Интегрированный информационный библиотечный центр (хранение (архивный фонд) / выдача книг)	41,15	83	
336	ПМ	4,44	84	
337	Специал. для мальчиков (основная и старшая школа)	10,84		
338	Специал. для девочек (основная и старшая школа)	8,97		
339	Специал. для персонала	5,40		
340	Лесничная клетка (П1)	21,00		
340.1	Тамбур	7,20		
341	Кабинет с рабочим пространством для учителей Тип 1 (основная и старшая школа)	21,92		
342	Универсальное помещение с возможностью организации рекреатора	39,84	83	
343	Помещение музея	43,49		
344	Лесничная клетка (П1)	25,00		
345	Коридор / рекреация (основная и старшая школа)	195,20		
346	Коридор / рекреация (основная и старшая школа)	168,80		
347	Коридор	78,72		
348	Коридор	77,66		
		Всего	2246,3	

УСЛОВНЫЕ ОБОЗНАЧЕНИЯ

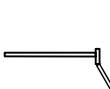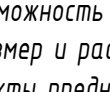- Существование молотых и/л ступи
 - Замена/и переорудови з аэобитовних блокоб
 - 1/425/2550/10/50/85.0 по ГОСТ Р 7652-2002, пошчино 100мм на клас с сиробитовних базальтовоу сеткоу, опитування
 - Замена/и переорудови з аэобитовних блокоб
 - 1/425/2550/10/50/85.0 по ГОСТ Р 7652-2002, пошчино 200мм на клас с сиробитовних базальтовоу сеткоу, опитування
 - Замена/и переорудови з опитовани односторонне вуглиноу на бис битови, пошчино 100мм
 - Замена/и переорудови з опитовани односторонне вуглиноу до 40, ровиноу пошчино 100мм
 - Замена/и отпеленные переорудови
- 
 - Замена/и переорудови сантисеткис (вдоскокоу) с одвими и неободиной фунтисурой
- 
 - Номер помещени по экспликации
- 
 - Отметка уровня пола эстако
- 
 - Маркировка опности/и замены/и двери, окон, переорудови,

1. Возможность устройства проемов в несущих стенах будет уточняться в проекте.
2. Размер и расположение вентиляционных шахт будет уточнен в проекте.
3. Шахты предназначены для прокладки инженерных коммуникаций и стояков (ВК, СС, ЗОМ), оборудуются лючками для обслуживания.
3. * категорирование по взрывопожарной опасности данных помещений выполнить на этапе проектирования.
4. Марки ограждений смотреть альбом 16-25/Г-П-А лист 61

					16-25/Г-П-АР		
					Капитальный ремонт объекта "ГБОУ Школа № 429 "Скопальная гора", расположенного по адресу: г.Москва, ул. Скопальной горы 5-я, д.16		
Изм.	Или	Лист	№ докум.	Подпись	Дата		
Решено		Листов			2016-01-18		
					Архитектурно-планировочные решения		
					Стадия	Лист	Листов
					р		
И. контр.	Губарева				2016-01-18		
Ген.пр.	Маркова				2016-01-18		
					План 3 этажа. М1:100		
							

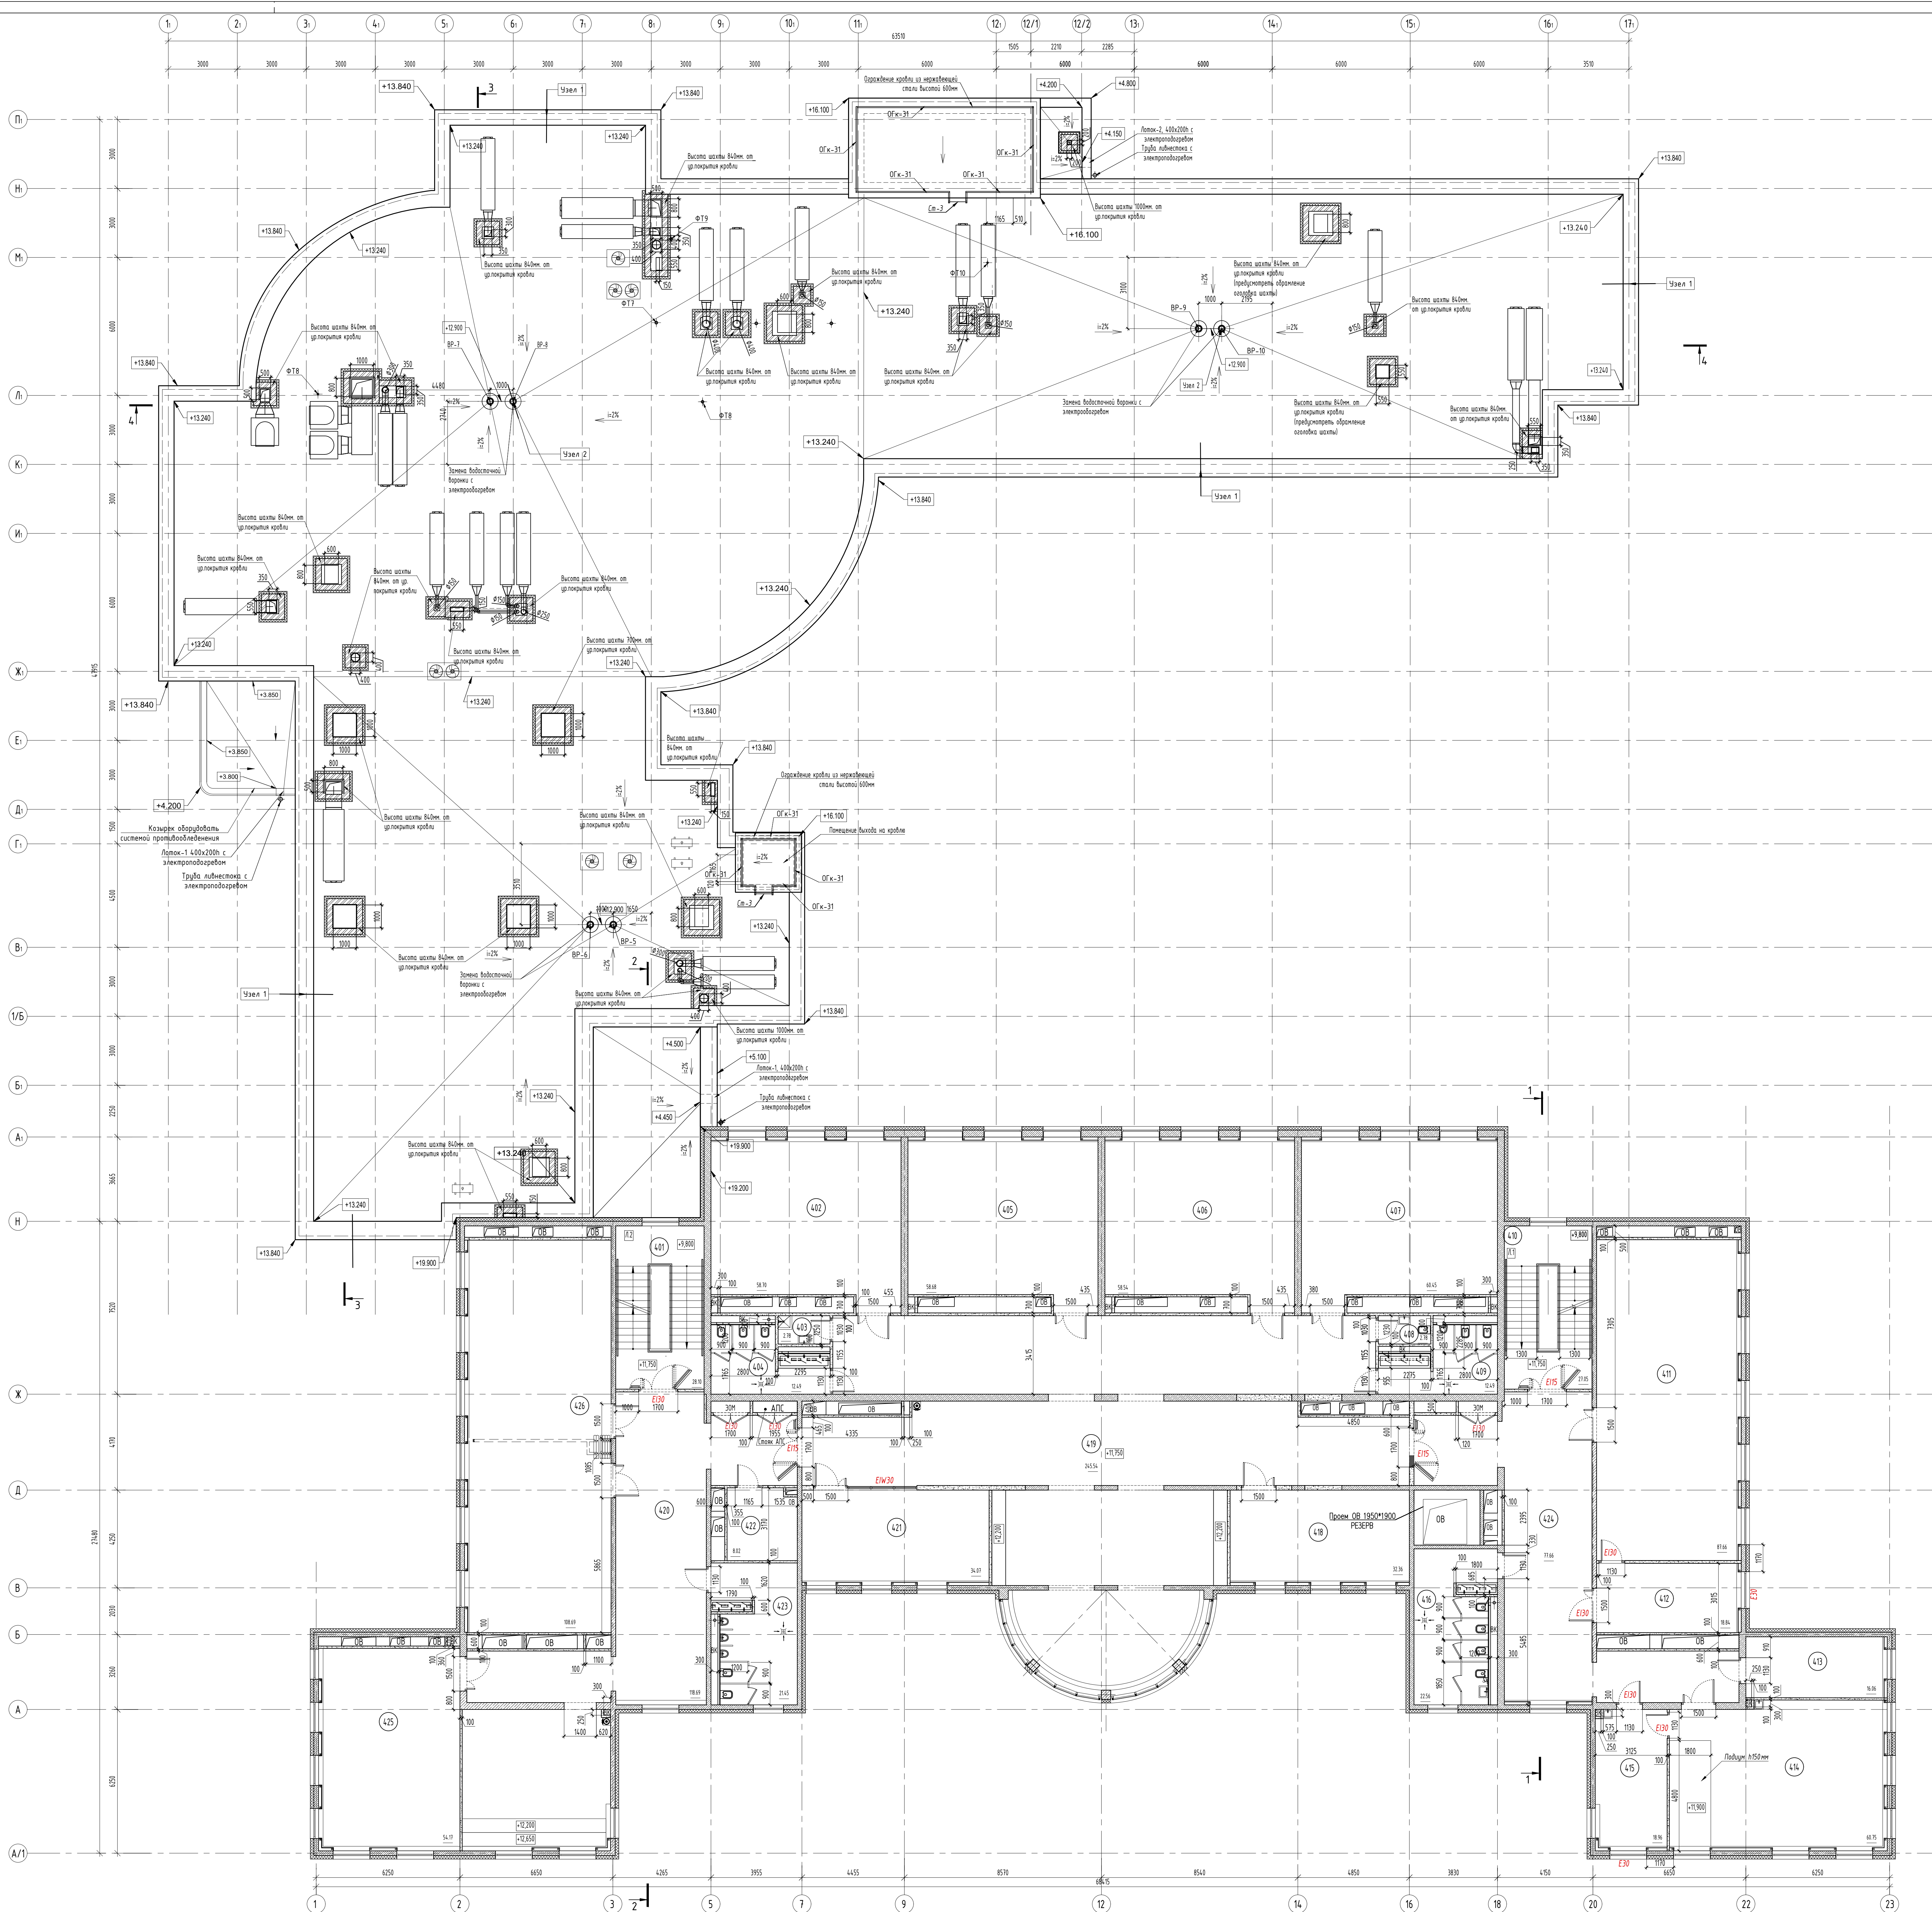

Номер помещения	Назначение	Площадь м2	Класс помещения
401	Лесничная каюта Тип Н2	28,81	
402	Кабинет русского языка и литературы	28,70	
403	ПМ	12,49	В1
404	Санин для девочек (основная и старшая школа)	21,48	
405	Кабинет русского языка и литературы	58,68	
406	Кабинет математики	58,54	
407	Кабинет математики	60,45	
408	Санин для персонала	2,18	
409	Санин для мальчиков (основная и старшая школа)	12,49	
410	Лесничная каюта (П1)	26,98	
411	Кабинет информационных технологий	87,66	
412	Лаборатория при кабинете информационных технологий	18,84	В3
413	Административный кабинет тип 1 (основная и старшая школа)	16,03	
414	Учебные кабинеты для изучения естественных химия	60,75	
415	Лаборатория кабинета химии	16,96	В3
416	Санин для девочек с комнатой личной гигиены (основная и старшая школа)	22,56	
417	Подсобное помещение	7,30	В4
418	Кабинет иностранного языка (основная и старшая школа)	32,36	
419	Коридор с рекреацией	245,54	
420	Коридор с рекреацией	198,69	
421	Кабинет иностранного языка (основная и старшая школа)	31,07	
422	Помещение слуха	8,42	В4
423	Санин для мальчиков (основная и старшая школа)	21,45	
424	Коридор	17,66	
425	Кабинет истории Тип 1	54,17	
426	Кабинет информатики с возможностью деления на два помещения	108,69	
427	Лесничная каюта (П1)	21,00	
428	Помещение фойе на крыльце	12,96	
	Всего	4.178,5	

- Существование множителя $\sqrt{N}$ станы
- Замена переходов из элементов блоков
1/625x250M/050/05.0 по ГОСТ Р 7952-2002, толщину 10мм
на клею с армированием базальтовой сеткой, опущенными
- Замена переходов из элементов блоков
1/625x250M/050/05.0 по ГОСТ Р 7952-2002, толщину 20мм
на клею с армированием базальтовой сеткой, опущенными
- Замена переходов из отбитых оснований брусками на все выступы
толщиной 10мм
- Замена переходов из отбитых оснований брусками до уз раковин
заточке 10мм
- Замена утепление перегородки
- Замена перегородки сантехническая
(пластмассой) с дверью и неизолированной фундаментом


201


8.000

E30/E30W/E30W

- Номер помещения по экспликации
- Отметка уровня пола запаса
- Маркировка сантехникой значимыми дверей, окон, перегородок.

1. Возможность устройства проемов в несущих стенах будет уточняться в проекте.
2. Размер и расположение вентиляционных шахт будет уточнен в проекте.
3. Шахты предназначены для прокладки инженерных коммуникаций и стоек ИВК, СВ, ЭОМ, оборудуются лючками для обслуживания.
3. ★ категорирование по взрывопожарной опасности данных помещений выполнять на этапе проектирования.
4. Марки оградений смотреть альбом 16-25/Г-П-АР лист 61

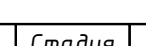				16-25/Г - П-АР		
				Капитальный ремонт объекта "ГБОУ Школа № 429 "Смоленская гора", расположенного по адресу: г.Москва, ул. Смоленской горы 5-А, 8, 4		
Изм	Кол-во	Лист	№ док	Подпись	Дата	
Разраб.		Антонова			09.01.2018	
				Архитектурно-планировочные решения		
				Стадия	Лист	Листов
						Р
Ис. контур	Губарева				09.01.2018	
ГИ	Мамцова				09.01.2018	
				Лист 4 из 4, всего: М.10.00		
				 АЗУРИТ		

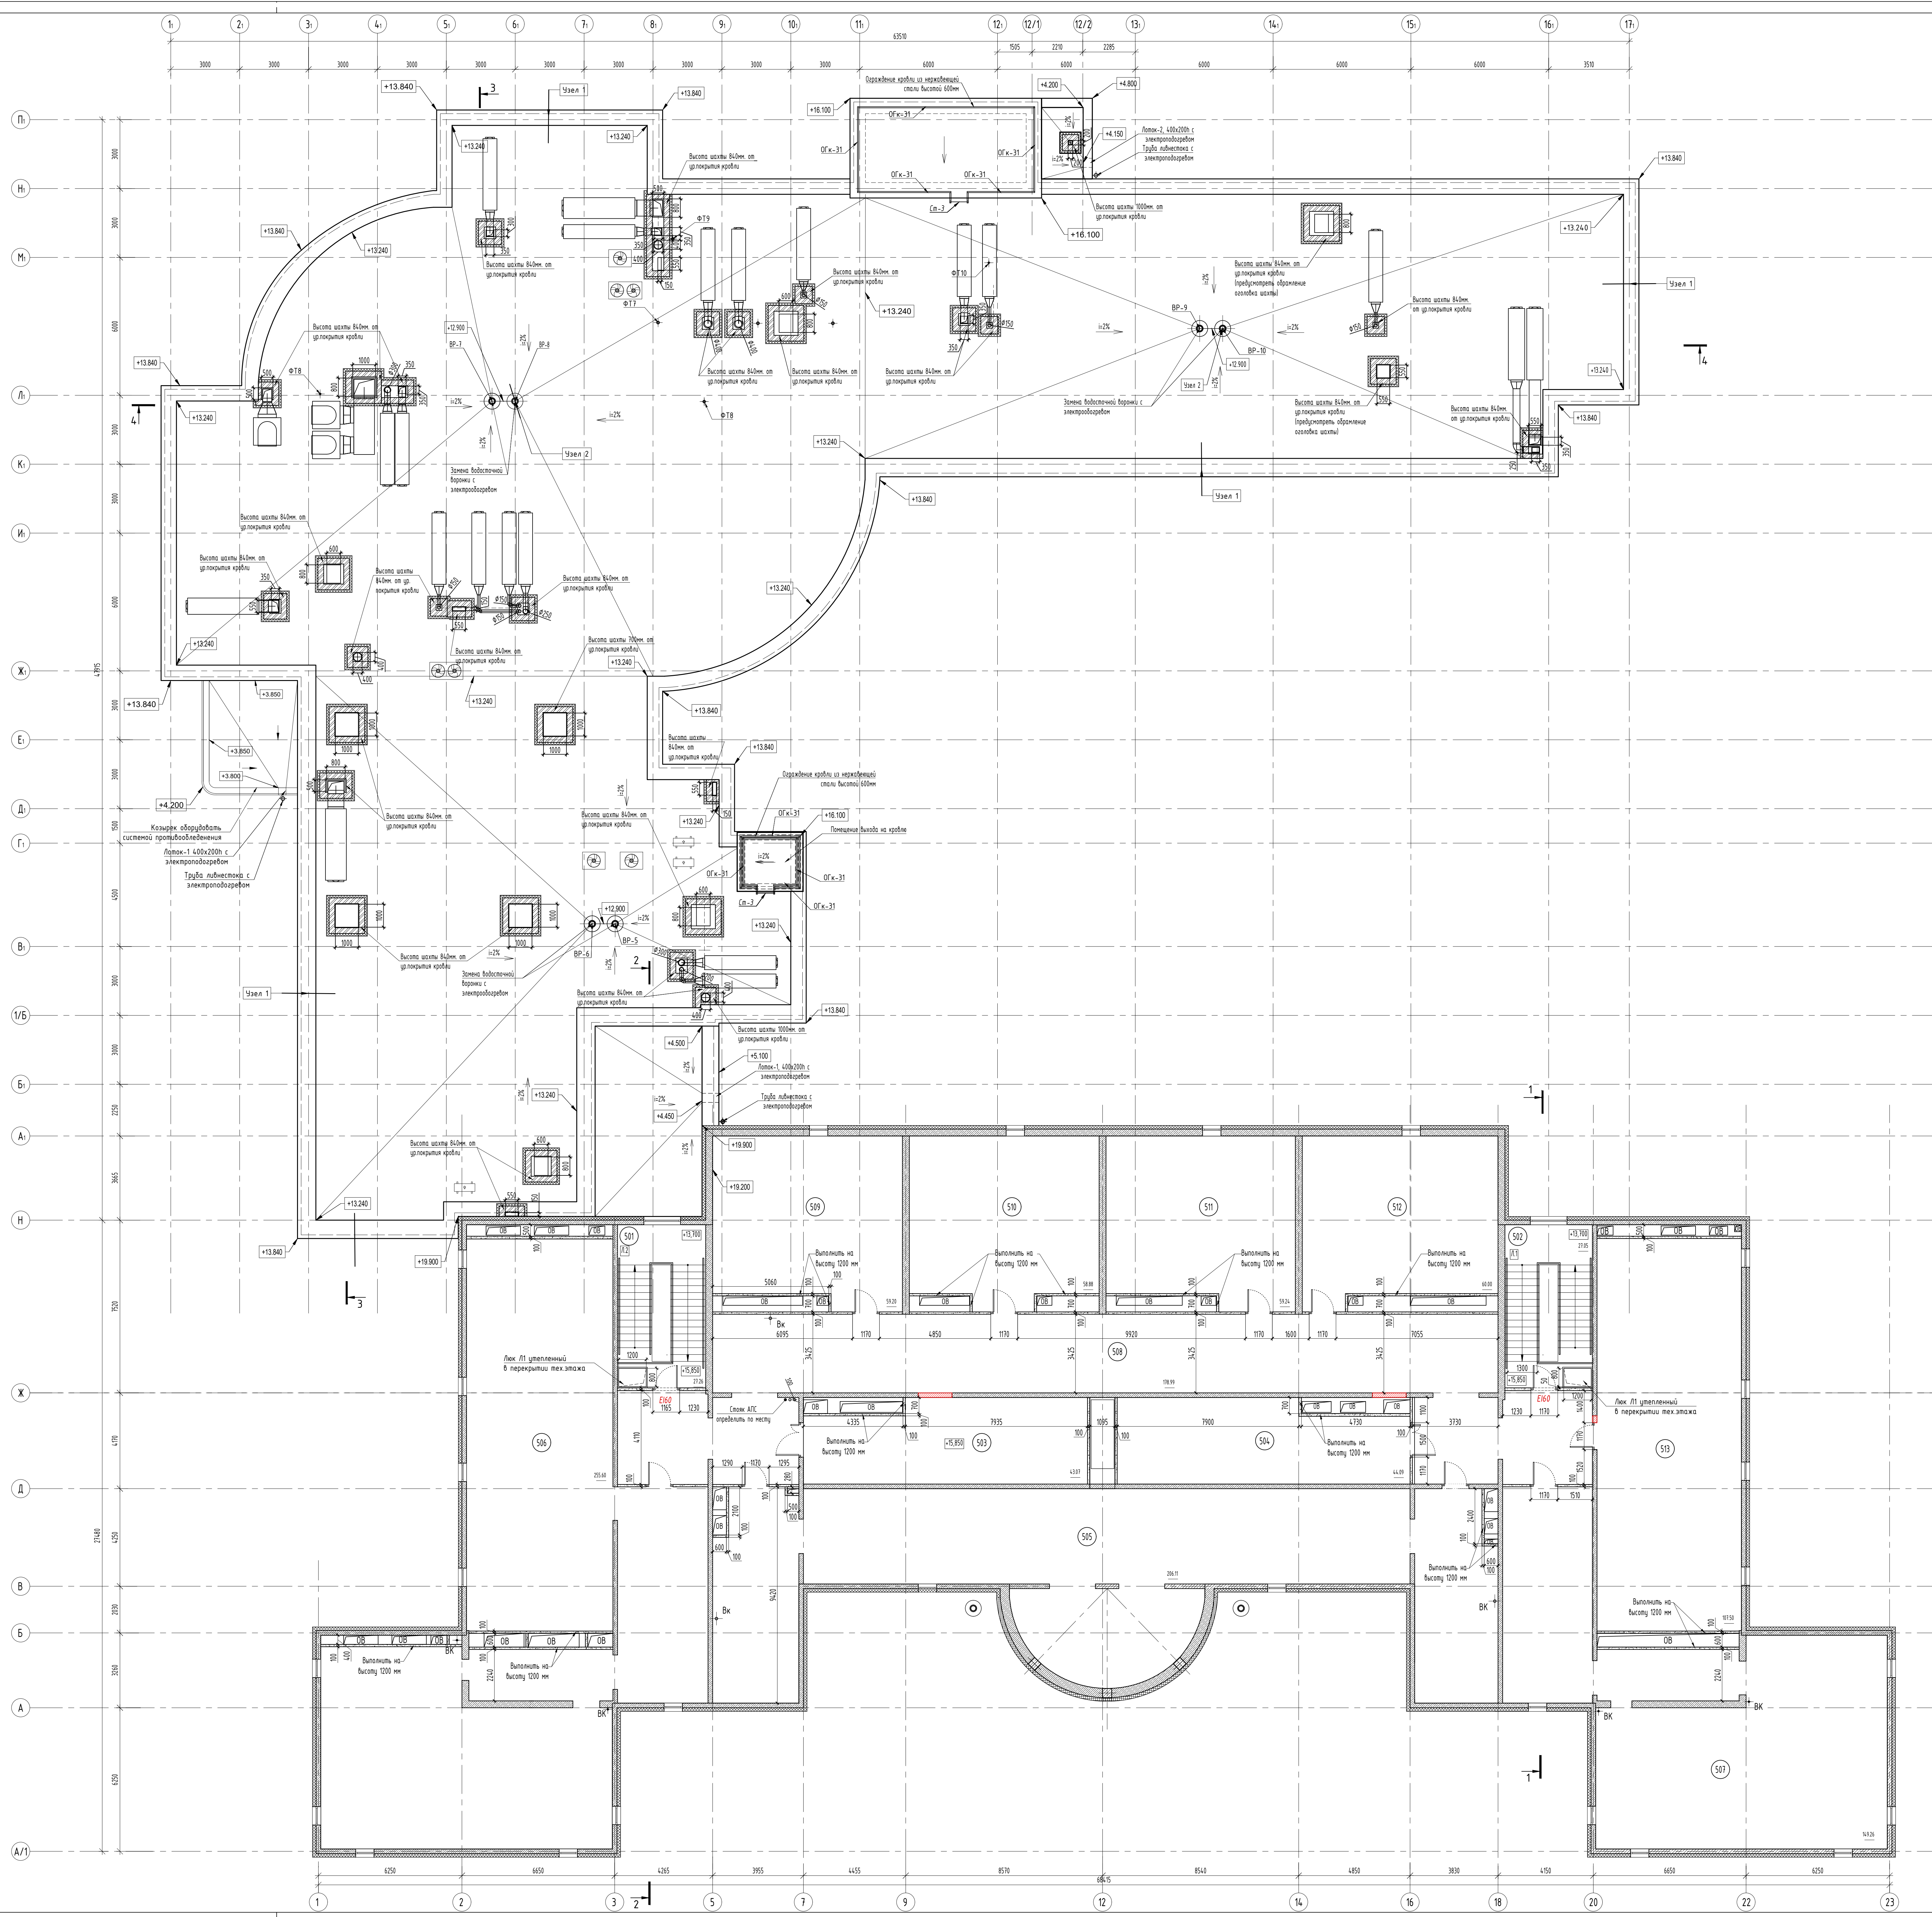


Экспликация помещений технического этажа			
Номер помещения	Наименование	Площадь м2	Кол. помещений
501	Лесничная клетка Тип Н2	27,26	
502	Лесничная клетка Тип Л1	27,05	
503	Вентилятора 1	43,07	83
504	Вентилятора 2	44,09	83
505	Техническое помещение	206,11	83
506	Техническое помещение	155,65	83

УСЛОВНЫЕ ОБОЗНАЧЕНИЯ


- Усиление монтажные и/или стены
- Усиление перегородки из заводских блоков 1/425x250x100/85,0 по ГОСТ Р 7652-2002, толщиной 100мм на клее с армированием базальтовой сеткой, опущенными
- Усиление перегородки из заводских блоков 1/425x250x100/85,0 по ГОСТ Р 7652-2002, толщиной 200мм на клее с армированием базальтовой сеткой, опущенными
- Усиление перегородки из заводских одноосторонне двусторонне на все выступы толщины 100мм
- Усиление перегородки из заводских одноосторонне двусторонне в пр. рабочих толщиной 100мм
- Усиление стальных перегородки
- Усиление перегородки самонесущих (полосчатой) с дверью и несоблюдения функции
- Нормы помещения по эксплуатации
- Отметки уровня пола этажа
- Маркировка оконных стоек, элементов дверей, окон, перегородок;

1. Возможность устройства проемов в несущих стенах будет уточняться в проекте.
- Размер и расположение вентиляционных шахт будет уточнен в проекте.
2. Шахты предназначены для прокладки инженерных коммуникаций и стояков (ВК, СС, ЗОМ) оборудуются люками для обслуживания.
3. ★ калориферование по взрывопожарной опасности данных помещений выполнить на этапе проектирования.
4. Марки ограждений смотреть альбом 16-25/Г-П-АР лист 61

[illegible]

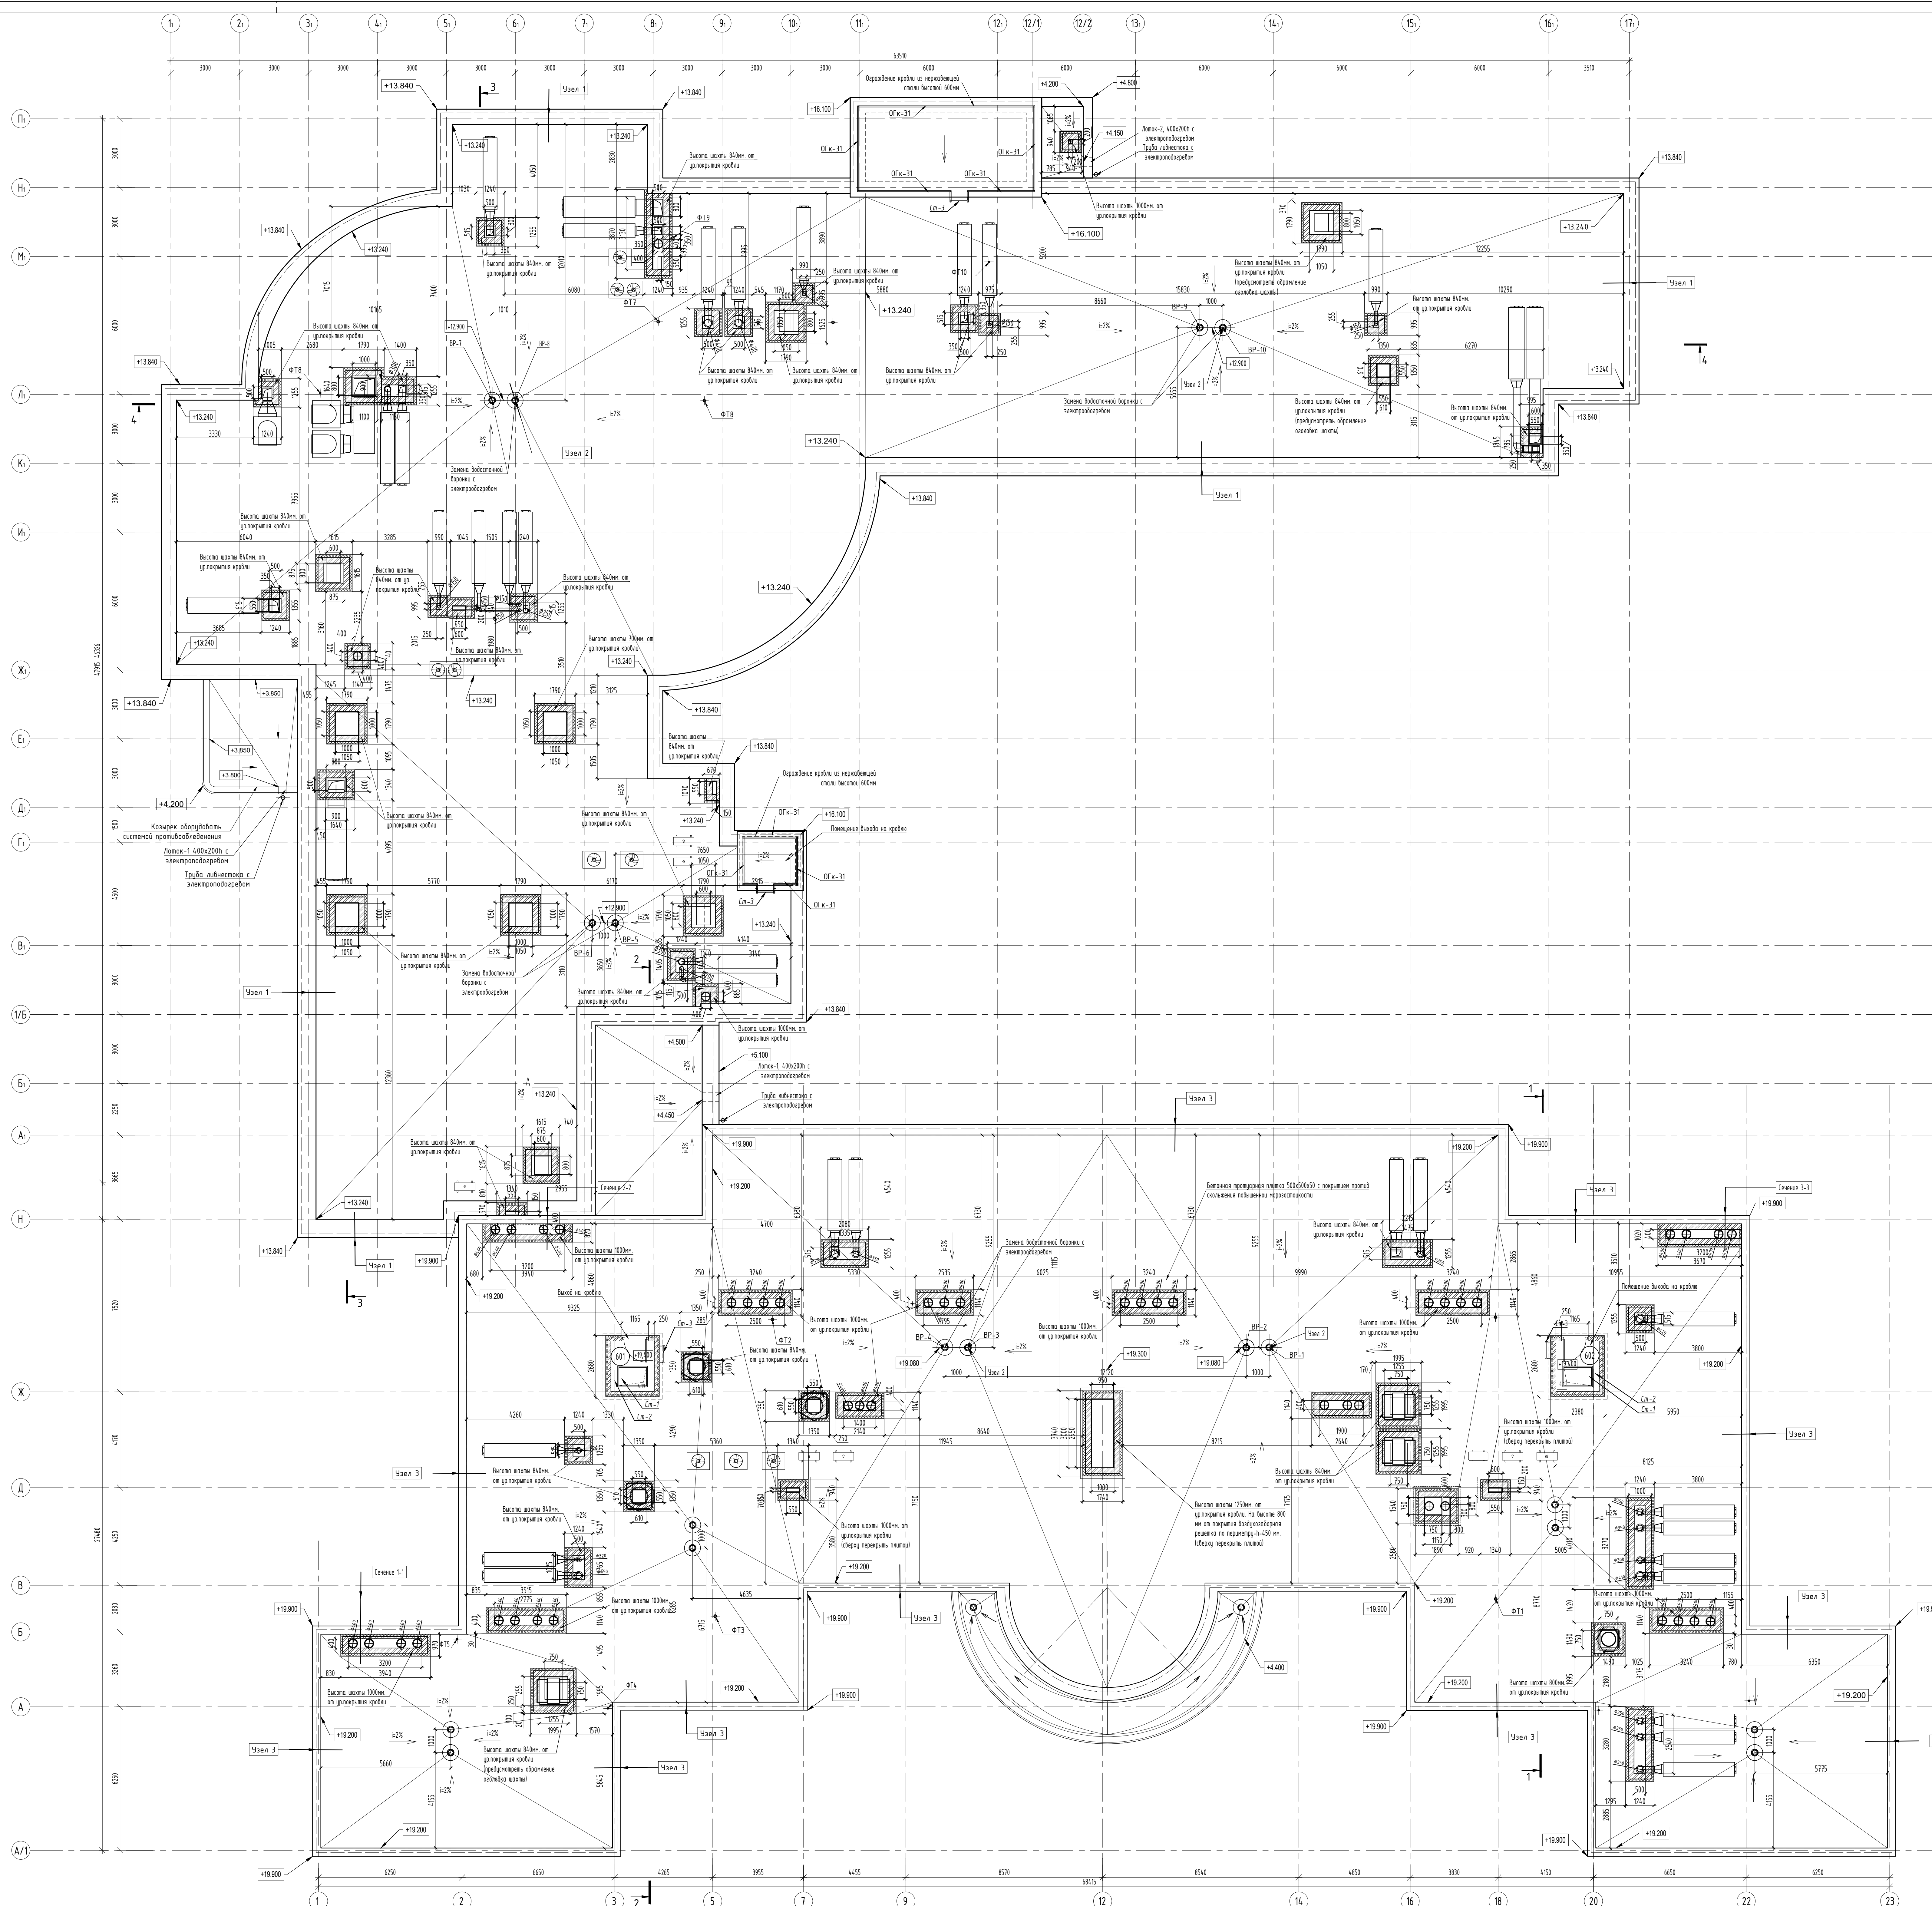

Фрагмент плана кровли в осях
20/Ж

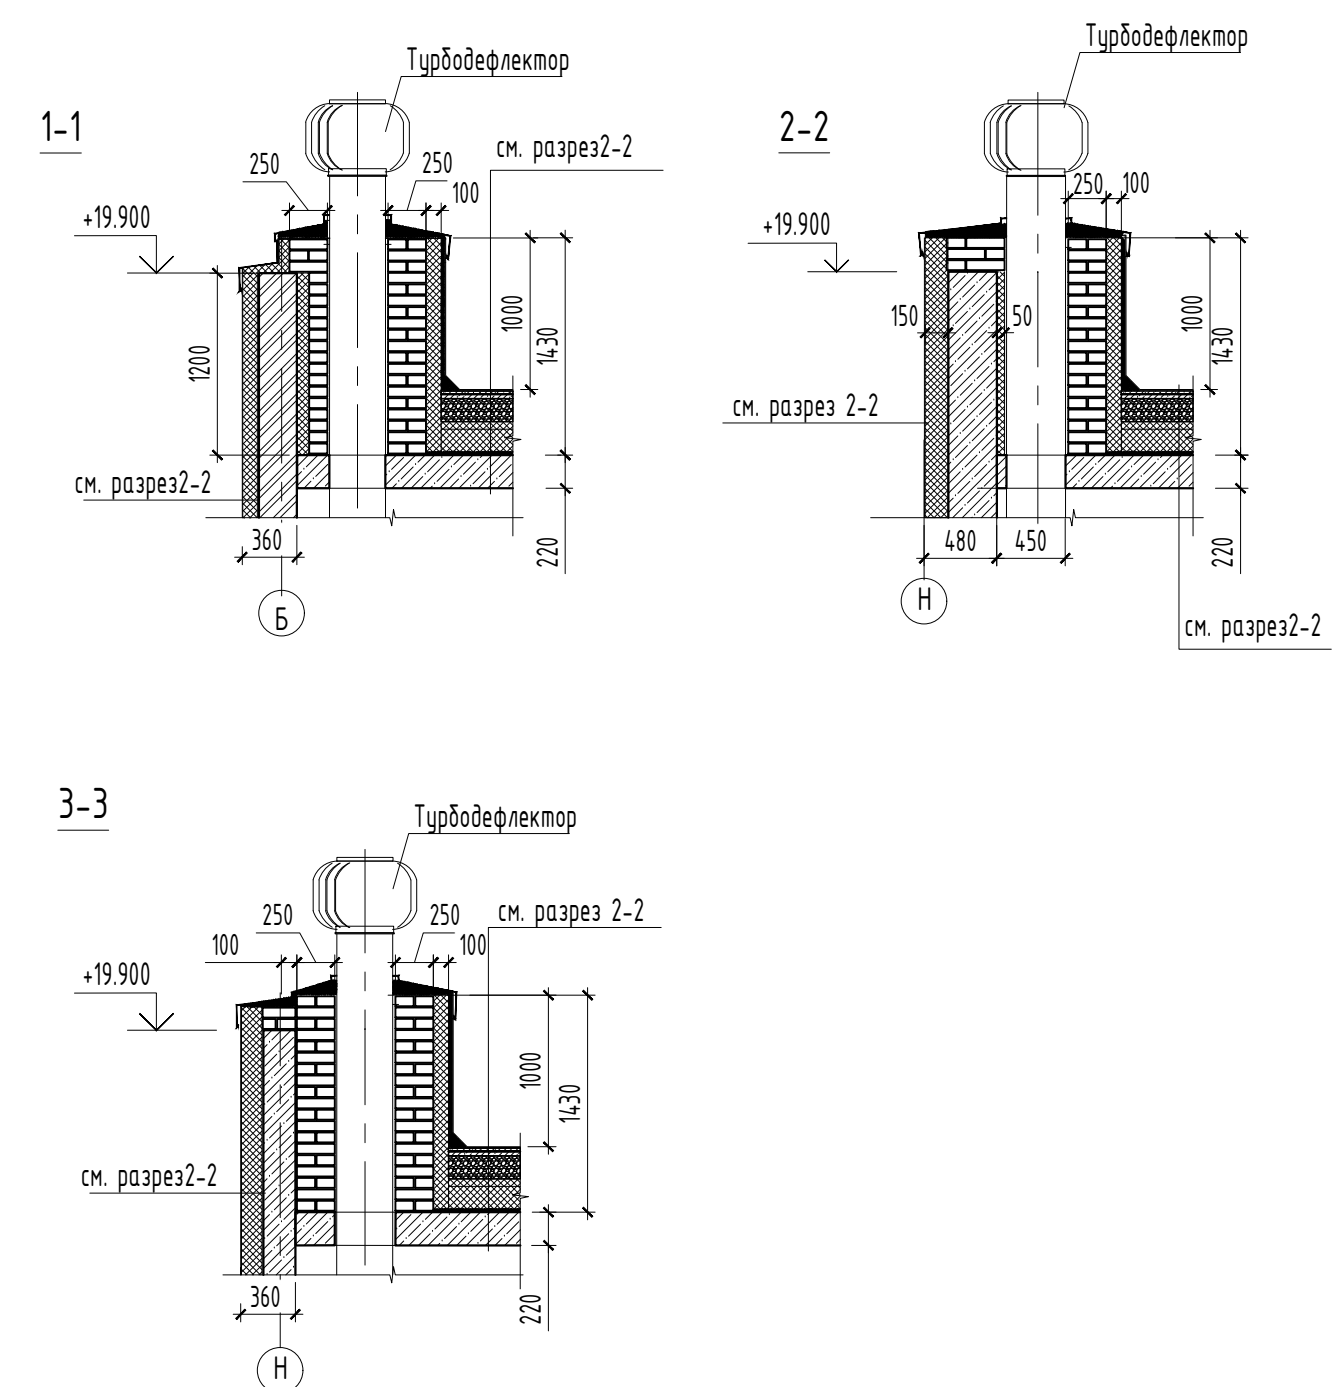

- Водосточная воронка (внутренний организованный водосток)
- Направление ската кровли к внутреннему организованному водостоку
- Бетонная продольная планка 500х300х50 с покрытием против скользящей морозостойкости
- Маркировка огнестойкости заменяемых дверей, окон, перегородок
- Отметка уровня пола этажа
- Отметка уровня кровли

1. Возможность устройства проемов в несущих стенах будет уточняться в проекте.
Размер и расположение вентиляционных шахт будет уточнен в проекте.
2. Шахты предназначены для прокладки инженерных коммуникаций и стоек (ВК, СС, ЗОМ), оборудованные люками для обслуживания.
3. ★ категорирование по взрывопожарной опасности данных помещений выполнить на этапе проектирования.
4. Марки ограждений смотреть альбом 16-25/Г-П-А лист 61

						16-25/Г-П-АР		
						Капитальный ремонт объекта ТБОУ Школа № 429 "Соколиная гора"		
						расположенного по адресу: г Москва, ул. Соколинкой гор 5-я, 6/1		
Изм.	Кол-во	Лист	№ док	Подпись	Дата			
Разработ			Литовских	<i>Литовских</i>	05.06.07			
						Архитектурно-планировочные решения		
						Страница	Лист	Листов
						Р		
						План кровли, М 1:100		
						 АЗУРИ		