


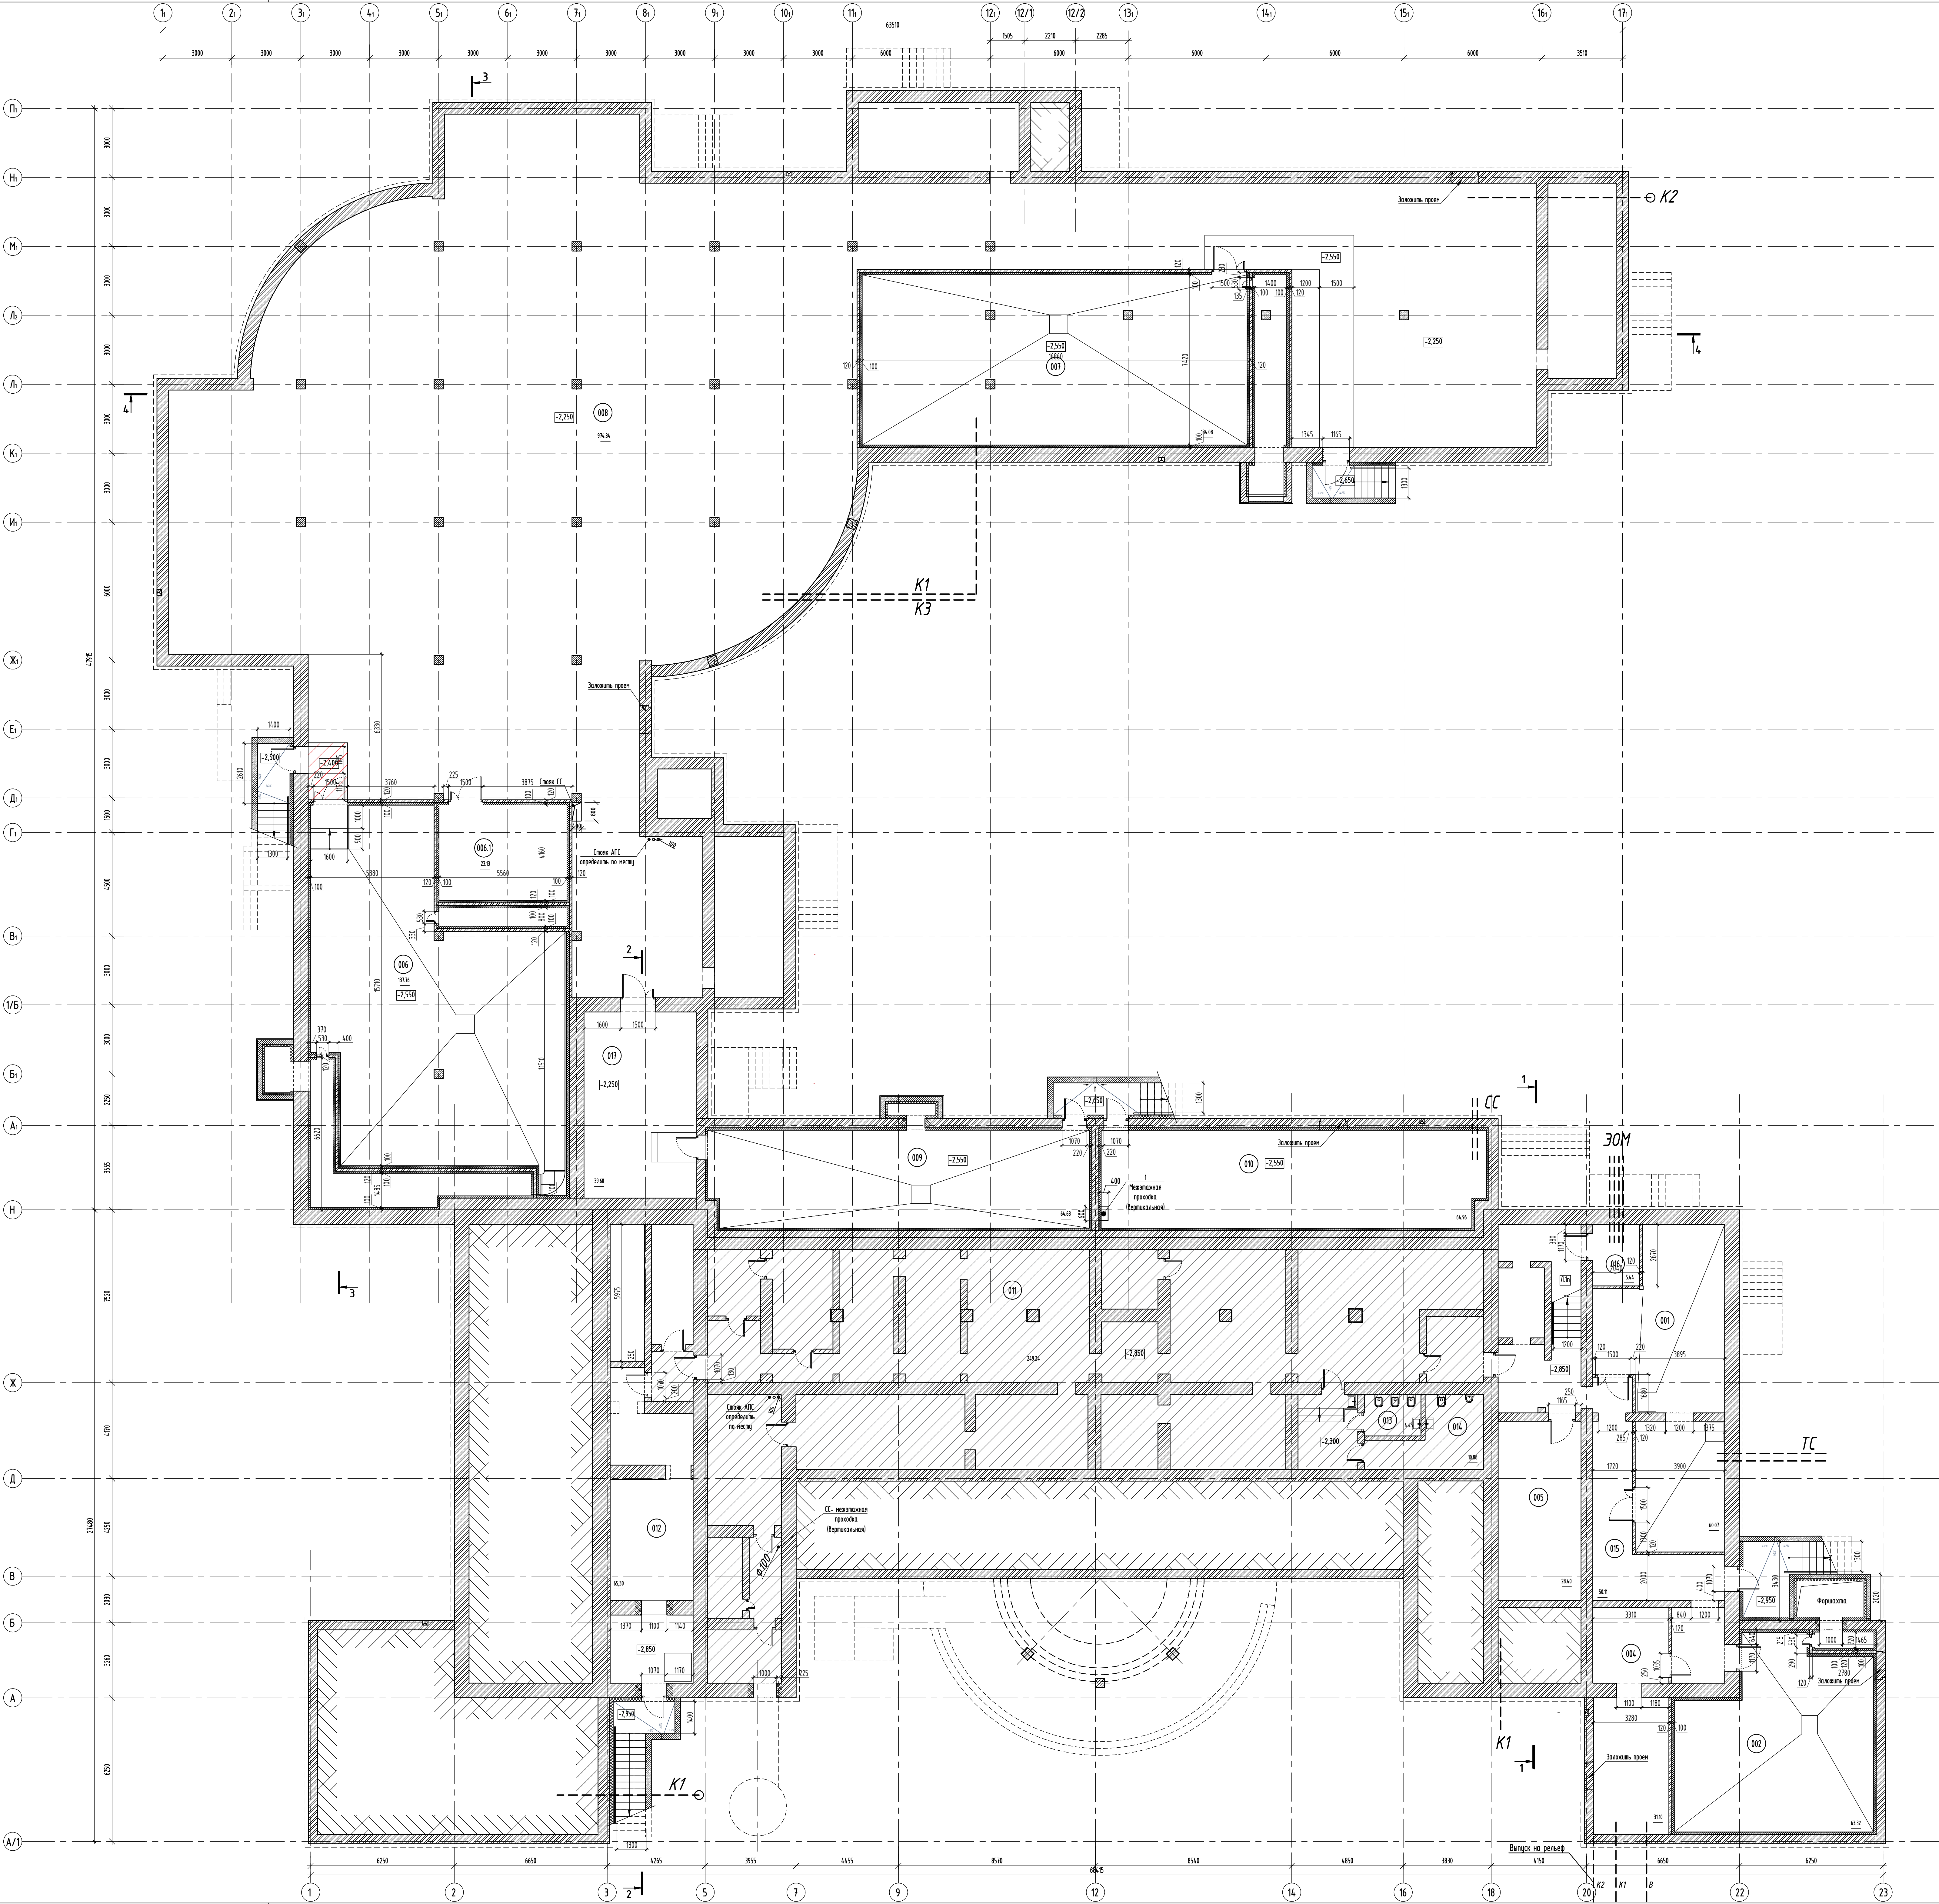


Экспликация помещений подвала

Номер помещения	Наименование	Площадь, м2	Кол. помещений
001	ИТП	60.07	Д
002	Вентилятор с форматором	63.32	В3
004	Водонапорный узел и насосная	31.10	Д
005	Техническое помещение	28.40	Д
006	Вентилятор	197.76	В3
006.1	Вентилятор систем приточной приточной вентиляции	23.03	Д
007	Вентилятор	138.94	В3
008	Техническое помещение для прокладки инженерных коммуникаций	974.84	В3
009	Вентилятор	64.68	В3
010	Техническое помещение	64.96	Д
011	Защитное помещение гражданской обороны	249.34	Д
012	Коридор	50.95	
013	Санитарная комната	10.88	
014	Санитарная комната	4.45	
015	Коридор	50.11	
016	Узел ввода электрических сетей	5.44	В4
017	Коридор	39.60	
Всего		1998.0	

УСЛОВНЫЕ ОБОЗНАЧЕНИЯ	
	- Существующие стены из полнотелого керамического кирпича
	- Занесение новых стен
	- Занесение дверных проемов из полнотелого кирпича 100мм, остекление
	- Номер помещения по экспликации
	- Маркировка оконности занесенных дверей
	- Плитка укладка пола
	- Помещение ГО ЧС
	- Пути эвакуации

- Возможность устройства проемов в несущих стенах будет уточняться в проекте. Разметка и расположение вентиляционных шахт будет уточнено в проекте.
- Шахты предназначены для прокладки инженерных коммуникаций и стояков (ВК, СС, ЗОМ), оборудуются лестницами для обслуживания.
- * Желательно рассмотреть возможность выполнения работ на этапе проектирования.
- Маркировка смотреть альбом 16-25/Г-П-АР лист 61

16-25/Г-П-АР	
Капитальный ремонт объекта "ГБОУ Школа № 429 "Соколовая гора", расположенного по адресу: г. Москва, ул. Соколовой горы 5-я, д. 14	
Имя (Фамилия)	Лист
Разработчик	Лист
Архитектурно-планировочные решения	Лист
И. номер	Губарева
Гип	Наркова
План подвала. М1:100	
АЗУРИТ	

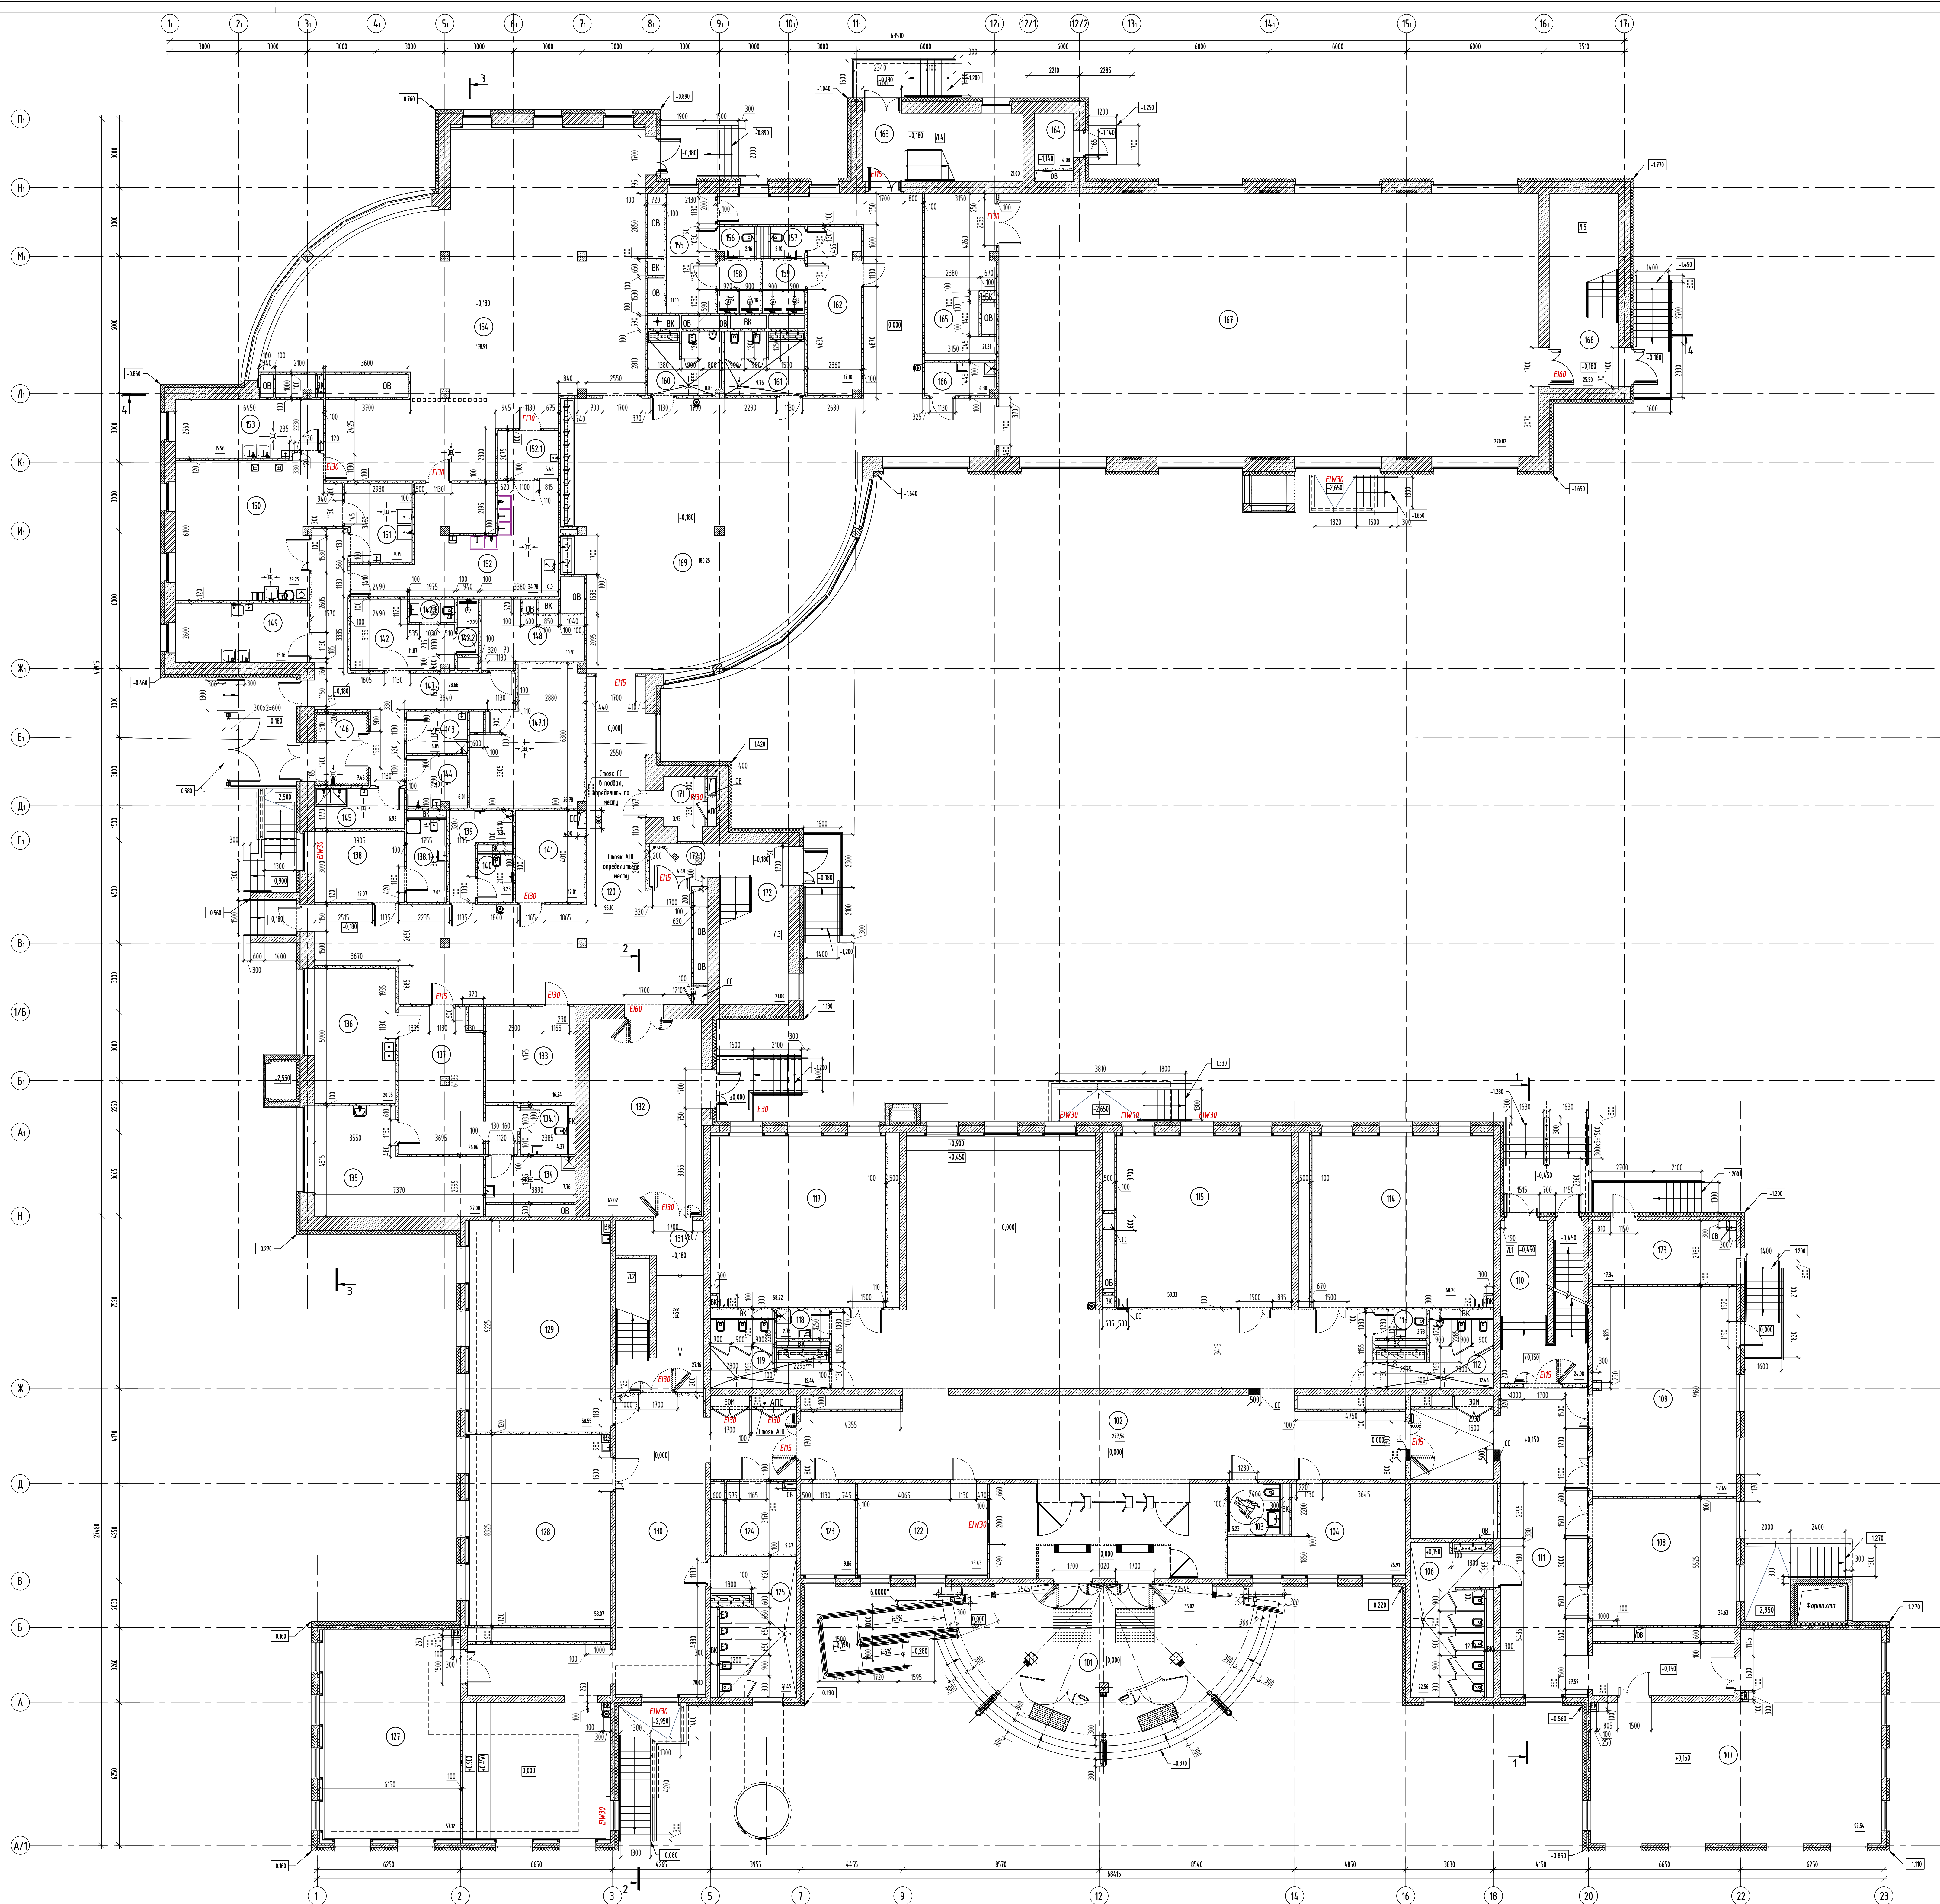


Код пометки	Наименование	Площадь, м2	Кол. помещений
101	Тюбюр	35,02	
102	Коридор с рекреацией	277,54	
103	Санитар для МН	5,33	
104	Административный кабинет тип 1 (начальная школа)	25,91	
106	Санитар для девочек (начальная школа)	27,25	
107	Гардеробная для обучающихся (основная и старшая школа)	93,54	
108	Гардеробная для обучающихся (основная и старшая школа)	35,25	
109	Гардеробная для обучающихся (начальная школа)	51,49	
110	Лестничная клетка (ЛК)	24,50	
111	Коридор	77,66	
112	Санитар для мальчиков (начальная школа)	12,44	
113	Санитар для персонала	2,78	
114	Чайные кабинеты (начальная школа)	60,20	
115	Чайные кабинеты (начальная школа)	58,33	
117	Чайные кабинеты (начальная школа)	58,22	
118	ПМН	2,38	84
119	Санитар для девочек (начальная школа)	12,44	
120	Коридор с рекреацией (основная и старшая школа)	95,10	
122	Комната спорт (с диспетчерским пунктом)	23,43	
123	Гардеробная комната (для учителей)	9,86	
124	Помещение связи	9,47	84
125	Санитар для мальчиков (начальная школа)	21,73	
127	Чайные кабинеты (начальная школа)	57,26	
128	Чайные кабинеты (начальная школа)	53,71	
129	Чайные кабинеты (начальная школа)	58,81	
130	Коридор с рекреацией	117,57	
131	Лестничная клетка Тип Н2	27,38	
132	Вестибюль	42,82	
133	Электрощитовая	16,24	83
134	Участок для производства дезинфекционных растворов и хранения уборочного инвентаря, предназначенные для помещений медицинского назначения	7,76	84
134.1	Туалет медблока	4,31	
135	Кабинет врача	21,00	
136	Процедурный (трибунный) кабинет	78,88	
137	Коридор	28,06	
138	Комната инструментов	12,87	
138.1	Санитар с душем	7,83	
139	ПМН	6,79	84
140	Санитар для персонала	3,27	
141	Помещение связи	11,07	83
142	Помещение для персонала	12,61	
142.1	Санитар для персонала	2,01	
142.2	Душевые	2,09	
143	ПМН	4,85	84
144	Помещение для временного хранения пищевых отходов	6,01	84
145	Клиппинг и мясочная оборотной тары	6,92	84
146	Защитный цех	7,45	84
147	Коридор	28,66	
147.1	Помещение с холодильным оборудованием	26,78	83
148	Клиппинг суши продуктов	18,81	83
149	Дозвоночный цех	10,16	83
150	Горячий цех	39,25	83
151	Мясочная для крупающей посуды	9,75	81
152	Мясочная для стейкобойной посуды	34,48	84
152.1	Предварочная	5,48	81
153	Холодный цех	15,96	83
154	Обеденный зал	118,91	
155	Раздевальня для мальчиков	17,10	
156	Санитар для мальчиков	2,16	
157	Санитар для девочек	2,30	
158	Душевые для мальчиков	4,15	
159	Душевые для девочек	4,45	
160	Санитар для мальчиков	8,71	
161	Санитар для девочек	9,76	
162	Раздевальня для девочек	17,10	
163	Лестничная клетка (ЛК)	21,00	
164	Техническое помещение	4,16	84
165	Сараица	21,21	83
166	ПМН	4,30	84
167	Экспериментальный спортивный зал	278,82	
168	Лестничная клетка (ЛК)	25,60	
169	Коридор с рекреацией (основная и старшая школа)	281,24	
171	Тех. помещения	3,93	84
172	Лестничная клетка (ЛК)	21,00	
172.1	Тюбюр	4,48	
173	Электрощитовая	17,34	83
Всего		2667,3	

	-Существующие моющие х/б стены
	-Зачистка перегородки из азбестовых блоков 1625х25х100/1500х85 по ГОСТ Р 19532-2022, пола на клею с приклеиванием базальтовой сетки, штукатурка
	-Зачистка перегородки из азбестовых блоков 1625х25х100/1500х85 по ГОСТ Р 19532-2022, пола на клею с приклеиванием базальтовой сетки, штукатурка
	-Зачистка перегородки из облицовки односторонней эмали толщиной 10мм
	-Зачистка перегородки из облицовки односторонней эмали толщиной 10мм
	-Зачистка оштукатуренных перегородки
	-Зачистка перегородки синтетическая (пластиковая) с обшивкой необходимой фурнитурой

1. Возможность устройства проемов в несущих стенах будет уточняться в проекте.
- Размер и расположение вентиляционных шахт будет уточнен в проекте.
2. Шахты предназначены для прокладки инженерных коммуникаций и стяжков (ВК, СС, ЗОМ), оборудуются лючками для обслуживания.
3. ★ категорирование по взрывопожарной опасности данных помещений выполнить на этапе проектирования.
4. Марки ограждений смотреть альбом 16-25/1 -П-А лист 61

						16-25/Г-П-АР		
						Капитальный ремонт объекта "БООУ Школа № 429 "Соколовая гора", расположенного по адресу: г.Москва, ул. Соколовой горы 5-я д.14		
Им.	Лист	Лист	№ док.	Подпись	Дата			
Разреш.	Лист	Лист	№ док.	Подпись	Дата			
					20.06.2018			
						Архитектурно-планировочные решения		
						Страница		
						р		
						Лист		
						Лист		
Им. контр.	Губарев				20.06.2018			
Гип.	Морозов				20.06.2018			
						Лист 1 из 3. М.1010		
						 АЗУРИТ		

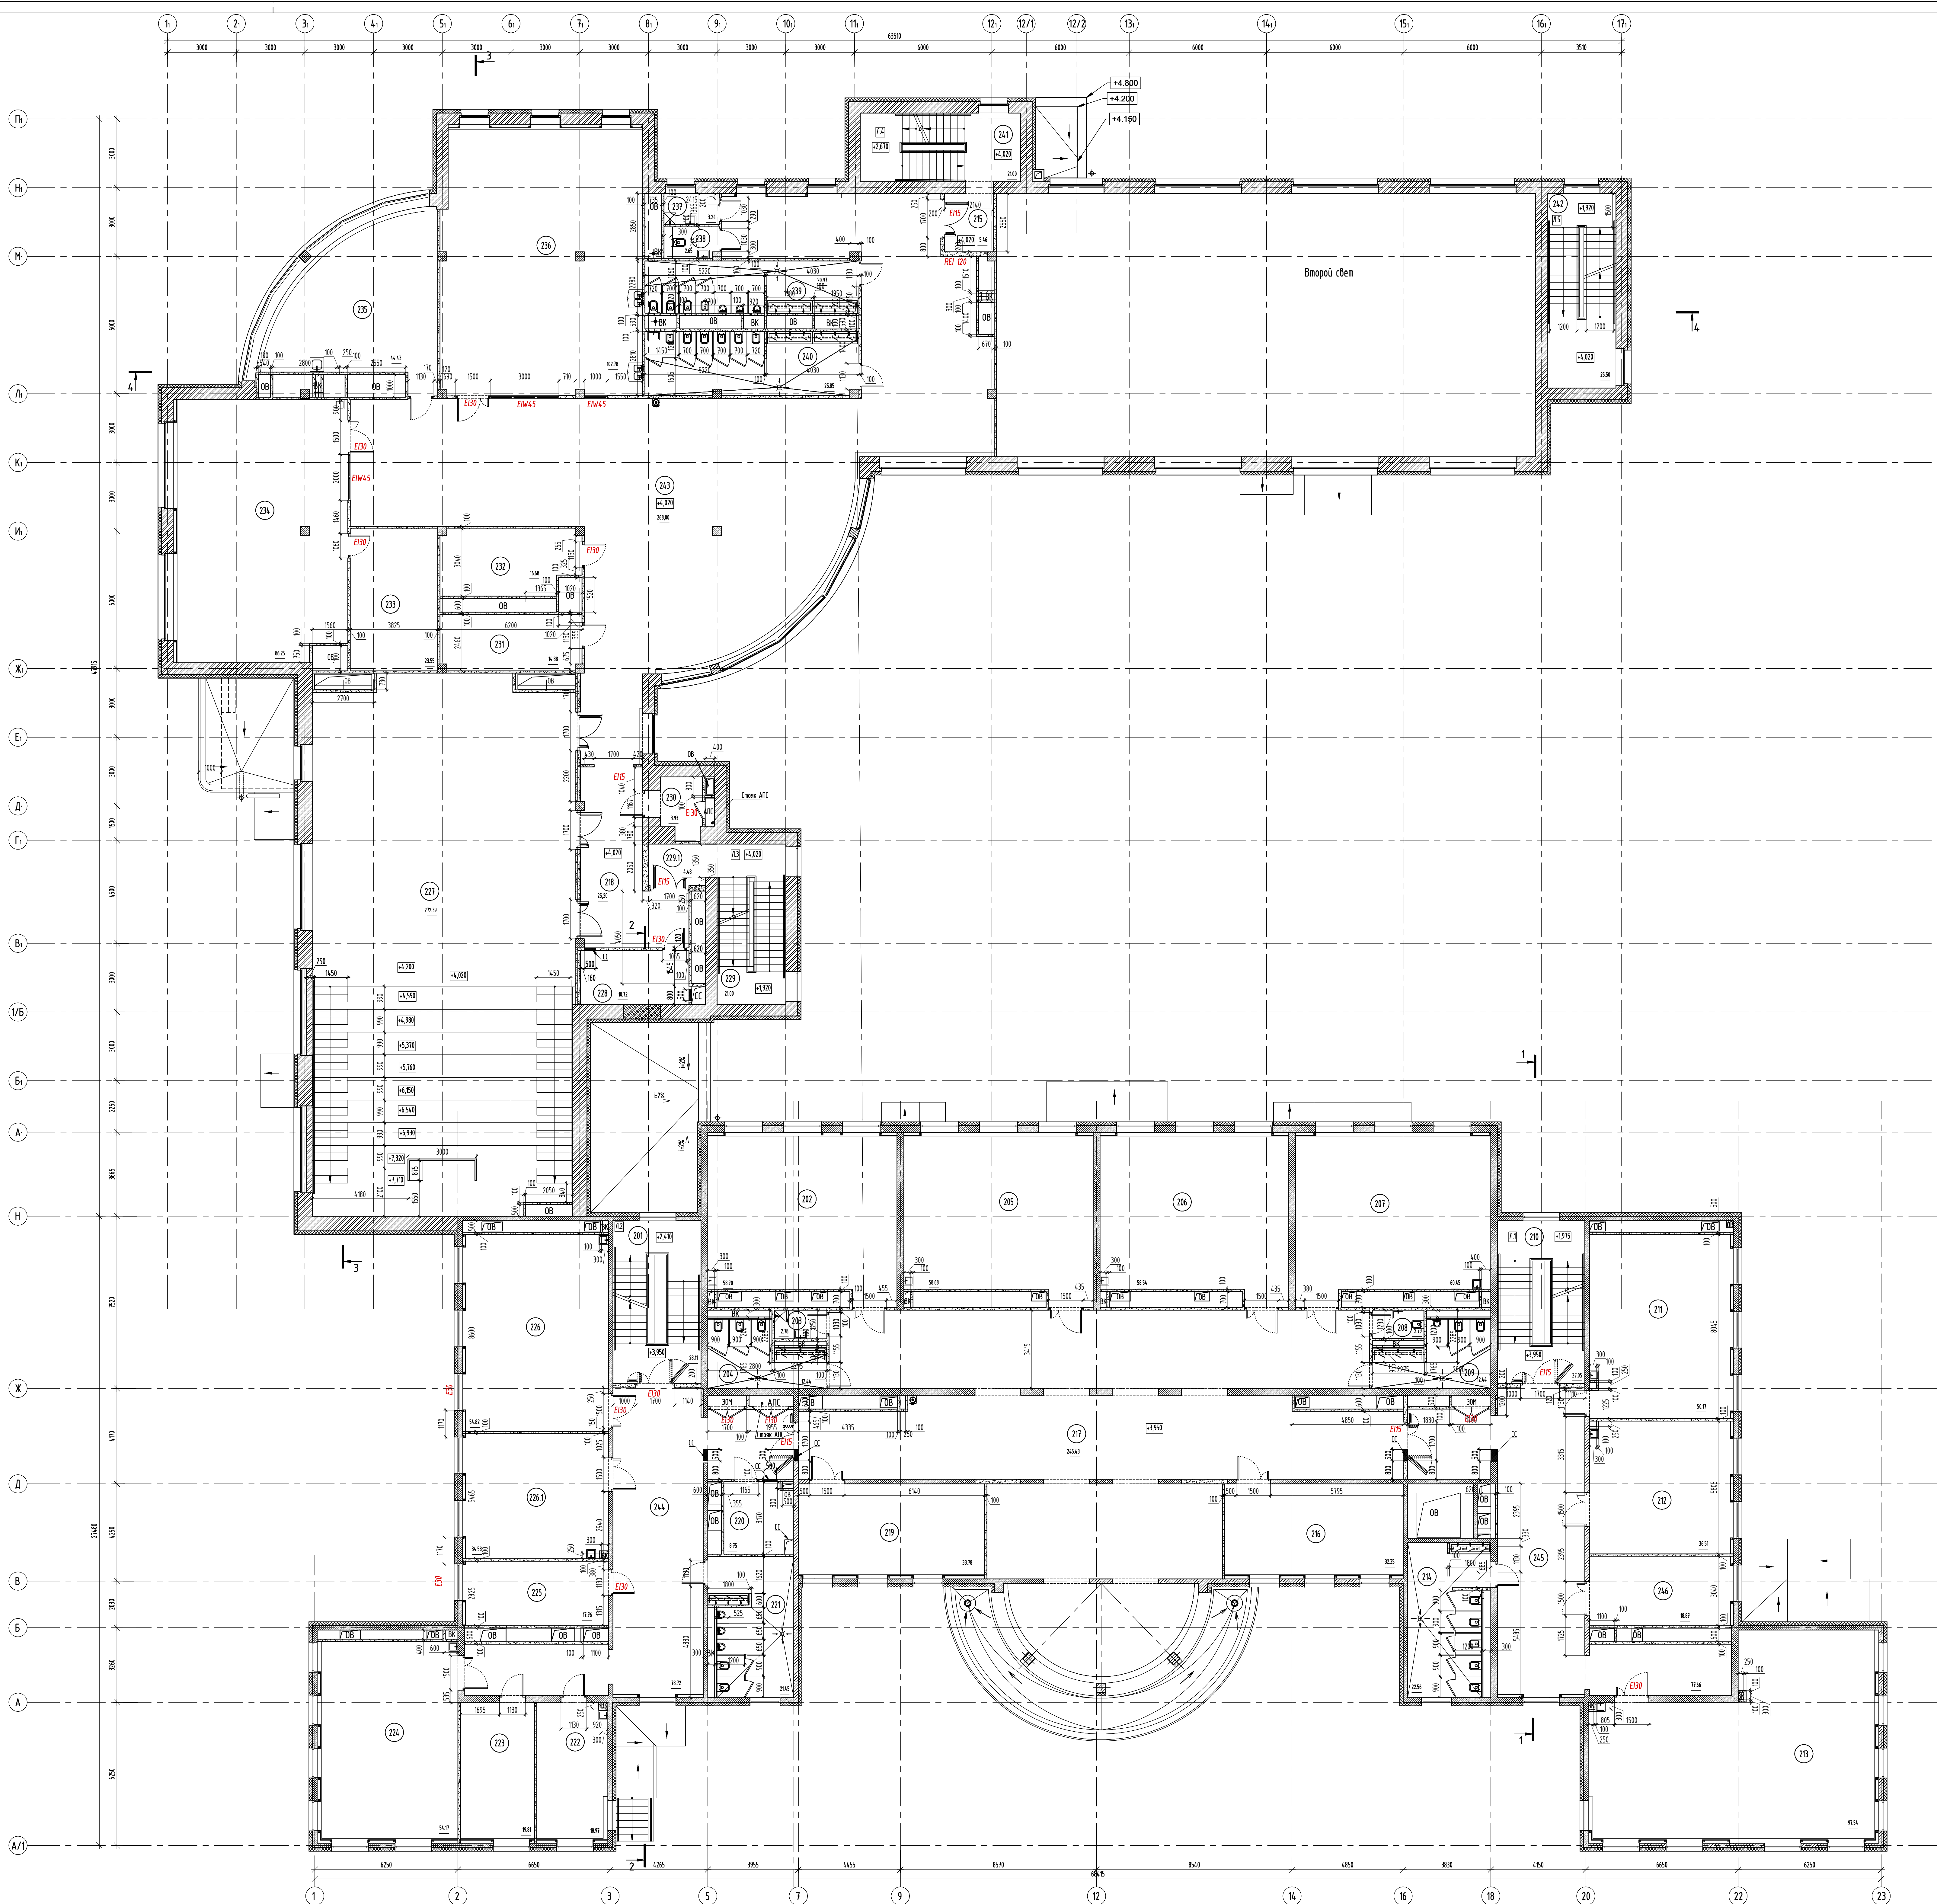


Экспликация помещений 2-го этажа			
Номер помещения	Наименование	Площадь, м ²	Кол. помещений
201	Лестничная клетка Тип Н2	2882	
202	Учебные кабинеты (начальная школа)	5870	
203	ПМ	278	84
204	Спальня для девочек (начальная школа)	1273	
205	Учебные кабинеты (начальная школа)	5688	
206	Учебные кабинеты (начальная школа)	5854	
207	Учебные кабинеты (начальная школа)	6045	
208	Спальня для персонала	279	
209	Спальня для мальчиков (начальная школа)	1244	
210	Лестничная клетка (ЛП)	2705	
211	Учебные кабинеты (начальная школа)	5617	
212	Кабинет иностранного языка (начальная школа)	50,51	
213	Лаборатория-исследовательский комплекс для изучения естественных наук	5702	83
214	Спальня для девочек (начальная школа)	2325	
215	Тюбик	146	
216	Кабинет для индивидуальных занятий с малой группой	3235	
217	Коридор с рекреацией (начальная школа)	2454,43	
218	Коридор	25,20	
219	Кабинет для индивидуальных занятий с малой группой	3378	
220	Помещение (физ)	875	84
221	Спальня для мальчиков (начальная школа)	2145	
222	Кабинет для индивидуальных занятий, 6 кв. с учителем-координатором	18,91	
223	Кабинет для индивидуальных занятий, 6 кв. с коррекционным педагогом	19,22	
224	Учебные кабинеты (начальная школа)	51,75	
225	Кабинет информатики (начальная школа)	16,37	83
226	Техническая мастерская	54,82	83
226.1	Кабинет иностранного языка (начальная школа)	34,58	
227	Мультифункциональное пространство с функцией выставочного зала (с экспозицией в учебном плане)	272,39	
228	Коридор	10,72	83
229	Помещение	21,00	
229.1	Тюбик	4,48	
230	Тех. помещение	3,93	84
231	Артистическая	14,75	
232	Кабинет информатики	16,85	83
233	Кабинет кабинета материальной технологии	23,55	83
234	Кабинет материальной технологии тип 2	66,65	83
235	Кабинет с рабочим пространством для учителей тип 1 (начальная школа)	14,23	
236	Кабинет материальной технологии тип 1	102,78	83
237	ПМ	33,34	84
238	Спальня для персонала	2,65	
239	Спальня для мальчиков (основная и старшая школа)	20,97	
240	Спальня для девочек с комнатой личной гигиены (основная и старшая школа)	25,85	
241	Лестничная клетка (ЛП)	21,00	
242	Лестничная клетка (ЛП)	25,00	
243	Коридор с рекреацией (основная и старшая школа)	268,20	
244	Коридор	78,72	
245	Коридор	17,66	
246	Административный кабинет	12,85	
		Всего	2745,3

УСЛОВНЫЕ ОБОЗНАЧЕНИЯ

- [illegible]




1. Возможность устройства проемов в несущих стенах будет уточняться в проекте.
- Размер и расположение вентиляционных шахт будет уточнен в проекте.
2. Шахты предназначение для прокладки инженерных коммуникаций и стояков (ВК, СС, ЗОМ) оборудуются лючками для обслуживания.
3. * категорирование по взрывопожарной опасности данных помещений выполнить на этапе проектирования.
4. Марки ограждений смотреть альбом 16-25/Г-П-АР лист 61

								16-25/Г-П-АР		
							Капитальный ремонт объекта "БСОУ Школа № 429 "Скопальная горка", расположенного по адресу: г Москва, ул Скопальной горы 5-в, д 14.			
Изм	Вкл	Лист	№ Док	Подпись	Дата	Архитектурно-планировочные решения				
Разработ		Литовская			29.04.16	Р		Листов		
Н. киндр		Григорьев			29.04.16	План 2 этажа. М:100				
Г. Маров					29.04.16					

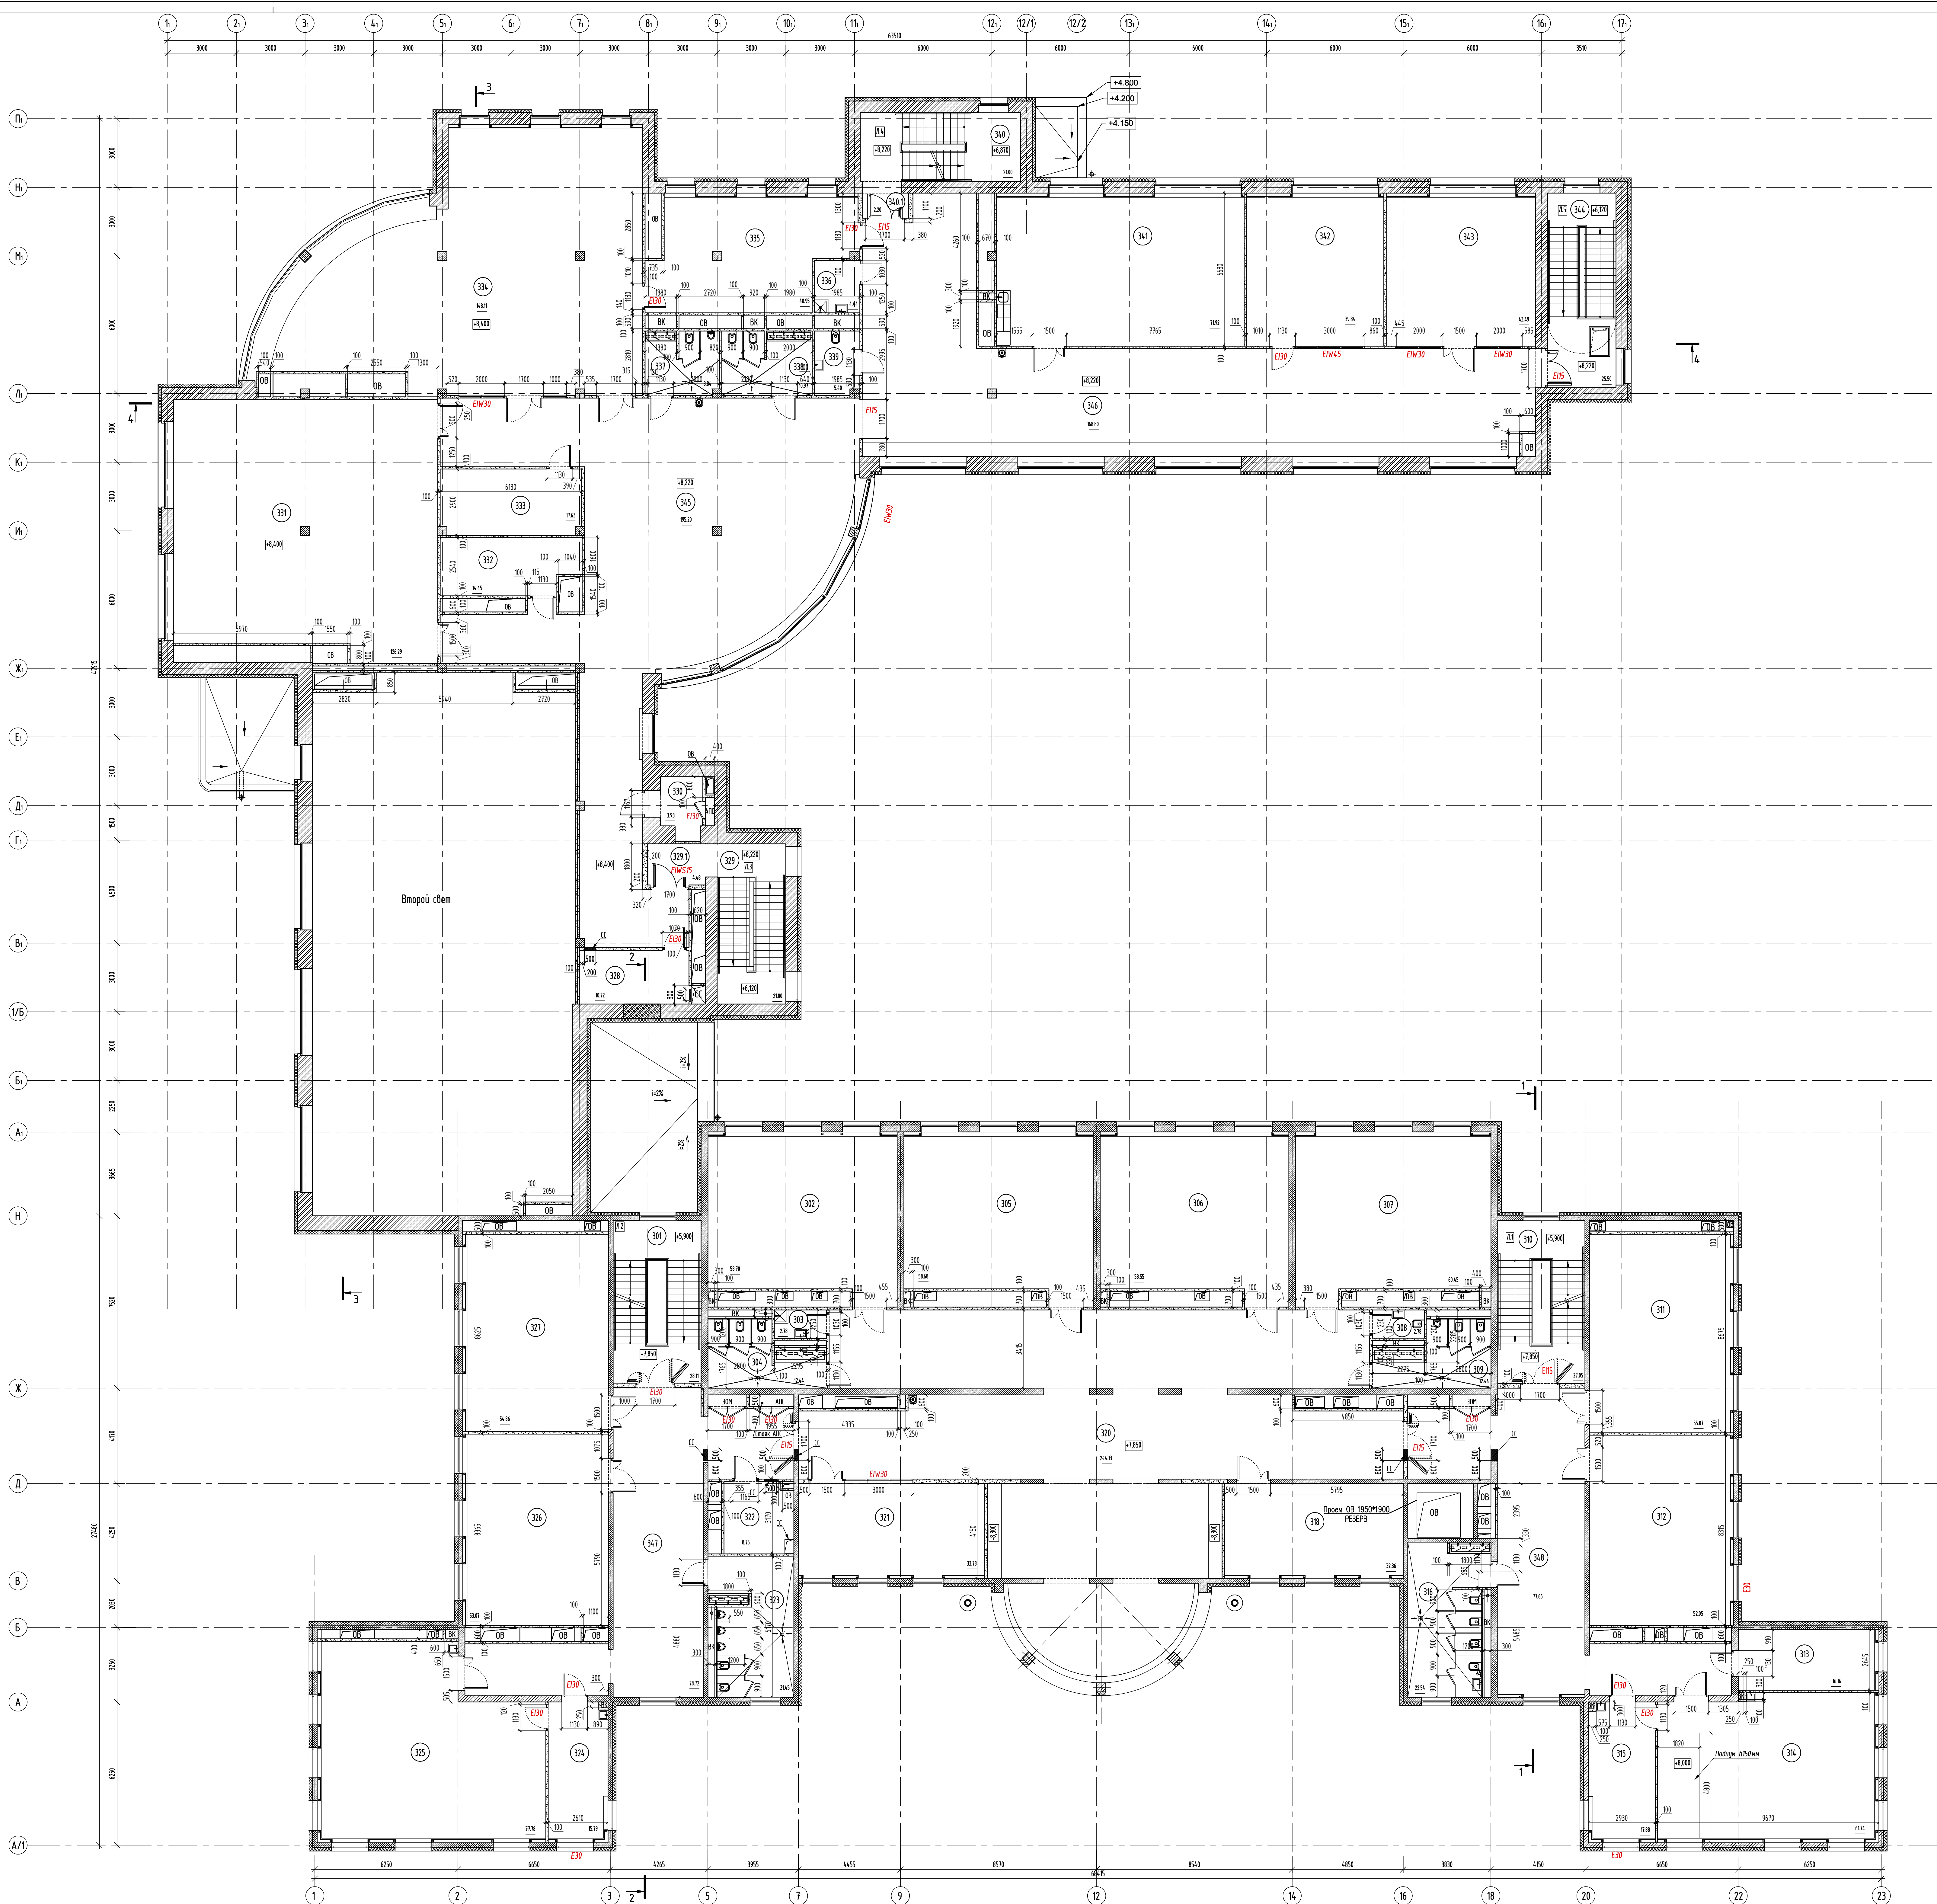


Экспликация помещений 3-го этажа			
Номер помещения	Наименование	Площадь, м2	Кол. помещ. в я
301	Лестничная клетка Тип ИЭ	28,82	
302	Кабинет русского языка и литературы	58,70	
303	ПМ	2,78	84
304	Специал. для девочек (основная и старшая школа)	12,44	
305	Кабинет русского языка и литературы	58,68	
306	Кабинет математики	58,55	
307	Кабинет математики	60,45	
308	Специал. для персонала	2,75	
309	Специал. для мальчиков (основная и старшая школа)	12,44	
310	Лестничная клетка (ЛП)	27,85	
311	Кабинет географии	55,07	
312	Универсальный учебный кабинет	56,05	
313	Кабинет для индивидуальных занятий, 6 в.ч. с медико-психологом	16,16	
314	Учебный кабинет для изучения естественных физики	61,02	
315	Лабортанская кабинет физики	18,82	83
316	Специал. для девочек с конной личной гигиены (основная и старшая школа)	73,25	
317	Подсобное помещение	6,64	84
318	Кабинет иностранного языка (основная и старшая школа)	32,36	
320	Корridor / рекреация	244,13	
321	Кабинет иностранного языка (основная и старшая школа)	33,18	
322	Помещение связи	8,75	84
323	Специал. для мальчиков (основная и старшая школа)	21,73	
324	Лабортанская кабинета биологии	55,93	
325	Учебный кабинет для изучения естественных: биология - ОБЗ	75,98	
326	Универсальный учебный кабинет	53,07	
327	Кабинет истории тип I	54,86	
328	Кроссовая	10,72	83
329	Лестничная клетка (ЛП)	21,00	
329.1	Тайндр	4,48	
330	Тех. помещение	3,93	84
331	Универсальное помещение с возможностью организации лингвистического зала (рекреация)	125,19	
332	Разделочная	14,45	
333	Разделочная	17,63	
334	Информационный информационный библиотечный центр с зоной для индивидуальных занятий	452,15	
335	Информационный информационный библиотечный центр (хранение (архивный фонд) / выдачи книг)	15,15	83
336	ПМ	4,44	84
337	Специал. для мальчиков (основная и старшая школа)	10,84	
338	Специал. для девочек (основная и старшая школа)	8,97	
339	Специал. для персонала	2,40	
340	Лестничная клетка (ЛП)	51,00	
340.1	Тайндр	21,20	
341	Кабинет с рабочим пространством для учителей Тип I (основная и старшая школа)	7,92	
342	Универсальное помещение с возможностью организации Медиацентра	39,84	83
343	Помещение музея	43,49	
344	Лестничная клетка (ЛП)	25,50	
345	Корridor / рекреация (основная и старшая школа)	195,20	
346	Корridor / рекреация (основная и старшая школа)	168,80	
347	Корridor	78,72	
348	Корridor	77,66	
		Всего	2246,3

УСЛОВНЫЕ ОБОЗНАЧЕНИЯ

 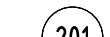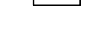- | | |
|---|---|
|  | - Установка металлических я/з стено |
|  | - Замена/ремонт перегородки из железобетонных блоков |
|  | -1/625/25х100/1050/85,0 по ГОСТ Р 7652-2002, толщиной 100мм
на кле с армированием базальтовой сеткой, опущенными |
|  | -Замена/ремонт перегородки из железобетонных блоков |
|  | -1/625/25х100/1050/85,0 по ГОСТ Р 7652-2002, толщиной 200мм
на кле с армированием базальтовой сеткой, опущенными |
|  | -Замена/ремонт перегородки из облицовки одностворчатые двустворчатые на все типы, толщиной 100мм |
|  | -Замена/ремонт перегородки из облицовки одностворчатые двустворчатые до 90, толщиной 100мм |
|  | -Замена/ремонт откосов перегородки |
|  | |
|  | -Замена/ремонт перегородки сантехническая (водостойкая) с дверью и необходимой фурнитурой |
|  | |
|  | -Монтаж помещения по эксплуатации |
|  | |
|  | -Отметка уровня пола эстака |
|  | -Маркировка окон/дверей/перегородки |

1. Возможность устройства проемов в несущих стенах будет уточняться в проекте.
- Размер и расположение вентиляционных шахт будет уточнен в проекте.
2. Шахты предназначены для прокладки инженерных коммуникаций и стояков (ВК, СС, ЭОМ, оборудуются лючками для обслуживания).
3. * калеворобование по взрывопожарной опасности данных помещений выполнить на этапе проектирования.
4. Марки ограждений смотреть альбом 16-25/Г-П-АР лист 61

					16-25/П -П-АР		
					Капитальный ремонт объекта "ТБОУ Школа № 429 "Скоковская гора", расположенного по адресу: г. Москва, ул. Скоковской горы 5-в, д.14		
Изм.	Кол. л.	Лист	№ док.	Подпись	Дата		
Разработ.		Литовских			2020.07.07		
Архитектурно-планировочные решения						Станд.	Лист
							Листов
И. команд.		Григорьев			2020.07.07		
Н. проект.		Григорьев			2020.07.07		
План 3 этажа. М1:100							

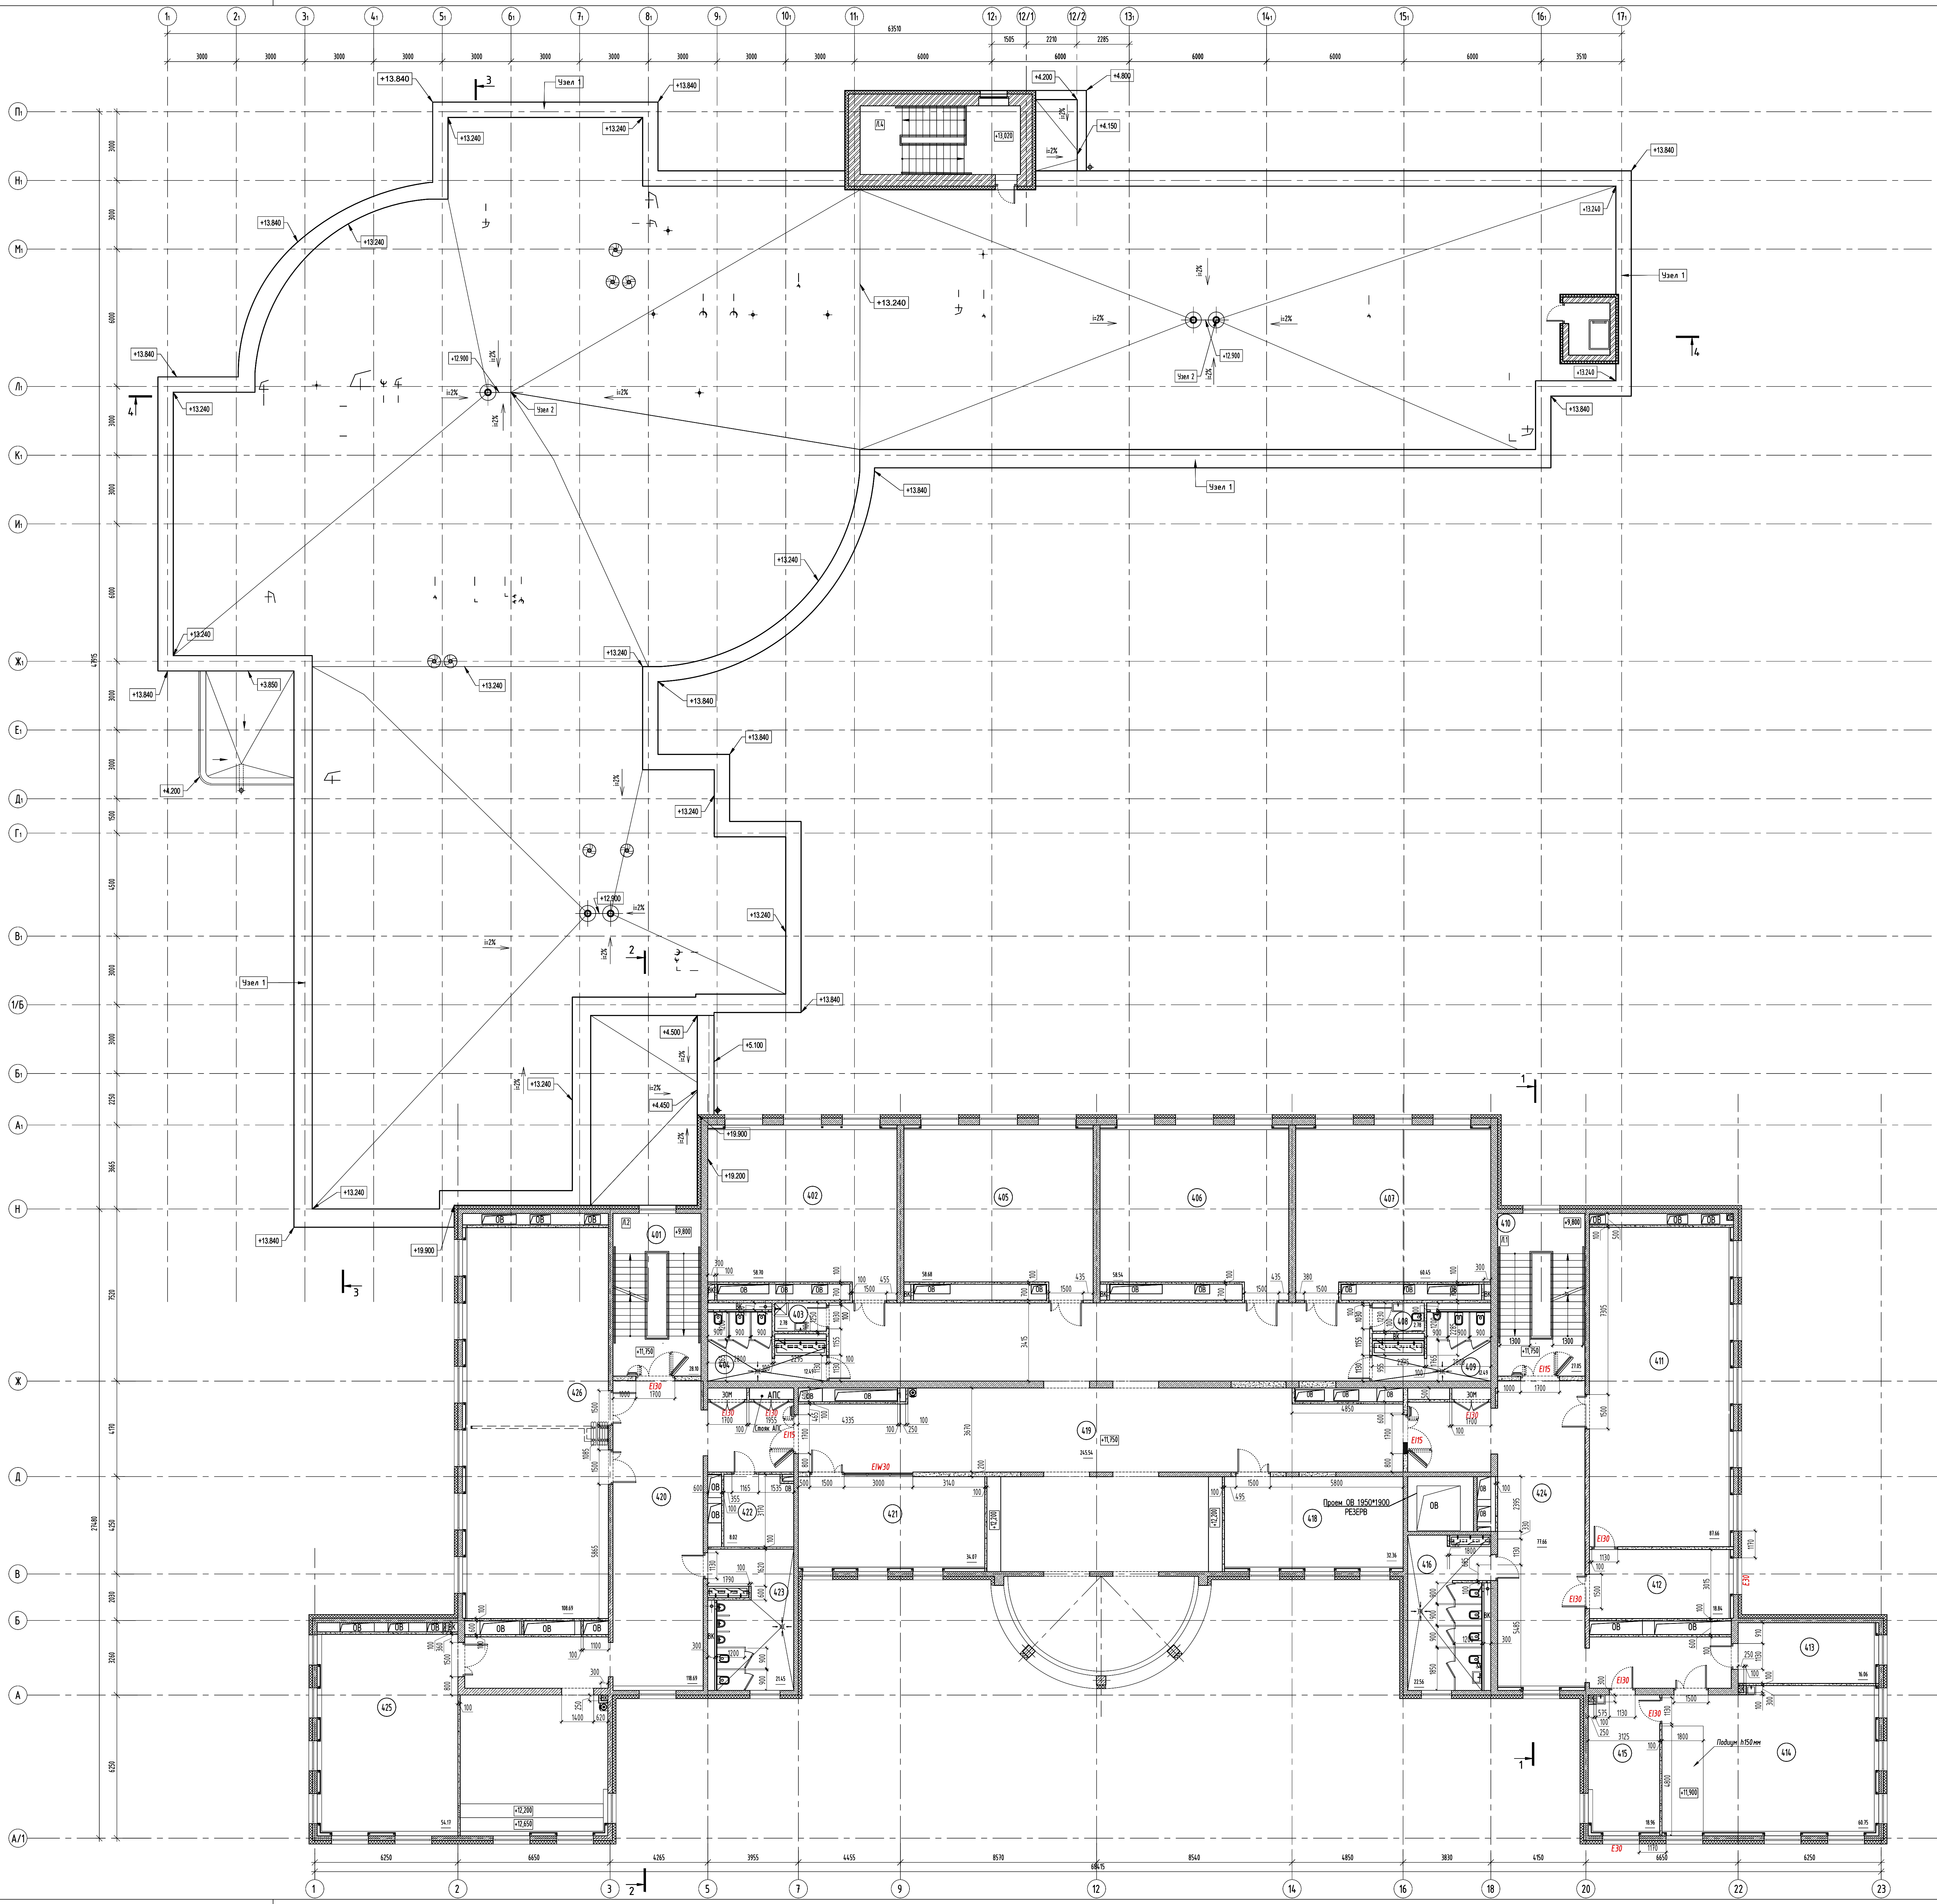

Экспликация помещений 4-го этажа

Номер помещения	Наименование	Площадь, м2	Кол. помещ.
401	Лестничная клетка Тип Н2	28.81	
402	Кабинет русского языка и литературы	58.70	
403	ПМ	2.78	В4
404	Санитар для девочек (основная и старшая школа)	12.49	
405	Кабинет русского языка и литературы	58.68	
406	Кабинет математики	58.54	
407	Кабинет математики	60.45	
408	Санитар для персонала	2.78	
409	Санитар для мальчиков (основная и старшая школа)	12.49	
410	Лестничная клетка (П)	26.98	
411	Кабинет информационных технологий	87.66	
412	Лаборантская при кабинете информационных технологий	18.84	В3
413	Административный кабинет тип 1 (основная и старшая школа)	16.03	
414	Учебные кабинеты для изучения естественных наук	60.75	
415	Лаборантская кабинета химии	18.96	В3
416	Санитар для девочек с комнатой личной гигиены (основная и старшая школа)	22.56	
417	Подсобная помещения	7.30	В4
418	Кабинет иностранного языка (основная и старшая школа)	32.36	
419	Коридор с ретерацией	245.54	
420	Коридор с ретерацией	108.69	
421	Кабинет иностранного языка (основная и старшая школа)	34.07	
422	Помещение связи	8.02	В4
423	Санитар для мальчиков (основная и старшая школа)	21.45	
424	Коридор	77.66	
425	Кабинет истории Тип 1	54.17	
426	Кабинет информатики с базисными данными трансформированной переработкой на два помещения	108.69	
427	Лестничная клетка (П)	21.00	
428	Помещение выхода на крышу	4.18	
Всего		1276.5	

УСЛОВНЫЕ ОБОЗНАЧЕНИЯ

- Существующие стены
- Замена перегородки из газобетонных блоков 1/625x250x100/050/050 по ГОСТ Р 7552-2012, толщиной 100мм на клею с армированием базальтовой сеткой, оштукатуренная
- Замена перегородки из газобетонных блоков 1/625x250x100/050/050 по ГОСТ Р 7552-2012, толщиной 200мм на клею с армированием базальтовой сеткой, оштукатуренная
- Замена перегородки из гипсокартона одностороннее обустройство на все выступы этажа толщиной 10мм
- Замена перегородки из гипсокартона одностороннее обустройство во уг. раковины толщиной 10мм
- Замена осветительные перегородки
- Замена перегородки синтетическая (влагостойкая) с дверью и необходимой фурнитурой
- Номер помещения по экспликации
- Отметка уровня пола этажа
- Маркировка геометрии замененных дверей, окон, перегородок

- Возможность устройства проемов в несущих стенах будет уточняться в проекте. Размер и расположение вентиляционных шахт будет уточнен в проекте.
- Шахты предназначены для прокладки инженерных коммуникаций и стоек (ВК, СС, ЗОМ), оборудуются лестницами для обслуживания.
- * категоризирование по взрывопожарной опасности данных помещений выполнять на этапе проектирования.
- Марки ограждений стен отбоя 16-25/Г-П-АР лист 61

				16-25/Г-П-АР		
				Капитальный ремонт объекта "ГБОУ Школа № 429 "Скопальная гора", расположенная по адресу: г. Москва, ул. Скопальной горы 5-я, д. 14		
И.п.	Кол.л.	Лист	№ док.	Подпись	Дата	Статус
Разработ		Литовская				
Архитектурно-планировочные решения				Стадия	Лист	Листов
				Р		
И.п. номер	Губарева			План 4 этажа. М1:100		
Гип	Наркова			АЗУРИТ		



Номер помещения	Наименование	Площадь м2	Кол. помещ.
501	Лесничная клетка Тип Н2	27.26	
502	Лесничная клетка Тип Л1	27.05	
503	Венткамера 1	43.07	В3
504	Венткамера 2	44.09	В3
505	Техническое помещение	206.11	В3
СЛС	Техническая подстанция	155.46	В3

УСЛОВНЫЕ ОБОЗНАЧЕНИЯ

- [illegible]

1. Возможность устройства проемов в несущих стенах будет уточняться в проекте.
2. Размер и расположение вентиляционных шахт будет уточнен в проекте.
3. Шахты предназначение для прокладки инженерных коммуникаций и стоек (ВК, СС, ЗОМ) оборудуются лючками для обслуживания.
4. * категорирование по взрывопожарной опасности данных помещений выполнить на этапе проектирования.
4. Марки ограждений смотреть альбом 16-25/Г-П-АР лист 61

						16-25/Г-П-АР								
						Капитальный ремонт объекта "БООУ Школа № 429 "Соколовая гора", расположенного по адресу: г. Москва, ул. Соколовой горы 5-в, д.14								
						Архитектурно-планировочные решения								
						<table><tr><td>Страница</td><td>Лист</td><td>Листов</td></tr><tr><td>р</td><td></td><td></td></tr></table>			Страница	Лист	Листов	р		
Страница	Лист	Листов												
р														
Изм.	Кол. в.	Листы	№ док.	Подпись	Дата									
Разреш.		Литовская		<i>Литовская</i>	20.06.2018									
И. к. инв.	К. инв.	Губарева		<i>Губарева</i>	20.06.2018									
Генп.		Морозова		<i>Морозова</i>	20.06.2018									
						Лист тех. записка. М.1100								
						 AZURIT								