


План 2 этажа

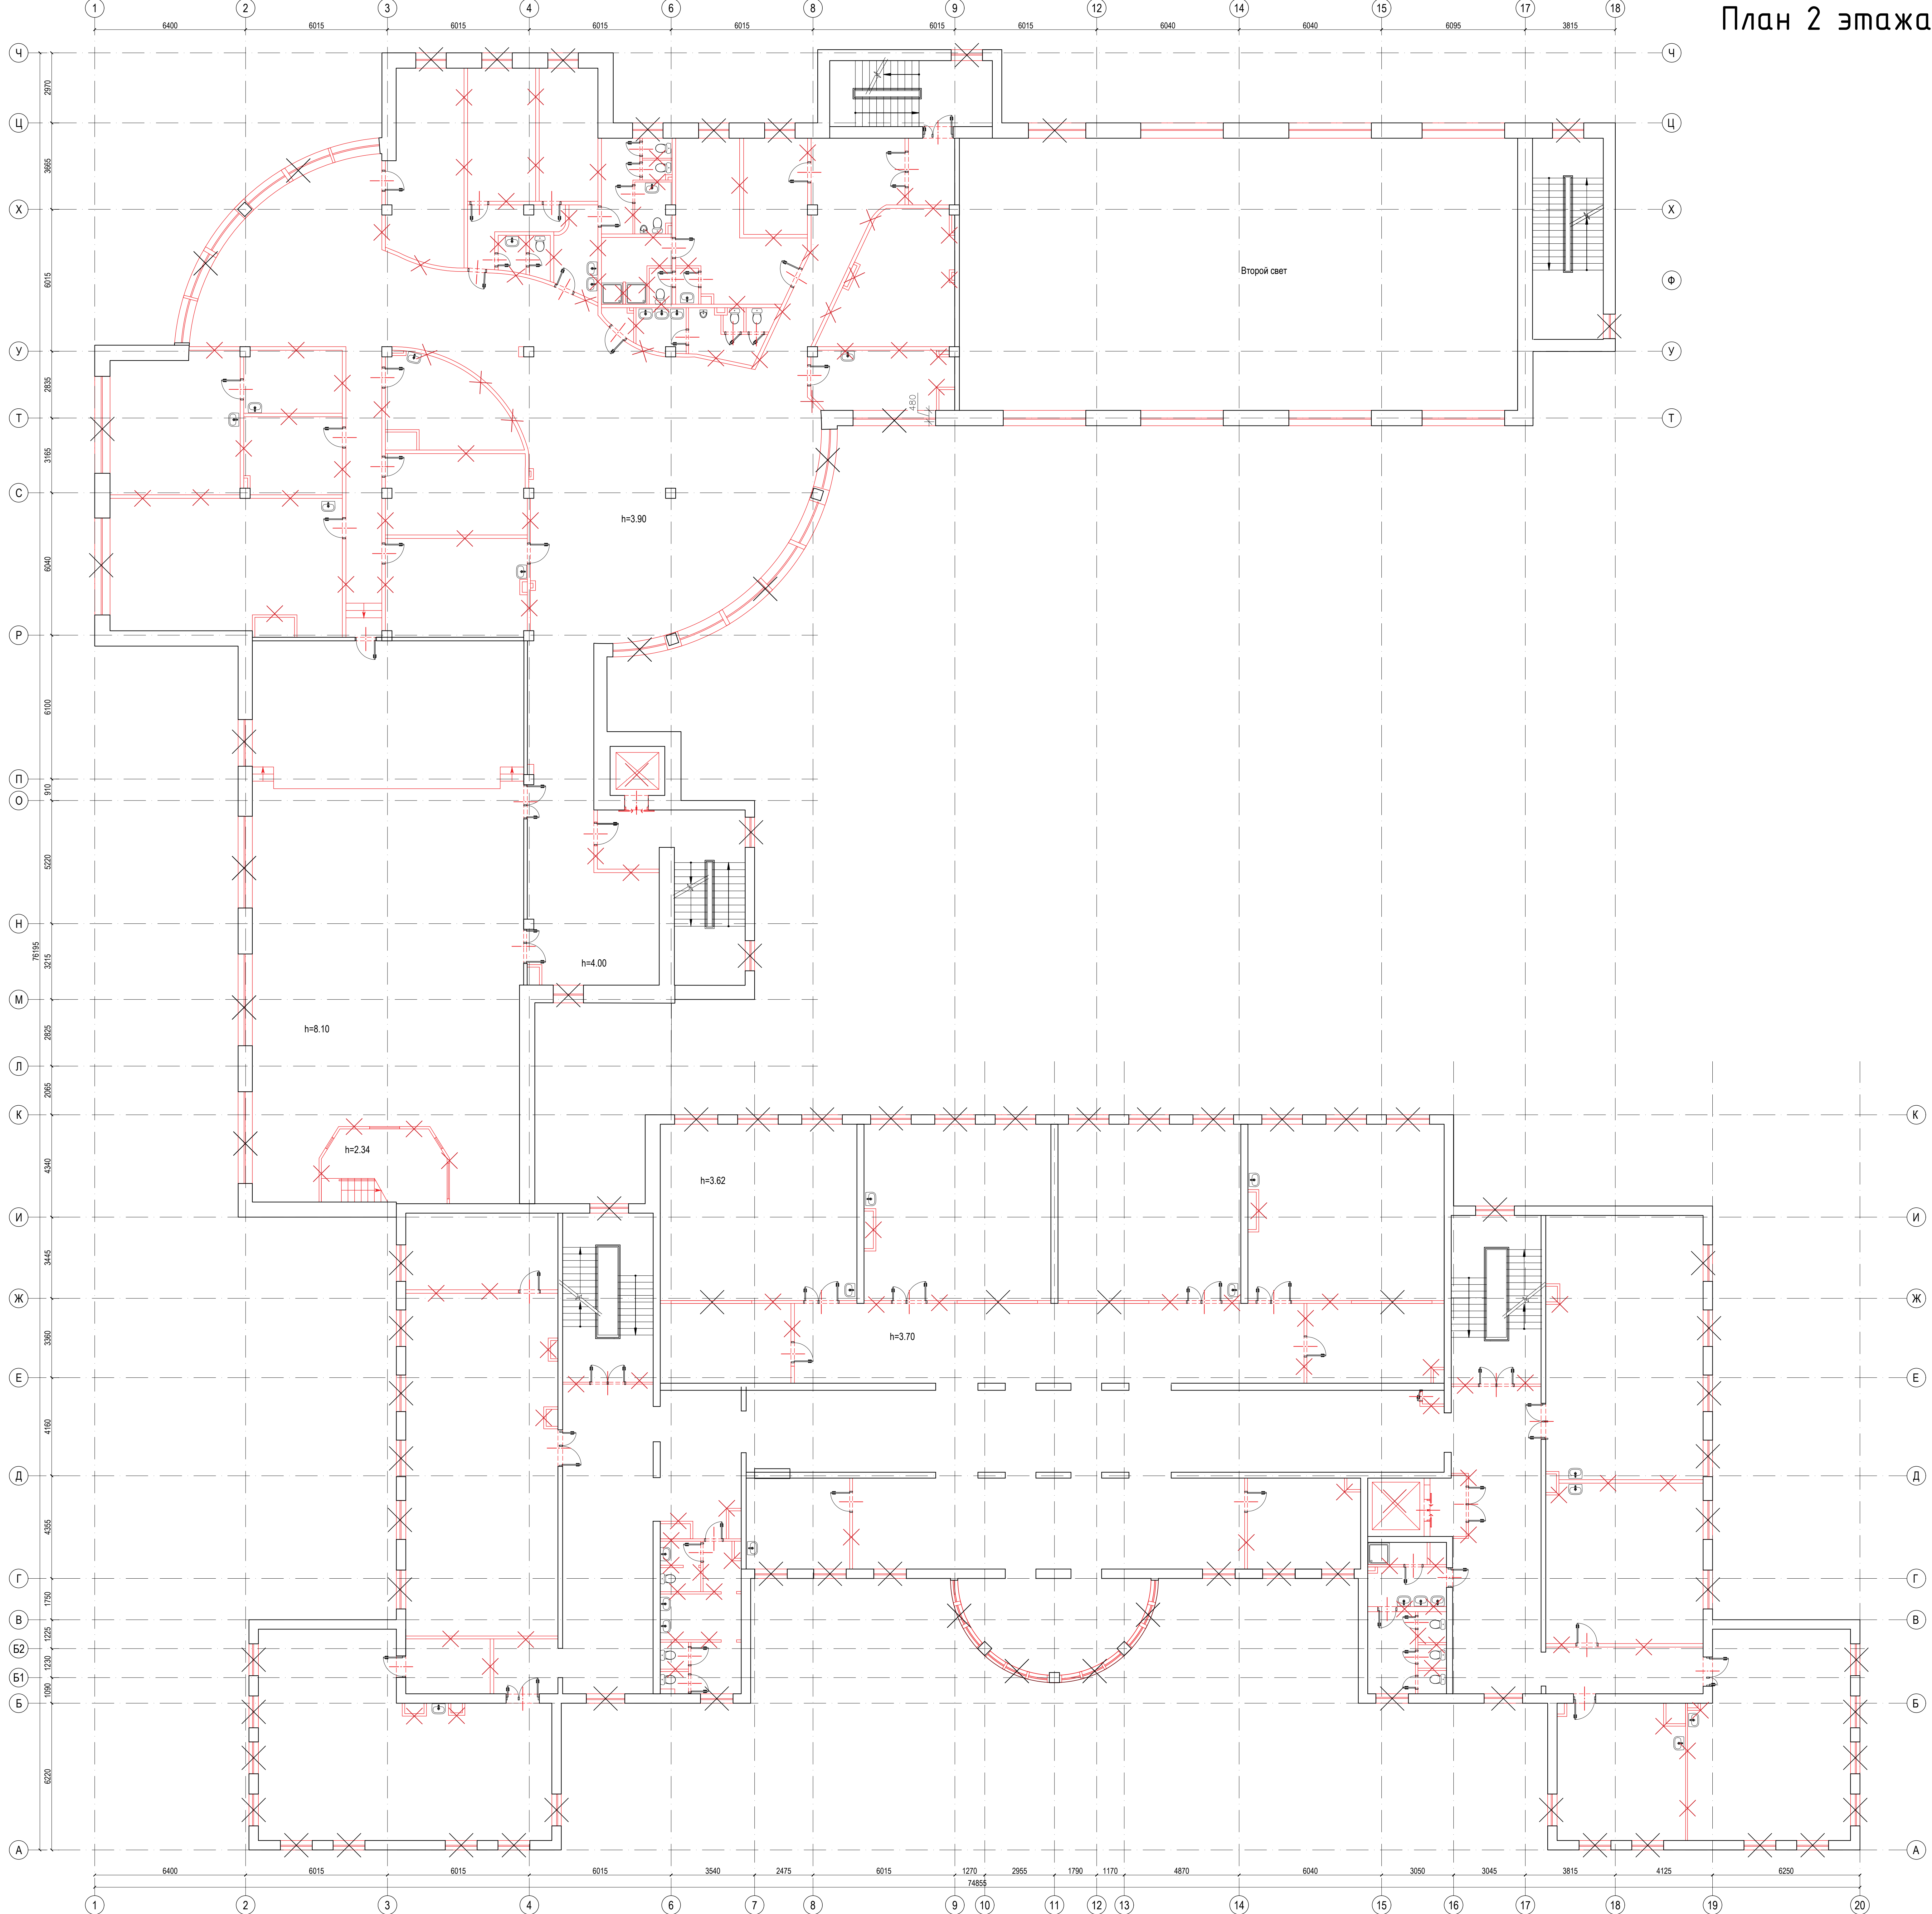

Условные обозначения:

- сохраняемые несущие конструкции
- демонтаж витражей
- демонтаж оконных блоков
- демонтаж внутренних окон и витражей
- демонтаж перегородок
- демонтаж внутренних дверных блоков
- демонтаж наружных дверных блоков
- разбираемые конструкции
- демонтаж стен под проем
- демонтаж лифта

					16-25/Г-П-АР							
					Капитальный ремонт общеобразовательного учреждения (ГБОУ "Школа №429", расположенного по адресу: г. Москва, 5-ая ул. Соколиной Горы, д.14)							
Изм.	Кол.уч.	Лист	№ док.	Подпись								
Разработ	Набородская				2016 г.				Склад	Лист	Листов	
ГЛАВ	Лавровская				2016 г.				П	3		
Н. контр.	Губарева				2016 г.				План демонтажа 2 этажа. М1:500			
Генп	Маркова				2016 г.				ФОРМАТ А0			