


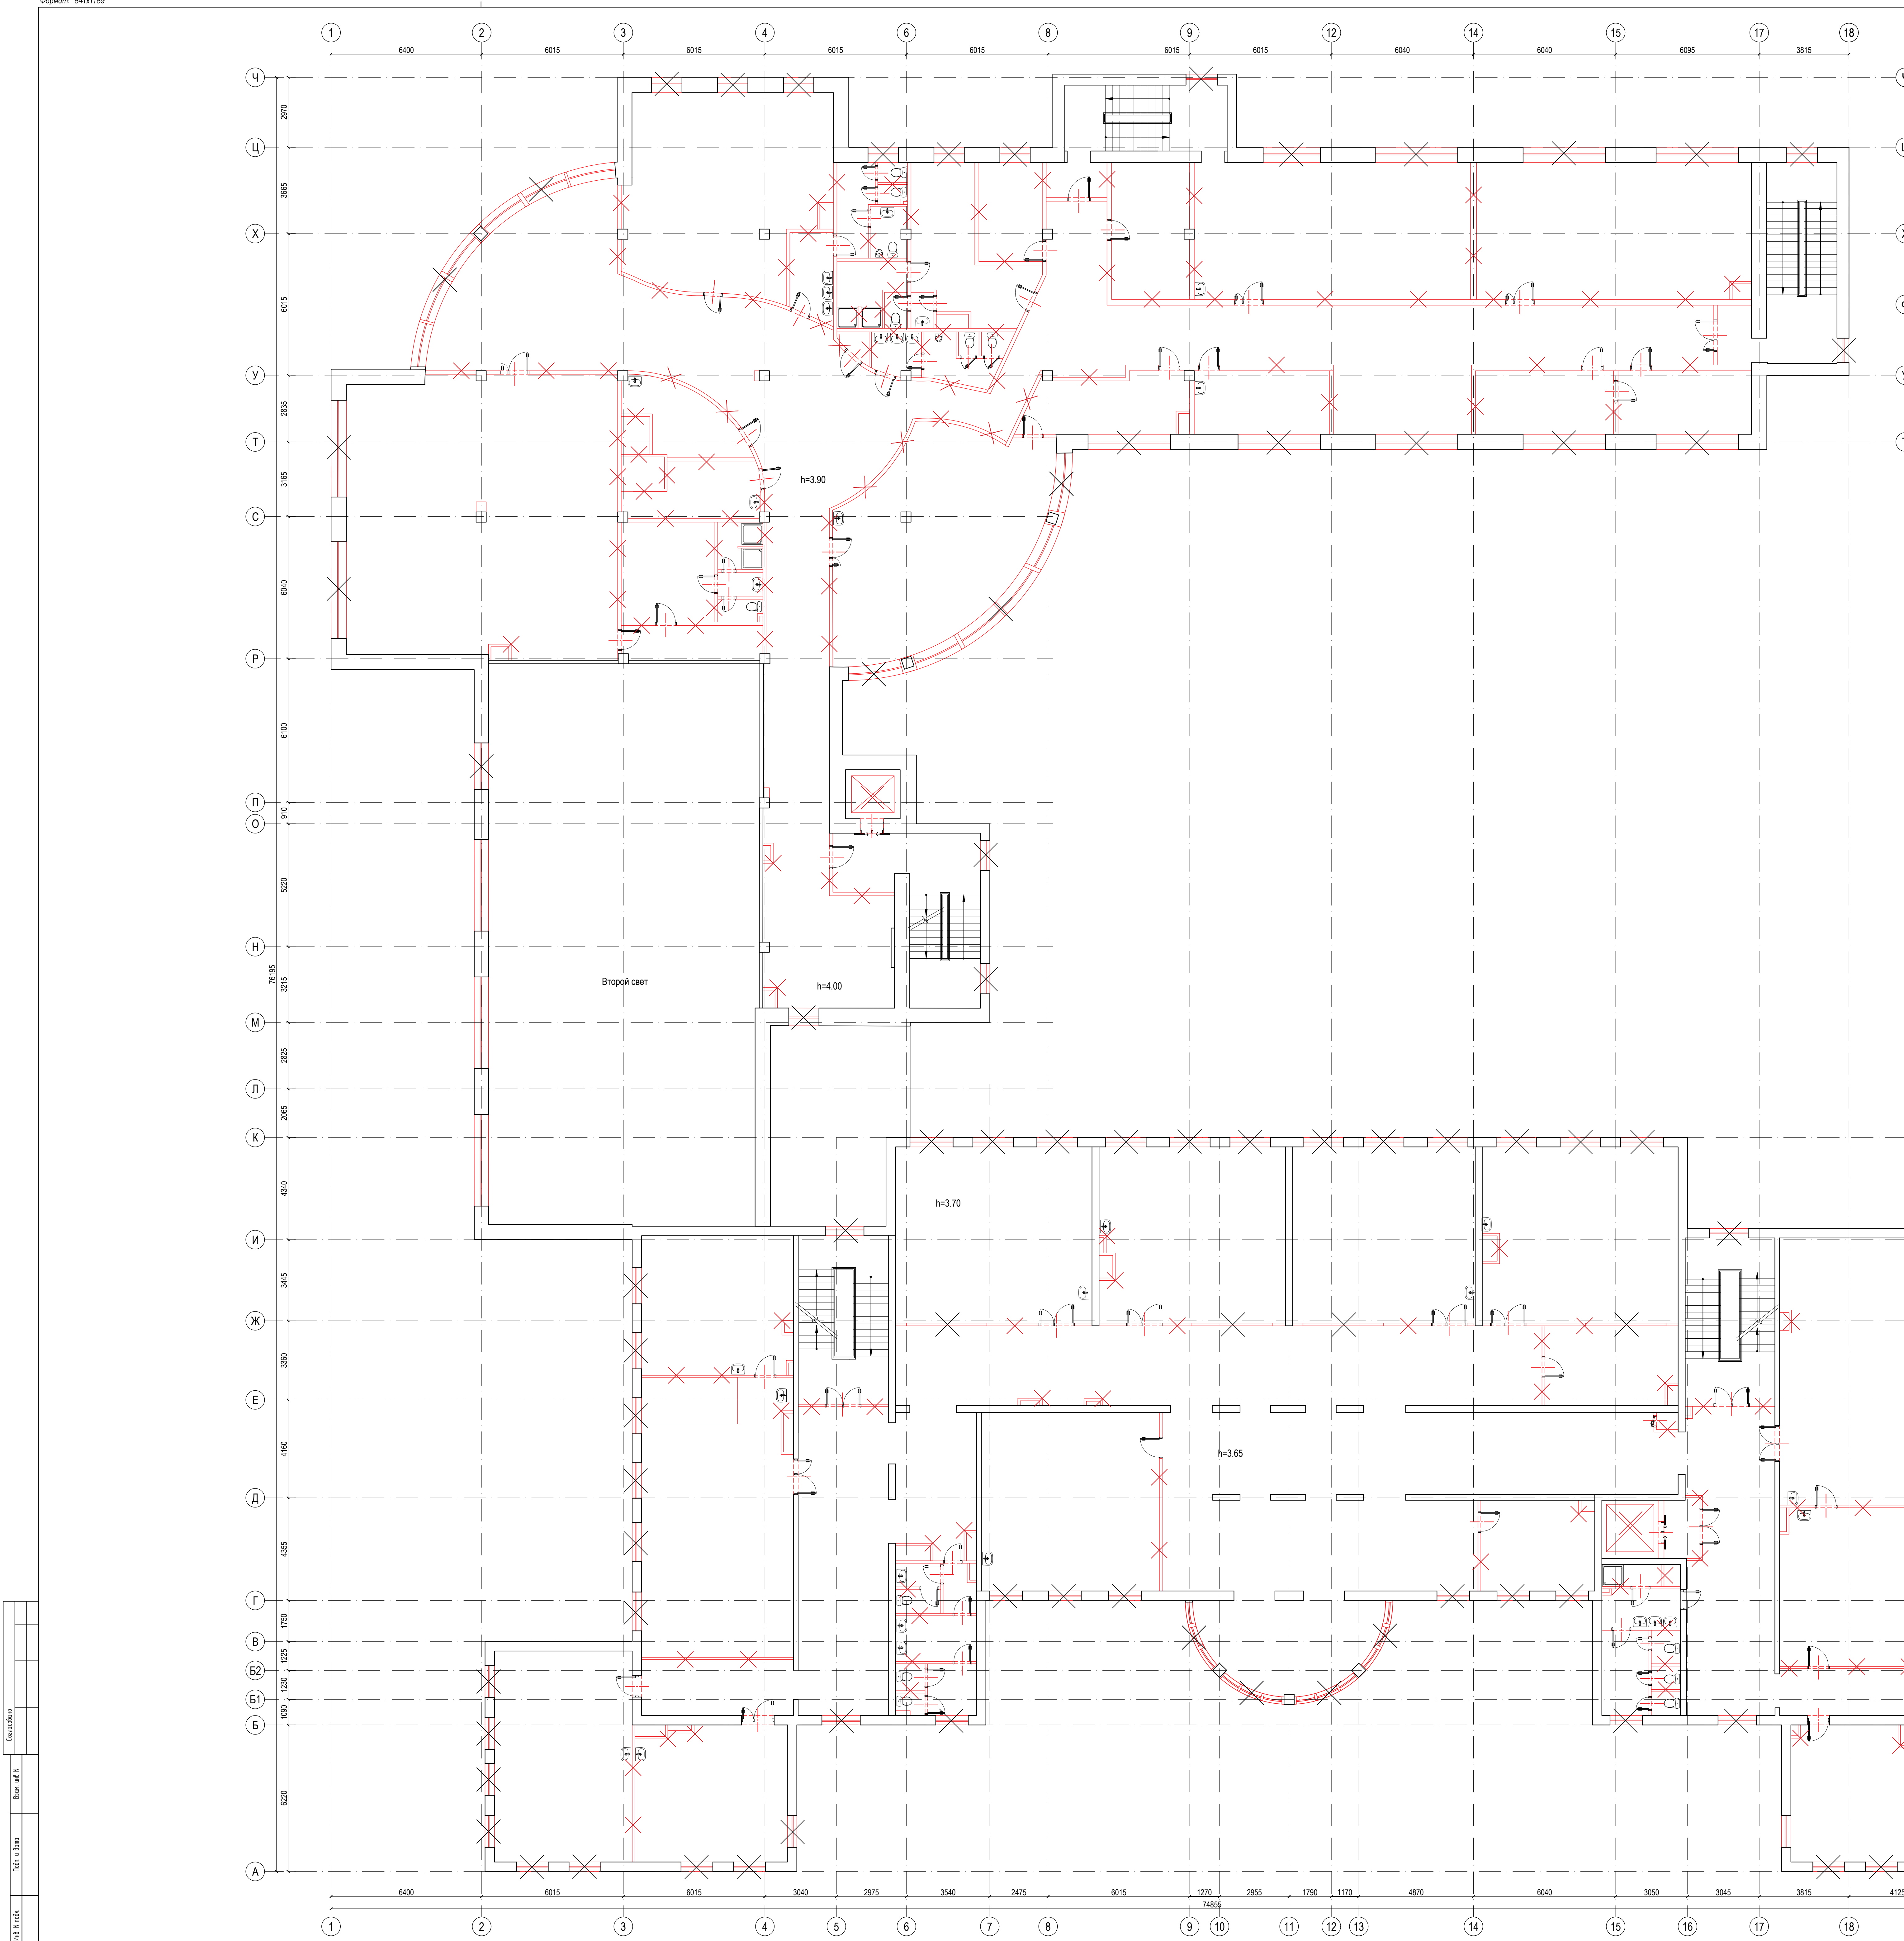

План 3 этажа

Условные обозначения:

- сохраняемые несущие конструкции
- демонтаж витражей
- демонтаж оконных блоков
- демонтаж внутренних окон и витражей
- демонтаж перегородок
- демонтаж внутренних дверных блоков
- демонтаж наружных дверных блоков
- разбираемые конструкции
- демонтаж стенки под проем
- демонтаж лифта

|           |             |      |        |         |         |
|-----------|-------------|------|--------|---------|---------|
| Имя       | Кол-во      | Лист | № доку | Подпись | Дата    |
| Разработ  | Нодоровская |      |        |         | 2024.04 |
| ГЛАВ      | Лавровская  |      |        |         | 2024.04 |
| Н. контр. | Губарева    |      |        |         | 2024.04 |
| Генп      | Маркова     |      |        |         | 2024.04 |

|  |  |  |  |  |  |   |      |        |
|--|--|--|--|--|--|---|------|--------|
|  |  |  |  |  |  | 16-25/Г-П-АР   |      |        |
|  |  |  |  |  |  | Капитальный ремонт общеобразовательного учреждения (ГБОУ "Школа №429", расположенного по адресу: г.Москва, 5-ая ул.Соколиной Горы, д.14) |      |        |
|  |  |  |  |  |  | Архитектурно-планировочные решения   |      |        |
|  |  |  |  |  |  | Склад   | Лист | Листов |
|  |  |  |  |  |  | П   | 4    |        |
|  |  |  |  |  |  | План демонтажа 3 этажа. М1.000   |      |        |
|  |  |  |  |  |  | АЗУРИТ   |      |        |
|  |  |  |  |  |  | ФОРМАТ А0   |      |        |