


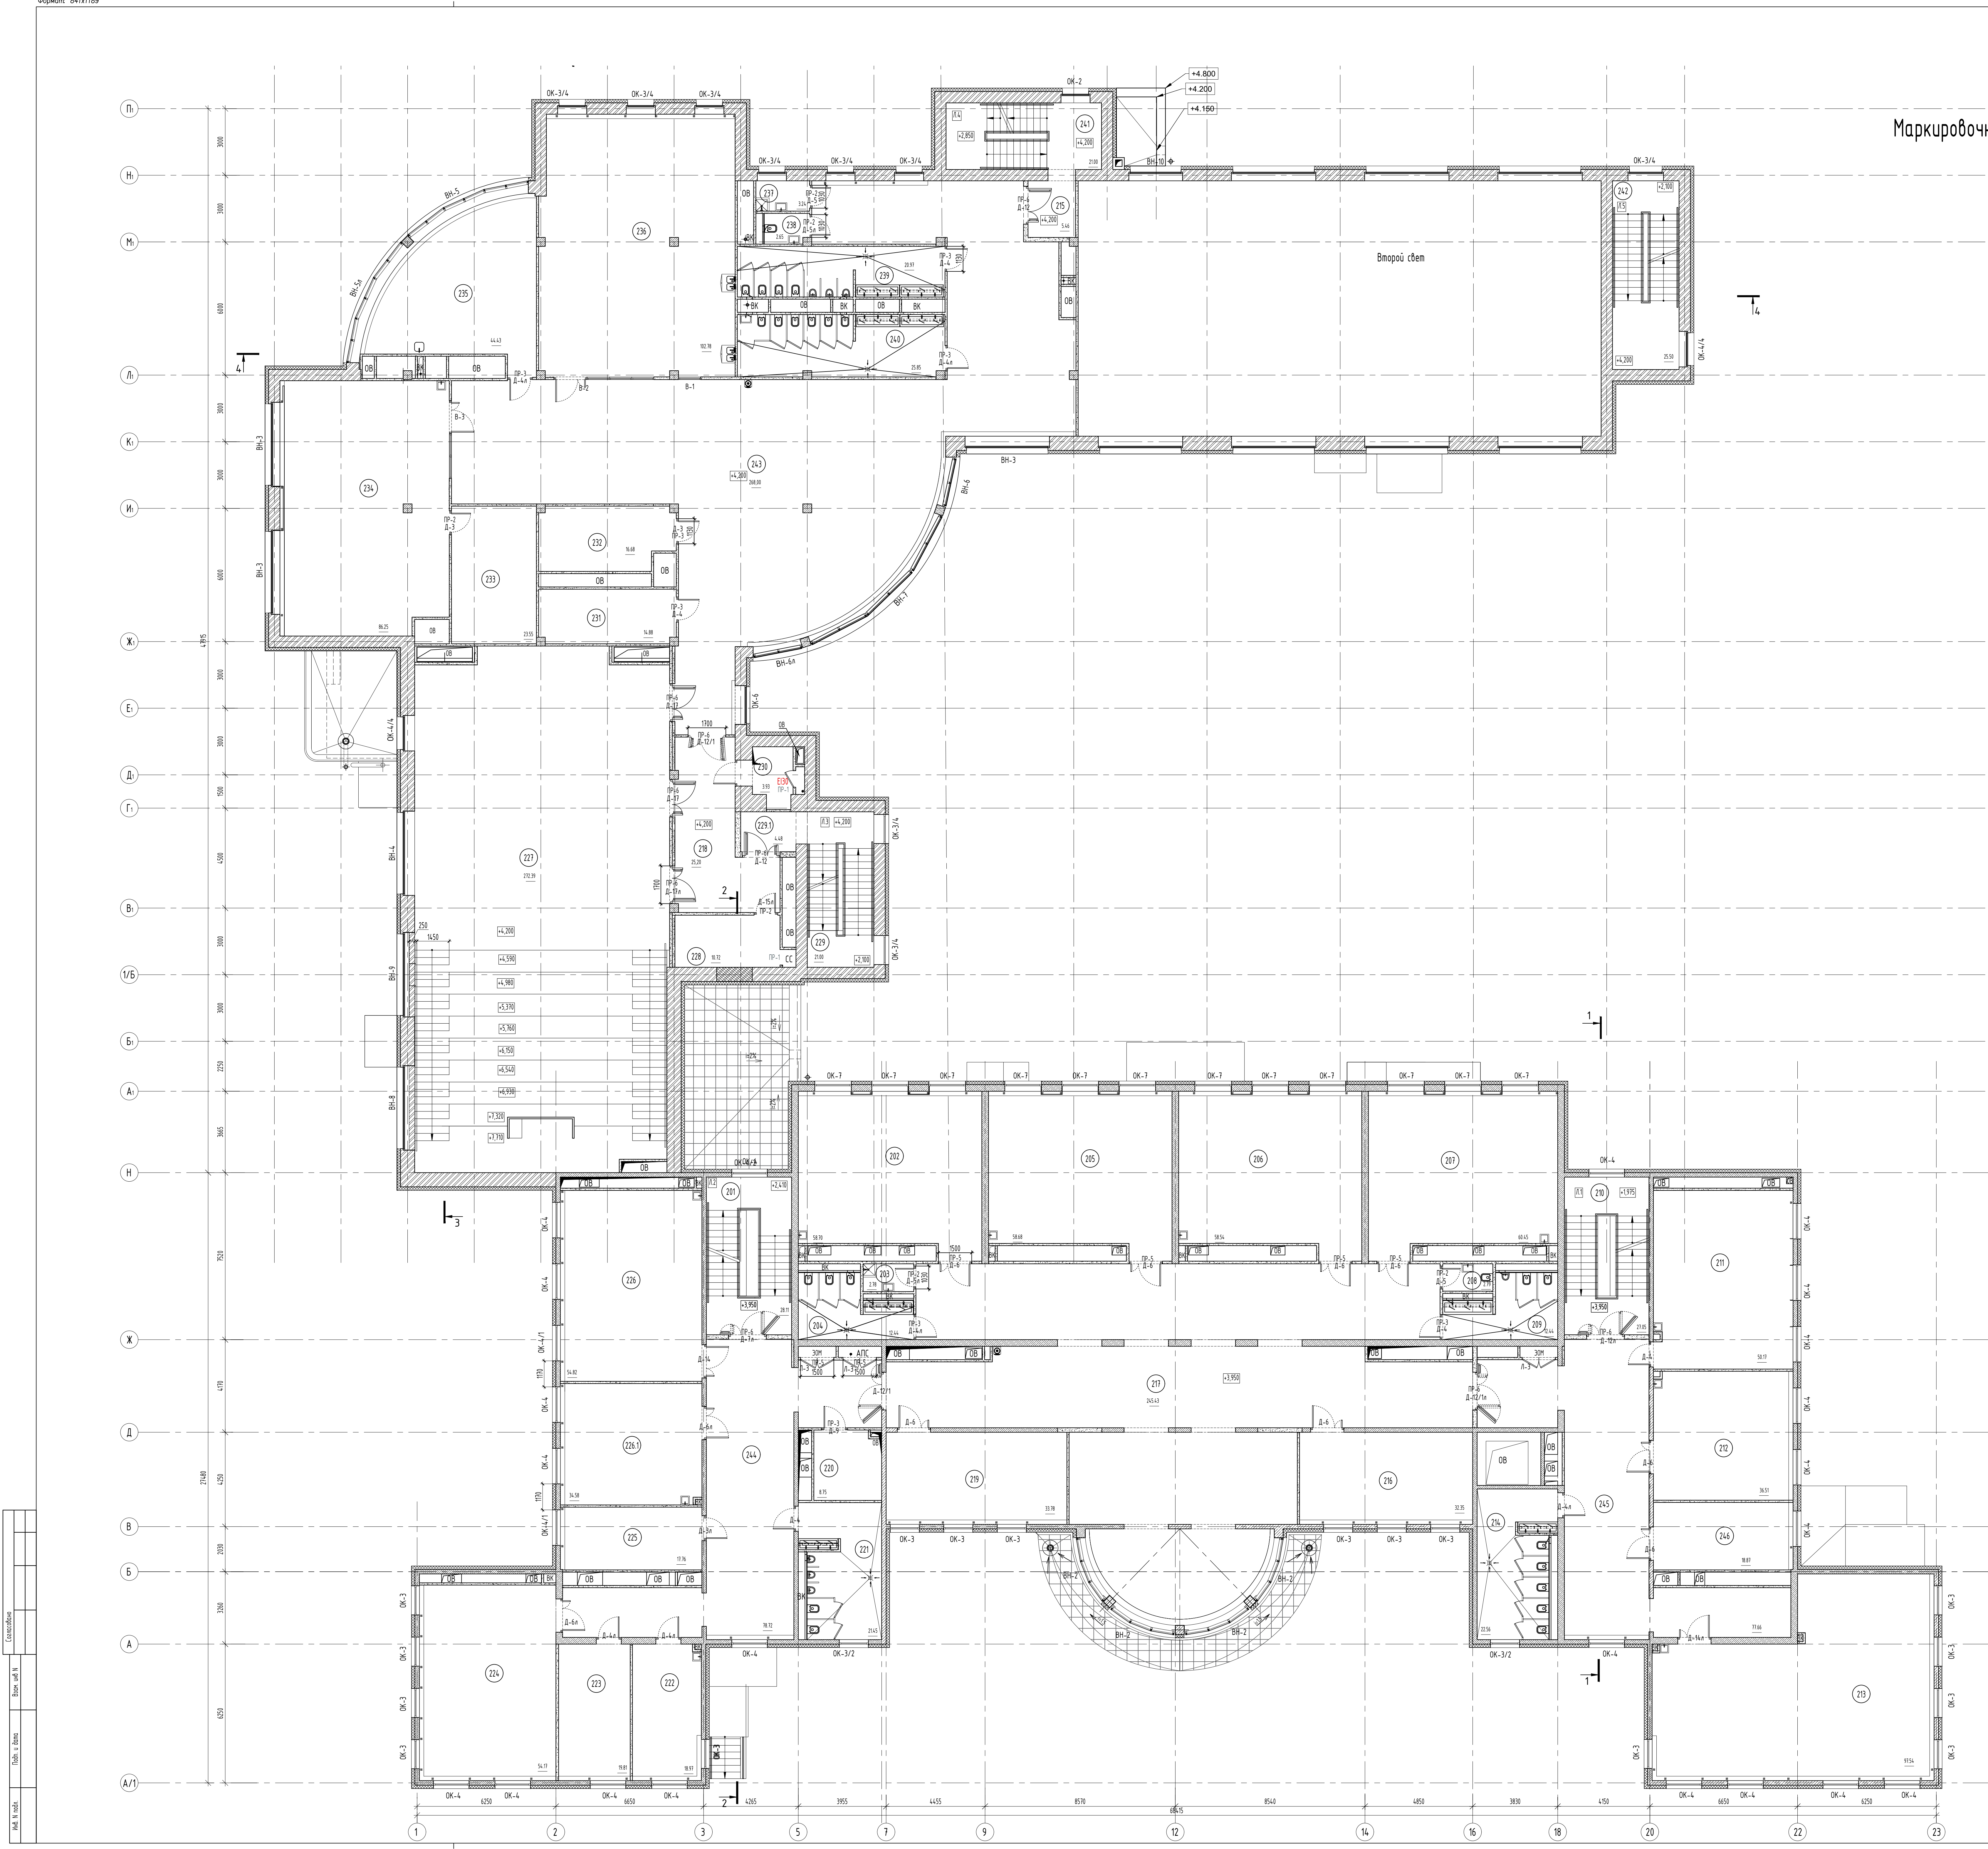

Маркировочный план 2 этажа.
М 1:100

Номер помеще-ния	Наименование	Площадь, м2	Кат. помеще-ния
201	Лестничная клетка, Тип И2	28,82	
202	Учебные кабинеты (начальная школа)	58,70	
203	ПМ	2,78	В4
204	Санитар для девочек (начальная школа)	12,73	
205	Учебные кабинеты (начальная школа)	58,68	
206	Учебные кабинеты (начальная школа)	58,54	
207	Учебные кабинеты (начальная школа)	60,45	
208	Санитар для персонала	2,79	
209	Санитар для мальчиков (начальная школа)	12,44	
210	Лестничная клетка (П0)	27,05	
211	Учебные кабинеты (начальная школа)	50,17	
212	Кабинет иностранного языка (начальная школа)	36,51	
213	Лабораторно-исследовательский комплекс для изучения естественных наук	97,02	В3
214	Санитар для девочек (начальная школа)	23,25	
215	Танцзал	5,46	
216	Кабинет для индивидуальных занятий с малой группой	32,35	
217	Коридор с рекреацией (начальная школа)	245,43	
218	Коридор	25,20	
219	Кабинет для индивидуальных занятий с малой группой	33,78	
220	Помещение (физ)	8,75	В4
221	Санитар для мальчиков (начальная школа)	21,45	
222	Кабинет для индивидуальных занятий, в т.ч. с учителем-логопедом	18,97	
223	Кабинет для индивидуальных занятий, в т.ч. с коррекционным педагогом	19,22	
224	Учебные кабинеты (начальная школа)	54,17	
225	Кладовая шкафы творческой мастерской	17,75	В3
226	Творческая мастерская	54,82	В3
226.1	Кабинет иностранного языка (начальная школа)	34,58	
227	Минифункциональное пространство с функцией автобуса зала (с эскалатор в шрифте пола)	272,39	
228	Кроссовая	10,72	В3
229	Лестничная клетка (П0)	21,00	
229.1	Танцзал	4,48	
230	Тех. помещение	3,93	В4
231	Архитектурная	14,75	
232	Кладовая шкафы	16,45	В3
233	Кладовая кабинеты материальной техники	23,55	В3
234	Кабинет с рабочим пространством для учителей тип 1 (начальная школа)	86,25	В3
235	Кабинет с рабочим пространством для учителей тип 1 (начальная школа)	44,43	
236	Кабинет материальной техники тип 1	102,78	В3
237	ПМ	3,24	В4
238	Санитар для персонала	2,45	
239	Санитар для мальчиков (основная и старшая школа)	28,97	
240	Санитар для девочек с комнатой личной гигиены (основная и старшая школа)	25,85	
241	Лестничная клетка (П0)	21,00	
242	Лестничная клетка (П0)	25,50	
243	Коридор и рекреация (основная и старшая школа)	268,00	
244	Коридор	78,72	
245	Коридор	77,66	
246	Административный кабинет	18,87	
	Всего	2245,3	


УСЛОВНЫЕ ОБОЗНАЧЕНИЯ

- Существующие молнии и/в стены
- Замена перегородки из газобетонных блоков 1/625x250x100/О50/0/85,0 по ГОСТ Р 10522-2022, толщиной 100мм на клеи с армированием базальтовой сеткой, штукатурная
- Замена перегородки из газобетонных блоков 1/625x250x100/О50/0/85,0 по ГОСТ Р 10522-2022, толщиной 200мм на клеи с армированием базальтовой сеткой, штукатурная
- Замена перегородки из гипсокартона однослойное 12,5мм на все высоту этажа толщиной 100мм
- Замена перегородки из гипсокартона однослойное 12,5мм до ур. рабочих полов толщиной 100мм
- Замена перегородки из гипсокартона
- Замена перегородки светопрозрачной (внешестетикой) с дверью и необходимой фурнитурой
- Номер помещения по экспликации
- Отметка уровня пола этажа
- Маркировка геометрии помещений: дверей, окон, перегородок;
- Марка окна
- Марка двери
- Марка перемычки проема

- Возможность устройства проемов в несущих стенах будет уточняться в проекте.
- Размер и расположение вентиляционных шахт будет уточнен в проекте.
- Шахты предназначены для прокладки инженерных коммуникаций и стоек ВК, СС, ЗСМ, оборудованные лестницами для обслуживания.
- ★ категорирование по взрывопожарной опасности данных помещений выполнять на этапе проектирования.

Имя, И.Ф.О.	Дата, Дата	Страна, Страна
Имя, И.Ф.О.	Дата, Дата	Страна, Страна

16-25/Г-П-АР.ВОР	
Капитальный ремонт объекта "ТБОУ Школа № 429 "Соколинская гора", расположенного по адресу: г.Москва, ул. Соколинской горы 5-а, д.14	
Имя, И.Ф.О.	Лист, Лист
Разработчик	Лист, Лист
Объемно-планировочные и архитектурные решения	
Маркировочный план 2 этажа. М 1:100	
И.И.И.	Г.И.И.
И.И.И.	Г.И.И.
АЗУРИТ	
ФОРМАТ А0	

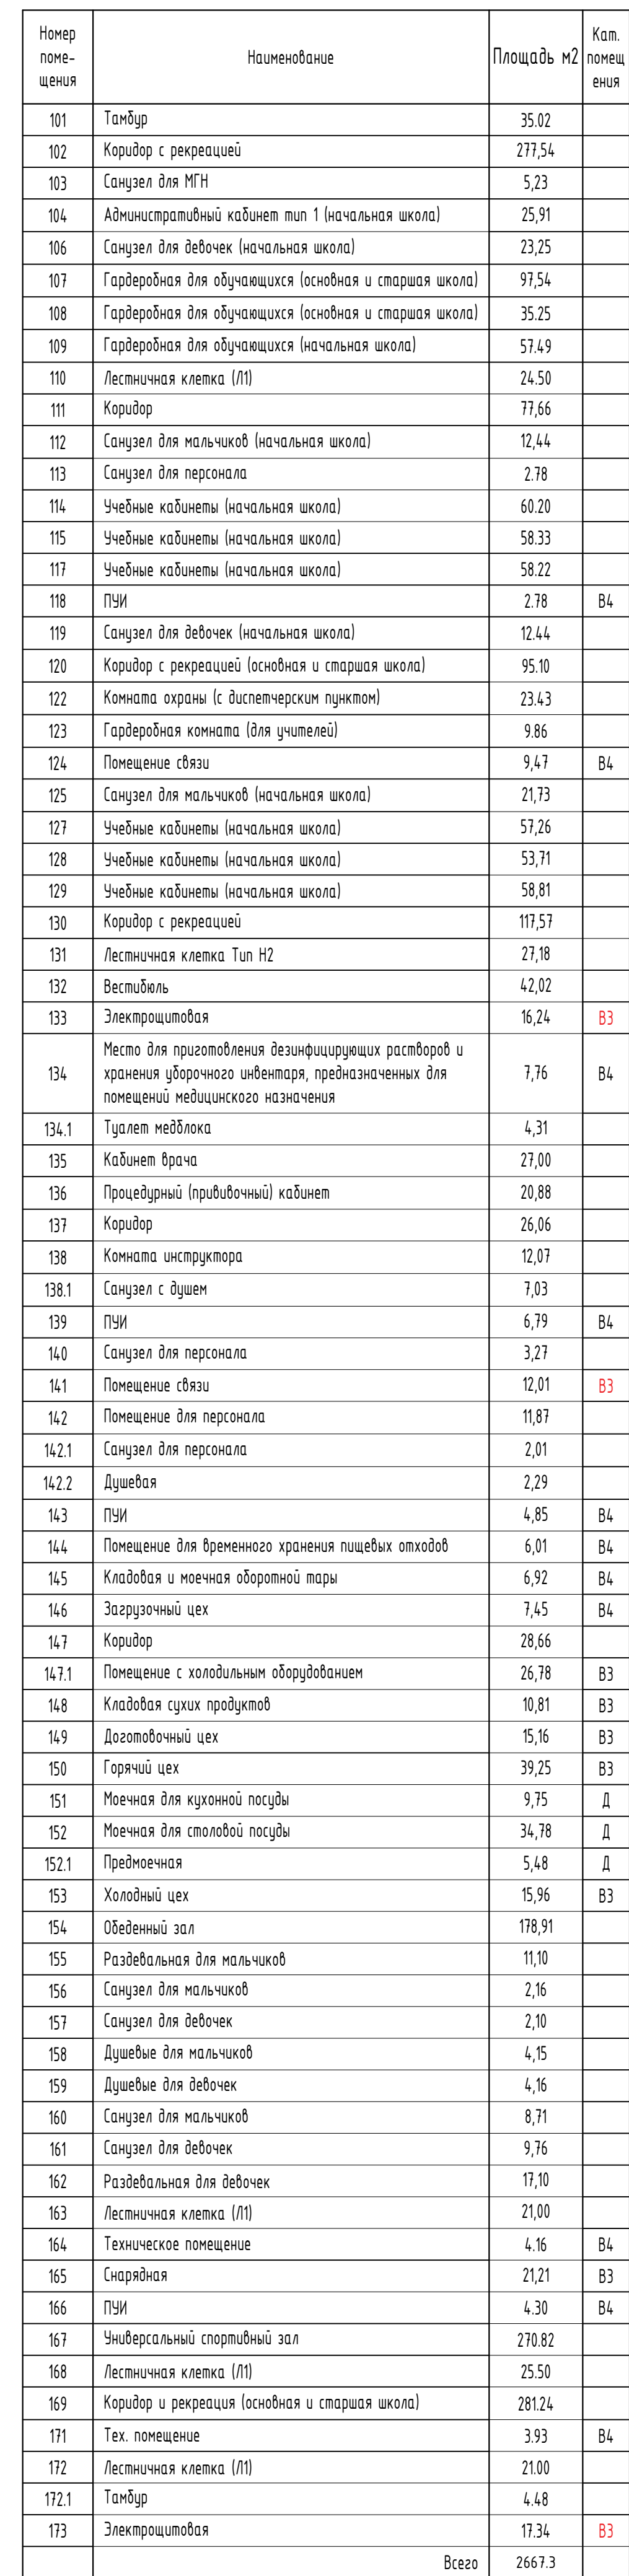

- Существенные монтажные х/б стыки
- Заполнение перерывов из заделываемых блоков 1/625x250x100/650/85, по ГОСТ Р 70522-2002, полици на клею + армирование базальтовой сеткой, штукатурка
- Заполнение перерывов из заделываемых блоков 1/625x250x100/650/85, по ГОСТ Р 70522-2002, полици на клею + армирование базальтовой сеткой, штукатурка
- Заполнение перерывов из силикатных однослойных закладной толщиной 100мм
- Заполнение перерывов из силикатных однослойных толщиной 100мм
- Заполнение сложенные перерывов
- Заполнение перерывов цементношпаклевкой (Магмашпакс) с фиброй и необходимой фурнитурой

 201 - Номер помещения по экспликации

 0301 - Отметка уровня пола по экспликации

ЕМ/СМ/ВМ/СВ/М

- ОК-1 - Марка окна
- Д-9 - Марка двери
- П-3 - Марка перемычки проема

[illegible]





Номер помещения	Наименование	Площадь м2	Кол. помещ.
001	ИТП	66,06	д
002	Венткамер с фанкермой	71,36	83
004	Водонагрев улет и насосная	11,10	д
005	Техническое помещение	28,40	д
006	Венткамера	137,76	83
006.1	Венткамер систем приточной противоточной вентиляции	23,13	д
007	Венткамера	138,94	83
008	Техническое помещение для прокладки инженерных коммуникаций	974,84	83
009	Венткамера	64,68	83
010	Техническое помещение	64,56	д
011	Защитное помещение для хранения орудий	2473,34	д
012	Коридор	50,95	д
013	Санузел женский	10,88	д
014	Санузел мужской	4,45	д
015	Коридор	2,108	д
016	Узел ввода электрических сетей	57,00	84
017	Коридор	39,60	д
	Всего	2010,2	


УСЛОВНЫЕ ОБОЗНАЧЕНИЯ


- Существующие стены из полнотелого керамического кирпича
- Замена монолитные X/V стены
- Замена перегородки из полнотелого кирпича 120мм, отштукатуренная
- Номер помещения по классификации
- Маркировка огнестойкости заменами дверей
- Отметка уровня пола запаса
- Помещения ГЗ ЧС
- Пути эвакуации
- Ок-1 - Марка окна
- Д-9 - Марка двери

1. Возможность устройства проемов в несущих стенах будет уточняться в проекте. Размер и расположение вентиляционных шахт будет уточнен в проекте.
2. Шахты предназначены для прокладки инженерных коммуникаций и стоек (ВК, СС, ЭОМ) оборудуются лючками для обслуживания.
3. * категорирование по взрывопожарной опасности данных помещений выполнить на этапе проектирования.

 						16-25/Г-П-АР ВОР		
						Капитальный ремонт объекта "ГБОУ Школа № 429 "Скопелина гора", расположенного по адресу: г.Москва, ул. Скопелиной №5-А, 014		
Изм	Кол-во	Лист	№Фох	Подпись	Дата			
Разработка		Литовская			2019.02.20			
						Объемно-планировочные и архитектурные решения	страниц	Листов
						п	17	
И контр.	Губарева				2019.02.20			
Гит	Нарышкин				2019.02.20			
						Маркировочный план подвала М 1:100	 АЗУРИТ	

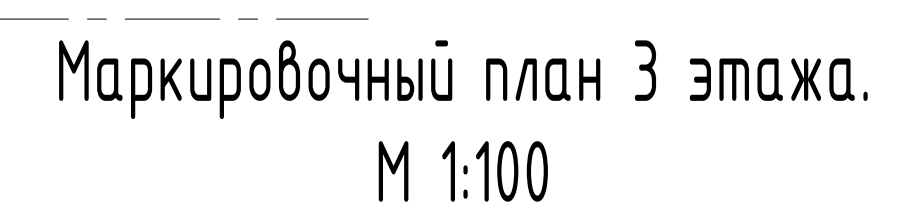[illegible]

 						16-25/Г - П-АР ВОР					
Изм.	Курс	Лист	№ обз	Подпись	Дата	Капитальный ремонт объекта "БСОУ Школа № 429 Соколовая гора", расположенное по адресу: г.Москва, ул. Сопенской горы 5-я, д.14 Объемно-планировочные и архитектурные решения					
Разработка		Архитектор			2020.07.28						
						Страница	Лист	Алфавит			
						П	20				
N контр.		г.доброго			2020.07.28	Модернизация лпдн 3 этажа М 1100					
ГИП		Никонов			2020.07.28						
						 АЗУРИТ					
						РОСАВТО ЛПД					

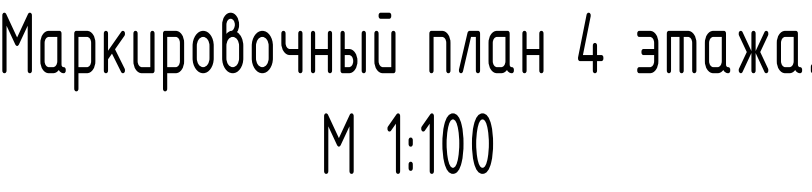

Экспликация помещений 4-го этажа

Помещение	Наименование	Площадь, м ²	Кол. помещ.
401	Лестничная клетка Тип Н2	28,81	
402	Кабинет русского языка и литературы	58,70	
403	Плп	2,78	84
404	Специал. каб. для физик. (основная и старшая школа)	12,49	
405	Кабинет русского языка и литературы	58,68	
406	Кабинет математики	58,51	
407	Кабинет математики	60,45	
408	Специал. каб. для физик.	2,78	
409	Специал. каб. для мальчиков (основная и старшая школа)	12,49	
410	Лестничная клетка IIII	26,93	
411	Кабинет информационных технологий	87,66	
412	Лаборатория при кабинете информационных технологий	18,84	83
413	Административный кабинет тип 1 (основная и старшая школа)	16,03	
414	Учебные кабинеты для изучения естественных наук	60,75	
415	Лаборатория кабинета химии	18,86	83
416	Специал. каб. для физик. с компьютер. технич. оснаст. (основная и старшая школа)	27,56	
417	Подсобное помещение	7,30	84
418	Кабинет иностранного языка (основная и старшая школа)	32,36	
419	Коридор с рекреацией	245,54	
420	Коридор с рекреацией	118,69	
421	Кабинет иностранного языка (основная и старшая школа)	34,07	
422	Помещение связи	8,02	84
423	Специал. каб. для мальчиков (основная и старшая школа)	21,45	
424	Коридор	77,66	
425	Кабинет истории Тип 1	54,17	
426	Кабинет информатики с возможностью деления трансформированной перегородкой на два помещения	108,69	
427	Лестничная клетка IIII	20,80	
428	Помещение выхода на крыло	4,78	
	Всего	1296,5	

УСЛОВНЫЕ ОБОЗНАЧЕНИЯ

- Существующие многоярусные х/б стелы
- Уменьшение перегородки из газобетонных блоков 1/625/250/100/050/05,0 по ГОСТ Р 19512-2012, толщиной 100мм на клею с односторонним базальтовым сеткой, штукатуркой
- Уменьшение перегородки из газобетонных блоков 1/625/250/100/050/05,0 по ГОСТ Р 19512-2012, толщиной 200мм на клею с односторонним базальтовым сеткой, штукатуркой
- Уменьшение перегородки из акрилового анионированного вспененного на все высоту здания толщиной 100мм
- Уменьшение перегородки из акрилового анионированного вспененного до ур. кровли толщиной 100мм
- Уменьшение ослепленных перегородки
- Уменьшение перегородки ступенчатая (Возвратная) с верхней и нижней частью фанитной
- Номер помещения на этикетках
- Отметки урובה пола этажа
- Маркировка сантехнических значимых дверей, окон, перегородок;
- Марка кини
- Д-9
- Марка перемычки проема

						16-25/Г.-П.АР.ВОР					
						Капитальный ремонт объекта "БСОУ Школа № 429 "Скоkelьная гора", расположенного по адресу: г Москва, ул Скоkelьной горы 5-я, д14.					
Имя Разработчик	Авт. Литература	№Фак Литература	Подпись	Дата	Объемно-планировочные и архитектурные решения						
				2020.07.01							
Н. Контр.	Губарева			2020.07.20	Максированный план 4 этажа. М 1:100						
ГИП	Мамеев			2020.07.20							
							З1				
							ПРОЕКТ 40				

Номер пояснения	Наименование	Площадь, м ²	Кол- пояснений
501	Вспомогательная клетка Тун H2	27,26	
502	Вспомогательная клетка Тун H1	27,05	
503	Вспомогательная 1	43,07	03
504	Вспомогательная 2	44,89	03
505	Техническое помещение	206,11	03
506	Техническое помещение	255,60	03
507	Техническое помещение	143,26	03
508	Техническое помещение	178,99	03
509	Техническое помещение	59,20	03
510	Техническое помещение	58,88	03
511	Техническое помещение	59,24	03
512	Техническое помещение	60,00	03
513	Техническое помещение	107,50	03
		Итого	1276,25

	- Существующие многоэтажные Ж/Б стены
	- Заменяемые перегородки из разовитых блоков
	1/625/25x100/0,50/0,50 по ГОСТ Р 19522-2012, толщину 100мм на клее + армирование базальтовой сеткой, отсутствующее
	- Заменяемые перегородки из разовитых блоков
	1/625/25x100/0,50/0,50 по ГОСТ Р 19522-2012, толщину 100мм на клее + армирование базальтовой сеткой, отсутствующее
	- Заменяемые перегородки из склеиваемого одностороннего акустического вспененного полиуретана толщиной 100мм
	- Заменяемые перегородки из склеиваемого одностороннего акустического вспененного полиуретана толщиной 100мм
	- Заменяемые оклеиваемые перегородки
	- Заменяемые перегородки сантехнические (влагостойкие) с дверью и необходимой фурнитурой
	- Номер помещения по эксплуатации
	- Ометка потолка пола эвакуации
	- Маркировка огнеустойчивости заменяемых дверей, окон, перегородок
	- Марка окна
	- Марка двери
	- Марка перемычки проема

№	Модель	Сечение
1	ПР-1 гравит. 130-180мм	
2	ПР-2 гравит. 1030мм	
3	ПР-3 гравит. 1030-1130мм	
4	ПР-4 гравит. 1030мм	
5	ПР-5 гравит. 1500мм	
6	ПР-6 гравит. 1700мм	
7	ПР-7 гравит. 2030мм	

№	Марка	Обозначение	Наименование	Кол-во, шт.						
				Полбор	1 эт.	2 эт.	3 эт.	4 эт.	Мех. эт.	Всего
1	PP-1	ГОСТ 8569-93 ГОСТ 40-93	1.50м -50х4	4	2	2	2	-	-	10
2	PP-2	ГОСТ 8569-93 ГОСТ 40-93	1.50м -50х4	1	8	6	3	2	-	20
3	PP-3	ГОСТ 8569-93 ГОСТ 40-93	1.50м -50х4	-	34	8	12	5	5	64
4	PP-4	ГОСТ 8569-93 ГОСТ 40-93	1.50м -50х4	-	-	-	-	-	-	-
5	PP-5	ГОСТ 8569-93 ГОСТ 40-93	1.50м -50х4	4	5	-	-	-	-	9
6	PP-6	ГОСТ 8569-93 ГОСТ 40-93	1.50м -50х4	-	7	8	6	3	-	24
7	PP-7	ГОСТ 8569-93 ГОСТ 40-93	1.50м -50х4	-	1	-	-	-	-	1

						16-25/Г-П-АР.ВОР		
						Календарный ремонт объекта "БОО Школа № 429 "Скоkelная зор", расположенного по адресу зМосква, ул. Скоkelной зор 5-я, 814		
Изм.	Колес.	Лист	Лист	Подпись	Дата			
Разработчик		Лист	Лист	<i>Р.С.</i>	2024.01.28			
						Объемно-планировочные и архитектурные решения		
						Стенда	Лист	Лист
						П	22	
И. контр.	Г.обарва	Лист	Лист	<i>Р.С.</i>	2024.01.28			
Г.П.	Немцова	Лист	Лист	<i>Р.С.</i>	2024.01.28			
						Маркировочный лент. знак. М 1100 Спецификация первичник.		
								