

Схема расположения форшахты в/о 14.1-K1


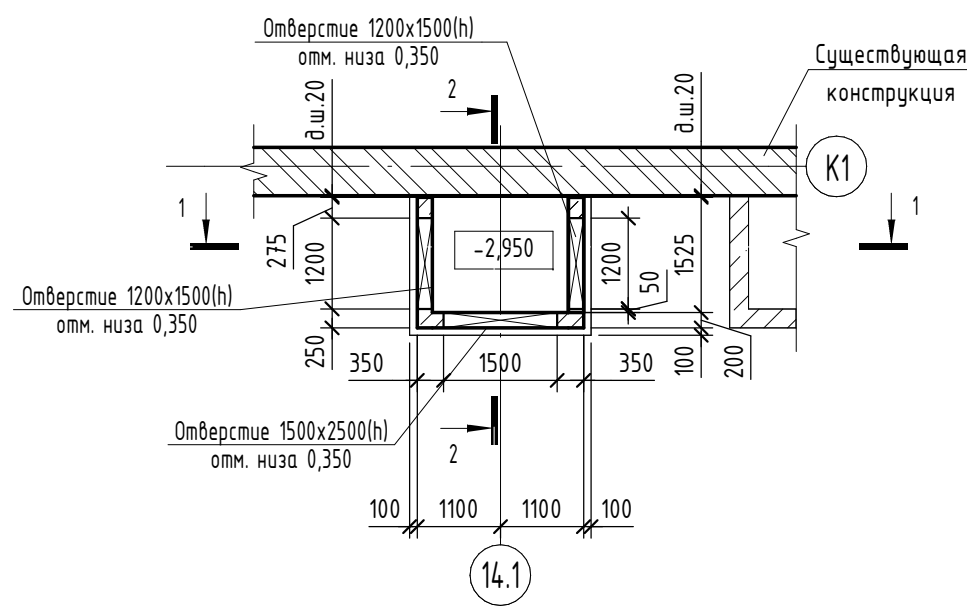


Схема расположения арматурных выпусков вундаментной плиты в/о 14.1-K1

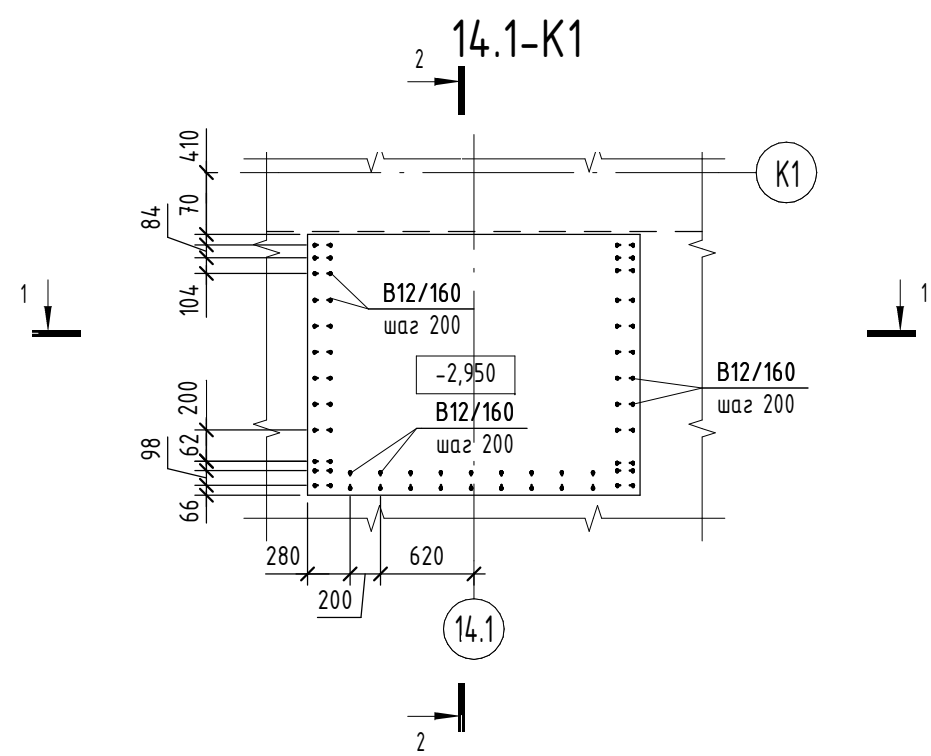

1-1 Опалубка

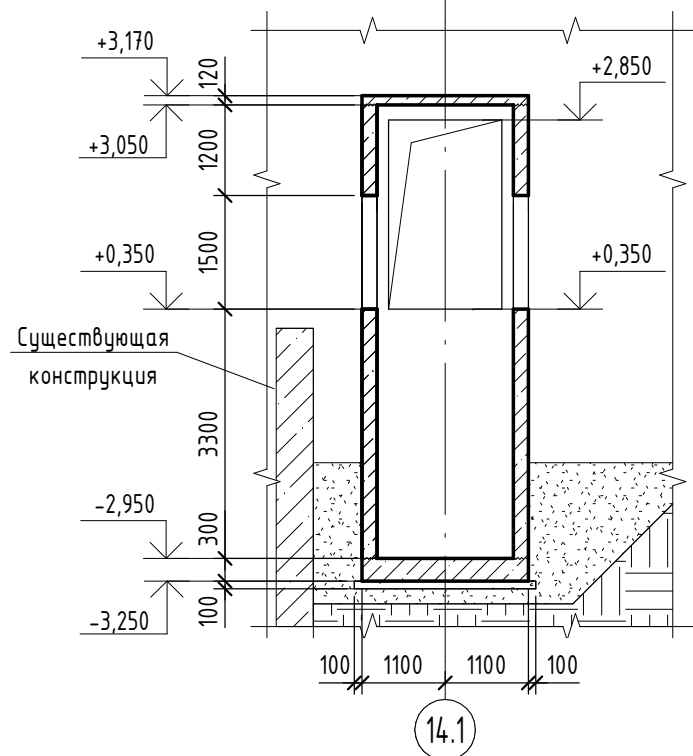


Схема обрамления отверстия в стене 1200х1500



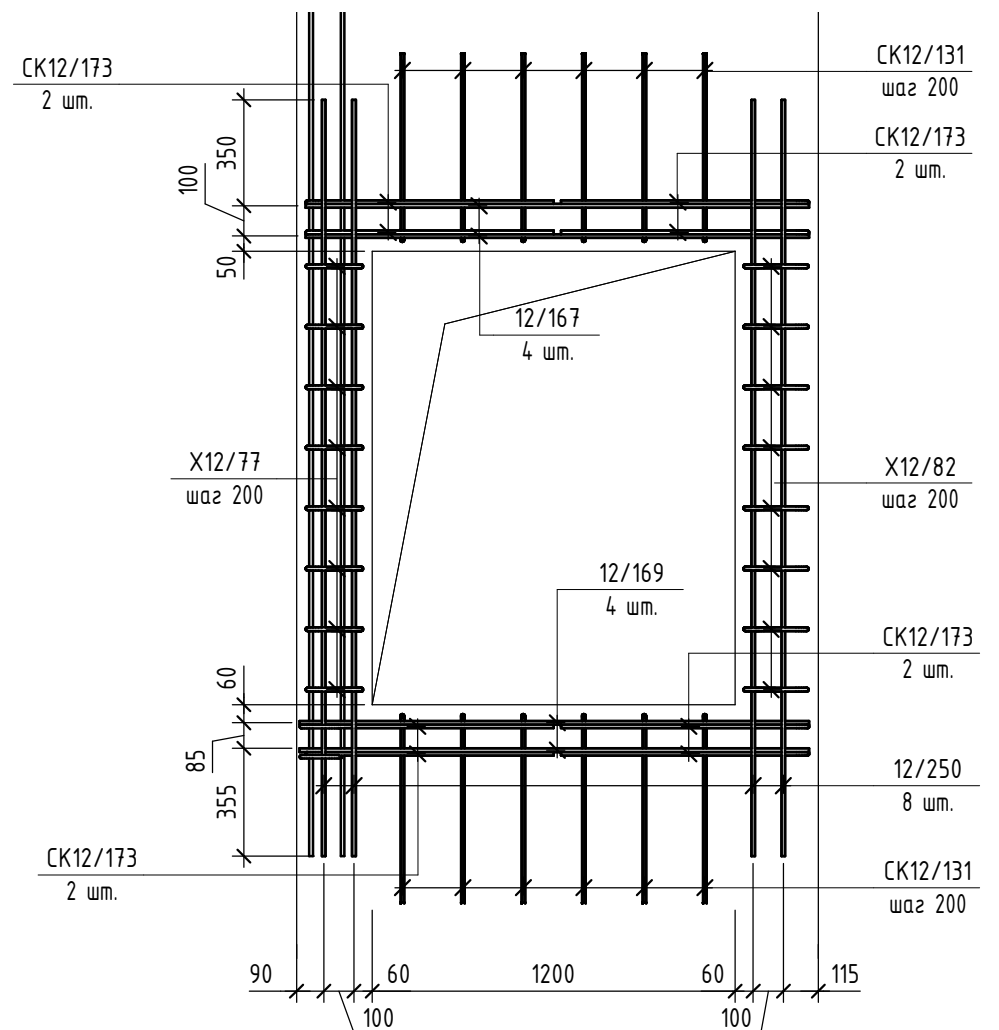



Схема обрамления отверстия в стене 1500х2500

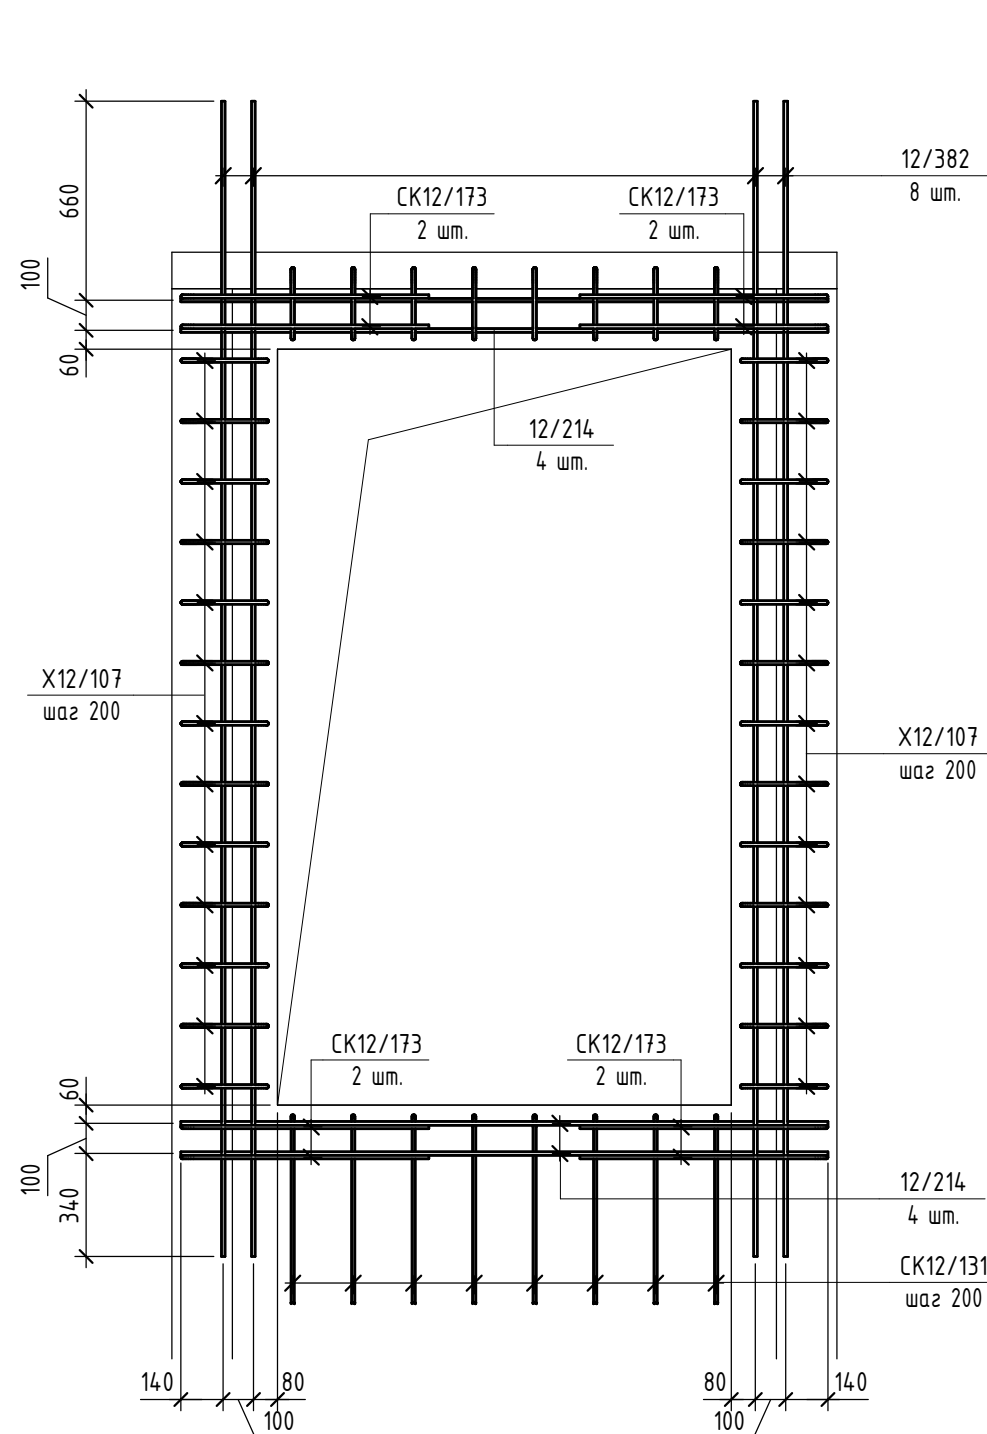

1-1 Армирование

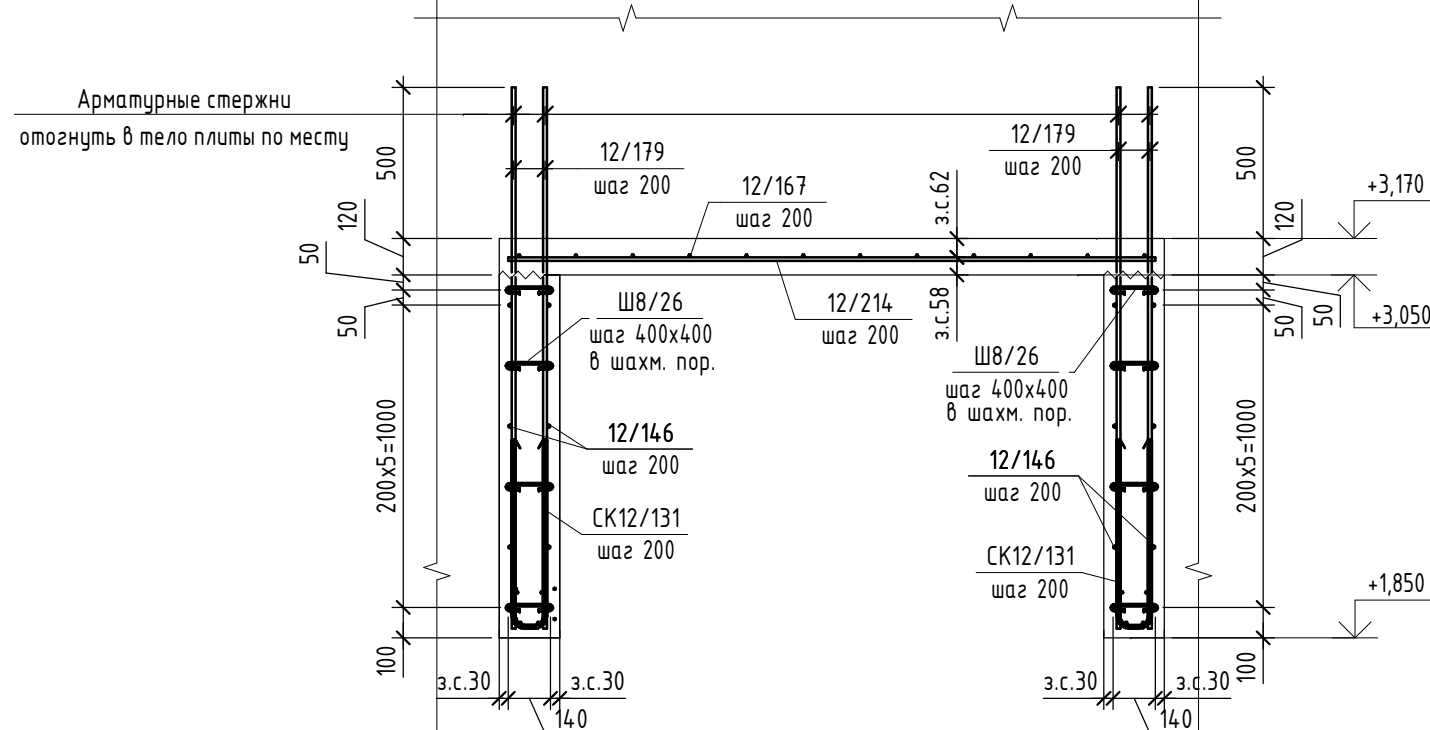

2-2 Армирование

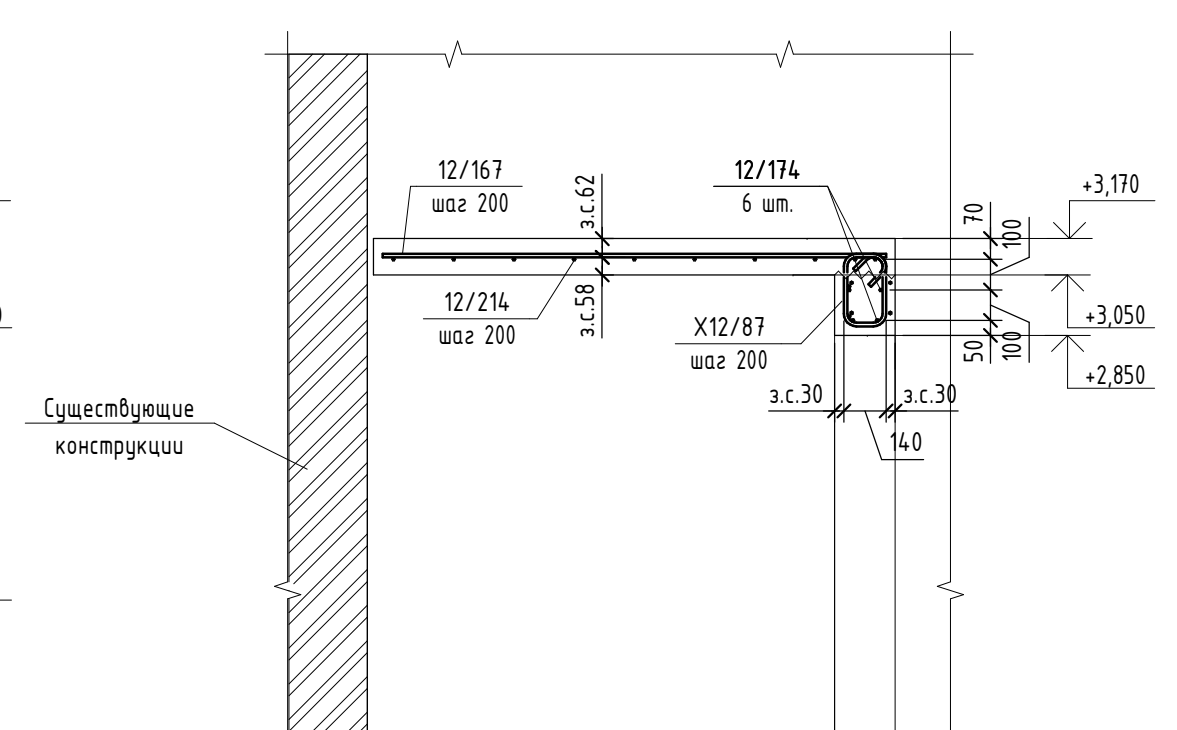

2-2 Опалубка

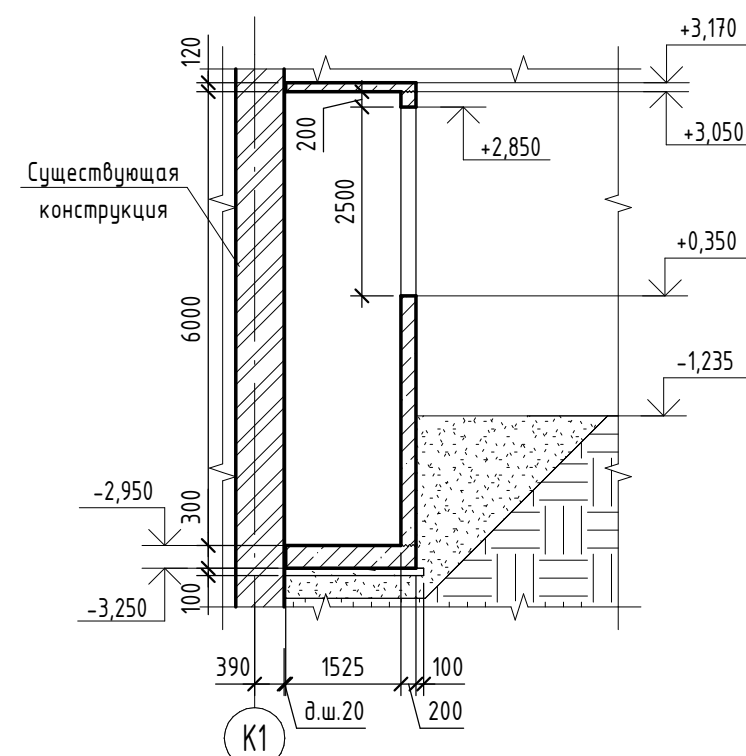


Схема расположения шпилек с шагом 400х400 в шахматном порядке


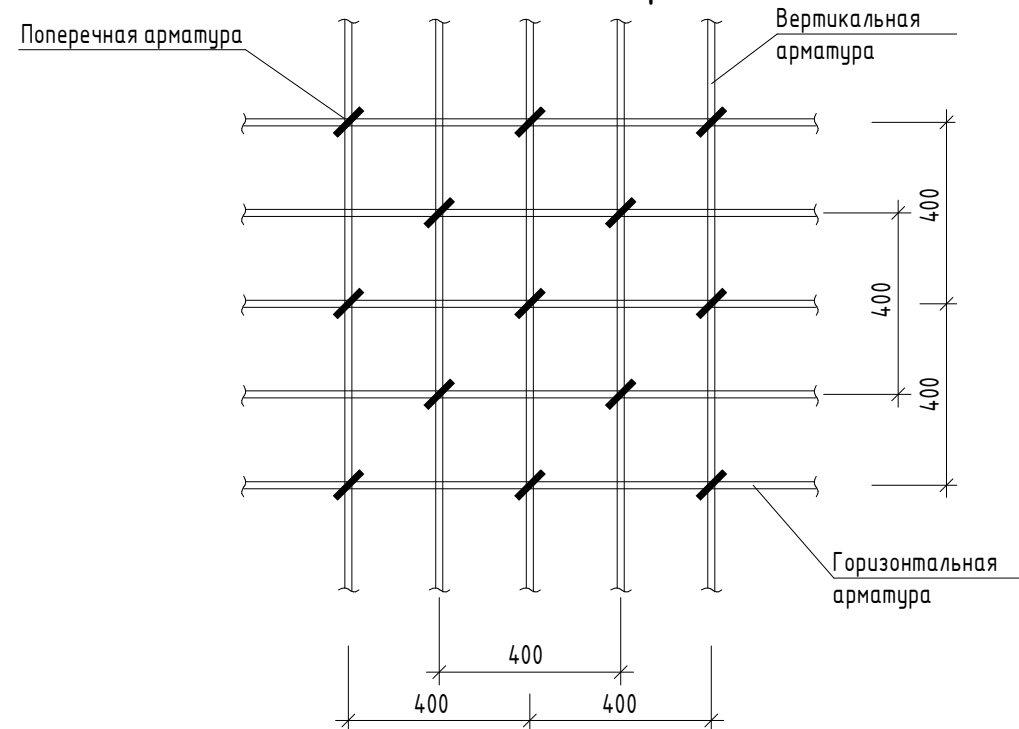


Схема стыка арматурных стержней (перепуск стержней без сварки)

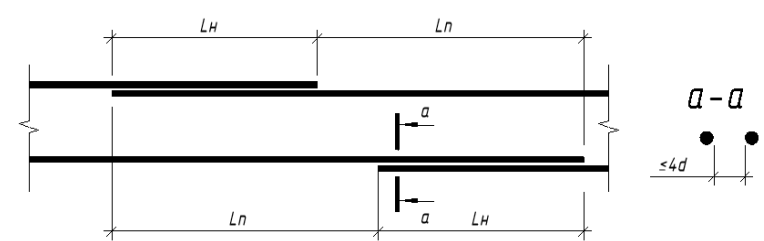

Тип арматуры	Длина нахлеста Lн	Длина анкеровки	Смещение нахлеста Lп, не менее	Позиция
Ø12 A500C	595	500	800	«варианты»


Условные обозначения:
з.с. - защитный слой бетона
~~~~~ - шов бетонирования  
-0,070 - Отметка верха и толщина плиты перекрытия  
+200

Маркировка позиций арматуры


Диаметр стержня, мм  
Длина стержня, см  
12/220  
6/200  
Шаг установки стержней, мм  
Количество стержней, шт  
Тип гнутой детали  
Диаметр стержня, мм  
Длина стержня, см  
X 12/140  
6/200  
Шаг установки стержней, мм  
Количество стержней, шт  
Диаметр стержня, мм  
12  
шаг 200  
Шаг установки стержней, мм

- Архитектурные планы и разрезы здания см. чертежи марки АР.
- Фактическое расположение существующих конструкций уточнить по месту.
- Общие указания см. лист 1.
- В основании фундаментов принят песок средней крупности с послойным уплотнением с коэффициентом уплотнения  $k=0.95$ .
- В случае обнаружения ниже подошвы проектируемого фундамента слабых грунтов, насыпи или грунтовых вод обратиться к проектной организации для принятия проектных решений.
- Для доковых поверхностей фундаментной плиты и стен соприкасающихся с грунтом, выполнить гидроизоляция 2 слоями горячего битума.
- Обратную засыпку пазух котлована выполнить песком средней крупности с послойным уплотнением с коэффициентом уплотнения  $k=0.95$ .
- Основное горизонтальное армирование фундаментной плиты выполняется отдельными стержнями Ø12A500C, крестообразные пере- сечения арматурных стержней вязать отожженной вязальной проволокой Ø10 мм в соответствии с требованиями приложения Ж ГОСТ 10922-2012, п. Ж5. Для фиксации нижних рядов арматуры и обеспечения защитного слоя применять незвлекательные фиксаторы из бетона или пластика.

Типовой Г-образный узел расположения арматурных стержней

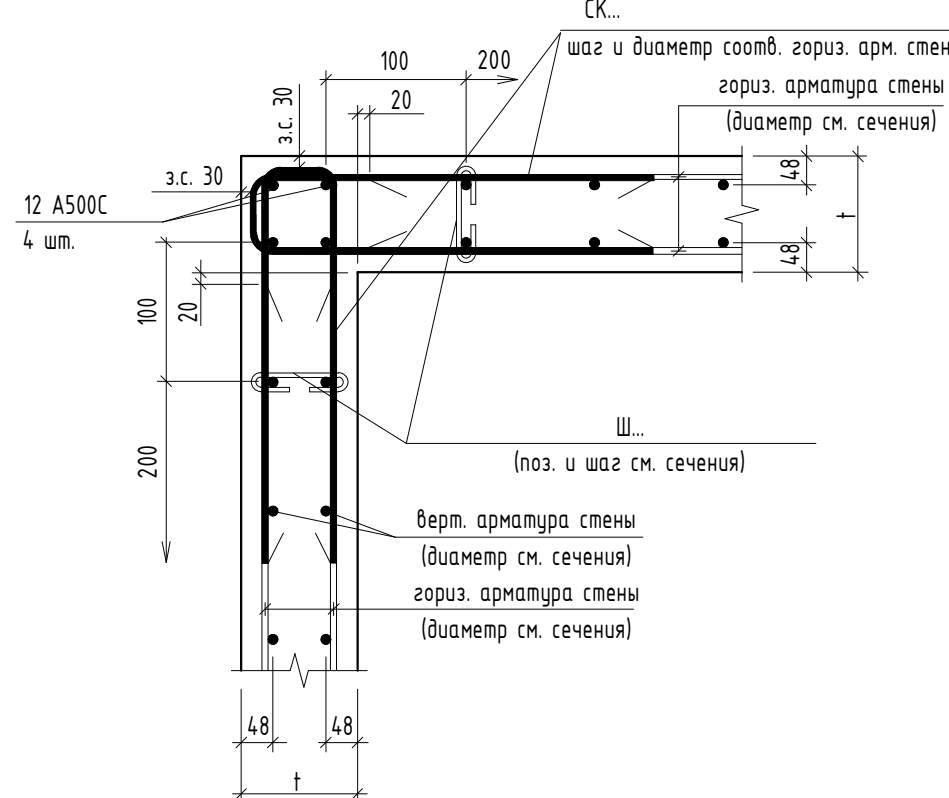

Типовой торцевой узел расположения арматурных стержней

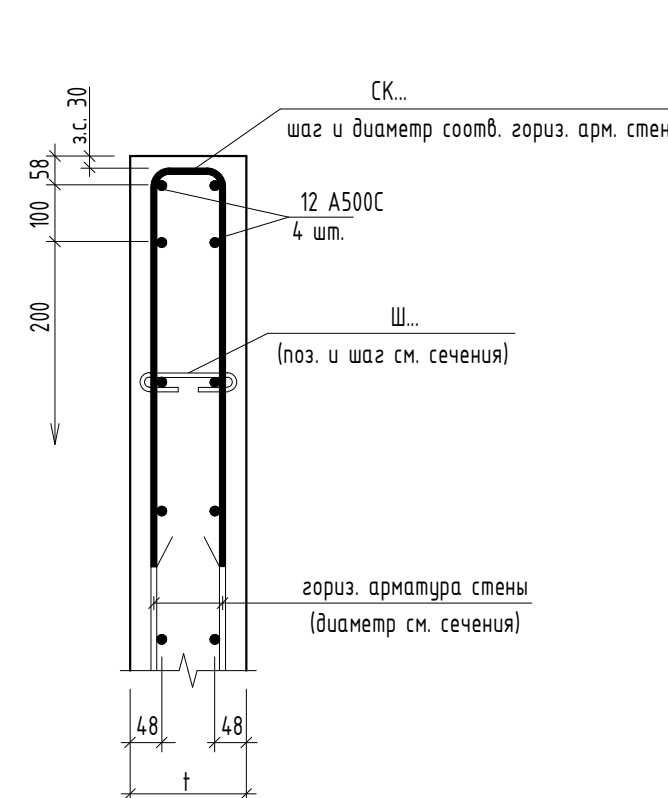

|          |               |      |        |         |   |                                                                |        |
|----------|---------------|------|--------|---------|---|----------------------------------------------------------------|--------|
|          |               |      |        |         | 16-25/Г-Р-КР2   |                                                                |        |
|          |               |      |        |         | Капитальный ремонт объекта "ГБОУ "Школа №429 "Сокольная гора", расположенного по адресу: г.Москва, ул.Соколиной Горы 5-ая, д.14 |                                                                |        |
| Изм.     | Кол.          | Лист | № док. | Подпись | Дата   | Конструктивные решения                                         | Стация |
| Разраб.  | Чех           |      |        |         | 99.99.99   |                                                                | Лист   |
| Проверил | Дидж          |      |        |         | 99.99.99   | Р                                                              | 6      |
| Н.контр. | Губарева Е.В. |      |        |         | 99.99.99   | Схема расположения форшахты в/о 14.1-K1. Опалубка. Армирование |        |
| ГИП      | Маркова       |      |        |         | 99.99.99   |                                                                |        |