

ВЕДОМОСТЬ РАБОЧИХ ЧЕРТЕЖЕЙ ОСНОВНОГО КОМПЛЕКТА КР5

Лист	Наименование	Примечание
1	Общие данные	
2	План перекрытия над подвалом в осях 1.1-17.1/Н-П1	
3	План перекрытия над подвалом в осях 1.1-17.1/Н-П1. Элементы усиления	
4	Спецификация элементов усиления к плану перекрытия над подвалом	
5	План перекрытия над 1 этажом в осях 1.1-17.1/Н-П1	
6	План перекрытия над 1 этажом в осях 1.1-17.1/Н-П1. Элементы усиления	
7	Спецификация элементов усиления к плану перекрытия над 1 этажом	
8	План перекрытия над 1 этажом в осях 1-23/А/1-В1	
9	План перекрытия над 1 этажом в осях 1-23/А/1-В1. Элементы усиления	
10	Спецификация элементов усиления к плану перекрытия над 1 этажом	
11	План перекрытия над 2 этажом в осях 1-23/А/1-В1	
12	План перекрытия над 2 этажом в осях 1-23/А/1-В1. Элементы усиления	
13	Спецификация элементов усиления к плану перекрытия над 2 этажом	
14	План перекрытия над 2 этажом в осях 1.1-17.1/Н-П1	
15	План перекрытия над 2 этажом в осях 1.1-17.1/Н-П1. Элементы усиления	
16	Спецификация элементов усиления к плану перекрытия над 2 этажом	
17	План перекрытия над 3 этажом в осях 1-23/А/1-В1	
18	План перекрытия над 3 этажом в осях 1-23/А/1-В1. Элементы усиления	
19	Спецификация элементов усиления к плану перекрытия над 3 этажом	
20	План перекрытия над 4 этажом в осях 1-23/А/1-В1	
21	План перекрытия над 4 этажом в осях 1-23/А/1-В1. Элементы усиления	
22	Принципиальные узлы замоноличивания проёмов	
23	Спецификация элементов усиления к плану перекрытия над 4 этажом	
24	План покрытия в осях 1.1-17.1/Н-П1	
25	План покрытия в осях 1.1-17.1/Н-П1. Элементы усиления	
26	Спецификация элементов усиления к плану покрытия	


ОБЩИЕ УКАЗАНИЯ

1. Данным комплектом выполнены чертежи по устройству и усилению вновь пробиваемых проёмов в плитах перекрытия. Комплект чертежей разработан на основании технического задания
2. Все работы выполнять в соответствии с требованиями СП 70.13330.2012 "Несущие и ограждающие конструкции".
3. ТРЕБОВАНИЯ К ВЫПОЛНЕНИЮ МОНОЛИТНЫХ РАБОТ:
- 3.1. Заполнение проёмов запроектировано из тяжелого бетона В25 по ГОСТ 26633-2015.
- 3.2. Армирование конструкций выполнять отдельными стержнями класса А500С по ГОСТ 34028-2016 с перевязкой их в местах пересечений вязальной проволокой Ø0,8-1,0мм. В сетках перевязывается не менее 50% всех пересечений арматуры, при этом перевязка выполняется в шахматном порядке.
- 3.3. Изготовление гнутых стержней производить в холодном состоянии по месту.
- 3.4. Бетонные работы выполнять при среднесуточной температуре воздуха выше +5С° или в соответствии с отдельным проектом производства работ в зимнее время.
- 3.5. Опалубку с конструкций снимать только после набора бетоном 40% проектной прочности.
- 3.6. Бетон должен соответствовать требованиям ГОСТ 26633-2015. Контроль прочности бетона следует производить неразрушающим методом по ГОСТ 22690-2015, ГОСТ 10180-2012
4. ТРЕБОВАНИЯ К ИЗГОТОВЛЕНИЮ И МОНТАЖУ СТАЛЬНЫХ КОНСТРУКЦИЙ:
- 4.1. Материалы стальных конструкций должны удовлетворять требованиям ГОСТ 27772-2021.
- 4.2. Материалы для сварки должны соответствовать табл. Г1 СП 16.13330.2017.
- 4.3. Сварные соединения должны удовлетворять требованиям раздела 4.10 ГОСТ 23118-2019.
- 4.4. Все металлоконструкции должны быть огрунтованы в один слой грунтовкой ГФ-021 по ГОСТ 25129-2020 и защищены от коррозии двумя слоями эмали ПФ-115 по ГОСТ 6465-2023. Для улучшения качества окраски рекомендуется применять грунтовки с преобразователем ржавчины. Общая толщина лакокрасочного покрытия, включая грунтовку, не менее 55 мкм
5. Технические решения, принятые в рабочих чертежах, соответствуют требованиям экологических, санитарно-гигиенических, противопожарных и других норм, действующих на территории Российской Федерации и обеспечивают безопасную для жизни людей эксплуатацию объекта при соблюдении предусмотренных рабочими чертежами мероприятий.
6. Открытые участки стальных элементов обработать огнезащитным составом, обеспечивающим предел огнестойкости не менее R120.

Взам. инв Н	
Подп. и дата	
Инв. Н подл.	

						16-25/Г -Р - КР5			
						Капитальный ремонт объекта "ГБОУ Школа №429 "Соколиная гора", расположенного по адресу: г. Москва, ул. Соколиной горы 5-я, д. 14.			
Изм	Кол.уч	Лист	№ док	Подпись	Дата	Конструктивные решения	Стадия	Лист	Листов
Разраб.		Варнашов			01.09.2026		Р	1	26
Проверил		Прудников			01.09.2026				
						Общие данные			
Н. контр.		Губарева			01.09.2026				
ГИП		Маркова			01.09.2026				


План перекрытия над подвалом в осях 1.1-17.1/Н-П.1

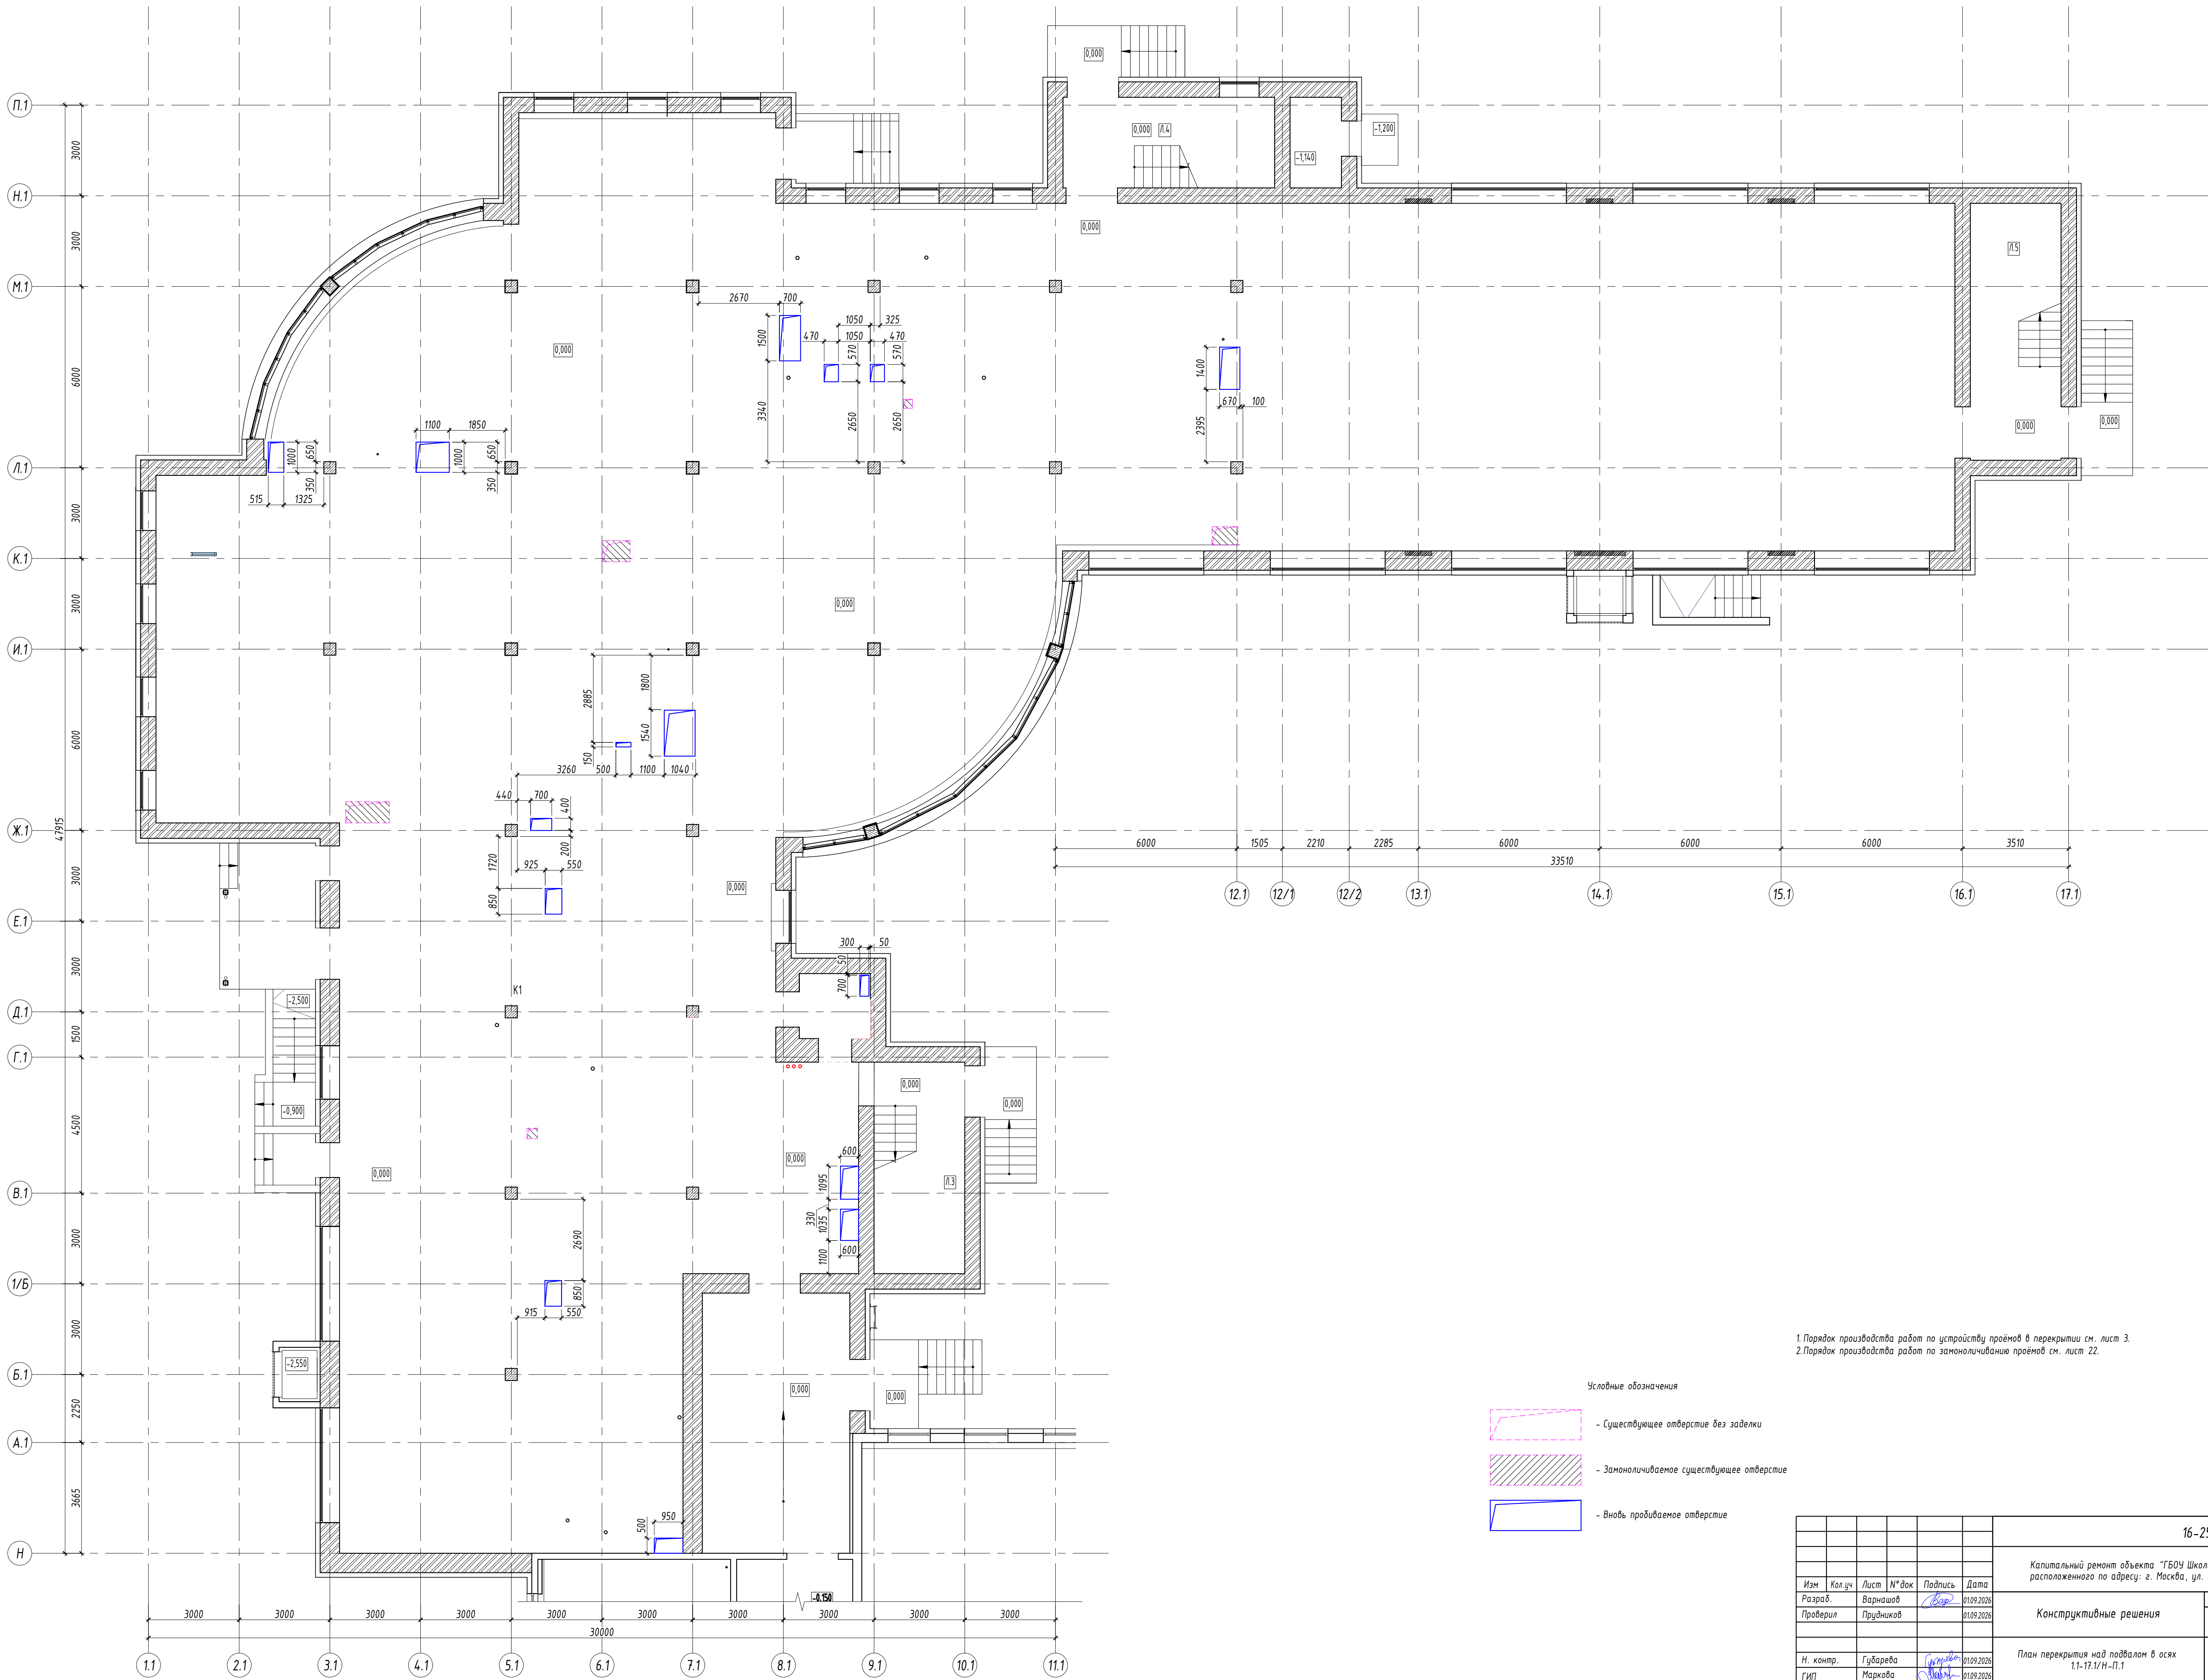

1.Порядок производства работ по устройству проёмов в перекрытии см. лист 3.
2.Порядок производства работ по замоноличиванию проёмов см. лист 22.

Составлено	ВК	ЗМ	СС
ГАП			
ОВ			
Взам. инв. Н.			
Подп. и дата			
Инв. Н. подл.			

						16-25/Г-Р-КР5		
						Капитальный ремонт объекта "ГБОУ Школа №429 "Соколиная гора", расположенного по адресу: г. Москва, ул. Соколиной горы 5-я, д. 14.		
Изм.	Кол.уч.	Лист	№ док	Подпись	Дата	Конструктивные решения	Стадия	Лист
Разраб.	Варнашов	01.09.2026		Вар	01.09.2026		Р	2
Проверил	Прудников	01.09.2026						
						План перекрытия над подвалом в осях 1.1-17.1/Н-П.1		
Н. контр.	Гударева	01.09.2026		Гударева	01.09.2026	АЗУРИТ		
ГИП	Маркова	01.09.2026		Маркова	01.09.2026			

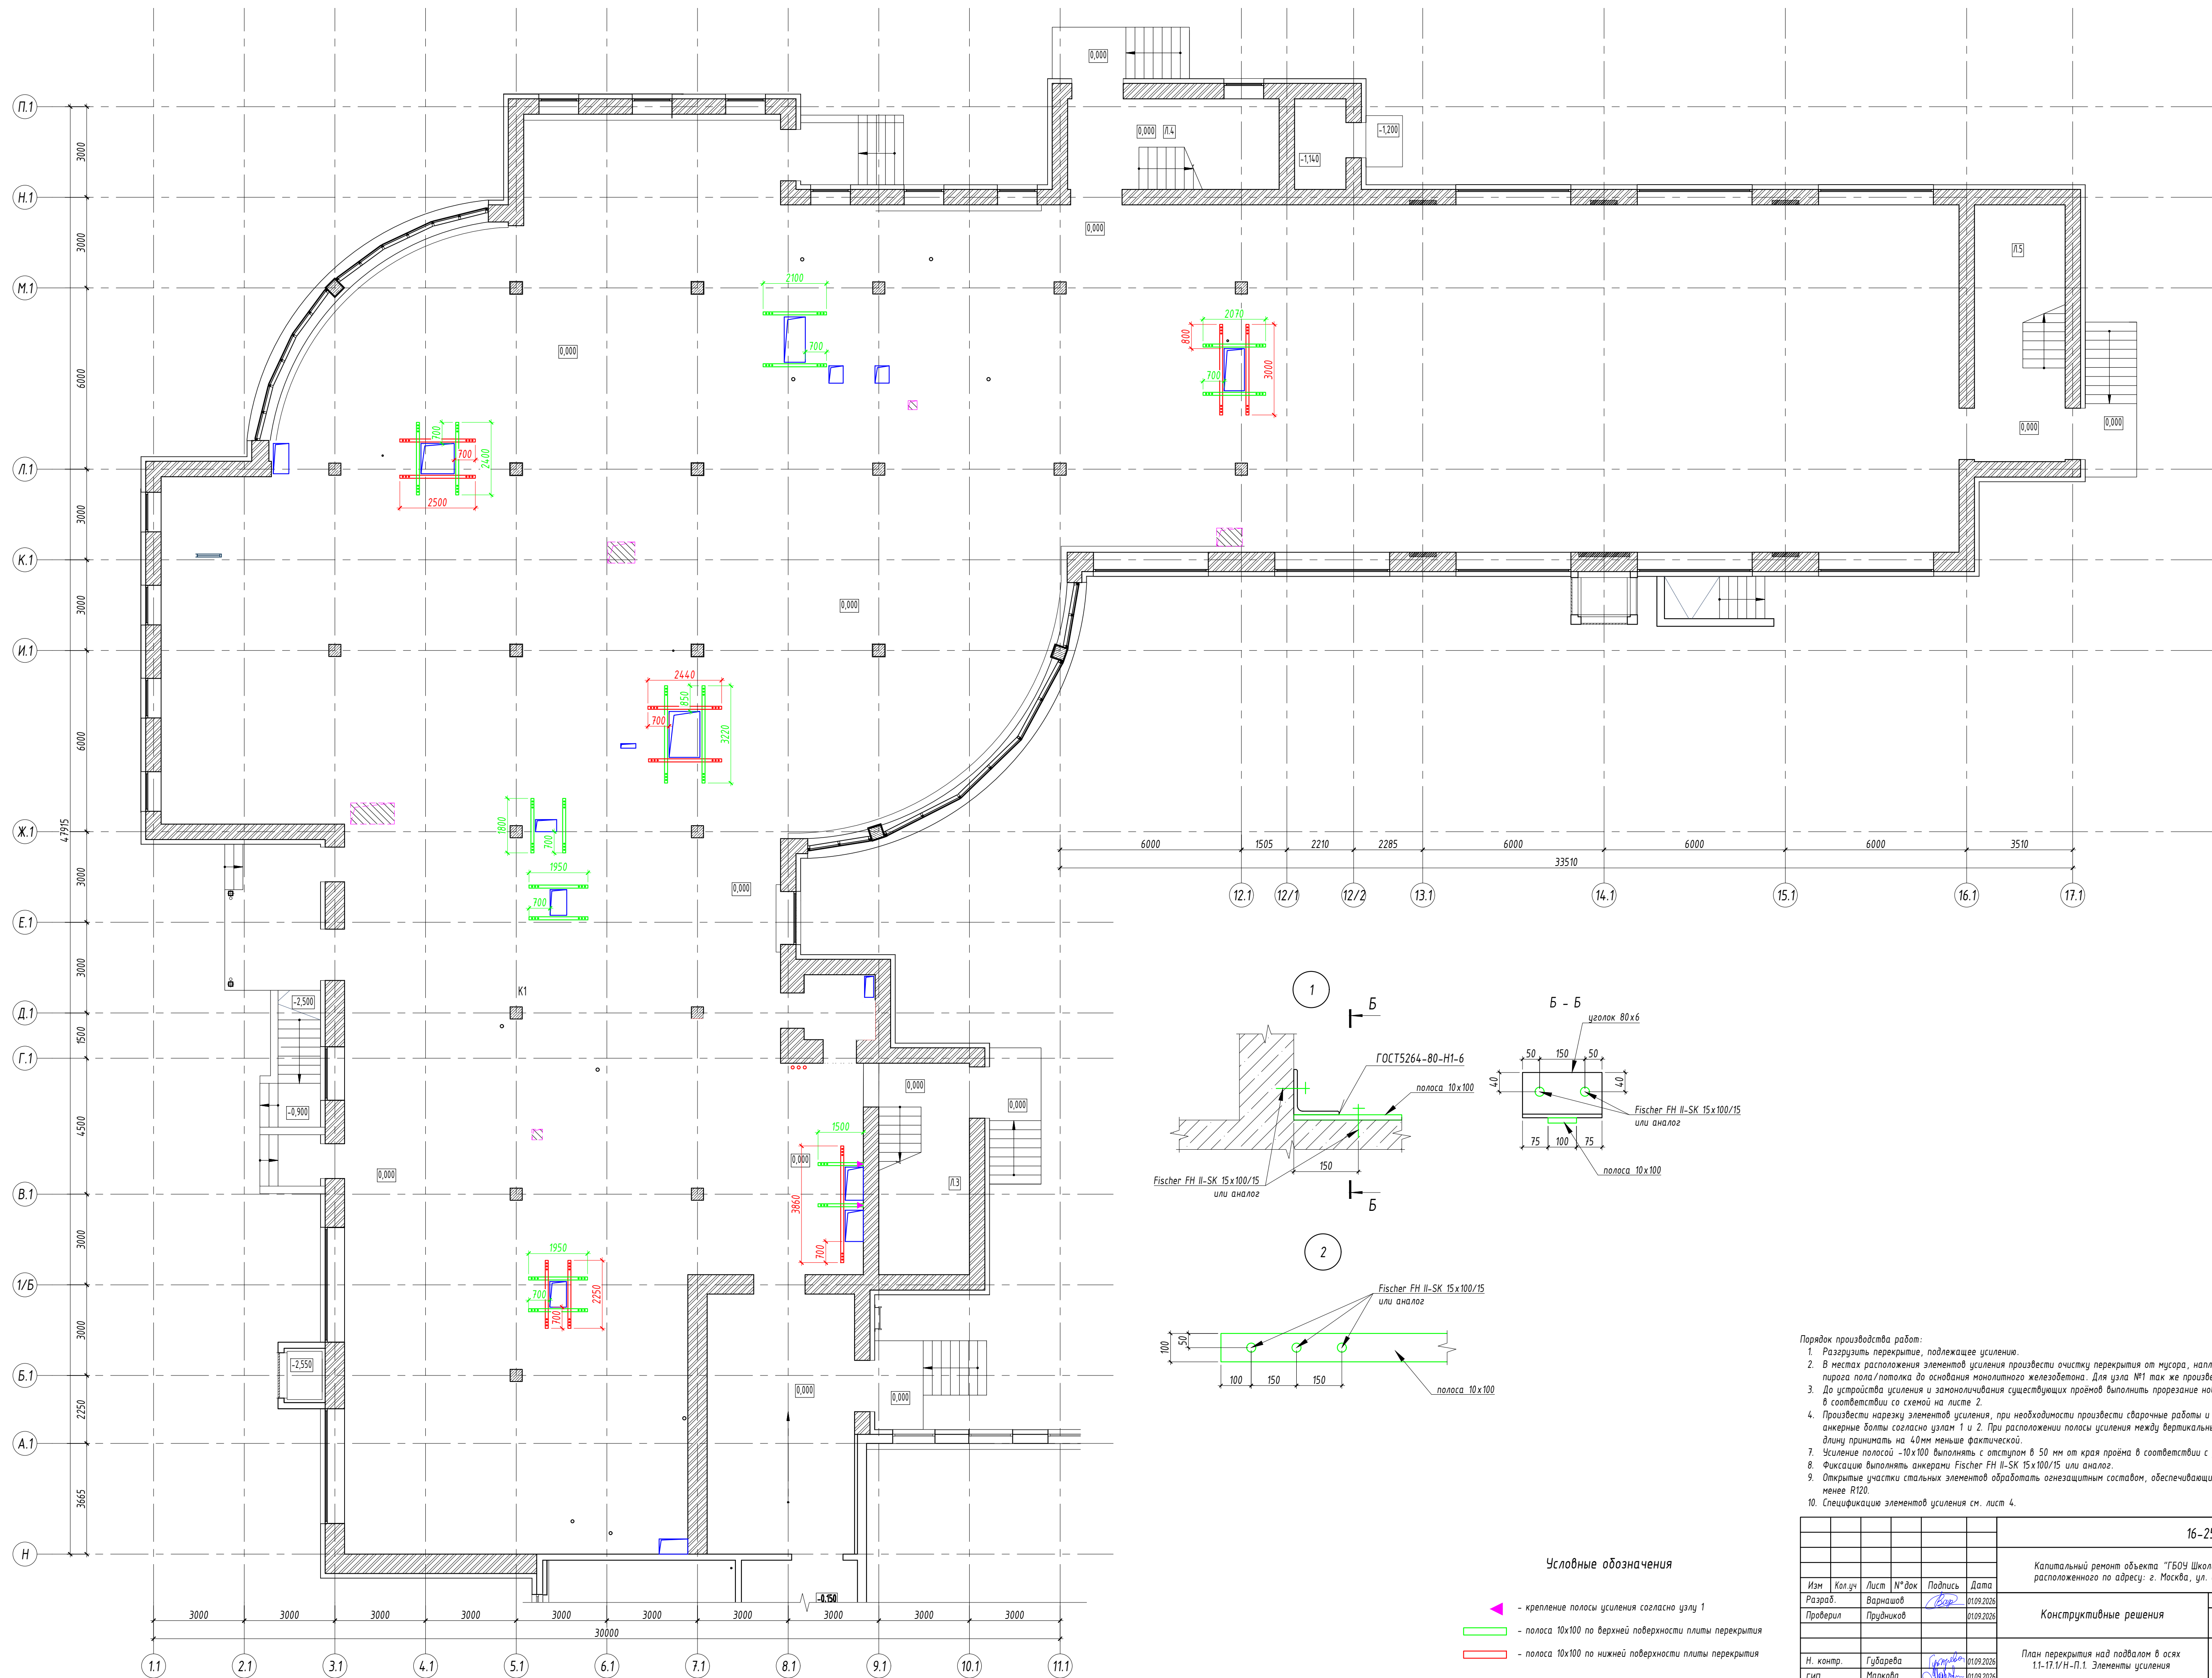


						16-25/Г - Р - КР5					
						Капитальный ремонт объекта "ГБОУ Школа №429 "Сокольная гора", расположенного по адресу: г. Москва, ул. Соколиной горы 5-я, э. 14.					
Изм.	Кол.уч	Лист	№ док	Подпись	Дата	Конструктивные решения	Станд	Лист	Листов		
Разработ		Варнашов			01/09/2026						
Проверил		Гудачников			01/09/2026		Р	З			
Н. контр.		Губарева			01/09/2026	План перекрытия над подвалом в осях 1.1-17.Н-П.1. Элементы усиления		АЗУРИТ			
ГИП		Маркова			01/09/2026						

Спецификация элементов усиления к плану перекрытия над подвалом

Поз.	Обозначение	Наименование	Кол.	Масса ед., кг	Примечание
	ГОСТ 34028-2016	Ø10 А500С L=м.п.	205,7	0,616	126,7
	ГОСТ 103-2006	-10х100 L=м.п.	60,5	7,85	474,9
	ГОСТ 8509-93	Уголок 80х80х6 L=м.п.	0,5	7,36	3,7
	Анкерный болт втулочный	Fischer FH II-SK 15х100/15 (или аналог)			150 шт.
		Материалы			
	ГОСТ 25029-2020	Грунтовка ГФ-021 (за 1 раз)			6,21 м²
	ГОСТ 6465-2023	Эмаль ПФ-115 (за 2 раза)			12,42 м²
	ГОСТ 26633-2015	Бетон В25			0,47 м³
	ГОСТ 28013-98	Цементно-песчаный раствор М100			7,8 м³

Взам. инв. N											
Подп. и дата								16-25/Г -Р - КР5			
		Изм	Кол.уч	Лист	№ док	Подпись	Дата	Капитальный ремонт объекта "ГБОУ Школа №429 "Соколиная гора", расположенного по адресу: г. Москва, ул. Соколиной горы 5-я, д. 14.			
		Разраб.		Варнашов			01.09.2026				
Инв. N подл.		Проверил		Прудников		01.09.2026	Конструктивные решения	Стадия	Лист	Листов	
								Р	4		
		Н. контр.		Гударева			01.09.2026	Спецификация элементов усиления к плану перекрытия над подвалом	 АЗУРИТ		
		ГИП		Маркова			01.09.2026				

План перекрытия над 1 этажом в осях 1.1-17.1/Н-П.1

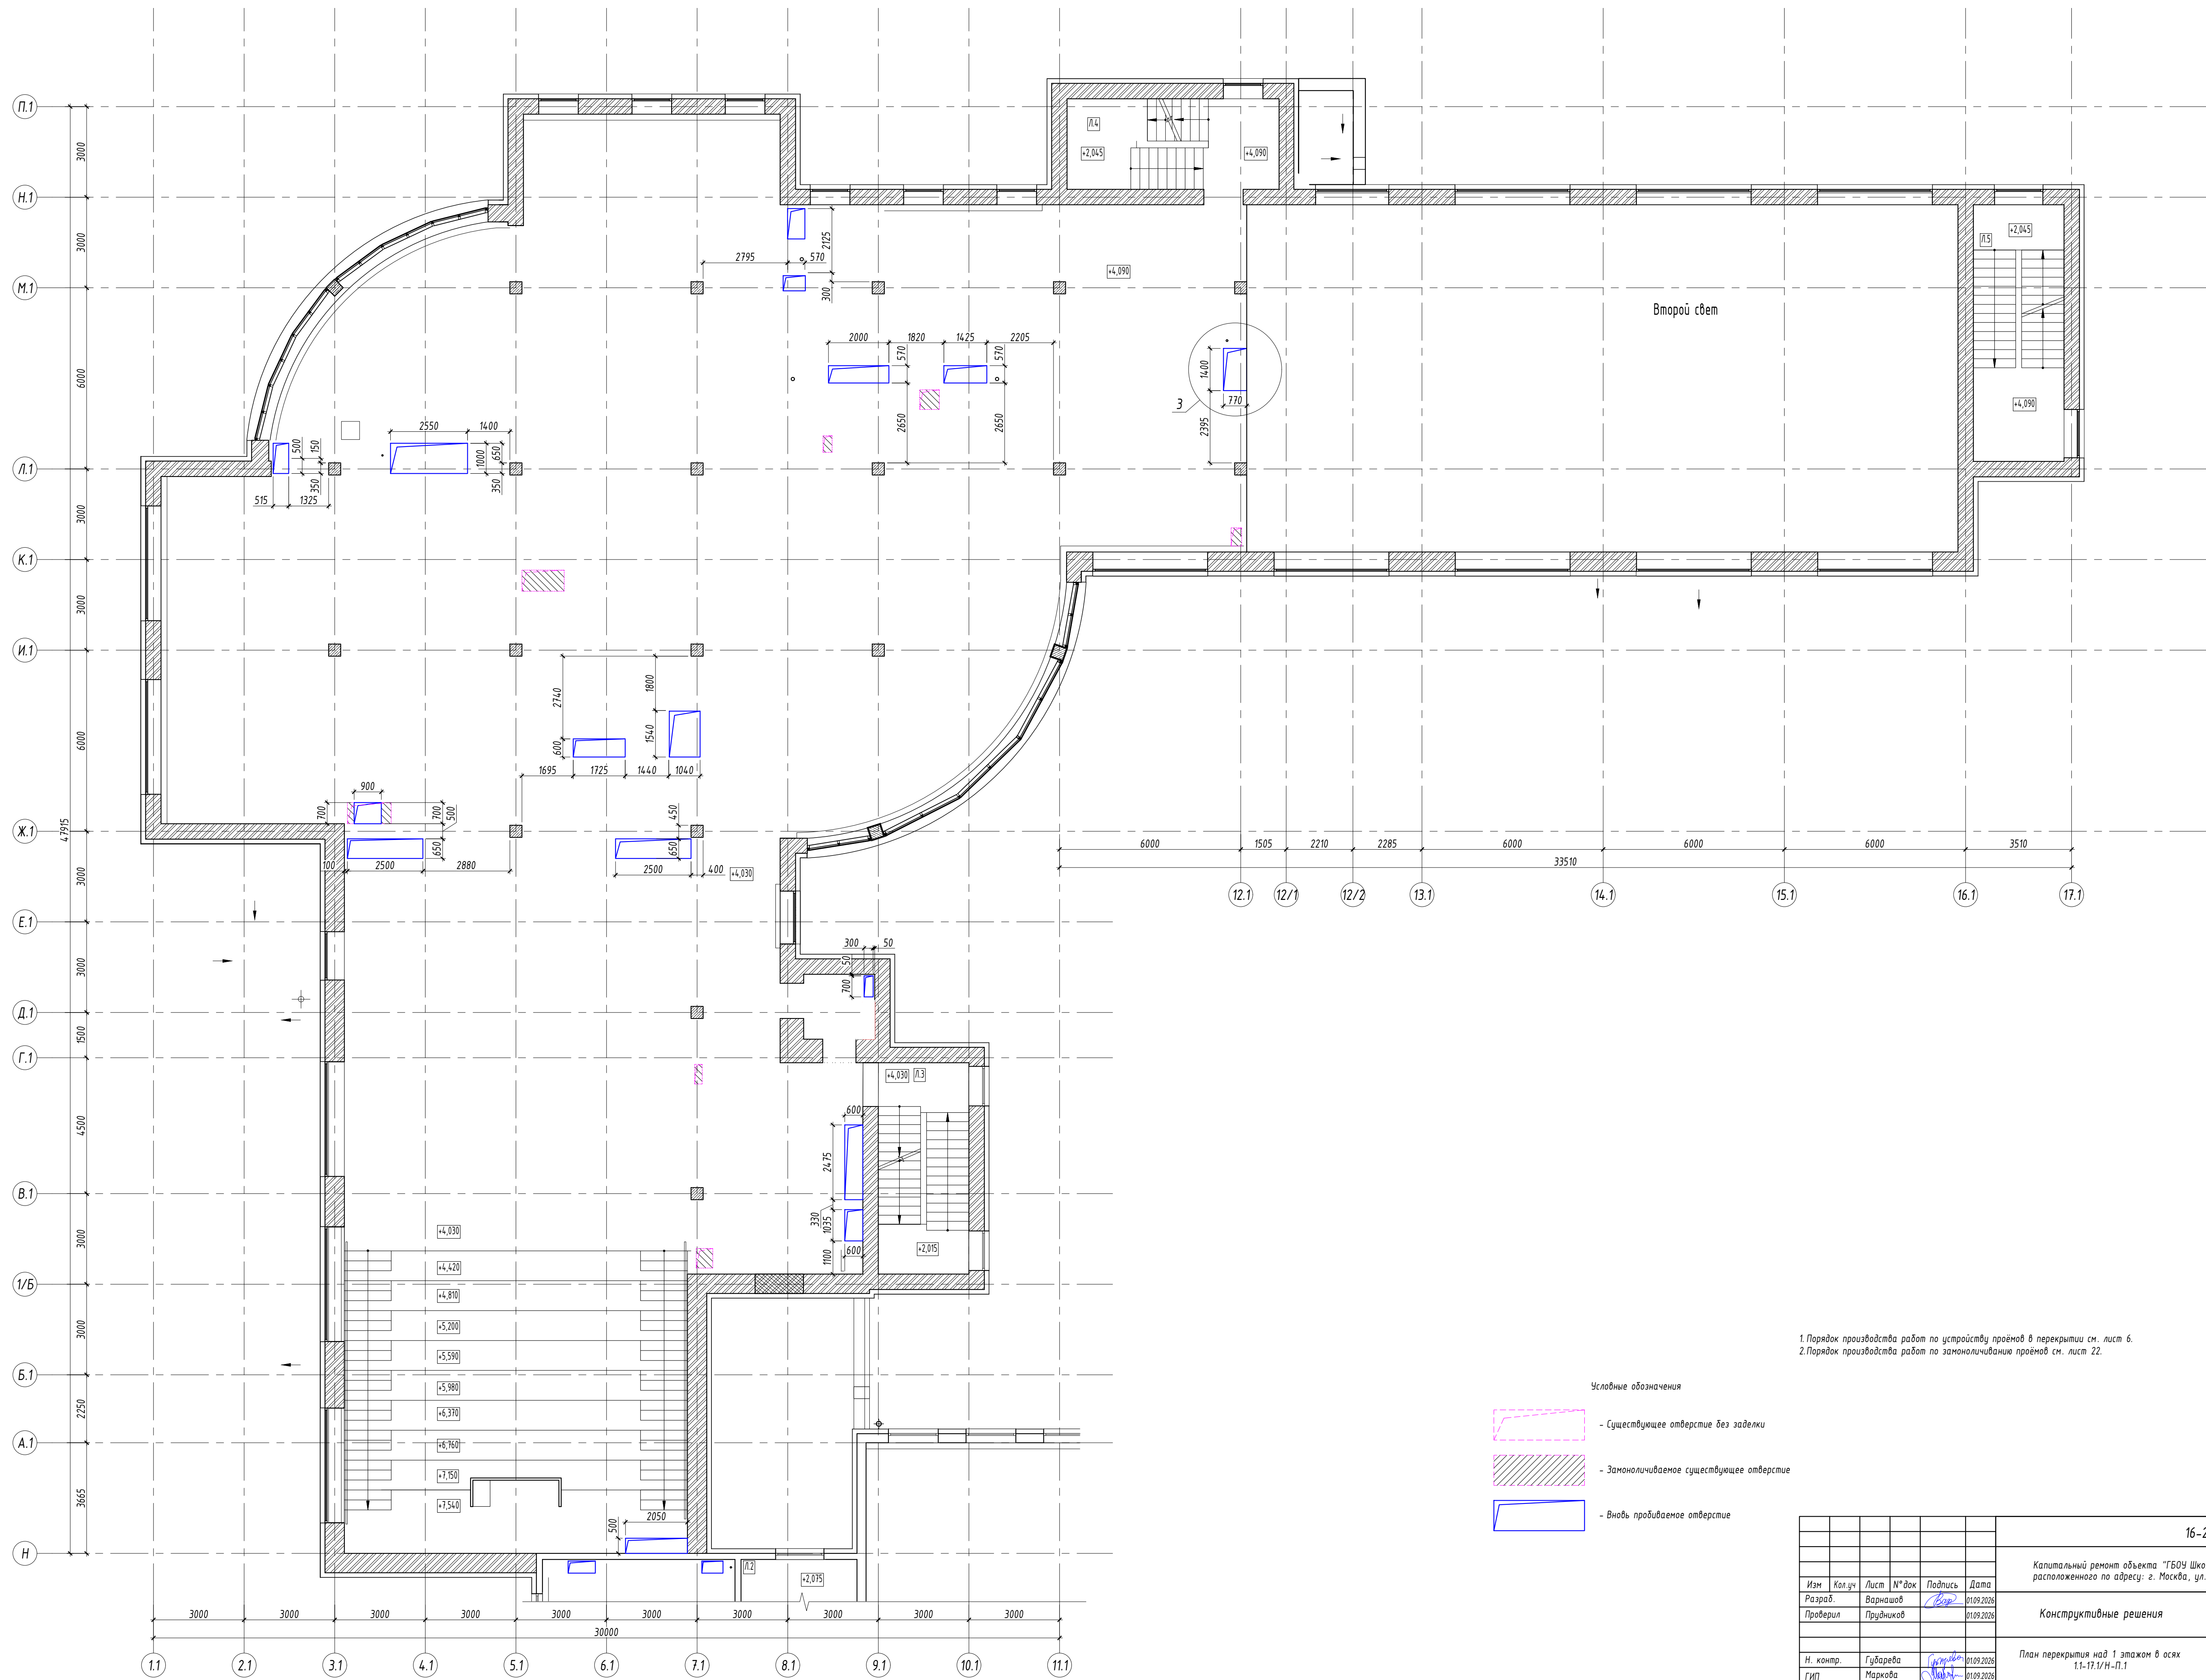


1.Порядок производства работ по устройству проёмов в перекрытии см. лист 6.
2.Порядок производства работ по замоноличиванию проёмов см. лист 22.

Условные обозначения

- Существующее отверстие без заделки
- Замоноличиваемое существующее отверстие
- вновь пробиваемое отверстие

						16-25/Г-Р-КР5		
						Капитальный ремонт объекта "ГБОУ Школа №429 "Соколиная гора", расположенного по адресу: г. Москва, ул. Соколиной горы 5-я, д. 14.		
Изм.	Кол.уч.	Лист	№ док	Подпись	Дата	Конструктивные решения	Стадия	Лист
Разраб.	Вариантов	01.09.2026		Вар	01.09.2026		Р	5
Проверил	Прудников	01.09.2026						
						План перекрытия над 1 этажом в осях 1.1-17.1/Н-П.1		
Н. контр.	Гударева	01.09.2026		Гударева	01.09.2026	АЗУРИТ		
ГИП	Маркова	01.09.2026		Маркова	01.09.2026			

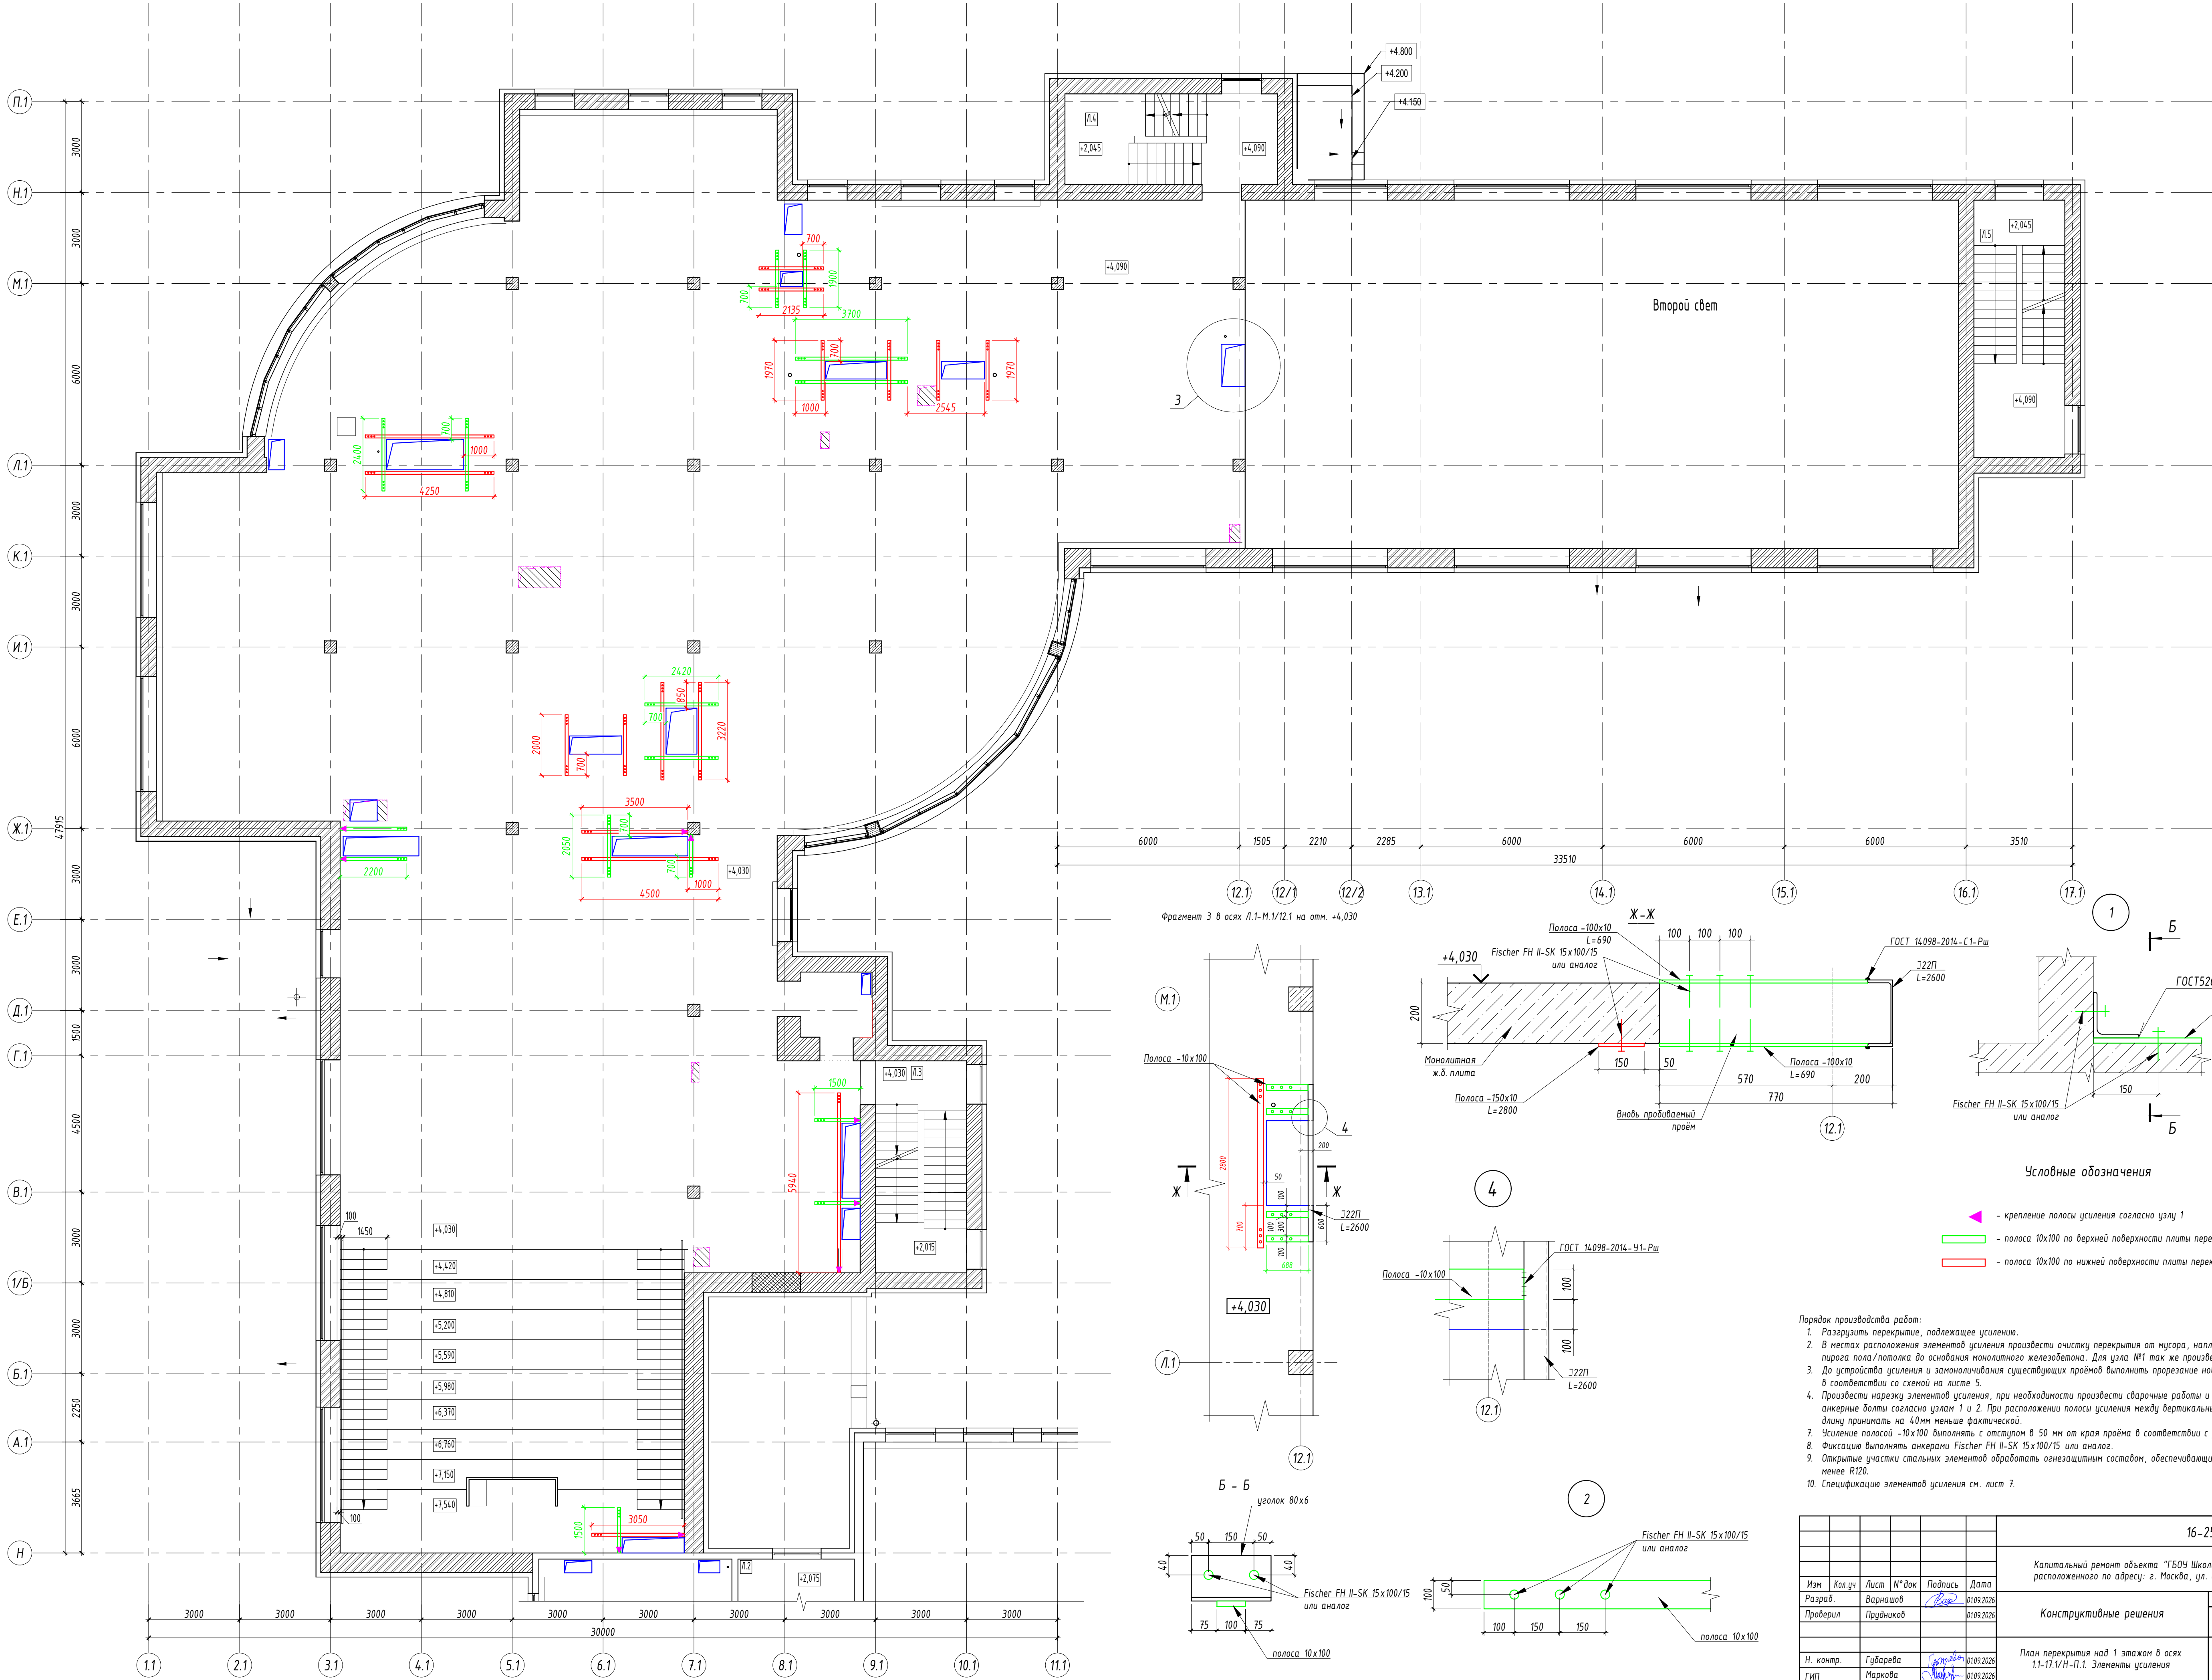

Условные обозначения

- ▲ - крепление полосы усиления согласно узлу 1
- - полоса 10x100 по верхней поверхности плиты перекрытия
- - полоса 10x100 по нижней поверхности плиты перекрытия

Порядок производства работ:


- Разрезать перекрытие, подлежащее усилению.
- В местах расположения элементов усиления произвести очистку перекрытия от мусора, наливов раствора, элементов старого пола/потола до основания монолитного железобетона. Для узла №1 так же произвести очистку участка стены.
- До устройства усиления и замоноличивания существующих проёмов выполнить прорезание новых проёмов в плите перекрытия, в соответствии со схемой на листе 5.
- Произвести нарезку элементов усиления, при необходимости произвести сварочные работы и выполнение отверстий под анкерные болты согласно узлам 1 и 2. При расположении полосы усиления между вертикальными монолитными конструкциями длину принимать на 40мм меньше фактической.
- Усиление полосой -10x100 выполнять с отступом в 50 мм от края проёма в соответствии с разрезом В-В на листе 21.
- Фиксацию выполнять анкерами Fischer FH II-SK 15x100/15 или аналог.
- Открытые участки стальных элементов обработать огнезащитным составом, обеспечивающим предел огнестойкости не менее R120.
- Спецификация элементов усиления см. лист 7.

					16-25/Г-Р-КР5		
					Капитальный ремонт объекта "ГБОУ Школа №429 "Сокольная гора", расположенного по адресу: г. Москва, ул. Соколовой горы 5-я, д. 14.		
					Конструктивные решения		
					Стадия	Лист	Листов
					Р	6	
					План перекрытия над 1 этажом в осях 1.1-17.1/Н-П.1. Элементы усиления		
Изм.	Кол. изм.	Лист	№ док.	Подпись	Дата		
Разраб.	Вариантов	01/09/2026					
Проверил	Прудников	01/09/2026					
Н. контр.	Гударева	01/09/2026					
ГИП	Маркова	01/09/2026					

Спецификация элементов усиления к плану перекрытия над 1 этажом


Поз.	Обозначение	Наименование	Кол.	Масса ед., кг	Примечание
	ГОСТ 34028-2016	Ø10 А500С L=м.п.	205,7	0,616	126,7
	ГОСТ 103-2006	-10x100 L=м.п.	89,7	7,85	704,1
	ГОСТ 8509-93	Уголок 80x80x6 L=м.п.	2,3	7,36	16,6
	ГОСТ 8240-97	Швеллер 22П L=м.п.	2,6	14,2	36,9
	Анкерный болт втулочный	Fischer FH II-SK 15x100/15 (или аналог)			198 шт.
		Материалы			
	ГОСТ 25029-2020	Грунтовка ГФ-021 (за 1 раз)			9,13 м ²
	ГОСТ 6465-2023	Эмаль ПФ-115 (за 2 раза)			18,26 м ²
	ГОСТ 26633-2015	Бетон В25			0,54 м ³
	ГОСТ 28013-98	Цементно-песчаный раствор М100			7,8 м ³

Взам. инв. N										
Подп. и дата								16-25/Г -Р - КР5		
		Изм	Кол.уч	Лист	№ док	Подпись	Дата	Капитальный ремонт объекта "ГБОУ Школа №429 "Соколиная гора", расположенного по адресу: г. Москва, ул. Соколиной горы 5-я, д. 14.		
		Разраб.		Варнашов			01.09.2026			
Проверил		Прудников			01.09.2026	Конструктивные решения	Стадия	Лист	Листов	
							Р	7		
Инв. N подл.		Н. контр.		Гударева			01.09.2026	Спецификация элементов усиления к плану перекрытия над 1 этажом		
		ГИП		Маркова			01.09.2026			
								 АЗУРИТ		

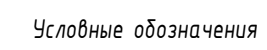

1. Порядок производства работ по устройству проёмов в перекрытии см. лист 9.
2. Порядок производства работ по замоноличиванию проёмов см. лист 22.




FORMAT A1

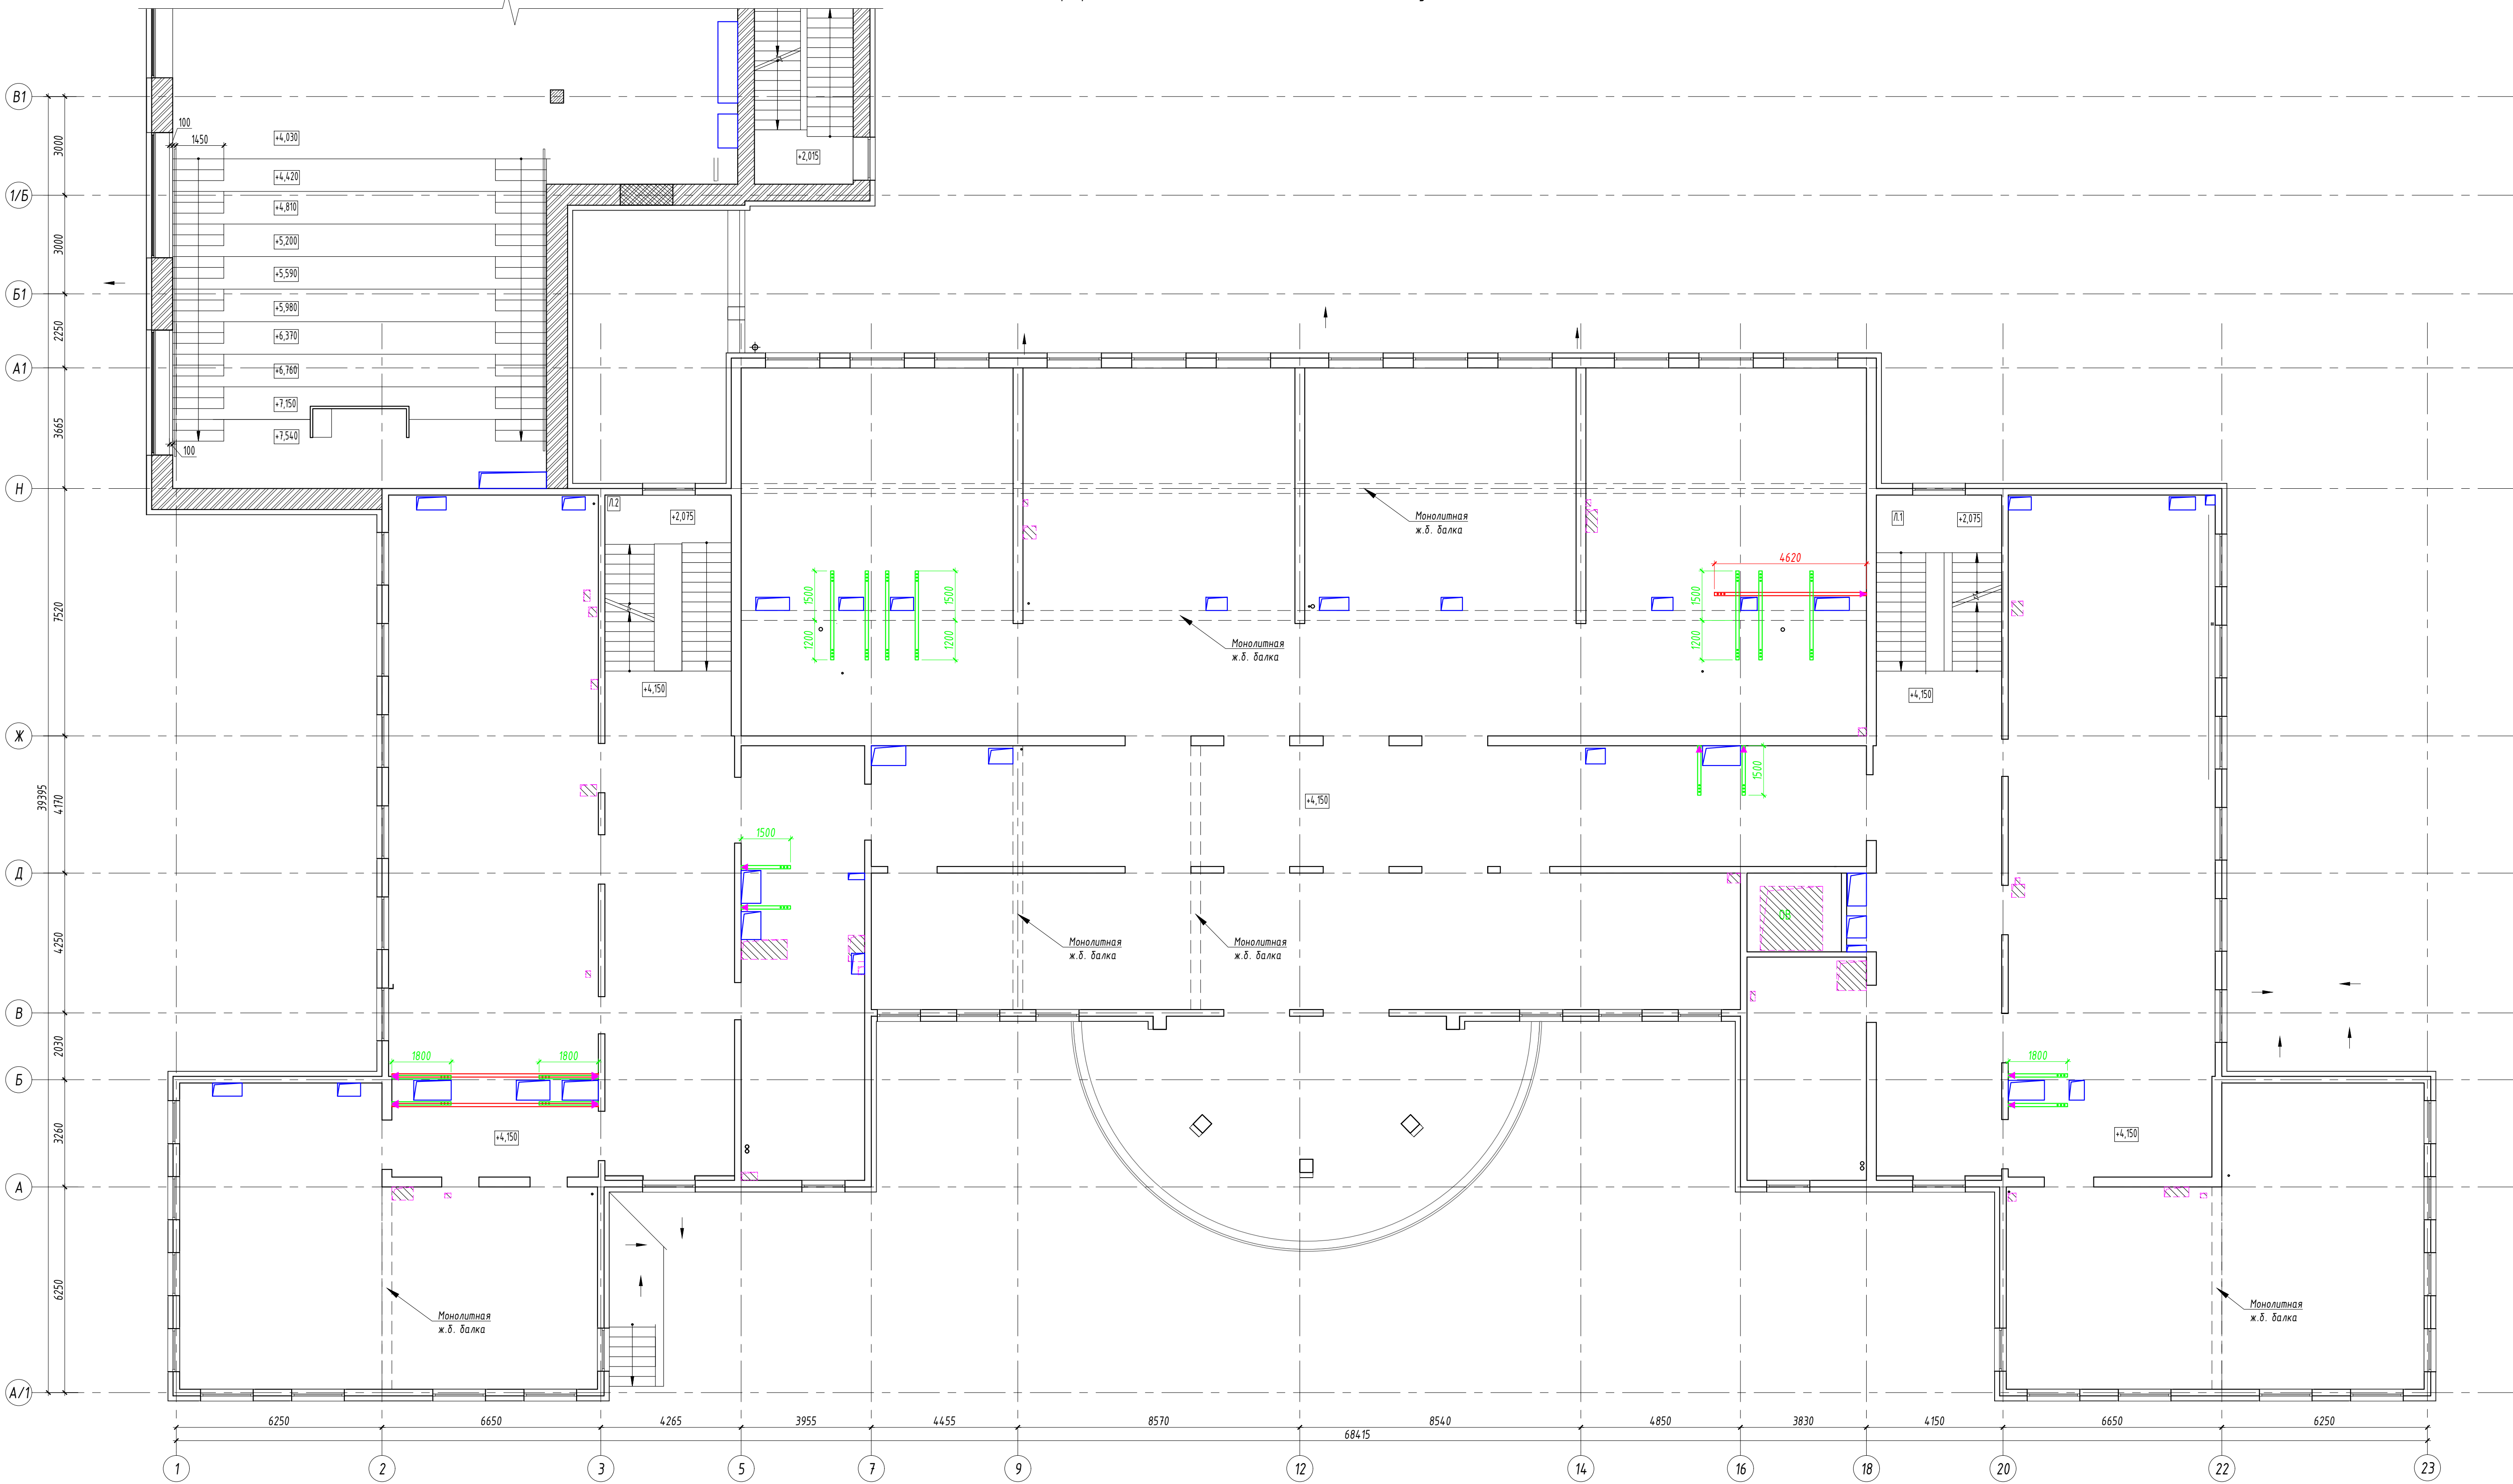

- Порядок производства работ:
- Разрушить перекрытие, подлежащее усилению.
 - В местах расположения элементов усиления произвести очистку перекрытия от мусора, наливов раствора, элементов пирога пола/потолка до основания монолитного железобетона. Для узла №1 так же произвести очистку участка стены.
 - До устройства усиления и замоноличивания существующих проёмов выполнить прорезание новых проёмов в плите перекрытия, в соответствии со схемой на листе 8.
 - Произвести нарезку элементов усиления, при необходимости произвести сварочные работы и выполнение отверстий под анкерные болты согласно узлам 1 и 2. При расположении полосы усиления между вертикальными монолитными конструкциями длину принимать на 40мм меньше фактической.
 - Усиление полосой -10х100 выполнять с отступом в 50 мм от края проёма в соответствии с разрезом В-В на листе 21.
 - Фиксация выполнять анкерами Fischer FH II-SK 15х100/15 или аналог.
 - Открытые участки стальных элементов обработать огнезащитным составом, обеспечивающим предел огнестойкости не менее R120.
 - Спецификация элементов усиления см. лист 10.

Условные обозначения

- ▲ - крепление полосы усиления согласно узлу 1
- - полоса 10х100 по верхней поверхности плиты перекрытия
- - полоса 10х100 по нижней поверхности плиты перекрытия

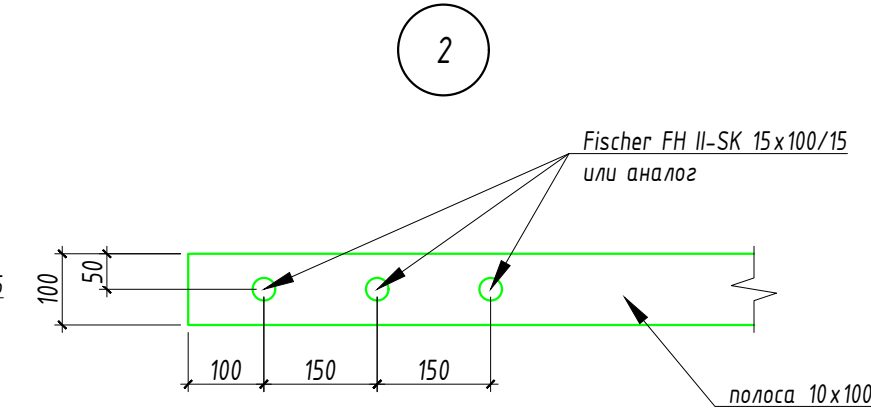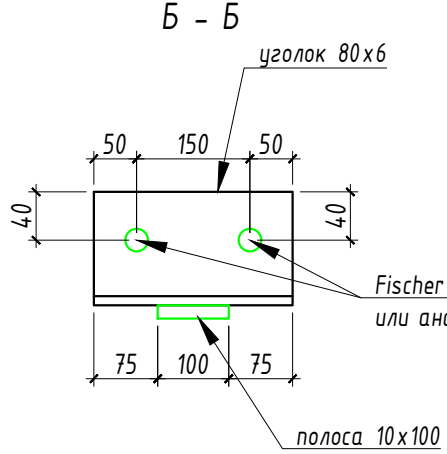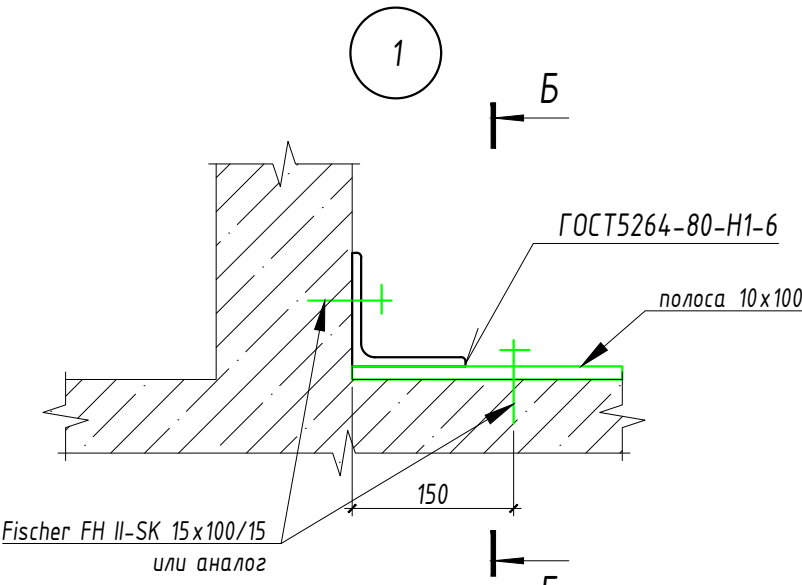

Вариант №	
Лист №	
Имя и дата	
Имя и подпись	


					16-25/Г - Р - КР5		
					Капитальный ремонт объекта "ГБОУ Школа №429 "Соколиная гора", расположенного по адресу: г. Москва, ул. Соколиной горы 5-я, д. 14.		
Изм	Кол.уч	Лист	№ док	Подпись	Дата		
Разработ		Варнашов		<i>Вар</i>	01.09.2026	Стадия	Лист
Проверил		Прудников			01.09.2026	Р	9
Конструктивные решения							
План перекрытия над 1 этажом в осях 1-23/А/1-В1. Элементы усиления							
Н. контр.		Губарева		<i>Губарева</i>	01.09.2026	 АЗУРИ	
ГИП		Маркова		<i>Маркова</i>	01.09.2026		
ФОРМАТ А1							

Спецификация элементов усиления к плану перекрытия над 1 этажом

Поз.	Обозначение	Наименование	Кол.	Масса ед., кг	Примечание
	ГОСТ 34028-2016	Ø10 А500С L=м.п.	205,7	0,616	126,7
	ГОСТ 103-2006	-10x100 L=м.п.	54,7	7,85	429,4
	ГОСТ 8509-93	Уголок 80x80x6 L=м.п.	3,8	7,36	27,6
	Анкерный болт втулочный	Fischer FH II-SK 15x100/15 (или аналог)			120 шт.
		Материалы			
	ГОСТ 25029-2020	Грунтовка ГФ-021 (за 1 раз)			6,646 м ²
	ГОСТ 6465-2023	Эмаль ПФ-115 (за 2 раза)			13,3 м ²
	ГОСТ 26633-2015	Бетон В25			1,57 м ³
	ГОСТ 28013-98	Цементно-песчаный раствор М100			7,8 м ³

Взам. инв N										
Подп. и дата							16-25/Г -Р - КР5			
	Изм	Кол.уч	Лист	№ док	Подпись	Дата				
	Разраб.		Варнашов			01.09.2026				
Инв. N подл.	Проверил		Прудников			01.09.2026	Конструктивные решения	Стадия	Лист	Листов
								Р	10	
	Н. контр.		Гударева			01.09.2026	Спецификация элементов усиления к плану перекрытия над 1 этажом	 АЗУРИТ		
	ГИП		Маркова			01.09.2026				

План перекрытия над 2 этажом в осях 1-23/А/1-В1

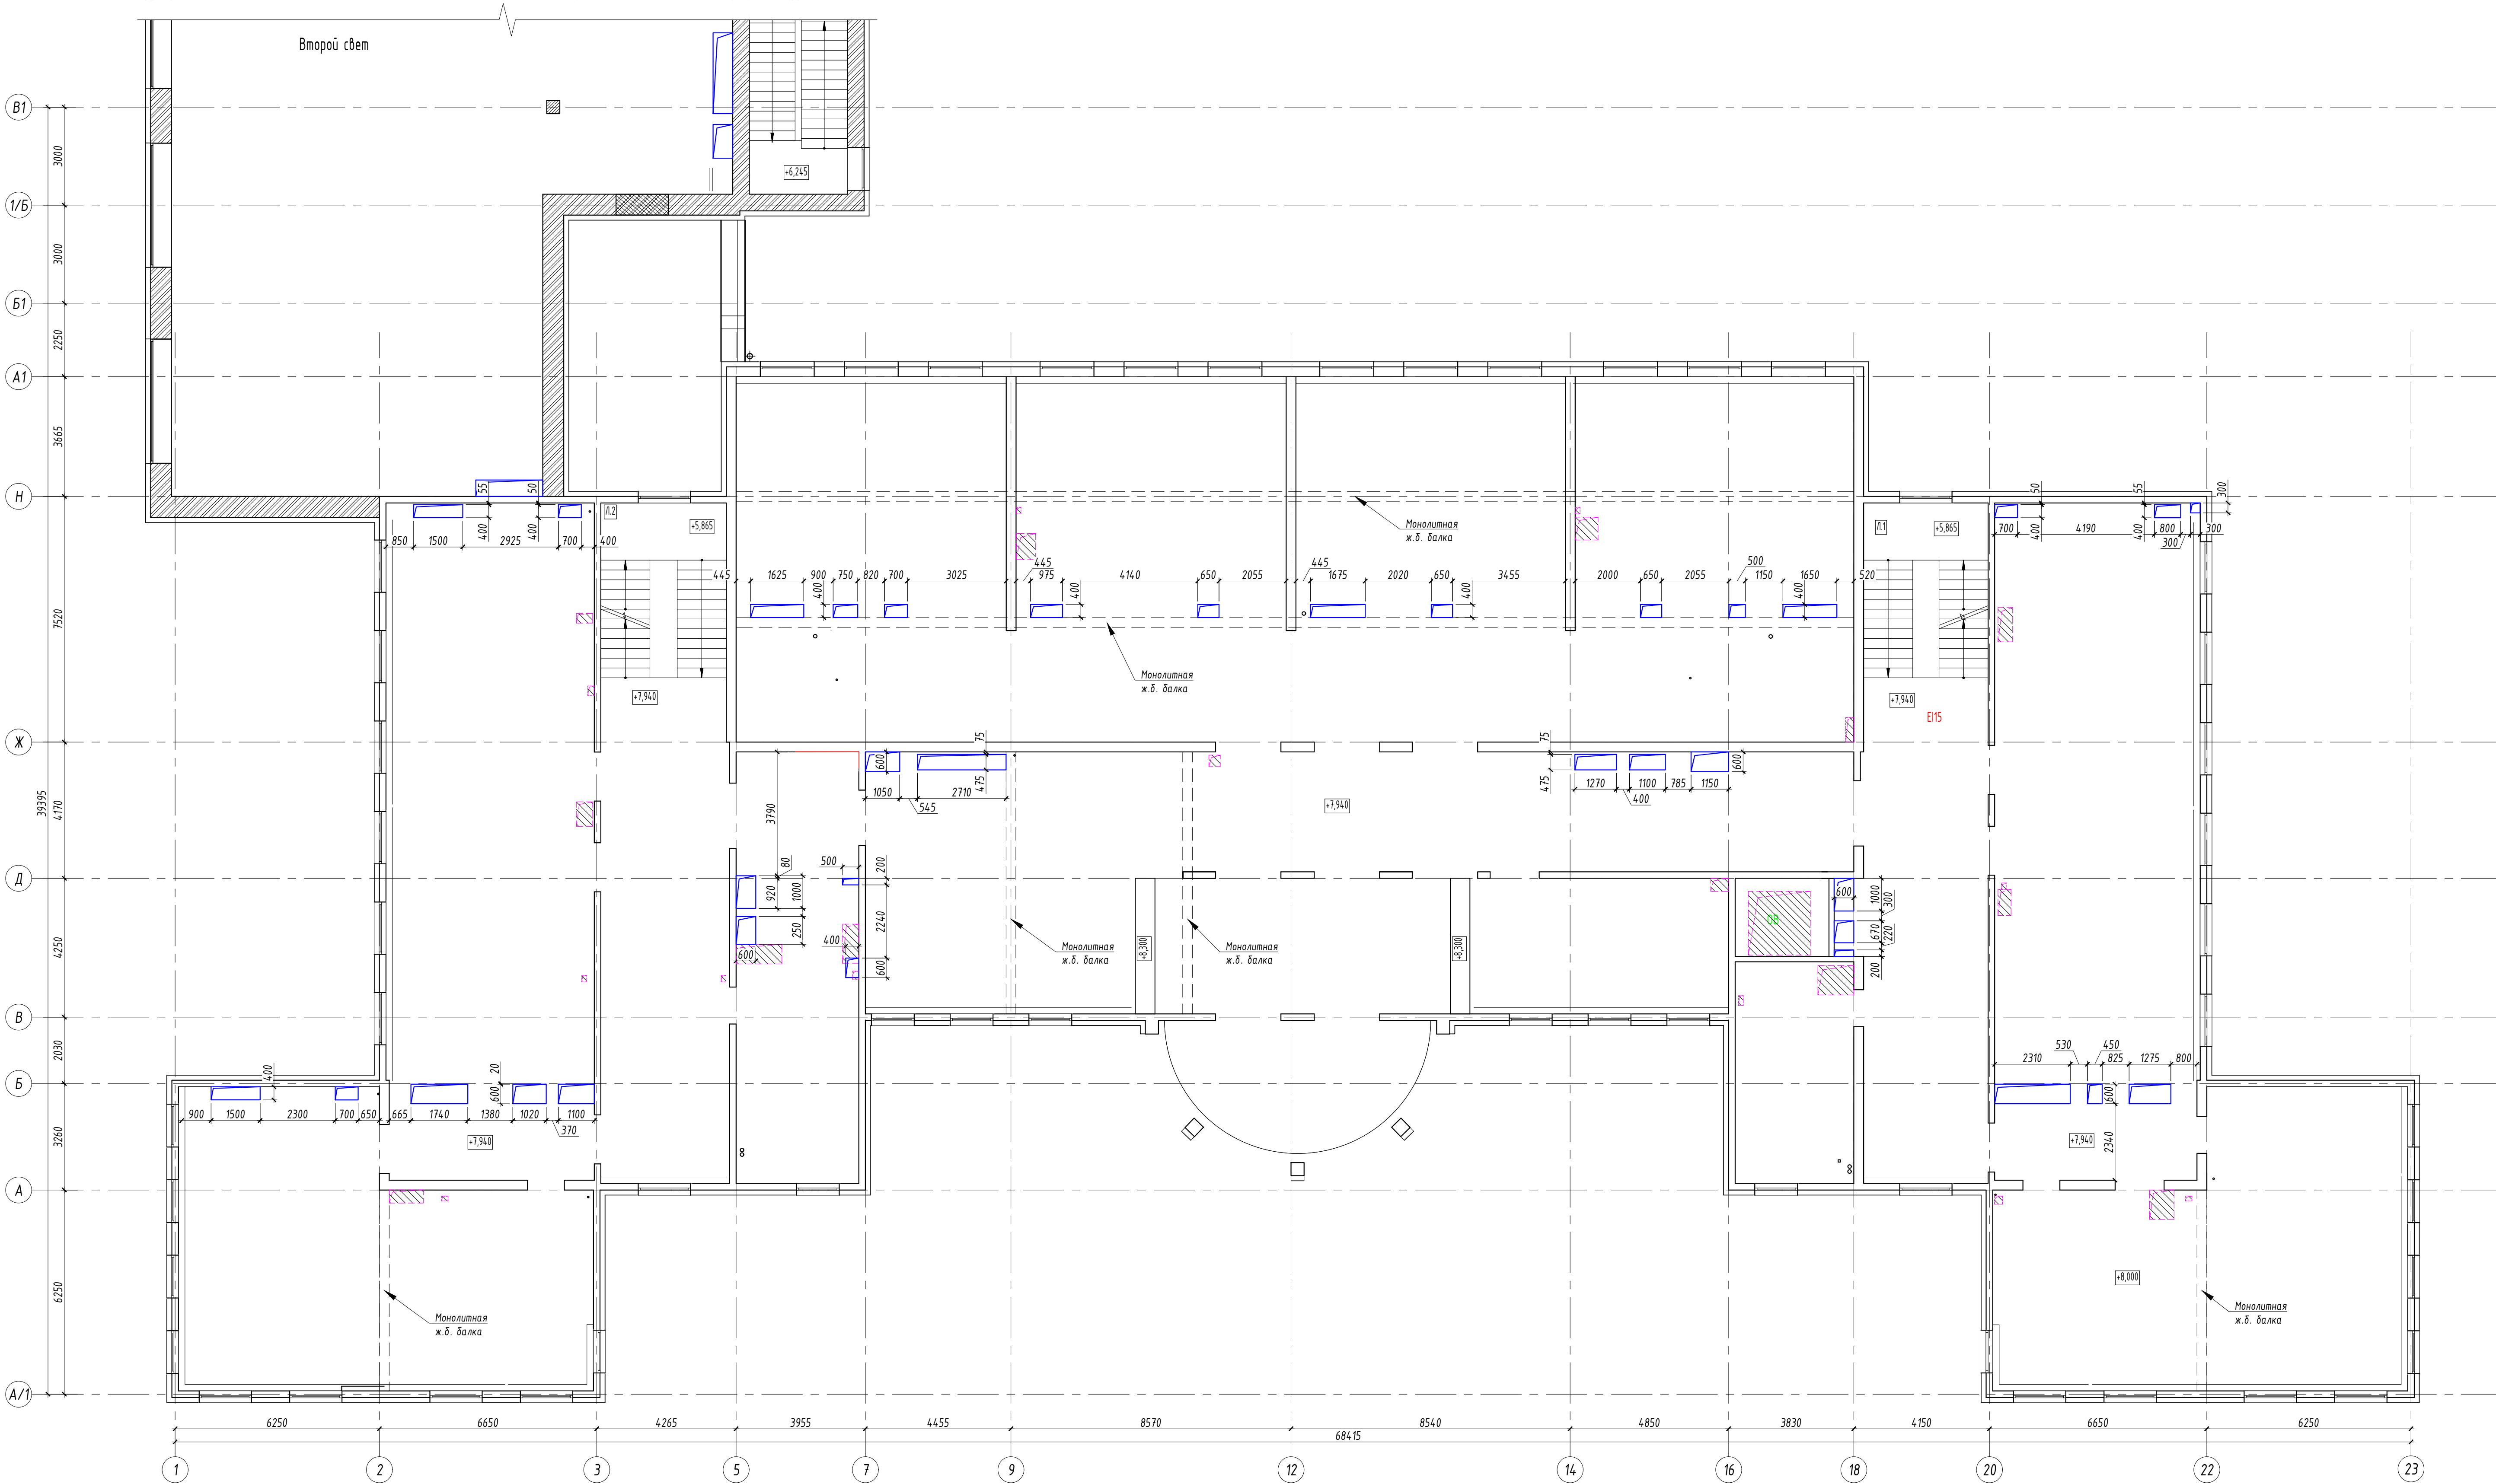


Условные обозначения

- Существующее отверстие без заделки
- Замоноличиваемое существующее отверстие
- вновь пробиваемое отверстие

1.Порядок производства работ по устройству проёмов в перекрытии см. лист 12.
2.Порядок производства работ по замоноличиванию проёмов см. лист 22.

						16-25/Г-Р-КР5		
						Капитальный ремонт объекта "ГБОУ Школа №429 "Соколиная гора", расположенного по адресу: г. Москва, ул. Соколиной горы 5-я, д. 14.		
Изм.	Кол. изм.	Лист	№ док.	Подпись	Дата	Конструктивные решения	Стадия	Лист
Разраб.		Варнашов	01.09.2026	Вар			Р	11
Проверил		Прудников	01.09.2026					
						План перекрытия над 2 этажом в осях 1-23/А/1-В1		
Н. контр.		Гударева	01.09.2026	Гударева		АЗУРИТ		
ГИП		Маркова	01.09.2026	Маркова				

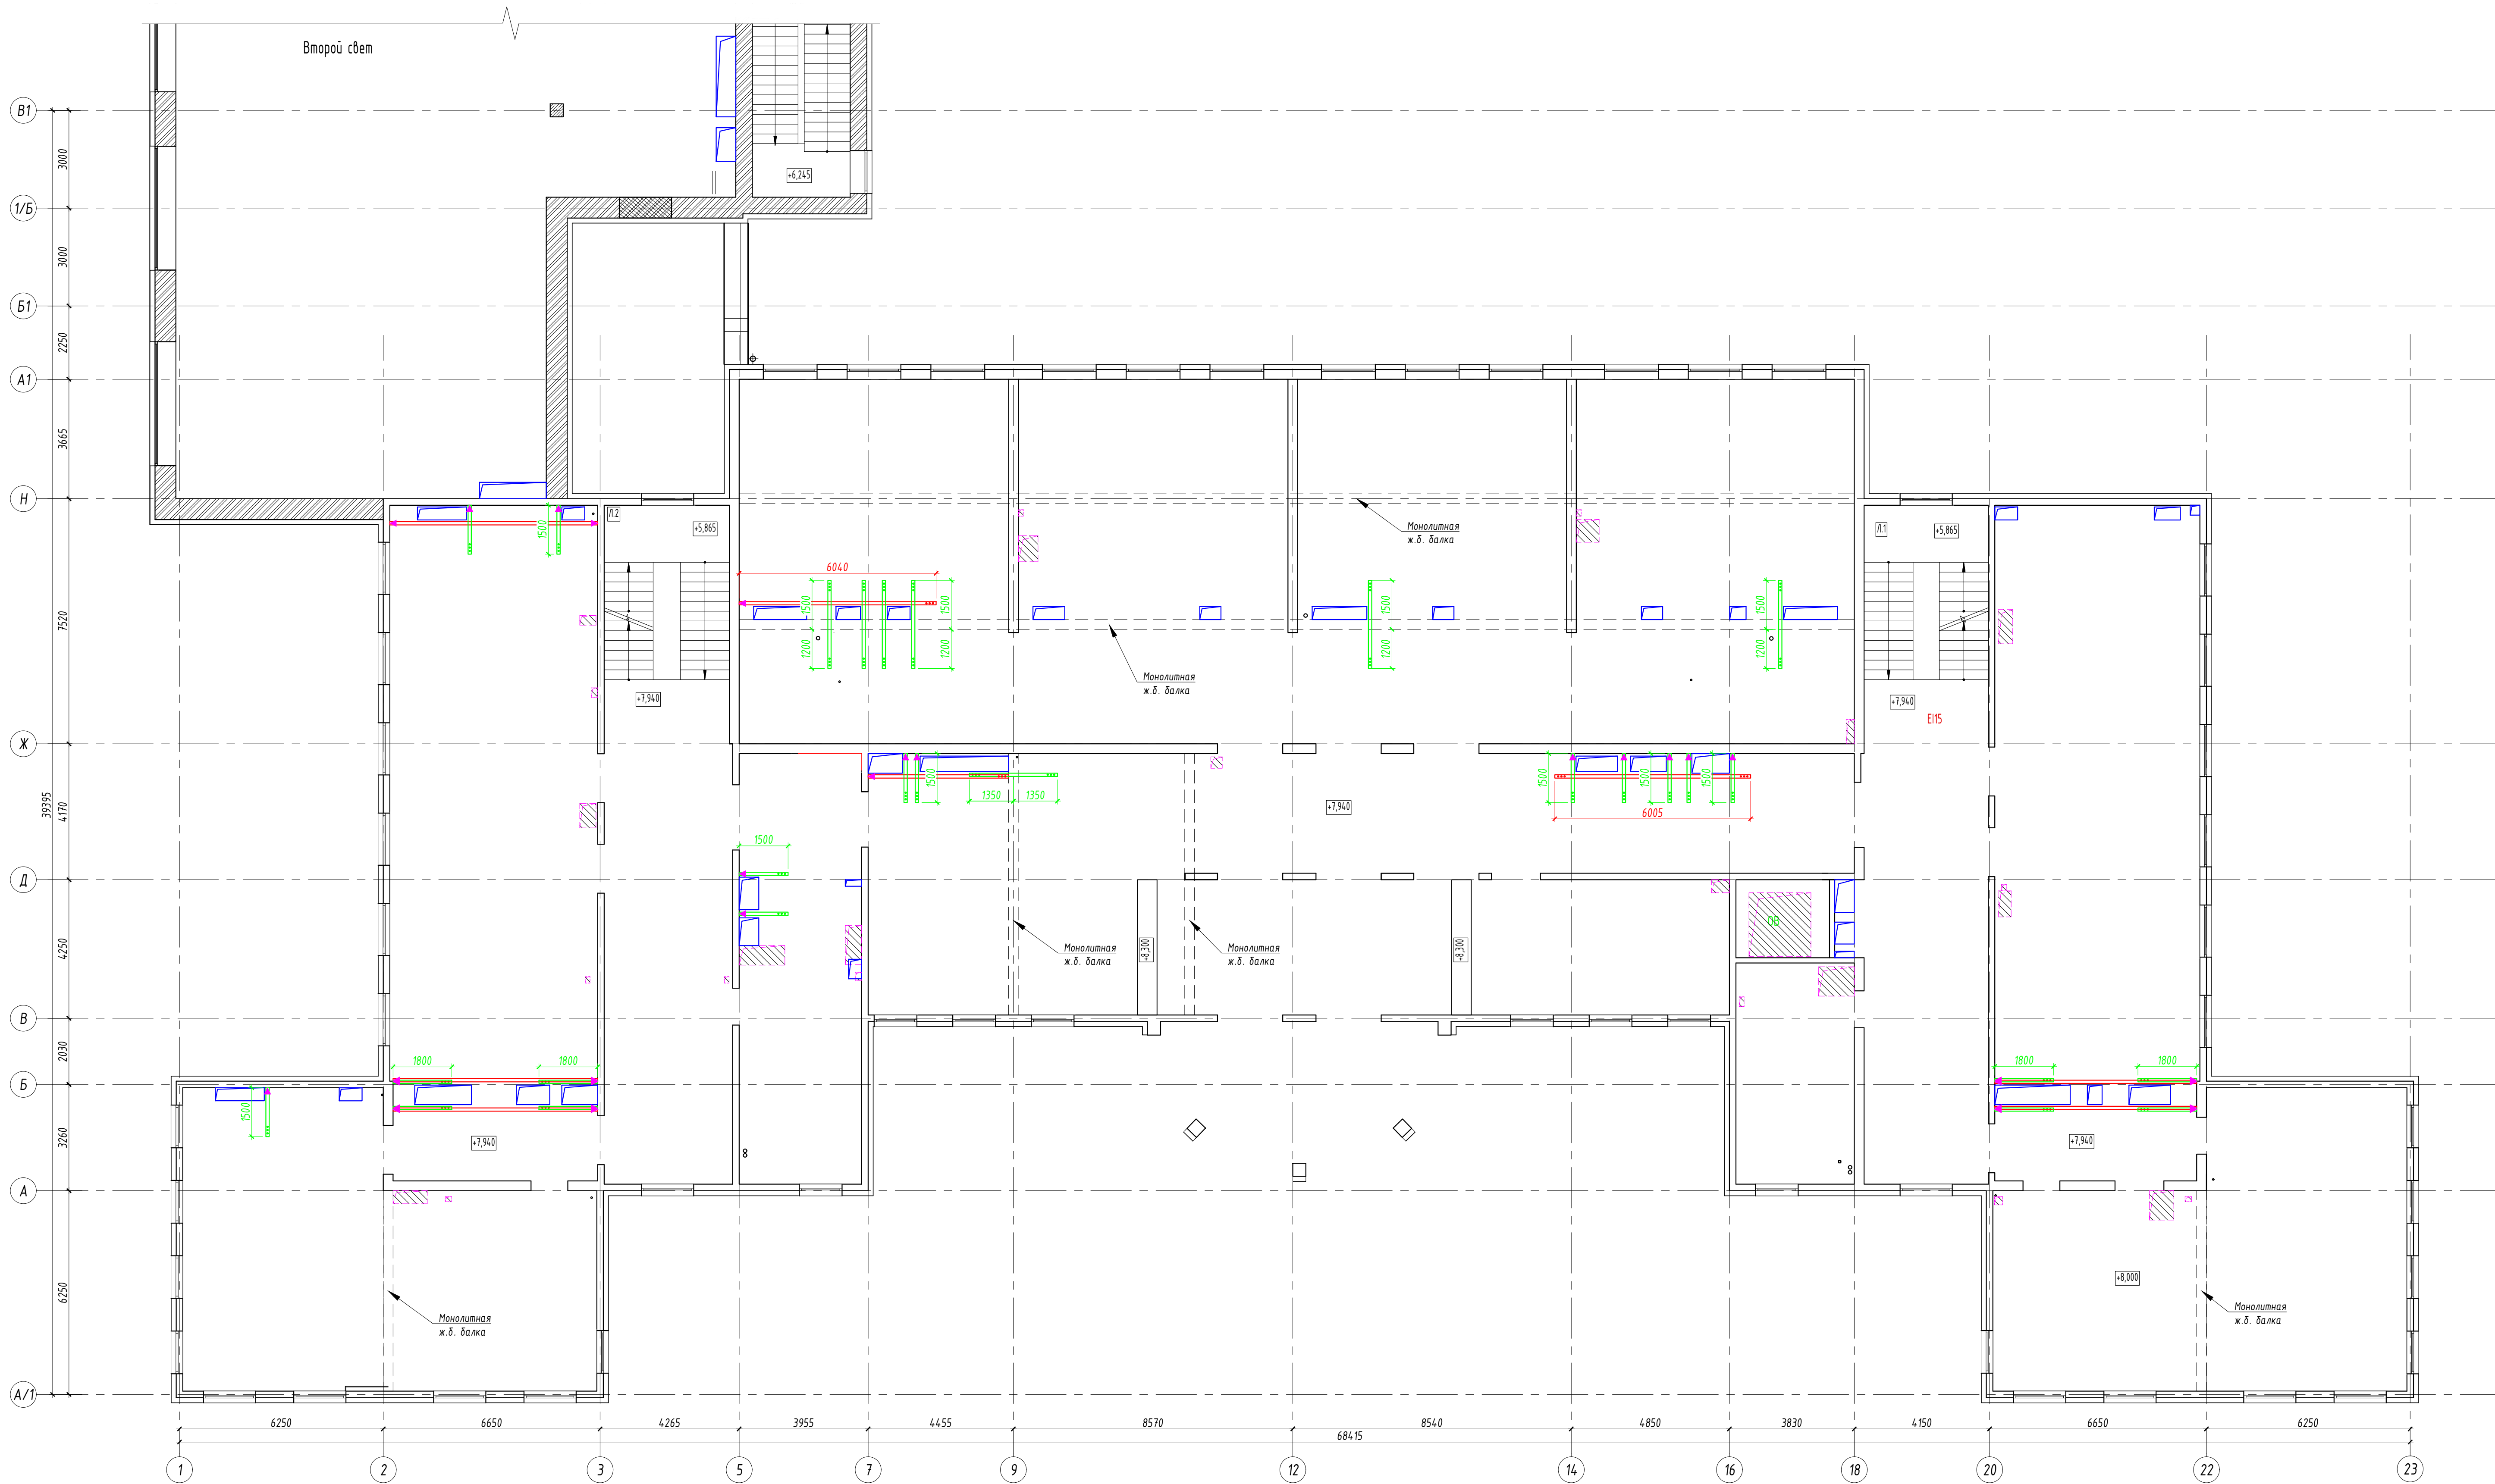


Условные обозначения

- ▲ - крепление полосы усиления согласно узлу 1
- — — — — полоса 10х100 по верхней поверхности плиты перекрытия
- — — — — полоса 10х100 по нижней поверхности плиты перекрытия

Порядок производства работ:

- Разрушить перекрытие, подлежащее усилению.
- В местах расположения элементов усиления произвести очистку перекрытия от мусора, наливной раствора, элементов пирога пола/потолка до основания монолитного железобетона. Для узла №1 так же произвести очистку участка стены.
- До устройства усиления и замоноличивания существующих проемов выполнить прорезание новых проемов в плите перекрытия, в соответствии со схемой на листе 11.
- Произвести нарезку элементов усиления, при необходимости произвести сварочные работы и выполнение отверстий под анкерные болты согласно узлам 1 и 2. При расположении полосы усиления между вертикальными монолитными конструкциями длину принимать на 40мм меньше фактической.
- Усиление полосой -10х100 выполнять с отступом в 50 мм от края проёма в соответствии с разрезом В-В на листе 21.
- Фиксацию выполнять анкерами Fischer FH II-SK 15х100/15 или аналог.
- Открытые участки стальных элементов обрабатывать огнезащитным составом, обеспечивающим предел огнестойкости не менее R120.
- Спецификации элементов усиления см. лист 13.

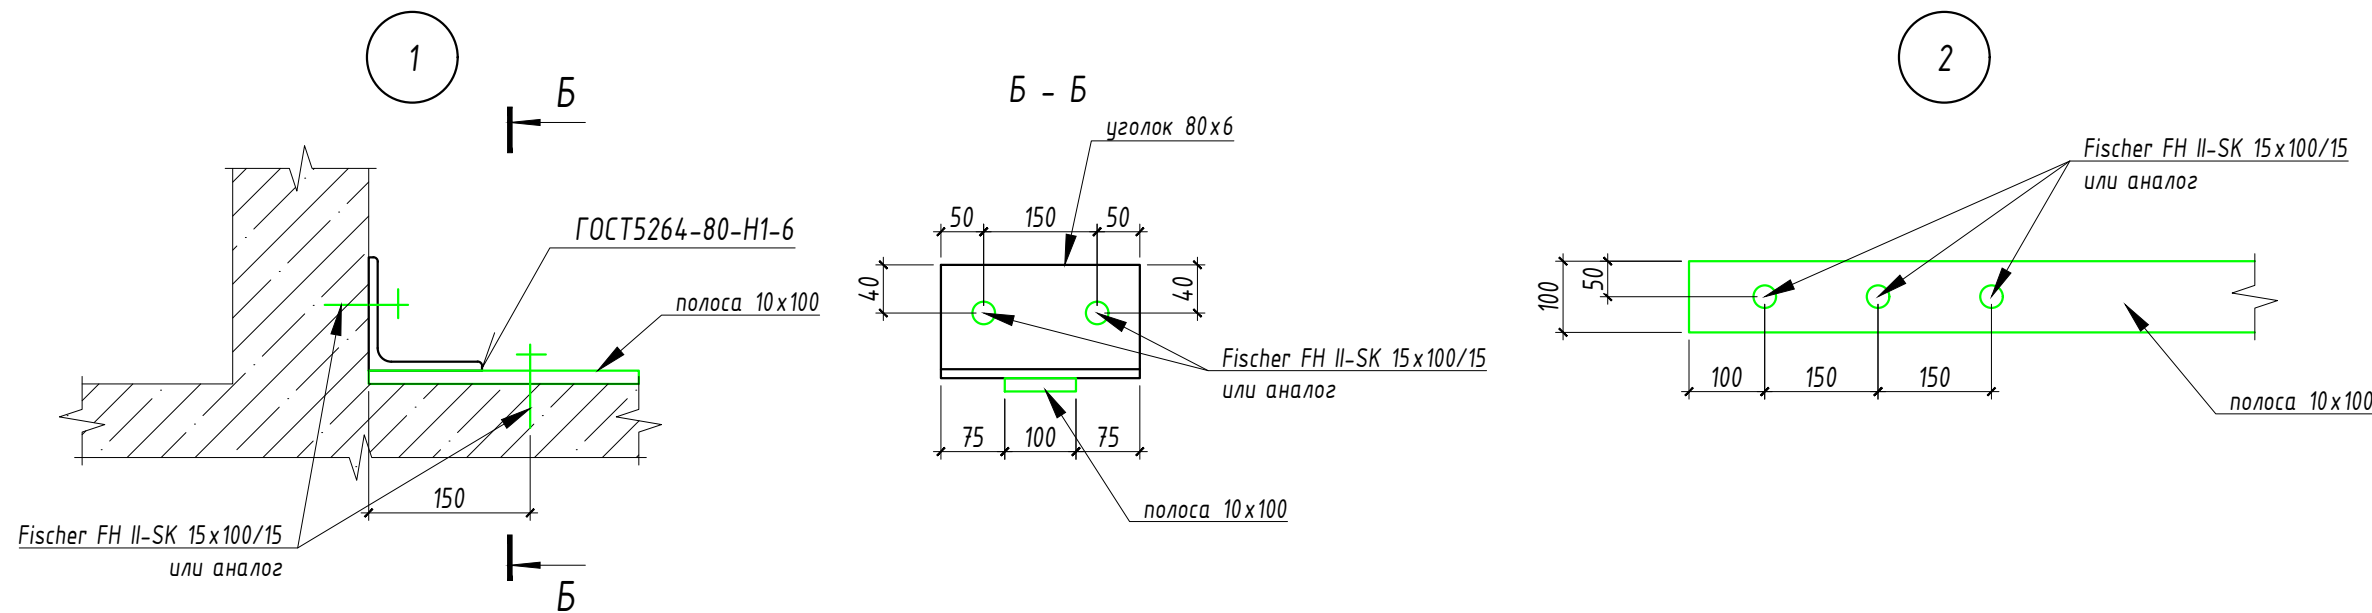


						16-25/Г-Р-КР5		
						Капитальный ремонт объекта "ГБОУ Школа №429 "Сокольная гора", расположенного по адресу: г. Москва, ул. Соколиной горы 5-я, д. 14.		
Изм.	Кол. изм.	Лист	№ док.	Подпись	Дата	Конструктивные решения	Стадия	Лист
Разраб.	Варнашов	01.09.2026					Р	12
Проверил	Прудников	01.09.2026						
План перекрытия над 2 этажом в осях 1-23/А/1-В1. Элементы усиления						АЗУРИТ		
Н. контр.	Гударева	01.09.2026				ФОРМАТ А1		
ГИП	Маркова	01.09.2026						

Спецификация элементов усиления к плану перекрытия над 2 этажом

Поз.	Обозначение	Наименование	Кол.	Масса ед., кг	Примечание
	ГОСТ 34028-2016	Ø10 А500С L=м.п.	205,7	0,616	126,7
	ГОСТ 103-2006	-10х100 L=м.п.	102,3	7,85	803,1
	ГОСТ 8509-93	Уголок 80х80х6 L=м.п.	8	7,36	58,9
	Анкерный болт втулочный	Fischer FH II-SK 15х100/15 (или аналог)			210 шт.
		Материалы			
	ГОСТ 25029-2020	Грунтовка ГФ-021 (за 1 раз)			12,74 м ²
	ГОСТ 6465-2023	Эмаль ПФ-115 (за 2 раза)			25,48 м ²
	ГОСТ 26633-2015	Бетон В25			2,07 м ³
	ГОСТ 28013-98	Цементно-песчаный раствор М100			7,8 м ³

Взам. инв N											
Подп. и дата								16-25/Г -Р - КР5			
								Капитальный ремонт объекта "ГБОУ Школа №429 "Соколиная гора", расположенного по адресу: г. Москва, ул. Соколиной горы 5-я, д. 14.			
Инв. N подл.		Изм	Кол.уч	Лист	№ док	Подпись	Дата	Конструктивные решения	Стадия	Лист	Листов
		Разраб.		Варнашов			01.09.2026		Р	13	
		Проверил		Прудников			01.09.2026				
								Спецификация элементов усиления к плану перекрытия над 2 этажом	 АЗУРИТ		
		Н. контр.		Гударева			01.09.2026				
		ГИП		Маркова			01.09.2026				

План перекрытия над 2 этажом в осях 1.1-17.1/Н-П.1

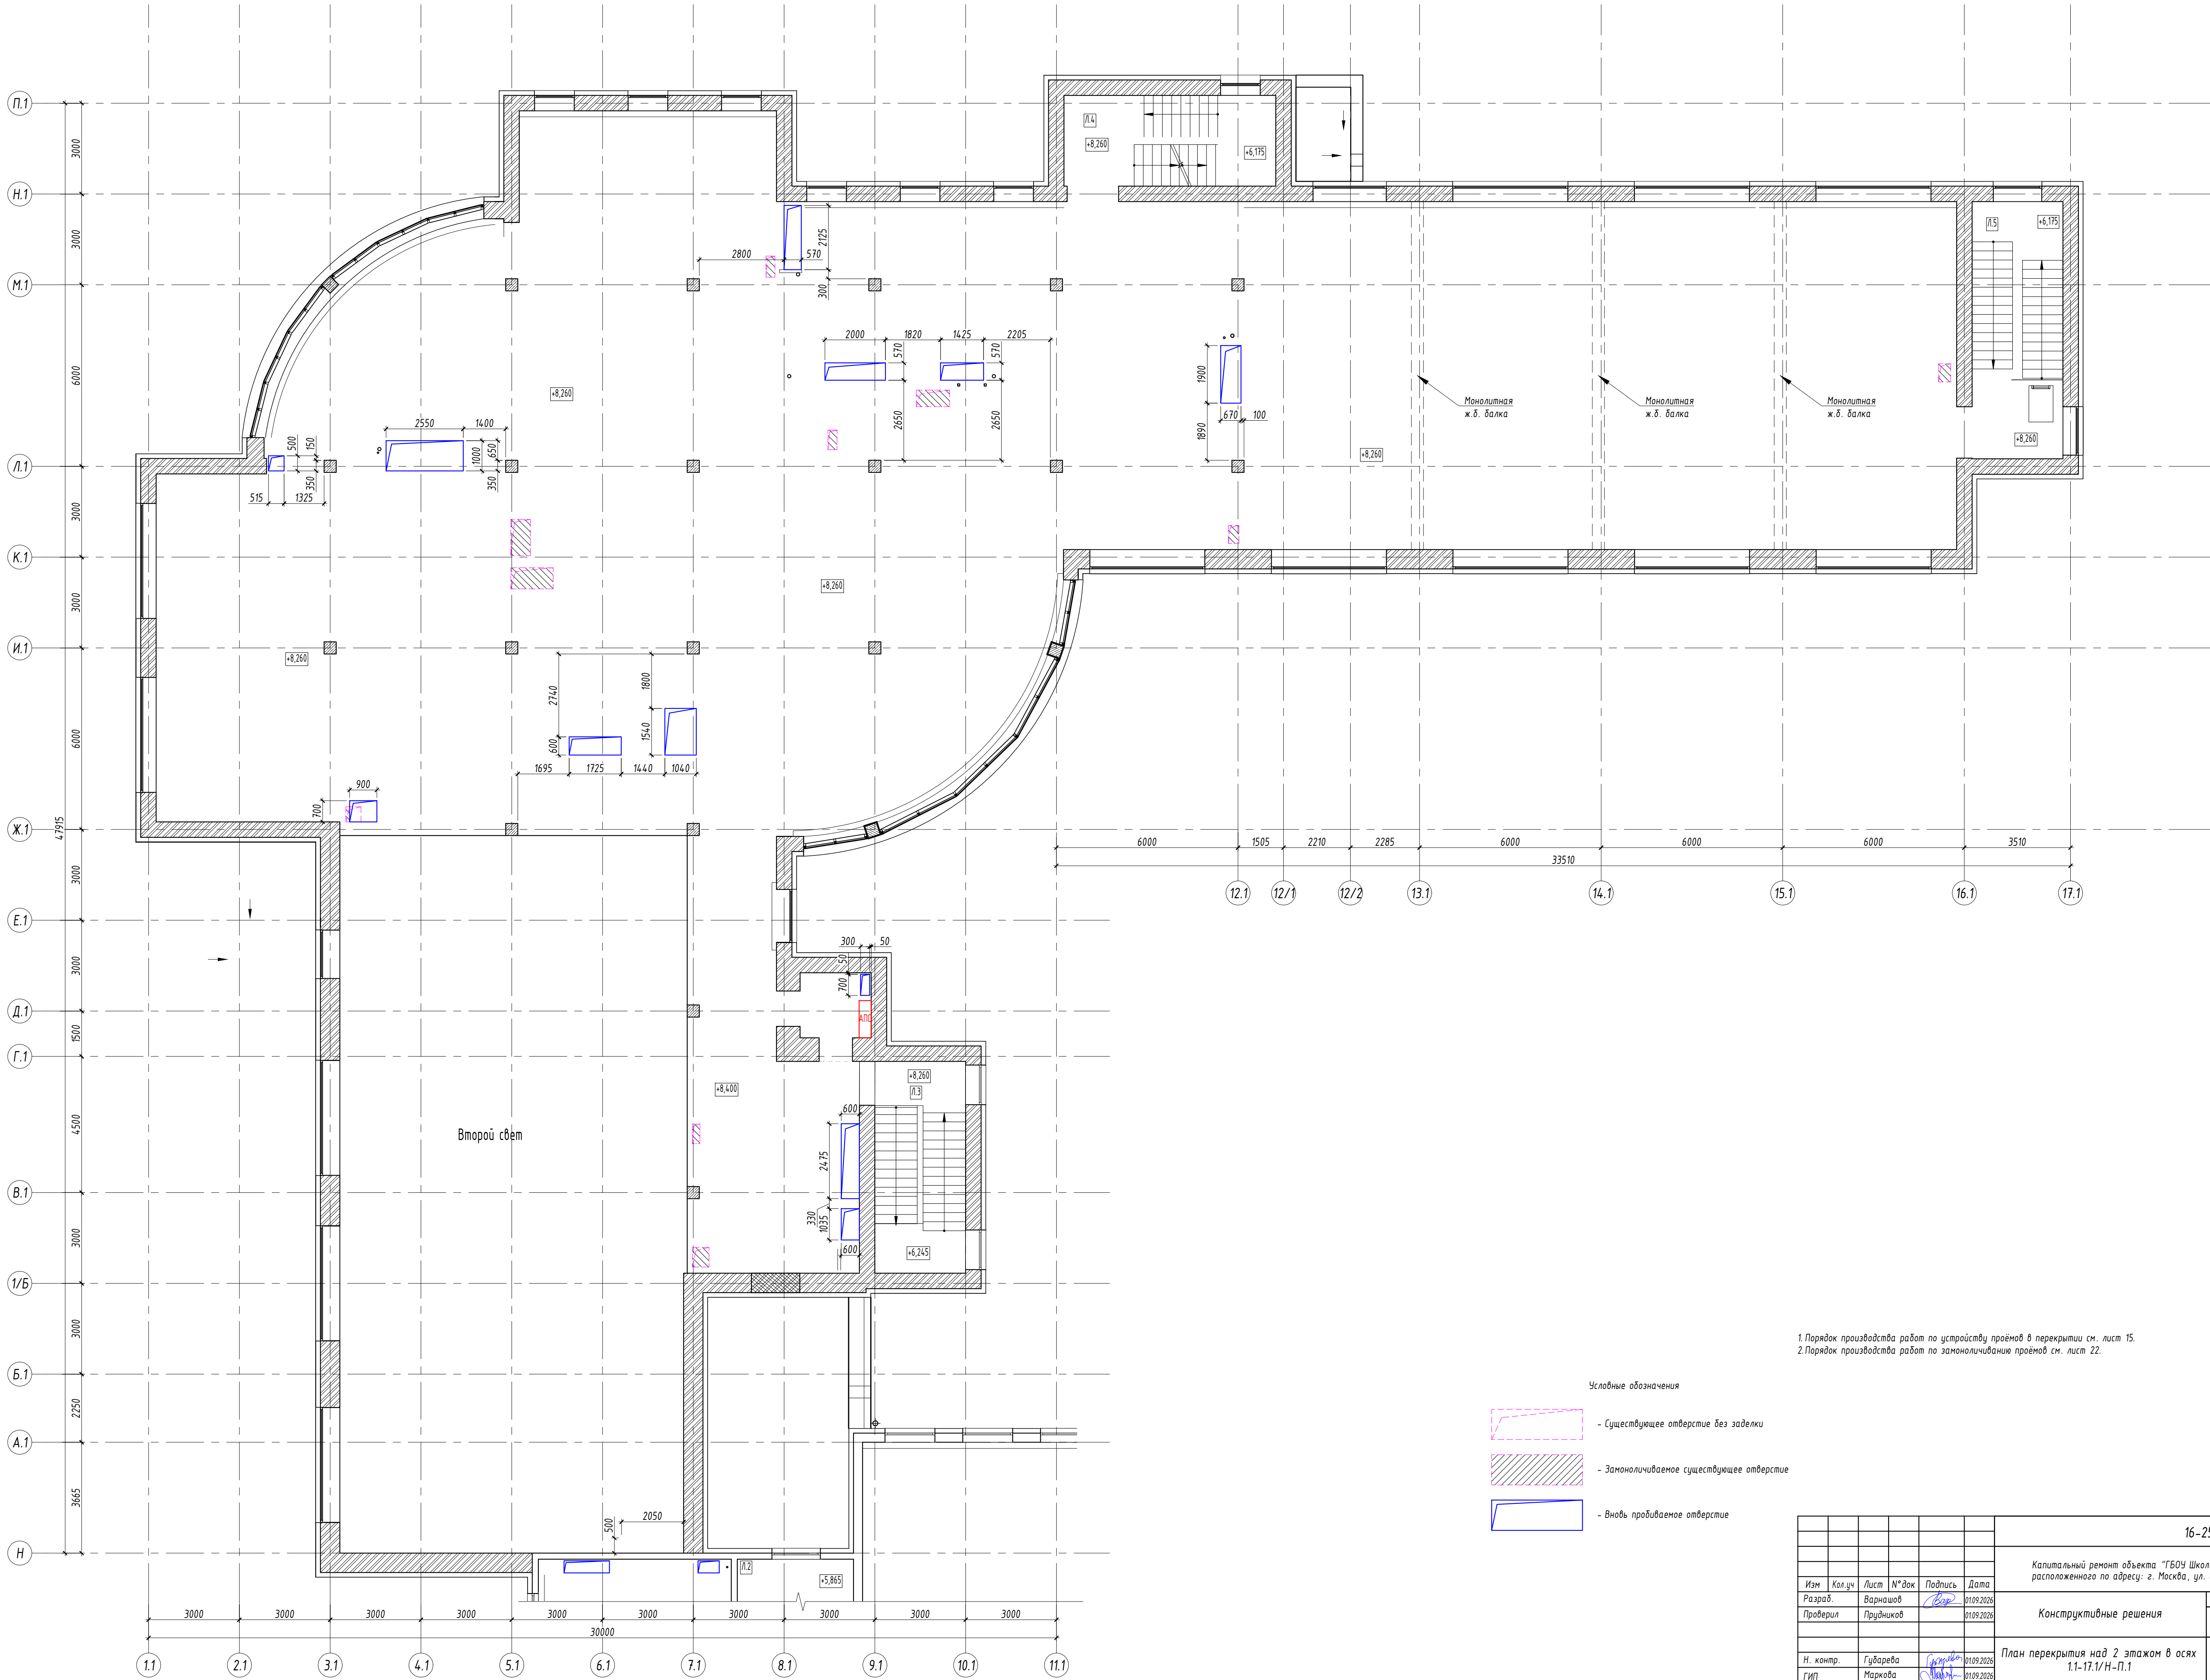


1.Порядок производства работ по устройству проёмов в перекрытии см. лист 15.
2.Порядок производства работ по замоноличиванию проёмов см. лист 22.

Условные обозначения

- Существующее отверстие без заделки
- Замоноличиваемое существующее отверстие
- вновь пробиваемое отверстие

						16-25/Г-Р-КР5		
						Капитальный ремонт объекта "ГБОУ Школа №429 "Соколиная гора", расположенного по адресу: г. Москва, ул. Соколиной горы 5-я, д. 14.		
Изм.	Кол.уч.	Лист	№ док	Подпись	Дата	Конструктивные решения	Стадия	Лист
Разраб.	Вариантов	01.09.2026		Вар	01.09.2026		Р	14
Проверил	Прудников	01.09.2026						
						План перекрытия над 2 этажом в осях 1.1-17.1/Н-П.1		
Н. контр.	Гударева	01.09.2026		Гударева	01.09.2026	АЗУРИТ		
ГИП	Маркова	01.09.2026		Маркова	01.09.2026			

Условные обозначения

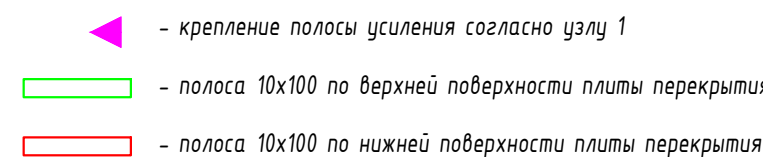


1. Разрушить перекрытие, подлежащее усилению.
2. В местах расположения элементов усиления произвести очистку перекрытия от мусора, наливов раствора, элементов порога пола/потола до основания монолитного железобетона. Для узла №1 так же произвести очистку участка стены.
3. До устройства покрытия и замоноличивания существующих проёмов выполнить прорезание новых проёмов в листе покрытия, в соответствии со схемой на листе 14.
4. Произвести нарезку элементов усиления, при необходимости произвести сварочные работы и выполнение отверстий под анкеры болты согласно узлам 1 и 2. При расположении болтов усиления между вертикальными монолитными конструкциями, расстояние между болтами должно быть не менее 40мм.
5. Усиление половой – 10х100 мм, с шагом 85 мм от края проёма в соответствии с разрезом В-В на листе 21.
6. Фиксацию выполнять анкеры Fischer F12-SK 15х100/15 мм аналог.
7. Открытые участки стальных элементов обрабатывать огнезащитным составом, обеспечивающим предел огнестойкости не менее R120.
8. Спецификация элементов усиления с лист 16.

						16-25/Г-Р - КР5			
						Капитальный ремонт объекта "ГБОУ Школа №429 "Соколовая гора", расположенного по адресу: г. Москва, ул. Соколовой горы 5-я, д. 14.			
Изм.	Кол. экз.	Лист	№ док.	Подпись	Дата	Конструктивные решения	Стандия	Лист	Листов
Разработ.	Варнашов				01.09.2025		Р	15	
Проверил	Прядняков				01.09.2025				
План перекрытия над 2 этажом в осях 1.1-17/Н-П.1. Элементы усиления							 AZURIT		
Н. контр.	Губарева				01.09.2025				
ГИП	Маркова				01.09.2025				

Спецификация элементов усиления к плану перекрытия над 2 этажом

Поз.	Обозначение	Наименование	Кол.	Масса ед., кг	Примечание
	ГОСТ 34028-2016	Ø10 А500С L=м.п.	205,7	0,616	126,7
	ГОСТ 103-2006	-10x100 L=м.п.	81,7	7,85	641,3
	ГОСТ 8509-93	Уголок 80x80x6 L=м.п.	1	7,36	7,4
	Анкерный болт втулочный	Fischer FH II-SK 15x100/15 (или аналог)			156 шт.
		Материалы			
	ГОСТ 25029-2020	Грунтовка ГФ-021 (за 1 раз)			8,48 м ²
	ГОСТ 6465-2023	Эмаль ПФ-115 (за 2 раза)			17 м ²
	ГОСТ 26633-2015	Бетон В25			1,4 м ³
	ГОСТ 28013-98	Цементно-песчаный раствор М100			7,8 м ³


Взам. инв. N													
Подп. и дата								16-25/Г -Р - КР5					
		Изм	Кол.уч	Лист	№ док	Подпись	Дата						
		Разраб.		Варнашов			01.09.2026	Конструктивные решения			Стадия	Лист	Листов
Проверил		Прудников			01.09.2026	Р	16						
Инв. N подл.							Спецификация элементов усиления к плану перекрытия над 2 этажом			 АЗУРИТ			
		Н. контр.		Гударева									01.09.2026
		ГИП		Маркова			01.09.2026						

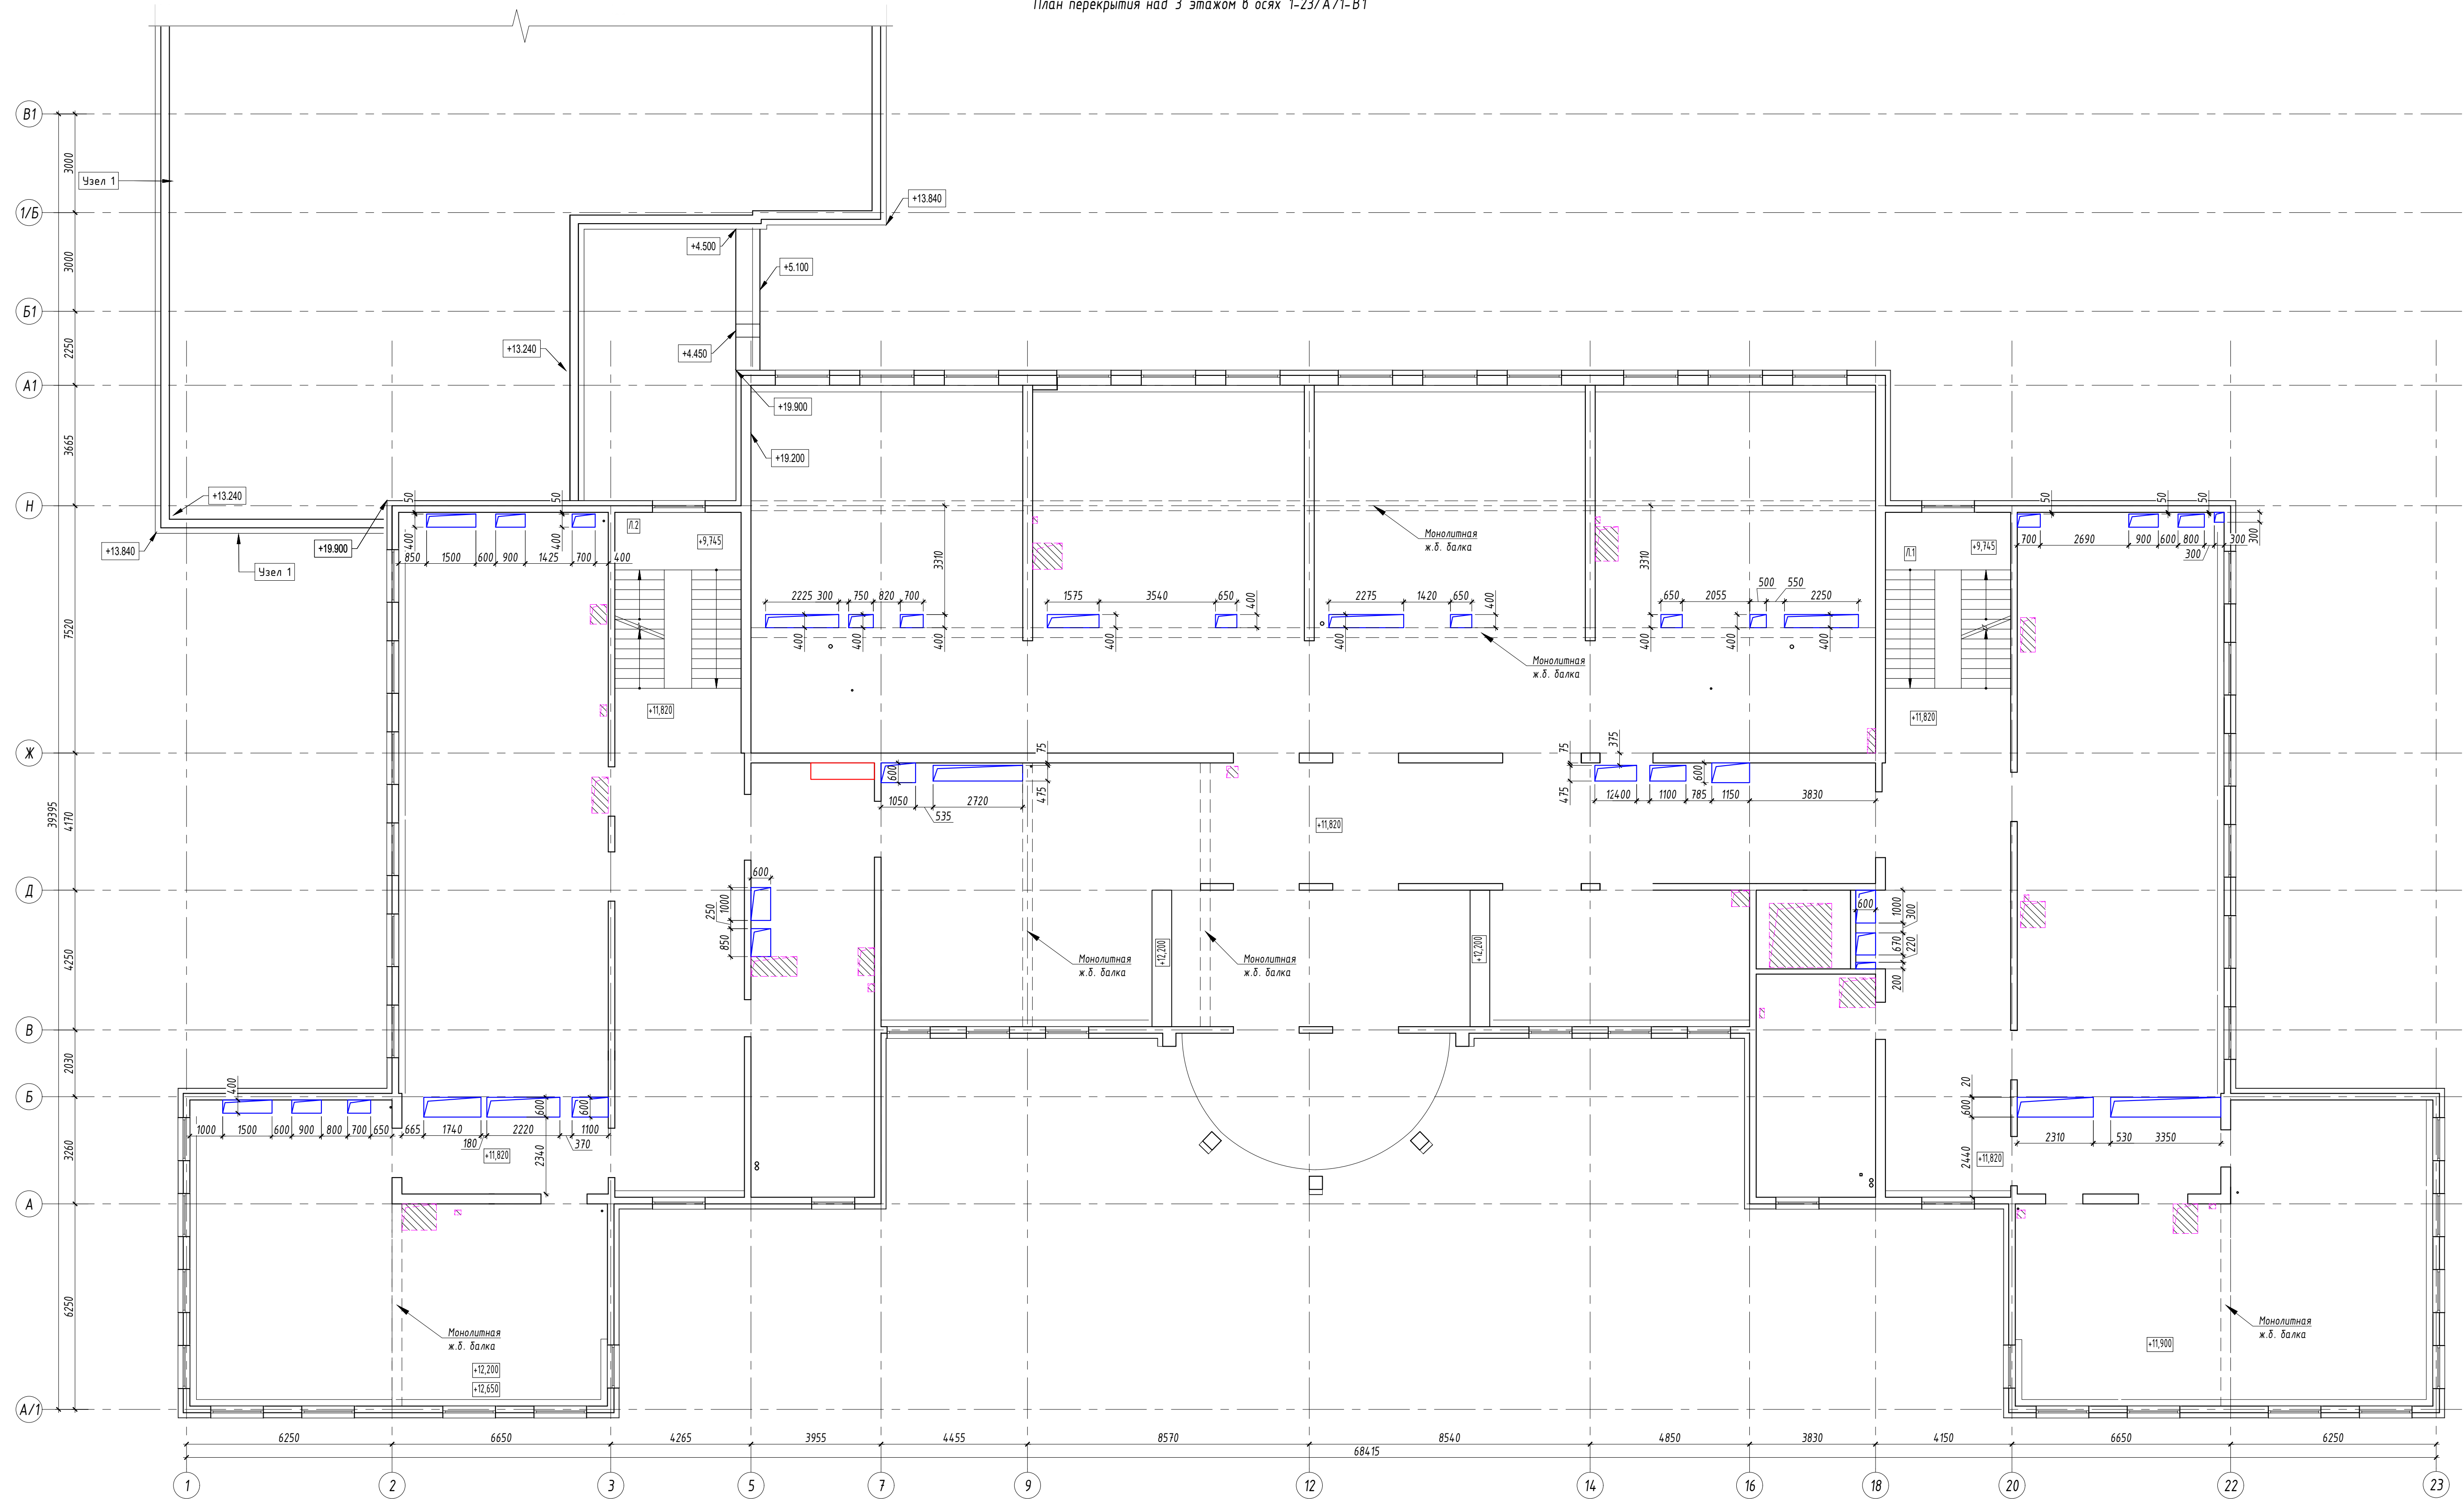


Условные обозначения



- Существующее отверстие без заделки

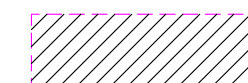


- Замоноличиваемое существующее отве

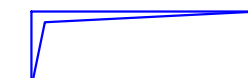

- Вновь пробиваемое отверстие

1. Порядок производства работ по устройству проёмов в перекрытии см. лист 18.
2. Порядок производства работ по замоноличиванию проёмов см. лист 22.

[illegible]

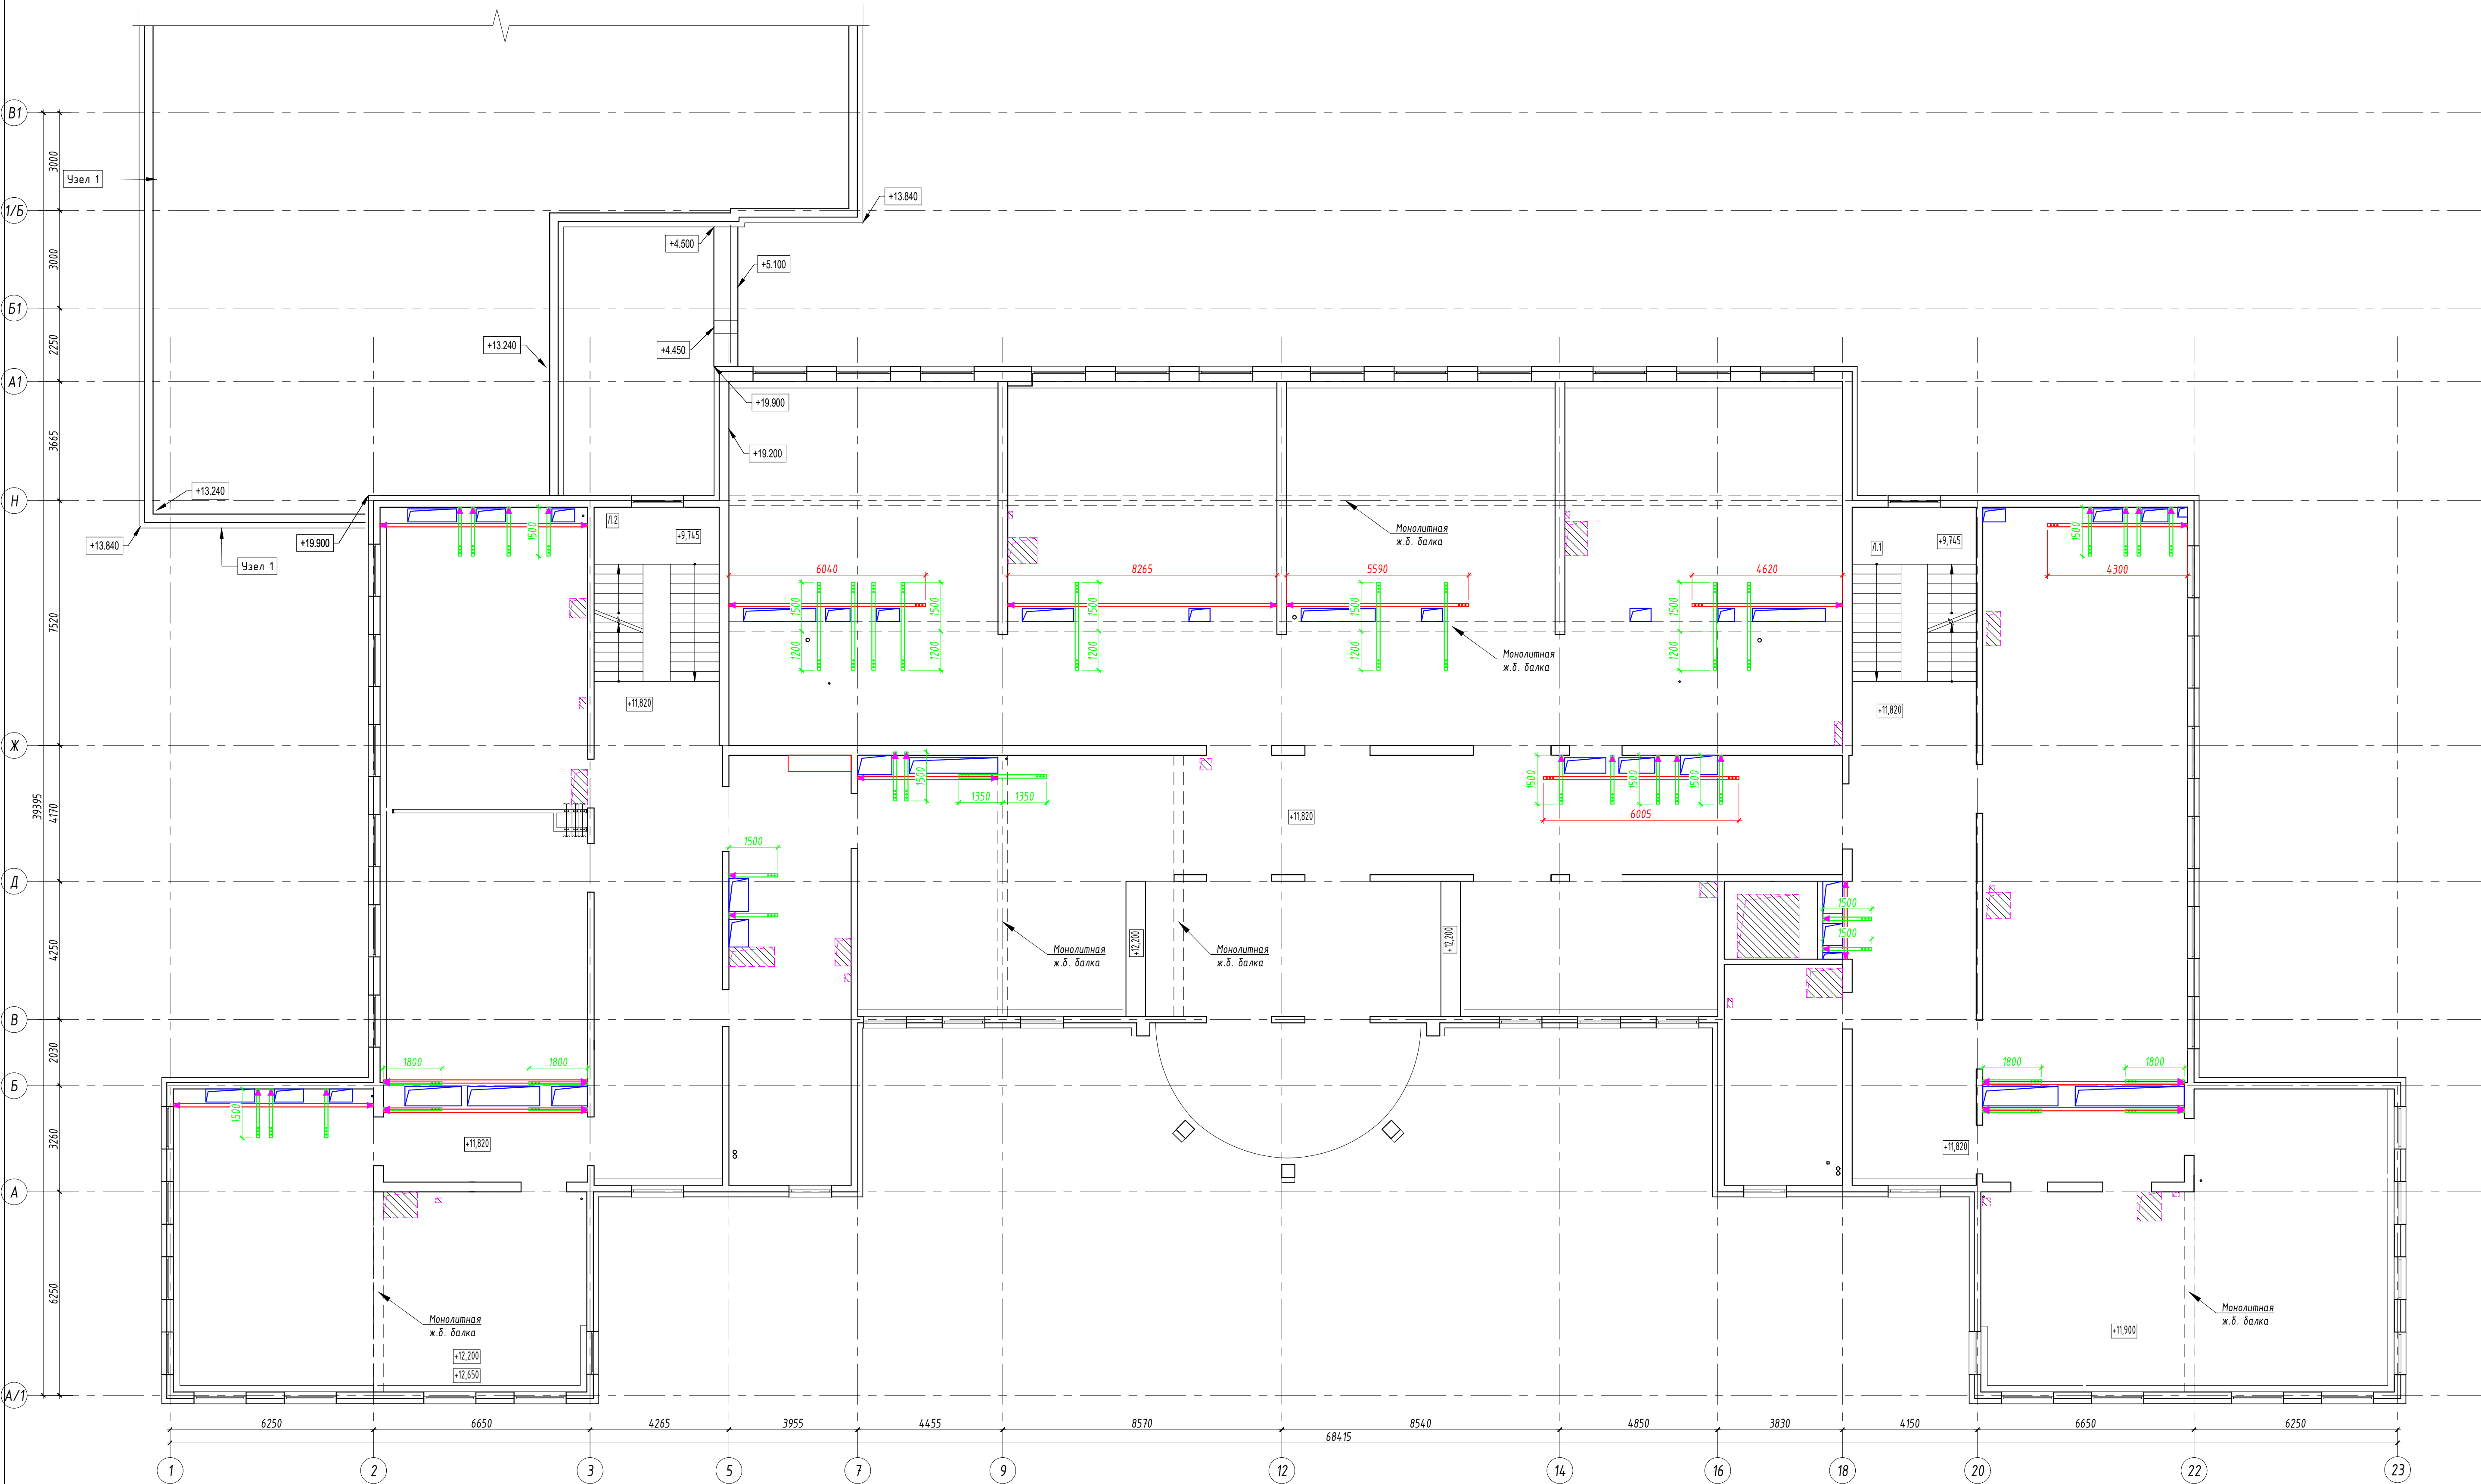



- Порядок производства работ:
1. Разгрузить перекрытие, подлежащее усилению.
 2. В местах расположения элементов усиления произвести очистку перекрытия от мусора, наливов раствора, элементов пирога пола/потолка до основания монолитного железобетона. Для узла №1 так же произвести очистку участка стены.
 3. До устройства усиления и замоналичивания существующих проёмов выполнить прорезание новых проёмов в плите покрытия, в соответствии со схемой на листе 17.
 4. Произвести нарезку элементов усиления, при необходимости произвести сварочные работы и выполнение отверстий под анкеры болты согласно узлам 1 и 2. При расположении полосы усиления между вертикальными монолитными конструкциями длину пронашивать на 40мм меньше фактической.
 7. Усиление полосой -10х100 выполнять с отступом в 50 мм от края проёма в соответствии с разрезом В-В на листе 21.
 8. Фиксация выполняемых анкеров Fischer FH II-SK 15х100/15 или аналог.
 9. Открытые участки стальных элементов обработать огнезащитным составом, обеспечивающим предел огнестойкости не менее R120.
 10. Спецификация элементов усиления см. лист 19.

					16-25/Г-Р-КР5		
					Капитальный ремонт объекта "ГБОУ Школа №429 "Соколиная гора", расположенного по адресу: г. Москва, ул. Соколиной горы 5-я, д. 14.		
Изм.	Кол.уч.	Лист	№ док	Подпись	Конструктивные решения	Стадия	Лист
Разраб.	Варнашов	01.09.2026		Вар		Р	18
Проверил	Прудников	01.09.2026					
					План перекрытия над 3 этажом в осях 1-23/А/1-В1. Элементы усиления		
Н. контр.	Гударева	01.09.2026		Гударева			
ГИП	Маркова	01.09.2026		Маркова			

Условные обозначения

- ▲ - крепление полосы усиления согласно узлу 1
- - полоса 10х100 по верхней поверхности плиты перекрытия
- - полоса 10х100 по нижней поверхности плиты перекрытия


Вариант и дата	Вариант и дата
Изд. № подл.	Изд. № подл.

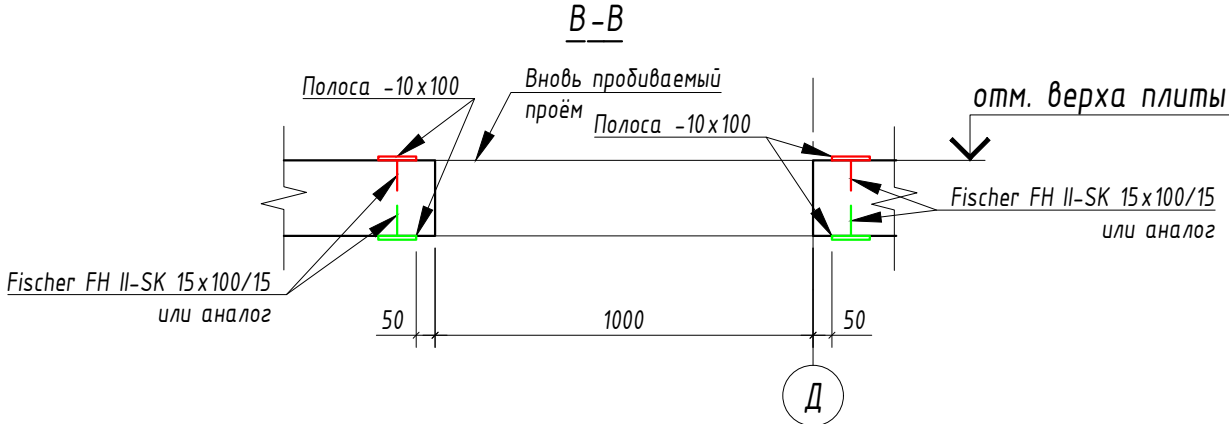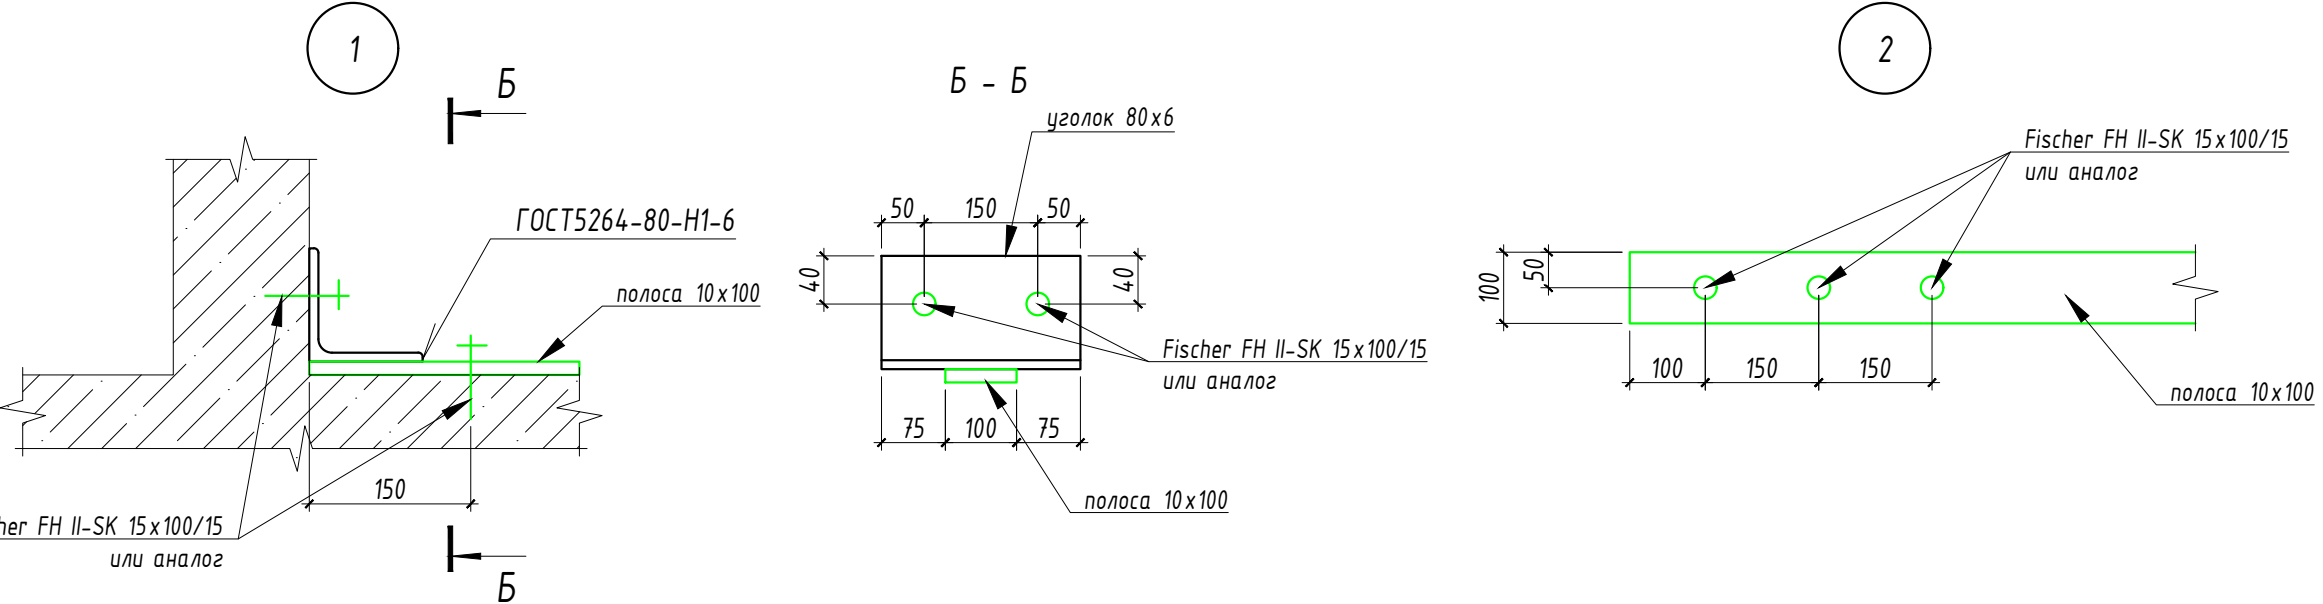



Спецификация элементов усиления к плану перекрытия над 3 этажом

Поз.	Обозначение	Наименование	Кол.	Масса ед., кг	Примечание
	ГОСТ 34028-2016	Ø10 А500С L=м.п.	205,7	0,616	126,7
	ГОСТ 103-2006	-10х100 L=м.п.	158,6	7,85	1245
	ГОСТ 8509-93	Уголок 80х80х6 L=м.п.	13	7,36	95,7
	Анкерный болт втулочный	Fischer FH II-SK 15х100/15 (или аналог)			324 шт.
		Материалы			
	ГОСТ 25029-2020	Грунтовка ГФ-021 (за 1 раз)			19,94 м ²
	ГОСТ 6465-2023	Эмаль ПФ-115 (за 2 раза)			39,88 м ²
	ГОСТ 26633-2015	Бетон В25			2,36 м ³
	ГОСТ 28013-98	Цементно-песчаный раствор М100			7,8 м ³

Взам. инв. N	
--------------	--	--	

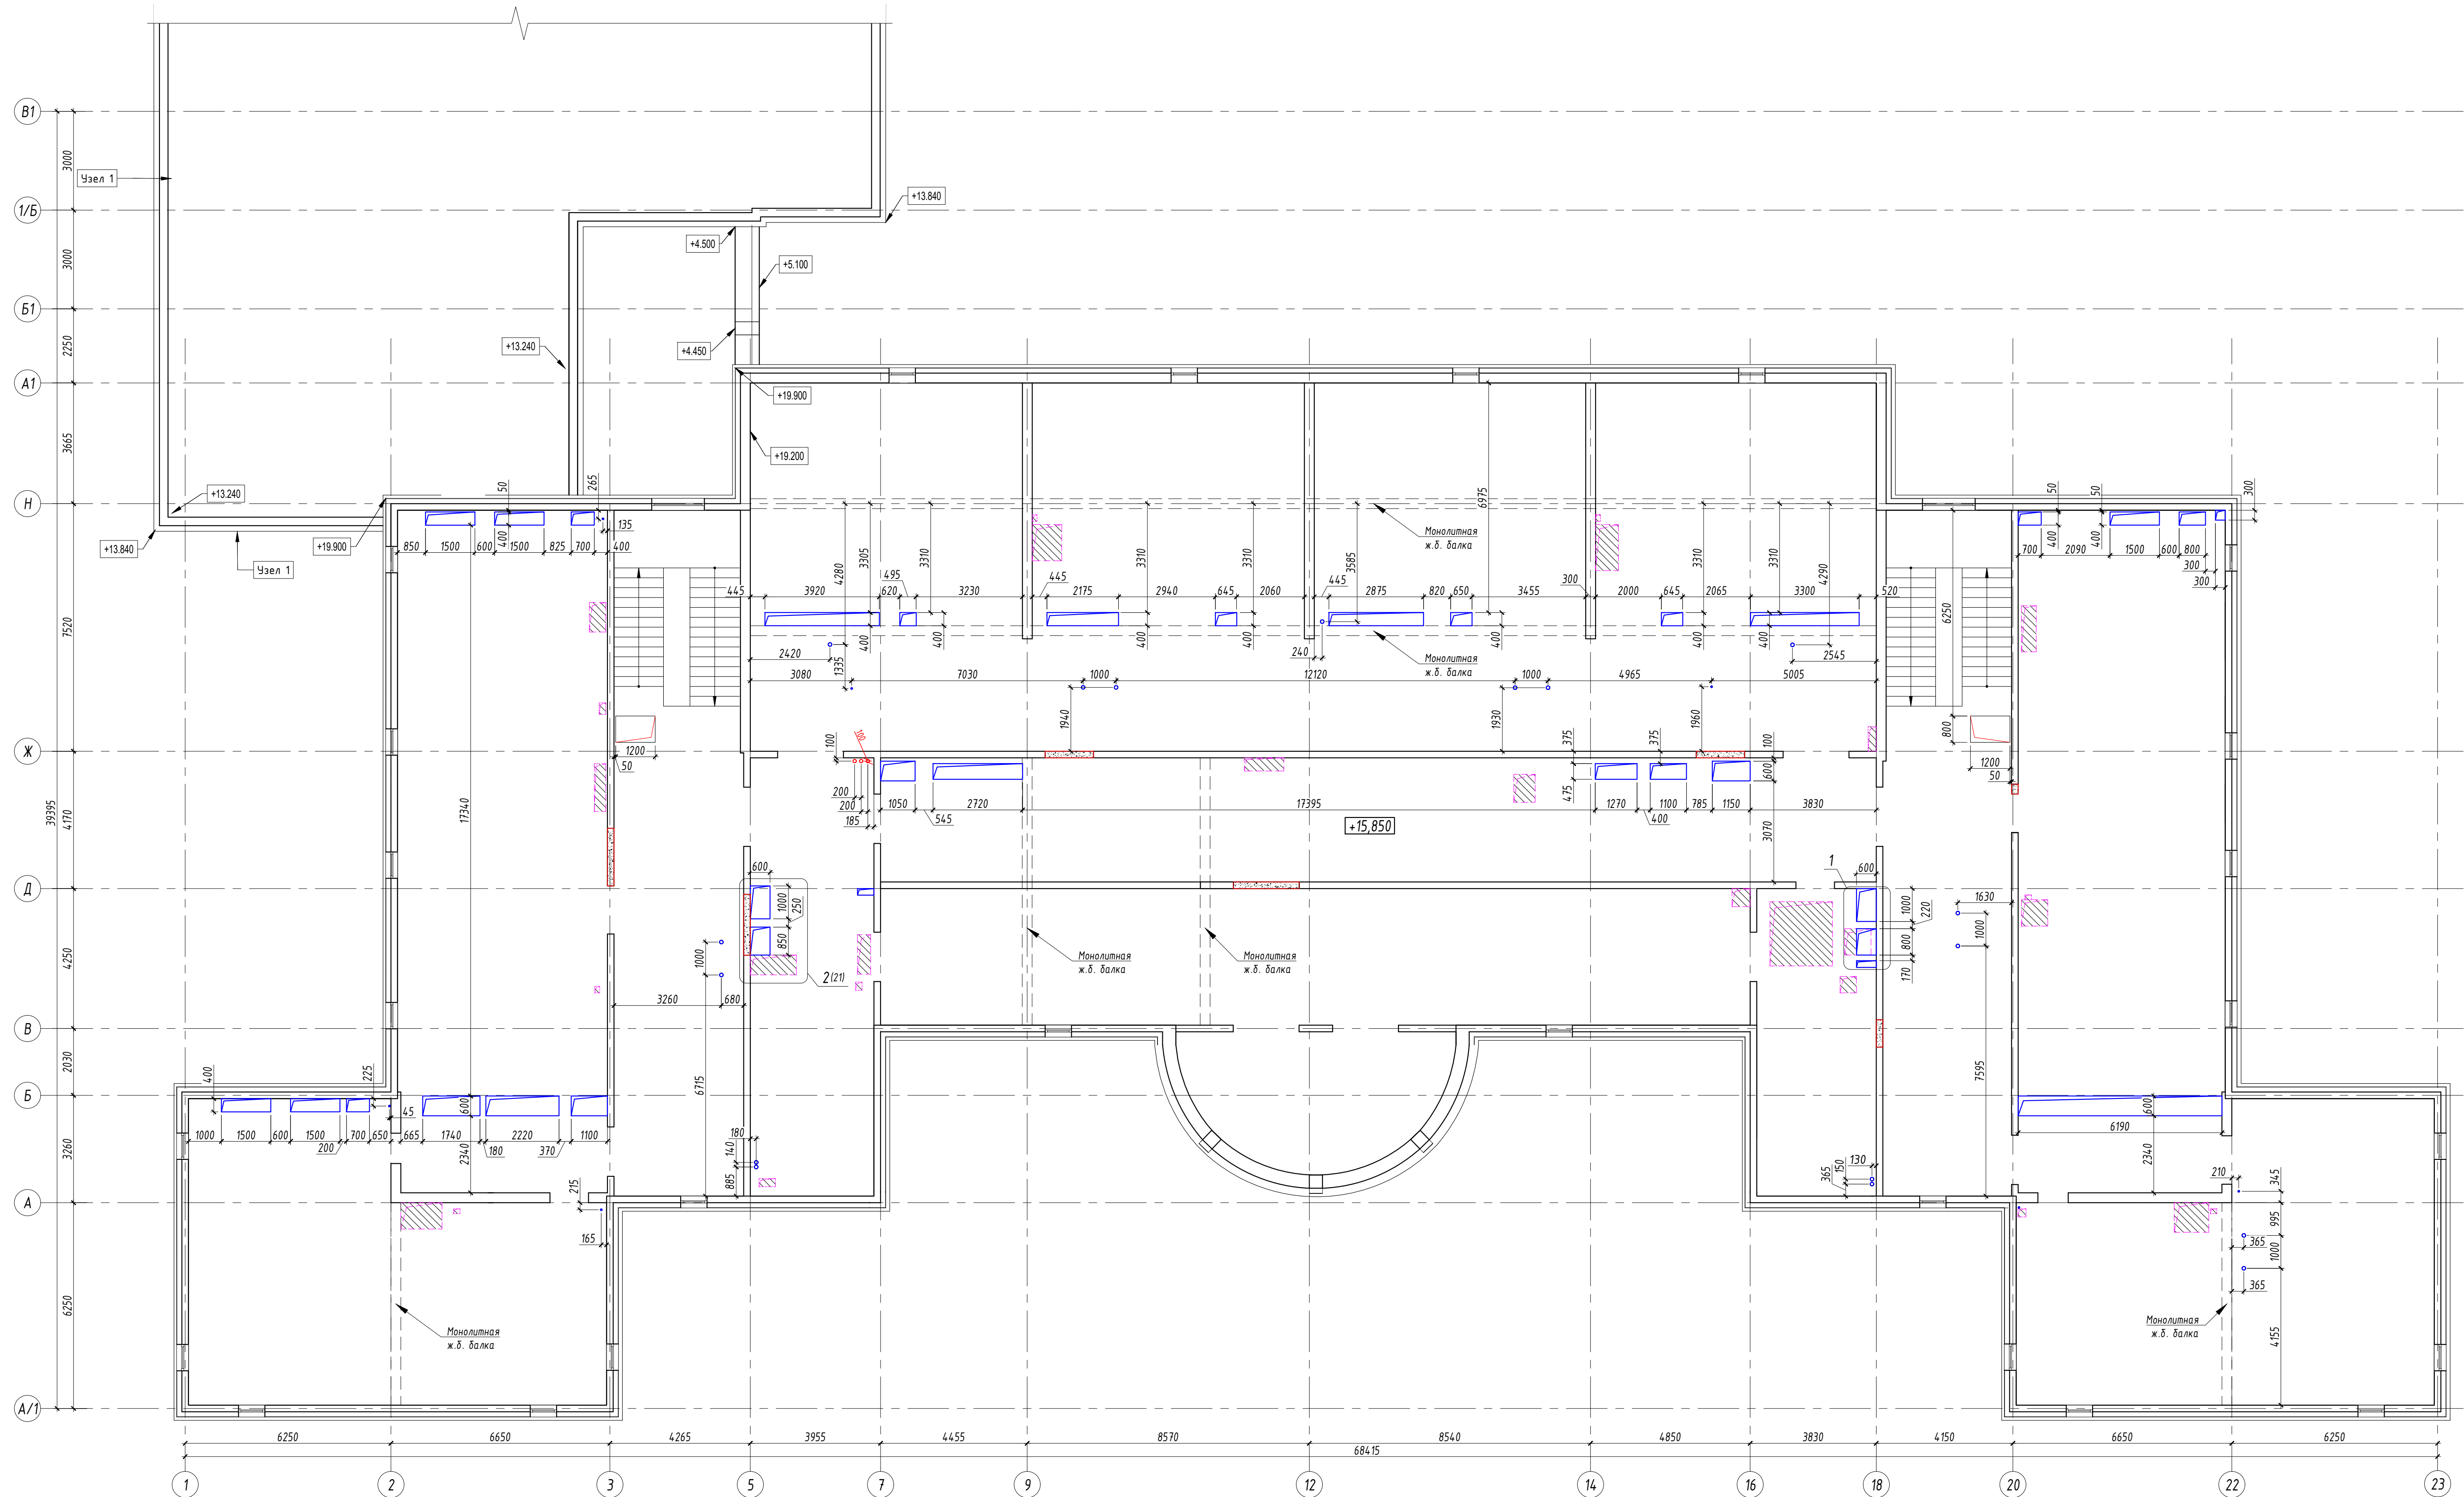


Фрагмент 1 в осях Д/18 на отм. +15,850

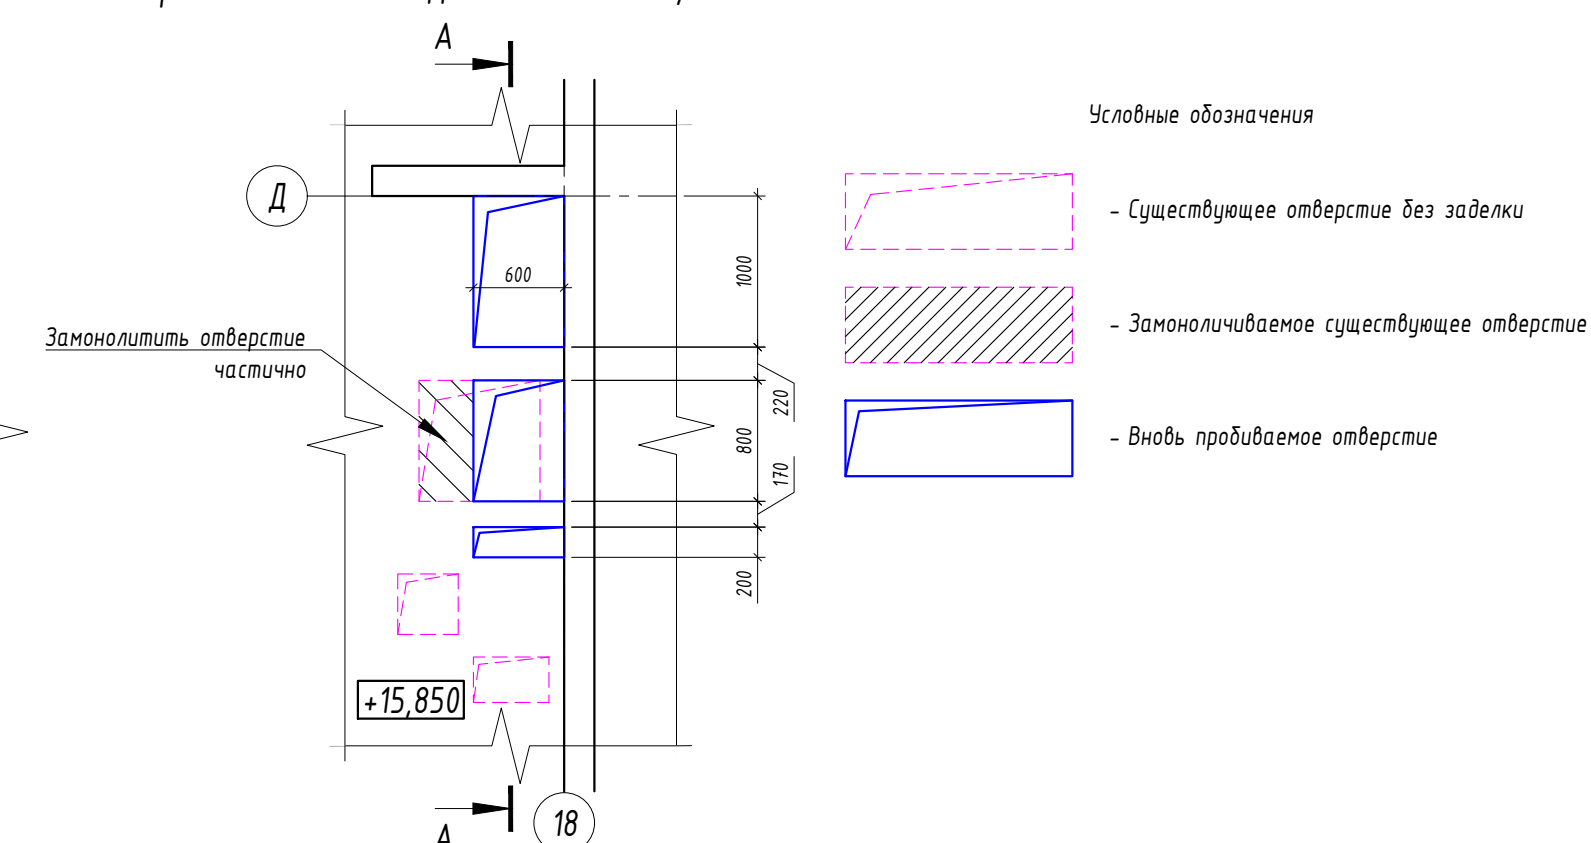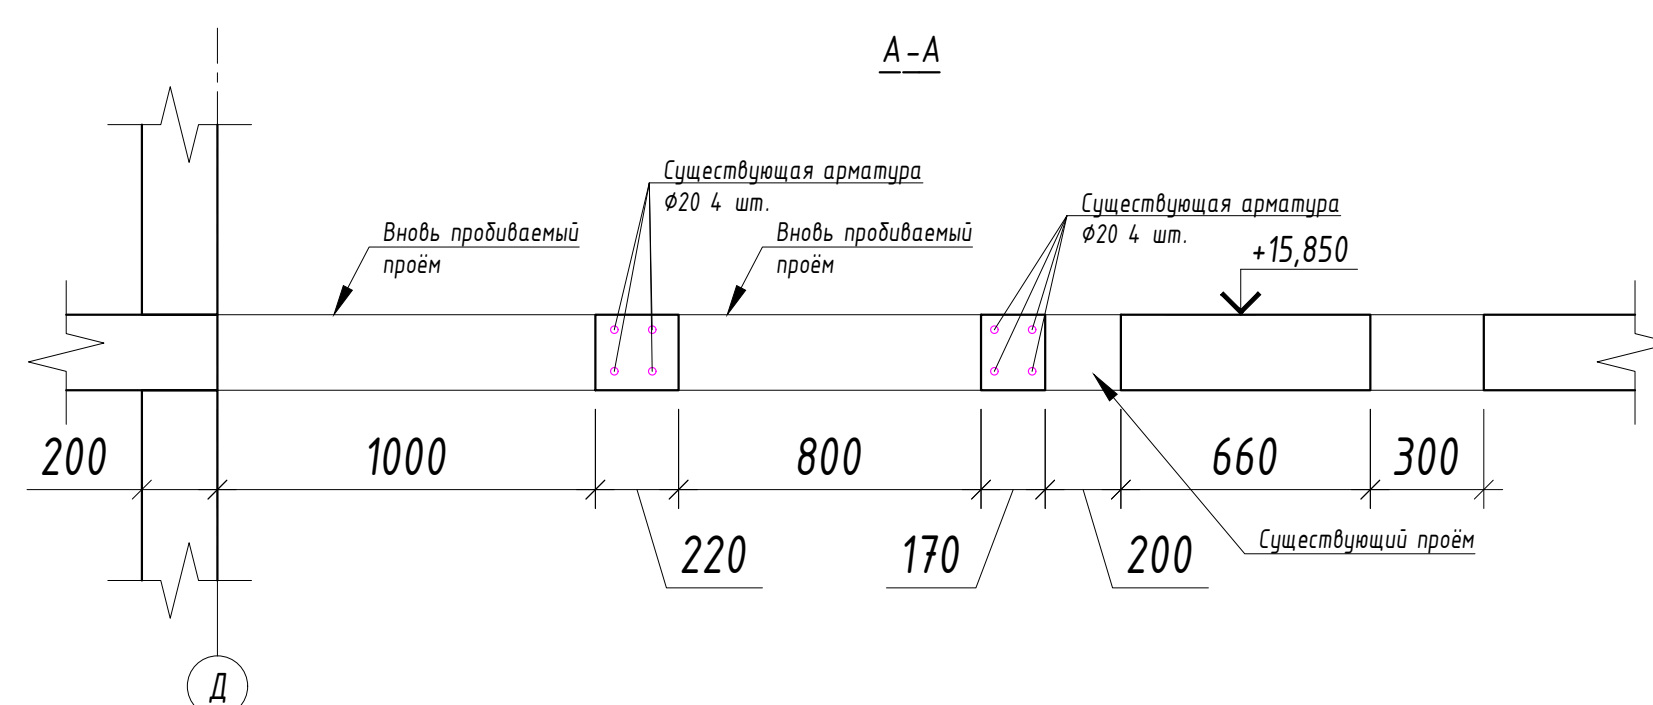


1. Порядок производства работ по устройству проёмов в перекрытии см. лист 21.
2. Порядок производства работ по замоноличиванию проёмов см. лист 22.

						16-25/Г - П - КР5					
						Капитальный ремонт объекта "ГБОУ Школа №829 "Сколияная зора", расположенного по адресу: г Москва, ул. Сколиной зори 5-я, д. 14.					
Изм	Кол.чк	Лист	№ док	Подпись	Дата	Конструктивные решения			Статья	Лист	Листов
Разработ		Варнашов		(Подп.)	0109.2026				Р	20	
Проверил		Прудников			0109.2026						
						План перекрытия над 4 этажом в осях 1-23/А/1-Б/1				АЗУРИТ	
Н. контр.		Губарева		(Подп.)	0109.2026						
ГИП		Маркова		(Подп.)	0109.2026						

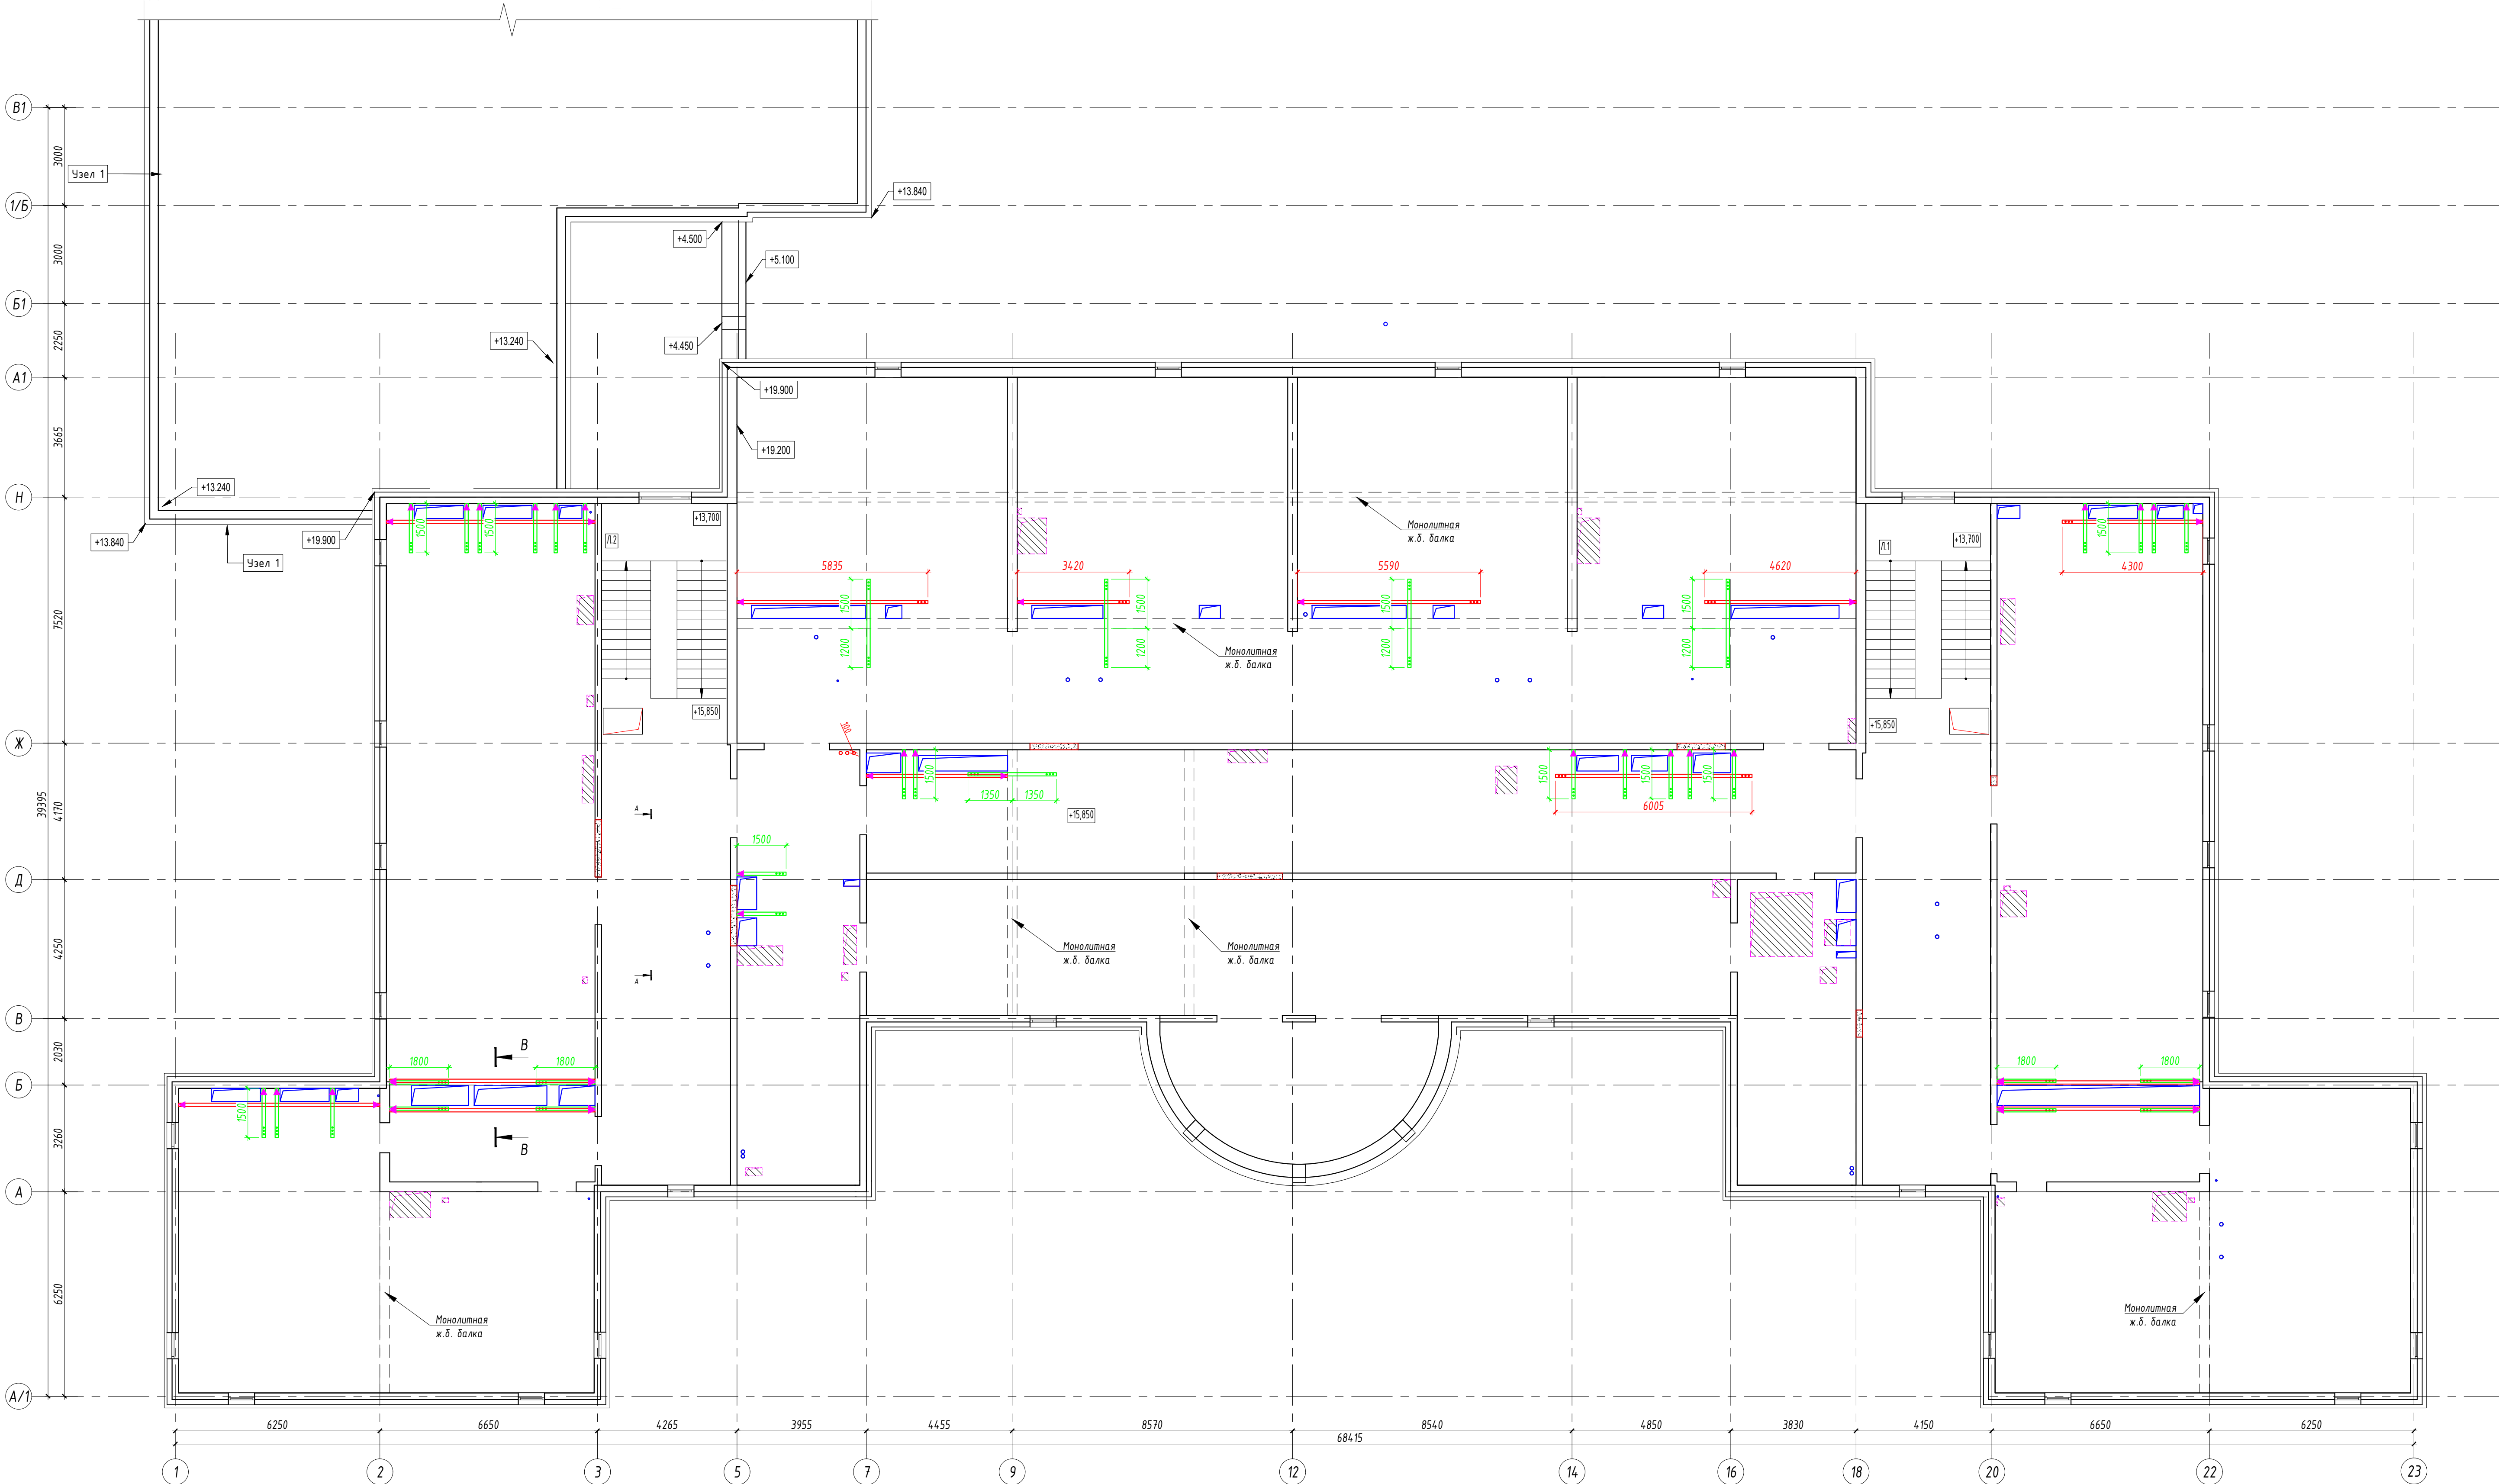

Условные обозначения

- ▲ - крепление полосы усиления согласно узлу 1
- (green) - полоса 10x100 по верхней поверхности плиты перекрытия
- (red) - полоса 10x100 по нижней поверхности плиты перекрытия

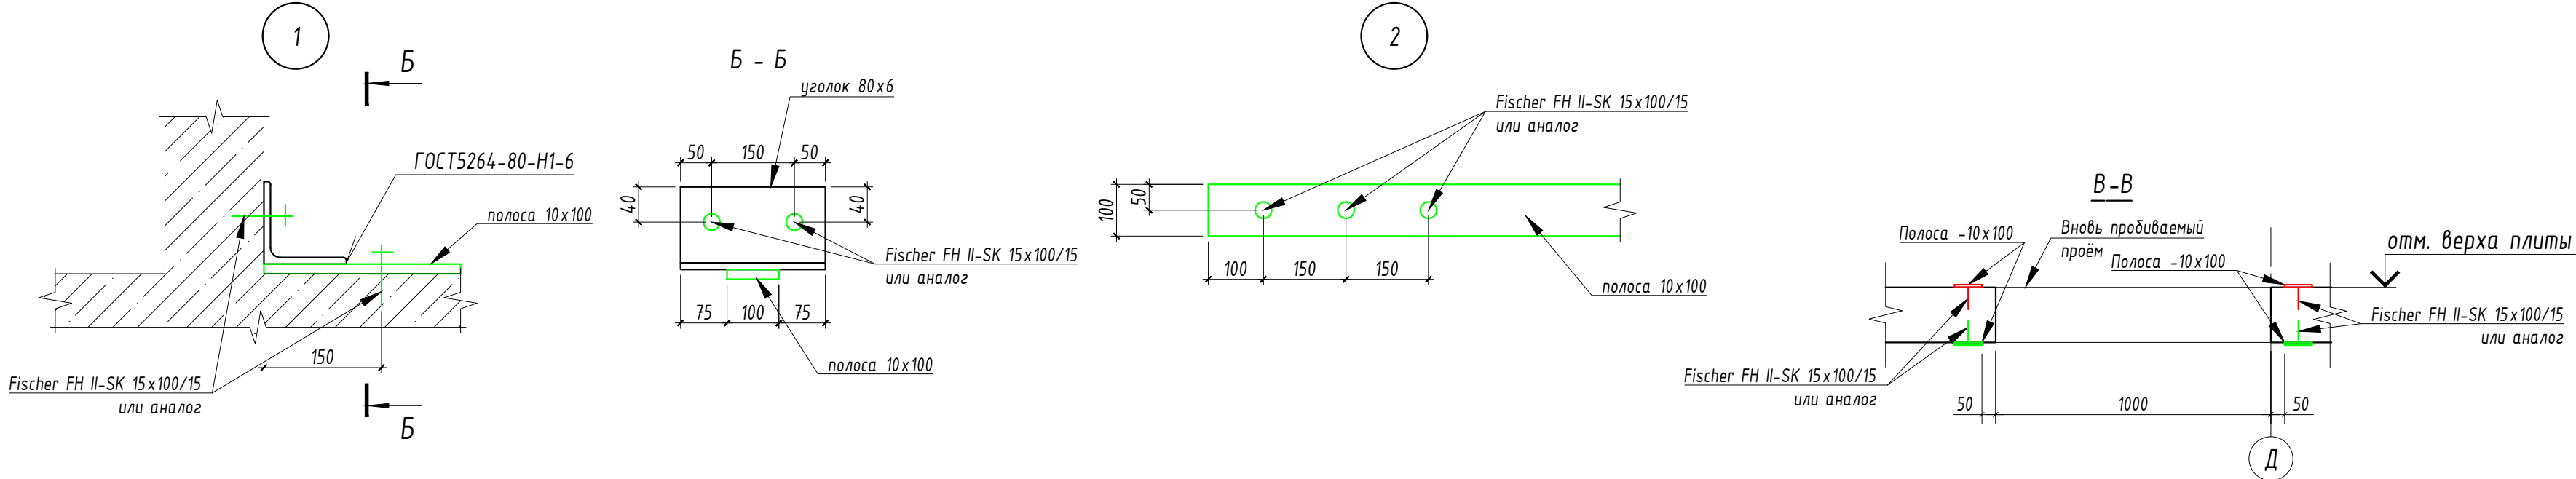


- Порядок производства работ:
- Разрушить перекрытие, подлежащее усилению.
 - В местах расположения элементов усиления произвести очистку перекрытия от мусора, наливой раствора, элементов пирога пола/потолка до основания монолитного железобетона. Для узла №1 так же произвести очистку участка стены.
 - До устройства усиления и замоноличивания существующих проёмов выполнить прорезание новых проёмов в плите перекрытия, в соответствии со схемой на листе 20.
 - Произвести нарезку элементов усиления, при необходимости произвести сварочные работы и выполнение отверстий под анкеры болты согласно узлам 1 и 2. При расположении полосы усиления между вертикальными монолитными конструкциями длину принимать на 40мм меньше фактической.
 - Усиление полосой -10x100 выполнять с отступом в 50 мм от края проёма в соответствии с разрезом В-В.
 - Фиксацию выполнять анкерами Fischer FH II-SK 15x100/15 или аналог.
 - Открытые участки стальных элементов обрабатывать огнезащитным составом, обеспечивающим предел огнестойкости не менее R120. Площадь обработки 7,7 м².
 - Спецификации элементов усиления см. лист 23.

						16-25/Г -Р - КР5				
						Капитальный ремонт объекта "ГБОУ Школа №429 "Соколиная гора", расположенного по адресу: г. Москва, ул. Соколиной горы 5-я, д. 14.				
Изм.	Кол.изм.	Лист	№ док.	Подпись	Дата	Конструктивные решения	Стадия	Лист	Листов	
Разраб.		Варнашов			01.09.2026		Р	21		
Проверил		Прудников			01.09.2026					
						План перекрытия над 4 этажом в осях 1-23/А/1-В1. Элементы усиления			 АЗУРИТ	
Н. контр.		Гударева			01.09.2026					
ГИП		Маркова			01.09.2026					

Спецификация элементов усиления к плану перекрытия над 4 этажом

Поз.	Обозначение	Наименование	Кол.	Масса ед., кг	Примечание
	ГОСТ 34028-2016	Ø10 А500С L=м.п.	205,7	0,616	126,7
	ГОСТ 103-2006	-10х100 L=м.п.	137	7,85	1075,5
	ГОСТ 8509-93	Уголок 80х80х6 L=м.п.	12,3	7,36	90,2
	Анкерный болт втулочный	Fischer FH II-SK 15х100/15 (или аналог)			288 шт.
		Материалы			
	ГОСТ 25029-2020	Грунтовка ГФ-021 (за 1 раз)			17,54 м ²
	ГОСТ 6465-2023	Эмаль ПФ-115 (за 2 раза)			35,08 м ²
	ГОСТ 26633-2015	Бетон В25			2,74 м ³
	ГОСТ 28013-98	Цементно-песчаный раствор М100			7,8 м ³


Взам. инв. N											
Подп. и дата								16-25/Г-Р-КР5			
								Капитальный ремонт объекта "ГБОУ Школа №429 "Соколиная гора", расположенного по адресу: г. Москва, ул. Соколиной горы 5-я, д. 14.			
Инв. N подл.		Изм	Кол.уч	Лист	№ док	Подпись	Дата	Конструктивные решения	Стадия	Лист	Листов
		Разраб.		Варнашов			01.09.2026		Р	23	
		Проверил		Прудников			01.09.2026				
		Н. контр.		Гударева			01.09.2026	Спецификация элементов усиления к плану перекрытия над 4 этажом	 АЗУРИТ		
ГИП		Маркова			01.09.2026						

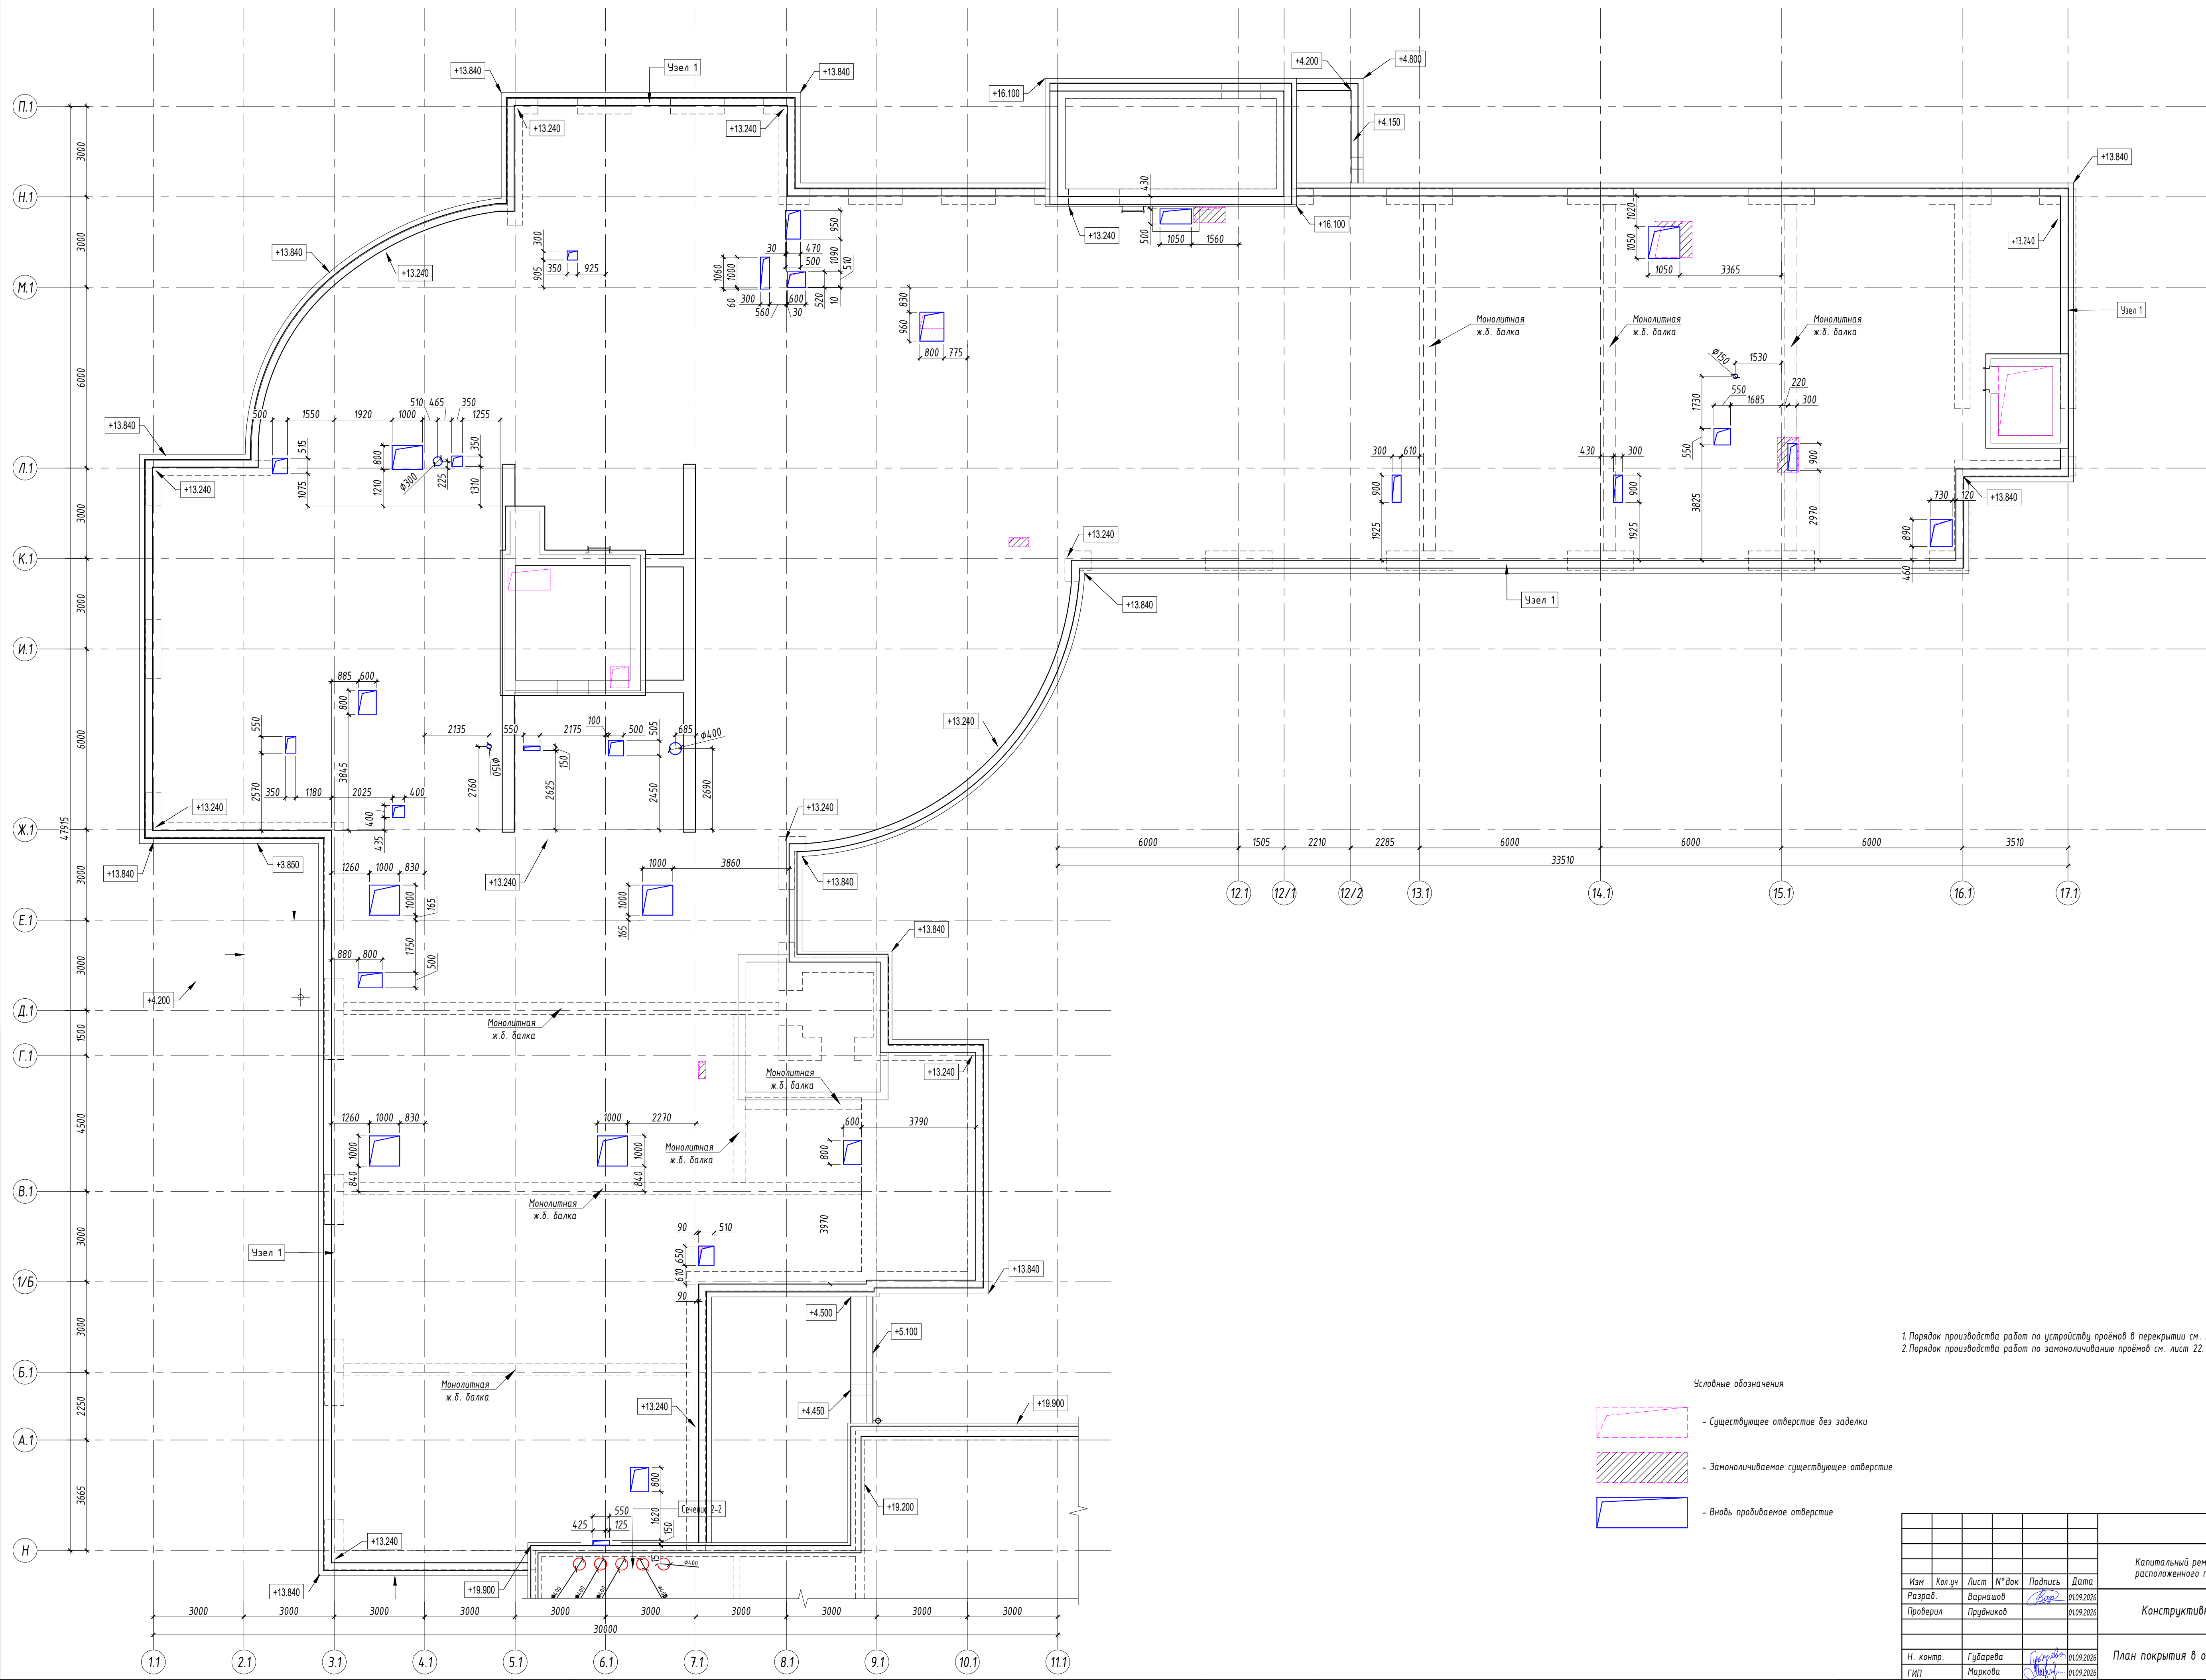

Условные обозначения

-
- Существующее отверстие без заделки
- Заманичиваемое существующее отверстие
- вновь пробиваемое отверстие

[illegible]

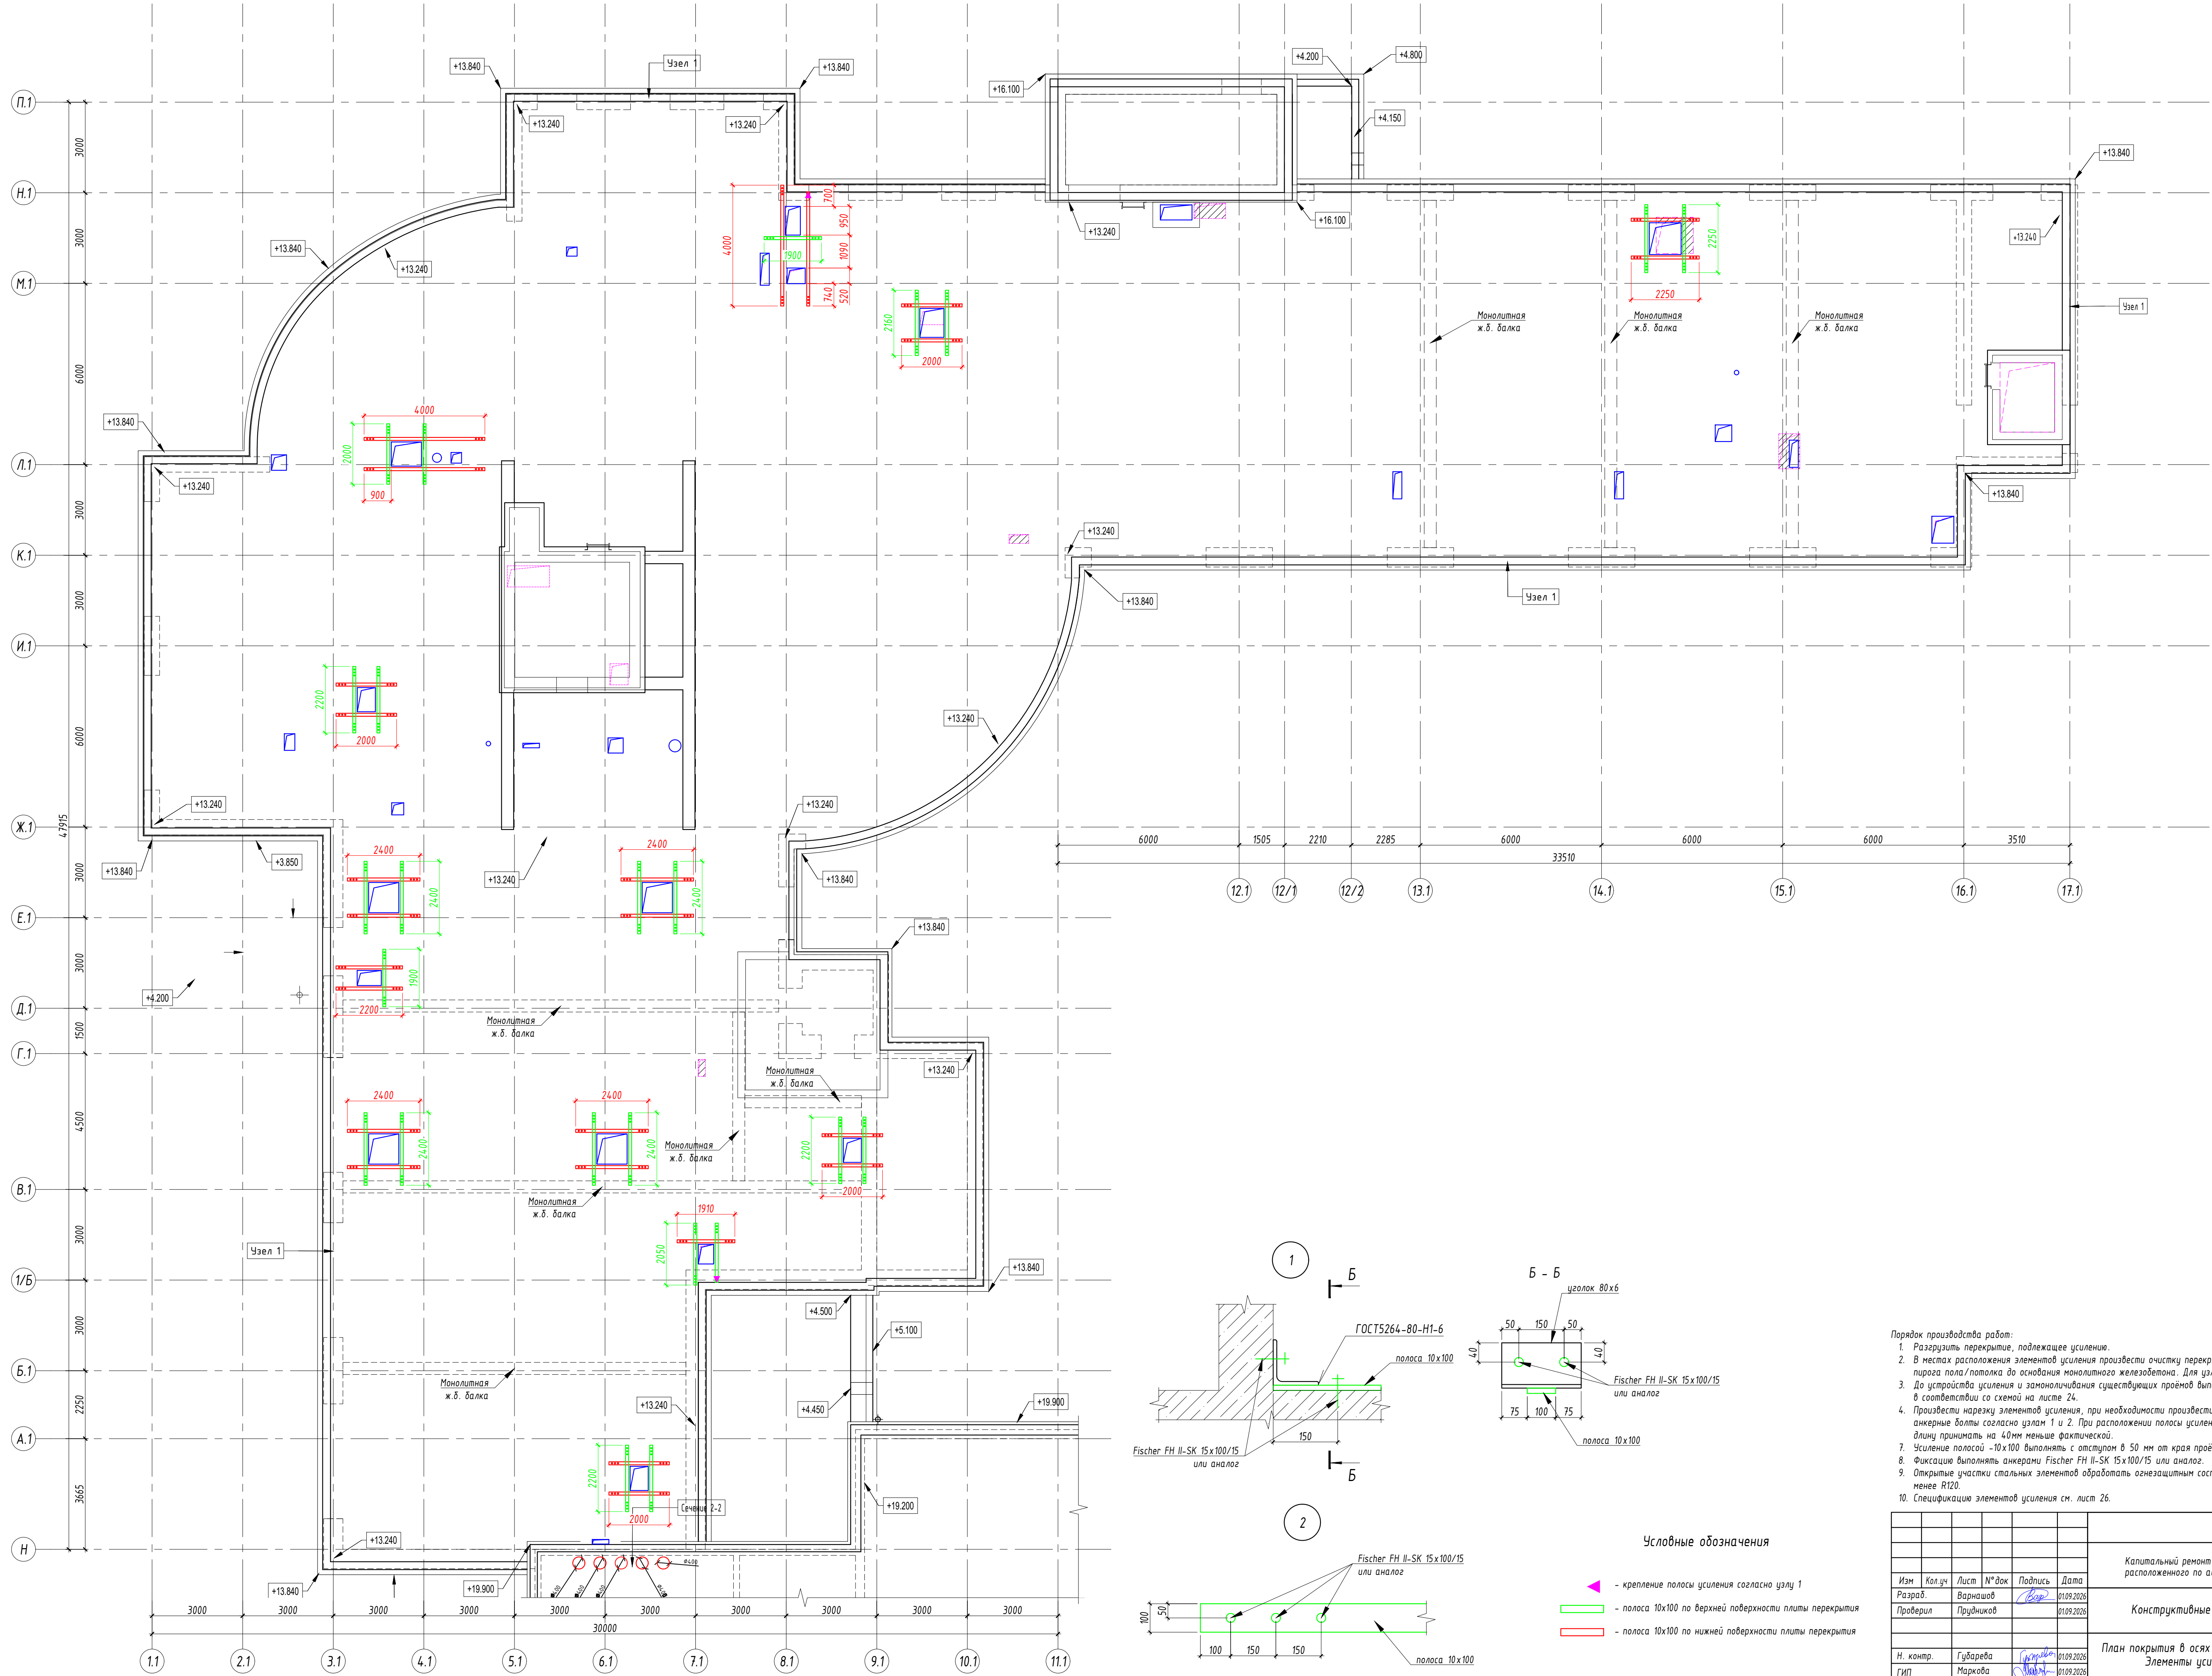

- Порядок производства работ:
1. Разрушить перекрытие, подлежащее усилению.
 2. В местах расположения элементов усиления произвести очистку перекрытия от мусора, наливов раствора, элементов пирога пола/потолка до основания монолитного железобетона. Для узла №1 так же произвести очистку участка стены.
 3. До устройства усиления и замоноличивания существующих проёмов выполнить прорезание новых проёмов в плите перекрытия, в соответствии со схемой на листе 24.
 4. Произвести нарезку элементов усиления, при необходимости произвести сварочные работы и выполнение отверстий под анкерные болты согласно узлам 1 и 2. При расположении полосы усиления между вертикальными монолитными конструкциями длину принимать на 40мм меньше фактической.
 7. Усиление полосой -10x100 выполнять с отступом в 50 мм от края проёма в соответствии с разрезом В-В на листе 21.
 8. Фиксацию выполнять анкерами Fischer FH II-SK 15x100/15 или аналог.
 9. Открытые участки стальных элементов обработать огнезащитным составом, обеспечивающим предел огнестойкости не менее R120.
 10. Спецификацию элементов усиления см. лист 26.

					16-25/Г-Р-КР5		
					Капитальный ремонт объекта "ГБОУ Школа №429 "Сокольная гора", расположенного по адресу: г. Москва, ул. Соколиной горы 5-я, д. 14.		
Изм.	Кол.уч.	Лист	№ док.	Подпись	Дата	Стандия	Лист
Разраб.	Варнашов			01.09.2026		Р	25
Проверил	Прудников			01.09.2026			
					Конструктивные решения		
					План покрытия в осях 1.1-17.1/Н-П.1. Элементы усиления		
Н. контр.	Губарева			01.09.2026			
ГИП	Маркова			01.09.2026			

Спецификация элементов усиления к плану покрытия						
Поз.	Обозначение	Наименование		Кол.	Масса ед., кг	Примечание
	ГОСТ 34028-2016	Ø10 A500C	L=м.п.	205,7	0,616	126,7
	ГОСТ 103-2006	-10x100	L=м.п.	119,5	7,85	938,1
	ГОСТ 8509-93	Уголок 80x80x6	L=м.п.	0,5	7,36	3,7
	Анкерный болт втулочный	Fischer FH II-SK 15x100/15 (или аналог)				294 шт.
		Материалы				
	ГОСТ 25029-2020	Грунтовка ГФ-021 (за 1 раз)				12,11 м²
	ГОСТ 6465-2023	Эмаль ПФ-115 (за 2 раза)				24,22 м²
	ГОСТ 26633-2015	Бетон В25				0,41 м³
	ГОСТ 28013-98	Цементно-песчаный раствор М100				7,8 м³

Взам. инв. N	
Подп. и дата	
Инв. N подл.	

						16-25/Г-Р-КР5					
						Капитальный ремонт объекта "ГБОУ Школа №429 "Соколиная гора", расположенного по адресу: г. Москва, ул. Соколиной горы 5-я, д. 14.					
Изм	Кол.уч	Лист	№ док	Подпись	Дата	Конструктивные решения			Стадия	Лист	Листов
Разраб.		Варнашов			01.09.2026				Р	26	
Проверил		Прудников			01.09.2026						
						Спецификация элементов усиления к плану покрытия			 АЗУРИТ		
Н. контр.		Гударева			01.09.2026						
ГИП		Маркова			01.09.2026						