

Схема расположения фундаментной плиты входной группы в/о 11.1/П.1 на отм. -1,700

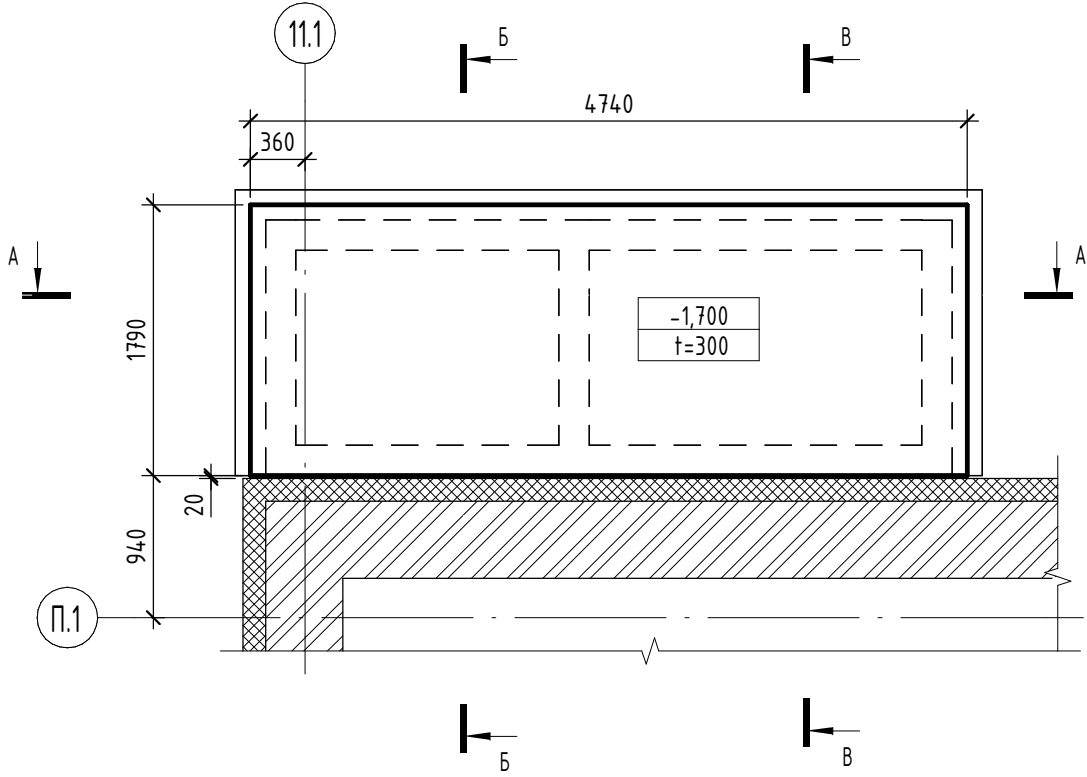


Схема расположения стен входной группы в/о 11.1/П.1 на отм. -1,700



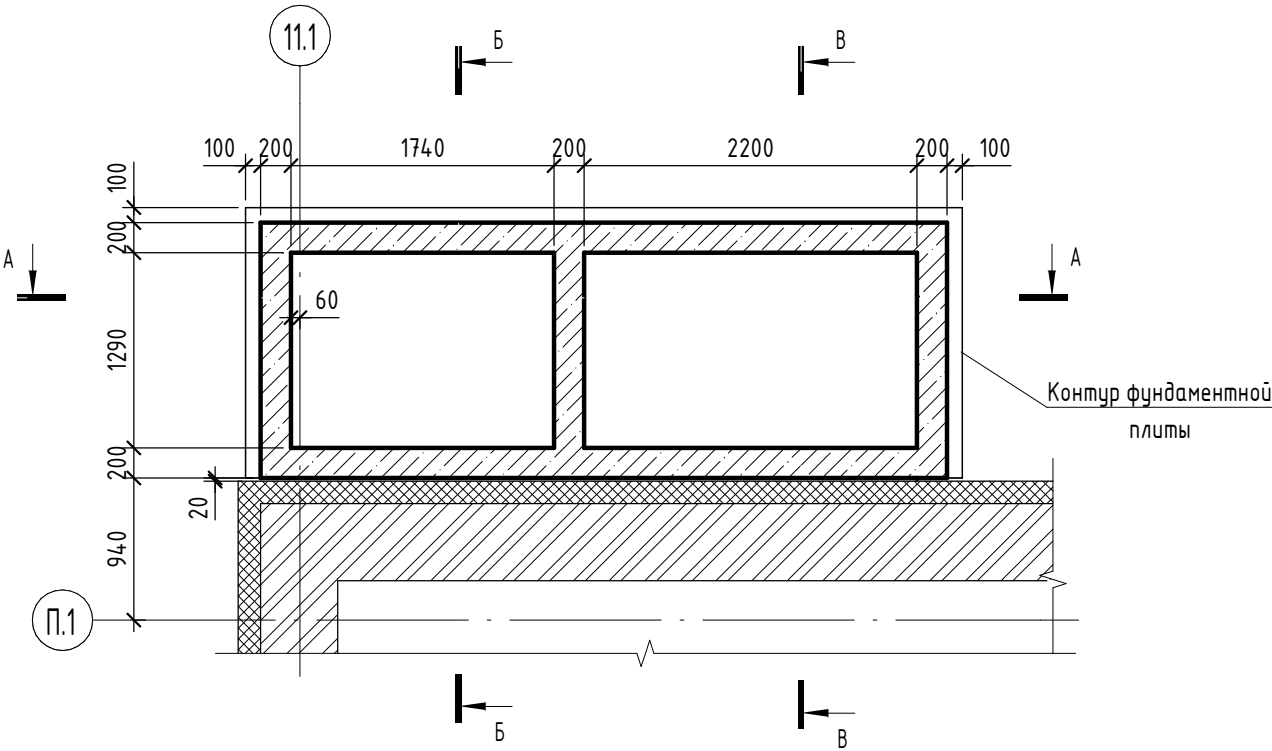


Схема расположения входной группы в/о 11.1/П.1 на отм. -0,070

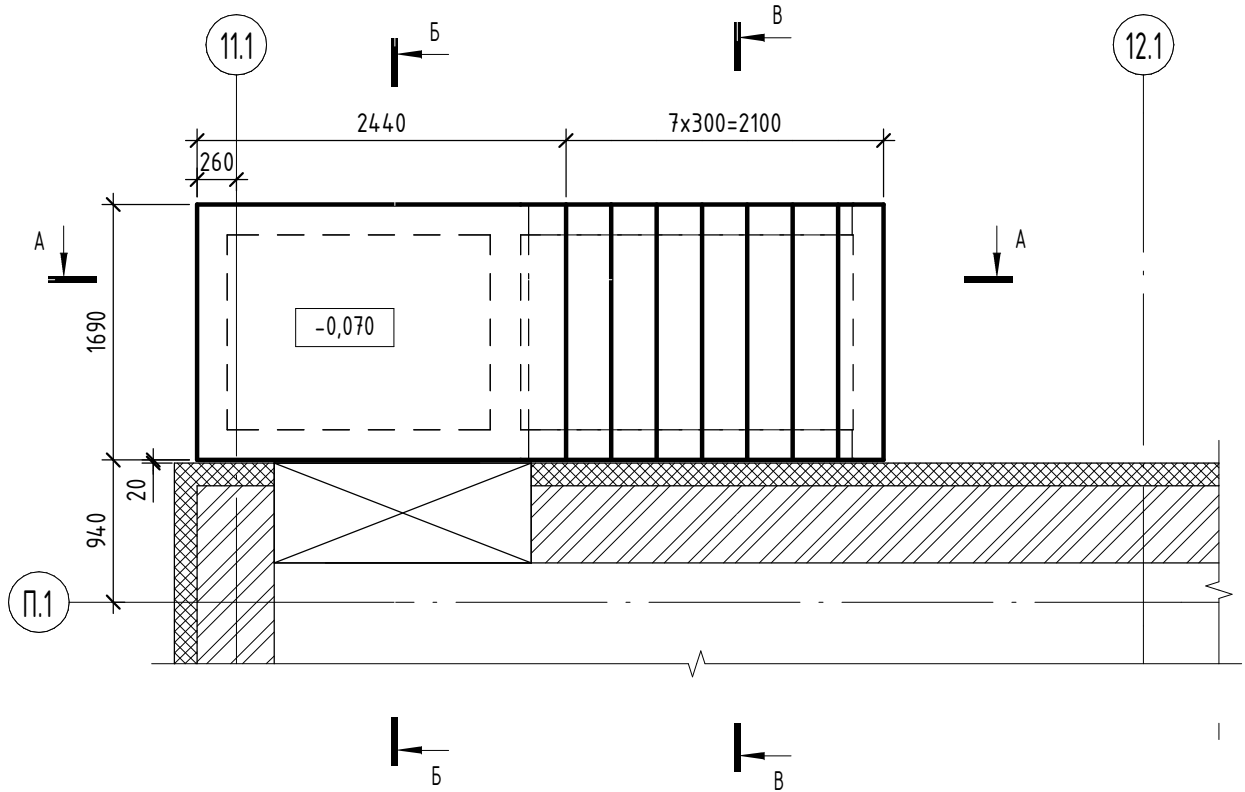

А-А

Опалубка

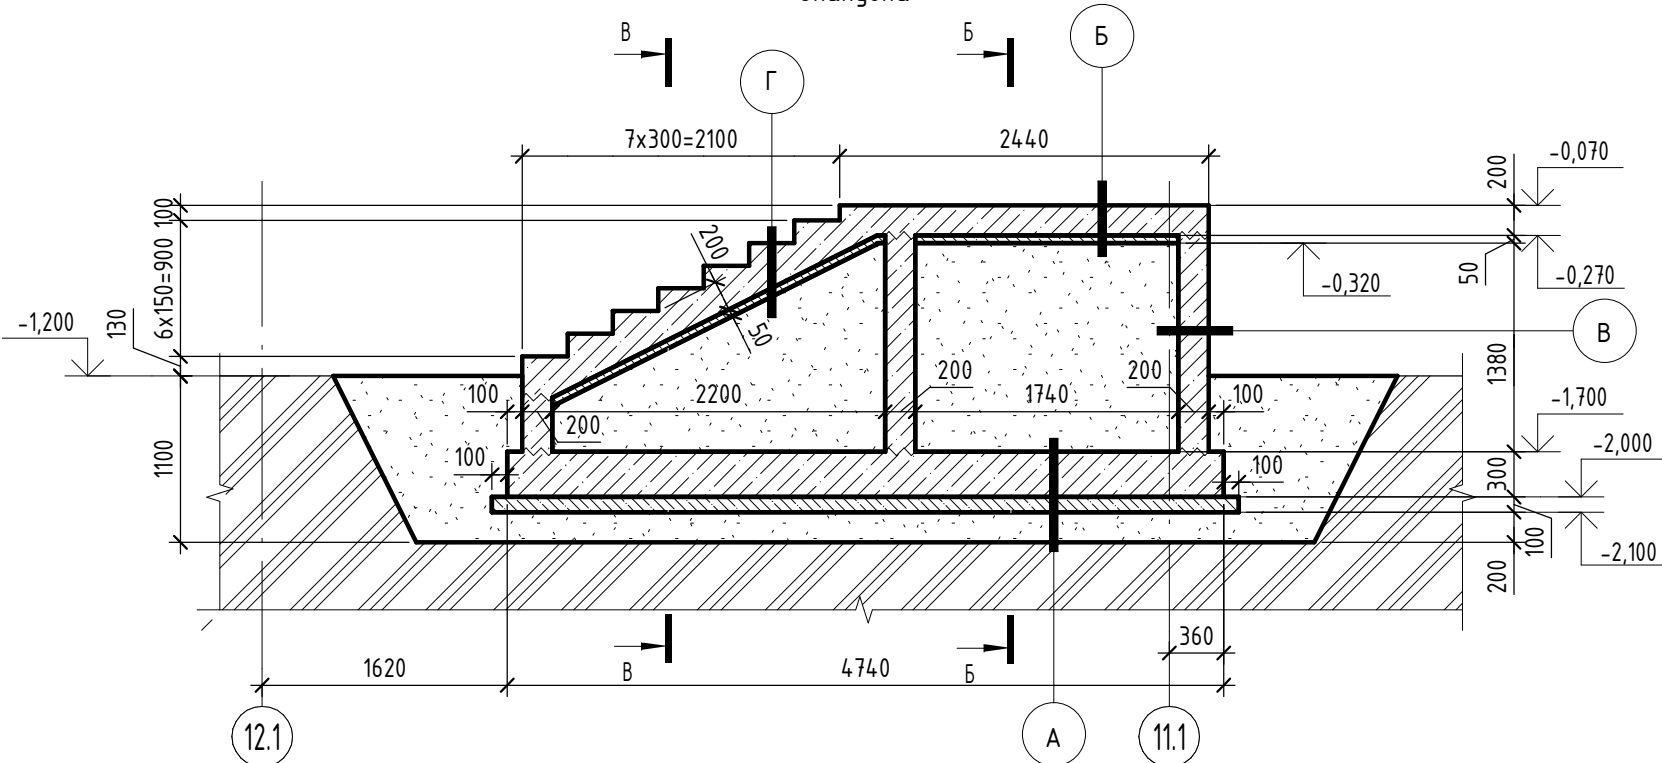

Ведомость расхода бетона, м³

Конструкция	Бетон класса		
	В7.5	B25 F150 W6	Итого
Фундаментная плита	0	2,55	2,55
Стены	0	2,88	2,88
Площадка	0	0,72	0,72
Лестничный марш	0	1,17	1,17
Бетонная подготовка	1,2	0	1,2
Всего	1,2	7,32	8,52

А

Монолитная плита (B25 W6 F150)	-300мм
Гидроизоляция обмазочная	-2 слоя
Бетонная подготовка В7,5	-100мм
Песок средней крупности	утрамбованный послойно (Купл=0,95)
Пленка ПЭ 200мкм	-2 слоя
Грунт основания	

Монолитная плита (B25 W6 F150) -200мм

Пленка ПЭ 200мкм	-2 слоя
Бетонная подготовка В7,5	-50мм
Засыпка песком средней крупности	утрамбованный послойно (Купл=0,95)
Пленка ПЭ 200мкм	-2 слоя

Б

Г

Гидроизоляция обмазочная	-2 слоя
Монолитная стена (B25 W6 F150) -200мм	
Пленка ПЭ 200мкм	-2 слоя
Засыпка песком средней крупности	утрамбованный послойно (Купл=0,95)

В

Монолитная лестница (B25 W6 F150) -200мм	
Пленка ПЭ 200мкм	-2 слоя
Бетонная подготовка В7,5	-50мм
Засыпка песком средней крупности	утрамбованный послойно (Купл=0,95)
Пленка ПЭ 200мкм	-2 слоя

- Общие данные см. лист 1
- Армирование см. лист 3
- Все конструкции соприкасающиеся с грунтом гидроизолировать 2 слоями обмазочной гидроизоляции на битумной основе по 2 слоям битумного праймера.

Ведомость расхода материалов

Поз.	Обозначение	Наименование	Кол.	Масса ед, кг	Примечание
		Материалы			
	ГОСТ 30693-2000	Гидроизоляция обмазочная (Битумная мастика)			23,98 м²
	ГОСТ 8736-2014	Песок средней крупности			17,7 м³
	ГОСТ 10354-82	Пленка полиэтиленовая 200 мкм (2 слоя)			24,76 м²

0,000=156,92


16-25/Г-Р-КР1

Капитальный ремонт объекта "ГБОУ "Школа №429 "Соколиная гора", расположенного по адресу: г.Москва, ул.Соколиной Горы 5-ая, д.14

Изм.	Кол.уч.	Лист	№ док.	Подпись	Дата	Конструктивные решения	Стадия	Лист	Листов
Разраб.	Шевченко	06.26					Р	2	
Проверил	Дидык	06.26							
Н.контр.	Губарева Е.В.	06.26				Схема расположения входной группы в/о 11.1/П.1			
ГИП	Маркова	06.26							



Схема армирования стен входной группы в/о 11.1/П.1 на отм -1,700

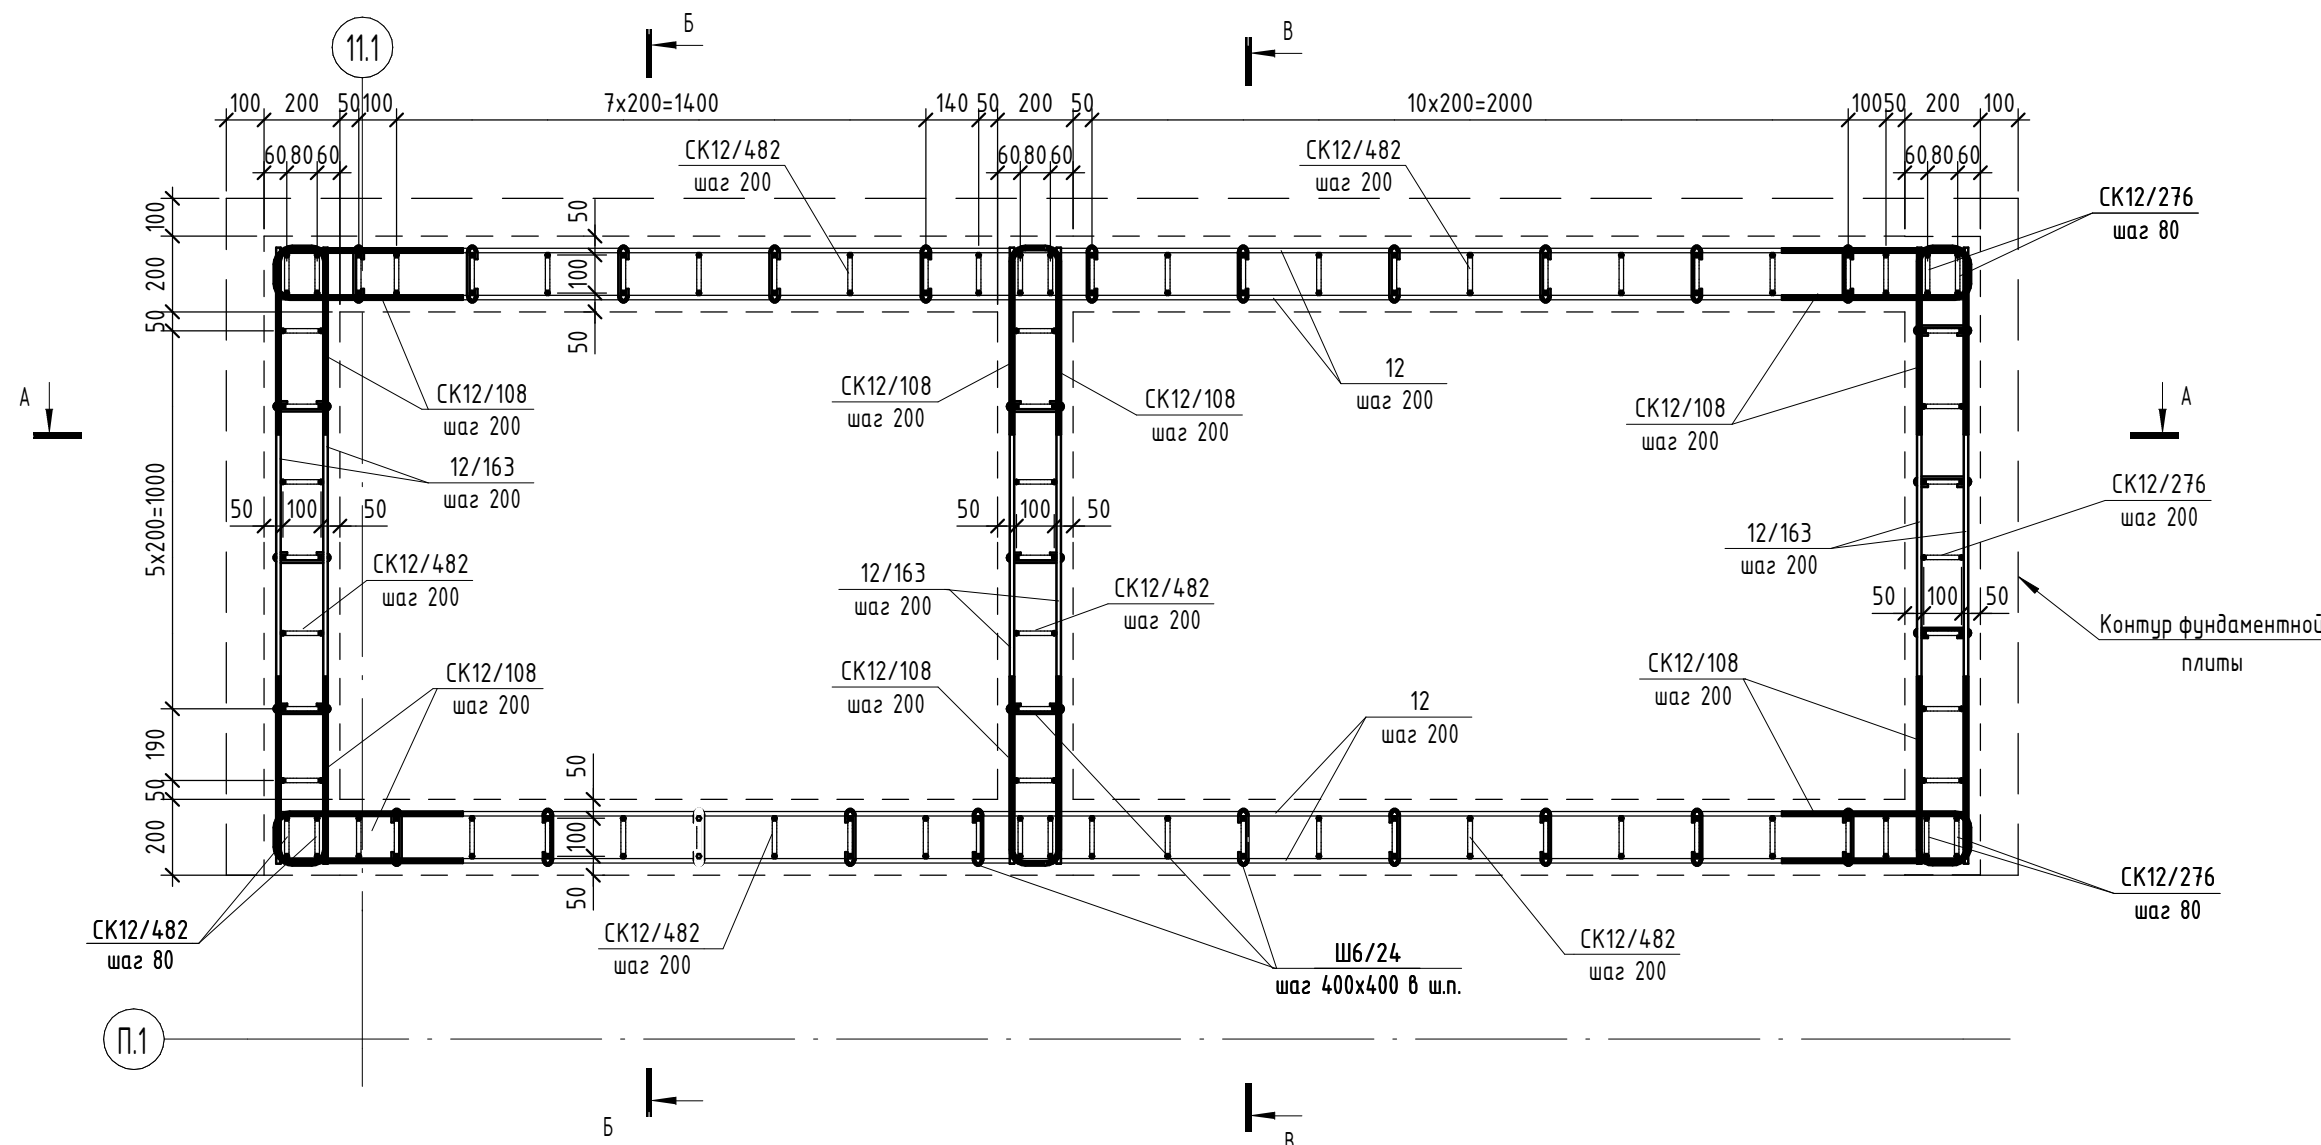

А-А
Армирование

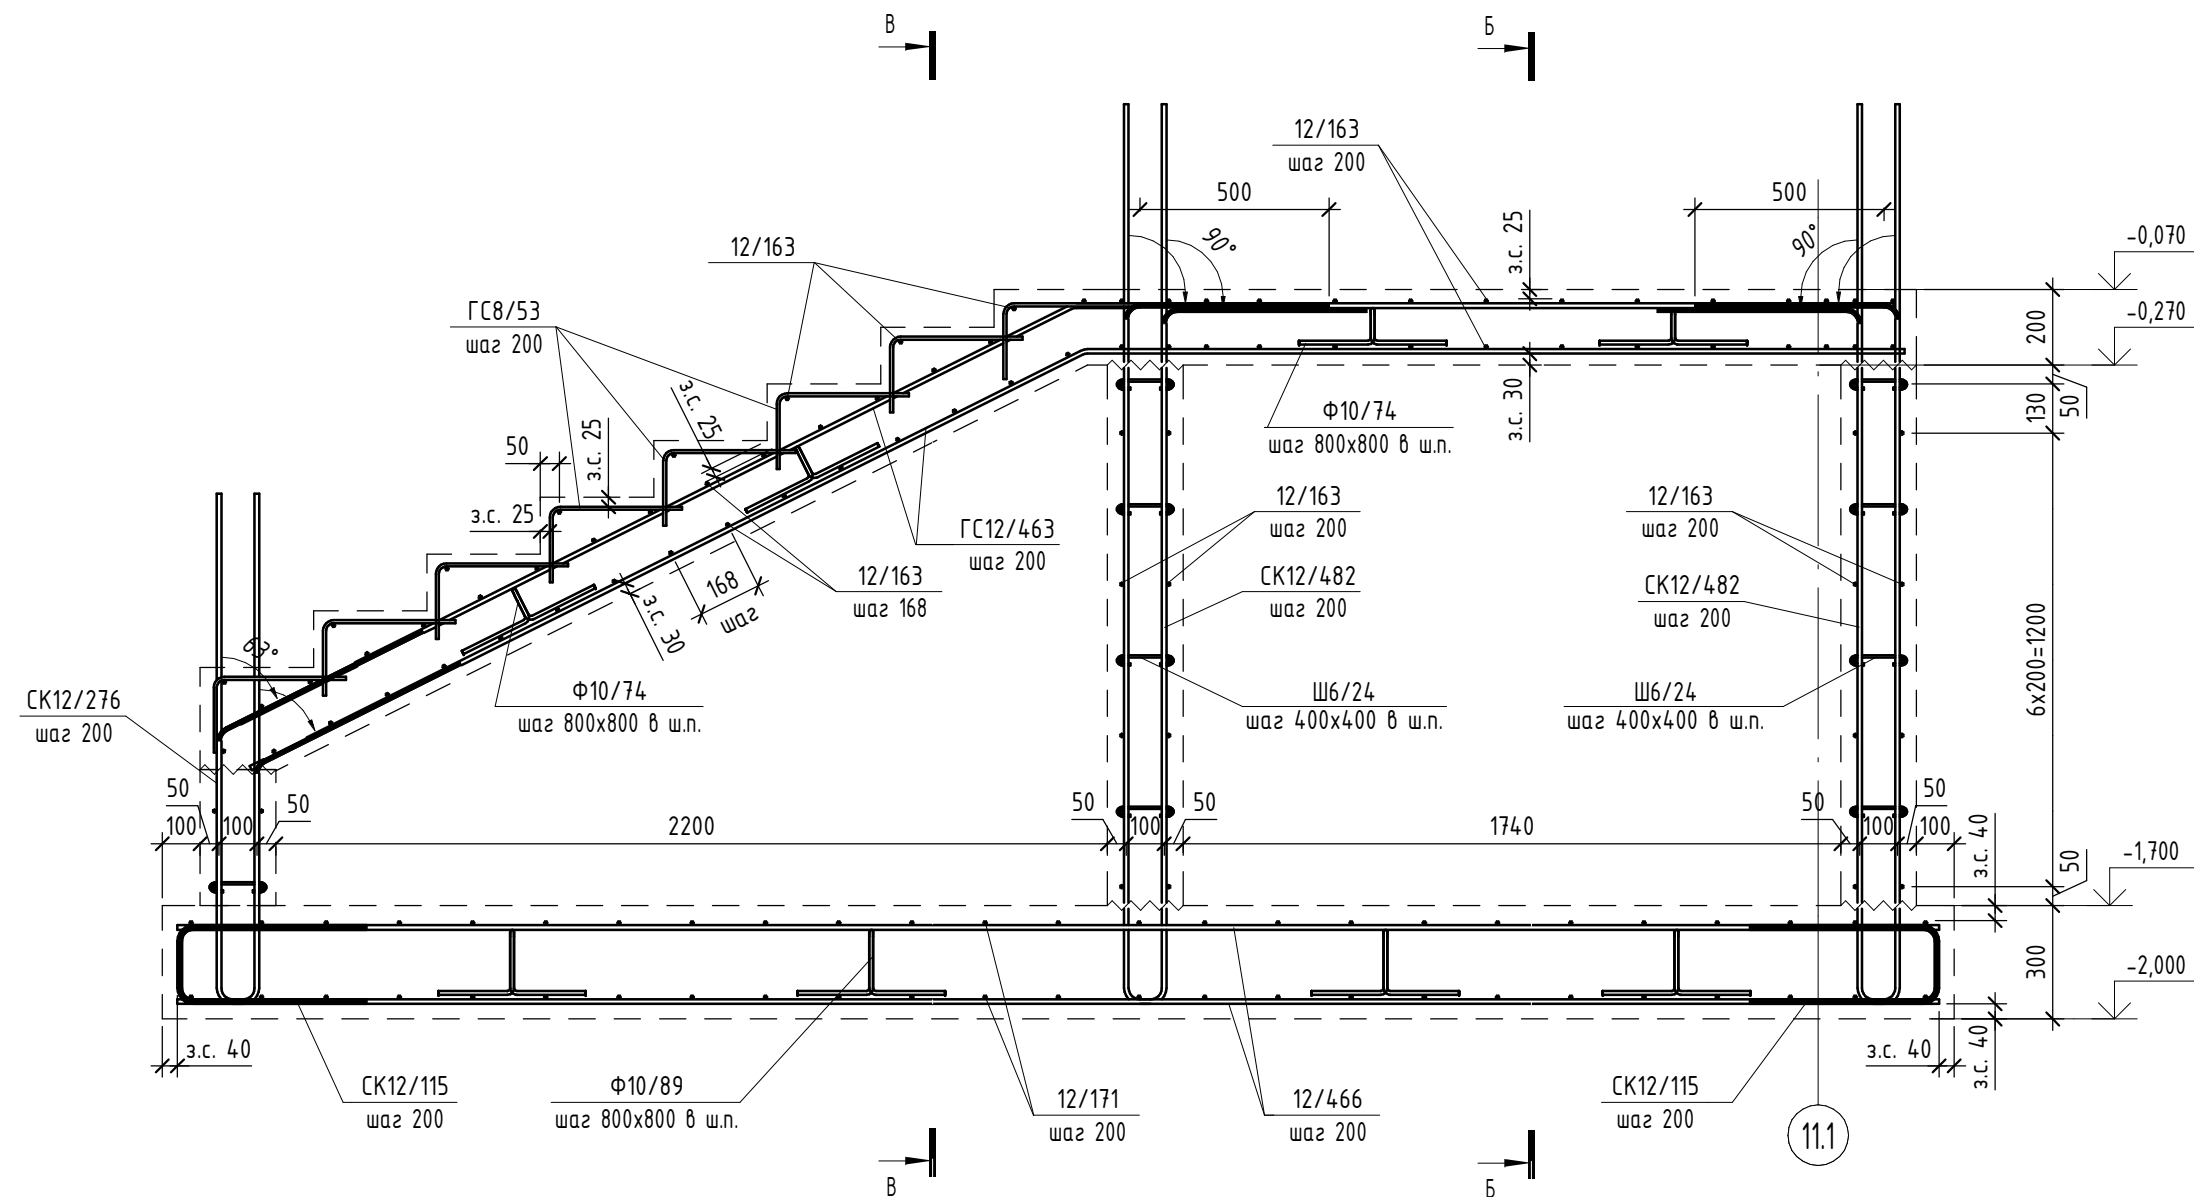


Схема расположения
фиксаторов Ф10



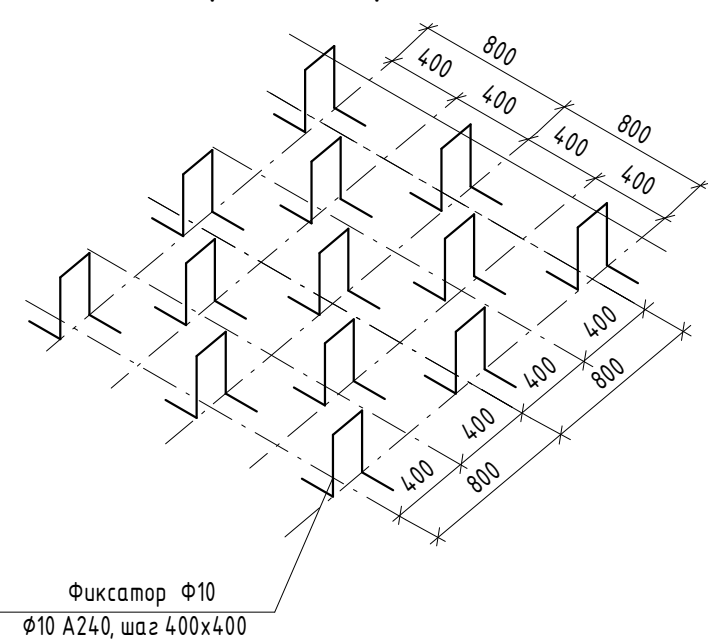



Схема расположения шпилек
с шагом 400х400
в шахматном порядке

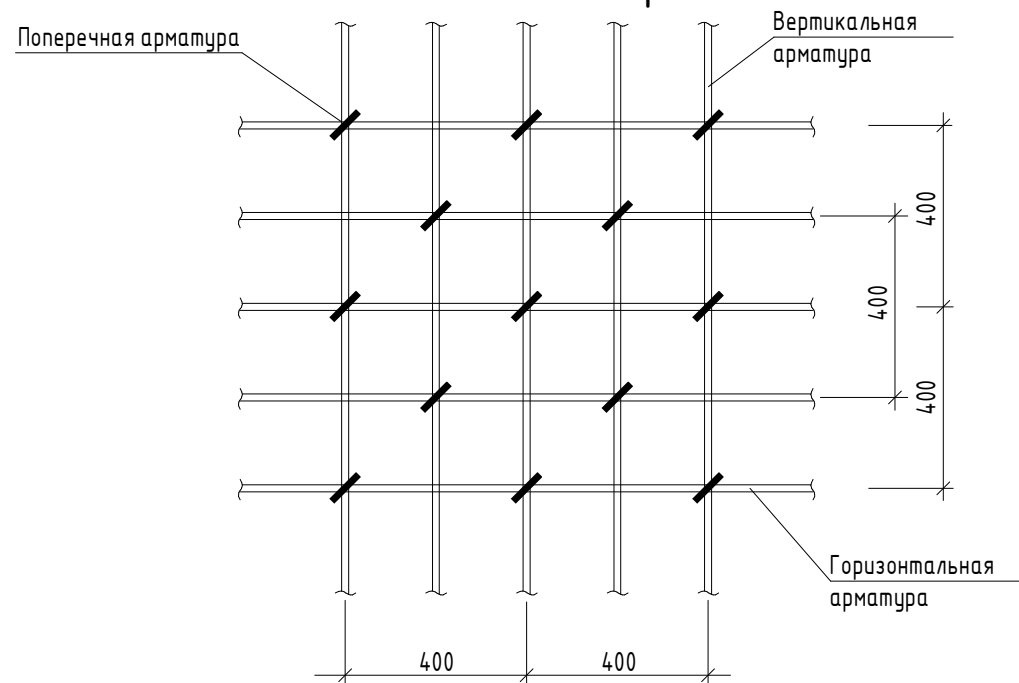

Б-Б
Армирование

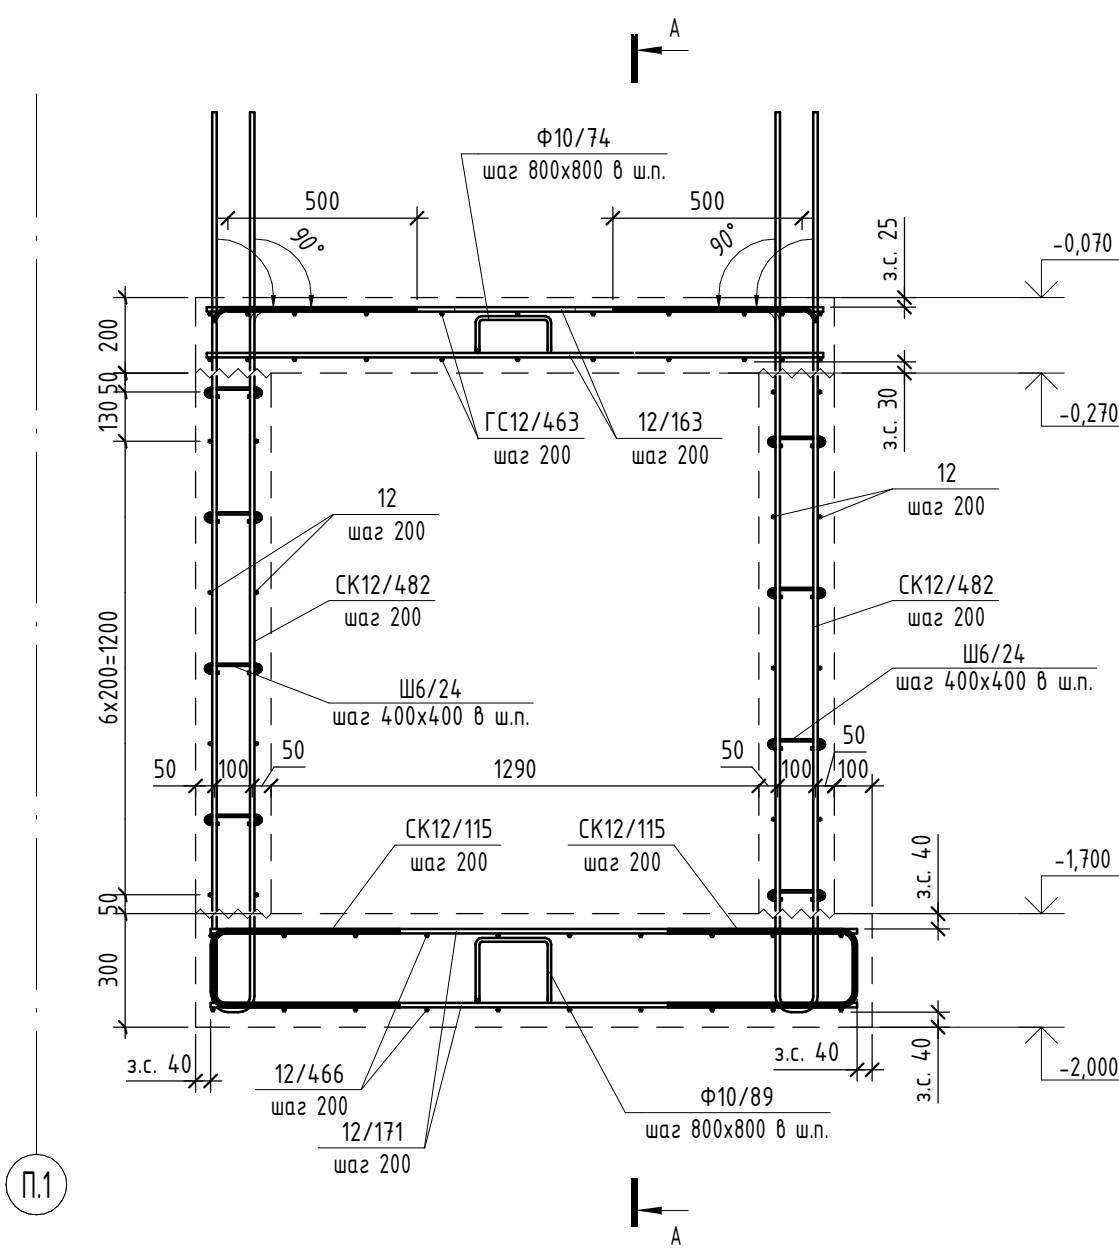

В-В
Армирование

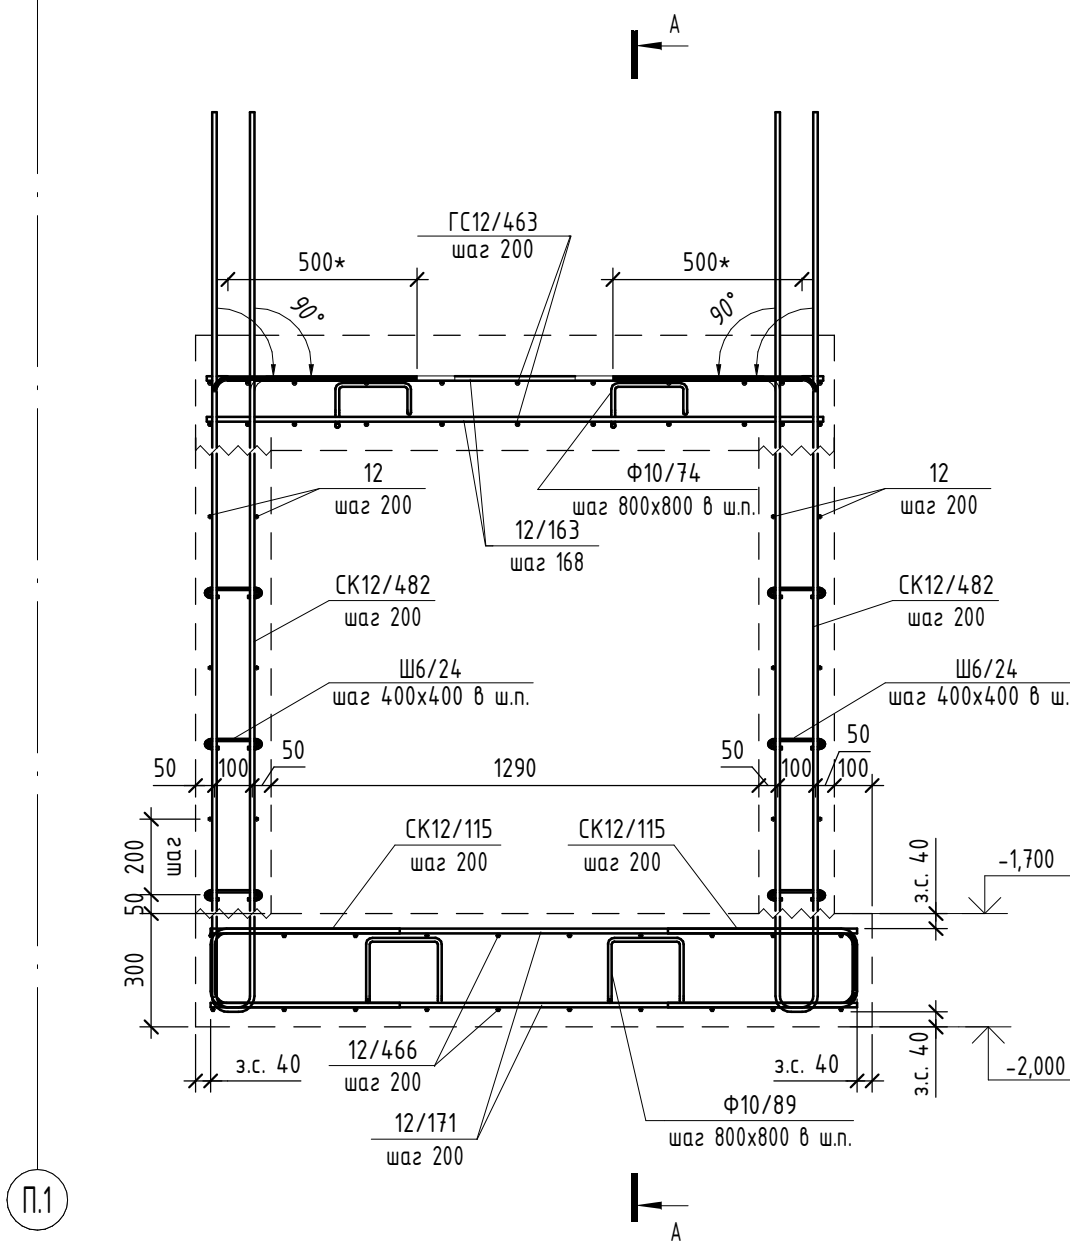

Ведомость деталей

Поз.	Эскиз
ГС8/53	
ГС12/463	
СК12/482	
СК12/276	
СК12/115	

Ведомость деталей


Поз.	Эскиз
СК12/108	
Ш6/24	
Ф10/89	
Ф10/74	

Примечание:
1) Размеры скел (СК) указаны по внутренним границам деталей.
2) Перед изготовлением гнутых элементов производителя работ выполнить пробный образец и сверить с фактическим армированием.

Спецификация элементов армирования входной группы


Поз.	Обозначение	Наименование	Кол.	Масса ед, кг	Примечание
		Наименование конструкции			
		Детали			
12	ГОСТ 34028-2016	Ø12 А500С L, поз.м	118	0,888	104,80
12/466	ГОСТ 34028-2016	Ø12 А500С L= 4660	20	4,139	82,78
12/171	ГОСТ 34028-2016	Ø12 А500С L= 1710	50	1,519	75,96
12/163	ГОСТ 34028-2016	Ø12 А500С L= 1630	103	1,448	149,21
ГС8/53	ГОСТ 34028-2016	Ø8 А500С L= 530	72	0,21	15,12
ГС12/463	ГОСТ 34028-2016	Ø12 А500С L= 4635	22	4,116	90,56
СК12/482	ГОСТ 34028-2016	Ø12 А500С L= 4815	66	4,276	282,24
СК12/276	ГОСТ 34028-2016	Ø12 А500С L= 2755	11	2,447	26,91
СК12/115	ГОСТ 34028-2016	Ø12 А500С L= 1155	70	1,026	71,82
СК12/108	ГОСТ 34028-2016	Ø12 А500С L= 1080	56	0,96	53,76
Ш6/24	ГОСТ 34028-2016	Ø6 А240 L= 240	180	0,054	9,72
Ф10/89	ГОСТ 34028-2016	Ø10 А240 L= 895	10	0,553	5,54
Ф10/74	ГОСТ 34028-2016	Ø10 А240 L= 745	10	0,46	4,60

Схема стыка арматурных стержней
(перепуск стержней без сварки)

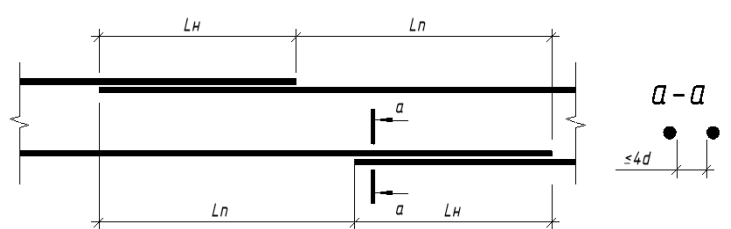

Тип арматуры	Длина нахлеста Lн	Длина анкеровки	Смещение нахлеста Lн, не менее
Ф12 А500С	595	500	800

Диаметр гибки арматуры

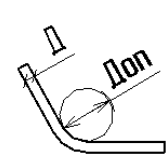

Диаметр стержня, мм	Минимальный диаметр оправки, мм
А240	
Ø6	15
Ø10	25
А500С	
Ø8	40
Ø12	60

Ведомость расхода стали, кг

Марка конструкции	Изделия арматурные						Всего
	Арматура класса						
	A240			A500C			
	ГОСТ 34028-2016			ГОСТ 34028-2016			
	Ø6	Ø10	Итого	Ø8	Ø12	Итого	
Фундаментная плита	0	5,5	5,5	0	539,7	539,7	545,3
Стены	9,7	0	9,7	0	210,7	210,7	220,4
Площадка	0	2,3	2,3	0	131,1	131,1	133,4
Лестничный марш	0	2,3	2,3	15,1	56,5	71,6	73,9
Общий расход	9,7	10,1	19,9	15,1	938	953,2	973

- Общие данные см. лист 1
- Опубличные чертежи см. лист 2
- * - арматуру обрезать по месту

Условные обозначения:
з.с. - защитный слой бетона
~~~~~ - шаг бетонирования

|   |               |      |        |         |      |
|---|---------------|------|--------|---------|------|
| 16-25/Г-Р-КР1   |               |      |        |         |      |
| Капитальный ремонт объекта "ГБОУ "Школа №429 "Сокольная гора", расположенного по адресу: г.Москва, ул.Сокольной Горы 5-ая, в.14 |               |      |        |         |      |
| Изм.   | Кол.уч.       | Лист | № док. | Подпись | Дата |
| Разраб.   | Шевченко      | 1    | 06.26  |         |      |
| Проверил   | Дидж          | 1    | 06.26  |         |      |
| Конструктивные решения   |               |      |        | Стадия  | Лист |
|   |               |      |        | Р       | 3    |
| Н.контр.   | Губарева Е.В. | 1    | 06.26  |         |      |
| ГИП   | Маркова       | 1    | 06.26  |         |      |
| Схема армирования входной группы в/о 11.1/П.1                                                                                   |               |      |        |         |      |
| АЗУРИТ   |               |      |        |         |      |