

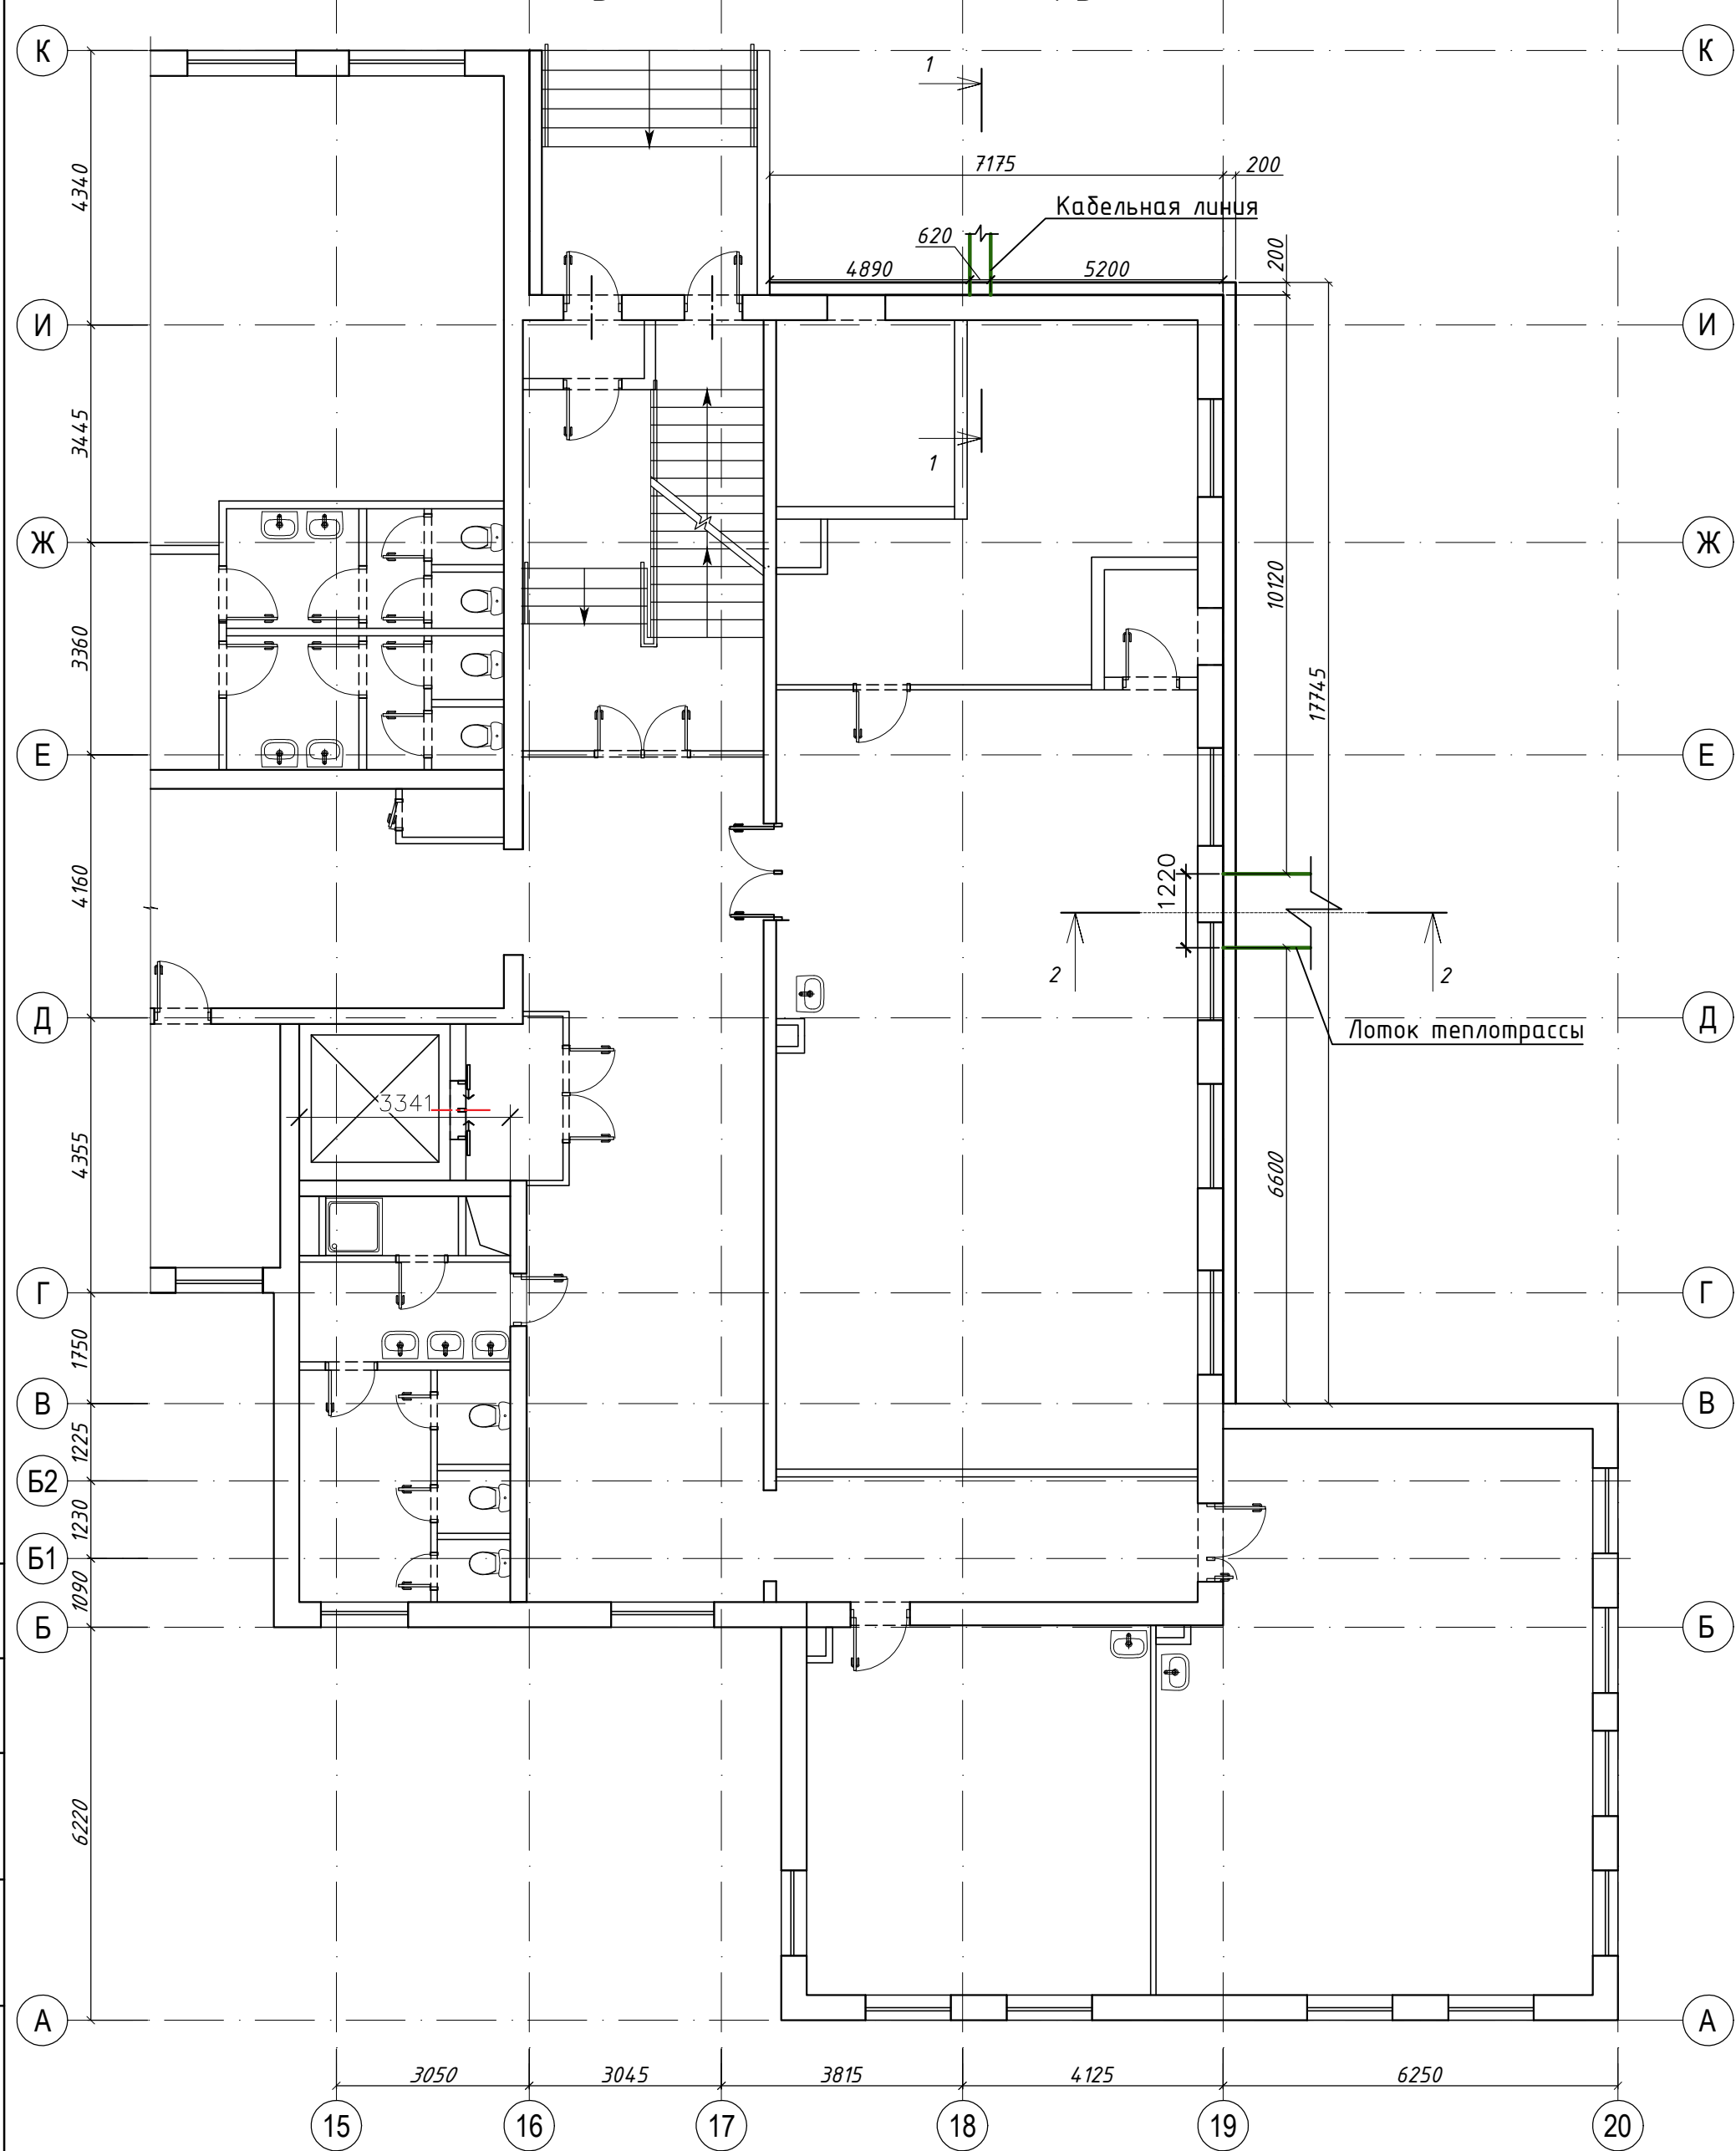


Схема усиления ленточного фундамента

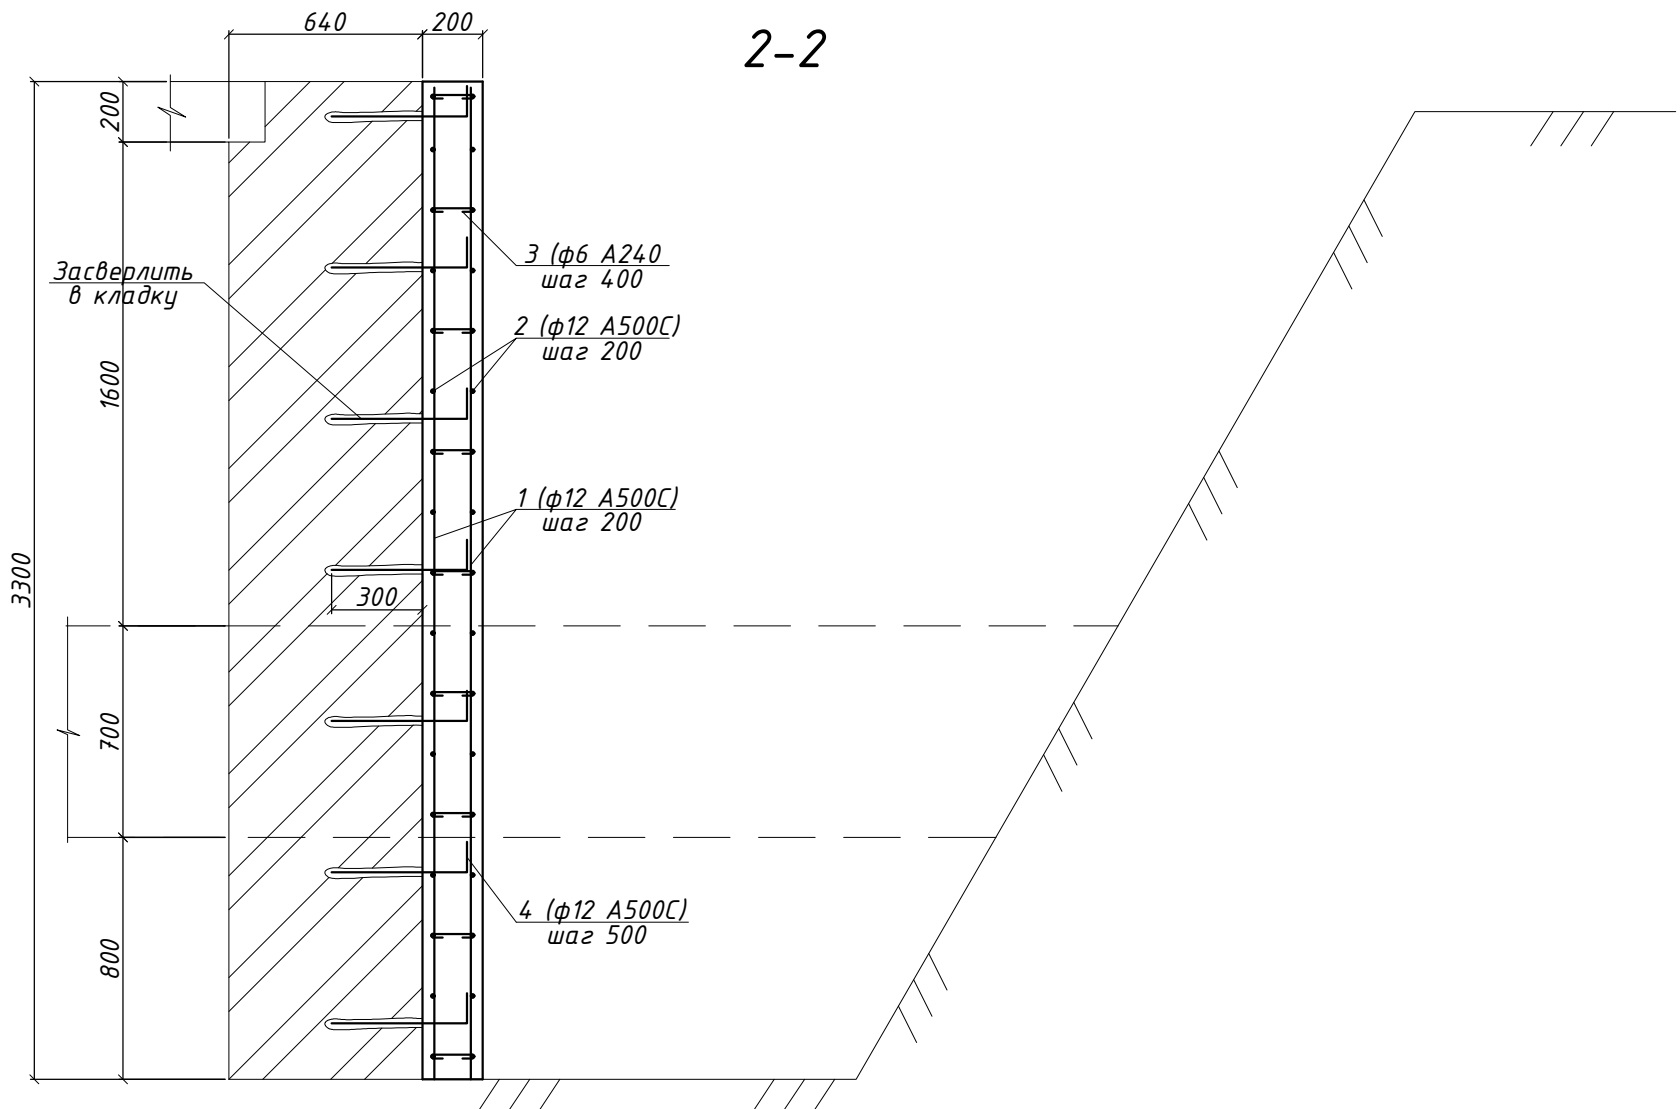

Спецификация элементов усиления дубового фундамента

Поз.	Обозначение	Наименование	Кол. шт.	Масса ед. кг.	Прим.
1	ГОСТ 34028-2016	Ø 12 A500C L= 3580	254	3.18	807.31
2	ГОСТ 34028-2016	Ø 12 A500C L (м.п.) 9546	-	0.888	847.68
3	ГОСТ 34028-2016	Ø 6 A240 L= 295	576	0.07	37.71
4	ГОСТ 34028-2016	Ø 12 A500C L= 550	357	0.49	174.32
		Бетон кл. В25, W6, F150 (м³)	16.6		

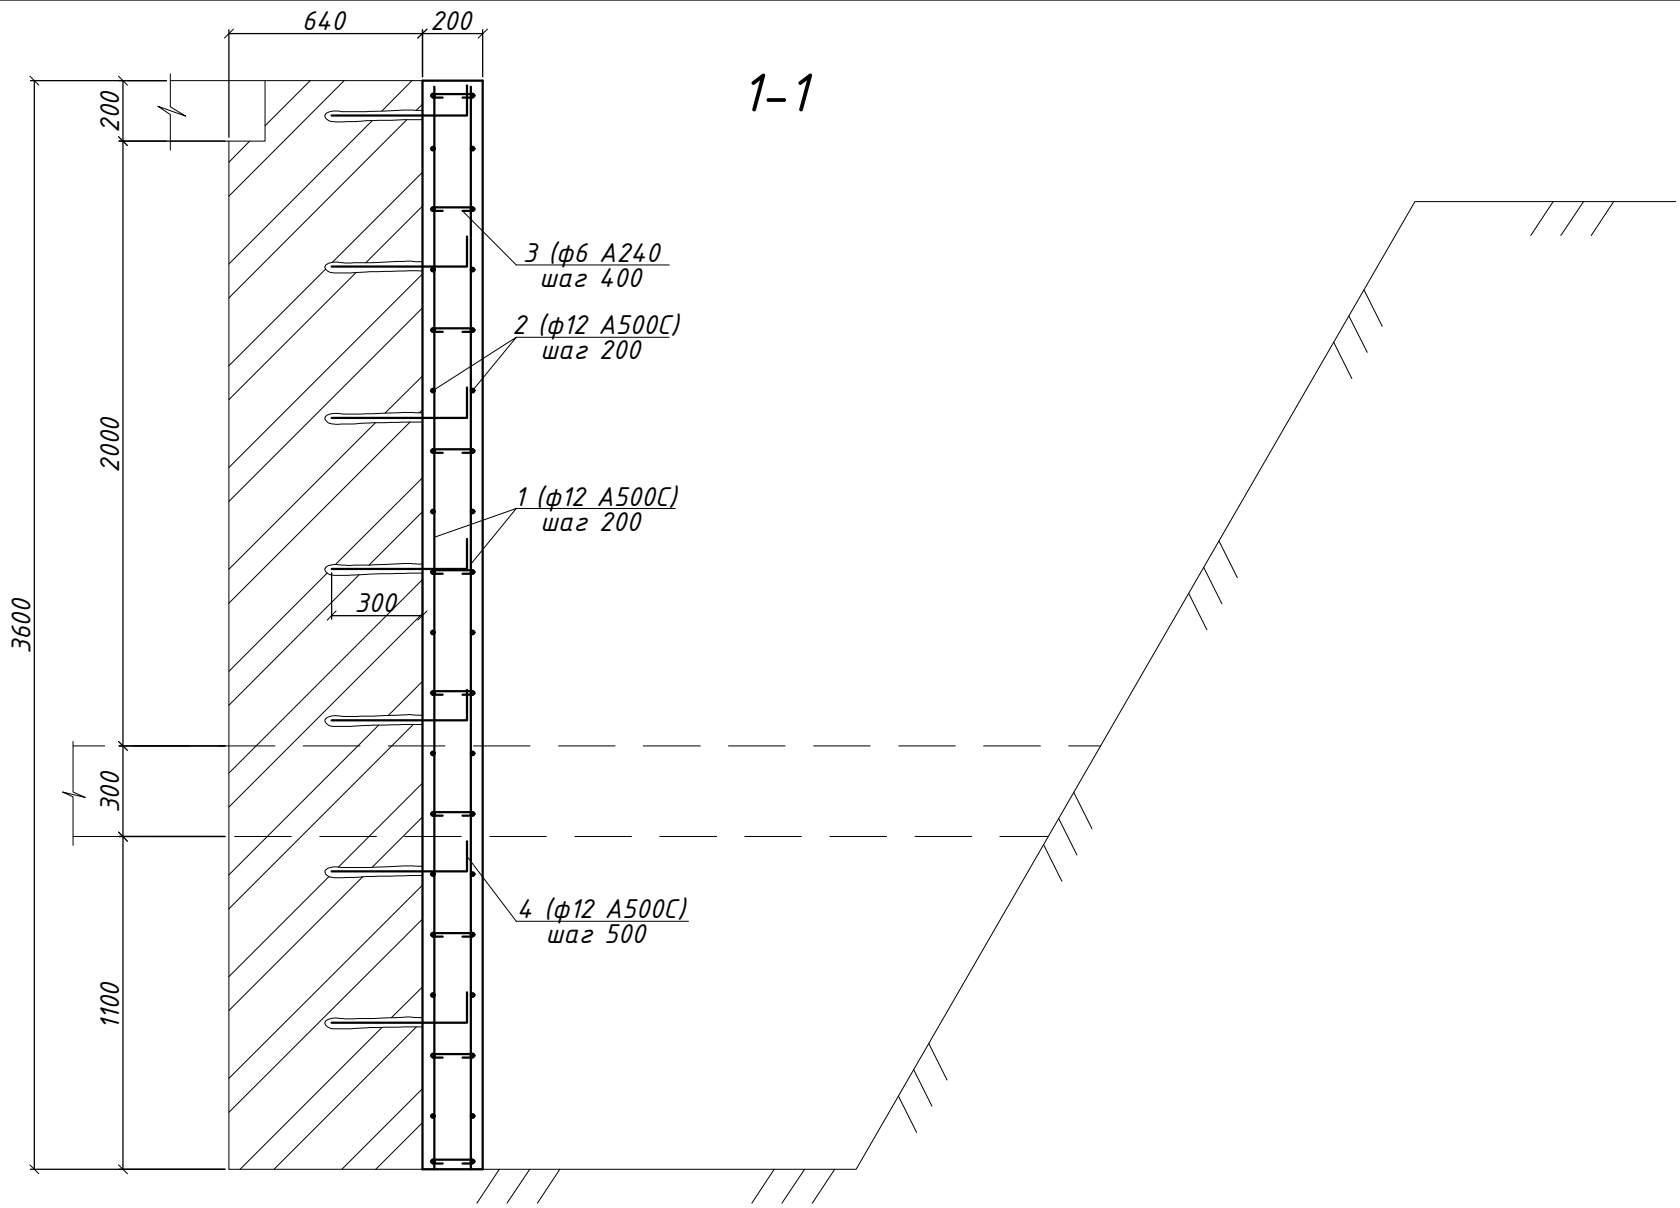

- Перед выполнением работ зачистить существующий дубовый фундамент от остатков грунтового основания компрессорным оборудованием.
- Элемент (поз. 4) завести в дубовую кладку для объединения каркаса усиления с существующим фундаментом.
- Бетонную смесь нанести послойно, методом торкретирования.
- Обход отверстий подходящих коммуникаций выполнять по месту методом резки арматуры.
- В процессе проведения работ не допускать обводнения основания грунта и существующей дубовой кладки.

Ведомость деталей

Поз.	Эскиз
3	
4	

						16-25/Г-Р-АН		
						Капитальный ремонт объекта "ГБОУ Школа № 429 "Соколиная гора", расположенного по адресу: г.Москва, ул. Соколиной горы 5-я, д.14		
Изм	Кол.уч	Лист	№ док	Подпись	Дата	Конструктивные решения	Стадия	Лист
Разраб.	Соловьева	06.2026					Р	
Проверил	Дидык	06.2026				Схема усиления ленточного фундамента		
Н. контр.	Гударева	06.2026						
ГИП	Маркова	06.2026						