
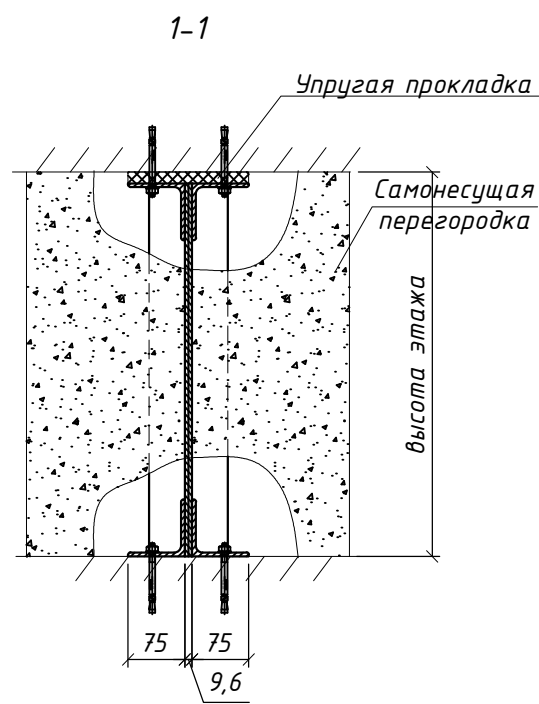
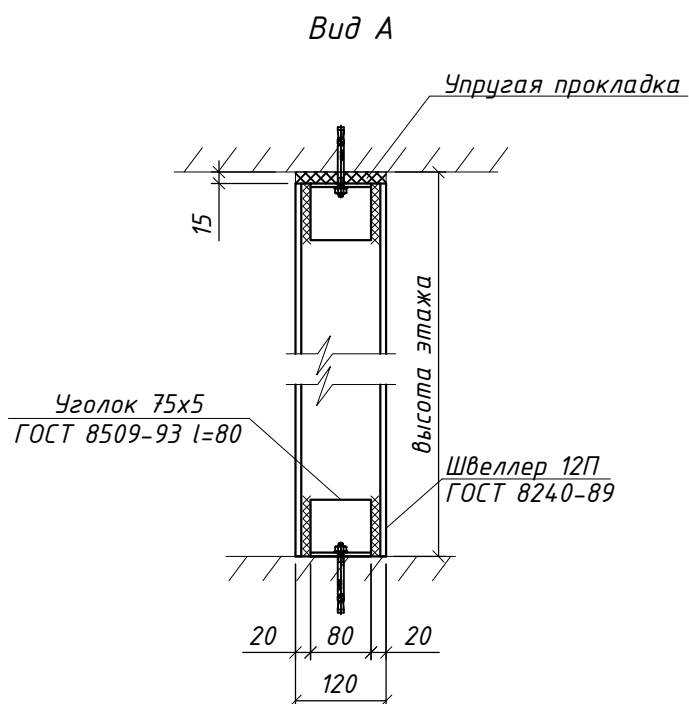


Узел раскрепления перегородок толщиной 100 мм

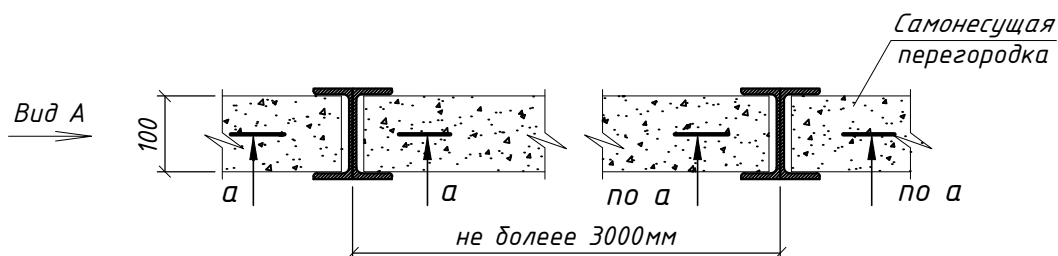

1. Схема раскрепления перегородки выполнена для перегородки толщиной 100мм.
2. Шаг раскрепления принять не более 3000мм. Для перевязанных простенков раскрепление не выполняется.
3. Швеллеры раскрепления свариваются между собой по полке с обеих сторон ручной дуговой сваркой по ГОСТ 5264-80*.
4. Катет сварного шва принять 5мм.
5. Крепление элемента раскрепления вести к перекрытию с помощью распорных клиновых анкеров М8х75. Анкер устанавливать согласно рекомендаций с контролем затяжки.
6. Сверху между перекрытием и элементом раскрепления установить упругую прокладку не менее 15 мм.

СОГЛАСОВАНО

ВЗАМ. ИНВ. N

ПОДПИСЬ И ДАТА

ИНВ. N ПОДЛ.

16-25/Г-Р-АН

Капитальный ремонт объекта "ГБОУ Школа № 429 "Соколиная гора", расположенного по адресу: г.Москва, ул. Соколиной горы 5-я, д.14

Изм	Кол.уч	Лист	№ док	Подпись	Дата
Разраб.		Соловьева			06.2026
Проверил		Дидык			06.2026
Н. контр.		Гударева			06.2026
ГИП		Маркова			06.2026

Конструктивные решения

Узел раскрепления перегородок
толщиной 100 мм

Стадия	Лист	Листов
Р		

