



АЗУРИТ

ООО ПСК «Азурит»

ИНН: 7722762829

Рег. № члена СРО

№ П-163-007722762829-0240

от 23.04.2019г. СРО АП «АПП»

Тел: 8 (495) 724-53-47

e-mail: info@psk-azurit.ru

Экз. №

Заказчик: "АНО «ОЭК Стройтрест»"

**Капитальный ремонт общеобразовательного учреждения
(ГБОУ «Школа № 429»), расположенного по адресу: г. Москва,
5-ая ул. Соколиной Горы д.14
1 этап**

РАБОЧАЯ ДОКУМЕНТАЦИЯ

Раздел "Конструктивные решения"

Элементы компоновки спортивного зала

16-25//Г-Р – КР4

Изм.	№ док.	Подп.	Дата



АЗУРИТ

ООО ПСК «Азурит»

ИНН: 7722762829

Рег. № члена СРО

№ П-163-007722762829-0240

от 23.04.2019г. СРО АП «АПП»

Тел: 8 (495) 724-53-47

e-mail: info@psk-azurit.ru

Экз. №

Заказчик: "АНО «ОЭК Стройтрест»"

**Капитальный ремонт общеобразовательного учреждения
(ГБОУ «Школа № 429»), расположенного по адресу: г. Москва,
5-ая ул. Соколиной Горы д.14
1 этап**

РАБОЧАЯ ДОКУМЕНТАЦИЯ

Раздел "Конструктивные решения"

Элементы компоновки спортивного зала

16-25//Г-Р – КР4

Том

Технический директор –
главный инженер

Главный инженер проекта



Н.А. Губарев

Н.В. Маркова

Изм.	№ док.	Подп.	Дата

СОГЛАСОВАНО

Ведомость рабочих чертежей основного комплекта

Лист	Наименование	Примечание
1	Общие данные	
2	Схема расположения конструкций крепления рам и щитов с кольцами спортзала	
3	Стойка тренировочного баскетбольного щита Ст1	
4	Стойка тренировочного баскетбольного щита Ст2	

Общие указания

Комплект чертежей разработан для монтажа элементов компоновки спортивного зала объекта “ГБОУ Школа № 429 “Соколиная гора”, расположенного по адресу: г. Москва, ул. Соколиной горы 5-я, д.14 в рамках программы капитального ремонта.

- В качестве элементов крепления используется стальные профили:
- лист стальной толщиной 6 и 10 мм по ГОСТ 19903-84*
 - труба стальная квадратного сечения 100х5 по ГОСТ 30245-2012
 - анкеры распорные клиновые М12х100 (типа Hilti HSA или аналогичные);


1. Монтаж элементов к местам установки вести после полной сборки элементов.
 2. Монтаж прочего оборудования спортзала вести с помощью распорных анкеров М12х100 в кирпичные стены.
 3. Комплект полного оборудования спортивного зала см. раздел ТХ.
- Стальные конструкции подлежат защите от коррозии грунтовкой ГФ 021 ГОСТ 25129-2020 и краской ПФ-115 по ГОСТ 6465-76. Цвет окрашиваемых поверхностей согласовать с заказчиком.
 - Производство работ выполнять в соответствии с:
 - разработанным проектом производства работ ППР, согласованного с проектной организацией;
 - СП 48.13330.2019 “Организация строительства”;
 - СП 70.13330.2012 “Несущие и ограждающие конструкции”;
 - СП 28.13330.2017 “Защита строительных конструкций от коррозии”;
 - СП 63.13330.2018 “Бетонные и железобетонные конструкции”;
 - СНиП 12-03-2001 часть 1 “Общие требования”;
 - СНиП 12-04-2002 часть 2 “Строительное производство”;
 - СП 49.13330.2010 “Безопасность труда в строительстве. Часть 2. Строительное производство”
 - действующих правил техники безопасности по каждому виду работ.

16-25/Г-Р-КР4

Капитальный ремонт объекта “ГБОУ Школа № 429 “Соколиная гора”, расположенного по адресу: г.Москва, ул. Соколиной горы 5-я, д.14

						16-25/Г-Р-КР4			
						Капитальный ремонт объекта "ГБОУ Школа № 429 "Соколиная гора", расположенного по адресу: г.Москва, ул. Соколиной горы 5-я, д.14			
Изм	Кол.уч	Лист	№ док	Подпись	Дата	Конструктивные решения	Стадия	Лист	Листов
Разраб.		Соловьева			07.2026		Р	1	
Проверил		Дидык			07.2026				
						Общие данные			
Н. контр.		Губарева			07.2026				
ГИП		Маркова			07.2026				

Схема расположения конструкций спортивного зала на первом этаже

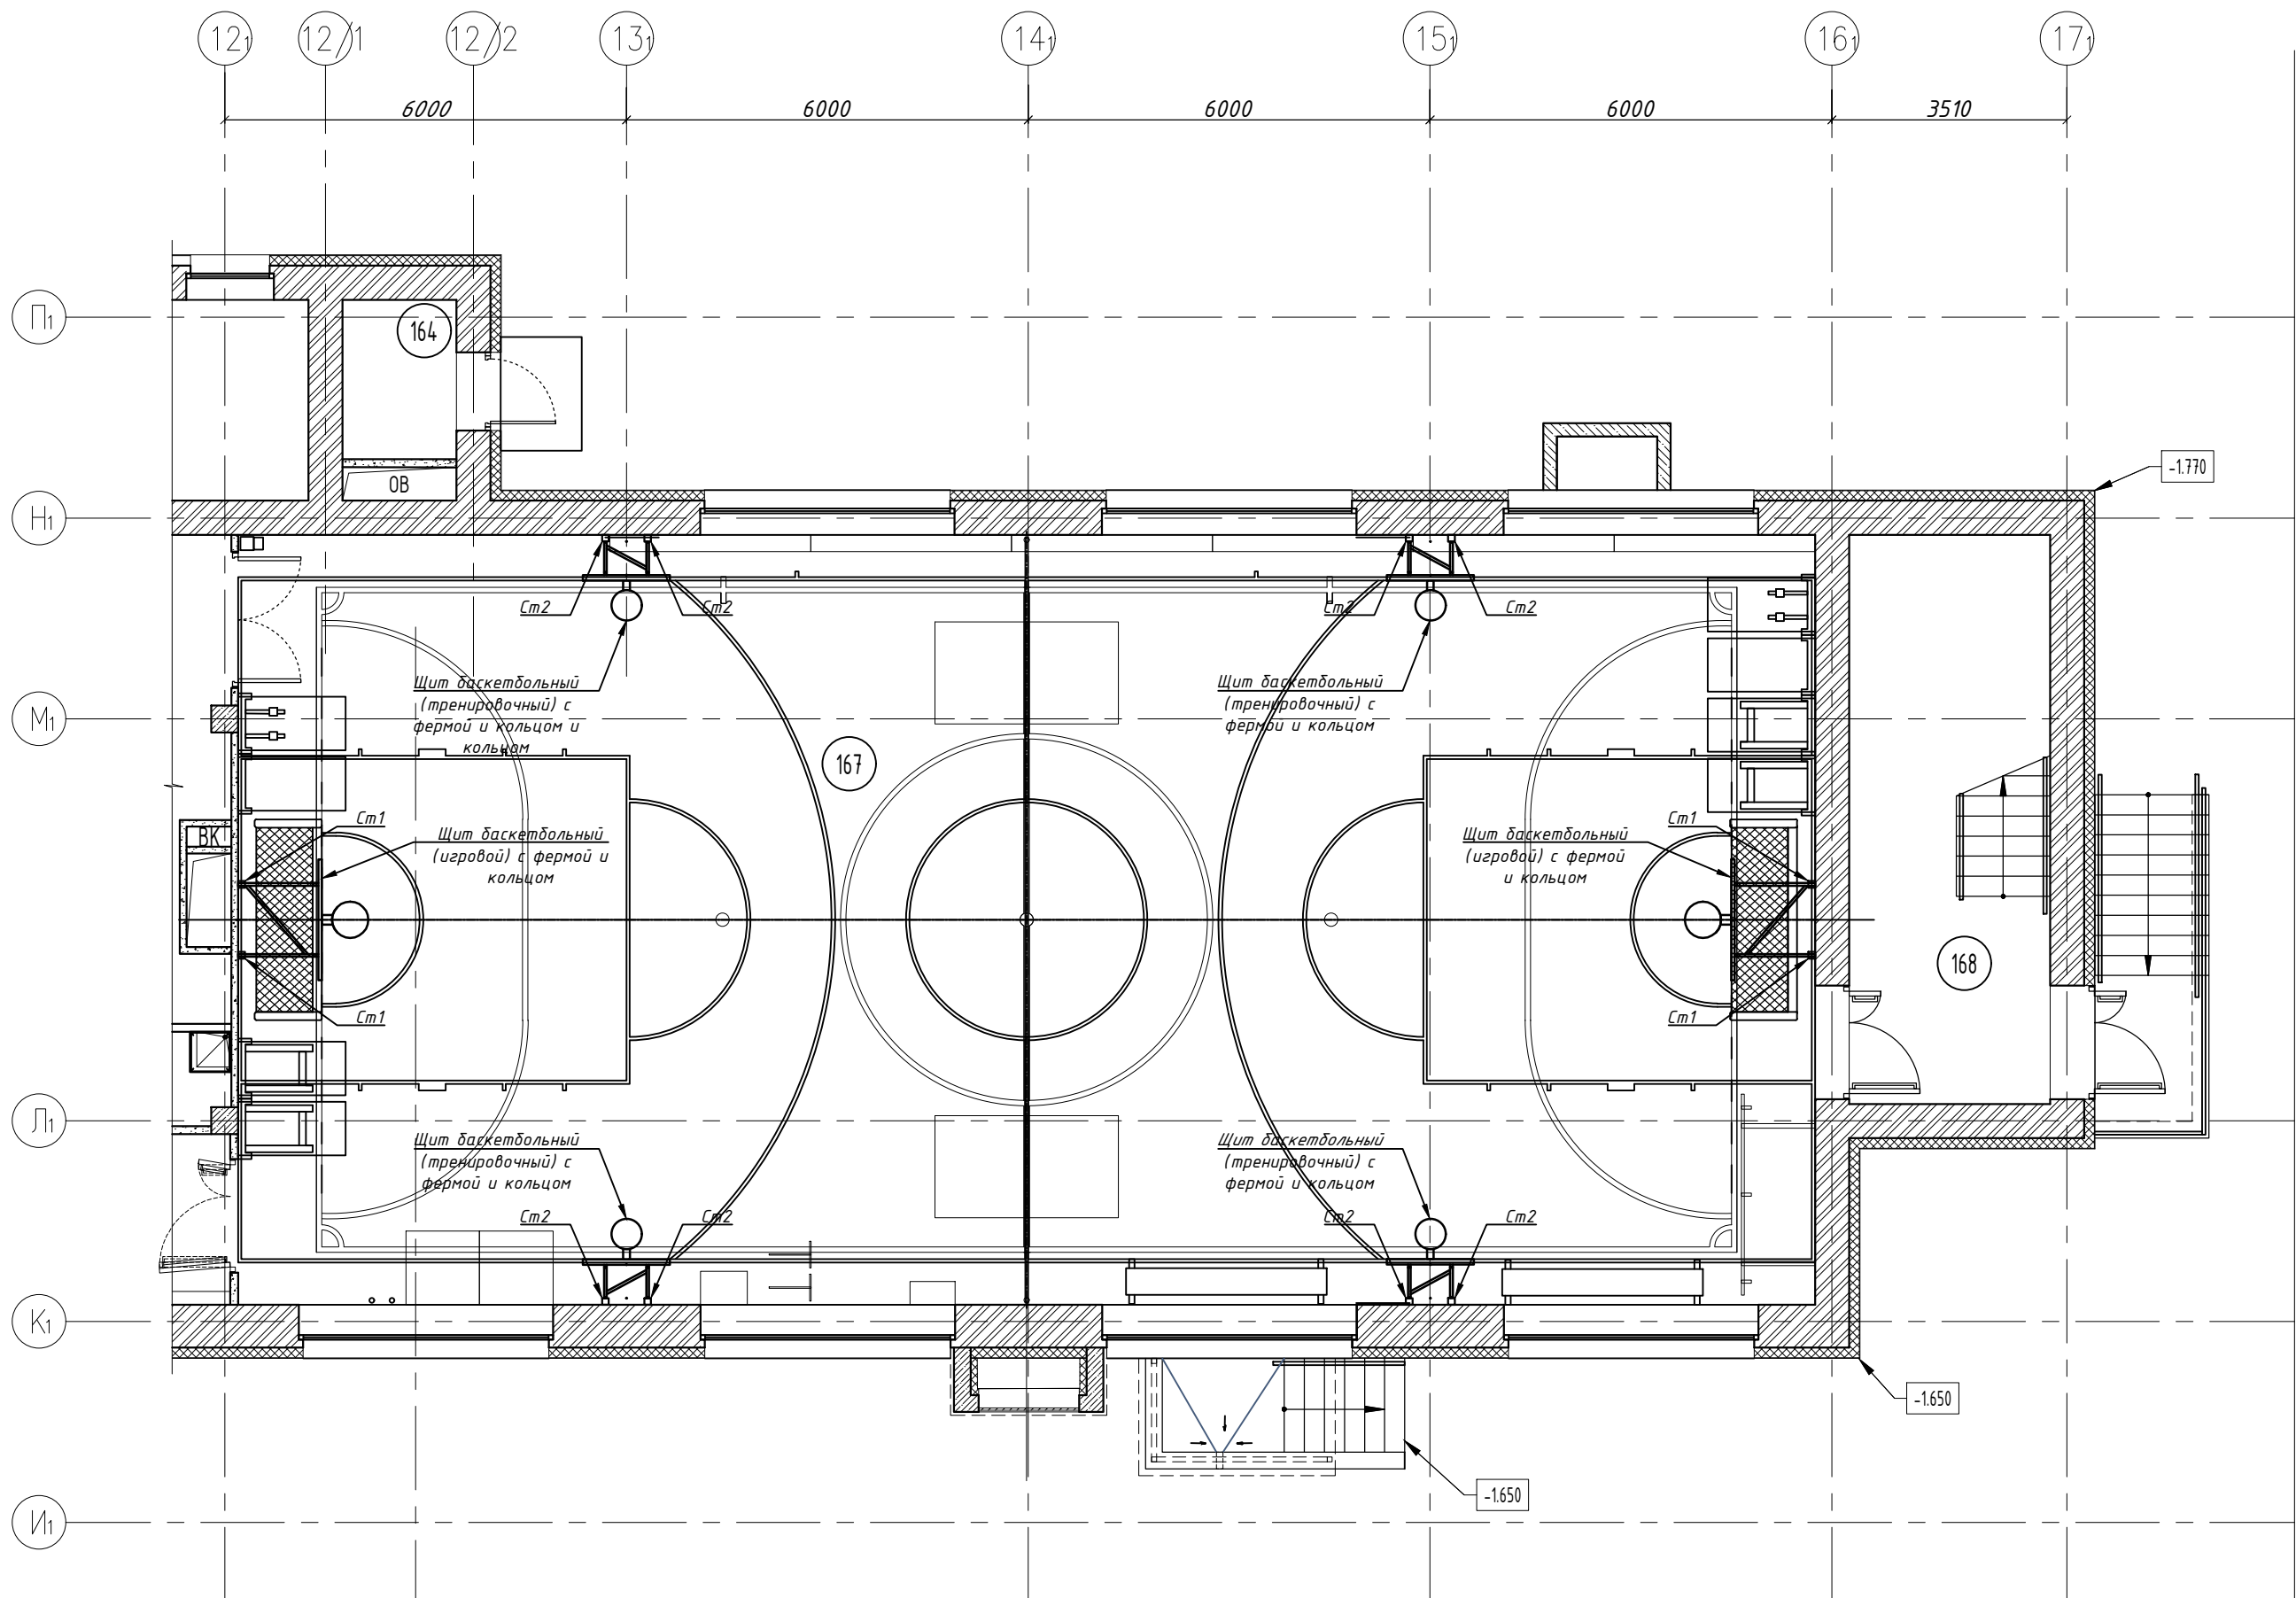





Спецификация к схема расположения стоек баскетбольных щитов

Поз.	Обозначение	Наименование	Кол. шт.	Масса ед. кг.	Прим.
Ст1		Стойка игрового баск. щита Ст1	4		
Ст2		Стойка тренировочного баск. щита Ст2	8		



СОГЛАСОВАНО					
ИНВ. N ПОДЛ.	ПОДПИСЬ И ДАТА		ВЗМ. ИНВ. N		

						16-25/Г-Р-КР4			
						Капитальный ремонт объекта "ГБОУ Школа № 429 "Соколиная гора", расположенного по адресу: г.Москва, ул. Соколиной горы 5-я, д.14			
Изм	Кол.уч	Лист	№ док	Подпись	Дата	Конструктивные решения	Стадия	Лист	Листов
Разраб.	Соловьева		07.2026				Р	2	
Проверил	Дидык		07.2026						
						Схема расположения конструкций крепления рам и щитов с кольцами спортзала			
Н. контр.	Гударева		07.2026						
ГИП	Маркова		07.2026						

Стойка тренировочного баскетбольного щита Ст2

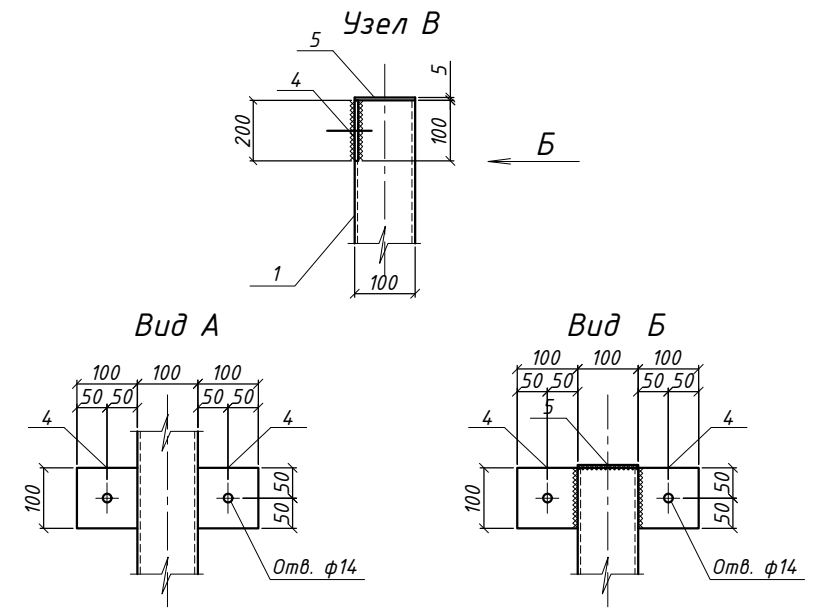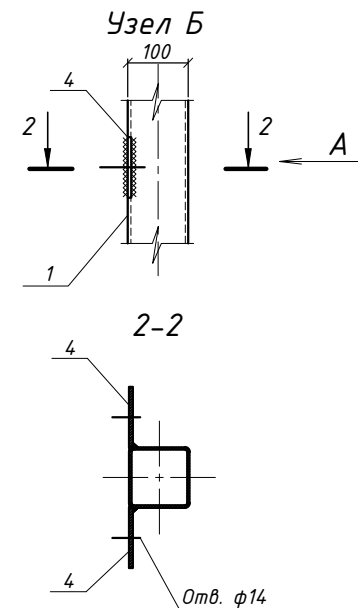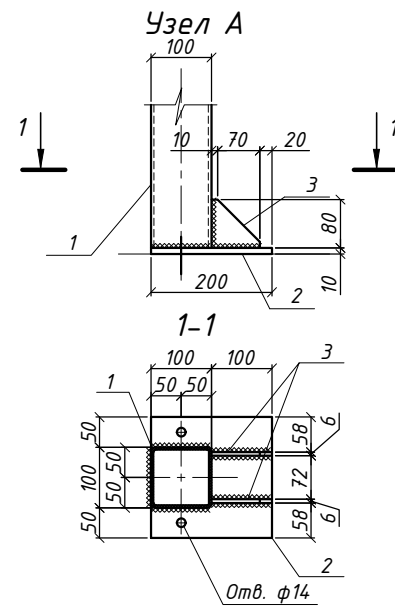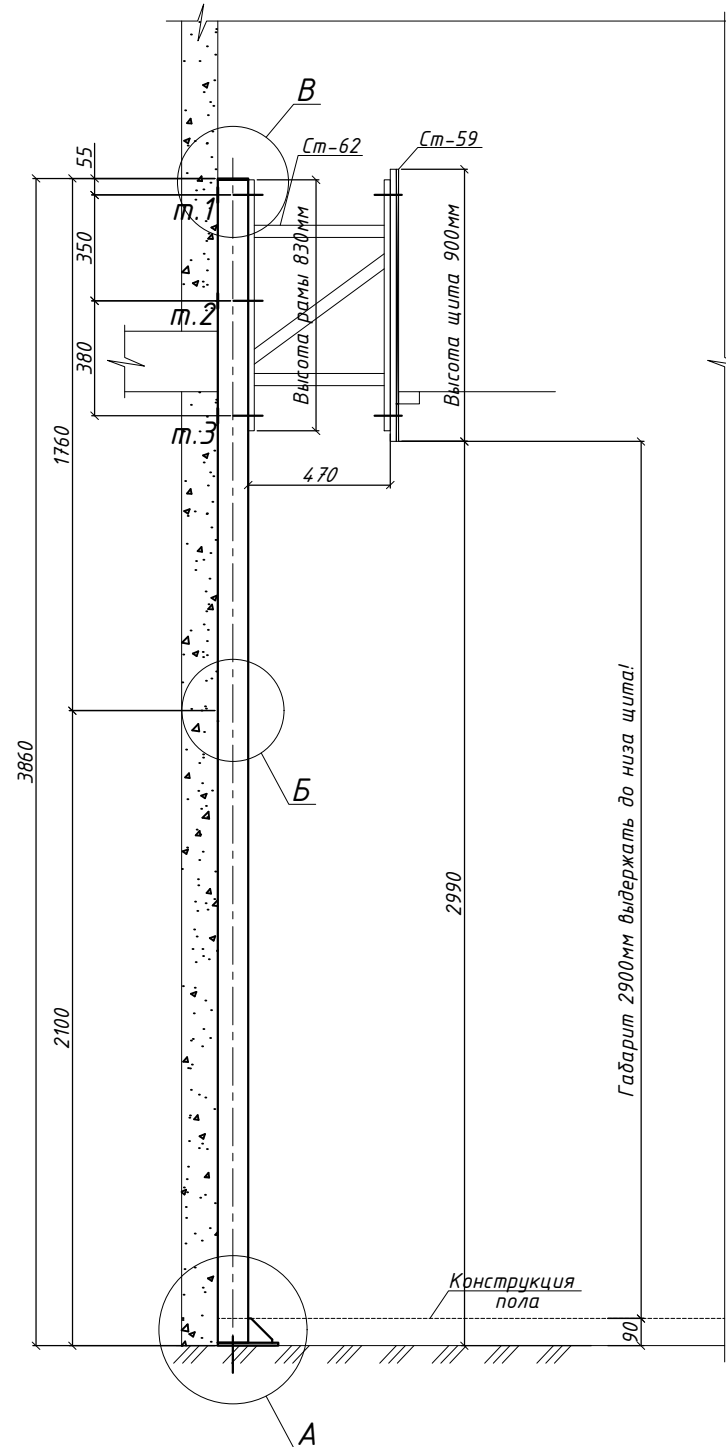

m.1, m.2, m.3

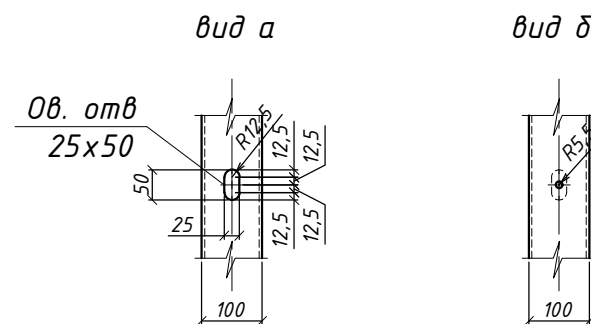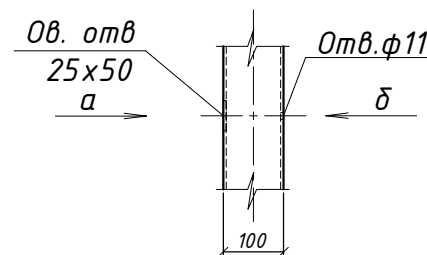

Спецификация элементов стойки тренировочного баскетбольного щита

Поз.	Обозначение	Наименование	Кол. шт.	Масса ед. кг.	Прим.
1		Труба $\frac{100 \times 5 \text{ ГОСТ } 30245-2012}{\text{С245 ГОСТ } 27772-88} L=3845$	1	55.41	55.41
2		Лист $\frac{10 \times 200 \text{ ГОСТ } 19903-2006}{\text{С245 ГОСТ } 27772-88} L=200$	1	3.14	3.14
3		Лист $\frac{6 \times 80 \text{ ГОСТ } 19903-2006}{\text{С245 ГОСТ } 27772-88} L=80$	2	0.31	0.62
4		Лист $\frac{6 \times 100 \text{ ГОСТ } 19903-2006}{\text{С245 ГОСТ } 27772-88} L=100$	4	0.48	1.92
5		Лист $\frac{6 \times 100 \text{ ГОСТ } 19903-2006}{\text{С245 ГОСТ } 27772-88} L=100$	1		
		Анкер M12x100	6		

1. Рассматривать совместно с л. 2.
2. Спецификацию элементов стоек см. л. 2.
3. Сварку выполнять по ГОСТ 5264-80*, катет сварного шва принять 6мм.
4. Стальные конструкции подлежат защите от коррозии грунтовкой ГФ 021, окраске краской типа ПФ-115 или аналогичной, цвет согласовать с заказчиком.,
5. Со стороны стены выполнить заранее 3 отвальных отверстия (м.1, м.2, м.3) размерами 50х25мм в стойке на указанных расстояниях для возможности монтажа фермы к стойке.
6. Крепление к перекрытию и стене выполнять с помощью механических распорных анкеров М12х100 в соответствии с рекомендациями производителя анкерного крепежа.

						16-25/Г-Р-КР4			
						Капитальный ремонт объекта "ГБОУ Школа № 429 "Соколиная гора", расположенного по адресу: г.Москва, ул. Соколиной горы 5-я, д.14			
Изм	Кол.уч	Лист	№ док	Подпись	Дата	Конструктивные решения	Стадия	Лист	Листов
Разраб.		Соловьева			07.2026		Р	4	
Проверил		Дидык			07.2026				
Н. контр.		Гударева			07.2026	Стойка тренировочного баскетбольного щита Ст2	 АЗУРИТ		
ГИП		Маркова			07.2026				