




План ввода силового кабеля в подвале здания

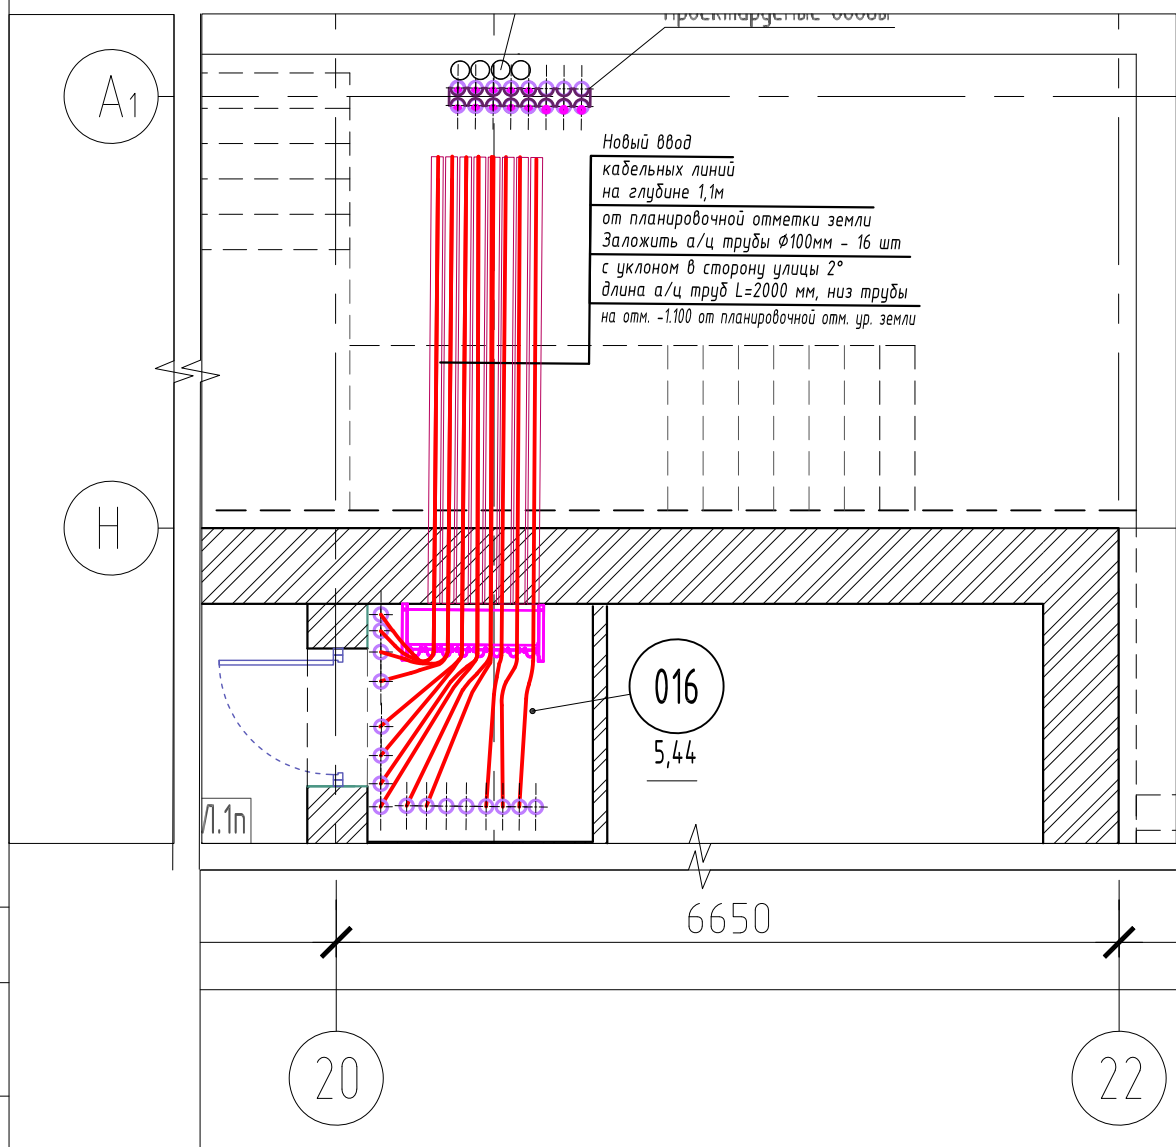

Разрез 1-1

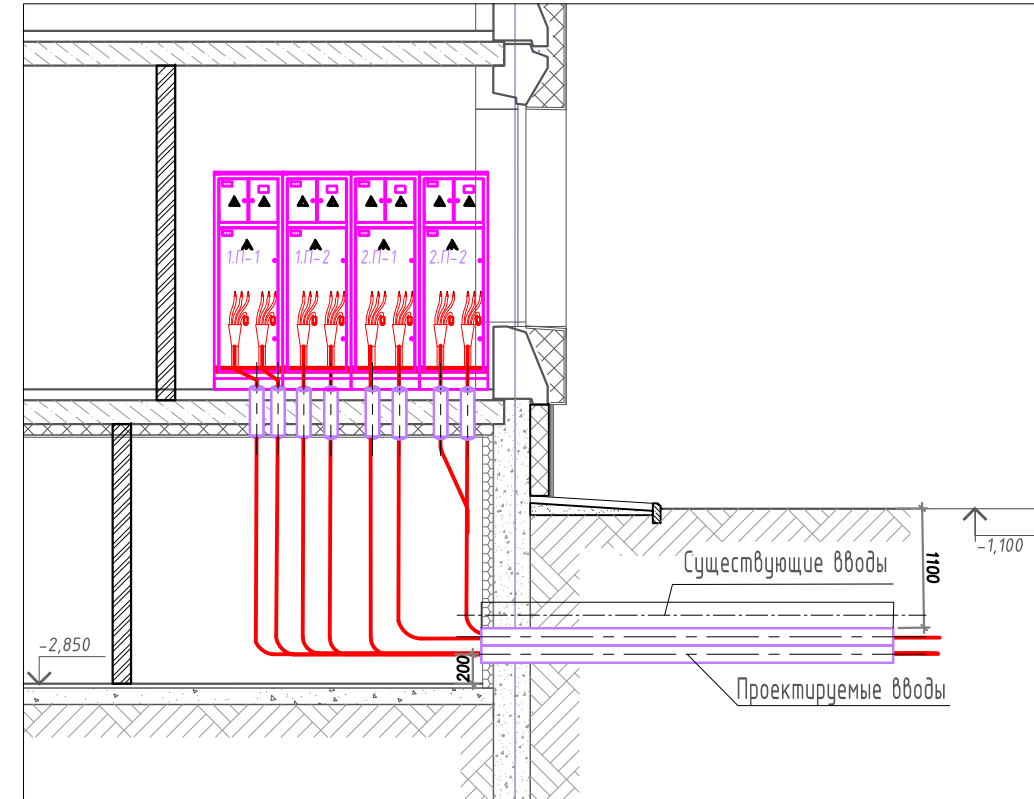

План расположения силовых щитов ВРУ

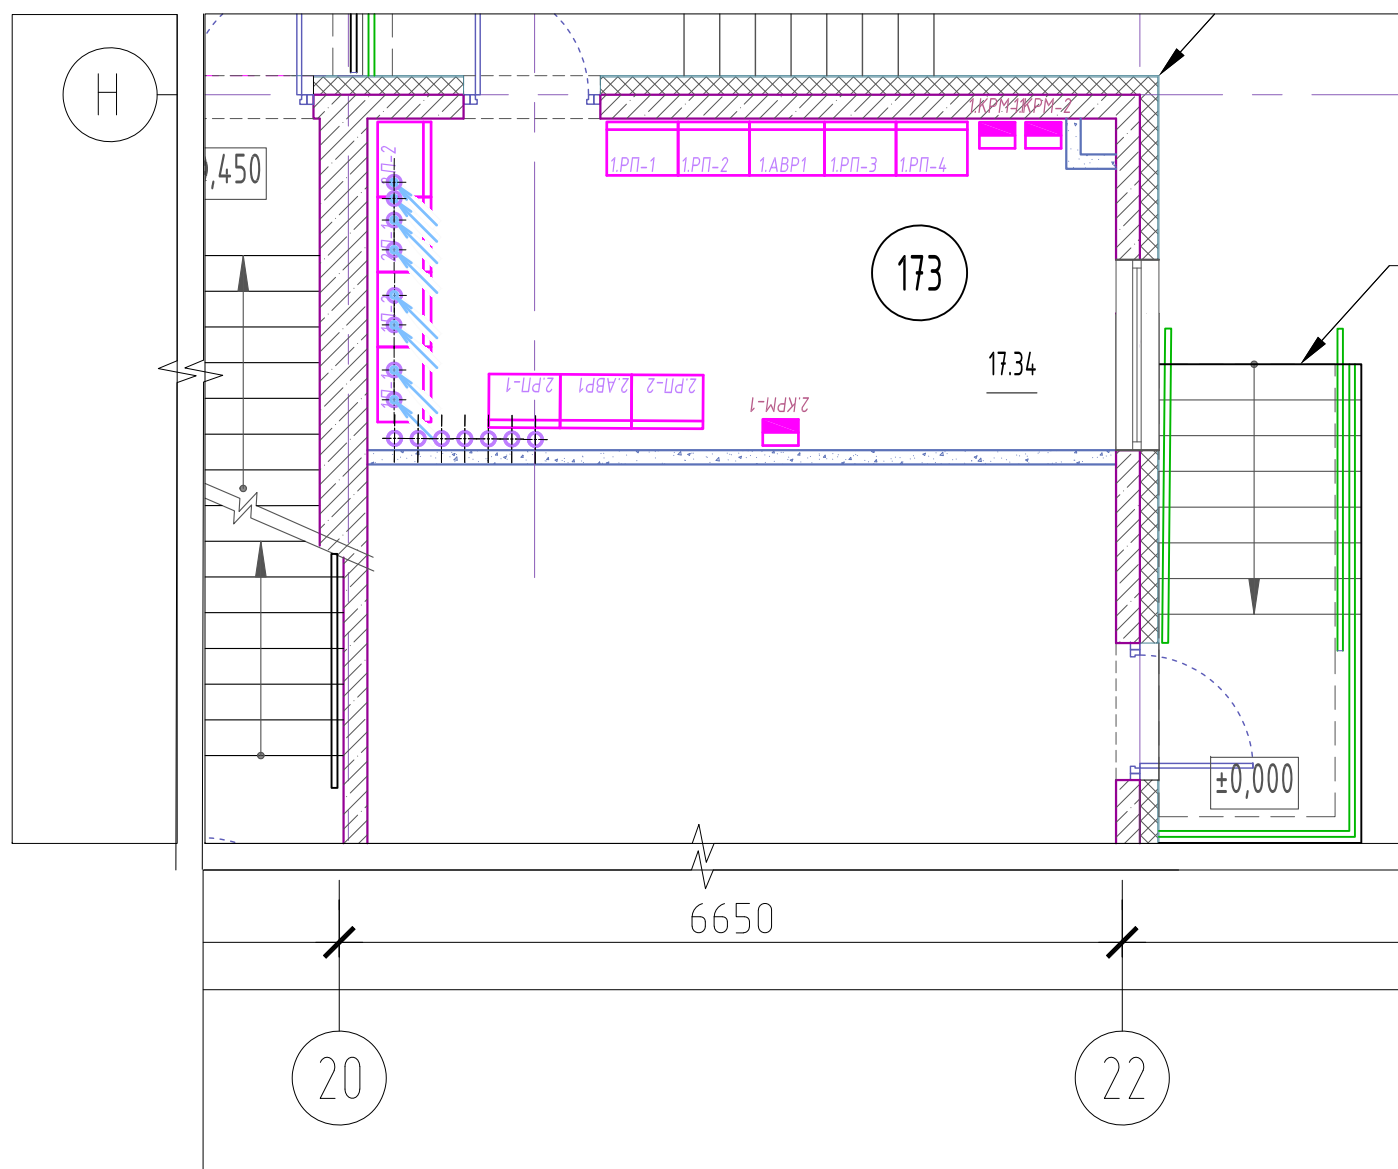

Согласовано				
Взам. инв. №				
Подп. и дата				
Инв. № подл.				

						Капитальный ремонт объекта "ГБОУ Школа № 429 "Соколиная гора", расположенного по адресу: г.Москва, ул. Соколиной горы 5-я, д.14			
Изм.	Кол.уч.	Лист	№ док.	Подп.	Дата	Система электроснабжения	Стадия	Лист	Листов
Разработал							П		
ГИП									
Н. Контроль						План ввода силового кабеля в здание			
Руководитель									