



# АЗУРИТ

ООО ПСК «Азурит»  
ИНН: 7722762829  
Рег. № члена СРО  
№ П-163-007722762829-0240  
от 23.04.2019г. СРО АП «АПП»

Тел: 8 (495) 724-53-47  
e-mail: info@psk-azurit.ru

Экз. №

Заказчик: "АНО «ОЭК Стройтрест»"

**«Капитальный ремонт общеобразовательного учреждения  
(ГБОУ «Школа № 429»), расположенного по адресу: г. Москва, 5-ая ул.  
Соколиной Горы д.14»**

## *РАБОЧАЯ ДОКУМЕНТАЦИЯ*

**Раздел "Внутренние системы водоснабжения и канализации"**

**1 этап**

**16-25/Г-Р – ВК**

| Изм. | № док. | Подп. | Дата |
|------|--------|-------|------|
|      |        |       |      |
|      |        |       |      |
|      |        |       |      |



# АЗУРИТ

ООО ПСК «Азурит»  
ИНН: 7722762829  
Рег. № члена СРО  
№ П-163-007722762829-0240  
от 23.04.2019г. СРО АП «АПП»

Тел: 8 (495) 724-53-47  
e-mail: info@psk-azurit.ru

Экз. №

Заказчик: "АНО «ОЭК Стройтрест»"

**«Капитальный ремонт общеобразовательного учреждения  
(ГБОУ «Школа № 429»), расположенного по адресу: г. Москва, 5-ая ул.  
Соколиной Горы д.14»**

## РАБОЧАЯ ДОКУМЕНТАЦИЯ

**Раздел "Внутренние системы водоснабжения и канализации"**

**1 этап**

**16-25/Г-Р – ВК**

Технический директор –  
главный инженер


Главный инженер проекта



Н.А. Губарев

Г.Н. Нименов

| Изм. | № док. | Подп. | Дата |
|------|--------|-------|------|
|      |        |       |      |
|      |        |       |      |
|      |        |       |      |

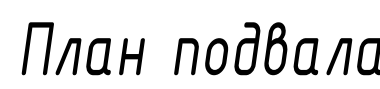

## Экспликация помещений подвала

| Номер помещения | Наименование                                                | Площадь, м2 | Кат. помещ. |
|-----------------|-------------------------------------------------------------|-------------|-------------|
| 001             | ИТП                                                         | 60.07       | Д           |
| 002             | Венткамера с фанкамерой                                     | 52.92       | В3          |
| 004             | Водомерный узел и насосная                                  | 4.124       | Д           |
| 005             | Техническое помещение                                       | 28.40       | Д           |
| 006             | Венткамера                                                  | 137.76      | В3          |
| 006.1           | Венткамера систем приточной противодымной вентиляции        | 23.13       | Д           |
| 007             | Венткамера                                                  | 138.94      | В3          |
| 008             | Техническое помещение для прокладки инженерных коммуникаций | 974.84      | В3          |
| 009             | Венткамера                                                  | 64.68       | В3          |
| 010             | Техническое помещение                                       | 64.96       | Д           |
| 011             | Защитное помещение гражданской обороны                      | 249.34      |             |
| 012             | Коридор                                                     | 50.95       |             |
| 013             | Санузел женский                                             | 10.88       |             |
| 014             | Санузел мужской                                             | 4.45        |             |
| 015             | Коридор                                                     | 50.11       |             |
| 016             | Узел ввода электрических сетей                              | 5.44        | В4          |
| 017             | Коридор                                                     | 39.60       |             |
|                 | Всего                                                       | 1997.7      |             |

### Условные обозначения

- |     |                                                                                   |
|-----|-----------------------------------------------------------------------------------|
| K1  | Канализация бытовая                                                               |
| K1n | Канализация бытовая в конструкции пола                                            |
| K1n | Канализация бытовая подвала                                                       |
| K2  | Водооток                                                                          |
| K3  | Канализация производственная                                                      |
| K3  | Канализация производственная в конструкции пола                                   |
| K4n | Канализация дренажная наружная                                                    |
| K4n | Канализация дренажная от систем вентиляции и кондиционирования в конструкции пола |

|                |           |                |                 |            |      |  |                                     |   |
|----------------|-----------|----------------|-----------------|------------|------|--|-------------------------------------|---|
|                |           |                |                 |            |      |  |                                     | 16-25/ГЛ-ВК   |
|                |           |                |                 |            |      |  |                                     | Капитальный ремонт объекта "БООШ Школа № 429 "Сколияная гора", расположенного по адресу: г.Москва, ул. Сколиной горы 5-я, 0.14 |
| Имя<br>Фамилия | Как зовут | Адрес<br>Улицы | №Экз.<br>Жилища | Подпись    | Дата |  |                                     | Страница Лист Листов   |
|                |           |                |                 | 2020.07.16 |      |  |                                     | Р 2   |
| Н. Контр.      | Воробей   |                |                 | 2020.07.18 |      |  |                                     |  АЗУРИТ                                   |
| Генп.          | Немцов    |                |                 | 2020.07.18 |      |  |                                     |   |
|                |           |                |                 |            |      |  | План подвала с сетями водоснабжения |   |

Условные обозначения:

- Канализация бытовая
- Канализация бытовая в конструкции пола
- Водосток
- Канализация производственная
- Канализация производственная в конструкции пола
- Канализация дренажная малоприя
- Канализация дренажная от систем вентиляции и кондиционирования в конструкции пола
- Канализация дренажная от систем вентиляции и кондиционирования

| Номер помещения | Наименование                                                                           | Площадь, м2 | Кол. единиц |
|-----------------|----------------------------------------------------------------------------------------|-------------|-------------|
| 201             | Лестничная клетка тип И2                                                               | 28,82       |             |
| 202             | Учебные кабинеты (начальная школа)                                                     | 58,78       |             |
| 203             | ПМ                                                                                     | 2,90        | 84          |
| 204             | Санитар для девочек (начальная школа)                                                  | 12,73       |             |
| 205             | Учебные кабинеты (начальная школа)                                                     | 58,68       |             |
| 206             | Учебные кабинеты (начальная школа)                                                     | 58,54       |             |
| 207             | Учебные кабинеты (начальная школа)                                                     | 60,45       |             |
| 208             | Санитар для персонала                                                                  | 2,03        |             |
| 209             | Санитар для мальчиков (начальная школа)                                                | 12,44       |             |
| 210             | Лестничная клетка И1                                                                   | 23,95       |             |
| 211             | Учебные кабинеты (начальная школа)                                                     | 56,51       |             |
| 212             | Кабинет иностранного языка (начальная школа)                                           | 50,17       |             |
| 213             | Лабораторно-исследовательский комплекс для изучения естественных наук                  | 91,02       | 83          |
| 214             | Санитар для девочек (начальная школа)                                                  | 23,25       |             |
| 215             | Тамбур                                                                                 | 5,46        |             |
| 216             | Кабинет для индивидуальных занятий с малой группой                                     | 32,35       |             |
| 217             | Коридор с рекреацией (начальная школа)                                                 | 245,43      |             |
| 218             | Коридор                                                                                | 35,20       |             |
| 219             | Кабинет для индивидуальных занятий с малой группой                                     | 23,78       |             |
| 220             | Помещение фойе                                                                         | 8,15        | 84          |
| 221             | Санитар для мальчиков (начальная школа)                                                | 21,45       |             |
| 222             | Кабинет для индивидуальных занятий, в т.ч. с учителями-логологами                      | 18,91       |             |
| 223             | Кабинет для индивидуальных занятий, в т.ч. с коррекционными педагогами                 | 19,22       |             |
| 224             | Учебные кабинеты (начальная школа)                                                     | 54,17       |             |
| 225             | Классовая комната (начальная школа)                                                    | 15,75       | 83          |
| 226             | Порожковая лестница                                                                    | 54,82       | 83          |
| 226.1           | Кабинет иностранного языка (начальная школа)                                           | 34,58       |             |
| 227             | Мультифункциональное пространство с функцией актового зала (с труппой в учебной школе) | 272,39      |             |
| 228             | Коридор                                                                                | 10,72       | 83          |
| 229             | Лестничная клетка И0                                                                   | 21,90       |             |
| 230.1           | Тамбур                                                                                 | 4,98        |             |
| 230             | Тех. помещение                                                                         | 3,33        | 84          |
| 231             | Артистический                                                                          | 14,65       |             |
| 232             | Классовая комната                                                                      | 16,75       | 83          |
| 233             | Классовая кабинета материальной технологии                                             | 22,55       | 83          |
| 234             | Кабинет материальной технологии тип 2                                                  | 36,85       | 83          |
| 235             | Кабинет с рабочим пространством для учителей тип 1 (начальная школа)                   | 44,43       |             |
| 236             | Кабинет материальной технологии тип 1                                                  | 102,78      | 83          |
| 237             | ПМ                                                                                     | 3,24        | 84          |
| 238             | Санитар для персонала                                                                  | 2,65        |             |
| 239             | Санитар для мальчиков (основная и старшая школа)                                       | 20,93       |             |
| 240             | Санитар для девочек с комнатой личной гигиены (основная и старшая школа)               | 25,85       |             |
| 241             | Лестничная клетка И0                                                                   | 21,00       |             |
| 243             | Коридор с рекреацией (основная и старшая школа)                                        | 268,00      |             |
| 244             | Коридор                                                                                | 78,72       |             |
| 245             | Коридор                                                                                | 77,66       |             |
| 246             | Административный кабинет                                                               | 18,87       |             |
| Всего           |                                                                                        | 3264,3      |             |

Условные обозначения:

- |      |                                                                                   |
|------|-----------------------------------------------------------------------------------|
| K1   | Канализация бытовая                                                               |
| K1   | Канализация бытовая в конструкции пола                                            |
| K2   | Водоотток                                                                         |
| K3   | Канализация производственная                                                      |
| K3   | Канализация производственная в конструкции пола                                   |
| K14ч | Канализация фреоновая напорная                                                    |
| K14в | Канализация фреоновая от систем вентиляции и кондиционирования в конструкции пола |
| K14в | Канализация фреоновая от систем вентиляции и кондиционирования                    |


|           |         |        |       |         |            |                                                                                              |   |      |                |
|-----------|---------|--------|-------|---------|------------|----------------------------------------------------------------------------------------------|---|------|----------------|
|           |         |        |       |         |            |                                                                                              |   |      | 16-25/Г - П-ВК |
|           |         |        |       |         |            |                                                                                              | Капитальный ремонт объекта "ТБОУ Школа № 429 "Скопальная горка", расположенного по адресу: г.Москва, ул. Скопальной горы 5-я, 81А |      |                |
| Изм.      | Как у   | Лист   | № док | Полтора | Дата       |                                                                                              |   |      |                |
| Резерв    |         | Шухова |       |         | 2020.07.09 |                                                                                              |   |      |                |
|           |         |        |       |         |            |                                                                                              | Система водоотведения   |      |                |
|           |         |        |       |         |            |                                                                                              | Статус   | Лист | Листов         |
|           |         |        |       |         |            |                                                                                              | P   | 4    |                |
| Н. контр. | Воробей |        |       |         |            |                                                                                              |   |      |                |
| ГИП       | Иванова |        |       |         | 2020.07.09 |                                                                                              |   |      |                |
|           |         |        |       |         |            | План 2 этажа с сетями водоотведения                                                          |   |      |                |
|           |         |        |       |         |            |  АЗУРИТ |   |      |                |

| Номер помещения | Назначение                                                                                     | Площадь м2 | Кол-во помещений |
|-----------------|------------------------------------------------------------------------------------------------|------------|------------------|
| 301             | Летничная клетка Тип И2                                                                        | 28,82      |                  |
| 302             | Кабинет русского языка и литературы                                                            | 38,70      |                  |
| 303             | ПМ                                                                                             | 2,78       | 84               |
| 304             | Салон для девочек (основная и старшая школа)                                                   | 12,44      |                  |
| 305             | Кабинет русского языка и литературы                                                            | 58,68      |                  |
| 306             | Кабинет математики                                                                             | 58,55      |                  |
| 307             | Кабинет математики                                                                             | 60,45      |                  |
| 308             | Салон для персонала                                                                            | 2,75       |                  |
| 309             | Салон для мальчиков (основная и старшая школа)                                                 | 12,44      |                  |
| 310             | Летничная клетка (И)                                                                           | 27,05      |                  |
| 311             | Кабинет географии                                                                              | 55,07      |                  |
| 312             | Информационный учебный кабинет                                                                 | 56,05      |                  |
| 313             | Кабинет для индивидуальных занятий, 8 вкл с педагогом-психологом                               | 16,16      |                  |
| 314             | Учебный кабинет для изучения естественных физика                                               | 11,32      |                  |
| 315             | Лаборатория кабинета физики                                                                    | 6,86       | 83               |
| 316             | Салон для девочек с компьютерной техникой (основная и старшая школа)                           | 23,25      |                  |
| 317             | Подсобное помещение                                                                            | 3,24       | 84               |
| 318             | Кабинет иностранного языка (основная и старшая школа)                                          | 66,38      |                  |
| 320             | Коридор с раздевалкой                                                                          | 244,13     |                  |
| 321             | Кабинет иностранного языка (основная и старшая школа)                                          | 33,78      |                  |
| 322             | Помещение туалета                                                                              | 8,75       | 84               |
| 323             | Салон для мальчиков (основная и старшая школа)                                                 | 21,73      |                  |
| 324             | Лаборатория кабинета биологии                                                                  | 5,93       | 83               |
| 325             | Учебный кабинет для изучения естественных биология с ГДР                                       | 71,78      |                  |
| 326             | Информационный учебный кабинет                                                                 | 53,07      |                  |
| 327             | Кабинет истории тип 1                                                                          | 54,86      |                  |
| 328             | Коридор                                                                                        | 70,72      | 83               |
| 329             | Летничная клетка (И)                                                                           | 10,10      |                  |
| 329.1           | Танбул                                                                                         | 4,70       |                  |
| 330             | Тех. помещения                                                                                 | 3,93       | 84               |
| 331             | Информационное помещение с возможностью организации административного дела (переворотов)       | 105,19     |                  |
| 332             | Раздевальня                                                                                    | 16,45      |                  |
| 333             | Раздевальня                                                                                    | 18,56      |                  |
| 334             | Информационный информационный библиотечный центр с линией для индивидуальных занятий           | 152,15     |                  |
| 335             | Информационный информационный библиотечный центр (проектирование библиотечной и выданных книг) | 41,15      | 83               |
| 336             | ПМ                                                                                             | 4,44       | 84               |
| 337             | Салон для мальчиков (основная и старшая школа)                                                 | 8,84       |                  |
| 338             | Салон для девочек (основная и старшая школа)                                                   | 10,97      |                  |
| 339             | Салон для персонала                                                                            | 5,90       |                  |
| 340             | Летничная клетка (И)                                                                           | 21,00      |                  |
| 341             | Кабинет с рабочим пространством для учителей Тип 1 (основная и старшая школа)                  | 21,92      |                  |
| 342             | Информационное помещение с возможностью организации Мобильности                                | 39,84      | 83               |
| 343             | Помещение туалета                                                                              | 43,49      |                  |
| 344             | Летничная клетка (И)                                                                           | 25,50      |                  |
| 345             | Кабинет с раздевалкой (основная и старшая школа)                                               | 192,00     |                  |
| 346             | Коридор с раздевалкой (основная и старшая школа)                                               | 177,67     |                  |
| 347             | Коридор                                                                                        | 78,72      |                  |
| 348             | Коридор                                                                                        | 77,66      |                  |
| Всего           |                                                                                                | 2244,9     |                  |

Условные обозначения

- |     |                                                                                   |
|-----|-----------------------------------------------------------------------------------|
| K1  | Канализация бытовая                                                               |
| K1  | Канализация бытовая в конструкции пола                                            |
| K2  | Водосток                                                                          |
| K3  | Канализация производственная                                                      |
| K3  | Канализация производственная в конструкции пола                                   |
| K4n | Канализация дренажная наружная                                                    |
| K4d | Канализация дренажная от систем вентиляции и кондиционирования в конструкции пола |
| K4d | Канализация дренажная от систем вентиляции и кондиционирования                    |

| |
|---|
| |
|---|

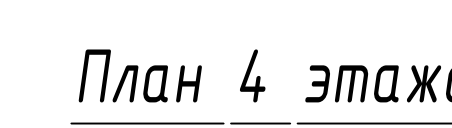

| Номер помещения | Наименование                                                                           | Площадь м2 | Кол. помещений |
|-----------------|----------------------------------------------------------------------------------------|------------|----------------|
| 401             | Лестничная клетка Тип И2                                                               | 28,81      |                |
| 402             | Кабинет русского языка и литературы                                                    | 58,70      |                |
| 403             | ПМ                                                                                     | 17,49      | 84             |
| 404             | Специал. для девочек (основная и старшая школа)                                        | 2,78       |                |
| 405             | Кабинет русского языка и литературы                                                    | 58,68      |                |
| 406             | Кабинет математики                                                                     | 58,54      |                |
| 407             | Кабинет математики                                                                     | 60,45      |                |
| 408             | Специал. для персонала                                                                 | 2,78       |                |
| 409             | Специал. для мальчиков (основная и старшая школа)                                      | 12,49      |                |
| 410             | Лестничная клетка (И)                                                                  | 26,98      |                |
| 411             | Кабинет информационных технологий                                                      | 87,66      |                |
| 412             | Лаборатория при кабинете информационных технологий                                     | 18,84      | 83             |
| 413             | Административный кабинет тип 1 (основная и старшая школа)                              | 16,03      |                |
| 414             | Учебные кабинеты для изучения естественных-химия                                       | 60,95      |                |
| 415             | Лаборатория кабинет химии                                                              | 16,76      | 83             |
| 416             | Специал. для девочек с коррекцией общей гигиены (основная и старшая школа)             | 22,56      |                |
| 417             | Подсобное помещение                                                                    | 7,30       | 84             |
| 418             | Кабинет иностранного языка (основная и старшая школа)                                  | 32,36      |                |
| 419             | Коридор с рекреацией                                                                   | 245,54     |                |
| 420             | Коридор с рекреацией                                                                   | 118,69     |                |
| 421             | Кабинет иностранного языка (основная и старшая школа)                                  | 34,07      |                |
| 422             | Помещение связи                                                                        | 8,02       | 84             |
| 423             | Специал. для мальчиков (основная и старшая школа)                                      | 21,45      |                |
| 424             | Коридор                                                                                | 71,66      |                |
| 425             | Кабинет истории Тип 1                                                                  | 54,17      |                |
| 426             | Кабинет информатики / возможности ведения приоспорожденного персонала на два помещения | 110,69     |                |
| 427             | Лестничная клетка (И)                                                                  | 28,81      |                |
| 428             | Помещение бытового на кровле                                                           | 4,38       |                |
|                 | Всего                                                                                  | 1276,5     |                |

|     |                                                                                |
|-----|--------------------------------------------------------------------------------|
| K1  | Кондиция бытовая                                                               |
| K1  | Кондиция бытовая в конструкции пола                                            |
| K2  | Водоотсек                                                                      |
| K3  | Кондиция производственная                                                      |
| K3  | Кондиция производственная в конструкции пола                                   |
| K4a | Кондиция дренажная котловая                                                    |
| K4a | Кондиция дренажная от систем вентиляции и кондиционирования в конструкции пола |
| K4b | Кондиция дренажная от систем вентиляции и кондиционирования                    |

[illegible]

План технического этажа


Экспликация помещений технического этажа

| Номер помеще-ния | Наименование             | Площадь м2 | Кол. помеще-ний |
|------------------|--------------------------|------------|-----------------|
| 501              | Лестничная клетка Тип П2 | 27.26      |                 |
| 502              | Лестничная клетка Тип П1 | 27.05      |                 |
| 503              | Венткамера 1             | 43.07      | 83              |
| 504              | Венткамера 2             | 44.09      | 83              |
| 505              | Техническое помещение    | 206.11     | 83              |
| 506              | Техническое помещение    | 255.60     | 83              |
| 507              | Техническое помещение    | 169.26     | 83              |
| 508              | Коридор                  | 178.99     |                 |
| 509              | Техническое помещение    | 59.20      | 83              |
| 510              | Техническое помещение    | 58.88      | 83              |
| 511              | Техническое помещение    | 58.24      | 83              |
| 512              | Техническое помещение    | 60.00      | 83              |
| 513              | Техническое помещение    | 107.50     | 83              |
| Всего:           |                          | 1276.25    |                 |

Условные обозначения:

- К1 — Канализация бытовая
- К1 — Канализация бытовая в конструкции пола
- К2 — Водосток
- К3 — Канализация производственная
- К3 — Канализация производственная в конструкции пола
- К1и — Канализация дренажная наружная
- К1и — Канализация дренажная от систем вентиляции и кондиционирования в конструкции пола
- К1и — Канализация дренажная от систем вентиляции и кондиционирования

|           |         |          |        |         |            |   |      |        |
|-----------|---------|----------|--------|---------|------------|---|------|--------|
|           |         |          |        |         |            | 16-25/Г-П-ВК   |      |        |
|           |         |          |        |         |            | Капитальный ремонт объекта "ГБОУ Школа № 429 "Скопальная гора",<br>расположенного по адресу: г.Москва, ул. Скопальной горы 5-я, в.14 |      |        |
| Изм.      | Кат. у. | Лист     | № док. | Подпись | Дата       | Система водоотведения   |      |        |
| Разработ  |         | Шушуба   |        |         | 2023.07.01 | Стандарт   | Лист | Листов |
|           |         |          |        |         |            | Р   | 7    |        |
| И. контр. |         | Воробьев |        |         | 2023.07.01 | План технического этажа с сетями водоотведения                                                                                       |      |        |
| ГМП       |         | Номов    |        |         | 2023.07.01 |  АЗУРИТ                                         |      |        |

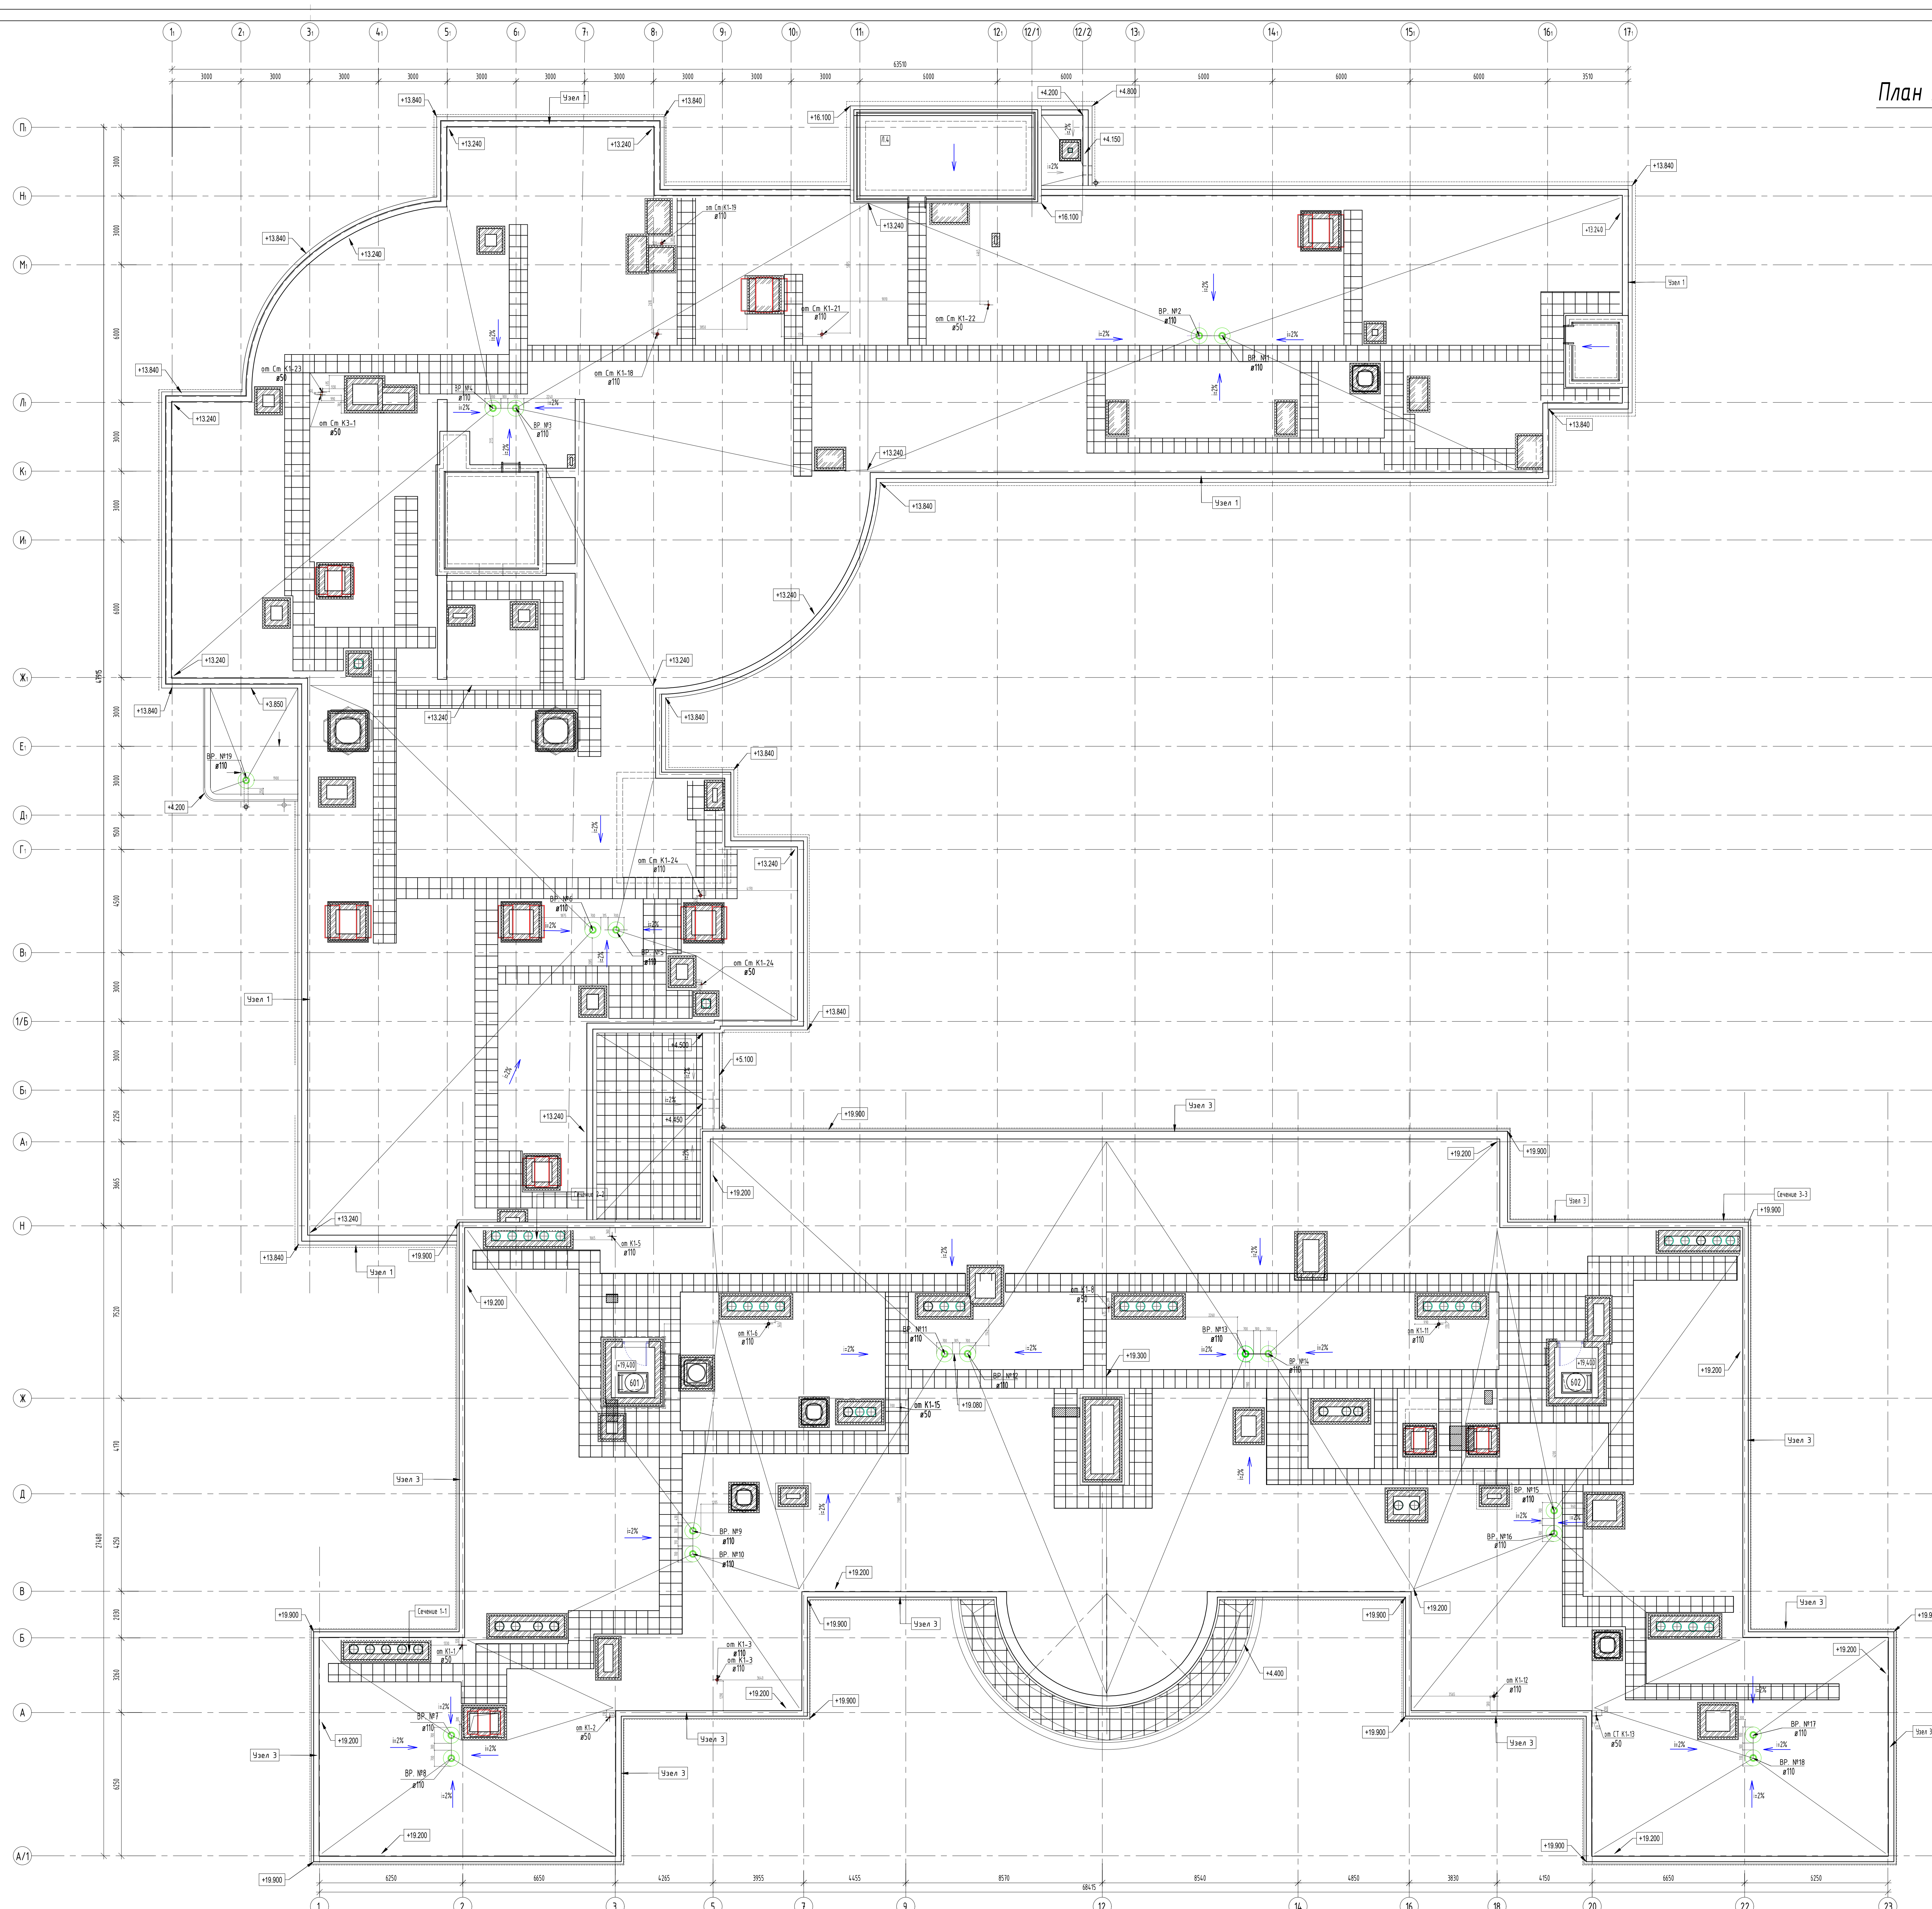

### Экспликация помещений кровли

| Номер помещения | Наименование                | Площадь м2 | Кол. помещений |
|-----------------|-----------------------------|------------|----------------|
| 601             | Помещение выхода на крыльцо | 4.19       |                |
| 602             | Помещение выхода на крыльцо | 5.19       |                |
|                 | Всего                       | 4.2        |                |

УСЛОВНЫЕ ОБОЗНАЧЕНИЯ

- Водосточная воронка с электроподогревом (внутренний организованный водоспуск)
- Выход канализационных стояков на кровлю

Примечание:  
1. Воронка ВР.№19 в 100 переходит с кровли в наружную водосточную систему.

|  |  |  |  |  |  |
|--|--|--|--|--|--|
|  |  |  |  |  |  |
|  |  |  |  |  |  |
06-25/(Г-Л)-ВХ

Капитальный ремонт объекта "ТБОУ Школа № 429 "Скопальная гора", расположенного по адресу: г.Москва, ул. Скопальной горы 5-я, д.14.

| Инв.<br>Разреш. | Код гр. | Лист<br>Широта | №'ов | Подпись | Дата       | Система водоотведения              |      |        |
|-----------------|---------|----------------|------|---------|------------|------------------------------------|------|--------|
|                 |         |                |      |         |            | Статус                             | Лист | Листов |
|                 |         |                |      |         |            | P                                  | 8    |        |
| N комп.         |         | Воробей        |      |         | 2020.07.06 | План кровли с сетями водоотведения |      |        |




**AZURIT**

Согласовано

Взам. инд. Н

Подп. и дата

Инв. N подл.

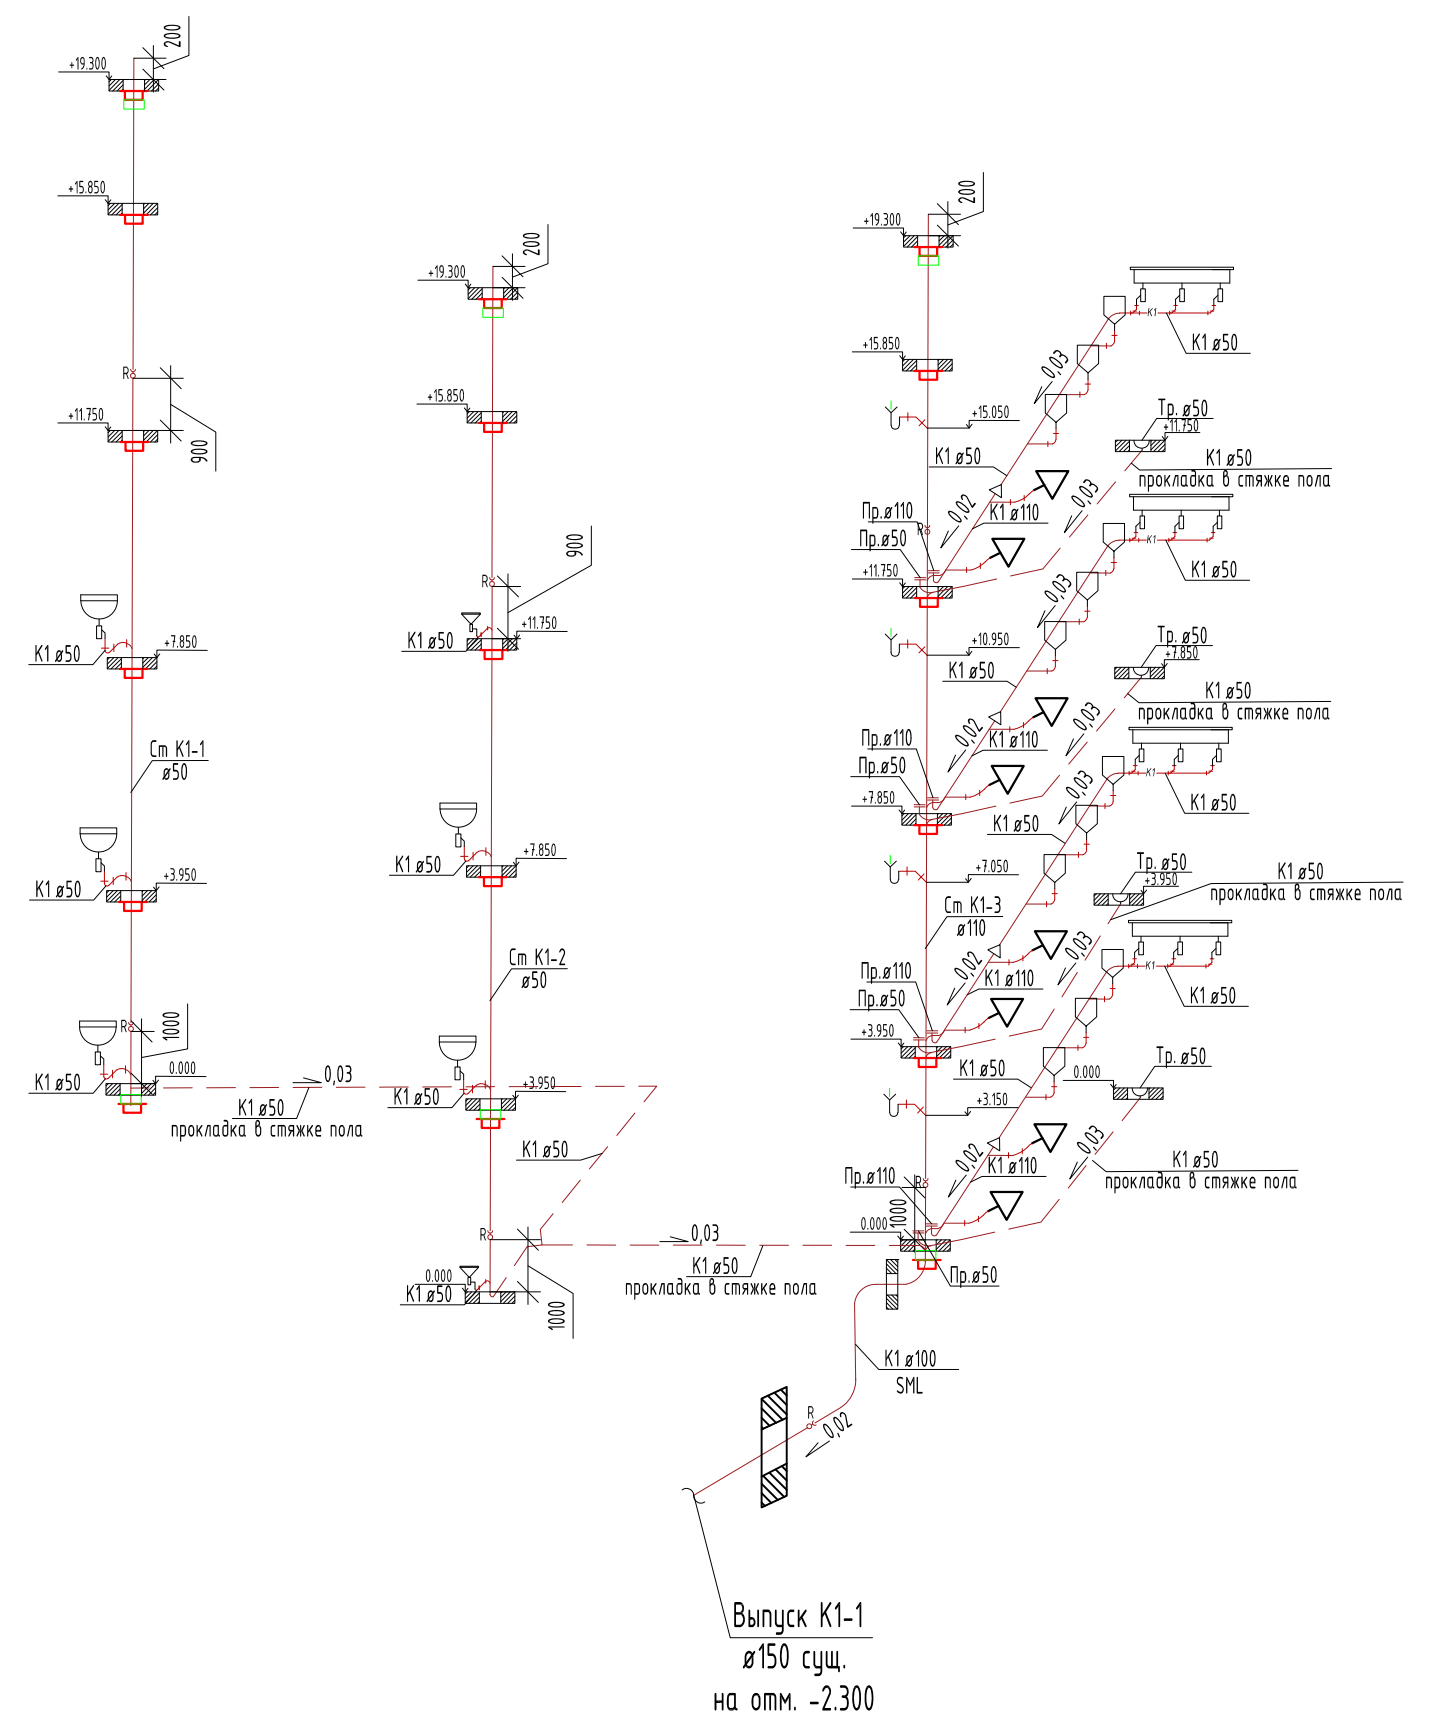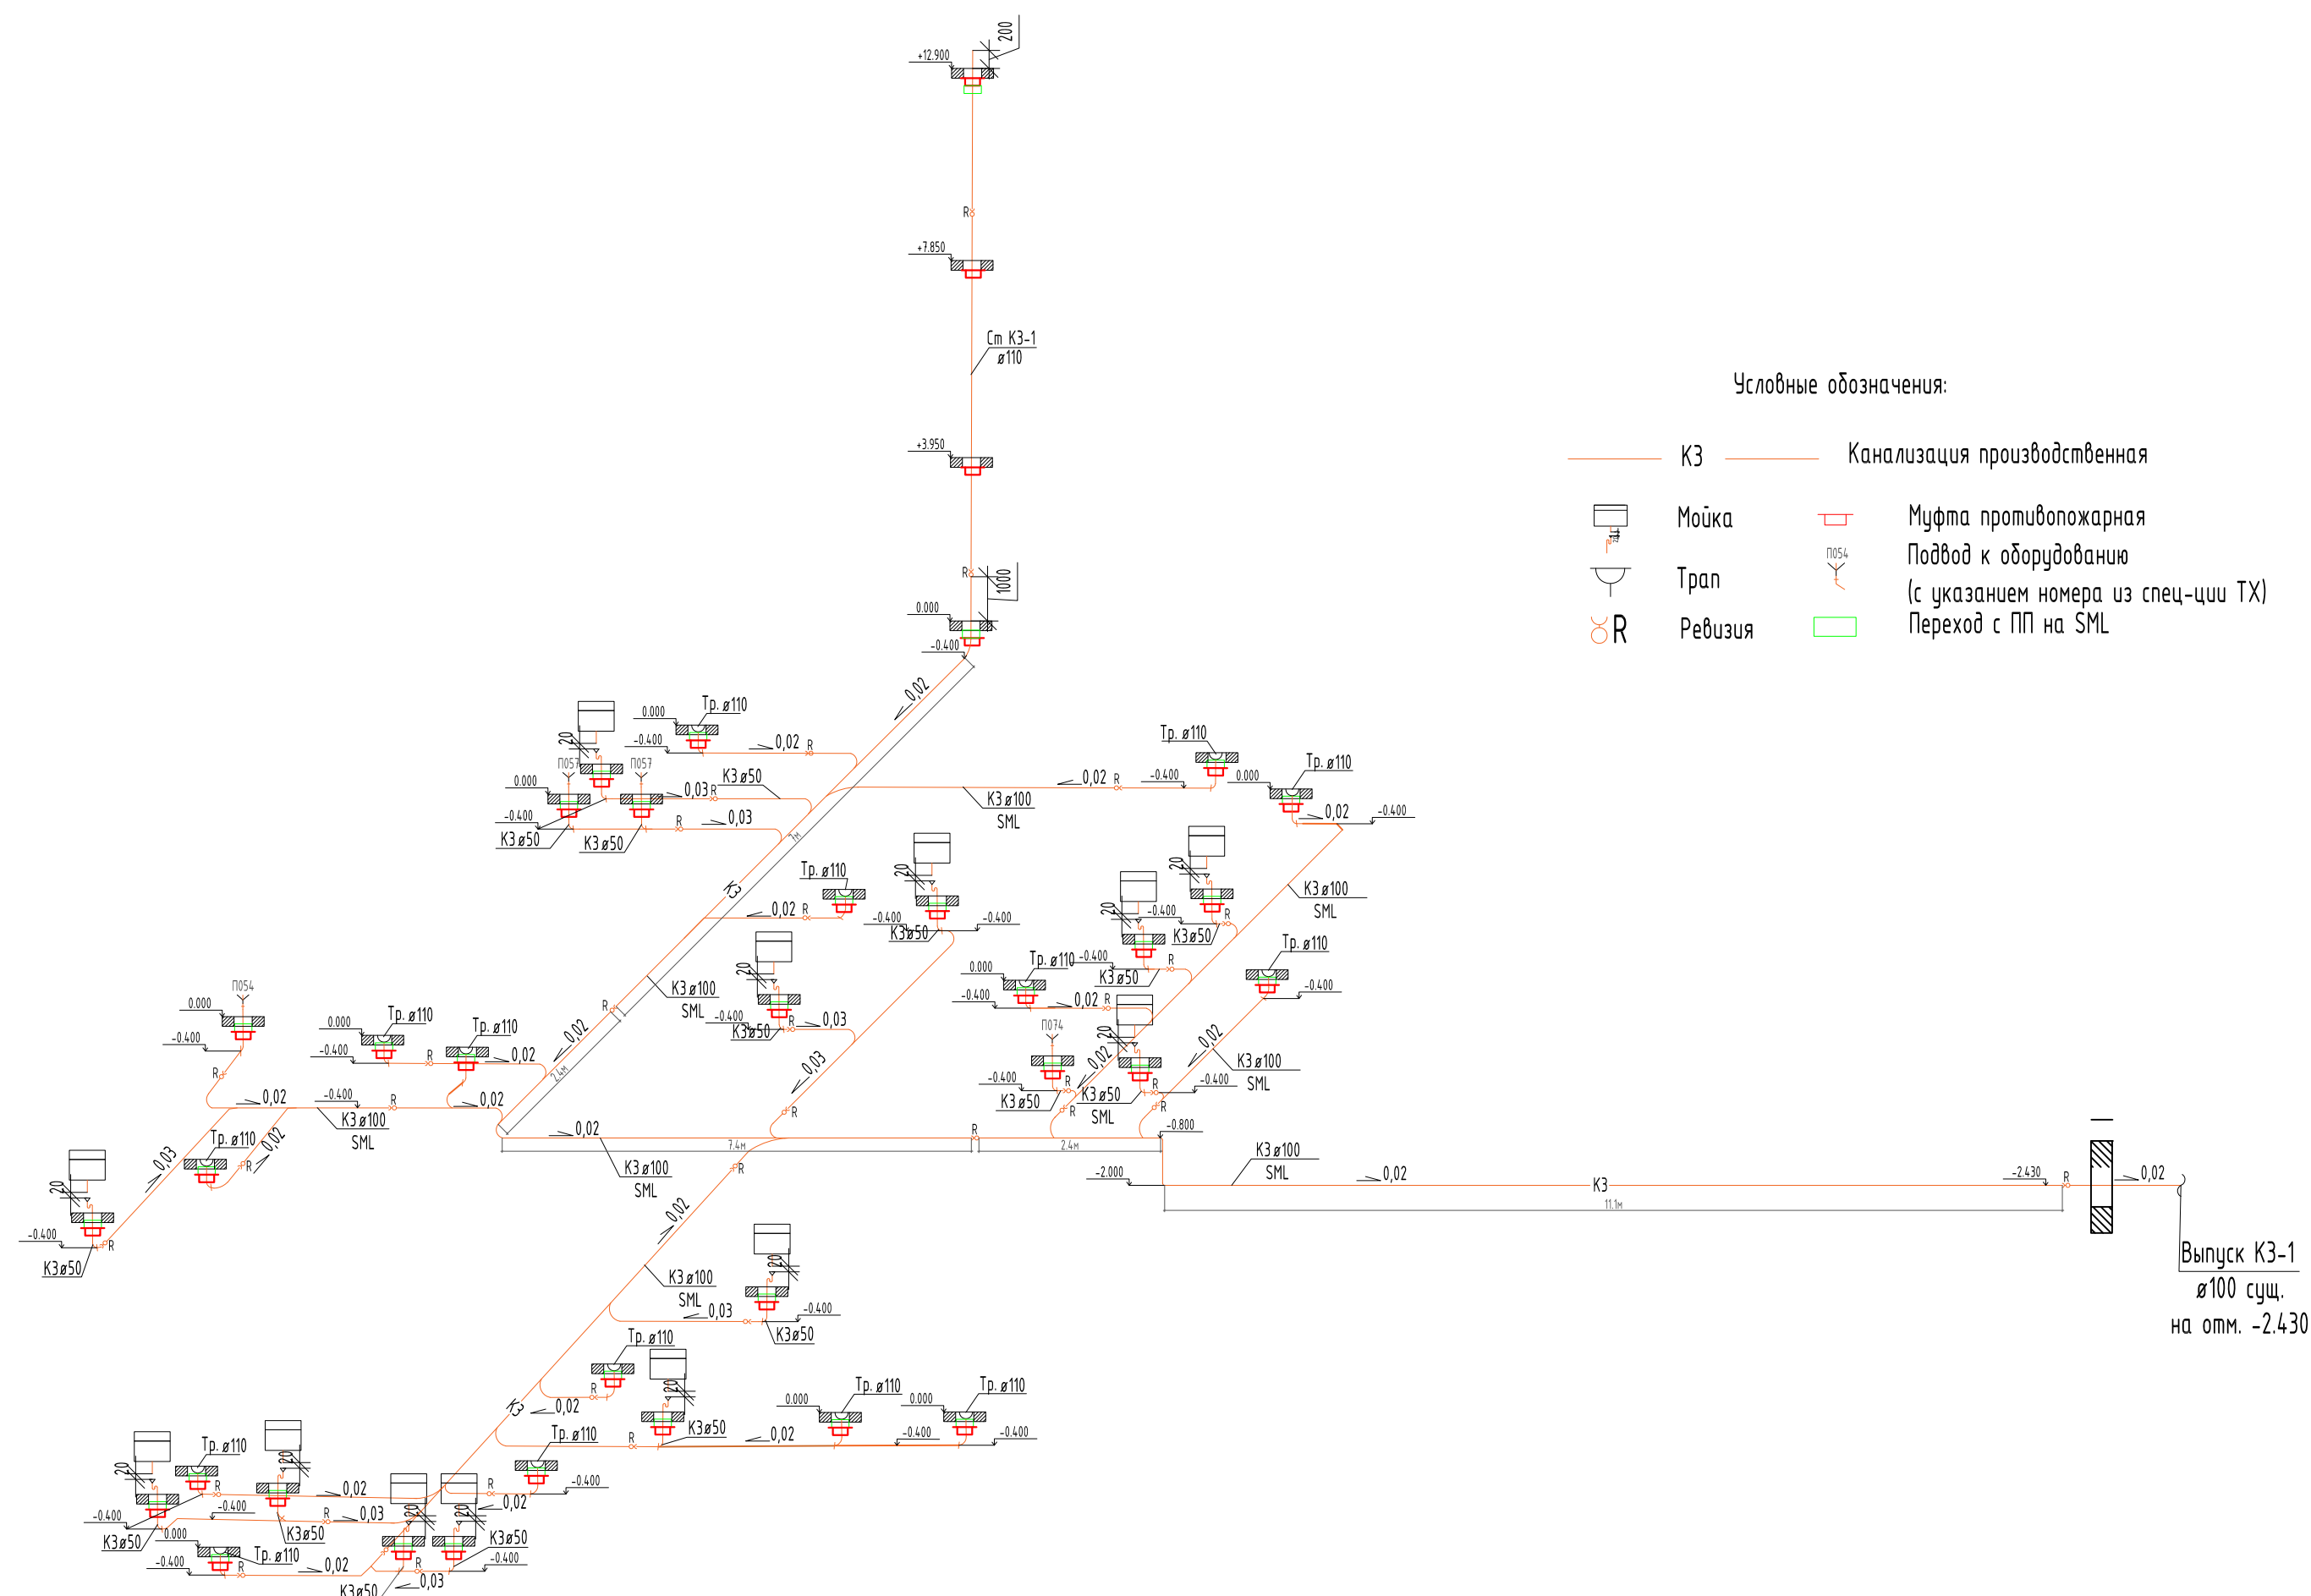

Условные обозначения:

K3

Канализация производственная

Мойка

Муфта противопожарная

Трап

Подвод к оборудованию

R

Ревизия

Переход с ПП на SML

K1

Канализация бытовая

K1

Канализация бытовая в конструкции пола

Питьевой фонтанчик

Поддон душевой

Умывальник

Переход

Трап

Прочистка

Унитаз

Ревизия

Переход с ПП на SML

Муфта противопожарная


Соединение дренажной системы кондиционирования со стояками K1 через капельную воронку

Писсуар

Примечание:  
1. Раковины в классах и санузлах начальной школы устанавливаются на высоте 0,5 м от пола до борта раковины. Для ученических классов и санузлов обучающихся 5-11 классов высота составляет 0,7-0,8 м от пола до борта раковины.  
2. Писсуары в санузлах начальной школы устанавливаются на высоте 0,5 м от пола до борта чаши. Для ученических классов и санузлов обучающихся 5-11 классов высота составляет 0,7-0,8 м от пола до борта чаши.  
3. Выводы стояков на кровлю выполнить из чужеродных труб.

|           |          |         |       |         |            |   |                                                                                       |        |        |
|-----------|----------|---------|-------|---------|------------|---|---------------------------------------------------------------------------------------|--------|--------|
|           |          |         |       |         |            | 16-25/Г-П-ВК   |                                                                                       |        |        |
|           |          |         |       |         |            | Капитальный ремонт объекта "ГБОУ Школа № 429 "Соколиная гора",<br>расположенного по адресу: г.Москва, ул. Соколиной горы 5-я, д.14 |                                                                                       |        |        |
| Изм       | Кол.уч   | Лист    | № док | Подпись | Дата       | Система водоотведения   | Стадия                                                                                | Лист   | Листов |
| Разраб.   |          | Шершова |       |         | 2026.07.01 |   | Р                                                                                     | 9      |        |
|           |          |         |       |         |            |   |                                                                                       |        |        |
|           |          |         |       |         |            |   |                                                                                       |        |        |
| Н. контр. | Ворожьев |         |       |         | 2026.07.01 | Аксонетрическая схема систем К3,<br>К1(выпуск К1-1)                                                                                |  | АЗУРИТ |        |
| ГИП       | Именов   |         |       |         | 2026.07.01 |   |                                                                                       |        |        |

|              |  |
|--------------|--|
| Согласовано  |  |
| Взам. инд. № |  |
| Подп. и дата |  |
| Инв. № подл. |  |

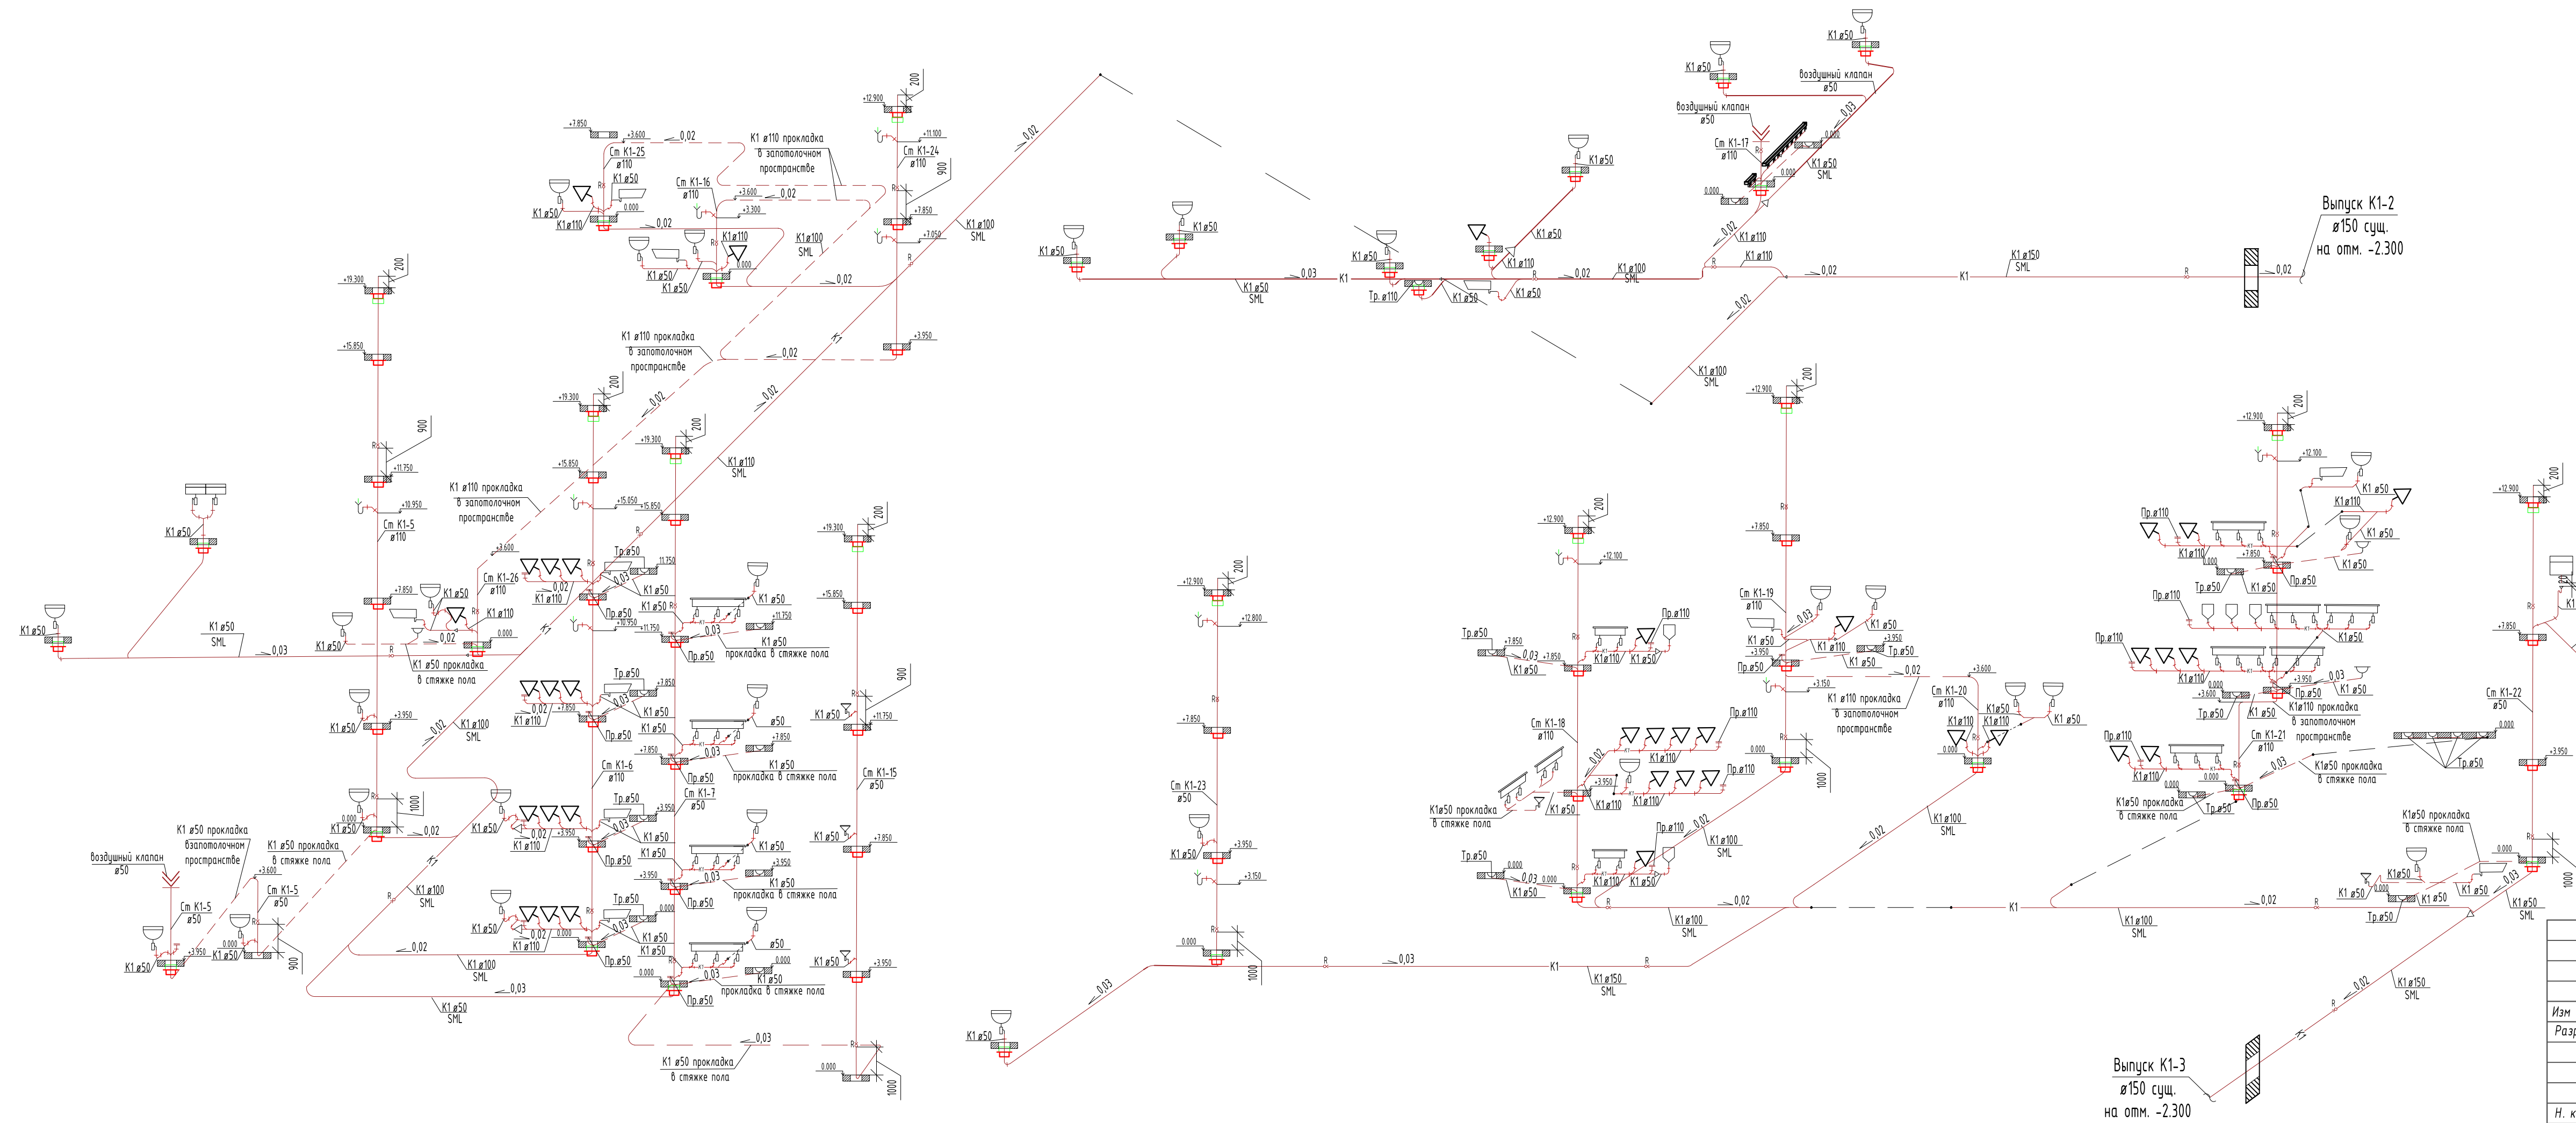

Условные обозначения:


- K1 — Канализация бытовая
- K1 — Канализация бытовая в конструкции пола
- Питьевой фонтанчик
- Поддон душевой
- Умывальник
- Переход
- Трап
- Прочистка
- Унитаз
- Редвизия
- Переход с ПП на SML
- Муфта противопожарная
- Соединение дренажной системы кондиционирования со стояками K1 через капельную воронку
- Мойка
- Писуар

Примечание:  
1. Раковины в классах и санузлах начальной школы устанавливаются на высоте 0,5 м от пола до борта раковины. Для учебных классов и санузлов обучающихся 5-11 классов высота составляет 0,7-0,8 м от пола до борта раковины.  
2. Писсуары в санузлах начальной школы устанавливаются на высоте 0,5 м от пола до борта чаши. Для учебных классов и санузлов обучающихся 5-11 классов высота составляет 0,7-0,8 м от пола до борта чаши.

|         |         |      |       |         |   |                                                     |         |
|---------|---------|------|-------|---------|---|-----------------------------------------------------|---------|
|         |         |      |       |         | 16-25/Г-П-ВК   |                                                     |         |
|         |         |      |       |         | Капитальный ремонт объекта "ГБОУ Школа № 429 "Соколиная гора", расположенного по адресу: г.Москва, ул. Соколиной горы 5-я, д.14 |                                                     |         |
| Изм.    | Кол.уч. | Лист | № док | Подпись | Дата   | Система водоотведения                               | Стадия  |
| Разраб. | Шершова |      |       |         | 2026.07.01   |                                                     | Р       |
|         |         |      |       |         |   | Аксонетрическая схема систем K1 (выпуск K1-2, K1-3) | Лист 10 |
|         |         |      |       |         |   | АЗУРИТ                                              |         |
|         |         |      |       |         |   | ФОРМАТ                                              |         |




|              |  |  |  |  |
|--------------|--|--|--|--|
| Согласовано  |  |  |  |  |
|              |  |  |  |  |
|              |  |  |  |  |
| Взам. инв. № |  |  |  |  |
|              |  |  |  |  |
| Подп. и дата |  |  |  |  |
|              |  |  |  |  |
| Инв. № подл. |  |  |  |  |

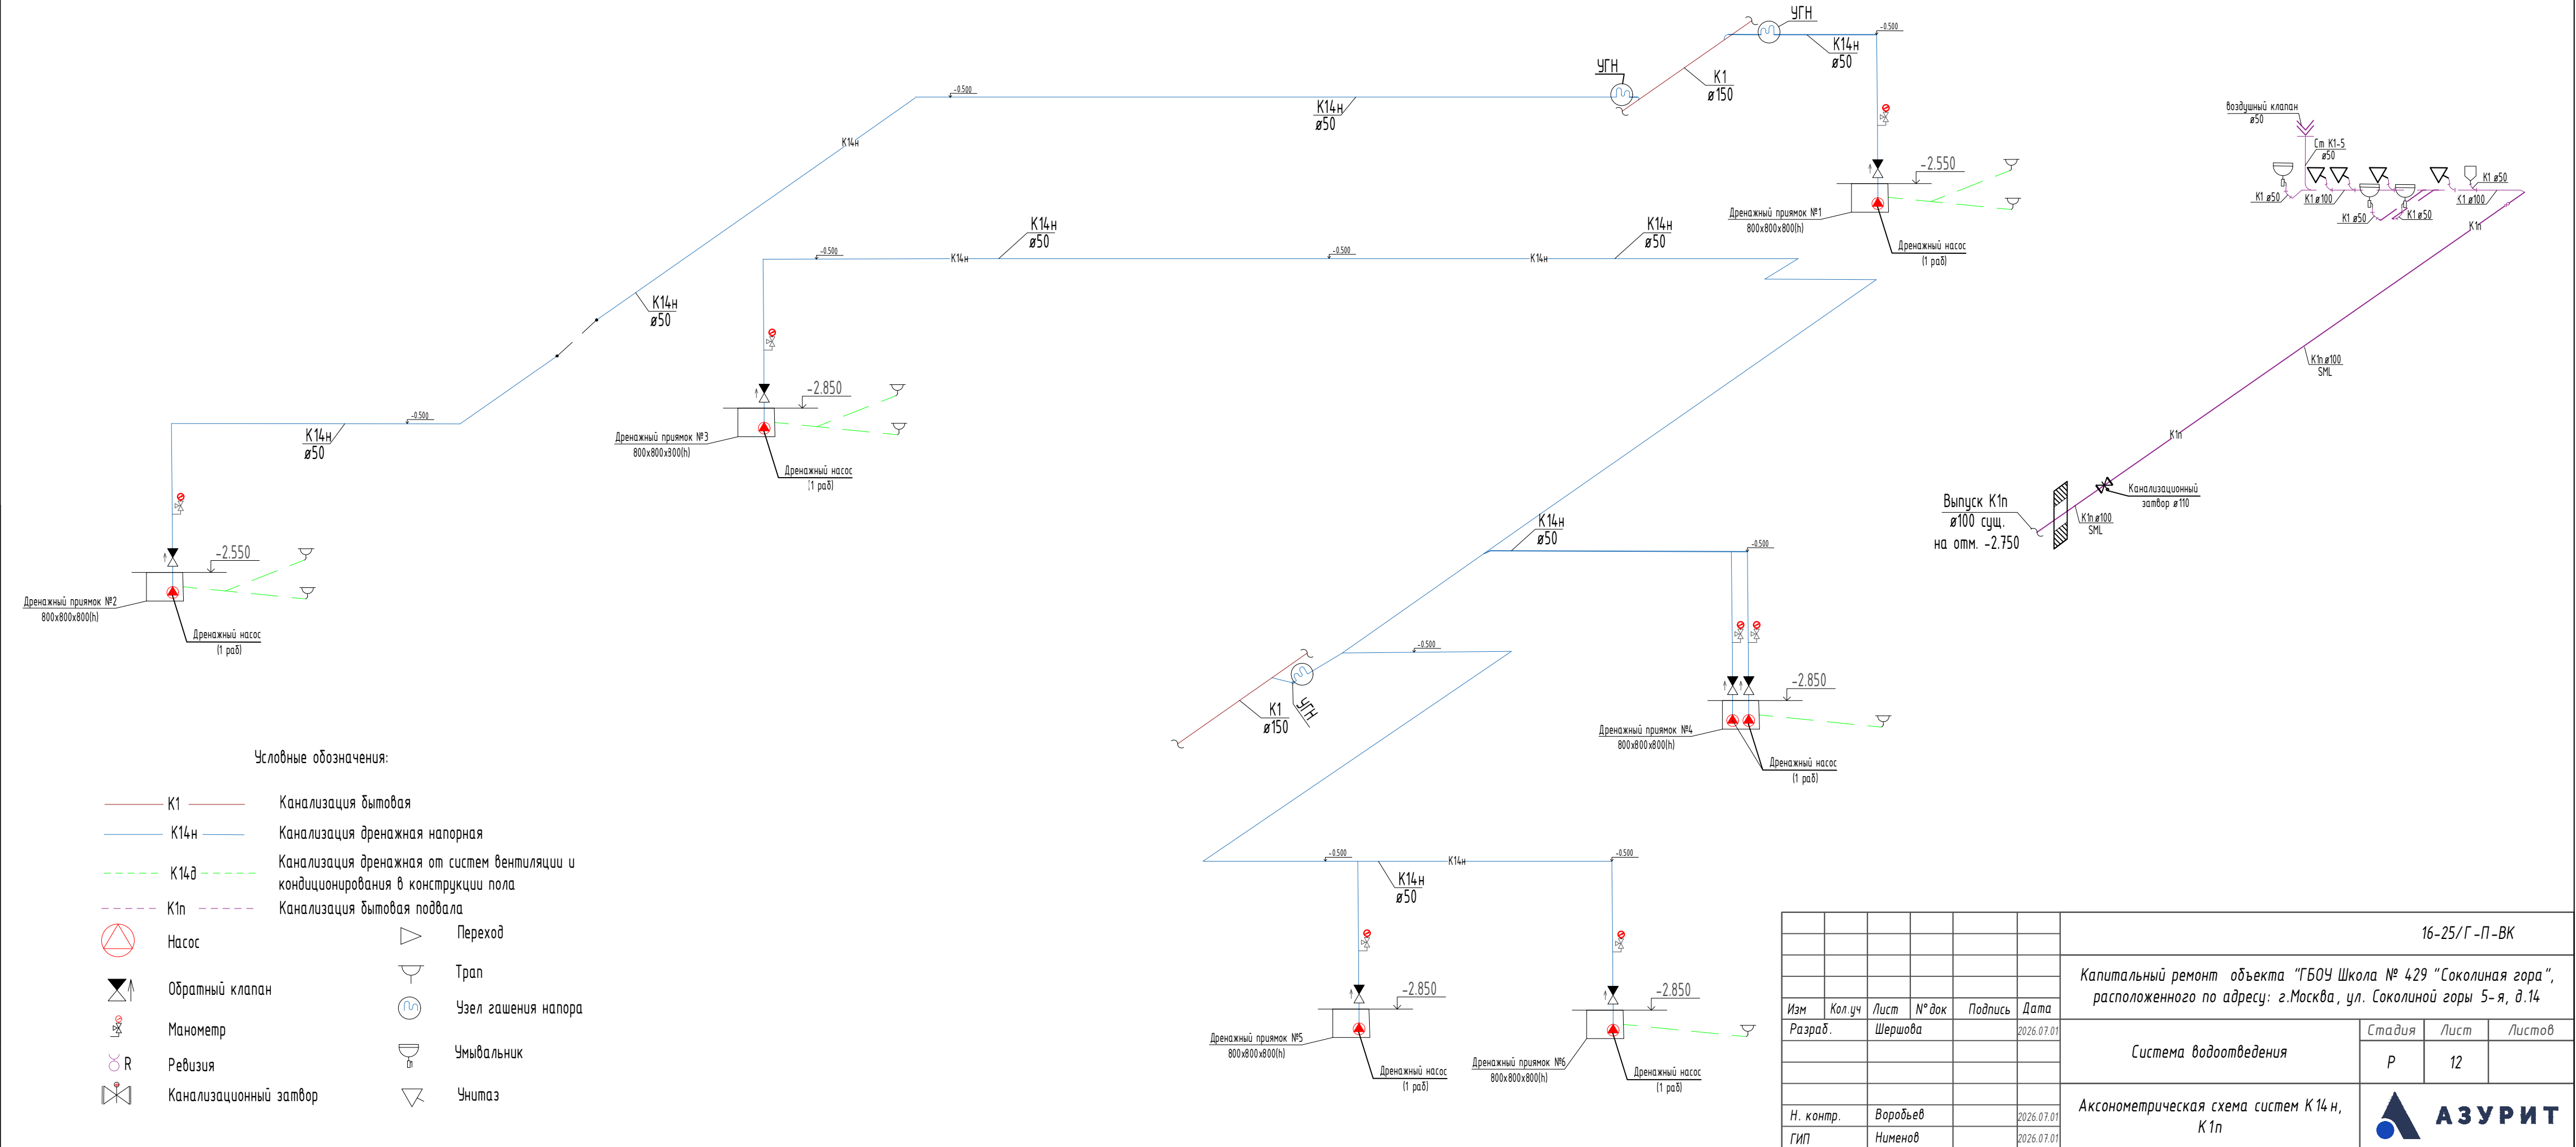


|           |          |         |       |         |            |   |        |      |
|-----------|----------|---------|-------|---------|------------|---|--------|------|
|           |          |         |       |         |            | 16-25/Г-П-ВК   |        |      |
|           |          |         |       |         |            | Капитальный ремонт объекта "ГБОУ Школа № 429 "Соколиная гора", расположенного по адресу: г.Москва, ул. Соколиной горы 5-я, д.14 |        |      |
| Изм       | Кол.уч   | Лист    | № док | Подпись | Дата       | Система водоотведения   | Стадия | Лист |
| Разраб.   |          | Шершова |       |         | 2026.07.01 |   | Р      | 12   |
|           |          |         |       |         |            | Аксонетрическая схема систем K14 н, K1п                                                                                         |        |      |
| Н. контр. | Воробьев |         |       |         | 2026.07.01 |   |        |      |
| ГИП       | Нименов  |         |       |         | 2026.07.01 |   |        |      |

|              |  |  |
|--------------|--|--|
| Согласовано  |  |  |
|              |  |  |
| Взам. инв. № |  |  |
|              |  |  |
| Подп. и дата |  |  |
|              |  |  |
| Инв. № подл. |  |  |
|              |  |  |

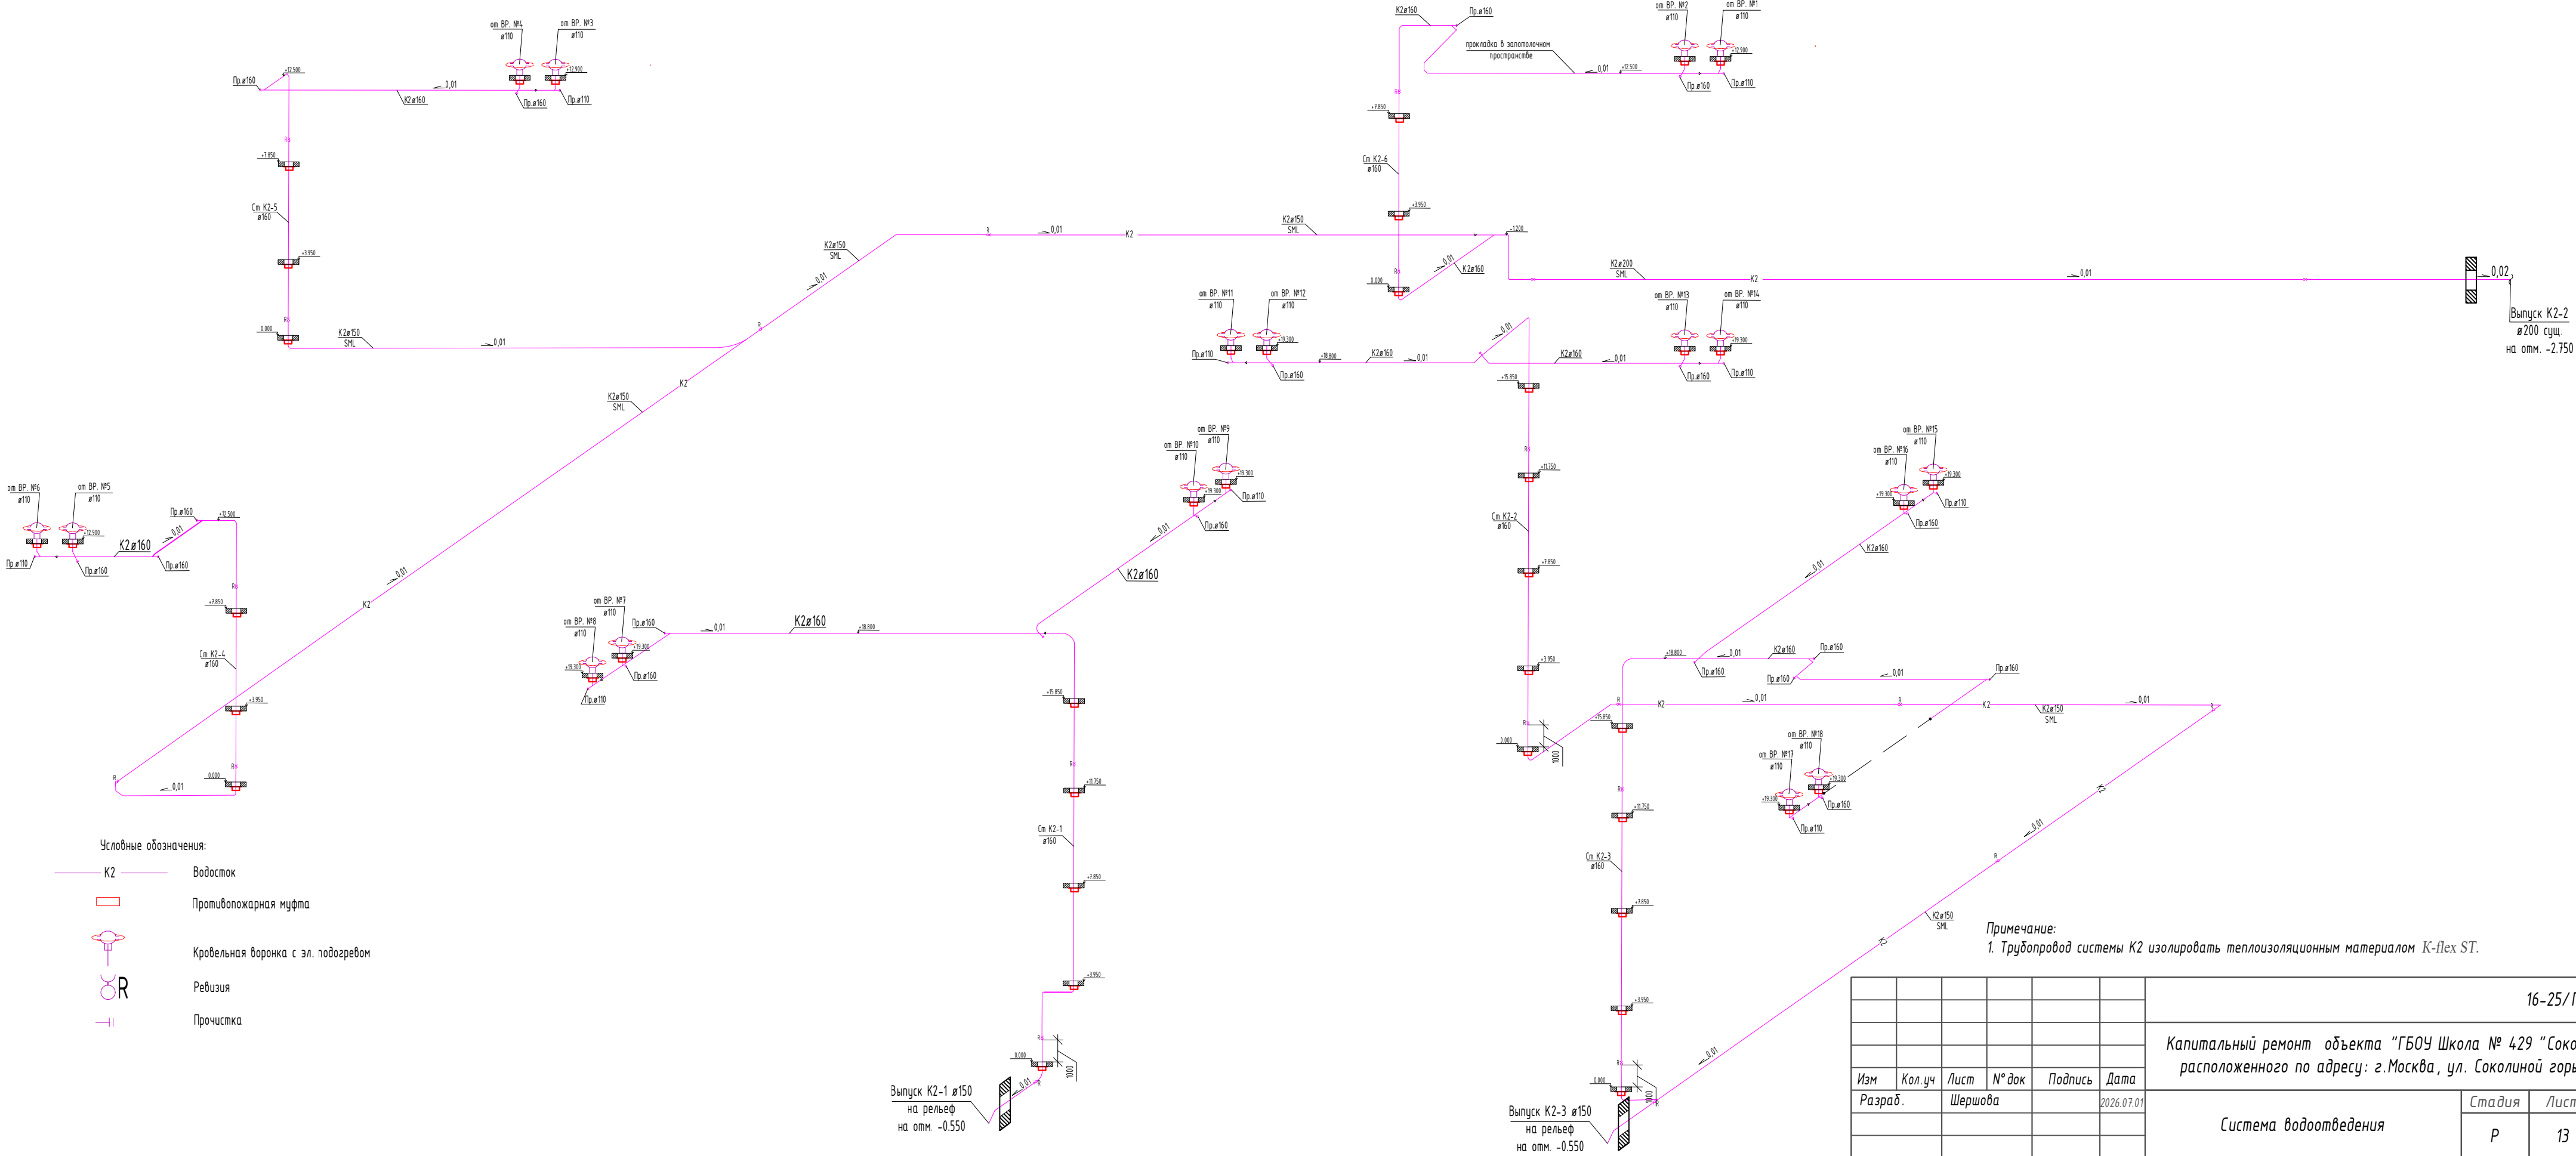


|           |        |          |       |         |            |   |  |   |      |        |
|-----------|--------|----------|-------|---------|------------|---|--|---|------|--------|
|           |        |          |       |         |            | 16-25/Г-П-ВК   |  |   |      |        |
|           |        |          |       |         |            | Капитальный ремонт объекта "ГБОУ Школа № 429 "Соколиная гора", расположенного по адресу: г.Москва, ул. Соколиной горы 5-я, д.14 |  |   |      |        |
| Изм       | Кол.уч | Лист     | № док | Подпись | Дата       |   |  |   |      |        |
| Разраб.   |        | Шершова  |       |         | 2026.07.01 | Система водоотведения   |  | Стадия                                                                                              | Лист | Листов |
|           |        |          |       |         |            |   |  | Р                                                                                                   | 13   |        |
|           |        |          |       |         |            |   |  |   |      |        |
|           |        |          |       |         |            |   |  |   |      |        |
|           |        |          |       |         |            | Аксонетрическая схема системы К2                                                                                                |  |  <b>АЗУРИТ</b> |      |        |
| Н. контр. |        | Воробьев |       |         | 2026.07.01 |   |  |   |      |        |
| ГИП       |        | Нименов  |       |         | 2026.07.01 |   |  |   |      |        |


Узел прохода стояков канализации через перекрытия

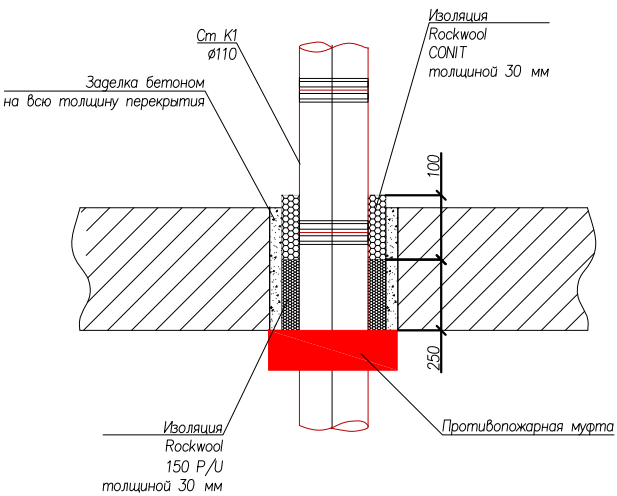


Узел прохода сетей К14н через стену

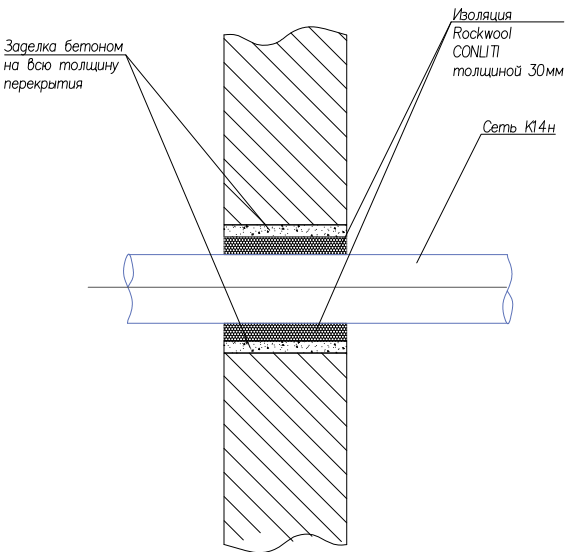


Узел прохода стояков канализации через перекрытия

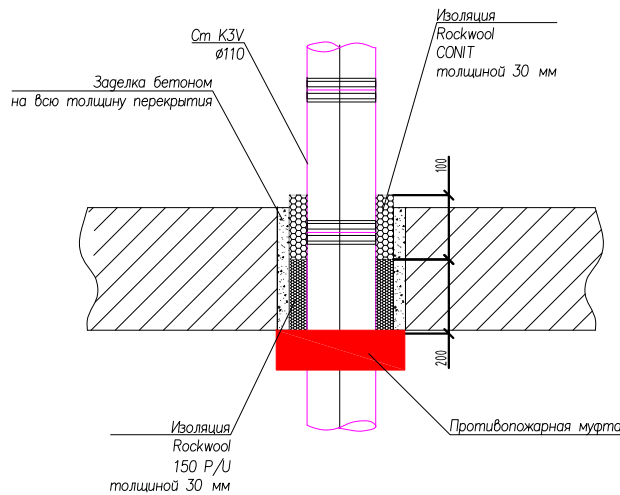


Узел прохода трубопроводов через наружную стену (серия 5.900-20)

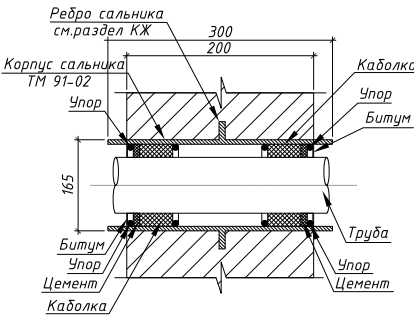

Узел монтажа дренажного насоса

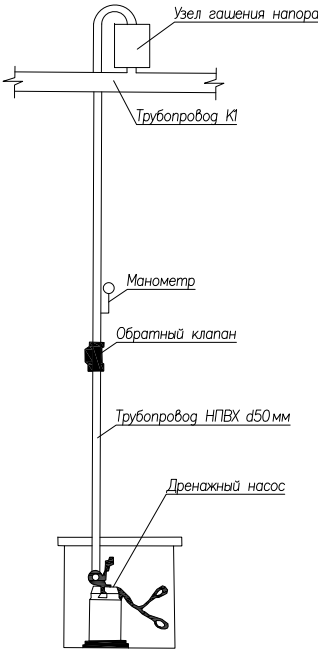

Узел монтажа канализационного затвора

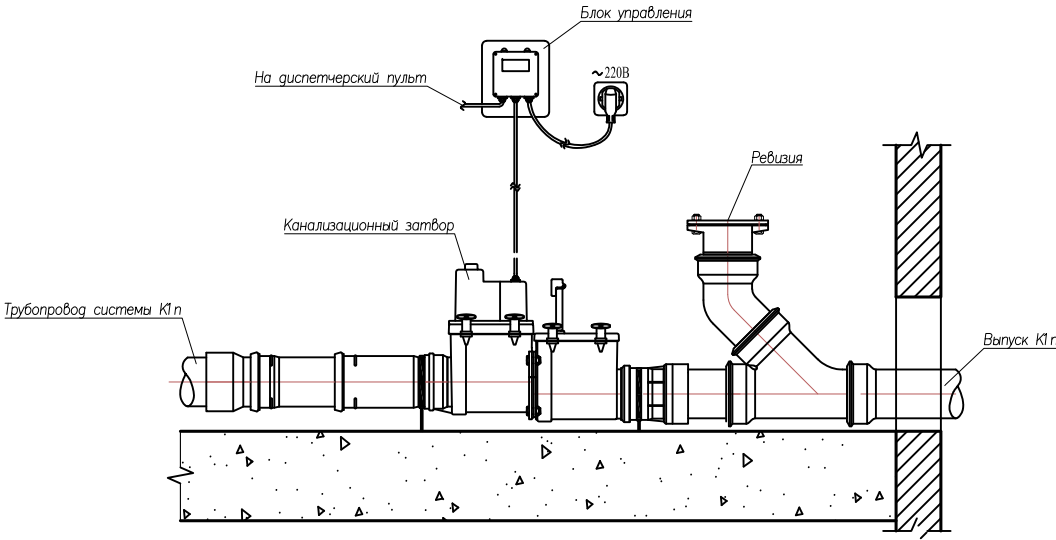

|              |  |  |  |  |  |
|--------------|--|--|--|--|--|
| Согласовано  |  |  |  |  |  |
| Взам. инв. N |  |  |  |  |  |
| Подп. и дата |  |  |  |  |  |
| Инв. N подл. |  |  |  |  |  |

|           |        |          |       |         |            |   |                                                                                       |      |        |
|-----------|--------|----------|-------|---------|------------|---|---------------------------------------------------------------------------------------|------|--------|
|           |        |          |       |         |            | 16-25/Г -П-ВК   |                                                                                       |      |        |
|           |        |          |       |         |            | Капитальный ремонт объекта "ГБОУ Школа № 429 "Соколиная гора",<br>расположенного по адресу: г.Москва, ул. Соколиной горы 5-я, д.14 |                                                                                       |      |        |
| Изм       | Кол.уч | Лист     | № док | Подпись | Дата       | Система водоотведения   | Стадия                                                                                | Лист | Листов |
| Разраб.   |        | Шершова  |       |         | 2026.07.01 |   | Р                                                                                     | 14   |        |
|           |        |          |       |         |            |   |                                                                                       |      |        |
|           |        |          |       |         |            | Типовые узлы   |  |      |        |
| Н. контр. |        | Воробьев |       |         | 2026.07.01 |   |                                                                                       |      |        |
| ГИП       |        | Именов   |       |         | 2026.07.01 |   |                                                                                       |      |        |

|                                     |            |   |                                                    |                                      |                                      |                       |   |                   |                                                                                       |        |
|-------------------------------------|------------|---|----------------------------------------------------|--------------------------------------|--------------------------------------|-----------------------|---|-------------------|---------------------------------------------------------------------------------------|--------|
| Формат А3                           | Позиция    | Наименование и техническая характеристика   | Тип, марка, обозначение документа, опросного листа | Код оборудования, изделия, материала | Завод-изготовитель                   | Единица измерения     | Количество   | Масса единицы, кг | Примечание                                                                            |        |
|                                     |            | Система бытовой и производственной канализации (К1, К3) ниже 0.000   |                                                    |                                      |                                      |                       |   |                   |                                                                                       |        |
|                                     |            |   |                                                    |                                      |                                      |                       |   |                   |                                                                                       |        |
|                                     | 1          | Трап Ø50 для внутренних помещений с решёткой 138x138 мм в подрамнике 145*145 мм, с "сухим" сифоном "Primus", с вертикальным выпуском.<br>Гидроизоляционный комплект, состоящий из обжимной фланец из нержавеющей стали с гидроизоляционным полимербитумным полотном, резинового уплотнительного кольца и комплекта саморезов | HL3100Pr/HL8300.H                                  |                                      | ООО "ХЛ-РУС" Россия                  | шт                    | 7   |                   |                                                                                       |        |
|                                     | 2          | Переходник с полипропилена (ПП) на чугун, свинец, сталь, Ø110/ Ø100   |                                                    |                                      |                                      | шт                    | 28   |                   |                                                                                       |        |
|                                     | 3          | Переходник с полипропилена (ПП) на чугун, свинец, сталь, Ø50/ Ø50   |                                                    |                                      |                                      | шт                    | 36   |                   |                                                                                       |        |
|                                     | 4          | Ревизия SML Ø100   |                                                    |                                      |                                      | шт                    | 21   |                   |                                                                                       |        |
|                                     | 5          | Ревизия SML Ø50   |                                                    |                                      |                                      | шт                    | 19   |                   |                                                                                       |        |
|                                     | 6          | Ревизия SML Ø150   |                                                    |                                      |                                      | шт                    | 4   |                   |                                                                                       |        |
|                                     | 7          | Труба чугун SML безраструбная Ø50 с фасонными изделиями   |                                                    |                                      |                                      | м                     | 160   |                   |                                                                                       |        |
|                                     | 8          | Труба чугун SML безраструбная Ø100 с фасонными изделиями   |                                                    |                                      |                                      | м                     | 230   |                   |                                                                                       |        |
|                                     | 9          | Труба чугун SML безраструбная Ø150 с фасонными изделиями   |                                                    |                                      |                                      | м                     | 20   |                   |                                                                                       |        |
|                                     | 10         | Подвеска (направляющая) для крепления труб к строит. конструкциям Ø50   |                                                    |                                      |                                      | шт                    | 120   |                   |                                                                                       |        |
|                                     | 11         | Подвеска (направляющая) для крепления труб к строит. конструкциям Ø100   |                                                    |                                      |                                      | шт                    | 210   |                   |                                                                                       |        |
|                                     | 12         | Опоры и крепление трубопроводов (С245)   |                                                    |                                      |                                      | т                     | 0,6   |                   |                                                                                       |        |
| Согласовано                         | 13         | TESI AquaBlade® Подвесной унитаз, глубокий смыв, сидение и крышка T352801 или T352701 заказывается дополнительно, с крепежом TT0299598 (для полностью скрытого монтажа)   |                                                    |                                      | ООО «Идеал Стандарт Солюшенс» Россия | шт                    | 4   |                   |                                                                                       |        |
|                                     | 14         | TESI Тонкое сидение и крышка для унитазов T0082,T0087,T0083,T0077,T0075,T0079,T3503,T0078, тип SANDWICH, с функцией плавного закрытия, легкоъемное, шарниры металл/пластик   |                                                    |                                      | Vidima                               | шт                    | 4   |                   |                                                                                       |        |
|                                     | 15         | OLEAST™ P1 Пневматическая панель смыва (для комбинации с пневматическим переходным комплектом - заказывается дополнительно), двойной смыв   |                                                    |                                      | ООО «Идеал Стандарт Солюшенс» Россия | шт                    | 4   |                   |                                                                                       |        |
|                                     |            |   |                                                    |                                      |                                      |                       |   |                   |                                                                                       |        |
| Изм. Кол.уч. Лист №док Подпись Дата |            |   |                                                    |                                      |                                      |                       | 16-25/Г-Р-ВК-СО   |                   |                                                                                       |        |
|                                     |            |   |                                                    |                                      |                                      |                       | «Капитальный ремонт объекта «ГБОУ «Школа № 429 «Соколиная гора», расположенного по адресу: г. Москва, ул. Соколиной горы 5-я, д.14» |                   |                                                                                       |        |
|                                     | Изм.       | Кол.уч.   | Лист                                               | №док                                 | Подпись                              | Дата                  |   |                   |                                                                                       |        |
|                                     | Разработал | Воронова   |                                                    |                                      | 01.07.26                             | Система водоотведения |   | Стадия            | Лист                                                                                  | Листов |
|                                     | Проверил   | Маркова   |                                                    |                                      | 01.07.26                             |                       |   | Р                 | 1                                                                                     | 4      |
|                                     |            |   |                                                    |                                      |                                      |                       |   |                   |                                                                                       |        |
| Интв. № подл.                       |            |   |                                                    |                                      |                                      |                       | Спецификация оборудования, изделий и материалов                                                                                     |                   |  |        |
|                                     |            |   |                                                    |                                      |                                      |                       |   |                   |                                                                                       |        |
| Инв. № подл. | Подпись и дата | Взам. инв. № |
|--------------|----------------|--------------|
|              |                |              |

| Позиция | Наименование и техническая характеристика   | Тип, марка, обозначение документа, опросного листа | Код оборудования, изделия, материала | Завод-изготовитель                   | Единица измерения | Количество | Масса единицы, кг | Примечание |      |
|---------|---|----------------------------------------------------|--------------------------------------|--------------------------------------|-------------------|------------|-------------------|------------|------|
| 16      | ТЕМРО Умывальник 50X44 см, 1 отверстие под смеситель, с отверстием перелива, для монтажа с колонной Т422901 или полуколонной Т423001, без крепежа (рекомендуемый крепеж - WW965340) |                                                    |                                      | ООО «Идеал Стандарт Солюшенс» Россия | компл.            | 3          |                   |            |      |
| 17      | IDEALSMART Смеситель для умывальника В0459АА   |                                                    |                                      | IDEALSMART                           | компл.            | 3          |                   |            |      |
| 18      | Дизайн сифон для умывальника 1 1/4"   |                                                    |                                      | ООО «Идеал Стандарт Солюшенс» Россия | компл.            | 3          |                   |            |      |
| 19      | Решетка слива G 1 1/4" (в случае установки смесителя без донного клапана)   |                                                    |                                      | ООО «Идеал Стандарт Солюшенс» Россия | компл.            | 3          |                   |            |      |
| 20      | Писсуар подвода сзади в комплекте с соединительным комплектом и сифоном   |                                                    |                                      | ООО «Идеал Стандарт Солюшенс» Россия | компл.            | 1          |                   |            |      |
| 21      | Противопожарная самосрабатывающая муфта Огракс ПМ,Ø50мм   | ТУ 5285-027-13267785-04                            |                                      | ГК УНИХИМТЕК                         | шт                | 36         |                   |            |      |
| 22      | Противопожарная самосрабатывающая муфта Огракс-ПМ, Ø110мм   | ТУ 5285-027-13267785-04                            |                                      | ГК УНИХИМТЕК                         | шт                | 29         |                   |            |      |
|         |   |                                                    |                                      |                                      |                   |            |                   |            |      |
|         | <b><u>Система бытовой и производственной канализации (К1, К3) сантехоборудование, выше 0.000</u></b>                                                                                |                                                    |                                      |                                      |                   |            |                   |            |      |
|         |   |                                                    |                                      |                                      |                   |            |                   |            |      |
| 23      | TESI AquaBlade® Подвесной унитаз, глубокий смыв, сидение и крышка Т352801 или Т352701 заказывается дополнительно, с крепежом ТТ0299598 (для полностью скрытого монтажа)             |                                                    |                                      | ООО «Идеал Стандарт Солюшенс» Россия | шт                | 75         |                   |            |      |
| 24      | TESI Тонкое сидение и крышка для унитазов Т0082,Т0087,Т0083,Т0077,Т0075,Т0079,Т3503,Т0078, тип SANDWICH, с функцией плавного закрытия, легкоъемное, шарниры металл/пластик          |                                                    |                                      | Vidima                               | шт                | 75         |                   |            |      |
| 25      | OLEAST™ P1 Пневматическая панель смыва (для комбинации с пневматическим переходным комплектом - заказывается дополнительно), двойной смыв                                           |                                                    |                                      | ООО «Идеал Стандарт Солюшенс» Россия | шт                | 75         |                   |            |      |
| 26      | ТЕМРО Умывальник 50X44 см, 1 отверстие под смеситель, с отверстием перелива, для монтажа с колонной Т422901 или полуколонной Т423001, без крепежа (рекомендуемый крепеж - WW965340) |                                                    |                                      | ООО «Идеал Стандарт Солюшенс» Россия | компл.            | 41         |                   |            |      |
| 27      | IDEALSMART Смеситель для умывальника В0459АА   |                                                    |                                      | IDEALSMART                           | компл.            | 41         |                   |            |      |
| 28      | Дизайн сифон для умывальника 1 1/4"   |                                                    |                                      | ООО «Идеал Стандарт Солюшенс» Россия | компл.            | 41         |                   |            |      |
| 29      | Решетка слива G 1 1/4" (в случае установки смесителя без донного клапана)   |                                                    |                                      | ООО «Идеал Стандарт Солюшенс» Россия | компл.            | 41         |                   |            |      |
| 30      | Писсуар подвода сзади в комплекте с соединительным комплектом и сифоном   |                                                    |                                      | ООО «Идеал Стандарт Солюшенс»        | компл.            | 20         |                   |            |      |
|         |   |                                                    |                                      |                                      |                   |            |                   |            |      |
|         |   |                                                    |                                      |                                      |                   |            |                   |            | Лист |
|         |   |                                                    |                                      | 16-25/Г-Р-ВК-СО                      |                   |            |                   |            | 2    |
|         |   |                                                    |                                      | Изм.                                 | Кол.у             | Лист       | № док             | Подпись    | Дата |

| Инв. № подл. | Подпись и дата | Взам. инв. № |
|--------------|----------------|--------------|
|              |                |              |

| Позиция | Наименование и техническая характеристика   | Тип, марка, обозначение документа, опросного листа | Код оборудования, изделия, материала | Завод-изготовитель | Единица измерения | Количество | Масса единицы, кг | Примечание |
|---------|---|----------------------------------------------------|--------------------------------------|--------------------|-------------------|------------|-------------------|------------|
|         |   |                                                    |                                      | Россия             |                   |            |                   |            |
| 31      | Раковина на 2 слив индивидуального изготовления   |                                                    |                                      |                    | компл.            | 4          |                   |            |
| 32      | Раковина на 3 слив индивидуального изготовления   |                                                    |                                      |                    | компл.            | 20         |                   |            |
| 33      | Раковина на 4 слив индивидуального изготовления   |                                                    |                                      |                    | компл.            | 1          |                   |            |
| 34      | Раковина на 9 слив индивидуального изготовления   |                                                    |                                      |                    | компл.            | 1          |                   |            |
| 35      | Сифон для умывальника цельнометаллический   |                                                    |                                      |                    | шт                | 81         |                   |            |
| 36      | Душевой лоток с перфорированной решеткой, 55см, с сухим затвором   |                                                    |                                      |                    | шт                | 4          |                   |            |
| 37      | Смеситель для душа   |                                                    |                                      |                    | шт                | 6          |                   |            |
| 38      | Душевой поддон акрил 90х90 см   |                                                    |                                      |                    | шт                | 6          |                   |            |
| 39      | Сифон для душевого поддона с сухим гидрозатвором   |                                                    |                                      |                    | шт                | 9          |                   |            |
| 40      | Трап Ду 100 вертикальный регулируемый с нержавеющей решеткой, с сухим затвором Т 310.0 SDsP   |                                                    |                                      |                    | шт                | 9          |                   |            |
| 41      | Сифон с воронкой, с разрывом струи, белый DN50   |                                                    |                                      |                    | шт                | 85         |                   |            |
| 42      | Трап Ø50 для внутренних помещений с решёткой 138х138 мм в подрамнике 145*145 мм, с "сухим" сифоном "Primus", с вертикальным выпуском.<br>Гидроизоляционный комплект, состоящий из обжимной фланец из нержавеющей стали с гидроизоляционным полимербитумнымполотном, резинового уплотнительного кольца и комплекта саморезов |                                                    |                                      |                    | шт                | 32         |                   |            |
| 43      | Умывальник с настенным полупьедесталом   |                                                    |                                      |                    | компл.            | 1          |                   |            |
| 44      | Смеситель для умывальника   |                                                    |                                      |                    | компл.            | 1          |                   |            |
| 45      | Сифон бутылочный, унифицированный с выпуском и вертикальным отводом для умывальника   |                                                    |                                      |                    | компл.            | 1          |                   |            |
| 46      | Унитаз подвесной (ММГН)   |                                                    |                                      |                    | компл.            | 1          |                   |            |
| 47      | Сиденье-крышка: материал: дюропласт (цвет - белый)   |                                                    |                                      |                    | компл.            | 1          |                   |            |
| 48      | Опора для спины: материал опоры: алюминий (цвет - белый); материал подушки: полиуретан (цвет – белый)   |                                                    |                                      |                    | компл.            | 1          |                   |            |
| 49      | Система инсталляции   |                                                    |                                      |                    | компл.            | 1          |                   |            |
| 50      | Кнопка слива   |                                                    |                                      |                    | компл.            | 1          |                   |            |
| 51      | Крепление для умывальника   |                                                    |                                      |                    | компл.            | 1          |                   |            |
| 52      | Труба полипропиленовая РР-Н с раструбом серая б/нап Дн 63х1,8 (Ду 50), с фасонными частями   |                                                    |                                      |                    | м                 | 685        |                   |            |
| 53      | Труба полипропиленовая РР-Н с раструбом серая б/нап Дн 110х2,7 (Ду 100), с фасонными частями   |                                                    |                                      |                    | м                 | 594        |                   |            |
| 54      | Противопожарная самосрабатывающая муфта Огракс ПМ,Ø50мм   | ТУ 5285-027-13267785-04                            |                                      | ГК УНИХИМТЕК       | шт                | 50         |                   |            |
| 55      | Противопожарная самосрабатывающая муфта Огракс-ПМ, Ø110мм   | ТУ 5285-027-13267785-04                            |                                      | ГК УНИХИМТЕК       | шт                | 32         |                   |            |
| 56      | Опоры и крепления трубопроводов (С245)   |                                                    |                                      |                    | т                 | 0,8        |                   |            |
| 57      | Аэратор (воздушный клапан) d110 ПП   |                                                    |                                      |                    | шт                | 1          |                   |            |
| 58      | Аэратор (воздушный клапан) d50 ПП   |                                                    |                                      |                    | шт                | 1          |                   |            |
|         |   |                                                    |                                      |                    |                   |            |                   |            |

Изм.

Кол.у

Лист

№док

Подпись

Дата

16-25/Г-Р-ВК-СО

Лист

3

| Позиция | Наименование и техническая характеристика   | Тип, марка, обозначение документа, опросного листа | Код оборудования, изделия, материала | Завод-изготовитель | Единица измерения | Количество | Масса единицы, кг | Примечание             |
|---------|---|----------------------------------------------------|--------------------------------------|--------------------|-------------------|------------|-------------------|------------------------|
|         | <b>Водосток (К2) ниже и выше 0,000</b>   |                                                    |                                      |                    |                   |            |                   |                        |
|         |   |                                                    |                                      |                    |                   |            |                   |                        |
| 59      | Водосточная воронка с листвоуловителем, с теплоизоляцией, с гидроизоляционным полимербитумным полотном 500х500мм, с вертикальным выпуском, с эл.подогревом, Ø110 |                                                    |                                      | Россия             | шт                | 18         |                   |                        |
| 60      | Надставной элемент с полимер-битумным полотном   |                                                    |                                      | Россия             | шт                | 18         |                   |                        |
| 61      | Дренажное кольцо   |                                                    |                                      | Россия             | шт                | 18         |                   |                        |
| 62      | Удлинитель   |                                                    |                                      | Россия             | шт                | 18         |                   |                        |
| 63      | Патрубок компенсационный из полипропилена, Ø110мм   | ТУ 2248-065-42943419-2013                          | 531011.F                             | ООО "СИНИКОН"      | шт                | 18         |                   |                        |
| 64      | Переходник полипропилен/пвх на чугун/сталь Ø110   |                                                    |                                      | Россия             | шт                | 18         |                   |                        |
| 65      | Труба НПВХ серая SDR26 Дн 110х4,2 с фасонными частями   | ГОСТ Р 51613-2000                                  |                                      | Россия             | м                 | 100        |                   |                        |
| 66      | Труба НПВХ серая SDR26 Дн 160 х4,7 раструбная напорная, с фасонными частями                                                                                      | ГОСТ Р 51613-2000                                  |                                      | Россия             | м                 | 210        |                   |                        |
| 67      | Труба НПВХ серая SDR26 Дн 220 х4,9 раструбная напорная, с фасонными частями                                                                                      | ГОСТ Р 51613-2000                                  |                                      | Россия             | м                 | 15         |                   |                        |
| 68      | Ревизия Ø110/ Ø160   | ГОСТ 22689—2014                                    |                                      | Россия             | шт                | 12/22      |                   |                        |
| 69      | Противопожарная самосрабатывающая муфта Огракс ПМ,Ø110мм   | ТУ 5285-027-13267785-04                            |                                      | ГК УНИХИМТЕК       | шт                | 42         |                   |                        |
| 70      | Теплоизоляционный материал трубный "K-flex ST" S=9мм, Ø100/ Ø 160                                                                                                |                                                    |                                      | Россия             | м                 | 100/210    |                   |                        |
| 71      | НПВ" S=9мм, Ø200   |                                                    |                                      | Россия             | м                 | 15         |                   |                        |
| 72      | Крепление трубопроводов   |                                                    |                                      | Россия             | кг                | 600        |                   |                        |
|         |   |                                                    |                                      |                    |                   |            |                   |                        |
|         | <b>Дренажная канализация (К14н)</b>   |                                                    |                                      |                    |                   |            |                   |                        |
|         |   |                                                    |                                      |                    |                   |            |                   |                        |
| 73      | Погружной насос с закрытым рабочим колесом Н=10,0 м., Q=1,5 м3 /ч; U=3х380 В, N=1,1 кВт                                                                          |                                                    |                                      |                    | шт                | 5          |                   | Венткамеры             |
| 74      | -обратный клапан, композитный материал, Ø50 мм   |                                                    |                                      |                    | шт                | 5          |                   |                        |
| 75      | -задвижка муфтовая 50 мм   |                                                    |                                      |                    | шт                | 5          |                   |                        |
| 76      | Погружной насос с закрытым рабочим колесом Н=10,0 м., Q=1,5 м3 /ч; U=3х380 В, N=1,1 кВт                                                                          |                                                    |                                      |                    | шт                | 1          |                   | Узел ввода водопровода |
| 77      | -обратный клапан, композитный материал, Ø50 мм   |                                                    |                                      |                    | шт                | 1          |                   |                        |
| 78      | -задвижка муфтовая 50 мм   |                                                    |                                      |                    | шт                | 1          |                   |                        |
| 79      | Манометр с трубкой Бурдона, NS100 Манометр с трубкой Бурдона NS 100 , нержавеющая сталь стандарт EN 837-1                                                        |                                                    |                                      |                    | шт                | 6          |                   |                        |
| 80      | Трёхходовой кран, Ø15   |                                                    |                                      |                    | шт                | 6          |                   |                        |
| 81      | Труба НПВХ Ø50   |                                                    |                                      |                    | м                 | 80         |                   |                        |
| 82      | Труба НПВХ Ø80   |                                                    |                                      |                    | м                 | 30         |                   |                        |
| 83      | Отвод НПВХ, 50 мм, 87 градусов   |                                                    |                                      |                    | шт                | 11         |                   |                        |
| 84      | Тройник НПВХ 50х50 87 градусов   |                                                    |                                      |                    | шт                | 2          |                   |                        |
| 85      | Переход НПВХ 50-80   |                                                    |                                      |                    | шт                | 2          |                   |                        |
| 86      | Узел гашения напора с врезкой в трубу SML   |                                                    |                                      |                    | шт                | 3          |                   |                        |
|         |   |                                                    |                                      |                    |                   |            |                   |                        |
