
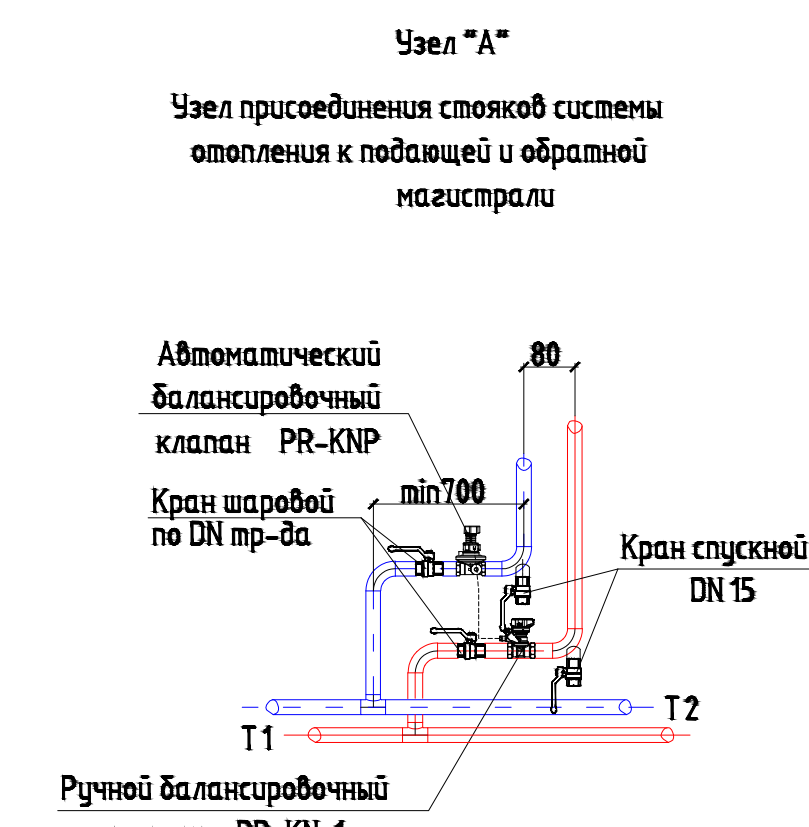



План технического этажа

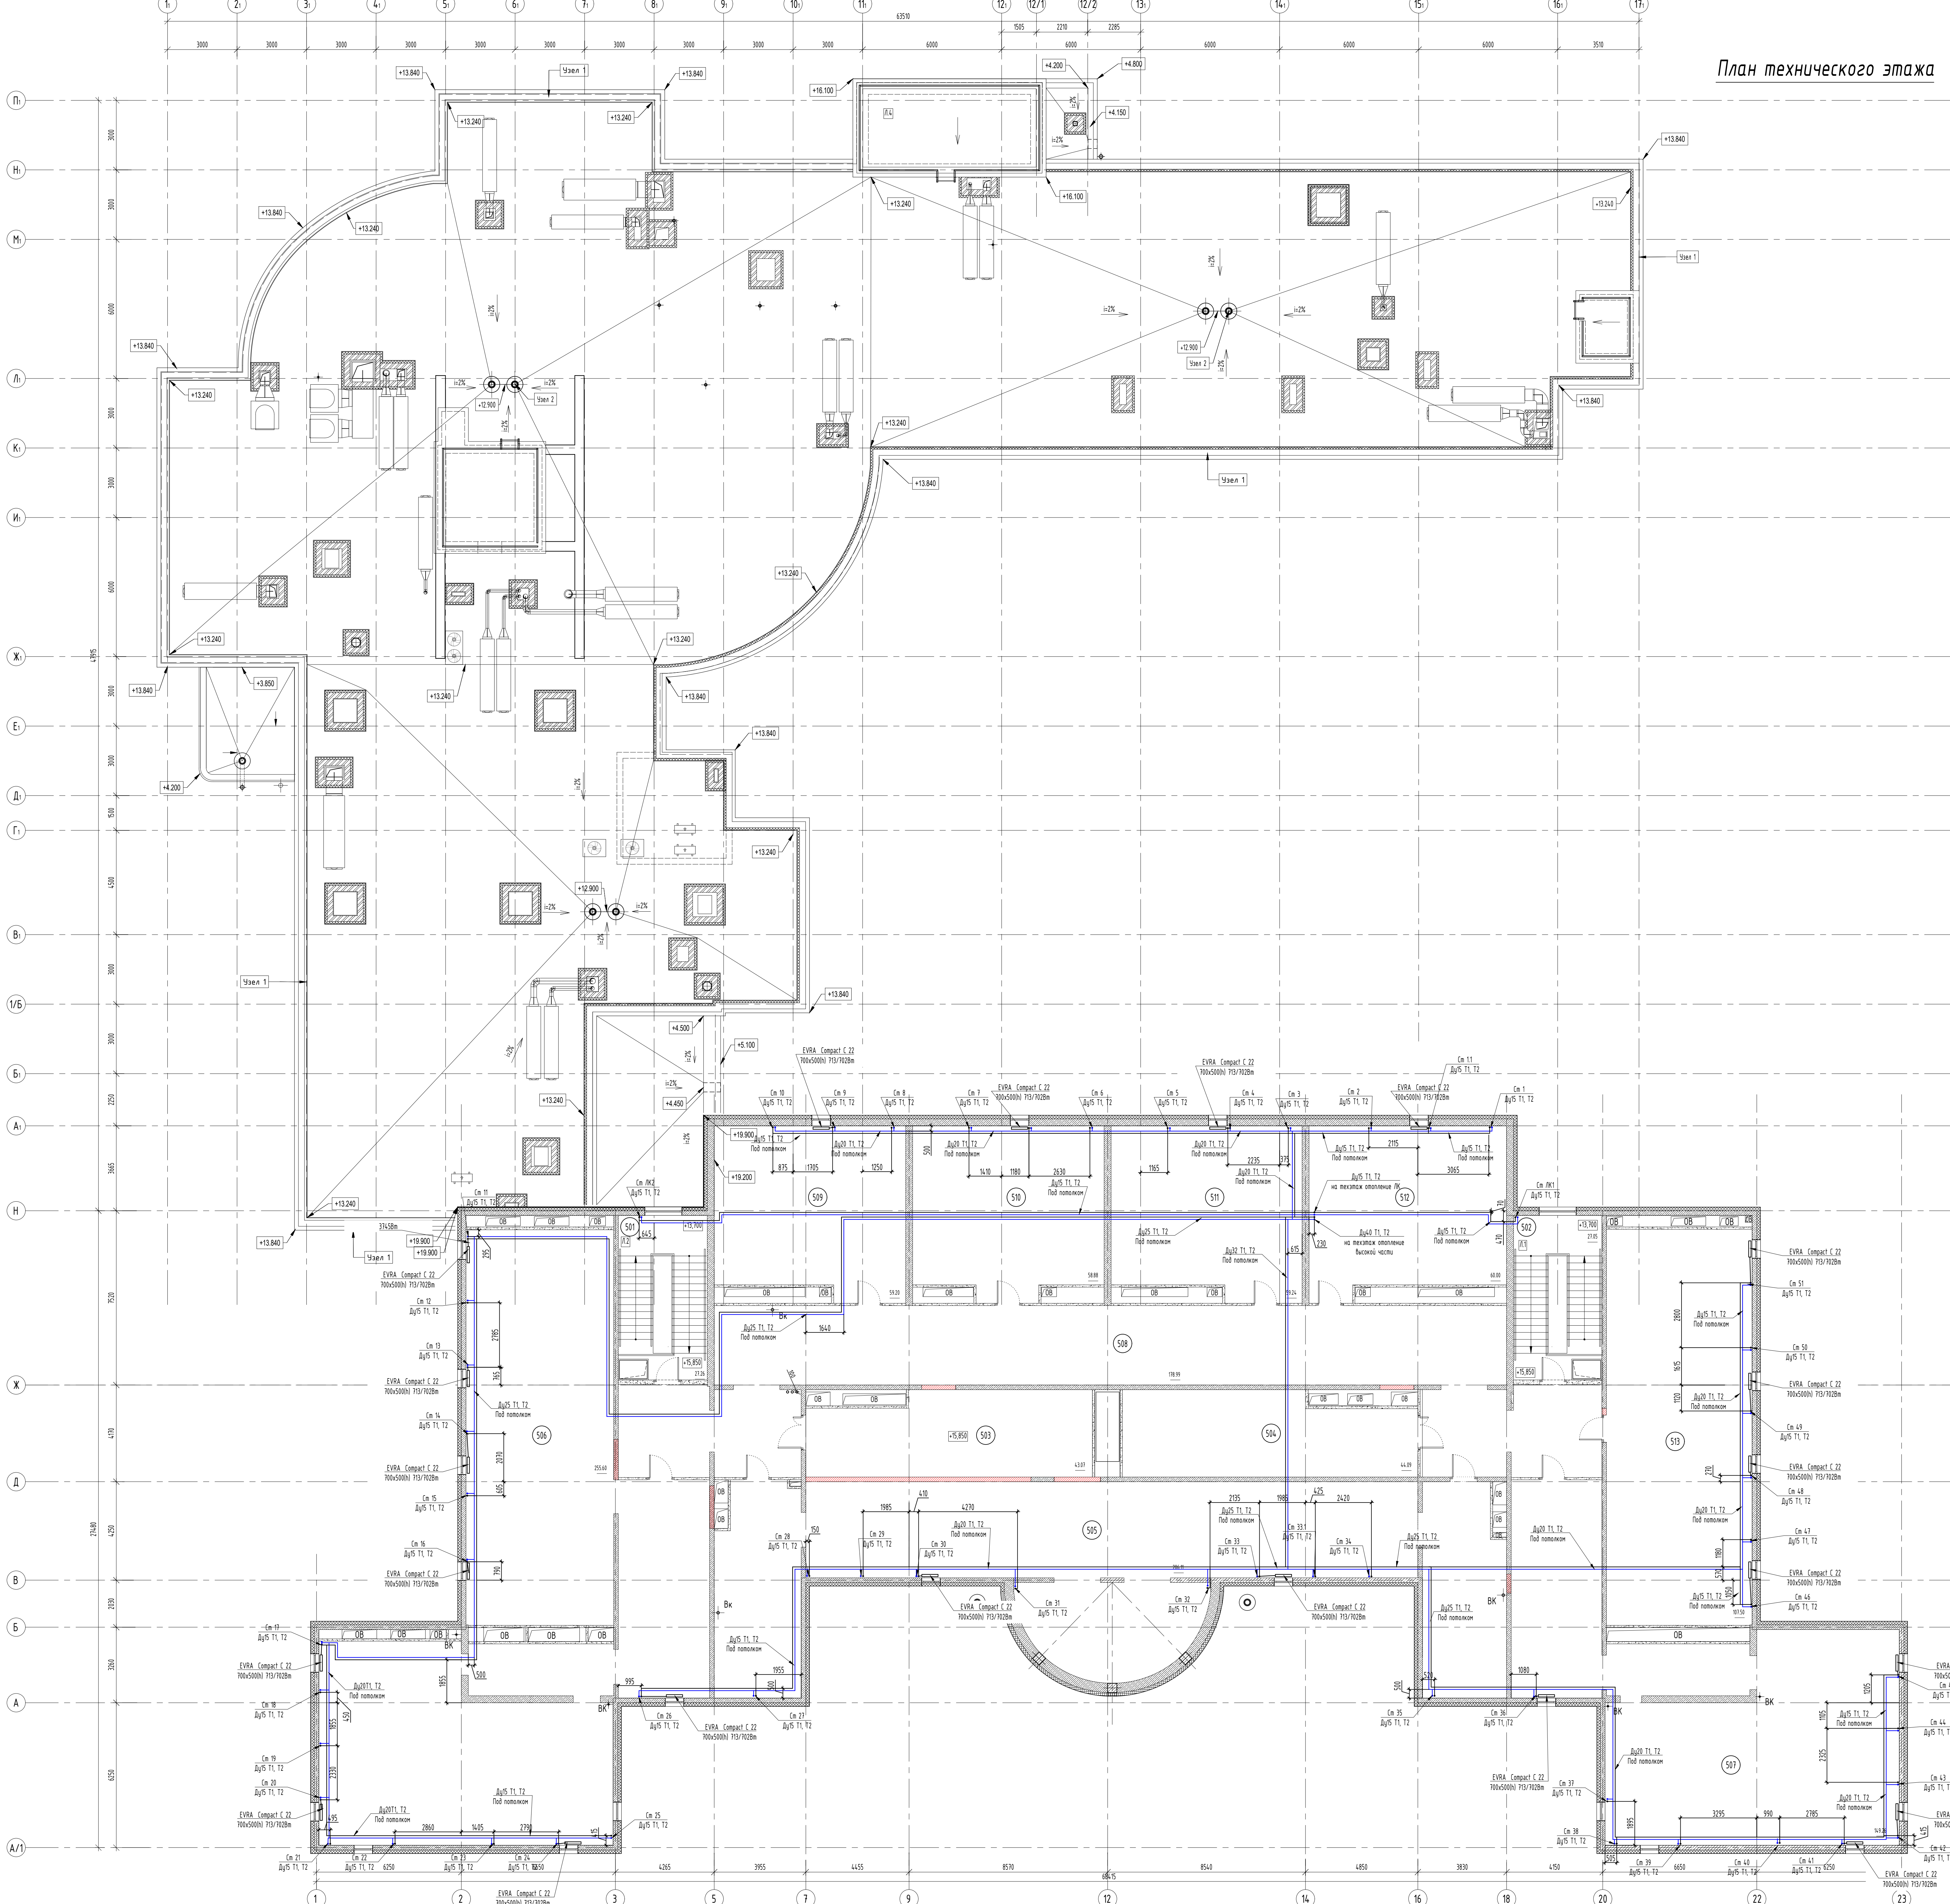

Условные обозначения:

- T11 — подающий трубопровод системы отопления ВГП
- T21 — обратный трубопровод системы отопления ВГП
- Автоматический воздухоотводчик
- Сливной кран
- Панельный радиатор
- Электрический кондектор
- ВТЗ (ТЭН)


Схема обвязки радиаторов с доковым подключением

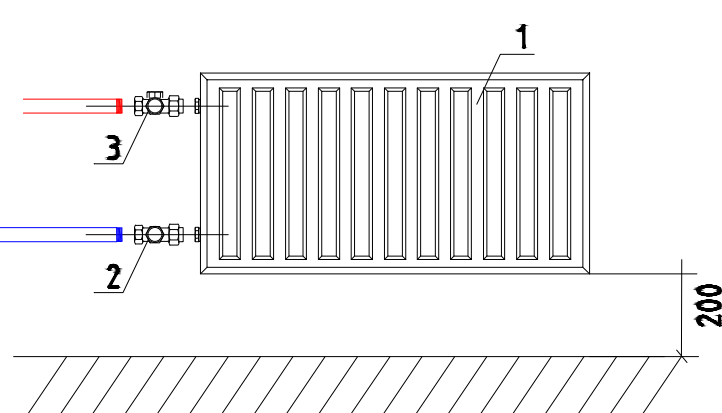

Спецификация оборудования

N	Наименование
1	Радиатор
2	Запорный радиаторный кран
3	Термостатический вентиль

Прокладка трубопроводов системы отопления через стены, перегородки и перекрытия

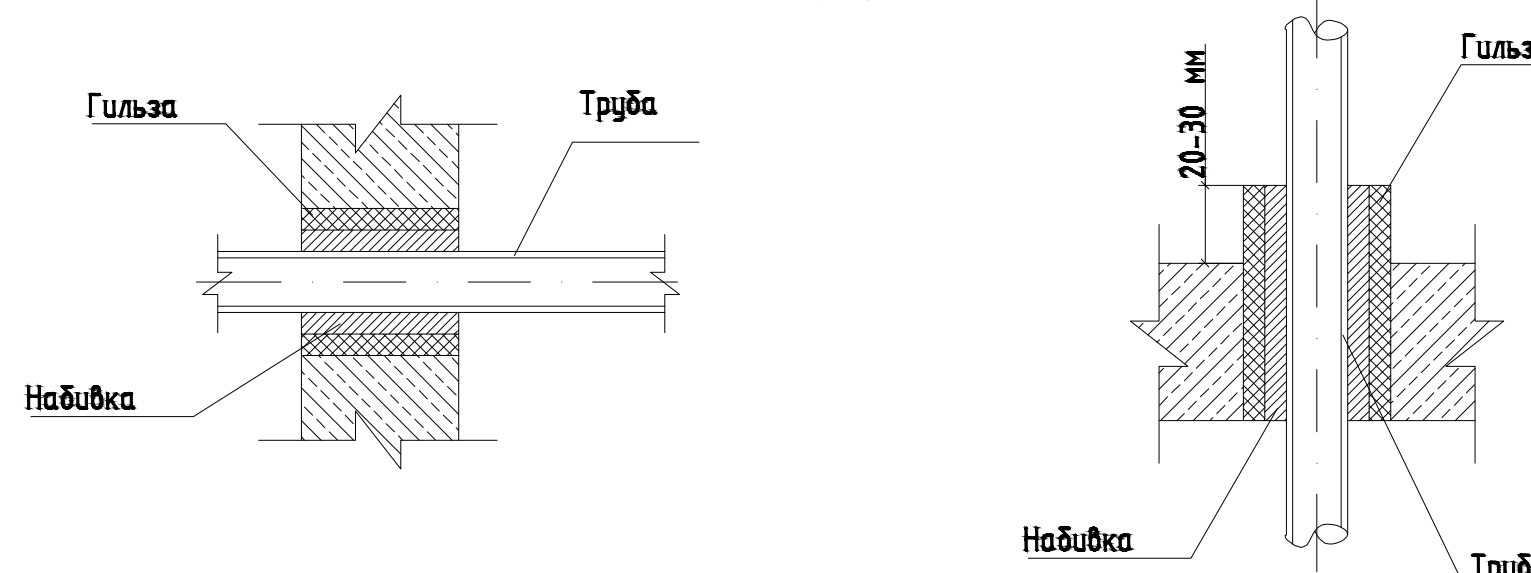

ПРИМЕЧАНИЕ:

- За условные отметки ±0,00 принята отметка уровня чистого пола 1 этажа.
- Все магистральные трубопроводы на теплотехнике прокладываются под потолком в теплоизоляции. Опуски к отопительным приборам не изолируются.
- Краны выложить в сторону стояков, сливные краны.
- В верхних точках установить воздухоотводчики, в нижних сливные краны.

					16-25/17-П-081		
					Капитальный ремонт объекта "ГБОУ Школа № 429 "Соколовая гора", расположенного по адресу: г.Москва, ул. Соколовой горы 5-я, д.14		
					Отопление		
					Страница	Лист	Листов
					Р	В	
					План технического этажа. М 1:100		
					АЗУРИТ		
					ФОРМАТ А0		