



Автоматический балансирующий клапан PR-KNP

Кран шаровый по DN 100-да

Кран спускной DN 15

min 700

80

T1 T2

Ручной балансирующий клапан DN 100-1

— T11 — подающий трубопровод системы отопления ВГП
— T21 — обратный трубопровод системы отопления ВГП

 -Автоматический воздухоподчик


 - Сливной кран

☐ -Панельный радиатор

 -Электрический конвектор

 -BT3 (TЭH)


Схема обвязки радиаторов с
боковым подключением

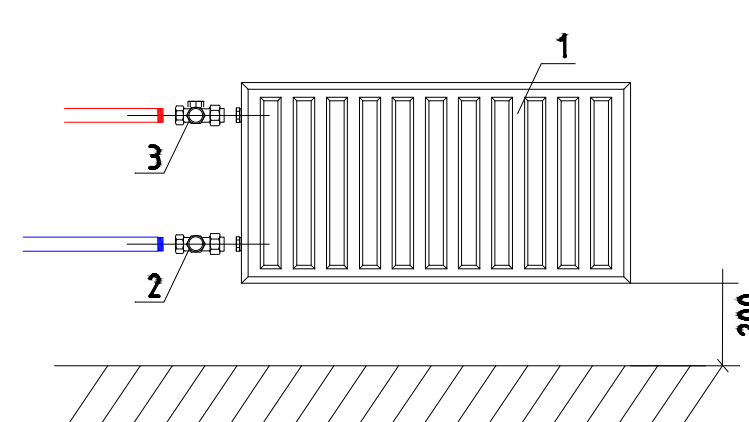

Спецификация оборудования

N	Наименование
1	Радиатор
2	Запорный радиаторный кран
3	Термостатический вентиль

Прокладка трубопроводов системы
отопления через стены, перегородки и
перекрытия

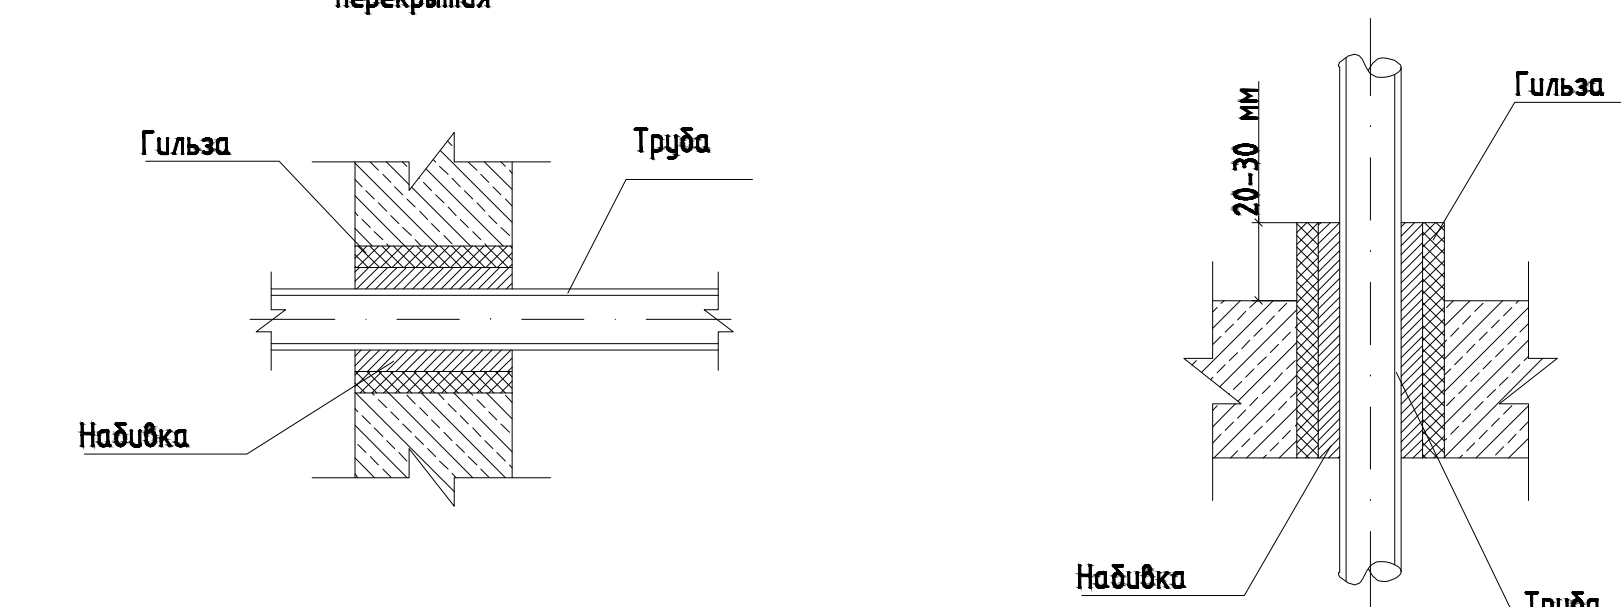

ПРИМЕЧАНИЕ:

1. За условную отметку $\pm 0,000$ принята отметка уровня чистого пола 1 этажа.
2. Все магистральные трубопроводы в подвале прокладываются открыто под наливком в теплоизоляции. Спуски к отопительным приборам не изолируются.
3. Склон выполняется в сторону стояков, сливных канав.
4. В верхних точках устанавливаются воздухоотводчики, в нижних сливные краны

					16-25/Г-П-081		
					Капитальный ремонт объекта "ТБОУ Школа № 429 "Скопальная гора", расположенное по адресу: г. Москва, ул. Скопальной горы 5-а, 8/14		
Изм.	Кол. экз.	Лист	№ док.	Подпись	Дата		
Разраб.		Литовских			2020.07.01		
						Исполнение	
						Страница	Лист
						Р	3
И. команд.	Губарева				2020.07.01		
Гендир.	Маркова				2020.07.01		
						План подвала. М 1:100	
						 АЗУРИТ	