

Ведомость рабочих чертежей основного комплекта

ОБЩИЕ УКАЗАНИЯ

Технические решения, принятые в настоящей рабочей документации, соответствуют заданию на разработку проектной документации, техническому заданию на разработку проектной документации, требованиям действующих технических регламентов, стандартов, сводов правил, других документов, содержащих установленные требования.

Рабочая документация разработана на устройство системы кабельного телевидения в рамках капитального ремонта общеобразовательного учреждения (ГБОУ "Школа № 429"), расположенного по адресу: г. Москва, 5-я ул. Соколиной Горы, д.14.

СИСТЕМА КАБЕЛЬНОГО ТЕЛЕВИДЕНИЯ

Для обеспечения услугами телевидения здания предусматривается установка эфирной антенны для приема эфирного телевидения, вещаемого в формате DVB-T2. Система предназначена для приема и доведения сигналов общероссийских обязательных общедоступных телеканалов, по которым транслируются (передаются) сообщения (сигналы) оповещения о чрезвычайных ситуациях.

На кровле объекта устанавливается приемная телевизионная антенна ДМВ диапазона EB45L TE. Направление антенны устанавливается на ТБ Останкино. Построение системы выполняется на базе оборудования «DiSat» (или аналог)

Для приема и распределения каналов СКТ в помещении серверной устанавливается базовая станция «Мини ГС» производства ООО «Корпорация ИнформТелеСеть». От головной станции подается сигнал в домовую распределительную сеть объекта.

Кабельная распределительная сеть обеспечивает передачу TV сигналов в полосе частот от 47 до 862 Мгц.

Магистральная сеть по зданию с применением магистрального кабеля РК 75-7-330нг(А)- LSL Tx, абонентская сеть выполнена кабелем Паракс РК 75-4.8-319нг(А)- LSL Tx.

В соответствии с федеральным законом №126-ФЗ «О связи» от 07.07.2003г., ст. 65, 66, при угрозе возникновения или при возникновении чрезвычайных ситуаций природного и техногенного характера, уполномоченные государственные органы имеют право на приоритетное использование любых сетей связи. Операторы связи должны предоставлять абсолютный приоритет всем сообщениям, касающимся безопасности человека на воде, на земле, в воздухе, космическом пространстве, а также сообщениям о крупных авариях, катастрофах, об эпидемиях, эпизоотиях и о стихийных бедствиях, связанным с проведением неотложных мероприятий в области государственного управления, обороны страны, безопасности государства и обеспечения правопорядка.

Принятые проектные решения соответствуют действующим нормам и правилам проектирования и строительства. При соответствующем монтаже сетей связи возможность механического повреждения проводников и установочного оборудования сводится к минимуму.

		Дата
		Подпись
		Фамилия
		И.отд.долж.
Взам. инв.№		
Подп. и дата		
Инв.№. подл.		

Лист	Наименование	Примечание
1	Общие данные	
2	Зона действия	
3	Условные графические обозначения	
4	Структурная схема	
5	Схема электропитания оборудования	
6	Подвал. План	
7	1 этаж. План расположения оборудования	
8	2 этаж. План расположения оборудования	
9	3 этаж. План расположения оборудования	
10	4 этаж. План расположения оборудования	
11	Тех этаж. План	
12	Кровля. План расположения оборудования	
13	Шкаф Мини ГС	

Ведомость ссылочных и прилагаемых документов

Обозначение	Наименование	Примечание
	Ссылочные документы	
ФЗ от 30.12.2009 г. N 384-ФЗ (ред. от 02.07.2013)	"Технический регламент о безопасности зданий и сооружений"	
СП 134.13330.2022	"Системы электросвязи зданий и сооружений. Основные положения проектирования"	
ГОСТ Р 21.703-2020	"Правила выполнения рабочей документации проводных средств связи"	
ГОСТ Р 21.101-2020	"Основные требования к проектной и рабочей документации"	
ГОСТ Р 31565-2012	"Кабельные изделия. Требования пожарной безопасности"	
ПУЭ изд. 7	"Правила устройства электроустановок"	
СП 76.13330.2016	"Электротехнические устройства"	
	Прилагаемые документы	
16-25//Г-Р-СКТ-СО	Спецификация оборудования, изделий и материалов	На 2 листах

						16-25//Г-Р-СКТ			
						Выполнение проектно-изыскательных работ на капитальный ремонт общеобразовательного учреждения (ГБОУ "Школа № 429"), расположенного по адресу: г.Москва, 5-я ул. Соколиной горы, д.14			
Изм.	Кол.уч.	Лист	Идок.	Подп.	Дата	Система кабельного телевидения	Стадия	Лист	Листов
Разраб.		Панфилов			06.26		Р	1	13
Проверил		Поляков			06.26				
						Общие данные			
Н.контр.		Воробьев			06.26				
ГИП		Маркова			06.26				

УСЛОВНЫЕ ОБОЗНАЧЕНИЯ

Библиотека №87

Пятёрочка

ЛумиКофе

Клуб Штандарт

МВД

Сбербанк

Горздрав

Ароматный мир

У Пальча

Винлаб

Всё для дома

Апартаменты

Столички

Галерея

Яндекс М

Школа №129, школьное здание


просп. Буденного

Учебный корпус по адресу:
г.Москва, 5-я улица Соколиной
Горы, 14

Согласовано					
Инд.№, подп.	Подп. и дата	Взам. инд.№.			
				Фамилия	Дата
				И.отд долж.	Подпись

							16-25//Г-Р-СКТ		
							Выполнение проектно-изыскательных работ на капитальный ремонт общеобразовательного учреждения (ГБОУ "Школа № 429"), расположенного по адресу: г.Москва, 5-я ул. Соколиной горы, д.14		
Изм.	Кол.уч.	Лист	Индок.	Подп.	Дата		Статья	Лист	Листов
Разраб.		Панфилов			06.26	Система кабельного телевидения	Р	2	
Проверил		Поляков			06.26				
Н.контр.		Воробьев			06.26	Зона Действия		АЗУРИТ	
ГИП		Маркова			06.26				

Условные обозначения

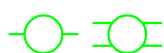


- Отвод тип ОТА на 2 и 4 направления



- Нагрузка согласованная 75 Ом

ДТА2Н

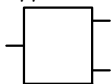

- делитель на 2 выхода



- Главная станция СКТ "Мини ГС"



- Радиорозетка СКТ в стену



- Кабель РК 75-4,8-319нз(А)-LSLTx (СКТ-А-XX) Абонентский



- Кабель РК 75-7-330нз(А)-LSLTx (СКТ-М-XX) Магистральный



- Кабель РК 75-7-330нз(А)-LSLTx (СКТ-П-XX) Приёмный



- Межэтажные проходки



- Лоток 200x50



- Лоток 400x50

Согласовано

	Дата
	Подпись
	Фамилия
	Н.отв.долж.

Взам. инв.№.

Подп. и дата

Инв.№. подл.

16-25//Г-Р-СКТ

Выполнение проектно-изыскательных работ на капитальный ремонт общеобразовательного учреждения (ГБОУ "Школа № 429"), расположенного по адресу: г.Москва, 5-я ул. Соколиной горы, д.14

Изм.	Кол.уч.	Лист	Ндоп.	Подп.	Дата
Разраб.		Панфилов			06.26
Проверил		Поляков			06.26
Н.контр.		Воробьев			06.26
ГИП		Маркова			06.26


Система кабельного телевидения

Стадия	Лист	Листов
Р	3	

Условные графические обозначения



АЗУРИТ

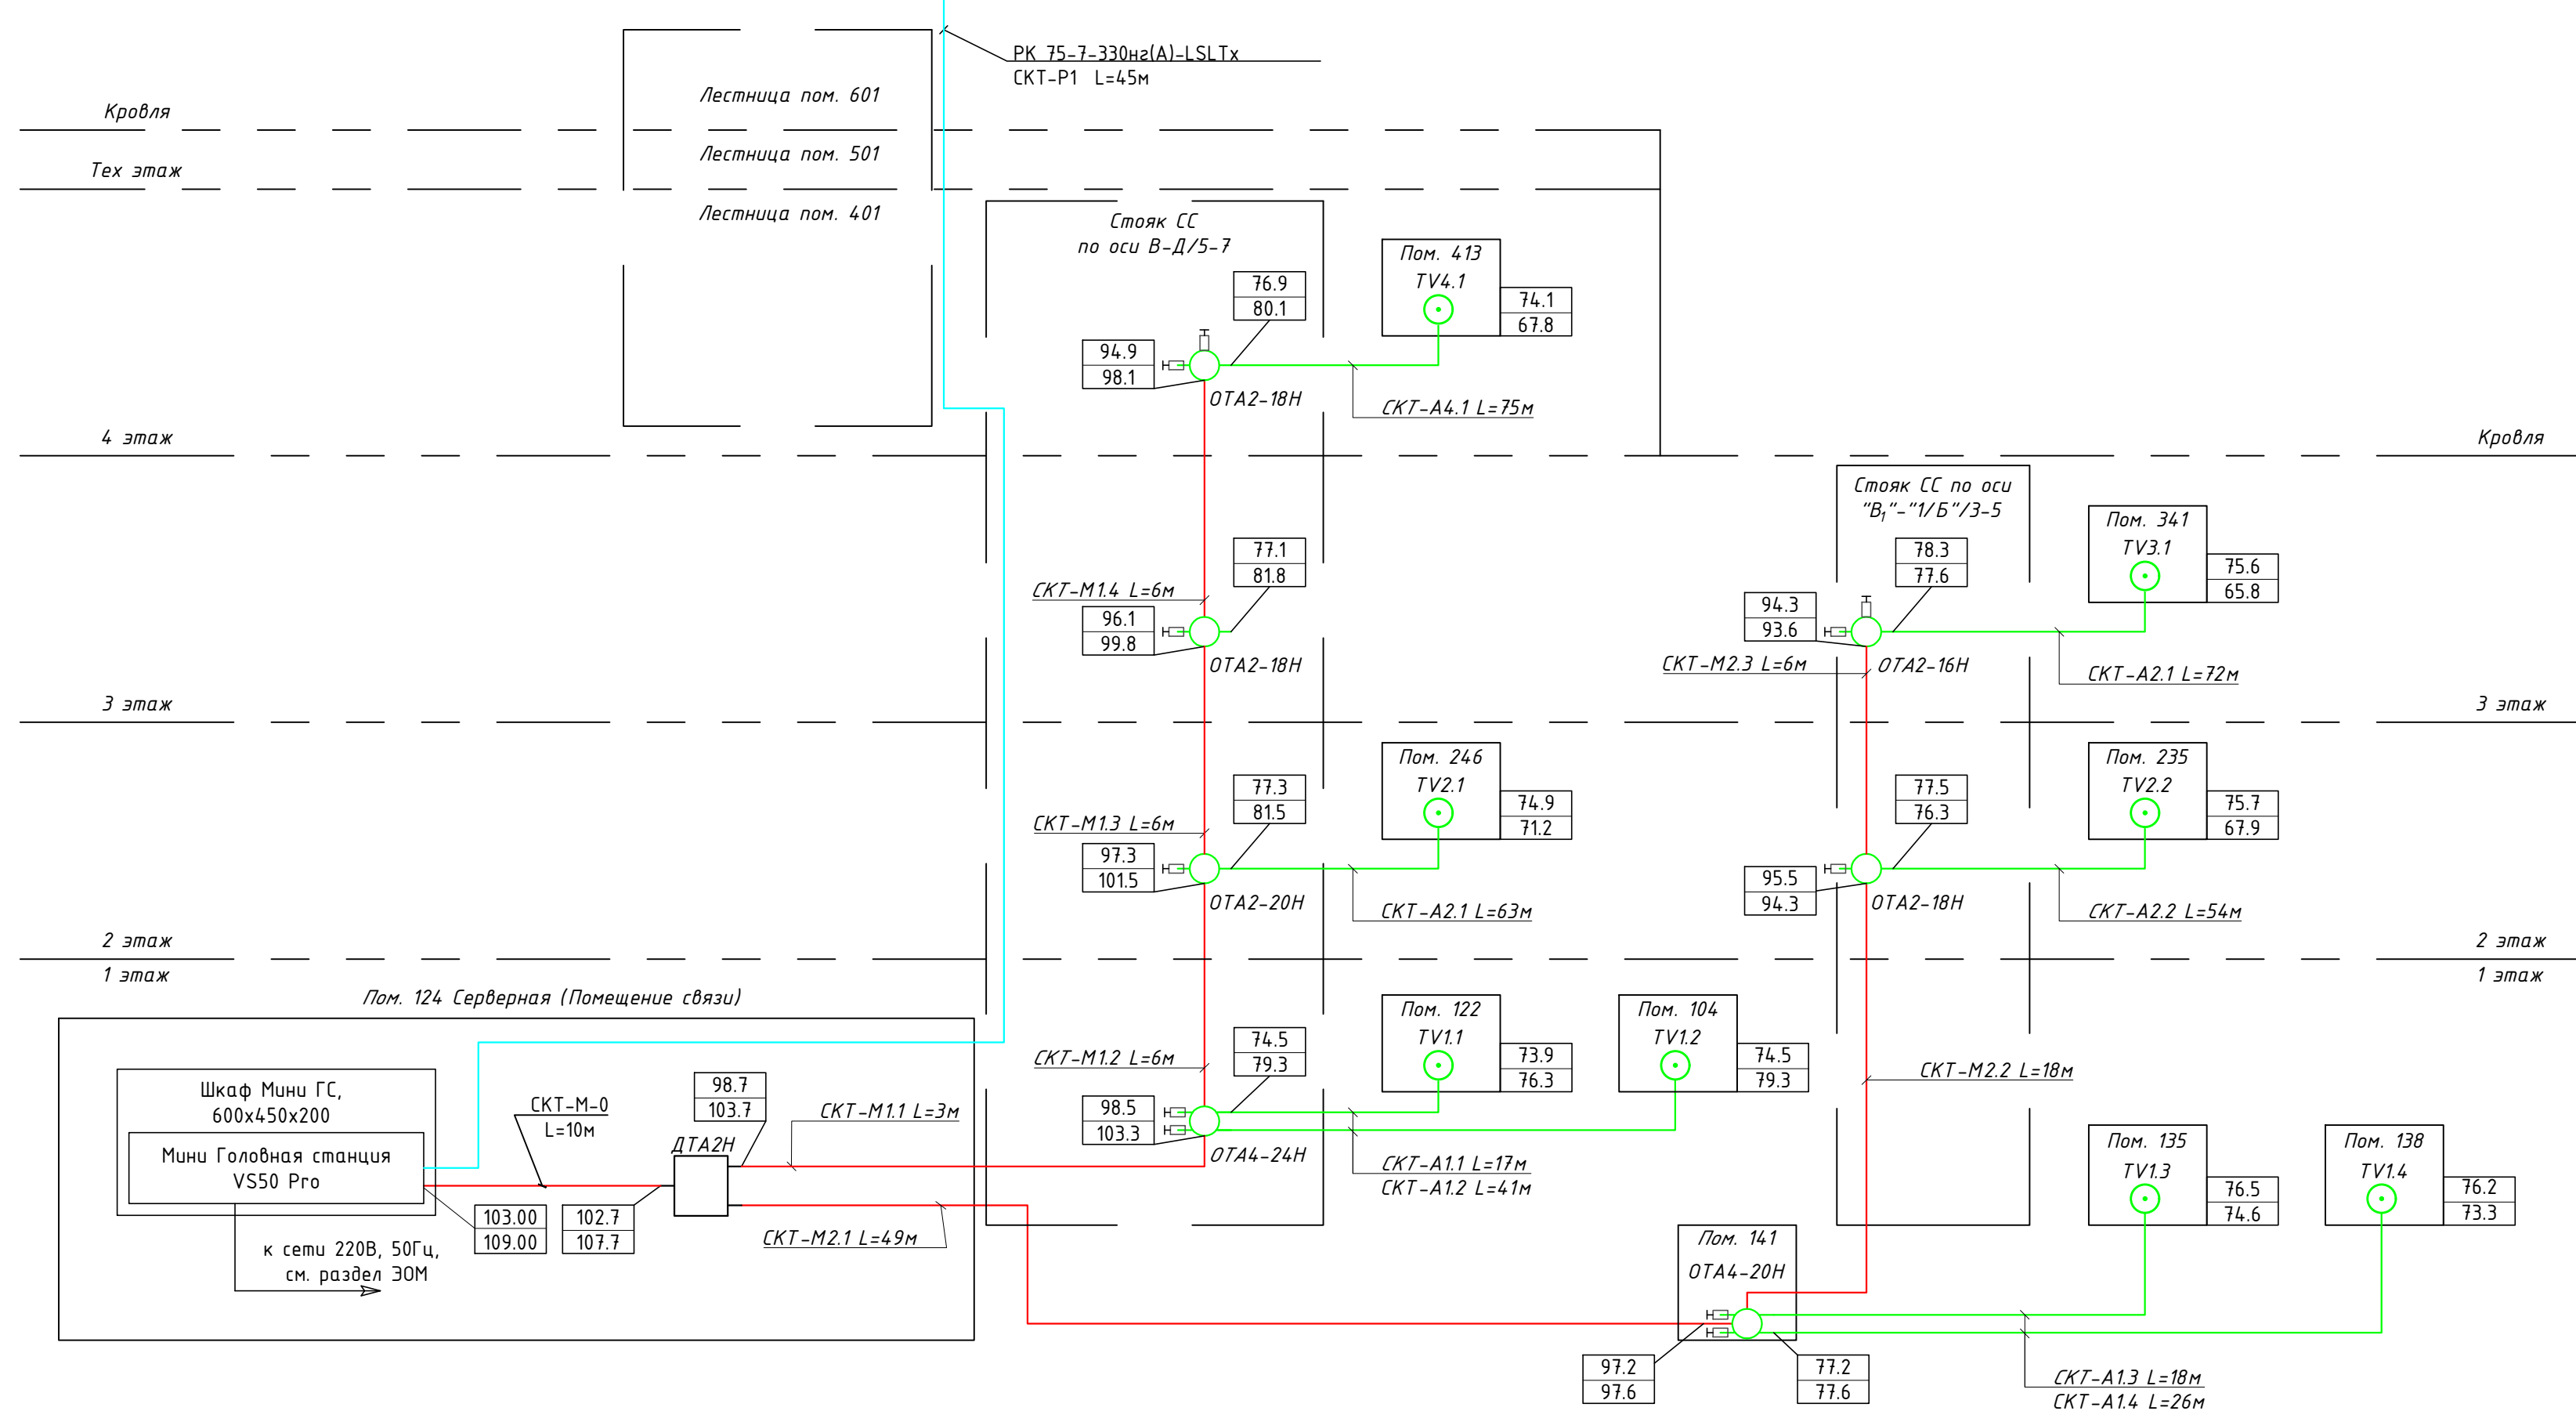


Примечание:

1. Установить в помещении серверной 124 на 1 этаже шкаф СКТ. ГС запрограммировать на частотный план согласно ТУ.
2. Расчет СКТ произведен из условий обеспечения уровней сигнала на абонентских отводах в пределах 72-84 дБмкВ и на абонентских ТВ розетках в пределах 60-80 дБмкВ.
3. Антенный усилитель АВ011 установить при недостаточном уровне сигнала на входе Мини-ГС менее 60.
4. Домовая распределительная сеть выполняется кабелем марки РК 75-7-330н(А)-LSLTx, абонентская РК 75-4,8-319н(А)-LSLTx.
5. В качестве абонентских устройств применяются ответвители типа ОТА серии "Н" на 2 и 4 отвода.
6. Ответвители устанавливаются в слаботочных стойках винтовым соединением.
7. Крепеж кабеля домовой распределительной сети в слаботочных шкафах осуществляется скобами не менее чем в двух точках.
8. Оконечные ТВ розетки устанавливаются в помещении согласно дизайн-проекта.
9. Все кабельные концы промаркировать в соответствии с типами подключаемых устройств.
10. Электропитание учтено смежным разделом ЭОМ.

- телевизионная розетка BRITE Розетка СКТ BR-A10-0-K01 с указанием номера этажа и порядкового номера
- кабель РК 75-7-330нз(А)-LSLTx (СКТ-Р1)
- кабель РК 75-7-330нз(А)-LSLTx (СКТ-М-XX)
- кабель РК 75-4,8-319 нз(А)-LSLTx (СКТ-А-XX)
- Отвод тип ОТА на 2 и 4 направления
- Нагрузка согласованная 75 Ом
- делитель на 2 выхода

						16-25//Г-Р-СКТ			
						Выполнение проектно-изыскательных работ на капитальный ремонт общеобразовательного учреждения (ГБОУ "Школа № 429"), расположенного по адресу: г.Москва, 5-я ул. Соколиной горы, д.14			
Изм.	Кол.уч.	Лист	Ивок.	Подп.	Дата	Система кабельного телевидения	Статья	Лист	Листов
Разраб.	Панфилов				06.26		Р	4	
Проверил	Поляков				06.26				
Н.контр.	Воробьев				06.26	Структурная схема		АЗУРИТ	
ГИП	Маркова				06.26				

Кроссовая (пом.137, 1 этаж)

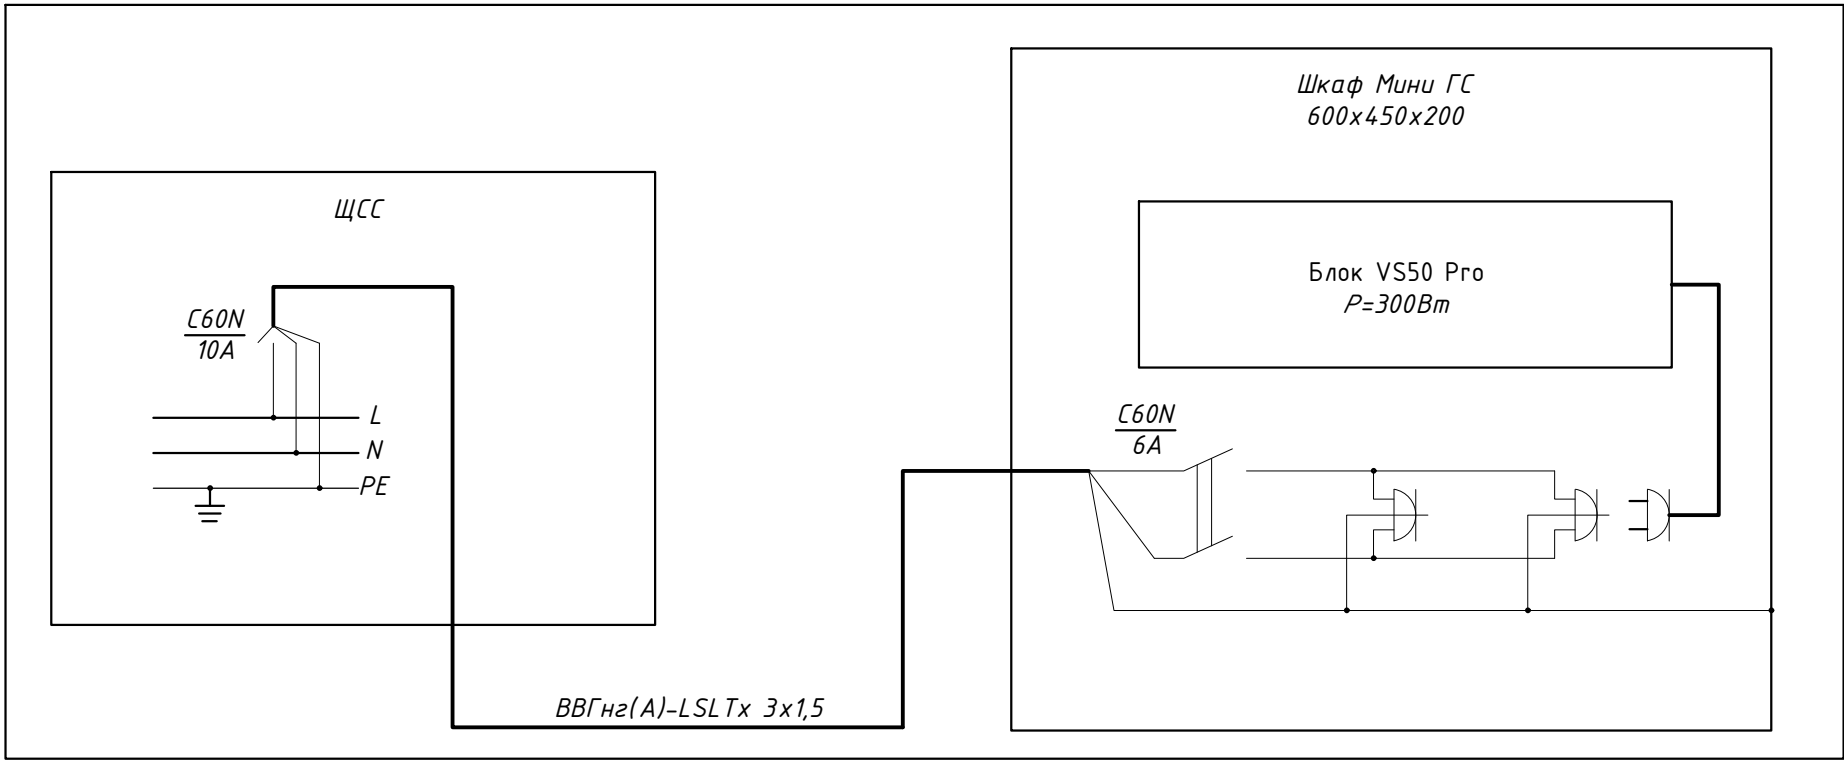


Все материалы для подключения оборудования к электроснабжению учтены в ЭОМ

						16-25//Г-Р-СКТ			
						Выполнение проектно-изыскательных работ на капитальный ремонт общеобразовательного учреждения (ГБОУ "Школа № 429"), расположенного по адресу: г.Москва, 5-я ул. Соколиной горы, д.14			
Изм.	Кол.уч.	Лист	Идок.	Подп.	Дата	Система кабельного телевидения	Стадия	Лист	Листов
Разраб.		Панфилов			06.26		Р	5	
Проверил		Поляков			06.26				
Н.контр.		Воробьев			06.26	Схема электрический соединений	 АЗУРИТ		
ГИП		Маркова			06.26				

Согласовано

Инв.№. подл.	Подп. и дата	Взам. инв.№.				
					Подпись	Дата

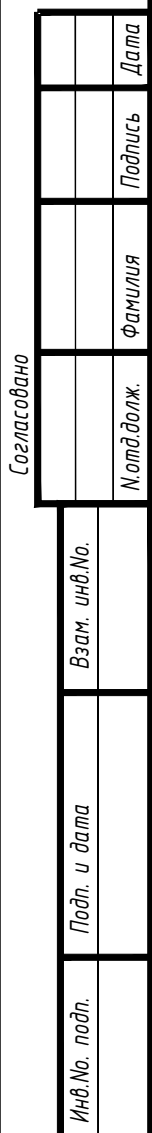


						16-25//Г-Р-СКТ
--	--	--	--	--	--	----------------

	Склад	Аванс	Аванс

	ρ	γ	
--	--------	----------	--


▲ АЗУРИТ

Figure 4.5

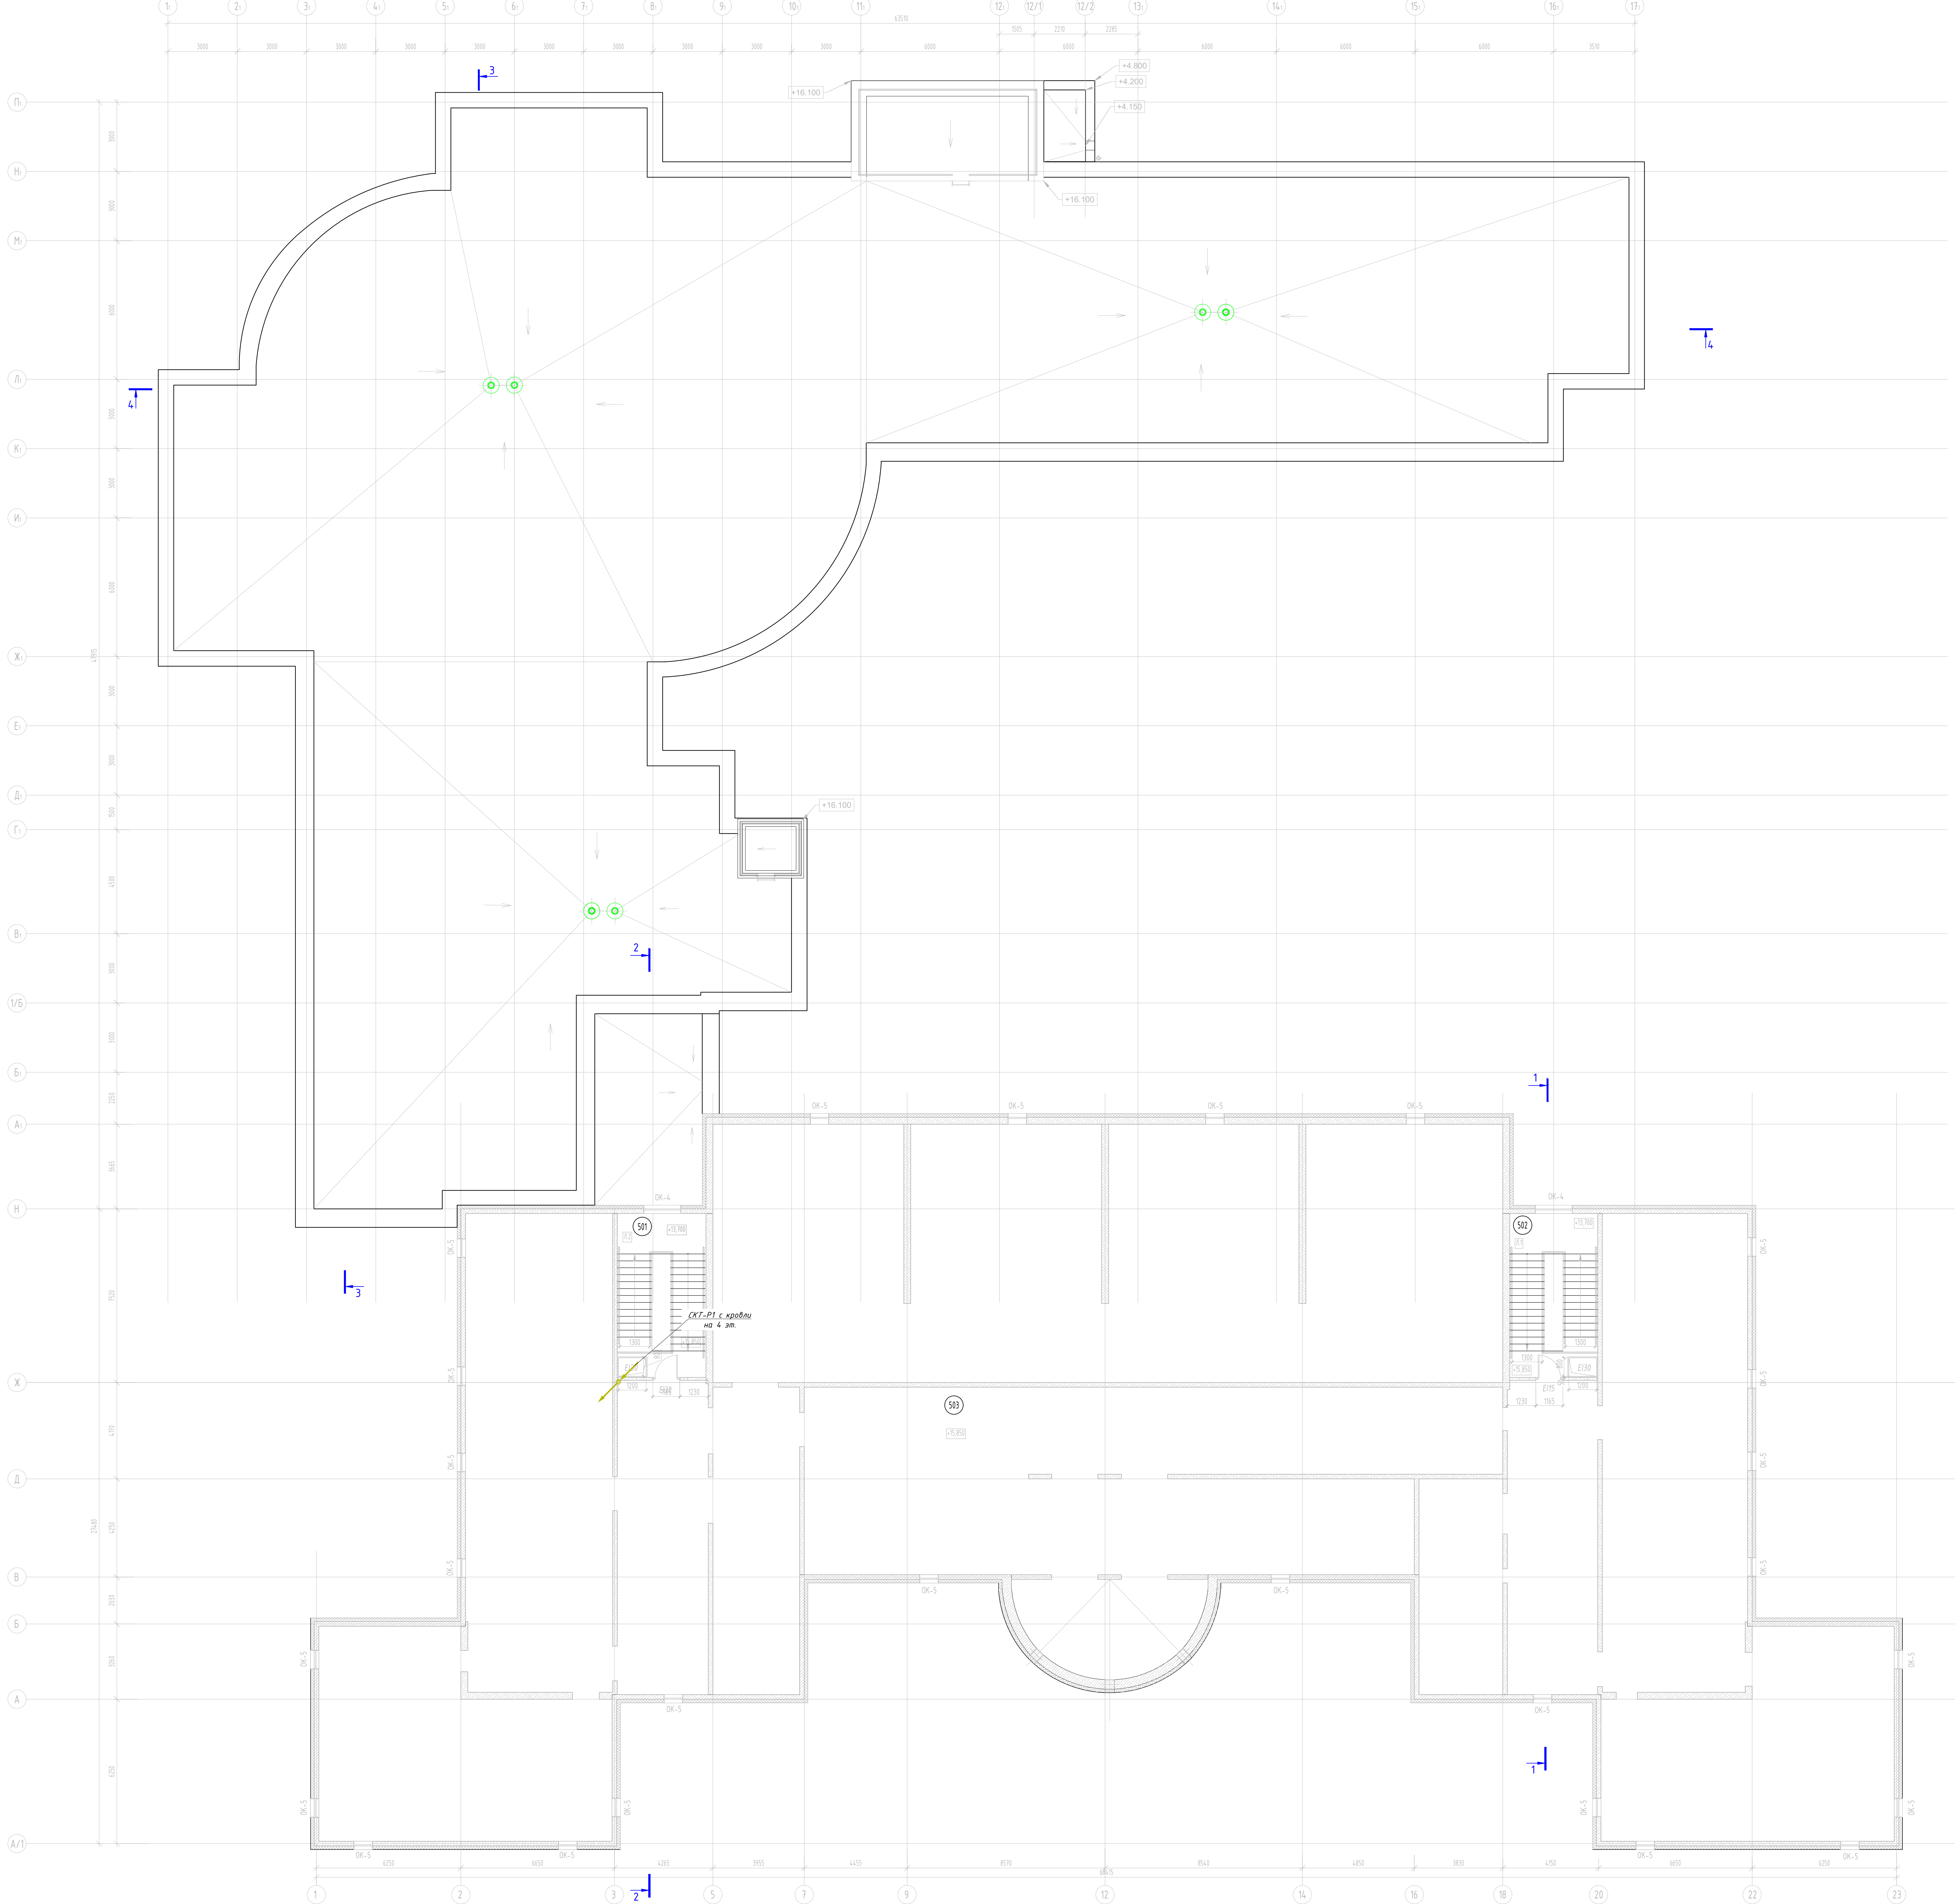

Экспликация помещений технического этажа

Номер помещения	Наименование	Площадь, м2	Кол. помещ.
501	Лестничная клетка Тип И2	28.81	
502	Лестничная клетка Тип И1	26.98	
503	Техническое помещение на этаж +15.825	1288.77	
	Всего	1344.6	

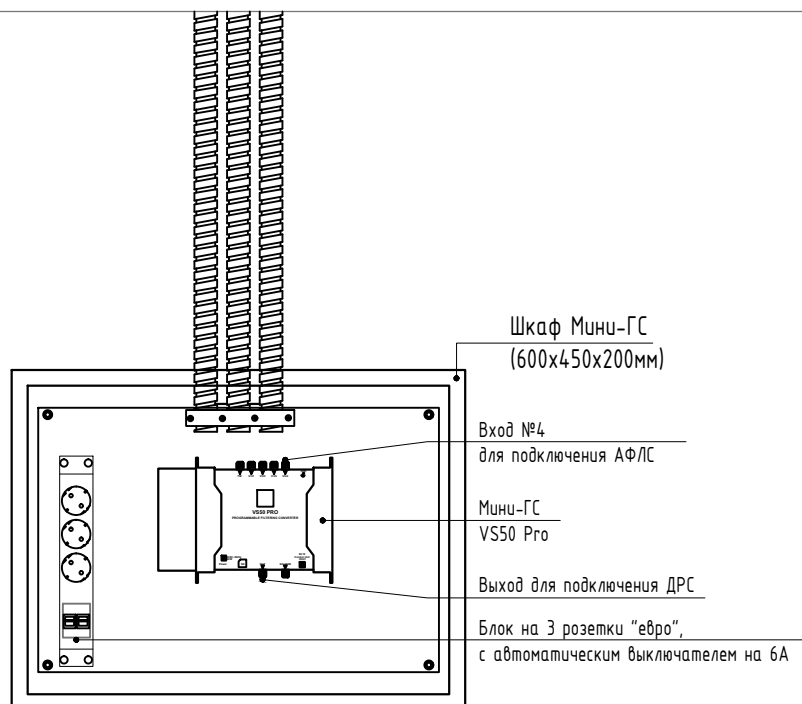

Взам. инв.№.

Подп. и дата

Инв.№. подп.

Мини ГС настроена на частотный план согласно ТУ ООО "Корпорация ИнформТелеСеть".

						16-25//Г-Р-СКТ			
						Выполнение проектно-изыскательных работ на капитальный ремонт общеобразовательного учреждения (ГБОУ "Школа № 429"), расположенного по адресу: г.Москва, 5-я ул. Соколиной горы, д.14			
Изм.	Кол.уч.	Лист	Ндок.	Подп.	Дата	Система кабельного телевидения	Стадия	Лист	Листов
Разраб.		Панфилов			06.26		Р	13	
Проверил		Поляков			06.26				
						Шкаф Мини ГС		АЗУРИТ	
Н.контр.		Воробьев			06.26				
ГИП		Маркова			06.26				