



АЗУРИТ

ООО ПСК «Азурит»

ИНН: 7722762829

Рег. № члена СРО

№ П-163-007722762829-0240

от 23.04.2019г. СРО АП «АПП»

Тел: 8 (495) 724-53-47

e-mail: info@psk-azurit.ru

Экз. №

Заказчик: "АНО «ОЭК Стройтрест»"

**«Капитальный ремонт общеобразовательного учреждения
(ГБОУ «Школа № 429»), расположенного по адресу: г. Москва, 5-ая ул.
Соколиной Горы д.14»**

РАБОЧАЯ ДОКУМЕНТАЦИЯ

Раздел "Технологические решения. Пищеблок"

1 этап

16-25/Г-Р – ТХ2

Изм.	№ док.	Подп.	Дата

Москва 2026



АЗУРИТ

ООО ПСК «Азурит»

ИНН: 7722762829

Рег. № члена СРО

№ П-163-007722762829-0240

от 23.04.2019г. СРО АП «АПП»

Тел: 8 (495) 724-53-47

e-mail: info@psk-azurit.ru

Экз. №

Заказчик: "АНО «ОЭК Стройтрест»"

**«Капитальный ремонт общеобразовательного учреждения
(ГБОУ «Школа № 429»), расположенного по адресу: г. Москва, 5-ая ул.
Соколиной Горы д.14»**

РАБОЧАЯ ДОКУМЕНТАЦИЯ

Раздел "Технологические решения. Пищеблок"

1 этап

16-25/Г-Р – ТХ2

Технический директор –
главный инженер

Главный инженер проекта



Н.А. Губарев

Г.Н. Неменов

Изм.	№ док.	Подп.	Дата

ВЕДОМОСТЬ РАБОЧИХ ЧЕРТЕЖЕЙ ОСНОВНОГО КОМПЛЕКТА ТХ

Лист	Наименование	Примечание
1	Общие данные	
2	Фрагмент плана 1-го этажа. Пищеблок	
3	Фрагмент плана 1-го этажа. Пищеблок. Подключение Эл	
4	Фрагмент плана 1-го этажа. Пищеблок. Подключение ВК	
5	Фрагмент плана 1-го этажа. Пищеблок. Подключение ОВ	

ВЕДОМОСТЬ ССЫЛОЧНЫХ И ПРИЛАГАЕМЫХ ДОКУМЕНТОВ

Обозначение	Наименование	Примечание
Прилагаемые документы		
16-25/Г-Р-ТХ2-СО	Спецификация технологического оборудования и мебели	на 13 листах

Настоящий проект выполнен в соответствии с действующими нормами и правилами /в том числе по пожарной безопасности.

Инженер-проектировщик ТХ  Волкова


ОБЩИЕ УКАЗАНИЯ

Подраздел «Технологические решения» по объекту “Капитальный ремонт общеобразовательного учреждения “ГБОУ «Школа № 429», расположенного по адресу: г. Москва, 5-ая ул. Соколиной горы д.14” разработан на основании утвержденного Задания на проектирование и в соответствии с действующими нормативными документами.


Рабочим проектом предусматривается оснащение в соответствии с функциональным назначением помещений.
Расстановка технологического оборудования и мебели, привязки необходимых коммуникаций, представлены на листах марки 16-25/Г-Р-ТХ2, а спецификация технологического оборудования и мебели со всеми техническими характеристиками – на листах марки 16-25/Г-Р-ТХ2-СО.

В процессе закупки набор и расстановка оборудования и мебели, а также привязки к инженерным коммуникациям могут быть откорректированы.


инв. №	подв.
инв. №	подп.
инв. №	подп.

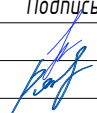						16-25/Г-Р-ТХ2					
						Капитальный ремонт общеобразовательного учреждения (ГБОУ «Школа № 429»), расположенного по адресу: г. Москва, 5-ая ул. Соколиной Горы д.14					
Изм	Кол.уч	Лист	№ док	Подпись	Дата	Технологические решения. Пищеблок	Стадия	Лист	Листов		
Разраб.		Волкова			2026.07		Р	1	5		
Проверил		Рябкова			2026.07						
Н. контр.		Гударев			2026.07	Общие данные					
ГИП		Неменов			2026.07						


Фрагмент плана 1 этажа. Пищедблок

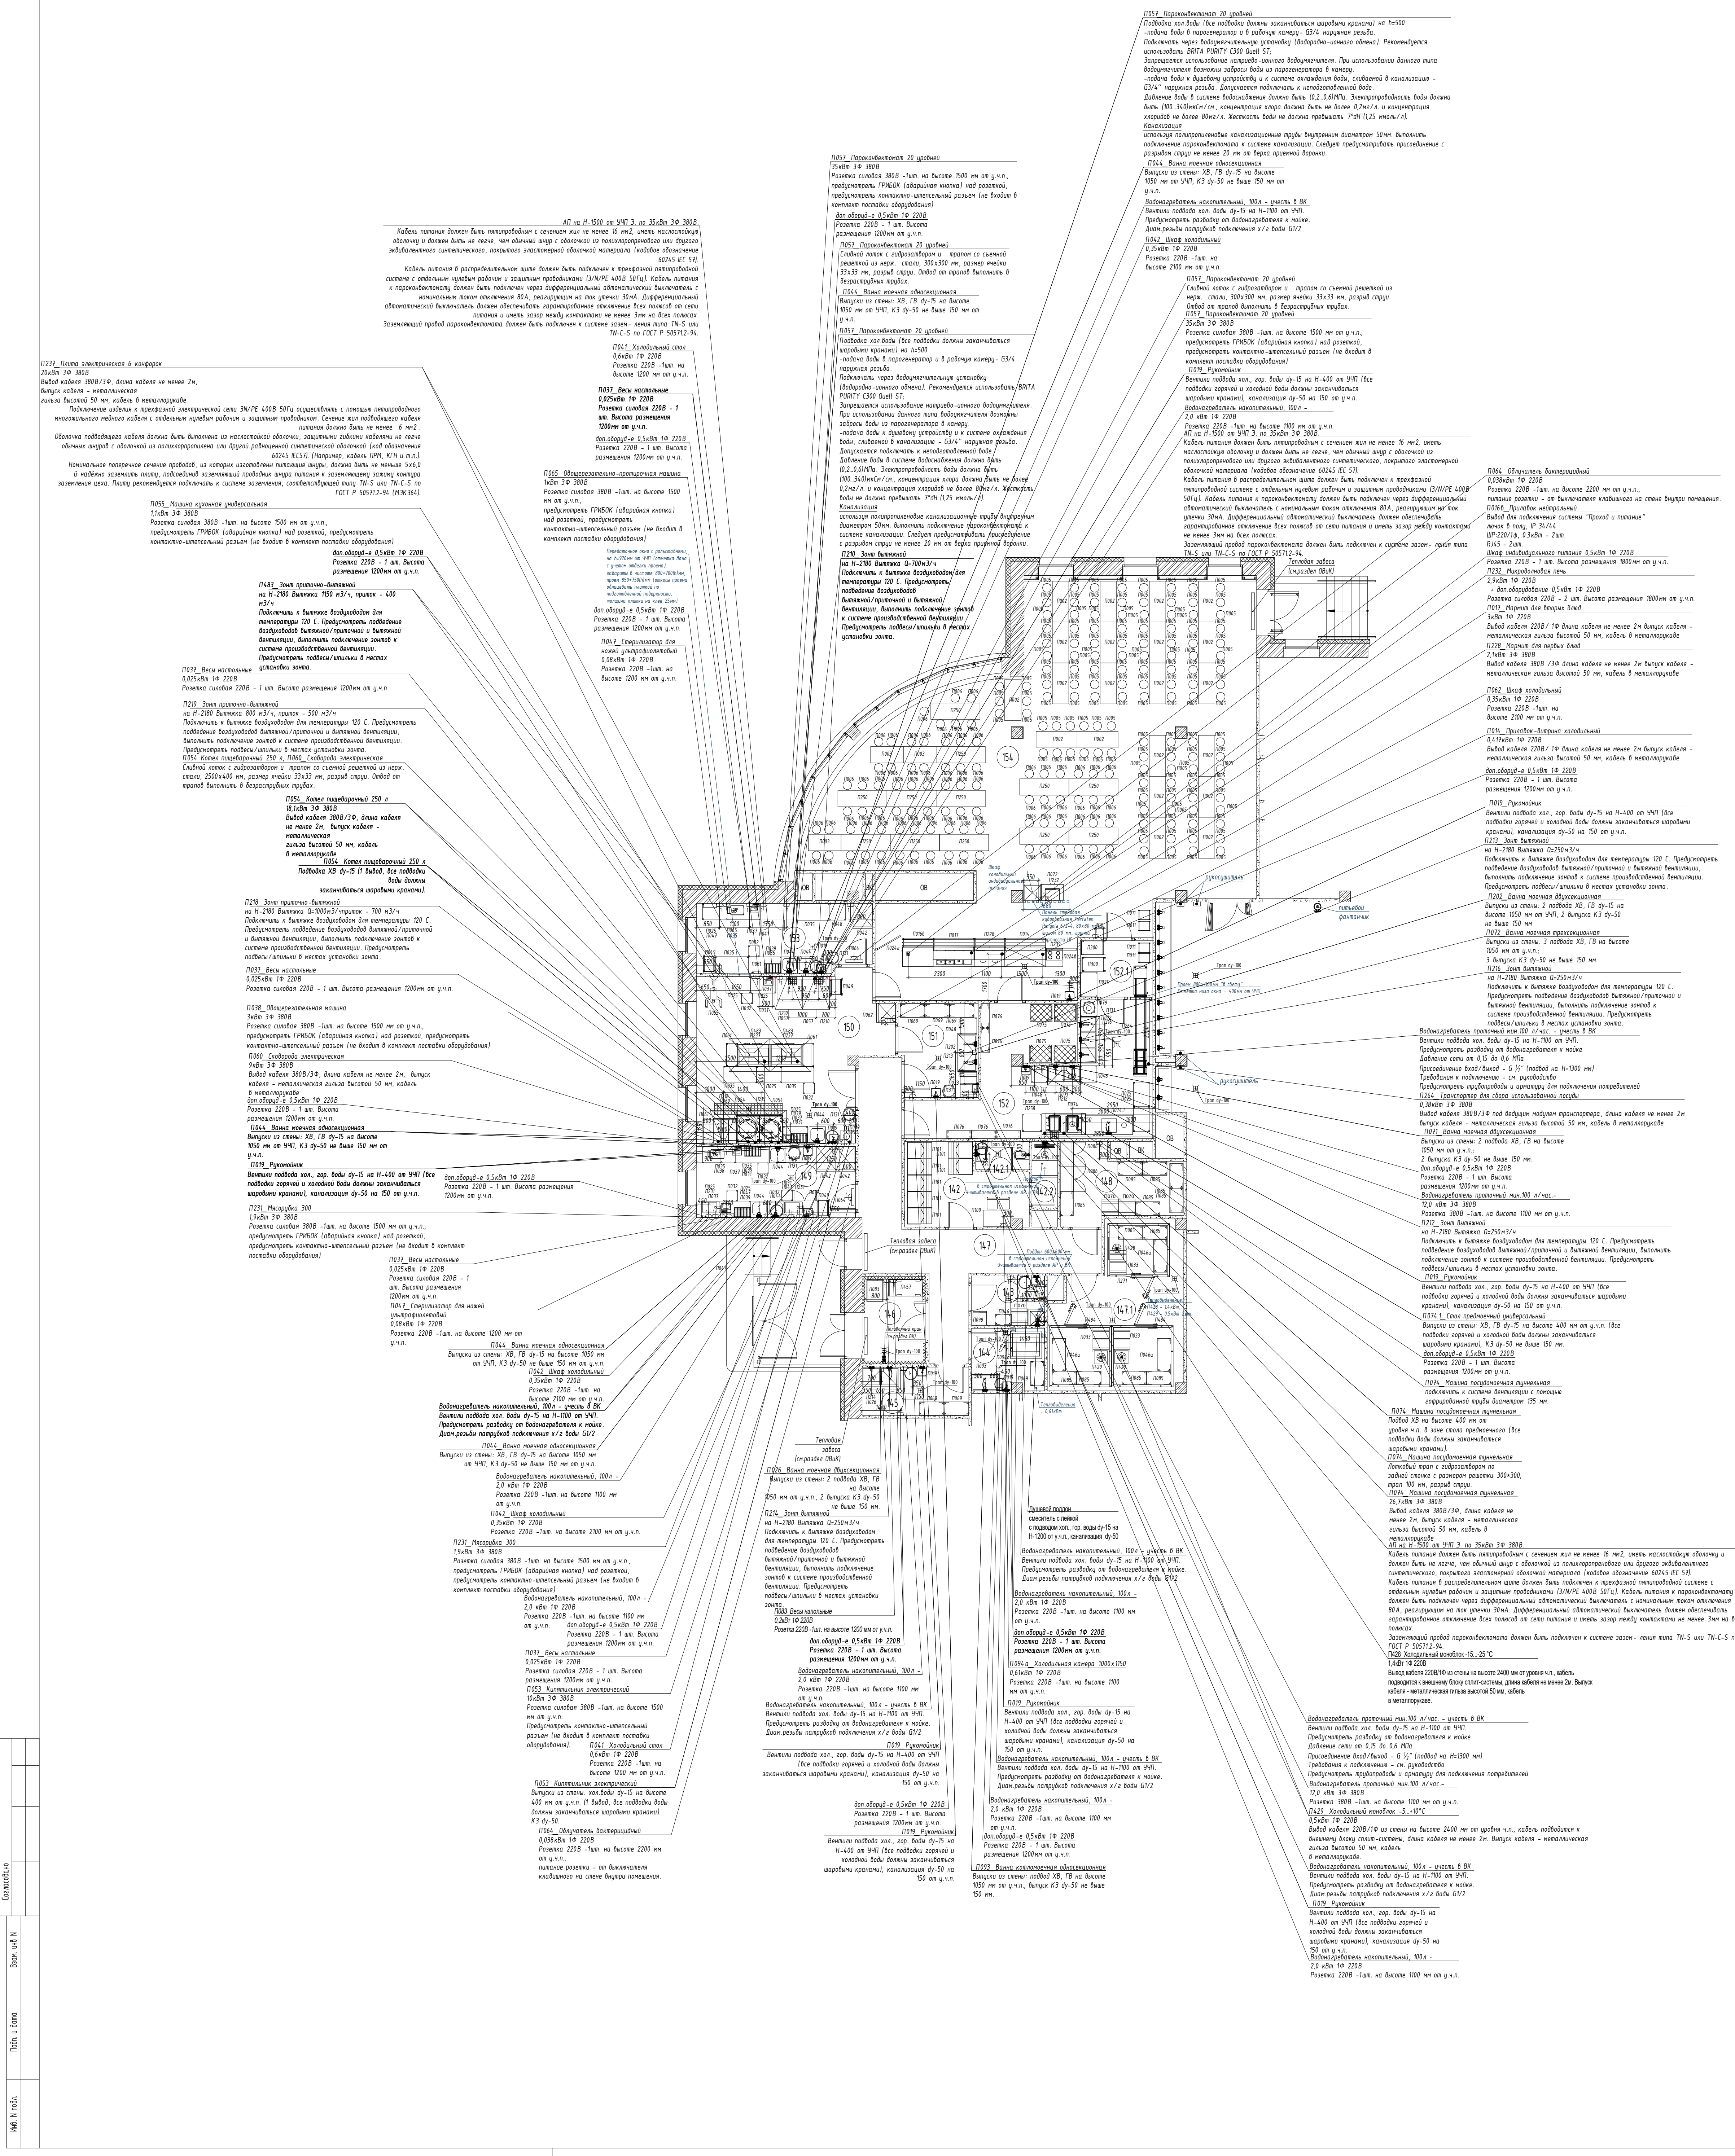

Фрагмент
Габаритный размеры и высоты козырька

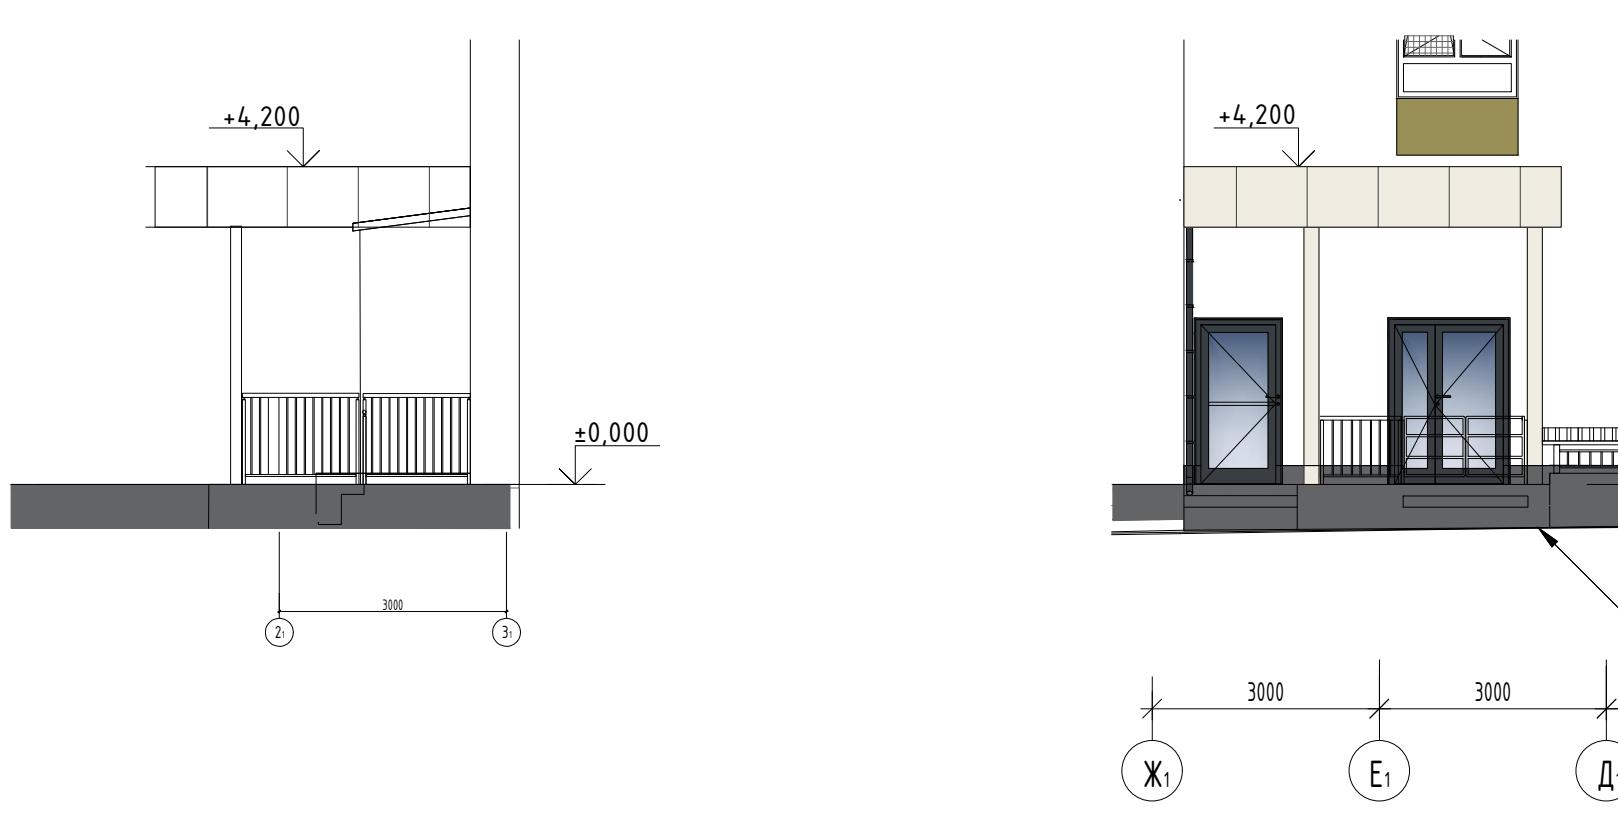


Фрагмент
Коридор с местом установкой
холодильного оборудования пом.14.71
разрез 1-1

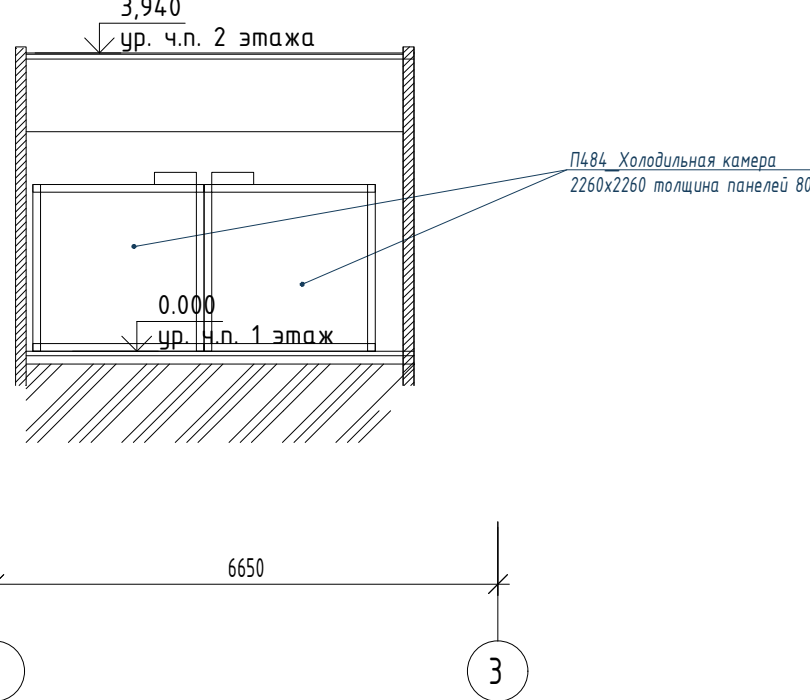


Экспликация помещений 1-го этажа

Номер помещения	Наименование	Площадь м2	Кат. помещения
14.2	Помещение для персонала	11,87	
14.2.1	Санузлы для персонала	2,01	
14.2.2	Душевая	2,29	
14.3	Г/УМ	4,85	В.4
14.4	Помещение для временного хранения пищевых отходов	6,01	В.4
14.5	Кладовая и мясная оборотная тары	6,92	В.4
14.6	Засушечный цех	7,45	В.4
14.7	Коридор	28,66	
14.7.1	Помещение с холодильным оборудованием	26,78	В.3
14.8	Кладовая сухих продуктов	10,81	В.3
14.9	Доготовочный цех	15,16	В.3
15.0	Горячий цех	39,25	В.3
15.1	Мясная для кухонной посуды	9,75	Д
15.2	Мясная для столовой посуды	34,78	Д
15.3	Предмечная	5,48	Д
15.4	Холодный цех	15,96	В.3
15.5	Обеденный зал	178,91	

Фрагмент
Габаритный размеры и высоты козырька

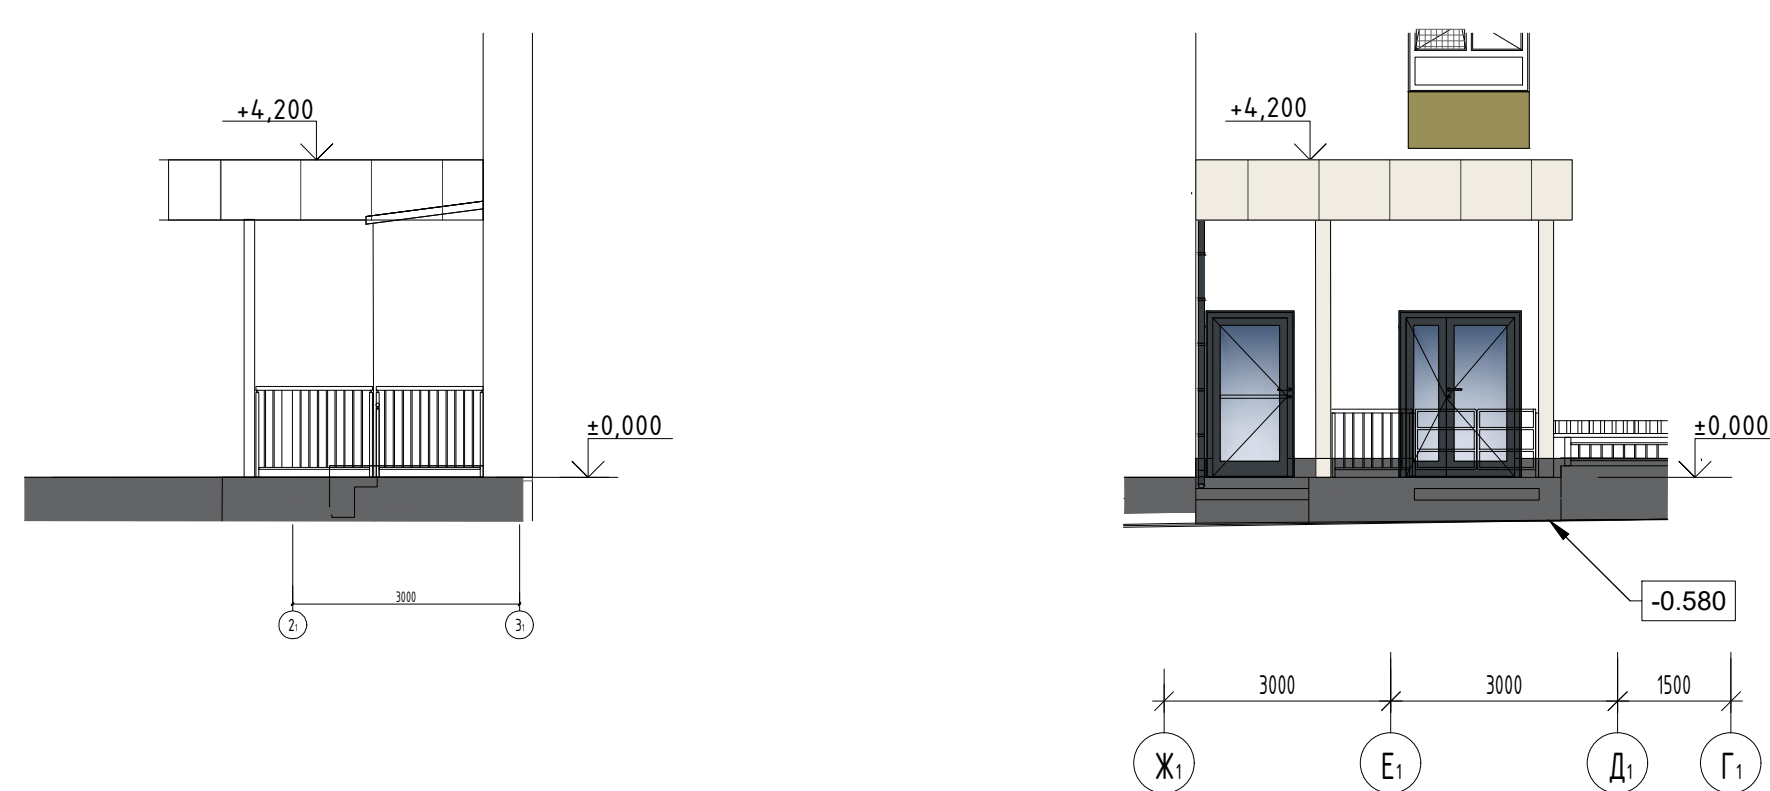


Фрагмент
Коридор с местом установки
холодильного оборудования пом.14.7.1
разрез 1-1

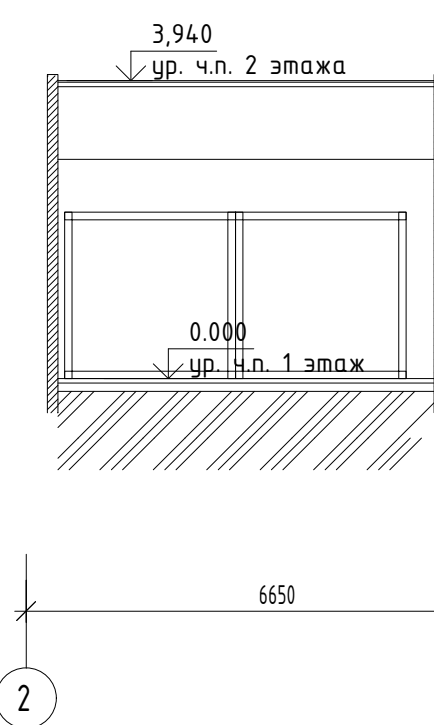


Экспликация помещений 1-го этажа

Номер помещения	Наименование	Площадь	Класс помещения
142	Помещение для персонала	1187	
142.1	Санузлы для персонала	2,01	
142.2	Душевая	2,29	
143	ПМ	4,85	В4
144	Помещение для временного хранения пищевых продуктов	6,01	В4
145	Кладовая и моечная оборотной тары	6,92	В4
146	Защитный цех	7,45	В4
147	Коридор	28,66	
147.1	Помещение с холодильным оборудованием	26,28	В3
148	Кладовая сухих продуктов	10,81	В3
149	Доголовоный цех	15,16	В3
150	Горячий цех	39,25	В3
151	Моечная для кухонной посуды	9,75	Д
152	Моечная для столовой посуды	34,78	Д
152.1	Предмоечная	5,48	Д
153	Холодный цех	15,96	В3
154	Обеденный зал	176,91	

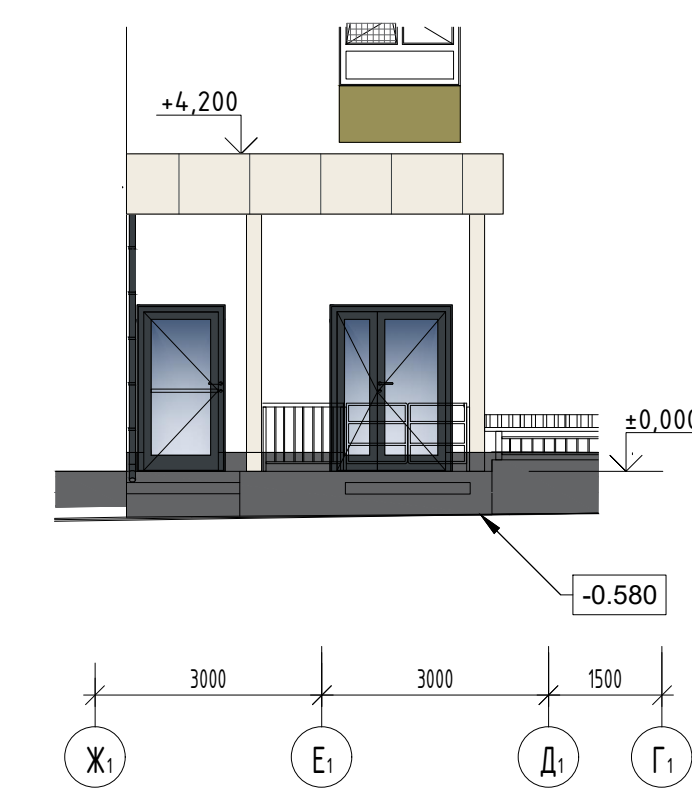

Номер помещения	Наименование	Площадь м2	Кол-во помещений
142	Помещение для персонала	11,87	
142.1	Санузел для персонала	2,01	
142.2	Душевая	2,29	
143	ПМ	4,85	В4
144	Помещение для временного хранения пищевых отходов	6,01	В4
145	Кладовая и моечная оборотной тары	6,92	В4
146	Смывочный цех	7,45	В4
147	Коридор	28,66	
147.1	Помещение с холодильным оборудованием	26,18	В3
148	Кладовая сухих продуктов	10,81	В3
149	Доголобный цех	15,16	В3
150	Горячий цех	39,25	В3
151	Моечная для кухонной посуды	31,53	В3
152	Моечная для столовой посуды	34,78	В3
152.1	Предмоечная	5,48	В3
153	Холодный цех	15,96	В3
154	Обеденный зал	178,91	

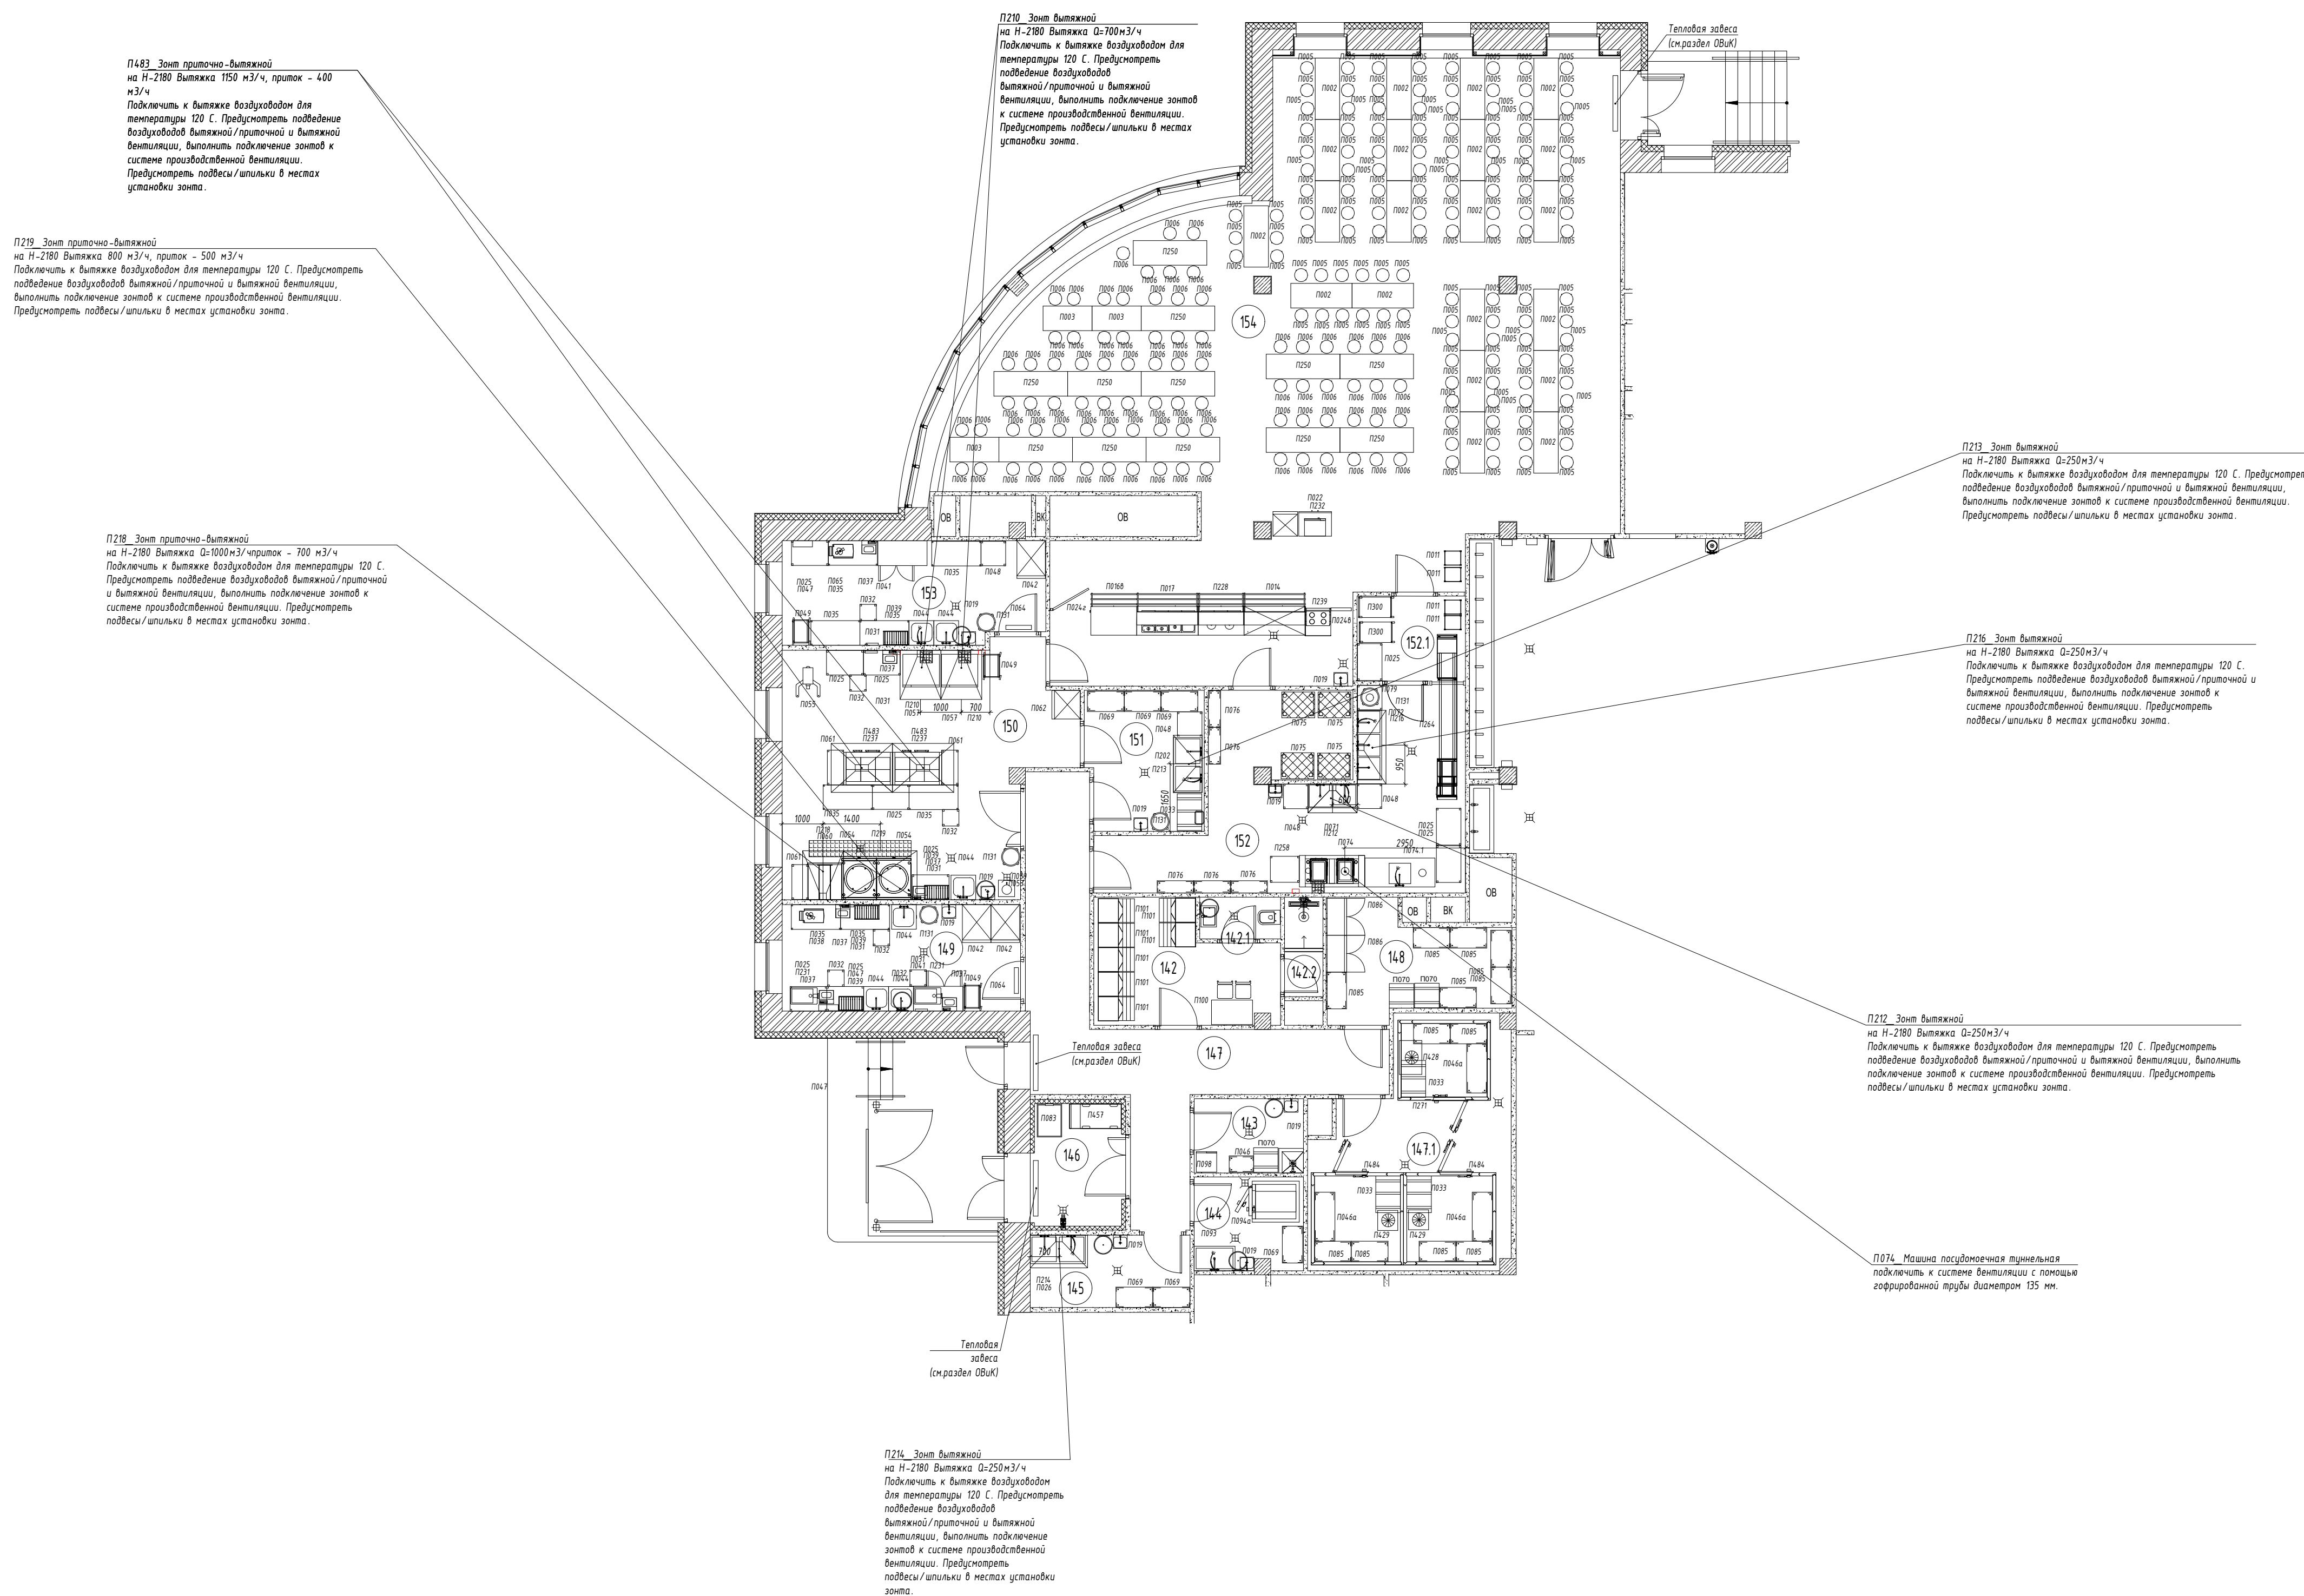

Согласовано

Изм. № подл.

Подп. и дата

Взам. инв. №

№ пом. в ГЧ	Помещение	Кол-во пом	№ поз. в ГЧ	Наименование	Ед. изм.	Кол-во	Марка оборудования	длина	ширина	высота	кВт	Ф	В	Примечание
154	Обеденный зал	1	П002	Стол обеденный школьный № 4, 1500х600	шт.	21		1500	600					
154	Обеденный зал	1	П003	Стол обеденный школьный № 5, 1200х600	шт.	3		1200	600					
154	Обеденный зал	1	П250	Стол обеденный школьный № 5, 1800х600	шт.	12		1800	600					
154	Обеденный зал	1	П005	Табурет №4	шт.	126								
154	Обеденный зал	1	П006	Табурет №5	шт.	84								
154	Обеденный зал	1	б/н	Шторы рулонные тип 1	к-т	9								штора на окно прямое - 1410*2600мм 3шт.; штора на полукруглый витраж 2000*2600мм 6шт.
154	Обеденный зал.	1	П300	Тележка для сбора посуды	шт.	2	ТСП-80/50, Кобор	800	500	940				
154	Обеденный зал.	1	П011	Тележка-шпилька для подносов	шт.	4	ШП-48/31, Кобор	310	480	1760				
154	Обеденный зал	1	П017	Мармит для вторых блюд тип 2	шт.	1	ЭМК-70КМ-01	1500	1030	1482	3	1	220	Вывод кабеля 220В/ 1Ф длина кабеля не менее 2м выпуск кабеля - металлическая гильза высотой 50 мм, кабель в металлорукаве
154	Обеденный зал	1	П228	Мармит для первых блюд тип 1	шт.	1	ПМЭС-70КМ, Абат	1120	705 (1030)	1240	2,1	3	380	Вывод кабеля 380В /3Ф длина кабеля не менее 2м выпуск кабеля - металлическая гильза высотой 50 мм, кабель в металлорукаве
154	Обеденный зал	1	П014	Прилавок-витрина холодильный тип 3	шт.	1	ПВВ(Н)-70КМ-С-01-НШ, Абат	1500	705 (1030)	1721	0,417	1	220	Вывод кабеля 220В/ 1Ф длина кабеля не менее 2м выпуск кабеля - металлическая гильза высотой 50 мм, кабель в металлорукаве
154	Обеденный зал	1	П239	Прилавок для столовых приборов и подносов тип 1	шт.	1	ПСП-70КМ, Абат	630	675	1242				
154	Обеденный зал	1	П016в	Прилавок нейтральный тип 2	шт.	1	ПВН-70КМ, Абат	1120	705 (1030)	1721				
154	Обеденный зал	1	П019	Рукомойник	шт.	1	ВРК-330, Atesy	332	337	152				Вентили подвода хол., гор. воды dy-15 на Н-400 от УЧП (все подводки горячей и холодной воды должны заканчиваться шаровыми кранами), канализация dy-50 на 150 от УЧП
154	Обеденный зал	1	б/н	Сифон для рукомойника.	шт.	1								
154	Обеденный зал	1	б/н	Смеситель для рукомойника	шт.	1								

						16-25/Г-Р-ТХ2-СО			
						Капитальный ремонт объекта "ГБОУ Школа № 429 "Соколиная гора", расположенного по адресу: г.Москва, ул. Соколиной горы 5-я, д.14			
Изм.	Кол. уч.	Лист	№ док	Подпись	Дата	Общие технологические решения	Стадия	Лист	Листов
Разработал	Волкова				07.26		Р	1	13
Проверил	Рябкова				07.26				
						Спецификация технологического оборудования и мебели			
Н.контроль	Губарев				07.26				
ГИП	Неменов				07.26				

Взам. инв. №

Подп. и дата

Инв. № подл.

№ пом. в ГЧ	Помещение	Кол-во пом.	№ поз. в ГЧ	Наименование	Ед. изм.	Кол-во	Марка оборудова ния		длина	ширина	высота	кВт	Ф	В	Примечание
154	Обеденный зал	1	П022	Шкаф-стол рабочий двухдверный тип 1	шт.	1			800	600	850				
154	Обеденный зал	1	П232	Микроволновая печь	шт.	1	Samsung MG30T5018AK/BW или аналог		517	297	425	2,9	1	220	Розетка силовая 220В - 2 шт. Высота размещения 1800мм от у.ч.п.
154	Обеденный зал	1	П024в	Ограждение тип 1	шт.	1									
154	Обеденный зал	1	П024г	Ограждение с калиткой (телескопической)	шт.	1									
154	Обеденный зал	1	П025	Стол производственный 900х600	шт.	1	СПП-223/900 , Техно-ТТ		900	600	850				
150	Горячий цех	1	П044	Ванна моечная односекционная тип 1	шт.	1	ВМ-С3606, Камик		600	600	850				Выпуски из стены: ХВ, ГВ dy-15 на высоте 1050 мм от УЧП, К3 dy-50 не выше 150 мм
150	Горячий цех	1	б/н	Сифон для ванны моечной	шт.	1									
150	Горячий цех	1	б/н	Смеситель для ванны моечной.	шт.	1									
150	Горячий цех	1	П037	Весы настольные	шт.	2	ПВм-3/32-ЖКИ, Мера		300	320	72	0,025	1	220	Розетка силовая 220В - 1 шт. Высота размещения 1200мм от у.ч.п.
150	Горячий цех	1	П210	Зонт вытяжной для пароконвектомата	шт.	2	Restoinox ЗВП-10/12		1000	1200	350				на Н-2180 Вытяжка Q=700м3/ч Подключить к вытяжке воздуховодом для температуры 120 С. Предусмотреть подведение воздуховодов вытяжной/приточной и вытяжной вентиляции, выполнить подключение зонтов к системе производственной вентиляции. Предусмотреть подвесы/шпильки в местах установки зонта.
150	Горячий цех	1	П219	Зонт приточно-вытяжной	шт.	1	Кобор ЗПВ-180/120/К		1800	1200	400				на Н-2180 Вытяжка 800 м3/ч, приток - 500 м3/ч Подключить к вытяжке воздуховодом для температуры 120 С. Предусмотреть подведение воздуховодов вытяжной/приточной и вытяжной вентиляции, выполнить подключение зонтов к системе производственной вентиляции. Предусмотреть подвесы/шпильки в местах установки зонта.
150	Горячий цех	1	П483	Зонт приточно-вытяжной 1500х1200	к-т	2	ЗПВН-03 1500/1200		1500	1200	400				на Н-2180 Вытяжка 1150 м3/ч, приток - 400 м3/ч Подключить к вытяжке воздуховодом для температуры 120 С. Предусмотреть подведение воздуховодов вытяжной/приточной и вытяжной вентиляции, выполнить подключение зонтов к системе производственной вентиляции. Предусмотреть подвесы/шпильки в местах установки зонта.
150	Горячий цех	1	П053	Кипятильник электрический	шт.	1	КНЭ-100-01, Дебис		250	250	360	10	3	380	Выпуски из стены: хол.воды dy-15 на высоте 400 мм от у.ч.п. (1 вывод, все подводы воды должны заканчиваться шаровыми кранами). К3 dy-50. Розетка силовая 380В -1шт. на высоте 1500 мм от у.ч.п. Предусмотреть контактно-штепсельный разъем (не входит в комплект поставки оборудования).

Изм.

Кол. уч.

Лист

№ док.

Подпись

Дата

16-25/Г-Р-ТХ2-СО

Лист
2

		№ пом. в ГЧ	Помещение	Кол-во пом.	№ поз. в ГЧ	Наименование	Ед. изм.	Кол-во	Марка оборудова ния		длина	ширина	высота	кВт	Ф	В	Примечание		
Взам. инв. №		150	Горячий цех	1	ПО54	Котел пищеварочный 250 л	шт.	2	КПЭМ-250/9Т, Абат		840	1000	1290	18,1	3	380	Подводка ХВ dy-15 (1 вывод, все подводки воды должны заканчиваться шаровыми кранами). Лотковый трап 1700* 300мм, трап 100 мм, разрыв струи. Вывод кабеля 380В/3Ф, длина кабеля не менее 2м выпуск кабеля - металлическая гильза высотой 50 мм, кабель в металлорукаве		
		150	Горячий цех	1	ПО31	Магнитный держатель для ножей	шт.	2	1970000, Sanelli		380	48	13						
		150	Горячий цех	1	ПО55	Машина кухонная универсальная	шт.	1	УКМ П, Торгмаш		920	596	877	1,1	3	380	Розетку 380В/3Ф предусмотреть на высоте 1500 мм от уровня ч.п., предусмотреть ГРИБОК (аварийная кнопка) над розеткой. Предусмотреть усиление плиты перекрытия в месте установки. Предусмотреть контактно-штепсельный разъем (не входит в комплект поставки оборудования).		
		150	Горячий цех	1	б/н	Набор гастроемкостей с крышками для пароконвектомата 20 уровней	набор	2											
		150	Горячий цех	1	ПО57	Пароконвектомат 20 уровней	шт.	2	Чувашторгтехника Abat ПКА 20-1/1ПМ2-01 или эквивалент		808	890	1780	35	3	380	Розетку 380В/3Ф предусмотреть на высоте 1500 мм от уровня ч.п., предусмотреть ГРИБОК (аварийная кнопка) над розеткой. Подводка ХВ (все подводки должны заканчиваться шаровыми кранами). Лотковый трап с гидрозатвором по задней стенке с размером решетки 300*300, трап 100 мм, разрыв струи. Предусмотреть контактно-штепсельный разъем (не входит в комплект поставки оборудования).		
		150	Горячий цех	1	П237	Плита электрическая 6 конфорок тип 2	шт.	2	ПЭ-0,54Ш, Продмаш		1200	800	850	20	3	380	Вывод кабеля 380В/3Ф длина кабеля не менее 2м выпуск кабеля - металлическая гильза высотой 50 мм, кабель в металлорукаве		
		150	Горячий цех	1	ПО32	Подставка под кухонный инвентарь	шт.	2	ПКИ-П- 400.400.420-02 Атеси		400	400	400						
		150	Горячий цех	1	ПО59	Подставка под электрокипятильник	шт.	1	АТЕSY ПК-870		400	400	400						
		150	Горячий цех	1	ПО39	Полка для хранения разделочных досок	шт.	1	ПН-115/600, Техно-ТТ		600	355	270						
		150	Горячий цех	1	ПО19	Рукомойник	шт.	1	ВРК-330, Atesy		332	337	152				Вентили подвода хол., гор. воды dy-15 на Н-400 от УЧП (все подводки горячей и холодной воды должны заканчиваться шаровыми кранами), канализация dy-50 на 150 от УЧП		
		150	Горячий цех	1	б/н	Сифон для рукомойника.	шт.	1											
		150	Горячий цех	1	б/н	Смеситель для рукомойника	шт.	1											
Подп. и дата		150	Горячий цех	1	ПО60	Сковорода электрическая 70 л	шт.	1	Abat ЭСК-90-0,47-70 или аналог		840	1045	940	9	3	380	Лотковый трап с фронтальной стороны оборудования шириной не менее 300 мм, длиной в соответствии с разделом ТХ, трап 100 мм, разрыв струи. .Вывод кабеля 380В/3Ф, длина кабеля не менее 2м выпуск кабеля - металлическая		
Инв. № подл.																		16-25/Г-Р-ТХ2-СО	Лист 3
												Изм.	Кол. уч.	Лист	№ док.	Подпись	Дата		

Взам. инв. №

Подп. и дата

Инв. № подл.

№ пом. в ГЧ	Помещение	Кол-во пом.	№ поз. в ГЧ	Наименование	Ед. изм.	Кол-во	Марка оборудова ния		длина	ширина	высота	кВт	Ф	В	Примечание
															гильза высотой 50 мм, кабель в металлорукаве
150	Горячий цех	1	П218	Зонт приточно-вытяжной 1000х1200	шт.	1	ЗПВН-04 1000/1200		1000	1200	400				на Н-2180 Вытяжка Q=1000м3/ч, приток - 700 м3/ч Подключить к вытяжке воздуховодом для температуры 120 С. Предусмотреть подведение воздуховодов вытяжной/приточной и вытяжной вентиляции, выполнить подключение зонтов к системе производственной вентиляции. Предусмотреть подвесы/шпильки в местах установки зонта.
150	Горячий цех	1	П025	Стол производственный 900х600	к-т	4	СПП-223/900 , Техно-ТТ		900	600	850				
150	Горячий цех	1	П035	Стол производственный 1200х600	к-т	2	СП-223/1200, Техно-ТТ		1200	600	850				
150	Горячий цех	1	П061	Стол-вставка нейтральная тип 2	шт.	3	ПМП-40		400	850	850				
150	Горячий цех	1	П131	Тележка с баком для отходов	шт.	1	КАУМАН ТБ-23		450	450	500				
150	Горячий цех	1	П049	Тележка-шпилька для гастрೋмкостей	шт.	1	СТР-331/406, Техно-ТТ		370	545	1510				
150	Горячий цех	1	П062	Шкаф холодильный 500	шт.	1	СМ105-S, Полаир		697	695	1960	0,35	1	220	Розетка 220В -1шт. на высоте 2100 мм от у.ч.п.
153	Холодный цех	1	П044	Ванна моечная односекционная тип 1	шт.	2	ВМ-С3606, Камик		600	600	850				Выпуски из стены: ХВ, ГВ dy-15 на высоте 1050 мм от УЧП, К3 dy-50 не выше 150 мм
153	Холодный цех	1	б/н	Сифон для ванны моечной	шт.	2									
153	Холодный цех	1	б/н	Смеситель с душирующим устройством	шт.	1									
153	Холодный цех	1	б/н	Смеситель для ванны моечной.	шт.	2									
153	Холодный цех	1	П037	Весы настольные	шт.	1	ПВм-3/32-ЖКИ, Мера		300	320	72	0,025	1	220	Розетка силовая 220В - 1 шт. Высота размещения 1200мм от у.ч.п.
153	Холодный цех	1	П031	Магнитный держатель для ножей	шт.	1	1970000, Sanelli		380	48	13				
153	Холодный цех	1	П064	Облучатель бактерицидный	шт.	1	ОРУБн2-01-«КРОНТ» (ДЕЗАР-2н)		605	365	145	0,038	1	220	Розетка 220В -1шт. на высоте 2200 мм от у.ч.п., питание розетки - от выключателя клавишного на стене внутри помещения.
153	Холодный цех	1	П065	Овощерезательно-протирочная машина	шт.	1	Торгмаш МПР-350М		600	340	650	1	3	380	Розетка силовая 380В -1шт. на высоте 1500 мм от у.ч.п., предусмотреть ГРИБОК (аварийная кнопка) над розеткой, предусмотреть контактно-штепсельный разъем (не входит в комплект поставки оборудования)
153	Холодный цех	1	П032	Подставка под кухонный инвентарь	шт.	1	ПКИ-П- 400.400.420-02 Атеси		400	400	400				

Изм.

Кол. уч.

Лист

№ док.

Подпись

Дата

16-25/Г-Р-ТХ2-СО

Лист

4

Взам. инв. №	
Подп. и дата	
Инв. № подл.	

№ пом. в ГЧ	Помещение	Кол-во пом.	№ поз. в ГЧ	Наименование	Ед. изм.	Кол-во	Марка оборудова ния		длина	ширина	высота	кВт	Ф	В	Примечание
153	Холодный цех	1	П039	Полка для хранения разделочных досок	шт.	1	ПН-115/600, Техно-ТТ		600	355	270				
153	Холодный цех	1	П019	Рукомойник	шт.	1	ВРК-330, Atesy		332	337	152				Вентили подвода хол., гор. воды dy-15 на Н-400 от УЧП (все подводки горячей и холодной воды должны заканчиваться шаровыми кранами), канализация dy-50 на 150 от УЧП
153	Холодный цех	1	б/н	Сифон для рукомойника.	шт.	1									
153	Холодный цех	1	б/н	Смеситель для рукомойника	шт.	1									
153	Холодный цех	1	П047	Стерилизатор для ножей ультрафиолетовый	шт.	1	СТУ-1-18-02-1, Атеси		465	145	605	0,08	1	220	Розетка 220В -1шт. на высоте 1200 мм от у.ч.п.
153	Холодный цех	1	П048	Стол производственный 600х600	к-т	1	СПП-223/600 , Техно-ТТ		600	600	850				
153	Холодный цех	1	П035	Стол производственный 1200х600	к-т	4	СП-223/1200, Техно-ТТ		1200	600	850				
153	Холодный цех	1	П025	Стол производственный 900х600	шт.	1	СПП-223/900 , Техно-ТТ		900	600	850				
153	Холодный цех	1	П131	Тележка с баком для отходов	шт.	1	КАУМАН ТБ-23		450	450	500				
153	Холодный цех	1	П049	Тележка-шпилька для гастрೋмкостей	шт.	1	СТР-331/406, Техно-ТТ		370	545	1510				
153	Холодный цех	1	П041	Холодильный стол тип 2	шт.	1	ТМ2-С, Полаир		1200	600	850	0,6	1	220	Розетка 220В -1шт. на высоте 1200 мм от у.ч.п.
153	Холодный цех	1	П042	Шкаф холодильный 700	шт.	1	СМ-107С, Полаир		697	925	1960	0,35	1	220	Розетка 220В -1шт. на высоте 2100 мм от у.ч.п.
149	Доготовочный цех	1	П044	Ванна моечная односекционная тип 1	шт.	3	ВМ-С3606, Камик		600	600	850				Выпуски из стены: ХВ, ГВ dy-15 на высоте 1050 мм от УЧП, К3 dy-50 не выше 150 мм
149	Доготовочный цех	1	б/н	Сифон для ванны моечной	шт.	3									
149	Доготовочный цех	1	б/н	Смеситель для ванны моечной.	шт.	3									
149	Доготовочный цех	1	П037	Весы настольные	шт.	3	ПВм-3/32-ЖКИ, Мера		300	320	72	0,025	1	220	Розетка силовая 220В - 1 шт. Высота размещения 1200мм от у.ч.п.
149	Доготовочный цех	1	П031	Магнитный держатель для ножей	шт.	2	1970000, Sanelli		380	48	13				
149	Доготовочный цех	1	П231	Мясорубка 300	шт.	2	МИМ300, Белторгмаш		680	400	460	1,9	3	380	Розетку380В/3Ф предусмотреть на высоте 1500 мм от уровня ч.п., предусмотреть ГРИБОК (аварийная кнопка) над розеткой. Предусмотреть контактно-штепсельный разъем (не входит в комплект поставки оборудования).

						16-25/Г-Р-ТХ2-СО		Лист
								5
Изм.	Кол. уч.	Лист	№ док.	Подпись	Дата			

Взам. инв. №

Подп. и дата

Инв. № подл.

№ пом. в ГЧ	Помещение	Кол-во пом.	№ поз. в ГЧ	Наименование	Ед. изм.	Кол-во	Марка оборудова ния		длина	ширина	высота	кВт	Ф	В	Примечание
149	Доготовочный цех	1	ПО38	Овощерезательная машина	шт.	1	МПР-350М-02		600	300	650	1	3	380	Розетку 380В/3Ф предусмотреть на высоте 1500 мм от уровня ч.п., предусмотреть ГРИБОК (аварийная кнопка) над розеткой. Предусмотреть контактно-штепсельный разъем (не входит в комплект поставки оборудования).
149	Доготовочный цех	1	ПО32	Подставка под кухонный инвентарь	шт.	3	ПКИ-П- 400.400.420-02 Атеси		400	400	400				
149	Доготовочный цех	1	ПО39	Полка для хранения разделочных досок	шт.	2	ПН-115/600, Техно-ТТ		600	355	270				
149	Доготовочный цех	1	ПО64	Облучатель бактерицидный	шт.	1	ОРУБн2-01-«КРОНТ» (ДЕЗАР-2н)		605	365	145	0,038	1	220	Розетка 220В -1шт. на высоте 2200 мм от у.ч.п., питание розетки - от выключателя клавишного на стене внутри помещения.
149	Доготовочный цех	1	ПО19	Рукомойник	шт.	1	ВРК-330, Atesy		332	337	152				Вентили подвода хол., гор. воды dу-15 на Н-400 от УЧП (все подводки горячей и холодной воды должны заканчиваться шаровыми кранами), канализация dу-50 на 150 от УЧП
149	Доготовочный цех	1	б/н	Сифон для рукомойника.	шт.	1									
149	Доготовочный цех	1	б/н	Смеситель для рукомойника	шт.	1									
149	Доготовочный цех	1	ПО47	Стерилизатор для ножей ультрафиолетовый	шт.	1	СТУ-1-18-02-1, Атеси		465	145	605	0,08	1	220	Розетка 220В -1шт. на высоте 1200 мм от у.ч.п.
149	Доготовочный цех	1	ПО25	Стол производственный 900х600	к-т	2	СПП-223/900 , Техно-ТТ		900	600	850				
149	Доготовочный цех	1	ПО35	Стол производственный 1200х600	к-т	2	СП-223/1200, Техно-ТТ		1200	600	850				
149	Доготовочный цех	1	ПИ31	Тележка с баком для отходов	шт.	1	КАУМАН ТБ-23		450	450	500				
149	Доготовочный цех	1	ПО49	Тележка-шпилька для гастрೋмкостей	шт.	1	СТР-331/406, Техно-ТТ		370	545	1510				
149	Доготовочный цех	1	ПО41	Холодильный стол тип 2	шт.	1	ТМ2-С, Полаир		1200	600	850	0,6	1	220	Розетка 220В -1шт. на высоте 1200 мм от у.ч.п.
149	Доготовочный цех	1	ПО42	Шкаф холодильный 700	шт.	2	СМ-107С, Полаир		697	925	1960	0,35	1	220	Розетка 220В -1шт. на высоте 2100 мм от у.ч.п.
145	Кладовая и моечная оборотной тары	1	ПО26	Ванна моечная двухсекционная тип 2	шт.	1	К-ВМО-2/1340/700, КАУМАН		1340	700	850				Выпуски из стены: 2 подвода ХВ, ГВ на высоте 1050 мм от у.ч.п., 2 выпуска КЗ dу-50 не выше 150 мм.
145	Кладовая и моечная оборотной тары	1	б/н	Сифон для ванны моечной	шт.	2									
145	Кладовая и моечная оборотной тары	1	б/н	Смеситель с душирующим устройством	шт.	1									

		№ пом. в ГЧ	Помещение	Кол- во пом.	№ поз. в ГЧ	Наименование	Ед. изм.	Кол-во	Марка оборудова ния		длина	ширина	высота	кВт	Ф	В	Примечание		
		145	Кладовая и моечная оборотной тары	1	П214	Зонт вытяжной	шт.	1	МВО-1,4МСВ-0,8П ТЕХНО-ТТ		1400	800	400				на Н-2180 Вытяжка Q=250м3/ч Подключить к вытяжке воздуховодом для температуры 120 С. Предусмотреть подведение воздуховодов вытяжной/приточной и вытяжной вентиляции, выполнить подключение зонтов к системе производственной вентиляции. Предусмотреть подвесы/шпильки в местах установки зонта.		
		145	Кладовая и моечная оборотной тары	1	П019	Рукомойник	шт.	1	ВРК-330, Atesy		332	337	152				Вентили подвода хол., гор. воды dy-15 на Н-400 от УЧП (все подводки горячей и холодной воды должны заканчиваться шаровыми кранами), канализация dy- 50 на 150 от УЧП		
		145	Кладовая и моечная оборотной тары	1	б/н	Сифон для рукомойника.	шт.	1											
		145	Кладовая и моечная оборотной тары	1	б/н	Смеситель для рукомойника	шт.	1											
		145	Кладовая и моечная оборотной тары	1	П069	Стеллаж с перфорированными полками 900x500	шт.	2	СТР-524/900, Техно-ТТ		900	500	1800						
		152	Моечная для столовой посуды	1	П071	Ванна моечная двухсекционная тип 1	шт.	1	ВМ2 ПроК (Россия)		1200	600	850				Выпуски из стены: 2 подвода ХВ, ГВ на высоте 1050 мм от у.ч.п.; 2 выпуска К3 dy-50 не выше 150 мм.		
		152	Моечная для столовой посуды	1	б/н	Сифон для ванны моечной	шт.	2											
		152	Моечная для столовой посуды	1	б/н	Смеситель для ванны моечной.	шт.	1											
		152	Моечная для столовой посуды	1	б/н	Смеситель с душирующим устройством	шт.	1											
		152	Моечная для столовой посуды	1	П072	Ванна моечная трехсекционная тип 2	шт.	1	ВМ3 ПроК (Россия), 1700x600x850		1700	600	850				Выпуски из стены: 3 подвода ХВ, ГВ на высоте 1050 мм от у.ч.п., 3 выпуска К3 dy-50 не выше 150 мм.		
		152	Моечная для столовой посуды	1	б/н	Сифон для ванны моечной	шт.	3											
152	Моечная для столовой посуды	1	б/н	Смеситель для ванны моечной.	шт.	2													
Взам. инв. №		152	Моечная для столовой посуды	1	б/н	Смеситель с душирующим устройством	шт.	1											
		152	Моечная для столовой посуды	1	П212	Зонт вытяжной 1200x700	шт.	1	МВО-1,2МСВ-0,7П, Техно-ТТ		1200	700	350				на Н-2180 Вытяжка Q=250м3/ч Подключить к вытяжке воздуховодом для температуры 120 С. Предусмотреть подведение воздуховодов вытяжной/приточной и вытяжной вентиляции, выполнить подключение зонтов к системе производственной вентиляции. Предусмотреть подвесы/шпильки в местах установки зонта.		
		152	Моечная для столовой посуды	1	П216	Зонт вытяжной 1800x700	шт.	1	МВО-1,8МСВ-0,7ПК, Техно-ТТ		1800	700	400				на Н-2180 Вытяжка Q=250м3/ч Подключить к вытяжке воздуховодом для температуры 120 С. Предусмотреть подведение воздуховодов вытяжной/приточной и вытяжной вентиляции, выполнить подключение зонтов к		
Инв. № подл.																		16-25/Г-Р-ТХ2-СО	Лист 7
		Изм.	Кол. уч.	Лист	№ док.	Подпись	Дата												

		№ пом. в ГЧ	Помещение	Кол-во пом.	№ поз. в ГЧ	Наименование	Ед. изм.	Кол-во	Марка оборудова ния		длина	ширина	высота	кВт	Φ	В	Примечание		
																	системе производственной вентиляции. Предусмотреть подвесы/шпильки в местах установки зонта.		
		152	Моечная для столовой посуды	1	П074	Машина посудомоечная туннельная	к-т	1	МПТ-1700-01 (левая), Абат		1595	770	1960	26,7	3	380	Подвод ХВ на высоте 400 мм от уровня ч.п. в зоне стола предмоечного (все подводки воды должны заканчиваться шаровыми кранами). Лотковый трап с гидрозатвором по задней стенке с размером решетки 300*300, трап 100 мм, разрыв струи. Предусмотреть подключение к системе вентиляции (патрубок или зонт вентиляционный - в соответствии с согласованным проектом ТХ). Вывод кабеля 380В/3Ф, длина кабеля не менее 2м выпуск кабеля - металлическая гильза высотой 50 мм, кабель в металлорукаве		
		152	Моечная для столовой посуды	1	П074.1	Стол предмоечный универсальный	шт.	1	СПМП-7-7, Абат		1715	705	1080				Выпуски из стены: ХВ, ГВ на высоте 400 мм от уровня ч.п. (все подводки горячей и холодной воды должны заканчиваться шаровыми кранами), К3 не выше 150 мм.		
		152	Моечная для столовой посуды	1	П019	Рукомойник	шт.	1	БРК-330, Atesy		332	337	152				Вентили подвода хол., гор. воды dy-15 на Н-400 от УЧП (все подводки горячей и холодной воды должны заканчиваться шаровыми кранами), канализация dy-50 на 150 от УЧП		
		152	Моечная для столовой посуды	1	б/н	Сифон для рукомойника.	шт.	1											
		152	Моечная для столовой посуды	1	б/н	Смеситель для рукомойника	шт.	1											
		152	Моечная для столовой посуды	1	П075	Стеллаж для сушки посуды	шт.	4	СПП-02, Проммаш		800	632	1600						
		152	Моечная для столовой посуды	1	П076	Стеллаж для хранения столовой посуды	шт.	5	СКС -90/30/430		900	300	1600						
		152	Моечная для столовой посуды	1	П258	Стол раздаточный для туннельных посудомоечных машин	шт.	1	СПМР-6-2, Абат		704	635	850						
		152	Моечная для столовой посуды	1	П079	Стол для сбора остатков пищи 600	шт.	1	НДСО-6/6БП, HiCOLD		600	600	850						
		152	Моечная для столовой посуды	1	П048	Стол производственный 600х600	к-т	2	СПП-223/600 , Техно-ТТ		600	600	850						
Взам. инв. №		152	Моечная для столовой посуды	1	П025	Стол производственный 900х600	шт.	3	СПП-223/900 , Техно-ТТ		900	600	850						
		152	Моечная для столовой посуды	1	П131	Тележка с баком для отходов	шт.	1	КАУМАН ТБ-23		450	450	500						
		152	Моечная для столовой посуды	1	П264	Транспортер для сбора использованной посуды	шт.	1	КАЮР-М		4040	500	850	0,38	3	380	Вывод кабеля 380В/3Ф под ведущим модулем транспортера, длина кабеля не менее 2м выпуск кабеля - металлическая гильза высотой 50 мм, кабель в металлорукаве		
Подп. и дата																			
		151	Моечная для кухонной посуды	1	П202	Ванна моечная двухсекционная тип 2	шт.	1	ВМСК-1/13/7-ЭЦ		1400	700	850				Выпуски из стены: 2 вывода ХВ, ГВ dy-15 на высоте 1050 мм от УЧП, 2 выпуска К3 dy-50 не выше 150 мм		
Инв. № подл.																	16-25/Г-Р-ТХ2-СО		Лист
																			8
		Изм.	Кол. уч.	Лист	№ док.	Подпись	Дата												

№ пом. в ГЧ	Помещение	Кол-во пом.	№ поз. в ГЧ	Наименование	Ед. изм.	Кол-во	Марка оборудова ния	длина	ширина	высота	кВт	Ф	В	Примечание
151	Моечная для кухонной посуды	1	б/н	Сифон для ванны моечной	шт.	2								
151	Моечная для кухонной посуды	1	б/н	Смеситель для ванны моечной.	шт.	1								
151	Моечная для кухонной посуды	1	б/н	Смеситель с душирующим устройством	шт.	1								
151	Моечная для кухонной посуды	1	П213	Зонт вытяжной	шт.	1	Техно-ТТ МВО-1,4МСВ-0,7П	1400	700	400				на Н-2180 Вытяжка Q=250м3/ч Подключить к вытяжке воздуховодом для температуры 120 С. Предусмотреть подведение воздуховодов вытяжной/приточной и вытяжной вентиляции, выполнить подключение зонтов к системе производственной вентиляции. Предусмотреть подвесы/шпильки в местах установки зонта.
151	Моечная для кухонной посуды	1	П019	Рукомойник	шт.	1	ВРК-330, Atesy	332	337	152				Вентили подвода хол., гор. воды dy-15 на Н-400 от УЧП (все подводки горячей и холодной воды должны заканчиваться шаровыми кранами), канализация dy-50 на 150 от УЧП
151	Моечная для кухонной посуды	1	б/н	Сифон для рукомойника.	шт.	1								
151	Моечная для кухонной посуды	1	б/н	Смеситель для рукомойника	шт.	1								
151	Моечная для кухонной посуды	1	П069	Стеллаж с перфорированными полками 900х500	шт.	3	СТР-524/900, Техно-ТТ	900	500	1800				
151	Моечная для кухонной посуды	1	П048	Стол производственный 600х600	к-т	1	СПП-223/600 , Техно-ТТ	600	600	850				
151	Моечная для кухонной посуды	1	П131	Тележка с баком для отходов	шт.	1	КАYMAN ТБ-23	450	450	500				
151	Моечная для кухонной посуды	1	П033	Подтоварник 900х600	шт.	1	ПТ906-3, Техно-ТТ	900	600	300				
146	Загрузочный цех	1	П083	Весы напольные тип 1	шт.	1	ТВ-М-300.2-А013, Масса-К	600	800	750	0,2	1	220	Розетка 220В -1шт. на высоте 1200 мм от у.ч.п.
146	Загрузочный цех	1	П457	Тележка грузовая платформенная	шт.	1	Аbat ТГ-6-1	1260	600	935				
148	Кладовая сухих продуктов	1	П070	Подтоварник 600х600	шт.	2	ПТ606-3, Техно-ТТ	600	600	300				
148	Кладовая сухих продуктов	1	П085	Стеллаж 900х500	шт.	6	СТР-124/900Техно-ТТ	900	500	1800				
148	Кладовая сухих продуктов	1	П086	Шкаф для хранения хлеба 900	шт.	2	ШКХ-90/50	900	500	1700				

						16-25/Г-Р-ТХ2-СО	Лист
							9
Изм.	Кол. уч.	Лист	№ док.	Подпись	Дата		

Взам. инв. №	
Подп. и дата	
Инв. № подл.	

№ пом. в ГЧ	Помещение	Кол-во пом.	№ поз. в ГЧ	Наименование	Ед. изм.	Кол-во	Марка оборудова ния	длина	ширина	высота	кВт	Ф	В	Примечание
147.1	Помещение с холодильным оборудованием	1	П033	Подтоварник 900х600	шт.	3	ПТ906-3, Техно-ТТ	900	600	300				
147.1	Помещение с холодильным оборудованием	1	П085	Стеллаж 900х500	шт.	6	СТР-124/900Техно-ТТ	900	500	1800				
147.1	Помещение с холодильным оборудованием	1	П046а	Стеллаж 1200х500	шт.	3	СТР-124/1200, Техно-ТТ	1200	500	1830				
147.1	Помещение с холодильным оборудованием	1	П271	Холодильная камера 2000х2300,толщина панелей 100	шт.	1	POLAIR кхн-7,71	2000	2300	2200				
147.1	Помещение с холодильным оборудованием	1	П484	Холодильная камера 2260х2260, толщина панелей 80	шт.	2	POLAIR кхн-9,0	2260	2260	2200				
147.1	Помещение с холодильным оборудованием	1	П428	Машина холодильная низкотемпературная	шт.	1	Polair MB214ST потолочный	830	550	665	1,4	1	220	Вывод кабеля 220В/1Ф из стены на высоте 2400 мм от уровня ч.п., кабель подводится к внешнему блоку сплит-системы, длина кабеля не менее 2м. Предусмотреть трап или выпуск КЗ в доступе вблизи холодильной камеры для подключения сливной трубки конденсата. Выпуск кабеля - металлическая гильза высотой 50 мм, кабель в металлорукаве. При размещении внешних блоков сплит-систем вне помещения с установкой холодильных камер предусмотреть отверстия в стенах на пути прокладки фреоновой трассы между внутренним и внешним блоком (диаметром не менее 100 мм для каждой трассы). При размещении сплит-систем в технических подвальных помещениях предусмотреть обеспыливающую отделку и полы с возможностью проведения влажной уборки и дезинфекции; Предусмотреть трап 100 мм или выпуск КЗ в доступе вблизи холодильной камеры для подключения сливной трубки конденсата. Обеспечить подведение приточно-вытяжной вентиляции или кондиционирование в помещениях, где устанавливаются внешние блоки сплит-систем.
147.1	Помещение с холодильным оборудованием	1	П429	Машина холодильная среднетемпературная	шт.	2	Polair Polair MM111Тпотолочный	1003	603	545	0,5	1	220	Вывод кабеля 220В/1Ф из стены на высоте 2400 мм от уровня ч.п., кабель подводится к внешнему блоку сплит-системы, длина кабеля не менее 2м. Предусмотреть трап или выпуск КЗ в доступе вблизи холодильной камеры для подключения сливной трубки конденсата. Выпуск кабеля - металлическая гильза высотой 50 мм, кабель в металлорукаве. При размещении внешних блоков сплит-систем вне помещения с установкой холодильных камер предусмотреть отверстия в стенах на пути прокладки фреоновой трассы между внутренним и

															16-25/Г-Р-ТХ2-СО		Лист
																	10
									Изм.	Кол. уч.	Лист	№ док.	Подпись	Дата			

Взам. инв. №

Подп. и дата

Инв. № подл.

№ пом. в ГЧ	Помещение	Кол-во пом.	№ поз. в ГЧ	Наименование	Ед. изм.	Кол-во	Марка оборудова ния		длина	ширина	высота	кВт	Ф	В	Примечание
															внешним блоком (диаметром не менее 100 мм для каждой трассы). При размещении сплит-систем в технических подвальных помещениях предусмотреть обеспыливающую отделку и полы с возможностью проведения влажной уборки и дезинфекции; Предусмотреть трап 100 мм или выпуск КЗ в доступе вблизи холодильной камеры для подключения сливной трубы конденсата. Обеспечить подведение приточно-вытяжной вентиляции или кондиционирование в помещениях, где устанавливаются внешние блоки сплит-систем.
144	Помещение для временного хранения пищевых отходов	1	П093	Ванна котломоечная односекционная	шт.	1	БК-2 ТММ		1000	600	850				Выпуски из стены: подвод ХВ, ГВ на высоте 1050 мм от у.ч.п., выпуск КЗ dy-50 не выше 150 мм.
144	Помещение для временного хранения пищевых отходов	1	б/н	Сифон для ванны моечной	шт.	1									
144	Помещение для временного хранения пищевых отходов	1	б/н	Смеситель с душирующим устройством	шт.	1									
144	Помещение для временного хранения пищевых отходов	1	П019	Рукомойник	шт.	1	BPK-330, Atesy		332	337	152				Вентили подвода хол., гор. воды dy-15 на Н-400 от УЧП (все подводки горячей и холодной воды должны заканчиваться шаровыми кранами), канализация dy-50 на 150 от УЧП
144	Помещение для временного хранения пищевых отходов	1	б/н	Сифон для рукомойника.	шт.	1									
144	Помещение для временного хранения пищевых отходов	1	б/н	Смеситель для рукомойника	шт.	1									
144	Помещение для временного хранения пищевых отходов	1	П069	Стеллаж с перфорированными полками 900х500	шт.	1	СТР-524/900, Техно-ГТ		900	500	1800				
144	Помещение для временного хранения пищевых отходов	1	П094а	Холодильная камера для отходов 1150х1000	шт.	1	Minicella MM 1 дверь (без пола) (1000х1150х2315) 80мм		1000	1150	2315	0,61	1	220	Розетка 220В -1шт. на высоте 1100 мм от у.ч.п.
143	Помещение для хранения уборочного инвентаря (Пищеблок)	1	П019	Рукомойник	шт.	1	BPK-330, Atesy		332	337	152				Вентили подвода хол., гор. воды dy-15 на Н-400 от УЧП (все подводки горячей и холодной воды должны заканчиваться шаровыми кранами), канализация dy-50 на 150 от УЧП
143	Помещение для хранения уборочного инвентаря (Пищеблок)	1	б/н	Сифон для рукомойника.	шт.	1									

		№ пом. в ГЧ	Помещение	Кол-во пом.	№ поз. в ГЧ	Наименование	Ед. изм.	Кол-во	Марка оборудова ния		длина	ширина	высота	кВт	Ф	В	Примечание		
		143	Помещение для хранения уборочного инвентаря (Пищевблок)	1	б/н	Смеситель для раукмойника	шт.	1											
		143	Помещение для хранения уборочного инвентаря (Пищевблок)	1	П046	Стеллаж	шт.	1	СТР-124/604Техно-ТТ		600	400	1820						
		143	Помещение для хранения уборочного инвентаря (Пищевблок)	1	П070	Подтоварник 600х600	шт.	1	ПТ606-3, Техно-ТТ		600	600	300						
		143	Помещение для хранения уборочного инвентаря (Пищевблок)	1	П098	Шкаф для хозяйственного инвентаря одностворчатый металлический	шт.	1	ШРХ-11 L500, Церера		500	500	1850						
		142	Помещение для персонала (включая душевую и санузел)	1	П100	Стол обеденный с 2 стульями	к-т	1			1000	600	750				стол + 2 стула		
		142	Помещение для персонала (включая душевую и санузел)	1	П101	Шкаф для одежды металлический двустворчатый	шт.	7	ШР 22 600 ВСК		600	500	1850				скамья в комплекте		
			Кухонный инвентарь	1	б/н	Венчик	шт.	2											
			Кухонный инвентарь	1	б/н	Доска разделочная	шт.	24											
			Кухонный инвентарь	1	б/н	Кассета для столовых приборов	шт.	3											
			Кухонный инвентарь	1	б/н	Кастрюля с крышкой, 3 л	шт.	3											
			Кухонный инвентарь	1	б/н	Кастрюля с крышкой, 5 л	шт.	3											
			Кухонный инвентарь	1	б/н	Котел с крышкой, 10 л	шт.	5											
			Кухонный инвентарь	1	б/н	Котел с крышкой, 20 л	шт.	5											
			Кухонный инвентарь	1	б/н	Котел с крышкой, 30 л	шт.	5											
			Кухонный инвентарь	1	б/н	Котел с крышкой, 40 л	шт.	2											
			Кухонный инвентарь	1	б/н	Котел с крышкой, 50 л	шт.	2											
			Кухонный инвентарь	1	б/н	Ложка разливательная 0,25 л	шт.	5											
																		16-25/Г-Р-ТХ2-СО	Лист
																			12
												Изм.	Кол. уч.	Лист	№ док.	Подпись	Дата		

Взам. инв. №	
Подп. и дата	
Инв. № подл.	

№ пом. в ГЧ	Помещение	Кол-во пом.	№ поз. в ГЧ	Наименование	Ед. изм.	Кол-во	Марка оборудова ния		длина	ширина	высота	кВт	Ф	В	Примечание
	Кухонный инвентарь	1	б/н	Ложка соусная	шт.	5									
	Кухонный инвентарь	1	б/н	Лопатка кулинарная	шт.	5									
	Кухонный инвентарь	1	б/н	Миска металлическая	шт.	30									
	Кухонный инвентарь	1	б/н	Набор дуршлагов	набор	2									
	Кухонный инвентарь	1	б/н	Нож консервный настольный	шт.	2									
	Кухонный инвентарь	1	б/н	Нож универсальный большой	шт.	12									
	Кухонный инвентарь	1	б/н	Нож универсальный малый	шт.	12									
	Кухонный инвентарь	1	б/н	Нож универсальный средний	шт.	12									
	Кухонный инвентарь	1	б/н	Поднос пластмассовый (для школьной столовой)	шт.	210									
	Кухонный инвентарь	1	б/н	Сито	шт.	2									
	Кухонный инвентарь	1	б/н	Скалка	шт.	2									
	Кухонный инвентарь	1	б/н	Сковорода с крышкой	шт.	5									
	Кухонный инвентарь	1	б/н	Сухарница	шт.	36									
	Кухонный инвентарь	1	б/н	Терка овощная универсальная	шт.	2									
	Кухонный инвентарь	1	б/н	Чайник	шт.	9									
	Кухонный инвентарь	1	б/н	Шумовка	шт.	5									

Примечание:
Данная спецификация оборудования и мебели является рекомендательной.
В процессе закупки в случае необходимости возможно уточнение наименования, кол-ва, габаритов и технических характеристик, а также возможна замена моделей и производителей (технические характеристики должны быть аналогичны или улучшены).