



АЗУРИТ

ООО ПСК «Азурит»
ИНН: 7722762829
Рег. № члена СРО
№ П-163-007722762829-0240
от 23.04.2019г. СРО АП «АПП»

Тел: 8 (495) 724-53-47
e-mail: info@psk-azurit.ru

Экз. №

Заказчик: "АНО «ОЭК Стройтрест»"

**«Капитальный ремонт общеобразовательного учреждения
(ГБОУ «Школа № 429»), расположенного по адресу: г. Москва, 5-ая ул.
Соколиной Горы д.14»**

РАБОЧАЯ ДОКУМЕНТАЦИЯ

Раздел "Технологические решения"

Технологические решения. Пищеблок

1 этап

16-25//Г-Р – ТХ2

Том

Изм.	№ док.	Подп.	Дата



АЗУРИТ

ООО ПСК «Азурит»
ИНН: 7722762829
Рег. № члена СРО
№ П-163-007722762829-0240
от 23.04.2019г. СРО АП «АПП»

Тел: 8 (495) 724-53-47
e-mail: info@psk-azurit.ru

Экз. №

Заказчик: "АНО «ОЭК Стройтрест»"

**«Капитальный ремонт общеобразовательного учреждения
(ГБОУ «Школа № 429»), расположенного по адресу: г. Москва, 5-ая ул.
Соколиной Горы д.14»**

РАБОЧАЯ ДОКУМЕНТАЦИЯ

Раздел "Технологические решения"

Технологические решения. Пищеблок

1 этап

16-25//Г-Р – ТХ2

Том

Технический директор –
главный инженер

Главный инженер проекта



Н.А. Губарев

Г.Н. Неменов

Изм.	№ док.	Подп.	Дата

ВЕДОМОСТЬ РАБОЧИХ ЧЕРТЕЖЕЙ ОСНОВНОГО КОМПЛЕКТА ТХ

Лист	Наименование	Примечание
1	Общие данные	
2	План 1-го этажа. Расстановка оборудования пищеблока	
3	План подключения технологического оборудования к сетям ВК	
4	План подключения технологического оборудования к сетям ВК	
5	План привязки вентиляционных зонтов	
6	План подключения технологического оборудования к сетям ЭС и СС.	
7	План подключения технологического оборудования к сетям ЭС и СС.	

ВЕДОМОСТЬ ССЫЛОЧНЫХ И ПРИЛАГАЕМЫХ ДОКУМЕНТОВ

Обозначение	Наименование	Примечание
Прилагаемые документы		
16-25/Г-Р-ТХ2.СО	Спецификация технологического оборудования и мебели	на 8 листах

Настоящий проект выполнен в соответствии с действующими нормами и правилами /в том числе по пожарной безопасности/.

Инженер- проектировщик ТХ  Волкова

ОБЩИЕ УКАЗАНИЯ

Подраздел «Технологические решения» по объекту ГБОУ «Школа № 1362» по адресу: Российская Федерация, город Москва, ул. Лечебная дом 20 разработан на основании утвержденного Задания на проектирование и в соответствии с действующими нормативными документами.

Рабочим проектом предусматривается оснащение в соответствии с функциональным назначением помещений. Расстановка технологического оборудования и мебели, привязки необходимых коммуникаций, представлены на листах марки 16-25/Г-Р-ТХ2, а спецификация технологического оборудования и мебели со всеми техническими характеристиками - на листах марки 16-25/Г-Р-ТХ2.СО.

В процессе закупки набор и расстановка оборудования и мебели, а также привязки к инженерным коммуникациям могут быть откорректированы.

УСЛОВНЫЕ ОБОЗНАЧЕНИЯ для ВК

ϕ 1/2" - Диаметр подвода в дюймах
ϕ 100 - Диаметр подвода в мм.
Н - Высота подвода в мм. от УЧП
● - ХВ (Холодная вода)
● - ГВ (Горячая вода)
● - К (Канализация)
 - Трап
 - Дренажный лоток

УСЛОВНЫЕ ОБОЗНАЧЕНИЯ для ЭОМ

 - Штепсельная розетка 220В
 - Штепсельная розетка 380В
 - Вывод кабеля
 - Аварийная кнопка(Грибок)
 - Лючок в полу

16-25/Г-Р-ТХ2


Капитальный ремонт объекта "ГБОУ Школа № 429", расположенного по адресу: г.Москва, ул. Соколиной горы 5-ая, д.14

						16-25/Г-Р-ТХ2			
						Капитальный ремонт объекта "ГБОУ Школа № 429", расположенного по адресу: г.Москва, ул. Соколиной горы 5-ая, д.14			
Изм	Кол.уч	Лист	№ док	Подпись	Дата	Технологические решения	Стадия	Лист	Листов
Разраб.		Волкова			25.06.2026		Р	1	7
Проверил		Рябкова			25.06.2026				
						Общие данные			
Н. контр.		Воробьев			25.06.2026				
ГИП		Мурашов			25.06.2026				


Инв. № подл.	
Подпись и дата	
Взам. инв. №	

Экспликация помещений 1-20 этажа


Номер помеще-ния	Наименование	Площадь м2	Кат. помеще-ния
142	Помещение для персонала	11,87	
142.1	Санузел для персонала	2,01	
142.2	Душевая	2,82	
143	П/УИ	4,85	В4
144	Помещение для временного хранения пищевых отходов	6,01	В4
145	Кладовая и моечная оборотной тары	6,92	В4
146	Загрузочный цех	7,45	В4
147	Коридор	28,66	
147.1	Помещение с холодильным оборудованием	26,78	В3
148	Кладовая сухих продуктов	10,93	В4
149	Дозировочный цех	15,16	В3
150	Горячий цех	39,25	В3
151	Моечная для кухонной посуды	9,75	Д
152	Моечная для столовой посуды	34,78	Д
152.1	Предмоечная	5,48	Д
153	Холодный цех	15,32	В3
154	Обеденный зал	184,39	

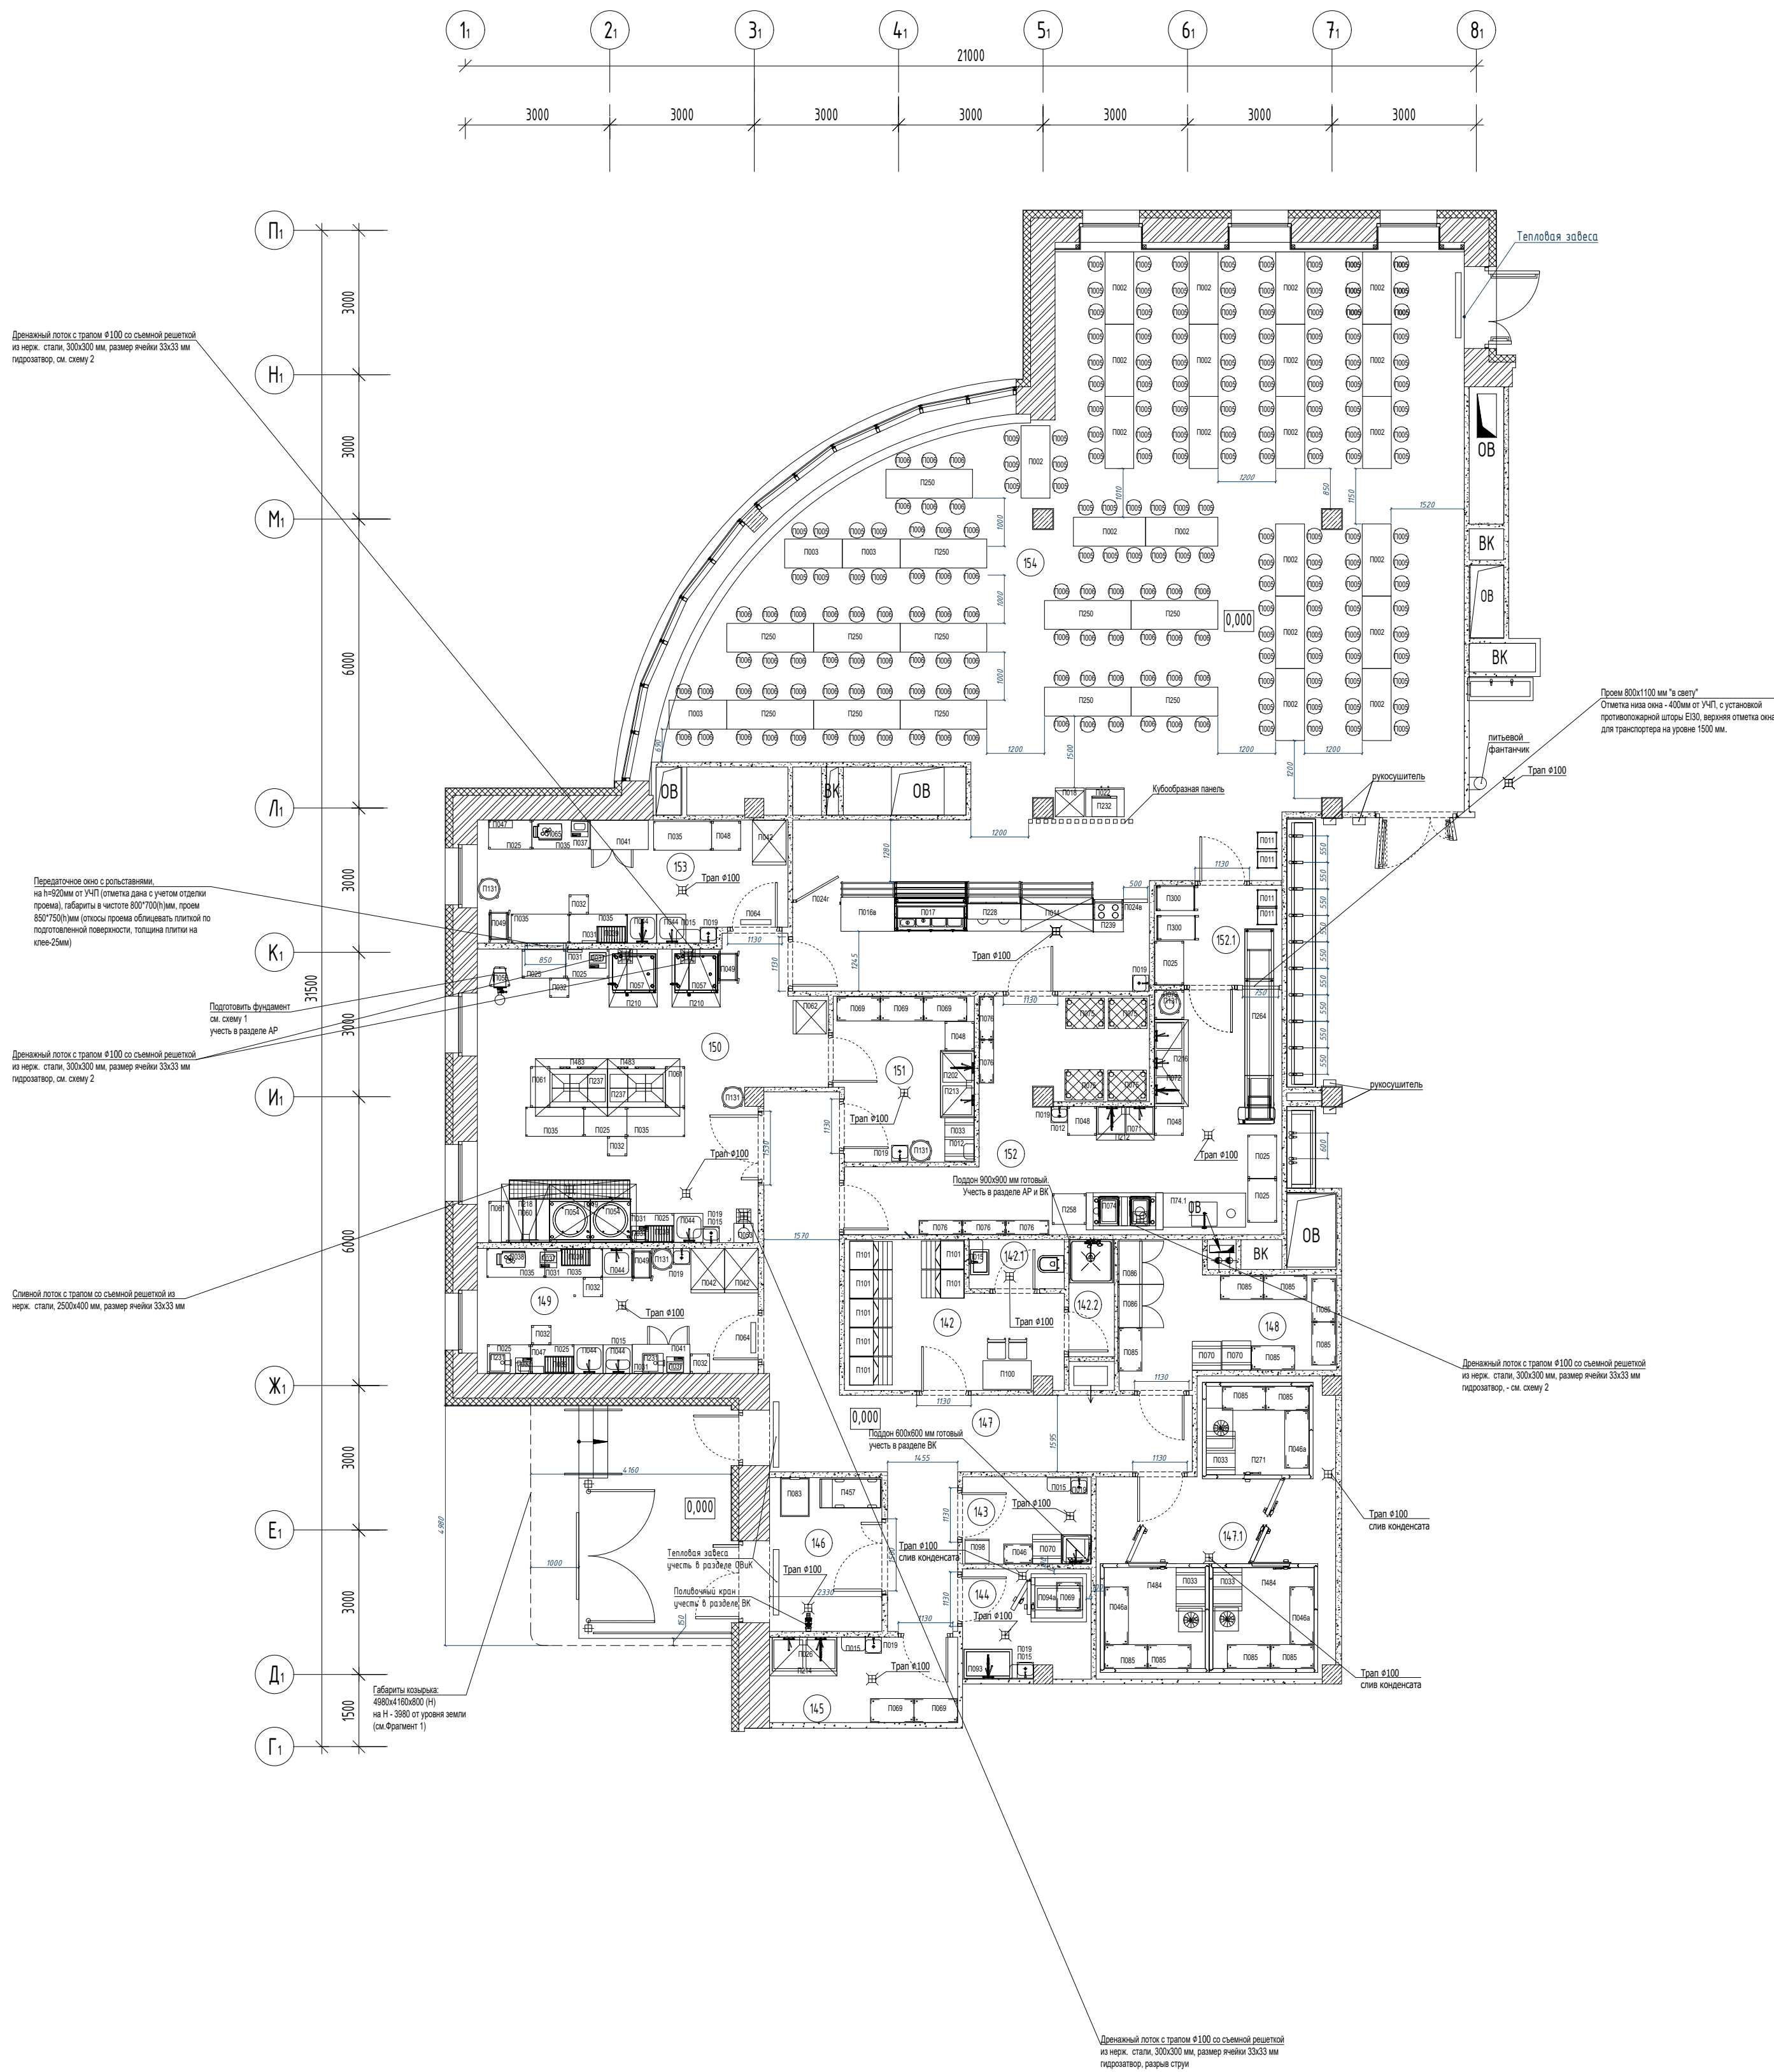

Фрагмент
Габаритный размеры и высоты козырька

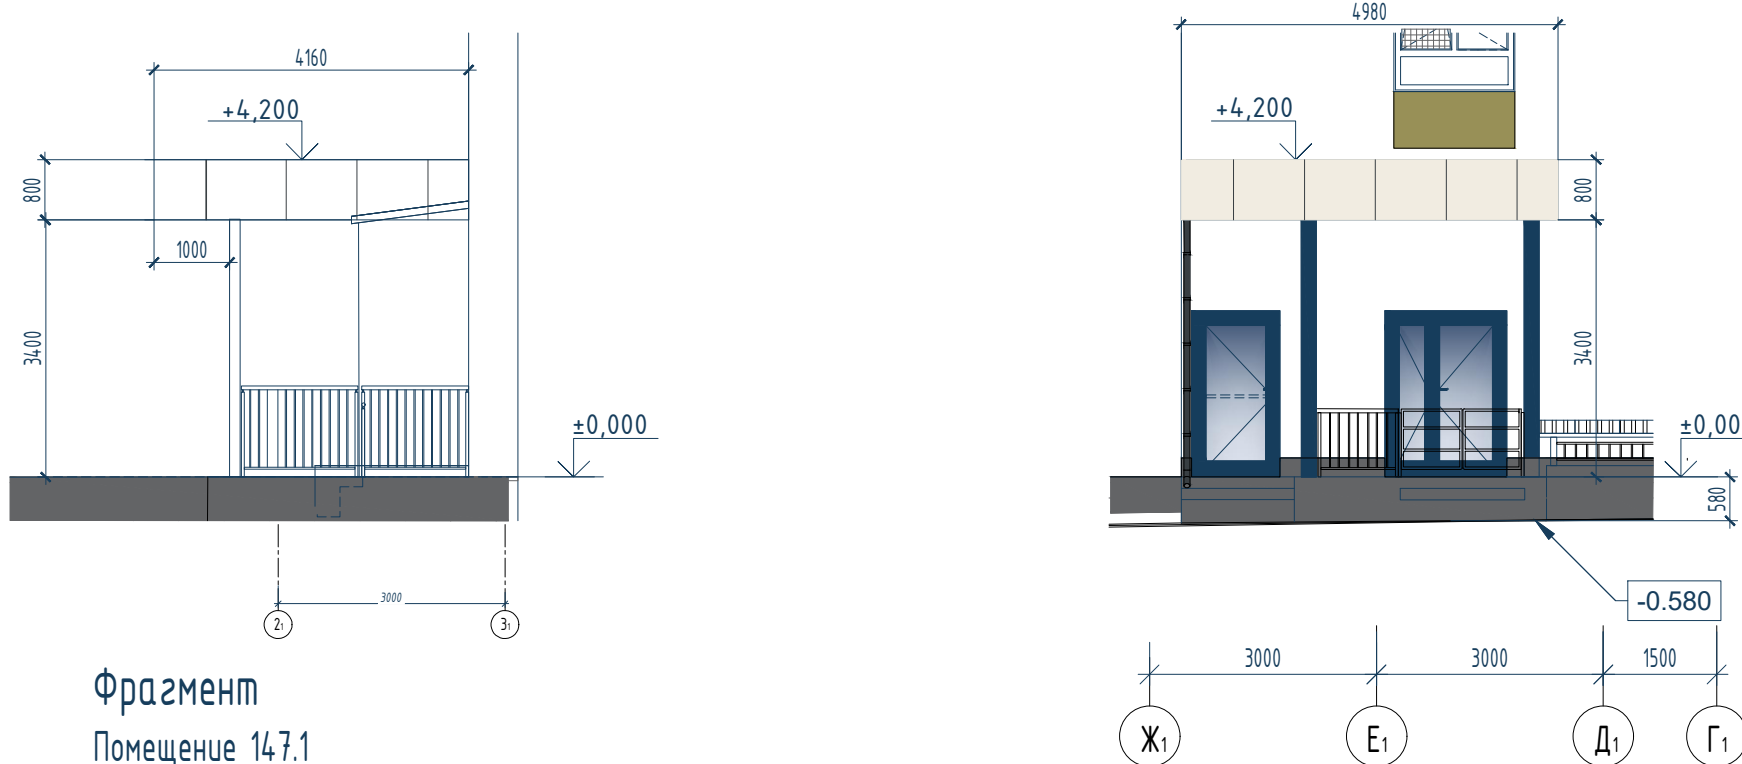


Фрагмент
Помещение 147.1
с холодильным оборудованием
разрез 1-1

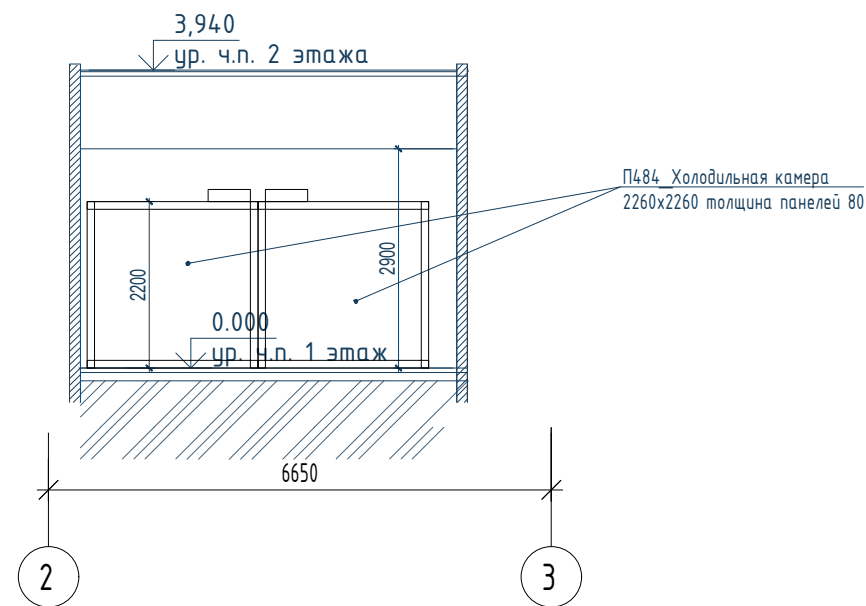

ПРИМЕЧАНИЕ:
1) Привязки канализационных трапов см. раздел ВК.
Уклон пола в местах размещения трапов и лотков должен составлять 1-2%.
Уклон пола в помещении с охлаждаемыми камерами не должен превышать 1%.
Дренажные лотки должны быть со съёмной антискользящей решеткой, установка вровень с полом, без уступов.
2) Размеры/привязки к стенам и перегородкам точек подключения оборудования к системам ОВ, ВК, ЭС, СС даны без учета внутренней отделки помещений.
3) Высоты указаны от УЧП(уровня чистого пола).
4) Разводку инженерных коммуникаций выполнить в скрытом исполнении.
5) Диаметры трапов - 100мм согласно СП 30.13330.2020.
6) Предусмотрено заземление для технологического оборудования по периметру помещений(см. раздел ЗОМ).
7) Мощность резервных розеток определяется в разделе ЗОМ согласно СП 256.1325800.2016


						16-25/Г-Р-ТХ2		
						Капитальный ремонт объекта "ГБОУ Школа № 429", расположенного по адресу: г.Москва, ул. Соколиной горы 5-ая, д.14		
Изм.	Кол.уч.	Лист	№ док.	Подпись	Дата	Технологические решения	Статус	Лист
Разраб.	Волкова				25.06.2026		Р	2
Проверил	Ряжкова				25.06.2026			7
						Фрагмент плана 1 этажа. Расстановка оборудования пищеблока. М 1:100	 АЗУРИТ	
Н. контр.	Ворожьев				25.06.2026			
ГИП	Муратов				25.06.2026			

Номер помещения	Наименование	Площадь м2	Кат. помещения
142	Помещение для персонала	11,87	
142.1	Санузел для персонала	2,01	
142.2	Душевая	2,82	
143	ПУИ	4,85	В4
144	Помещение для временного хранения пищевых отходов	6,01	В4
145	Кладовая и моечная оборотной тары	6,92	В4
146	Загрузочный цех	7,45	В4
147	Коридор	28,66	
147.1	Помещение с холодильным оборудованием	26,78	В3
148	Кладовая сухих продуктов	10,93	В4
149	Догоотовочный цех	15,16	В3
150	Горячий цех	39,25	В3
151	Моечная для кухонной посуды	9,75	Д
152	Моечная для столовой посуды	34,78	Д
152.1	Промывочная	5,48	Д
153	Холодный цех	15,32	В3
154	Обеденный зал	184,39	

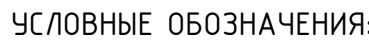

ϕ 1/2"	- Диаметр подвода в дюймах
ϕ 100	- Диаметр подвода в мм.
H	- Высота подвода в мм. от УЧП
●	- ХВ (Холодная вода)
●	- ГВ (Горячая вода)
●	- К (Канализация)
⌘	- Трап
⌘	- Дренажный лоток


Схема 2
Отвод сточных вод от пароконвектомата

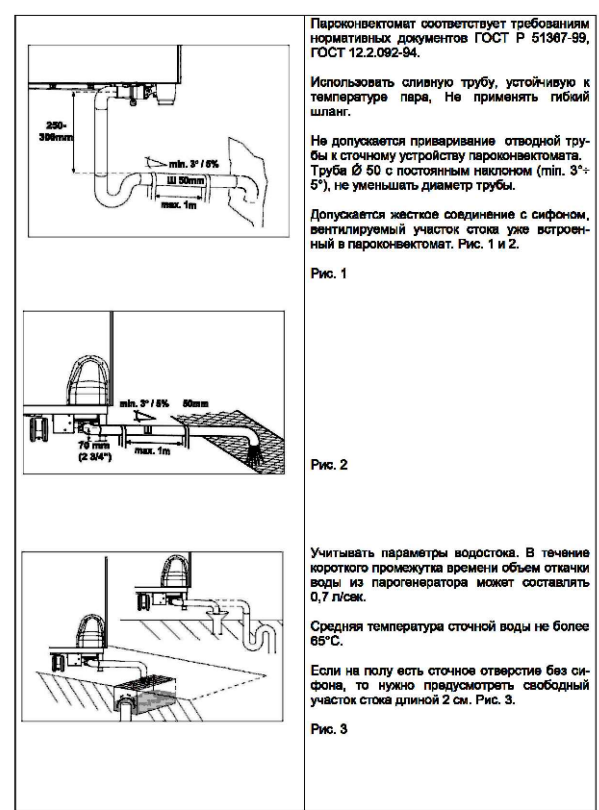

					16-25/Г-Р-ТХ2		
					Капитальный ремонт объекта "ГБОУ Школа № 429", расположенного по адресу: г.Москва, ул. Соколиной горы 5-ая, д.14		
Изм.	Колуч	Лист	№ док	Подпись	Дата		
Разработ.			Волкова		25.06.2025		
Проверил			Рябова		25.06.2025		
Технологические решения						Стандия	Лист
						Р	3
Н. контр.			Ворожьев		25.06.2025		
ГИП			Муратов		25.06.2025		
Фрагмент 1-го этажа. План подключения технологического оборудования к сетям ВК						 АЗУРИТ	

Инв. № подл.	Подпись и дата	Взам. инв. №


Номер помещения	Наименование	Площадь м2	Кат. помещения
142	Помещение для персонала	11,87	
142.1	Санузел для персонала	2,01	
142.2	Душевая	2,82	
143	ПУИ	4,85	В4
144	Помещение для временного хранения пищевых отходов	6,01	В4
145	Кладовая и моечная обратной тары	6,92	В4
146	Загрузочный цех	7,45	В4
147	Коридор	28,66	
147.1	Помещение с холодильным оборудованием	26,78	В3
148	Кладовая сухих продуктов	10,93	В4
149	Догоотовочный цех	15,16	В3
150	Горячий цех	39,25	В3
151	Моечная для кухонной посуды	9,75	Д
152	Моечная для столовой посуды	34,78	Д
152.1	Предмоечная	5,48	Д
153	Холодный цех	15,32	В3
154	Обеденный зал	184,39	

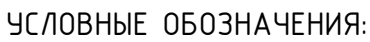

ϕ 1/2" - Диаметр подвода в дюймах
ϕ 100 - Диаметр подвода в мм.
H - Высота подвода в мм. от УЧП
● - ХВ (Холодная вода)
● - ГВ (Горячая вода)
● - К (Канализация)
⌘ - Трап
⌘ - Дренажный лоток

Схема 2

Отвод сточных вод от пароконвектомата

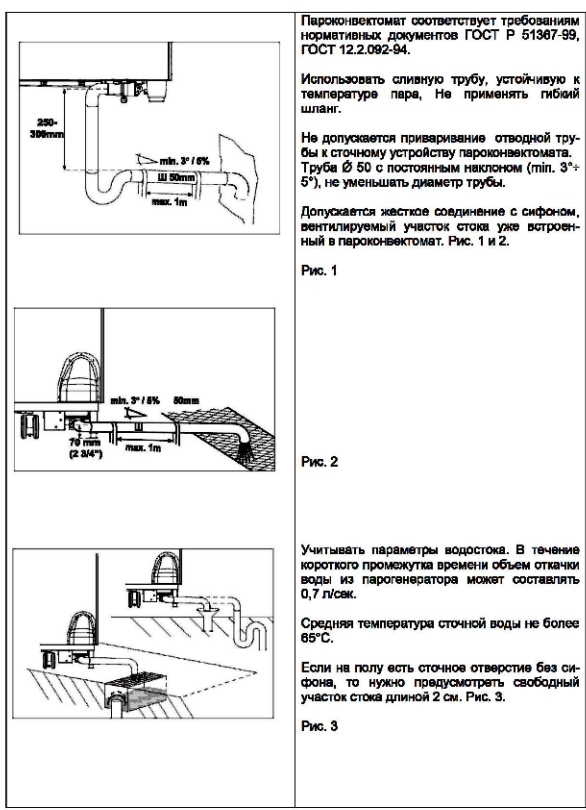


ПРИМЕЧАНИЕ:

- 1) Привязки канализационных трапов см. раздел ВК.
Уклон пола в местах размещения трапов и лок должен составлять 1-2%.
Уклон пола в помещении с охлаждаемыми камерами не должен превышать 1%.
Дренажные лотки должны быть со съемной антискользящей решеткой, установка вровень с полом, без уступов.
- 2) Размеры/привязки к стенам и перегородкам точек подключения оборудования к системам ВК даны без учета внутренней отделки помещений.
- 3) Оборудование для приготовления пищи и моечные ванны подключить к канализации с воздушным разрывом струи не менее 20 мм.


						16-25/Г-Р-ТХ2		
						Капитальный ремонт объекта "БЮУ Школа № 429", расположенного по адресу: г.Москва, ул. Соколиной горы 5-ая, д.14		
Изм.	Кол.уч	Лист	№ док	Подпись	Дата	Технологические решения		Статья
Разработ			Волкова		25.06.2026			Лист
Проверил			Райкова		25.06.2026	р		Листов
								4
								7
Н. контр.	Ворожьев				25.06.2026	Фрагмент 1-го этажа. План подключения технологического оборудования к сетям ВК (с оборудованием)		 АЗУРИТ
ГИП	Муршов				25.06.2026			

Номер помещения	Наименование	Площадь м2	Кат. помещ.
142	Помещение для персонала	11,87	
142.1	Санузел для персонала	2,01	
142.2	Душевая	2,82	
143	ПМ	4,85	В4
144	Помещение для временного хранения пищевых отходов	6,01	В4
145	Кладовая и моечная оборотной тары	6,92	В4
146	Загрузочный цех	7,45	В4
147	Коридор	28,66	
147.1	Помещение с холодильным оборудованием	26,78	В3
148	Кладовая сухих продуктов	10,93	В4
149	Догоотовочный цех	15,16	В3
150	Горячий цех	39,25	В3
151	Моечная для кухонной посуды	9,75	Д
152	Моечная для столовой посуды	34,78	Д
152.1	Предмоечная	5,48	
153	Холодный цех	15,32	В3
154	Обеденный зал	184,39	

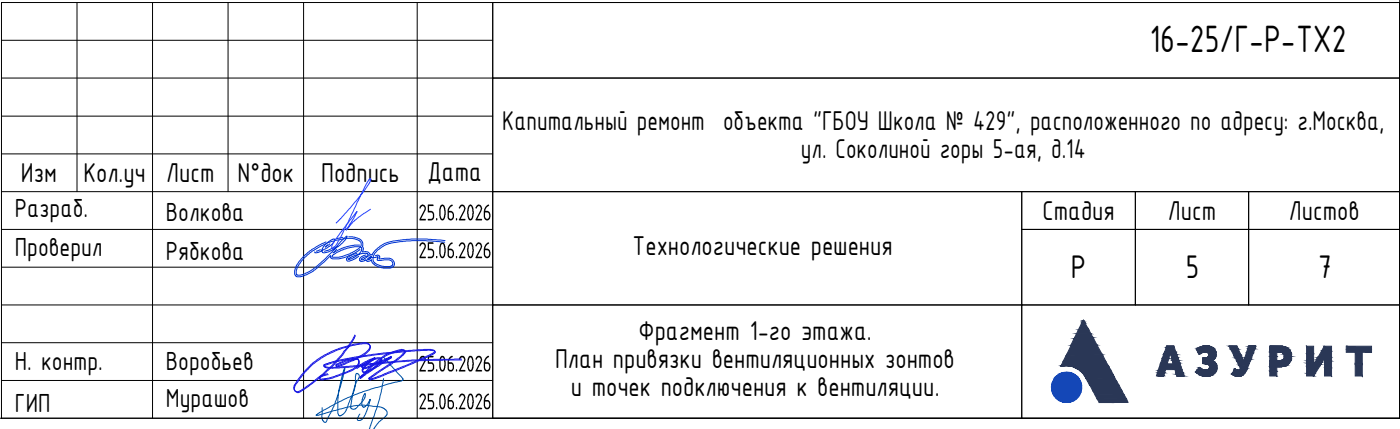


Экспликация помещений 1-го этажа

Номер помеще-ния	Наименование	Площадь м2	Кат. помеще-ния
14.2	Помещение для персонала	11,87	
14.2.1	Санузел для персонала	2,01	
14.2.2	Душевая	2,82	
14.3	ПУИ	4,85	В4
14.4	Помещение для временного хранения пищевых отходов	6,01	В4
14.5	Кладовая и моечная оборотной тары	6,92	В4
14.6	Загрузочный цех	7,45	В4
14.7	Коридор	28,66	
14.7.1	Помещение с холодильным оборудованием	26,78	В3
14.8	Кладовая сухих продуктов	10,93	В4
14.9	Дозировочный цех	15,16	В3
150	Горячий цех	39,25	В3
151	Моечная для кухонной посуды	9,75	Д
152	Моечная для столовой посуды	34,78	Д
152.1	Предмоечная	5,48	Д
153	Холодный цех	15,32	В3
154	Обеденный зал	184,39	

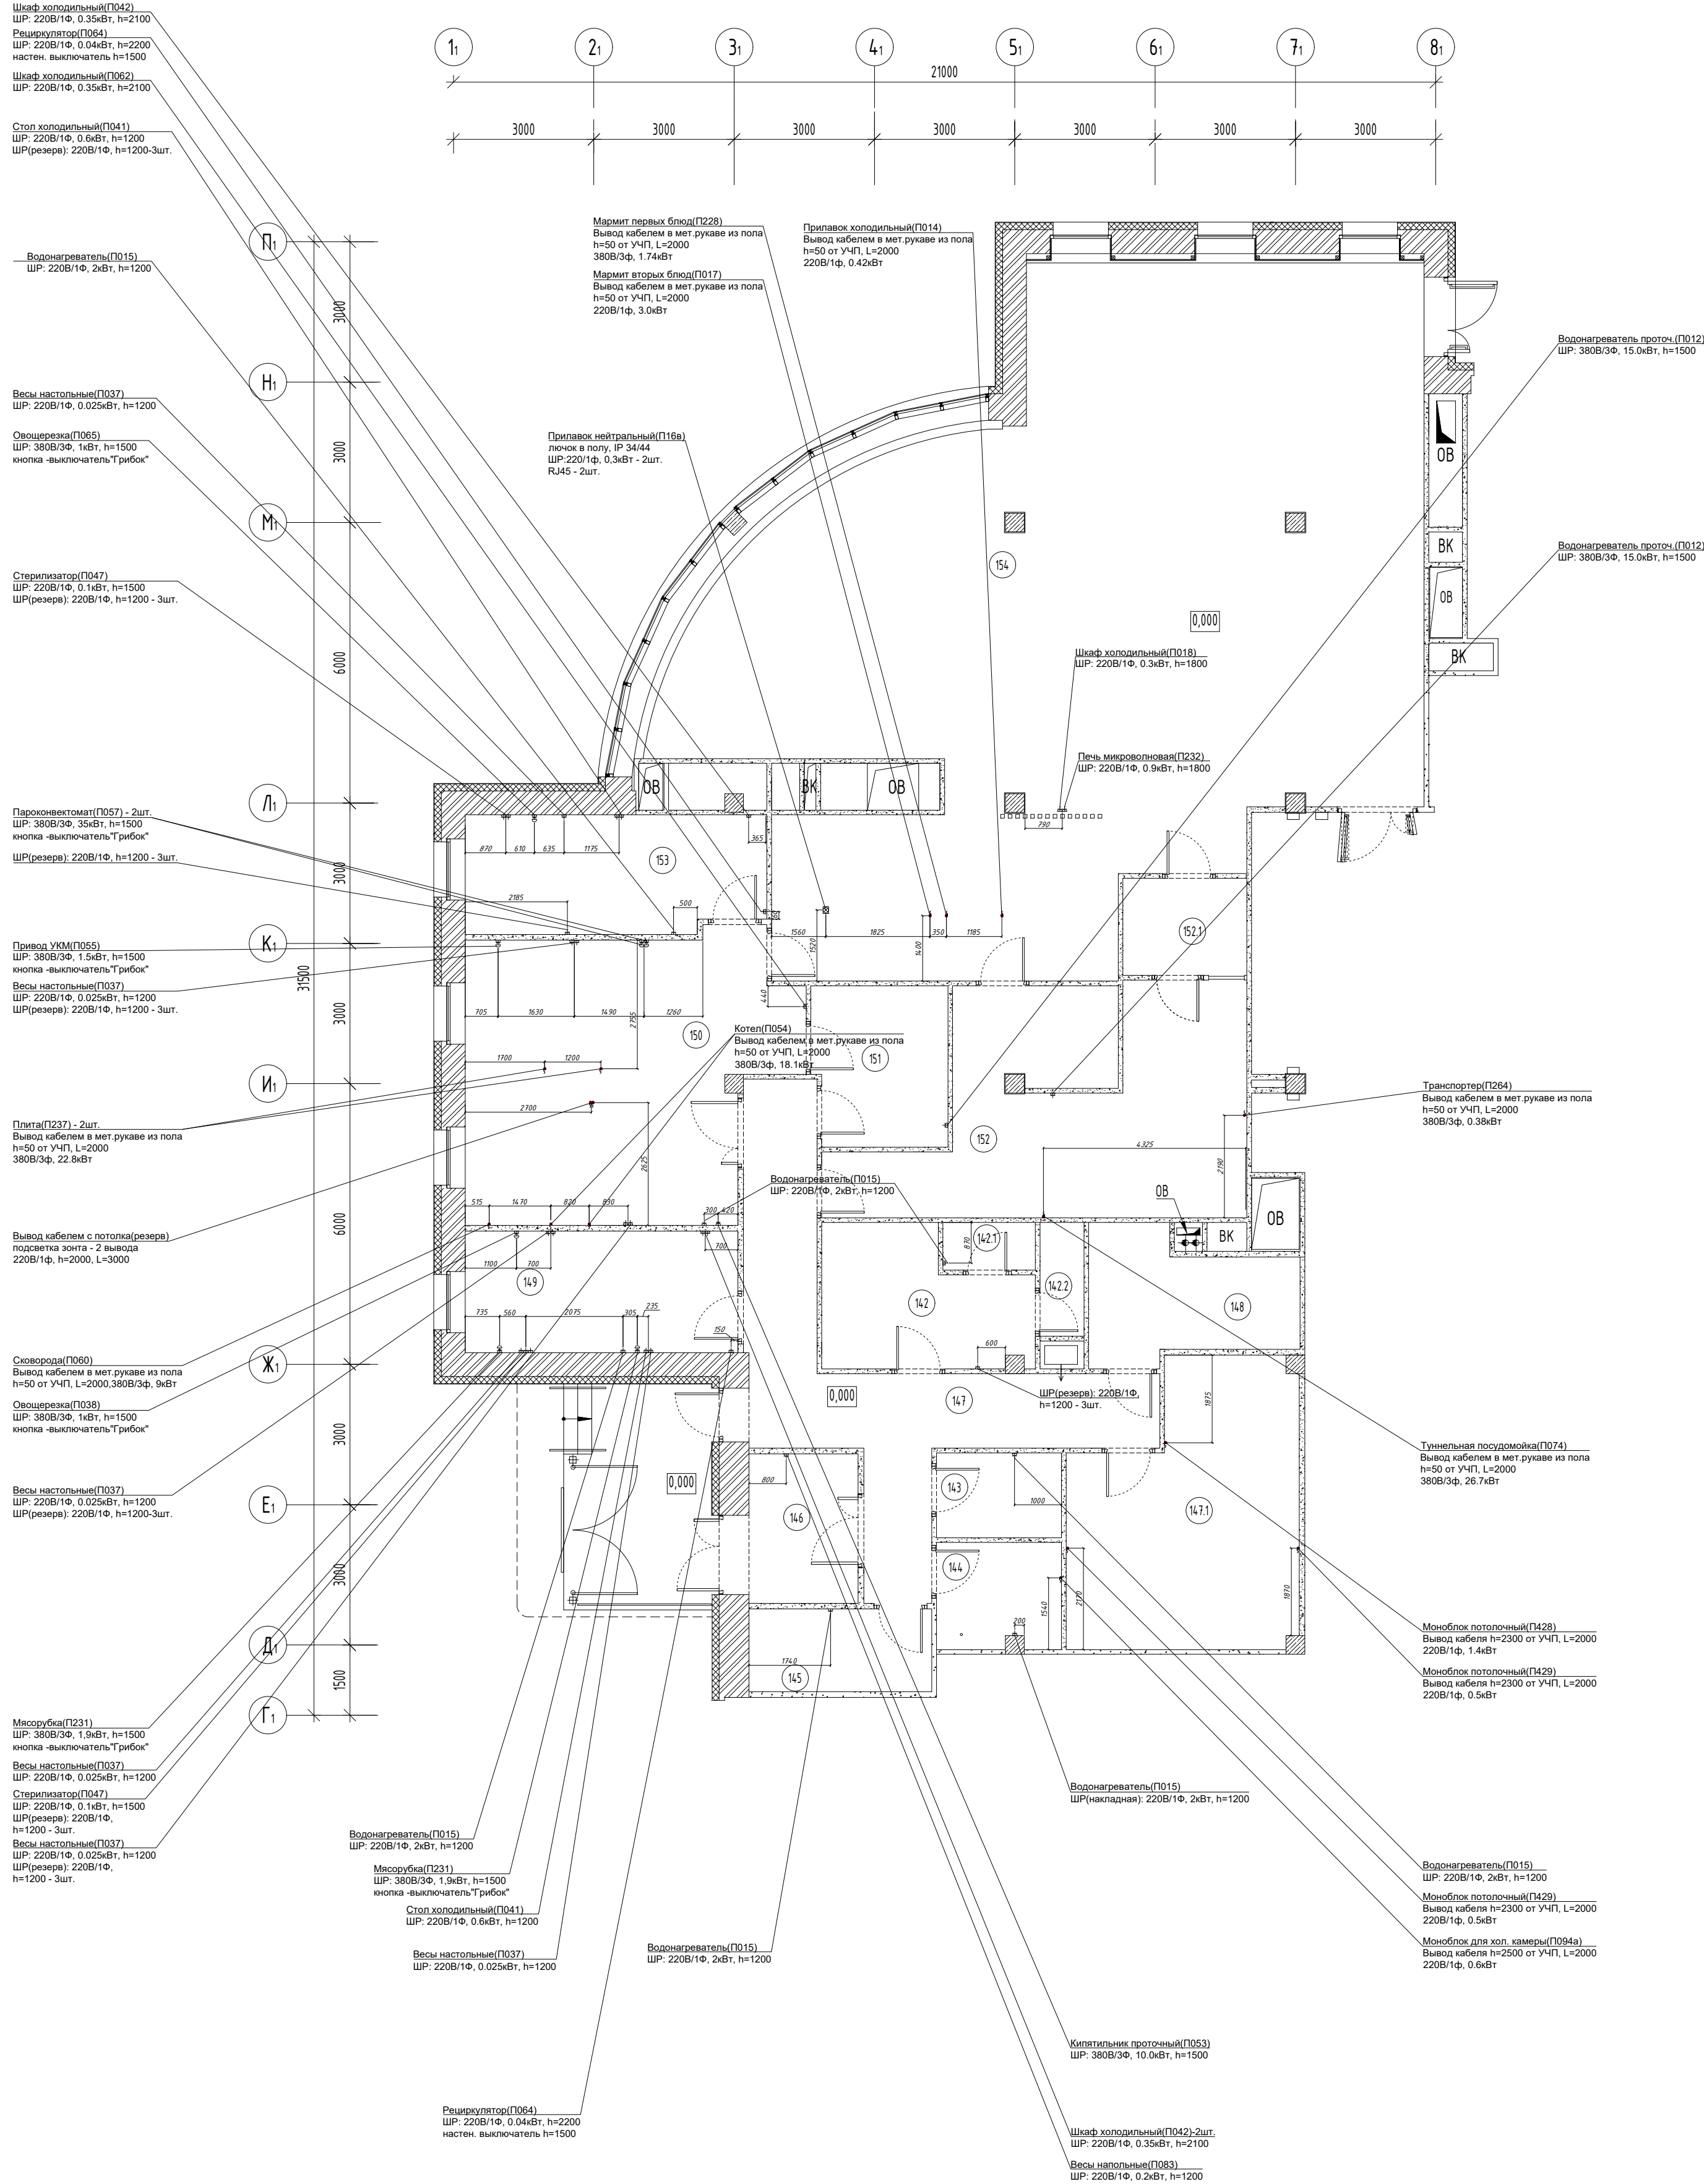

УСЛОВНЫЕ ОБОЗНАЧЕНИЯ:

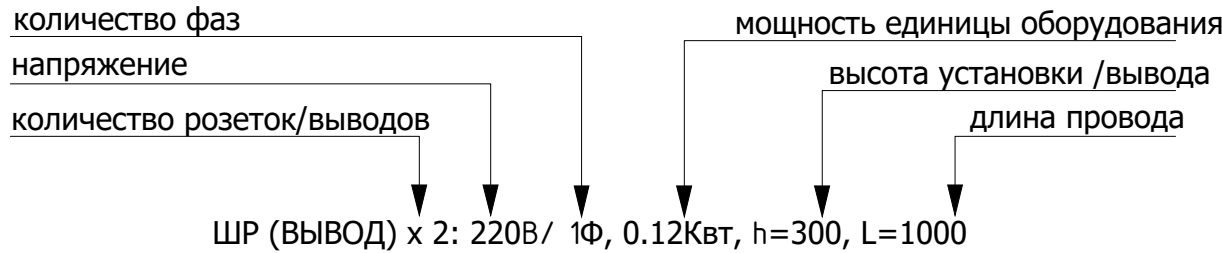

	- Штепсельная розетка 220В
	- Штепсельная розетка 380В
	- Вывод кабеля
	- Аварийная кнопка(Грибок)
	- Лючок в полу

ПРИМЕЧАНИЕ:

- 1) Размеры/привязки к стенам и перегородкам точек подключения оборудования к системам ЭС, СС даны без учета внутренней отделки помещений.
2) Высоты указаны от УЧП(уровня чистого пола).
3) Разводку инженерных коммуникаций выполнить в скрытом исполнении.
4) Предусмотрено заземление для технологического оборудования по периметру помещений(см. раздел ЗОМ).
5) Мощность резервных розеток определяется в разделе ЗОМ согласно СП 256.1325800.2016

№ пом. в ГЧ	Помещение	№ Поз.	Наименование	Ед. изм.	Кол- во	Марка оборудования	Габариты (ШхГхВ), мм	Напряж., В/ кол-во фаз	Эл. Мощность, кВт	ВК	ОВ	Примечание
----------------	-----------	-----------	--------------	-------------	------------	-----------------------	-------------------------	---------------------------	-------------------	----	----	------------

154	Обеденный зал	П002	Стол обеденный школьный № 4, 1500х600	шт.	21							
154	Обеденный зал	П003	Стол обеденный школьный № 5, 1200х600	шт.	3							
154	Обеденный зал	П250	Стол обеденный школьный № 5, 1800х600	шт.	12							
154	Обеденный зал	П005	Табурет №4	шт.	126							
154	Обеденный зал	П006	Табурет №5	шт.	84							
154	Обеденный зал	б/н	Шторы рулонные тип 1	к-т	9	1410х2600-3шт. 2000х2600 -6 шт						штора на окно прямое - 1410*2600мм 3шт.; штора на полукруглый витраж 2000*2600мм 6шт.
154	Обеденный зал.	П300	Тележка для сбора посуды	шт.	2	ТСП-80/50, Кобор	800х500х940					2 уровня, расстояние между уровнями 450мм
154	Обеденный зал.	П011	Тележка-шпилька для подносов	шт.	4	ШП-48/31, Кобор	310х480х1760					
154	Обеденный зал	П017	Мармит для вторых блюд тип 3	шт.	1	ЭМК-70КМ-01	1500х1030х1482	220В/1ф	3,012			
154	Обеденный зал	П228	Мармит для первых блюд тип 2	шт.	1	ПМЭС-70КМ, Абат	1120х705(1030)х1240	380В/3ф	1,742			
154	Обеденный зал	П014	Прилавок-витрина холодильный тип 3	шт.	1	ПВВ(Н)-70КМ-С-01-НПШ, Абат	1500х705(1030)х1721	220В/1ф	0,417		Холодильное оборудование	
154	Обеденный зал	П239	Прилавок для столовых приборов и подносов тип 1	шт.	1	ПСП-70КМ, Абат	630х675х1242					
154	Обеденный зал	П016в	Прилавок нейтральный тип 2	шт.	1	ПВН-70КМ, Абат	1120х705(1030)х1721	220В/1ф	0,03			
154	Обеденный зал	П019	Рукомойник	шт.	1	ВРК-330, Atesy	332х337х152			ХГВ, К		
154	Обеденный зал	б/н	Сифон для рукомойника.	шт.	1							
154	Обеденный зал	б/н	Смеситель для рукомойника	шт.	1							
154	Обеденный зал	П022	Шкаф-стол рабочий двухдверный тип 1	шт.	1		800х600х850					
154	Обеденный зал	П232	Микроволновая печь	шт.	1	Samsung MG30T5018AK/B W или аналог	517х297х425	220/1ф	0,9			
154	Обеденный зал	П024в	Ограждение тип 1	шт.	1							
154	Обеденный зал	П024г	Ограждение с калиткой (телескопической)	шт.	1							
154	Обеденный зал	П025	Стол производственный 900х600	шт.	1	СПП-223/900 , Техно-ТТ	900х600х850					

						16-25/Г-Р-ТХ2.СО			
						Капитальный ремонт объекта "ГБОУ Школа № 429 "Соколиная гора", расположенного по адресу: г.Москва, ул. Соколиной горы 5-я, д.14			
Изм.	Кол. уч.	Лист	№ док	Подпись	Дата				
Разработал	Волкова		07.26	Общие технологические решения			Стадия	Лист	Листов
Проверил	Рябкова		07.26				Р	1	8
Н.контроль	Воробьев		07.26	Спецификация технологического оборудования и мебели			 АЗУРИТ		
ГИП	Мурашов		07.26						

		№ пом. в ГЧ	Помещение	№ Поз.	Наименование	Ед. изм.	Кол-во	Марка оборудования	Габариты (ШхГхВ), мм	Напряж., В/ кол-во фаз	Эл. Мощность, кВт	ВК	ОВ	Примечание		
Взам. инв. №		154	Обеденный зал	П018	Шкаф холодильный	шт.	1		600х600х2000	220/1ф	0,3		холодильное оборудование			
		150	Горячий цех	П044	Ванна моечная односекционная тип 1	шт.	1	ВМ-С3606, Камик	600х600х850			ХГВ, К				
		150	Горячий цех	б/н	Сифон для ванны моечной	шт.	1									
		150	Горячий цех	б/н	Смеситель для ванны моечной.	шт.	1									
		150	Горячий цех	П037	Весы настольные	шт.	2	ПВм-3/32-ЖКИ, Мера	220х300х120	220/1ф	0,025					
		150	Горячий цех	П210	Зонт вытяжной пристенный для пароконвектомата	шт.	2	Restinox ЗВП-10/12	1000х1200х350				1200 куб.м/ч или по расчету			
		150	Горячий цех	П219	Зонт приточно-вытяжной	шт.	1	Restinox ЗВП-18/12	1800х1200х350				2000 куб.м/ч или по расчету			
		150	Горячий цех	П483	Зонт приточно-вытяжной 1500х1200	к-т	2	ЗПВН-03 1500/1200	1500х1200х400				2400 куб.м/ч или по расчету			
		150	Горячий цех	П053	Кипятильник электрический на подставке	к-т	1	КНЭ-100-01, Дебис	250х250х360	380/3ф	10	ХВ, К				
		150	Горячий цех	П054	Котел пищеварочный 250 л	шт.	2	КПЭМ-250/9Т, Абат	840х1000х1290	380/3ф	18,1	ХВ, К				
		150	Горячий цех	П031	Магнитный держатель для ножей	шт.	2	1970000, Sanelli	380х48х13							
		150	Горячий цех	П055	Машина кухонная универсальная	шт.	1	УКМ П, Торгмаш	920х586х887	380/3ф	1,1					
		150	Горячий цех	б/н	Набор гастроемкостей с крышками для пароконвектомата 20 уровней	набор	2									
		150	Горячий цех	П057	Пароконвектомат 20 уровней	шт.	2	Чувашторгтехника Abat ПКА 20-1/1ПМ2-01 или эквивалент	890х890х1780	380/3ф	35	ХВ, К умягчитель				
		150	Горячий цех	б/н	Водоумягчитель	шт.	3									
		150	Горячий цех	П237	Плита электрическая 6 конфорок тип 2	шт.	2	ПЭ-0,54Ш, Продмаш	1200х800х850	380/3ф	20					
		150	Горячий цех	П032	Подставка под кухонный инвентарь	шт.	2	ПКИ-П-400.400.420-02 Атеси	400х400х400							
		150	Горячий цех	П039	Полка для хранения разделочных досок	шт.	1	ПН-115/600, Техно-ТТ	600х355х270							
		150	Горячий цех	П019	Рукомойник	шт.	1	ВРК-330, Atesy	332х337х152				ХГВ,К			
		150	Горячий цех	б/н	Сифон для рукомойника.	шт.	1									
		150	Горячий цех	б/н	Смеситель для рукомойника	шт.	1									
		150	Горячий цех	П060	Сковорода электрическая 70 л	шт.	1	Abat ЭСК-90-0,47-70 или аналог	840х1045х940	380/3ф	12					
		150	Горячий цех	П218	Зонт приточно-вытяжной 1000х1200	шт.	1	ЗПВН-04 1000/1200	1000х1200х400							
Подп. и дата		150	Горячий цех	П025	Стол производственный 900х600	к-т	4	СПП-223/900 , Техно-ТТ	900х600х850							
		150	Горячий цех	П035	Стол производственный 1200х600	к-т	2	СП-223/1200, Техно-ТТ	1200х600х850							
		150	Горячий цех	П061	Стол-вставка нейтральная тип 2	шт.	3	ПМП-40	400х850х850							
		150	Горячий цех	П131	Тележка с баком для отходов	шт.	1	КАУМАН ТБ-23	450х450х500							
		150	Горячий цех	П049	Тележка-шпилька для гастрೋмкостей	шт.	1	СТР-331/406, Техно-ТТ	370х545х1510							
Инв. № подл.																Лист
										16-25/Г-Р-TX2.CO						2
		Изм.	Кол. уч.	Лист	№ док.	Подпись	Дата									

		№ пом. в ГЧ	Помещение	№ Поз.	Наименование	Ед. изм.	Кол-во	Марка оборудования	Габариты (ШхГхВ), мм	Напряж., В/ кол-во фаз	Эл. Мощность, кВт	ВК	ОВ	Примечание				
Взам. инв. №		150	Горячий цех	П062	Шкаф холодильный 500	шт.	1	СМ105-S, Полаир	697х695х1960	220/1ф	0,35		холодильное оборудование					
		150	Горячий цех	П015	Водонагреватель накопительный, 100л	шт.	1	ЭНВ-НЕРЖ-100 Теплокс	493х283х1187	220/1ф	2	ХВ						
		153	Холодный цех	П044	Ванна моечная односекционная тип 1	шт.	2	ВМ-С3606, Камик	600х600х850				ХГВ, К					
		153	Холодный цех	б/н	Сифон для ванны моечной	шт.	2											
		153	Холодный цех	б/н	Смеситель с душирующим устройством	шт.	1											
		153	Холодный цех	б/н	Смеситель для ванны моечной.	шт.	2											
		153	Холодный цех	П037	Весы настольные	шт.	1	ПВм-3/32-ЖКИ, Мера	220х300х120	220/1ф	0,25							
		153	Холодный цех	П031	Магнитный держатель для ножей	шт.	1	1970000, Sanelli	380х48х13									
		153	Холодный цех	П064	Облучатель бактерицидный	шт.	1	ОРУБн2-01-«КРОНТ» (ДЕЗАР-2н)	605х365х145	220/1ф	0,38							
		153	Холодный цех	П065	Овощерезательно-протирочная машина	шт.	1	Торгмаш МПР-350М	600х340х650	380/3ф	1							
		153	Холодный цех	П032	Подставка под кухонный инвентарь	шт.	1	ПКИ-П-400.400.420-02 Атеси	400х400х400									
		153	Холодный цех	П039	Полка для хранения разделочных досок	шт.	1	ПН-115/600, Техно-ТТ	600х355х270									
		153	Холодный цех	П019	Рукомойник	шт.	1	ВРК-330, Atesy	332х337х152				ХГВ, К					
		153	Холодный цех	б/н	Сифон для рукомойника.	шт.	1											
		153	Холодный цех	б/н	Смеситель для рукомойника	шт.	1											
		153	Холодный цех	П047	Стерилизатор для ножей ультрафиолетовый	шт.	1	СТУ-1-18-02-1, Атеси	400х150х600	220/1ф	0,08							
		153	Холодный цех	П048	Стол производственный 600х600	к-т	1	СПП-223/600 , Техно-ТТ	600х600х850									
		153	Холодный цех	П035	Стол производственный 1200х600	к-т	4	СП-223/1200, Техно-ТТ	1200х600х850									
		153	Холодный цех	П025	Стол производственный 900х600	шт.	1	СПП-223/900 , Техно-ТТ	900х600х850									
		153	Холодный цех	П131	Тележка с баком для отходов	шт.	1	КАУМАН ТБ-23	450х450х500									
		153	Холодный цех	П049	Тележка-шпилька для гастрoёмкостей	шт.	1	СТР-331/406, Техно-ТТ	370х545х1510									
		153	Холодный цех	П041	Холодильный стол тип 2	шт.	1	ТМ2-G, Полаир	1200х600х850	220/1ф	0,6							
		Подп. и дата		153	Холодный цех	П042	Шкаф холодильный 700	шт.	1	СМ-107G, Полаир	697х925х1960	220/1ф	0,35		Холодильное оборудование			
				153	Холодный цех	П015	Водонагреватель накопительный, 100л	шт.	1	ЭНВ-НЕРЖ-100 Теплокс	493х283х1187	220/1ф	2	ХВ				
				149	Доготовочный цех	П044	Ванна моечная односекционная тип 1	шт.	3	ВМ-С3606, Камик	600х600х850							
149	Доготовочный цех			б/н	Сифон для ванны моечной	шт.	3											
149	Доготовочный цех			б/н	Смеситель для ванны моечной.	шт.	3											
Инв. № подл.		149	Доготовочный цех	П037	Весы настольные	шт.	3	ПВм-3/32-ЖКИ, Мера	220х300х120	220/1ф	0,25							
		149	Доготовочный цех	П031	Магнитный держатель для ножей	шт.	2	1970000, Sanelli	380х48х13									
		149	Доготовочный цех	П231	Мясорубка 300	шт.	2	МИМ300, Белторгмаш	680х400х460	380/3ф	1,9							
											Изм.	Кол. уч.	Лист	№ док.	Подпись	Дата	16-25/Г-Р-ТХ2.СО	Лист
																		3

		№ пом. в ГЧ	Помещение	№ Поз.	Наименование	Ед. изм.	Кол- во	Марка оборудования	Габариты (ШхГхВ), мм	Напряж., В/ кол-во фаз	Эл. Мощность, кВт	ВК	ОВ	Примечание		
		149	Доготовочный цех	П038	Овощерезательная машина	шт.	1	МПР-350М-02	600х300х650	380/3ф	1					
		149	Доготовочный цех	П032	Подставка под кухонный инвентарь	шт.	3	ПКИ-П-400.400.420-02 Атеси	400х400х400							
		149	Доготовочный цех	П039	Полка для хранения разделочных досок	шт.	2	ПН-115/600, Техно-ТТ	600х355х270							
		149	Доготовочный цех	П064	Облучатель бактерицидный	шт.	1	ОРУБн2-01-«КРОНТ» (ДЕЗАР-2н)	605х365х145	220/1ф	0,038					
		149	Доготовочный цех	П019	Рукомойник	шт.	1	ВРК-330, Atesy	332х337х152				ХГВ, К			
		149	Доготовочный цех	б/н	Сифон для рукомойника.	шт.	1									
		149	Доготовочный цех	б/н	Смеситель для рукомойника	шт.	1									
		149	Доготовочный цех	П047	Стерилизатор для ножей ультрафиолетовый	шт.	1	СТУ-1-18-02-1, Атеси	400х150х600	220/1ф	0,08					
		149	Доготовочный цех	П025	Стол производственный 900х600	к-т	2	СПП-223/900 , Техно-ТТ	900х600х850							
		149	Доготовочный цех	П035	Стол производственный 1200х600	к-т	2	СП-223/1200, Техно-ТТ	1200х600х850							
		149	Доготовочный цех	П131	Тележка с баком для отходов	шт.	1	КАУМАН ТБ-23	450х450х500							
		149	Доготовочный цех	П049	Тележка-шпилька для гастрорёмокстей	шт.	1	СТР-331/406, Техно-ТТ	370х545х1510							
		149	Доготовочный цех	П041	Холодильный стол тип 2	шт.	1	ТМ2-G, Полаир	1200х600х850	220/1ф	0,6		Холодильное оборудование			
		149	Доготовочный цех	П042	Шкаф холодильный 700	шт.	2	СМ-107G, Полаир	697х925х1960	220/1ф	0,35		Холодильное оборудование			
		149	Доготовочный цех	П015	Водонагреватель накопительный, 100л	шт.	1	ЭНВ-НЕРЖ-100 Теплокс	493х283х1187	220/1ф	2	ХВ				
		145	Кладовая и моечная оборотной тары	П026	Ванна моечная двухсекционная тип 2	шт.	1	К-ВМО-2/1340/700, КАУМАН	1340х700х850			ХГВ, К				
		145	Кладовая и моечная оборотной тары	б/н	Сифон для ванны моечной	шт.	2									
		145	Кладовая и моечная оборотной тары	б/н	Смеситель с душирующим устройством	шт.	1									
		145	Кладовая и моечная оборотной тары	б/н	Смеситель для ванны моечной.	шт.	1									
		145	Кладовая и моечная оборотной тары	П214	Зонт вытяжной	шт.	1	МВО-1,4МСВ-0,8П ТЕХНО-ТТ	1400х800х400				250 куб.м/ч или по расчету			
		145	Кладовая и моечная оборотной тары	П019	Рукомойник	шт.	1	ВРК-330, Atesy	332х337х152			ХГВ, К				
		145	Кладовая и моечная оборотной тары	б/н	Сифон для рукомойника.	шт.	1									
		145	Кладовая и моечная оборотной тары	б/н	Смеситель для рукомойника	шт.	1									
		145	Кладовая и моечная оборотной тары	П069	Стеллаж с перфорированными полками 900х500	шт.	2	СТР-524/900, Техно-ТТ	900х500х1800							
		145	Кладовая и моечная оборотной тары	П015	Водонагреватель накопительный, 100л	шт.	1	ЭНВ-НЕРЖ-100 Теплокс	493х283х1187	220/1ф	2	ХВ				
		152	Моечная для столовой посуды	П071	Ванна моечная двухсекционная тип 1	шт.	1	ВМ2 ПроК (Россия)	1200х600х850			ХГВ, К				
		152	Моечная для столовой посуды	б/н	Сифон для ванны моечной	шт.	2									
		152	Моечная для столовой посуды	б/н	Смеситель для ванны моечной.	шт.	1									
		152	Моечная для столовой посуды	б/н	Смеситель с душирующим устройством	шт.	1									
Взам. инв. №															Лист 4	
										Изм.	Кол. уч.	Лист	№ док.	Подпись		Дата

		№ пом. в ГЧ	Помещение	№ Поз.	Наименование	Ед. изм.	Кол-во	Марка оборудования	Габариты (ШхГхВ), мм	Напряж., В/ кол-во фаз	Эл. Мощность, кВт	ВК	ОВ	Примечание		
152	Моечная для столовой посуды	П072	Ванна моечная трехсекционная тип 2	шт.	1	ВМЗ ПроК (Россия), 1700х600х850	1700х600х850					ХГВ, К				
		б/н	Сифон для ванны моечной	шт.	3											
		б/н	Смеситель для ванны моечной.	шт.	2											
		б/н	Смеситель с душирующим устройством	шт.	1											
		П212	Зонт вытяжной 1200х700	шт.	1	МВО-1,2МСВ-0,7П, Техно-ТТ	1200х700х400мм						250 куб.м/ч или по расчету			
		П216	Зонт вытяжной 1800х700	шт.	1	МВО-1,8МСВ-0,7ПК, Техно-ТТ	1800х700х400мм						400 куб.м/ч или по расчету			
		П074	Машина посудомоечная туннельная	к-т	1	МПТ-1700-01 (левая), Абат	1595х730х1965	380/3ф	26,7							
		б/н	Водоумягчитель	шт.	1											
		П019	Рукомойник	шт.	1	ВРК-330, Atesy	332х337х152					ХГВ, К				
		б/н	Сифон для рукомойника.	шт.	1											
		б/н	Смеситель для рукомойника	шт.	1											
		П075	Стеллаж для сушки посуды	шт.	4	СПП-02, Проммаш	800х632х1600									
		П076	Стеллаж для хранения столовой посуды	шт.	5	СКС -90/30/430	900х300х1600									
		П074.1	Стол предмоечный универсальный	шт.	1	СПМП-7-7, Абат	1715х705х1080					ХГВ, К				
		П258	Стол раздаточный для туннельных посудомоечных машин	шт.	1	СПМР-6-2, Абат	704х635х900									
		П079	Стол для сбора остатков пищи 600	шт.	1	НДСО-6/6БП, HiCOLD	600х600х850									
		П048	Стол производственный 600х600	к-т	2		600х600х850									
		П025	Стол производственный 900х600	шт.	3	СПП-223/900 , Техно-ТТ	900х600х850									
		П131	Тележка с баком для отходов	шт.	1	КАУМАН ТБ-23	450х450х500									
		152	Моечная для столовой посуды	П264	Транспортер для сбора использованной посуды	шт.	1	КАЮР-М	4045х765х880	380/3ф	0,38				Левое исполнение (лентаслева от ведущего модуля). Общая длина 4045мм. Транспортер КАЮР-М - Ведущий модуль (1м) код: 18714 Промежуточный модуль (2м) код: 18717 Натяжной модуль (1м) код: 18715 Комплект транспортной ленты код: 18789	
		152	Моечная для столовой посуды	П012	Водонагреватель проточный ЭВПЗ-15, 250л/час, 70С	шт.	1	ЭВПЗ-15 Гродторгмаш	315х220х520	380/3ф	15		ХВ			
		151	Моечная для кухонной посуды	П202	Ванна моечная двухсекционная тип 2	шт.	1	ВМСК-1/13/7-ЭЦ	1340х700х850				ХГВ, К			
		151	Моечная для кухонной посуды	б/н	Сифон для ванны моечной	шт.	2									
Инв. № подл.															16-25/Г-Р-ТХ2.CO	Лист
																5
		Изм.	Кол. уч.	Лист	№ док.	Подпись	Дата									

Взам. инв. №	
Подп. и дата	
Инв. № подл.	

№ пом. в ГЧ	Помещение	№ Поз.	Наименование	Ед. изм.	Кол-во	Марка оборудования	Габариты (ШхГхВ), мм	Напряж., В/ кол-во фаз	Эл. Мощность, кВт	ВК	ОВ	Примечание
151	Моечная для кухонной посуды	б/н	Смеситель для ванны моечной.	шт.	1							
151	Моечная для кухонной посуды	б/н	Смеситель с душирующим устройством	шт.	1							
151	Моечная для кухонной посуды	П213	Зонт вытяжной	шт.	1	Техно-ТТ МВО-1,4МСВ-0,7П	1400х700х400				250 куб.м/ч или по расчету	
151	Моечная для кухонной посуды	П019	Рукомойник	шт.	1	ВРК-330, Atesy	332х337х152			ХГВ, К		
151	Моечная для кухонной посуды	б/н	Сифон для рукомойника.	шт.	1							
151	Моечная для кухонной посуды	б/н	Смеситель для рукомойника	шт.	1							
151	Моечная для кухонной посуды	П069	Стеллаж с перфорированными полками 900х500	шт.	3	СТР-524/900, Техно-ТТ	900х500х1800					
151	Моечная для кухонной посуды	П048	Стол производственный 600х600	к-т	1	СПП-223/600 , Техно-ТТ	600х600х850					
151	Моечная для кухонной посуды	П131	Тележка с баком для отходов	шт.	1	КАУМАН ТБ-23	450х450х500					
151	Моечная для кухонной посуды	П012	Водонагреватель проточный ЭВПЗ-15, 250л/час, 70С	шт.	1	ЭВПЗ-15 Гродторгмаш	315х220х520	380/3ф	15	ХВ		
146	Загрузочный цех	П083	Весы напольные тип 1	шт.	1	ТВ-М-300.2-А013, Масса-К	600х800х750	220/1ф	0,2			
146	Загрузочный цех	П457	Тележка грузовая платформенная	шт.	1	Abat ТГ-6-1	1260х600х935					
148	Кладовая сухих продуктов	П070	Подтоварник 600х600	шт.	2	ПТ606-3, Техно-ТТ	600х600х300					
148	Кладовая сухих продуктов	П085	Стеллаж 900х500	шт.	6	СТР-124/900Техно-ТТ	900х500х1800					
148	Кладовая сухих продуктов	П086	Шкаф для хранения хлеба 900	шт.	2							
147.1	Помещение с холодильным оборудованием	П033	Подтоварник 900х600	шт.	3	ПТ906-3, Техно-ТТ	900х600х300					
147.1	Помещение с холодильным оборудованием	П085	Стеллаж 900х500	шт.	6	СТР-124/900Техно-ТТ	900х500х1800					
147.1	Помещение с холодильным оборудованием	П046а	Стеллаж 1200х500	шт.	3	СТР-124/1200, Техно-ТТ	1200х500х1830					
147.1	Помещение с холодильным оборудованием	П271	Холодильная камера 2000х2300,толщина панелей 100	шт.	1	POLAIR кхн-7,71	2000х2300х2200					
147.1	Помещение с холодильным оборудованием	П484	Холодильная камера 2260х2260, толщина панелей 80	шт.	2	POLAIR кхн-9,0	2260х2260х2200					
147.1	Помещение с холодильным оборудованием	П428	Машина холодильная низкотемпературная	шт.	1	Polair MB214ST потолочный	830х550х665	220/1ф	1,4		600 куб.м/ч или по расчету	-15...-25 °С, для камер 5.1 – 13 м3
147.1	Помещение с холодильным оборудованием	П429	Машина холодильная среднетемпературная	шт.	2	Polair MM111Т потолочный	1003х603х545	220/1ф	0,5		600 куб.м/ч или по расчету	... -5...+10 °С, для камер 1 – 9 м3
144	Помещение для временного хранения пищевых отходов	П093	Ванна котломоечная односекционная	шт.	1	ВК-2 ТММ	1000х600х850					

						16-25/Г-Р-ТХ2.СО				Лист
										6
Изм.	Кол. уч.	Лист	№ док.	Подпись	Дата					

Взам. инв. №	
Подп. и дата	
Инв. № подл.	

№ пом. в ГЧ	Помещение	№ Поз.	Наименование	Ед. изм.	Кол-во	Марка оборудования	Габариты (ШхГхВ), мм	Напряж., В/ кол-во фаз	Эл. Мощность, кВт	ВК	ОВ	Примечание
144	Помещение для временного хранения пищевых отходов	б/н	Сифон для ванны моечной	шт.	1							
144	Помещение для временного хранения пищевых отходов	б/н	Смеситель с душирующим устройством	шт.	1							
144	Помещение для временного хранения пищевых отходов	П019	Рукомойник	шт.	1	ВРК-330, Atesy	332x337x152					
144	Помещение для временного хранения пищевых отходов	б/н	Сифон для рукомойника.	шт.	1							
144	Помещение для временного хранения пищевых отходов	б/н	Смеситель для рукомойника	шт.	1							
144	Помещение для временного хранения пищевых отходов	П069	Стеллаж с перфорированными полками 600x500	шт.	1	СТР-524/900, Техно-ТТ	600x500x1800					
144	Помещение для временного хранения пищевых отходов	П094а	Холодильная камера для отходов 1150x1000	шт.	1	POLAIR KXH-1,28 Minicella MM 1	1150x1000x2355	220/1ф	0,6		600 куб.м/ч или по расчету	
144	Помещение для временного хранения пищевых отходов	П015	Водонагреватель накопительный, 100л	шт.	1	ЭНВ-НЕРЖ-100 Теплокс	493x283x1187	220/1ф	2	ХВ		
143	Помещение для хранения уборочного инвентаря (Пищеблок)	П019	Рукомойник	шт.	1	ВРК-330, Atesy	332x337x152			ХГВ, К		
143	Помещение для хранения уборочного инвентаря (Пищеблок)	б/н	Сифон для рукомойника.	шт.	1							
143	Помещение для хранения уборочного инвентаря (Пищеблок)	б/н	Смеситель для рукомойника	шт.	1							
143	Помещение для хранения уборочного инвентаря (Пищеблок)	П046	Стеллаж	шт.	1	СТР-124/604Техно-ТТ	600x400x1800					
143	Помещение для хранения уборочного инвентаря (Пищеблок)	П070	Подтоварник 600x600	шт.	1	ПТ606-3, Техно-ТТ	600x600x300					
143	Помещение для хранения уборочного инвентаря (Пищеблок)	П098	Шкаф для хозяйственного инвентаря одностворчатый металлический	шт.	1	ШРХ-11 L500, Церера	500x500x1850					
143	Помещение для хранения уборочного инвентаря (Пищеблок)	П015	Водонагреватель накопительный, 100л	шт.	1	ЭНВ-НЕРЖ-100 Теплокс	493x283x1187	220/1ф	2	ХВ		
142	Помещение для персонала (включая душевую и санузел)	П100	Стол обеденный с 2 стульями	к-т	1		1000x600x700					
142	Помещение для персонала (включая душевую и санузел)	П101	Шкаф для одежды металлический двустворчатый Скамья для раздевалок	к-т	7	ШР 22 600 ВСК	600x500x1850					скамья в комплекте
142.1	Санузел для персонала	П015	Водонагреватель накопительный, 100л	шт.	1	ЭНВ-НЕРЖ-100 Теплокс	493x283x1187	220/1ф	2	ХВ		

№ пом. в ГЧ	Помещение	№ Поз.	Наименование	Ед. изм.	Кол- во	Марка оборудования	Габариты (ШхГхВ), мм	Напряж., В/ кол-во фаз	Эл. Мощность, кВт	ВК	ОВ	Примечание
	Кухонный инвентарь	б/н	Венчик	шт.	2							
	Кухонный инвентарь	б/н	Доска разделочная	шт.	24							
	Кухонный инвентарь	б/н	Кассета для столовых приборов	шт.	3							
	Кухонный инвентарь	б/н	Кастрюля с крышкой, 3 л	шт.	3							
	Кухонный инвентарь	б/н	Кастрюля с крышкой, 5 л	шт.	3							
	Кухонный инвентарь	б/н	Котел с крышкой, 10 л	шт.	5							
	Кухонный инвентарь	б/н	Котел с крышкой, 20 л	шт.	5							
	Кухонный инвентарь	б/н	Котел с крышкой, 30 л	шт.	5							
	Кухонный инвентарь	б/н	Котел с крышкой, 40 л	шт.	2							
	Кухонный инвентарь	б/н	Котел с крышкой, 50 л	шт.	2							
	Кухонный инвентарь	б/н	Ложка разливательная 0,25 л	шт.	5							
	Кухонный инвентарь	б/н	Ложка соусная	шт.	5							
	Кухонный инвентарь	б/н	Лопатка кулинарная	шт.	5							
	Кухонный инвентарь	б/н	Миска металлическая	шт.	30							
	Кухонный инвентарь	б/н	Набор дуршлагов	набор	2							
	Кухонный инвентарь	б/н	Нож консервный настольный	шт.	2							
	Кухонный инвентарь	б/н	Нож универсальный большой	шт.	12							
	Кухонный инвентарь	б/н	Нож универсальный малый	шт.	12							
	Кухонный инвентарь	б/н	Нож универсальный средний	шт.	210							
	Кухонный инвентарь	б/н	Поднос пластмассовый (для школьной столовой)	шт.	230							
	Кухонный инвентарь	б/н	Сито	шт.	2							
	Кухонный инвентарь	б/н	Скалка	шт.	2							
	Кухонный инвентарь	б/н	Сковорода с крышкой	шт.	5							
	Кухонный инвентарь	б/н	Сухарница	шт.	36							
	Кухонный инвентарь	б/н	Терка овощная универсальная	шт.	2							
	Кухонный инвентарь	б/н	Чайник	шт.	9							
	Кухонный инвентарь	б/н	Шумовка	шт.	5							

Суммарная мощность оборудования без учета резерва, кВт:

260,4 кВт

Взам. инв. №	
Подп. и дата	
Инв. № подл.	

Примечание:
Данная спецификация оборудования и мебели является рекомендательной.
В процессе закупки в случае необходимости возможно уточнение наименования, кол-ва, габаритов и технических характеристик, а также возможна замена моделей и производителей (технические характеристики должны быть аналогичны или улучшены).