
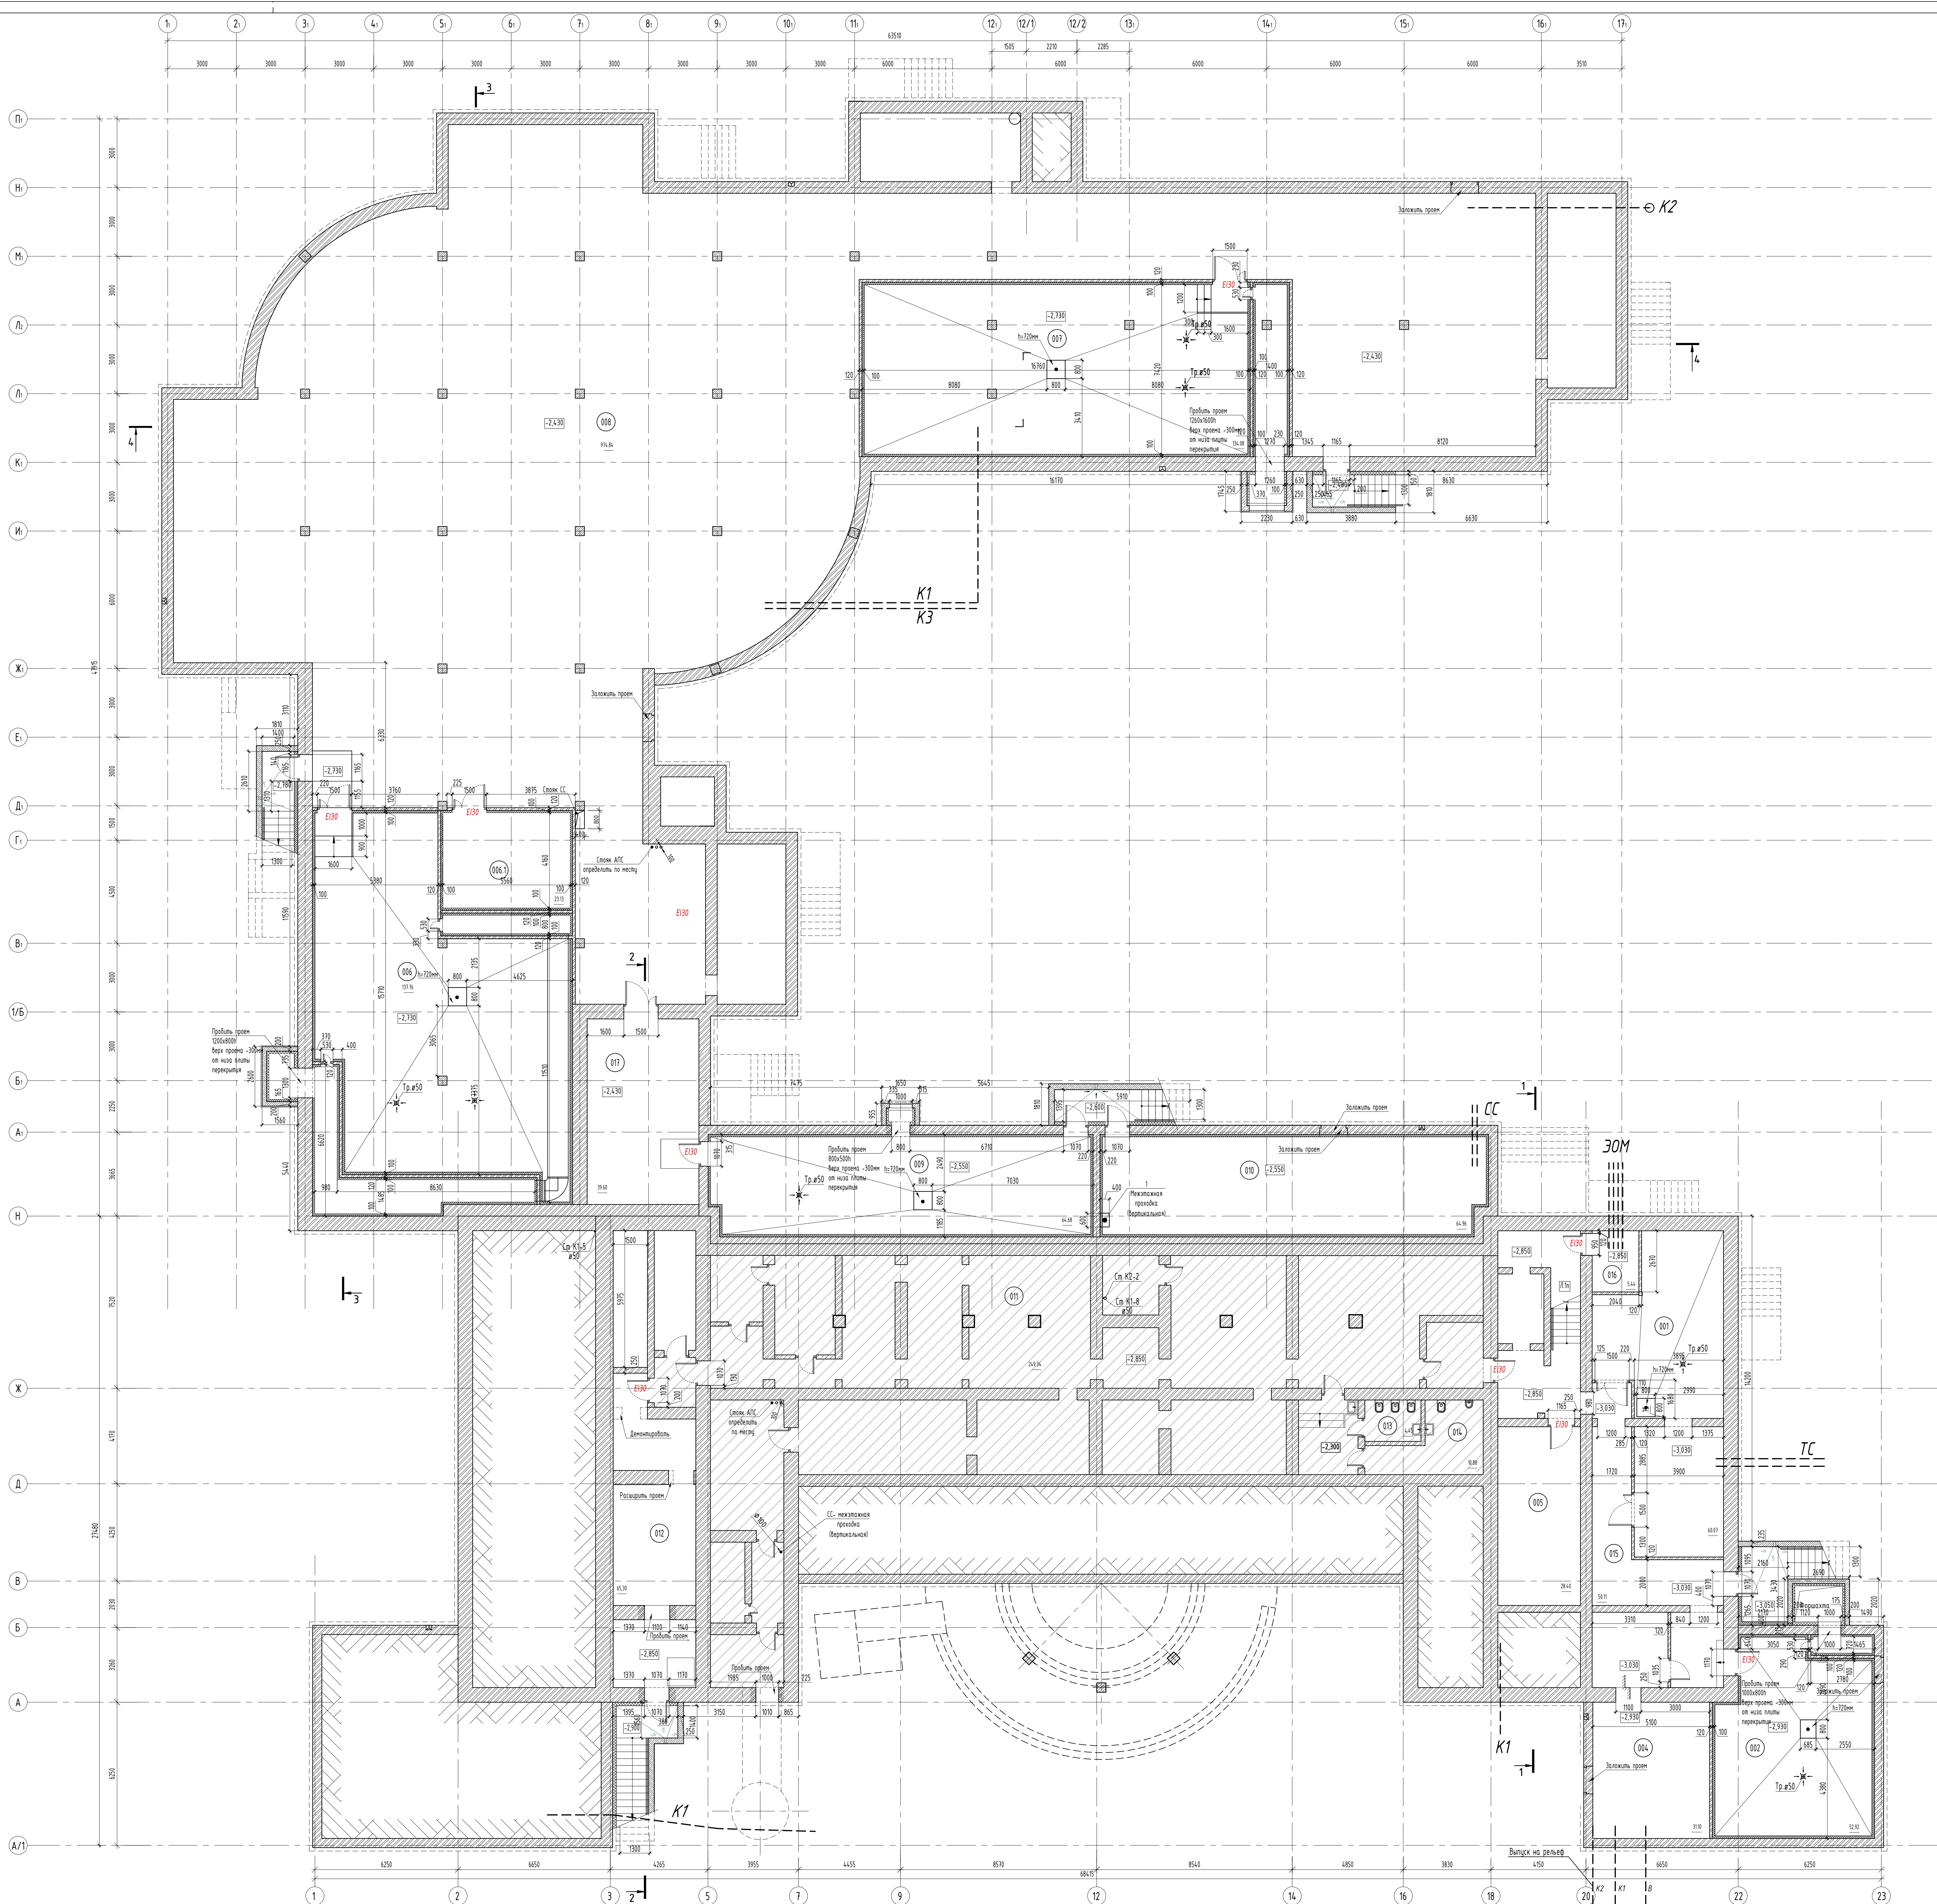
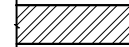
 


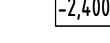


Экспликация помещений подвала			
Номер помещения	Наименование	Площадь, м2	Кол. помещений
001	ИТП	60,07	1
002	Венткамера с формовкой	52,92	83
004	Водомерный узел и исосная	41,24	1
005	Техническое помещение	28,40	1
006	Венткамера	137,76	83
006.1	Венткамер систем приточно-разбавной вентиляции	23,13	1
007	Венткамера	138,94	83
008	Техническое помещение для прокладки инженерных коммуникаций	974,84	83
009	Венткамера	64,68	83
010	Техническое помещение	64,96	1
011	Защитное помещение гражданской обороны	249,34	1
012	Коридор	50,95	1
013	Санузел женский	10,88	1
014	Санузел мужской	4,45	1
015	Коридор	50,11	1
016	Узел ввода электрических сетей	54,04	84
017	Коридор	39,60	1
		Всего	1997,7

УСЛОВНЫЕ ОБОЗНАЧЕНИЯ

	- Существующие стены из полнотелого кирпича
	- Замыкания монолитные X/Б стемы
	- Замыкания перегородки из полнотелого кирпича
	толщиной 120мм и 250 мм
	- Номер помещения по экспликации
	- Маркировка осязаемости замыкания дверей
	- Отметка уровня пола этажа
	- Помещения ГО ЧС
	- Пути эвакуации

1. Возможности устройства проемов в несущих стенах будут уточняться в проекте.
2. Размер и расположение вентиляционных шахт будут уточнен в проекте.
3. Шахты предназначены для прокладки инженерных коммуникаций и стоек (ВК, ЕС, ЗОМ), оборудованы лючками для обслуживания.
4. * Категорирование по взрывопожарной опасности данных помещений выполняется на этапе проектирования.
4. Марки ограждений смотреть альбом 16-25/Г-П-АР лист 61

					16-25/Г-П-АР	
					Капитальный ремонт объекта "ГБОУ Школа № 429 "Скопальная гора", расположенного по адресу: г. Москва, ул. Скопальной горы 5-а, д. 16	
					Архитектурно-планировочные решения	
					Состав	Лист
					Р	Листов
					Плн. подвала. М.1:100	
						

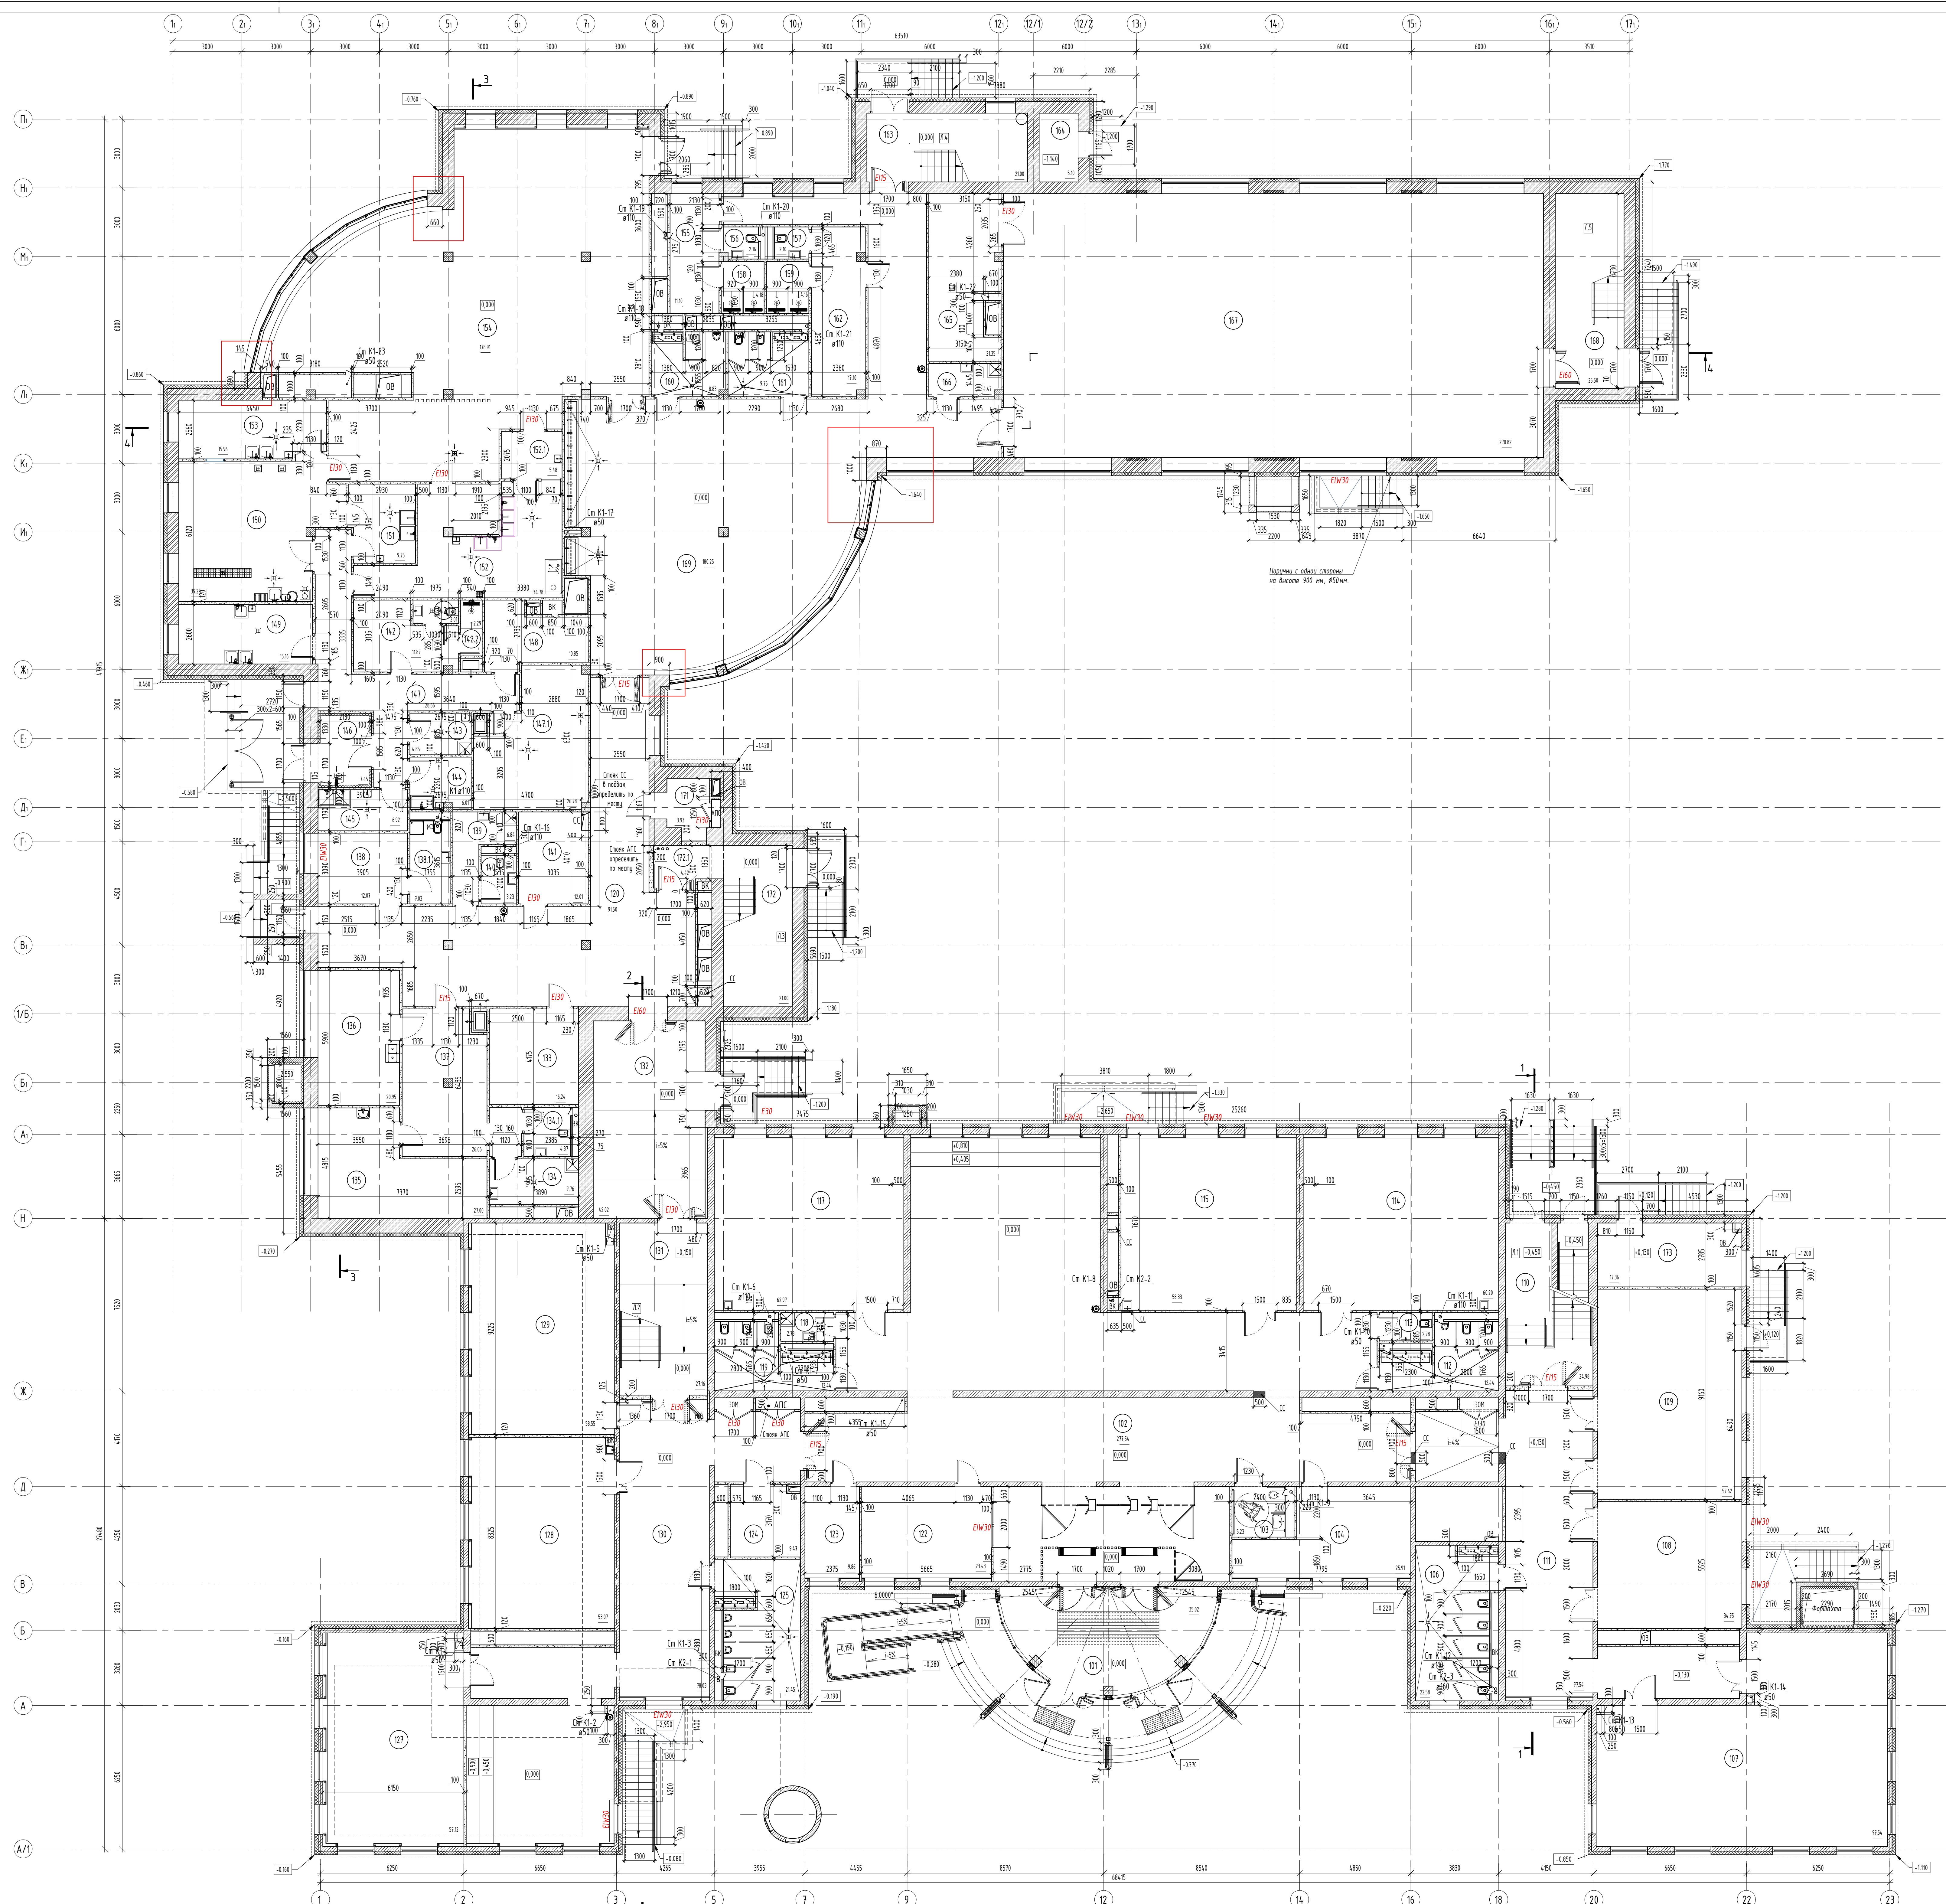


Помещение	Наименование	Площадь, кв. м	Кл. помещения
101	Танк	35,02	
102	Коридор с рекреацией	271,54	
103	Санкт для МП	5,23	
104	Административный кабинет тип 1 (начальная школа)	25,91	
105	Санкт для девочек (начальная школа)	23,25	
107	Гардероб для обучающихся (основная и старшая школа)	97,54	
108	Гардероб для обучающихся (основная и старшая школа)	34,75	
109	Гардероб для обучающихся (начальная школа)	51,62	
110	Лестничная клетка (ЛК)	24,50	
111	Коридор	71,54	
112	Санкт для мальчиков (начальная школа)	12,44	
113	Санкт для персонала	2,88	
114	Учебные кабинеты (начальная школа)	65,12	
115	Учебные кабинеты (начальная школа)	58,33	
117	Учебные кабинеты (начальная школа)	62,97	
118	ПСИ	2,28	Б4
119	Санкт для девочек (начальная школа)	12,44	
120	Коридор с рекреацией (основная и старшая школа)	21,50	
122	Комната охраны (с диспетчерским пунктом)	93,43	
123	Гардеробная комната (для учителей)	9,86	
124	Помещение связи	9,47	Б4
125	Санкт для мальчиков (начальная школа)	21,73	
127	Учебные кабинеты (начальная школа)	56,31	
128	Учебные кабинеты (начальная школа)	53,81	
129	Учебные кабинеты (начальная школа)	58,71	
130	Коридор с рекреацией	117,57	
131	Лестничная клетка Тип Н2	27,18	
132	Вестибюль	42,02	
133	Электрощитовая	16,26	Б3
134	Участок для прицепления дефилирующих расчетов и хранения оборудования инвентаря, предназначенного для помещений медицинского назначения	7,74	Б4
134.1	Туалет男用	4,31	
135	Кабинет броси	21,00	
136	Процедурный (приблюдный) кабинет	28,88	
137	Коридор	12,06	
138	Комната инструктора	26,97	
138.1	Санкт с душем	7,93	
139	ПСИ	6,39	Б4
140	Санкт для персонала	3,27	
141	Помещение связи	12,01	
142	Помещение для персонала	11,87	
142.1	Санкт для персонала	2,01	
142.2	Душевые	2,29	
143	ПСИ	4,85	Б4
144	Помещение для временного хранения личных вещей	6,01	Б4
145	Кладовая с вещами оборотной пары	6,92	Б4
146	Защитный щит	7,45	Б4
147	Коридор	28,66	
147.1	Помещение с холодильным оборудованием	26,78	Б3
148	Кладовая сухих продуктов	10,85	Б3
149	Дополнительный щит	15,16	Б3
150	Гарный щит	39,25	Б3
151	Менская для курной посуды	9,75	Д
152	Менская для столовой посуды	34,18	Д
152.1	Приемная	5,48	Д
153	Холодный щит	15,96	Б3
154	Обеденный зал	118,91	
155	Раздевалочная для мальчиков	10,10	
156	Санкт для мальчиков	2,16	
157	Санкт для девочек	2,10	
158	Душевые для мальчиков	4,15	
159	Душевые для девочек	4,15	
160	Санкт для мальчиков	8,71	
161	Санкт для девочек	8,76	
162	Раздевалочная для девочек	11,00	
163	Лестничная клетка (ЛК)	21,00	
164	Техническое помещение	21,30	Б4
165	Сараи	5,35	Б3
166	ПСИ	4,47	Б4
167	Экспериментальный спортивный зал	270,82	
168	Лестничная клетка (ЛК)	25,50	
169	Коридор с рекреацией (основная и старшая школа)	281,24	
171	Тех. помещение	3,93	Б4
172	Лестничная клетка (ЛК)	21,00	
172.1	Танк	4,42	
173	Электрощитовая	17,36	Б3
	Всего	2674,1	

	- Существующие типовые ж/б стены
	- Заменаемые перерывы из газоблоков 16/25x250x100/500, 85, 0 по ГОСТ Р 1952-2012, полные к клею с армированием базальтовой сеткой, оштукатуренные
	- Заменаемые перерывы из газоблоков 16/25x250x100/500, 85, 0 по ГОСТ Р 1952-2012, полные к клею с армированием базальтовой сеткой, оштукатуренные
	- Заменаемые перерывы из оштукатуренной однослойной сетки толщиной 100мм
	- Заменаемые перерывы из оштукатуренной однослойной сетки толщиной 100мм
	- Заменаемые ослепленные перерывы
	- Заменаемые перерывы синтетической (пластиковой) с обшивкой необходимой фурнитурой

- 201 - Номер помещения по экспликации
- 19.000 - Отметка уровня пола этажа
- E30/EI30/EIW30 - Маркировка огнестойкости заменяемых дверей, окон, перегородок;

1. Возможность устройства проемов в несущих стенах будет уточняться в проекте.
- Размер и расположение вентиляционных шахт будет уточнен в проекте.
2. Шахты предназначенные для прокладки инженерных коммуникаций и стояков (ВК, СС, ЭОМ, оборудуются лючками для обслуживания.
3. ★ категорирование по взрывопожарной опасности данных помещений выполнить на этапе проектирования.
4. Марки ограждений смотреть альбом 16-25/Г-П-АР лист 61

						16-25/Г-П-АР		
						Капительный ремонт объекта "БШУ № 129 "Смоленская и расположенного по адресу: г. Москва, ул. Смоленской горы 5-я,		
Изм.	Кол. в.	Лист	№ док.	Подпись	Дата			
Разработ		Литовская		<i>Литовская</i>	2020.07.09			
						Архитектурно-планировочные решения		
						Станд.	Лист	Лист
						Р		
И. н.пр.	Кол. в.	Лист	№ док.	Подпись	Дата			
И. н.пр.		Губарева		<i>Губарева</i>	2020.07.09			
						Лист 1 из 3а: М.1:00		
						 АЗУР		

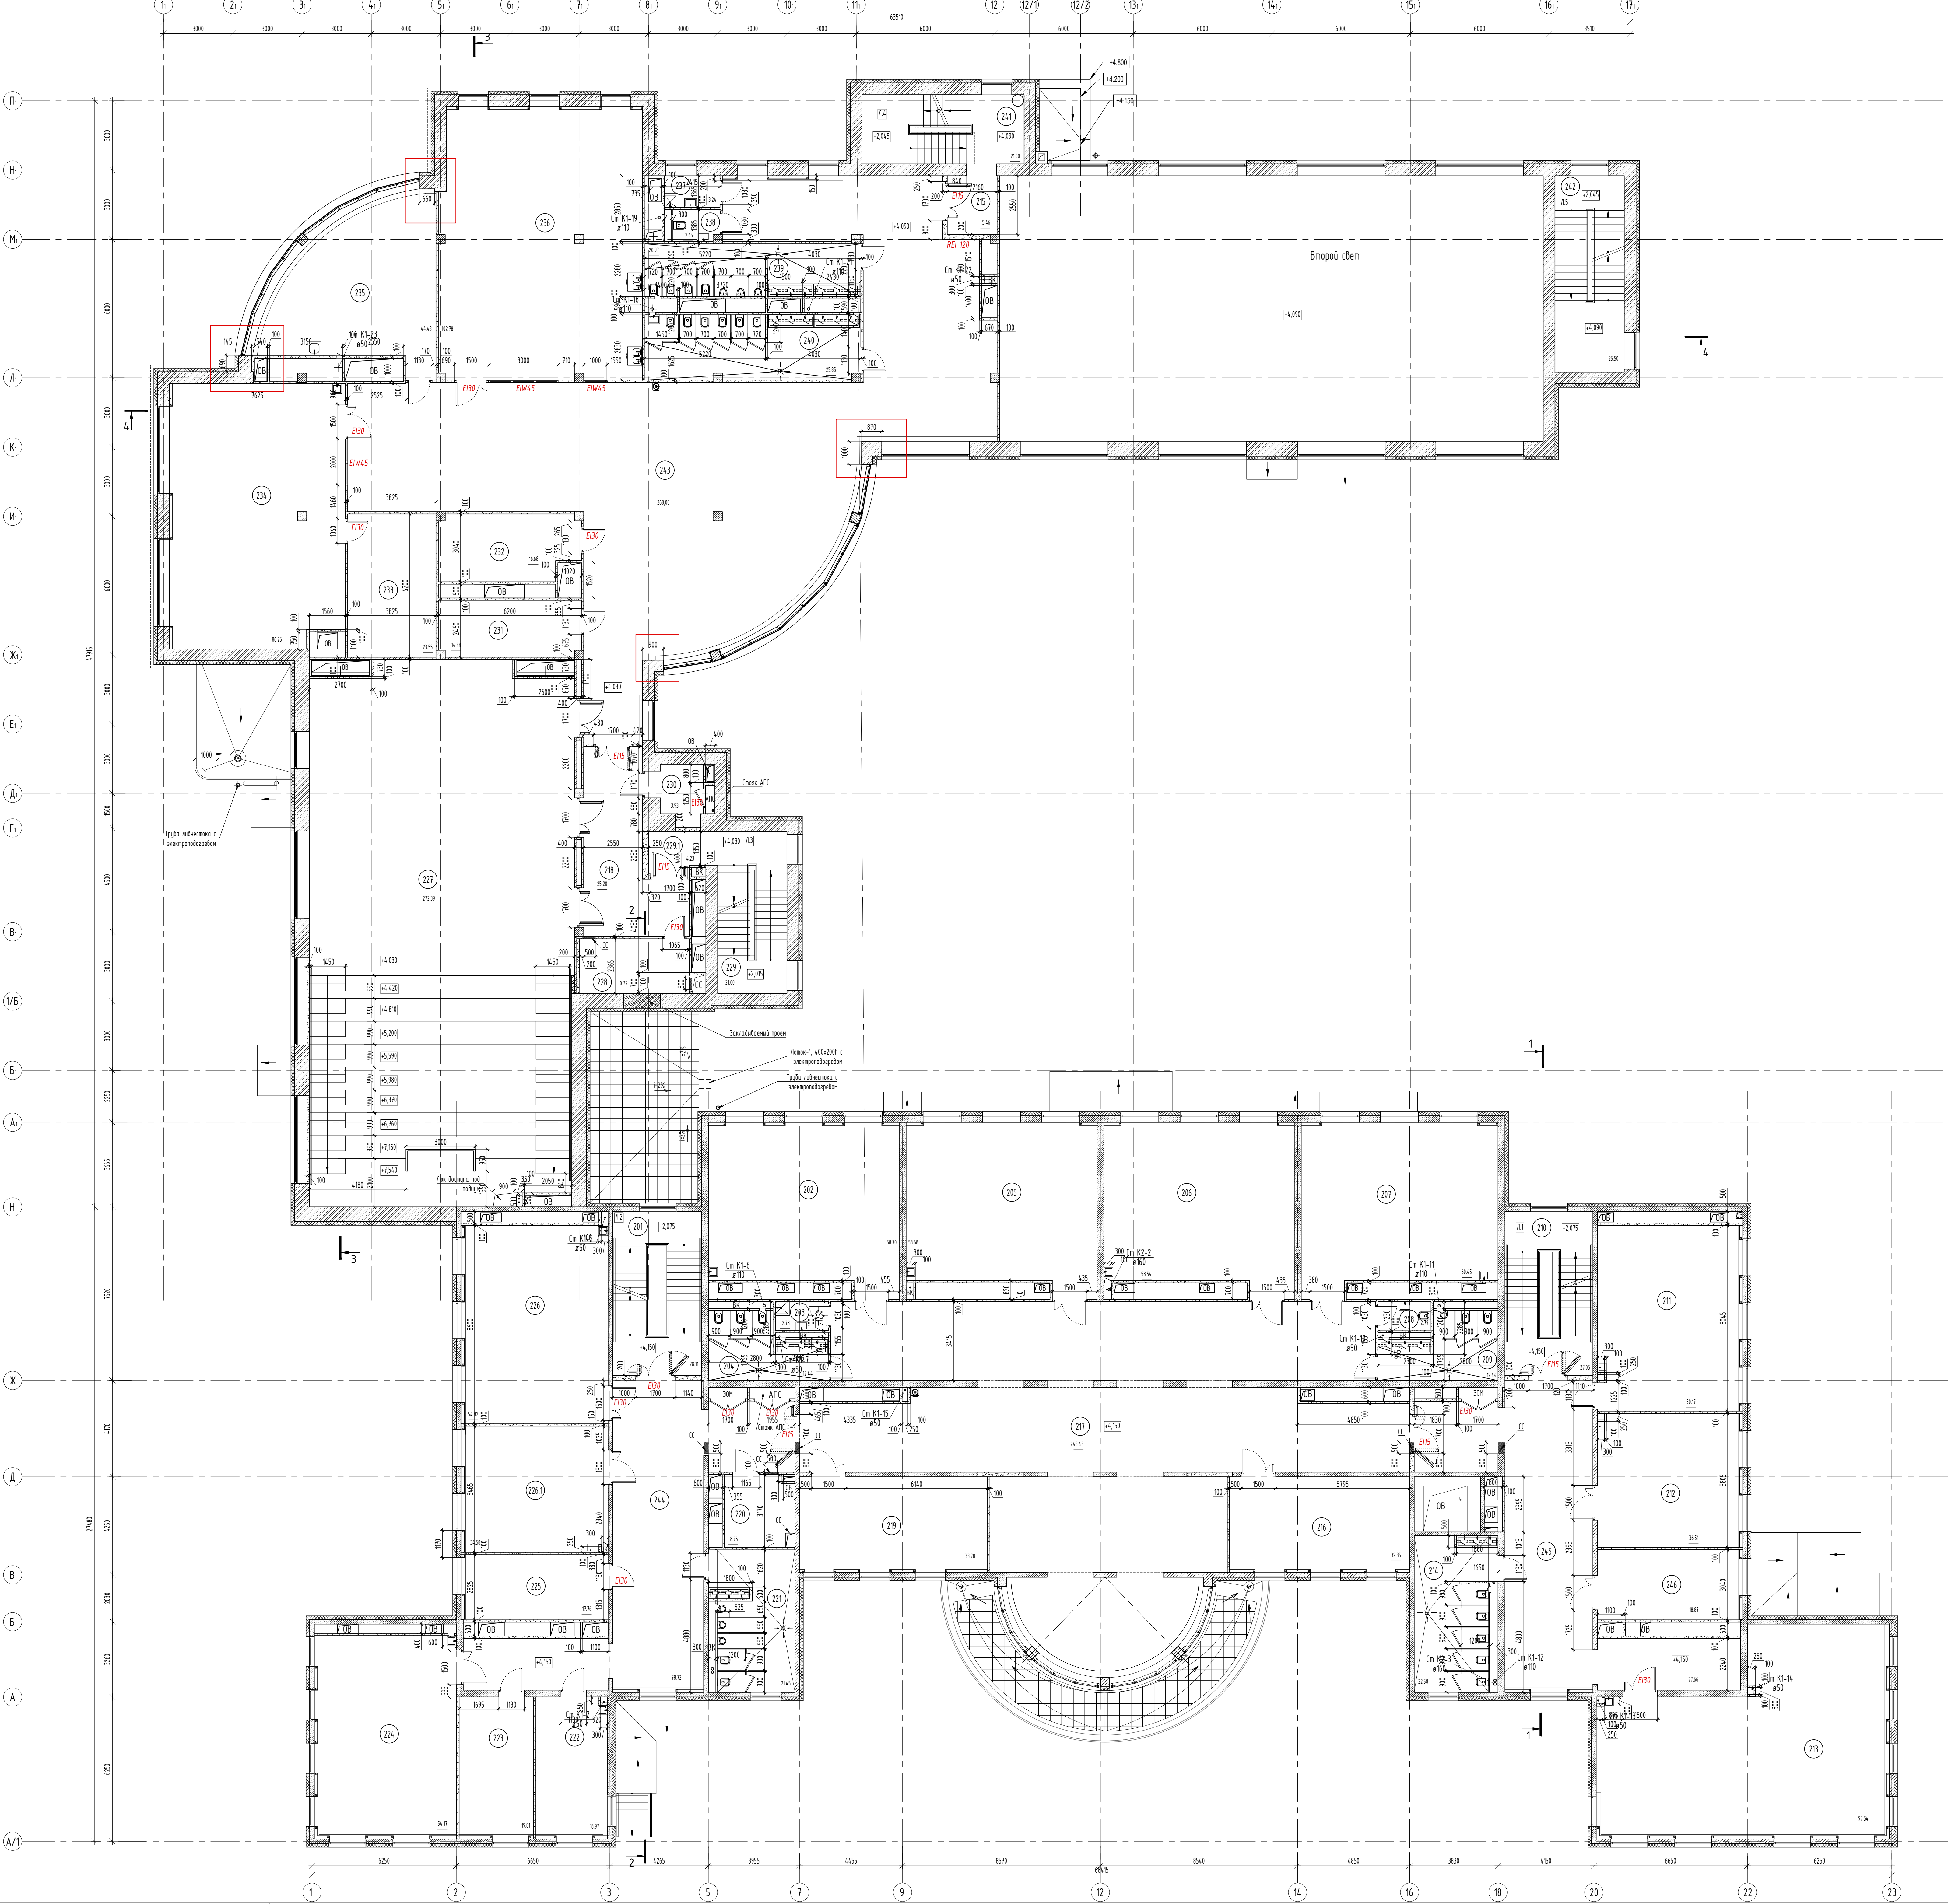

Экспликация помещений 2-го этажа


Номер помещения	Наименование	Площадь, м2	Кат. помещ.
201	Лестничная клетка Тип Н2	28,82	
202	Учебные кабинеты (начальная школа)	58,70	
203	ПНИ	2,78	В4
204	Санузел для девочек (начальная школа)	12,73	
205	Учебные кабинеты (начальная школа)	58,68	
206	Учебные кабинеты (начальная школа)	58,54	
207	Учебные кабинеты (начальная школа)	60,45	
208	Санузел для персонала	2,79	
209	Санузел для мальчиков (начальная школа)	12,44	
210	Лестничная клетка (ЛП)	27,05	
211	Учебные кабинеты (начальная школа)	50,17	
212	Кабинет иностранного языка (начальная школа)	36,51	
213	Лабораторно-исследовательский комплекс для изучения астрономии (п.п.)	97,02	В3
214	Санузел для девочек (начальная школа)	23,25	
215	Танцев	5,46	
216	Кабинет для индивидуальных занятий с малой группой	32,35	
217	Коридор с рекреацией (начальная школа)	245,43	
218	Коридор	25,20	
219	Кабинет для индивидуальных занятий с малой группой	33,78	
220	Помещение связи	8,75	В4
221	Санузел для мальчиков (начальная школа)	21,45	
222	Кабинет для индивидуальных занятий, в т.ч. с учителем-логопедом	18,97	
223	Кабинет для индивидуальных занятий, в т.ч. с коррекционным педагогом	19,22	
224	Учебные кабинеты (начальная школа)	54,17	
225	Классовая кабинетная творческой мастерской	11,75	В3
226	Творческая мастерская	54,82	В3
226.1	Кабинет иностранного языка (начальная школа)	34,58	
227	Многофункциональное пространство с функцией актового зала (с эстрадой в уровне пола)	272,39	
228	Классовая	10,72	В3
229	Лестничная клетка (ЛП)	21,00	
229.1	Танцев	4,23	
230	Тех. помещение	3,93	В4
231	Архитектурная	14,75	
232	Классовая кабинетная	16,45	В3
233	Классовая кабинетная материальной технологии	23,55	В3
234	Кабинет материальной технологии тип 2	86,25	В3
235	Кабинет с рабочим пространством для учителей тип 1 (начальная школа)	44,43	
236	Кабинет материальной технологии тип 1	102,78	В3
237	ПНИ	3,24	В4
238	Санузел для персонала	2,65	
239	Санузел для мальчиков (основная и старшая школа)	20,97	
240	Санузел для девочек с комнатой личной гигиены (основная и старшая школа)	25,85	
241	Лестничная клетка (ЛП)	21,00	
242	Лестничная клетка (ЛП)	25,50	
243	Коридор и рекреация (основная и старшая школа)	268,00	
244	Коридор	78,72	
245	Коридор	77,66	
246	Административный кабинет	18,87	
	Всего	2245,0	

УСЛОВНЫЕ ОБОЗНАЧЕНИЯ

- Существующие монолитные и/б стены
- Заполнение перегородки из газобетонных блоков 1/425х25х100/1500/85,0 по ГОСТ Р 76522-2022, толщиной 100мм на клею с армированием базальтовой сеткой, опущенная
- Заполнение перегородки из газобетонных блоков 1/425х25х100/1500/85,0 по ГОСТ Р 76522-2022, толщиной 200мм на клею с армированием базальтовой сеткой, опущенная
- Заполнение перегородки из акрилового одностронне звукопоглощающего материала толщиной 100мм
- Заполнение перегородки из акрилового одностронне звукопоглощающего материала толщиной 100мм
- Заполнение оштукатуренная перегородка
- Заполнение перегородки синтетическая (пластиковая) с дверью и необходимой фурнитурой
- 201 - Номер помещения по экспликации
- 0,000 - Отметка уровня пола этажа
- E300/EW300 - Маркировка оконных проемов, дверей, окон, перегородок

- Возможность устройства проемов в несущих стенах будет уточняться в проекте. Размер и расположение вентиляционных шахт будет уточнен в проекте.
- Шахты предназначены для прокладки инженерных коммуникаций и стояков (ВК, СТ, ЭОМ), оборудуются лестницами для обслуживания.
- Жиромаркировка по взрывопожарной опасности данных помещений выполняется на этапе проектирования.
- Марки горизонтальных сечений 16-25/Г-П-АР лист 61

16-25/Г-П-АР				
Капитальный ремонт объекта "ГБОУ Школа № 429 "Соколовая гора", расположенного по адресу: г. Москва, ул. Соколовой горы 5-я, д. 1/4				
Им. Разраб.	Лист	№ д.н.	Подпись	Дата
Архитектура-планировочные решения	Стандарт	Лист	Листов	
И. номер	Губарева	И. номер	И. номер	
И. номер	И. номер	И. номер	И. номер	

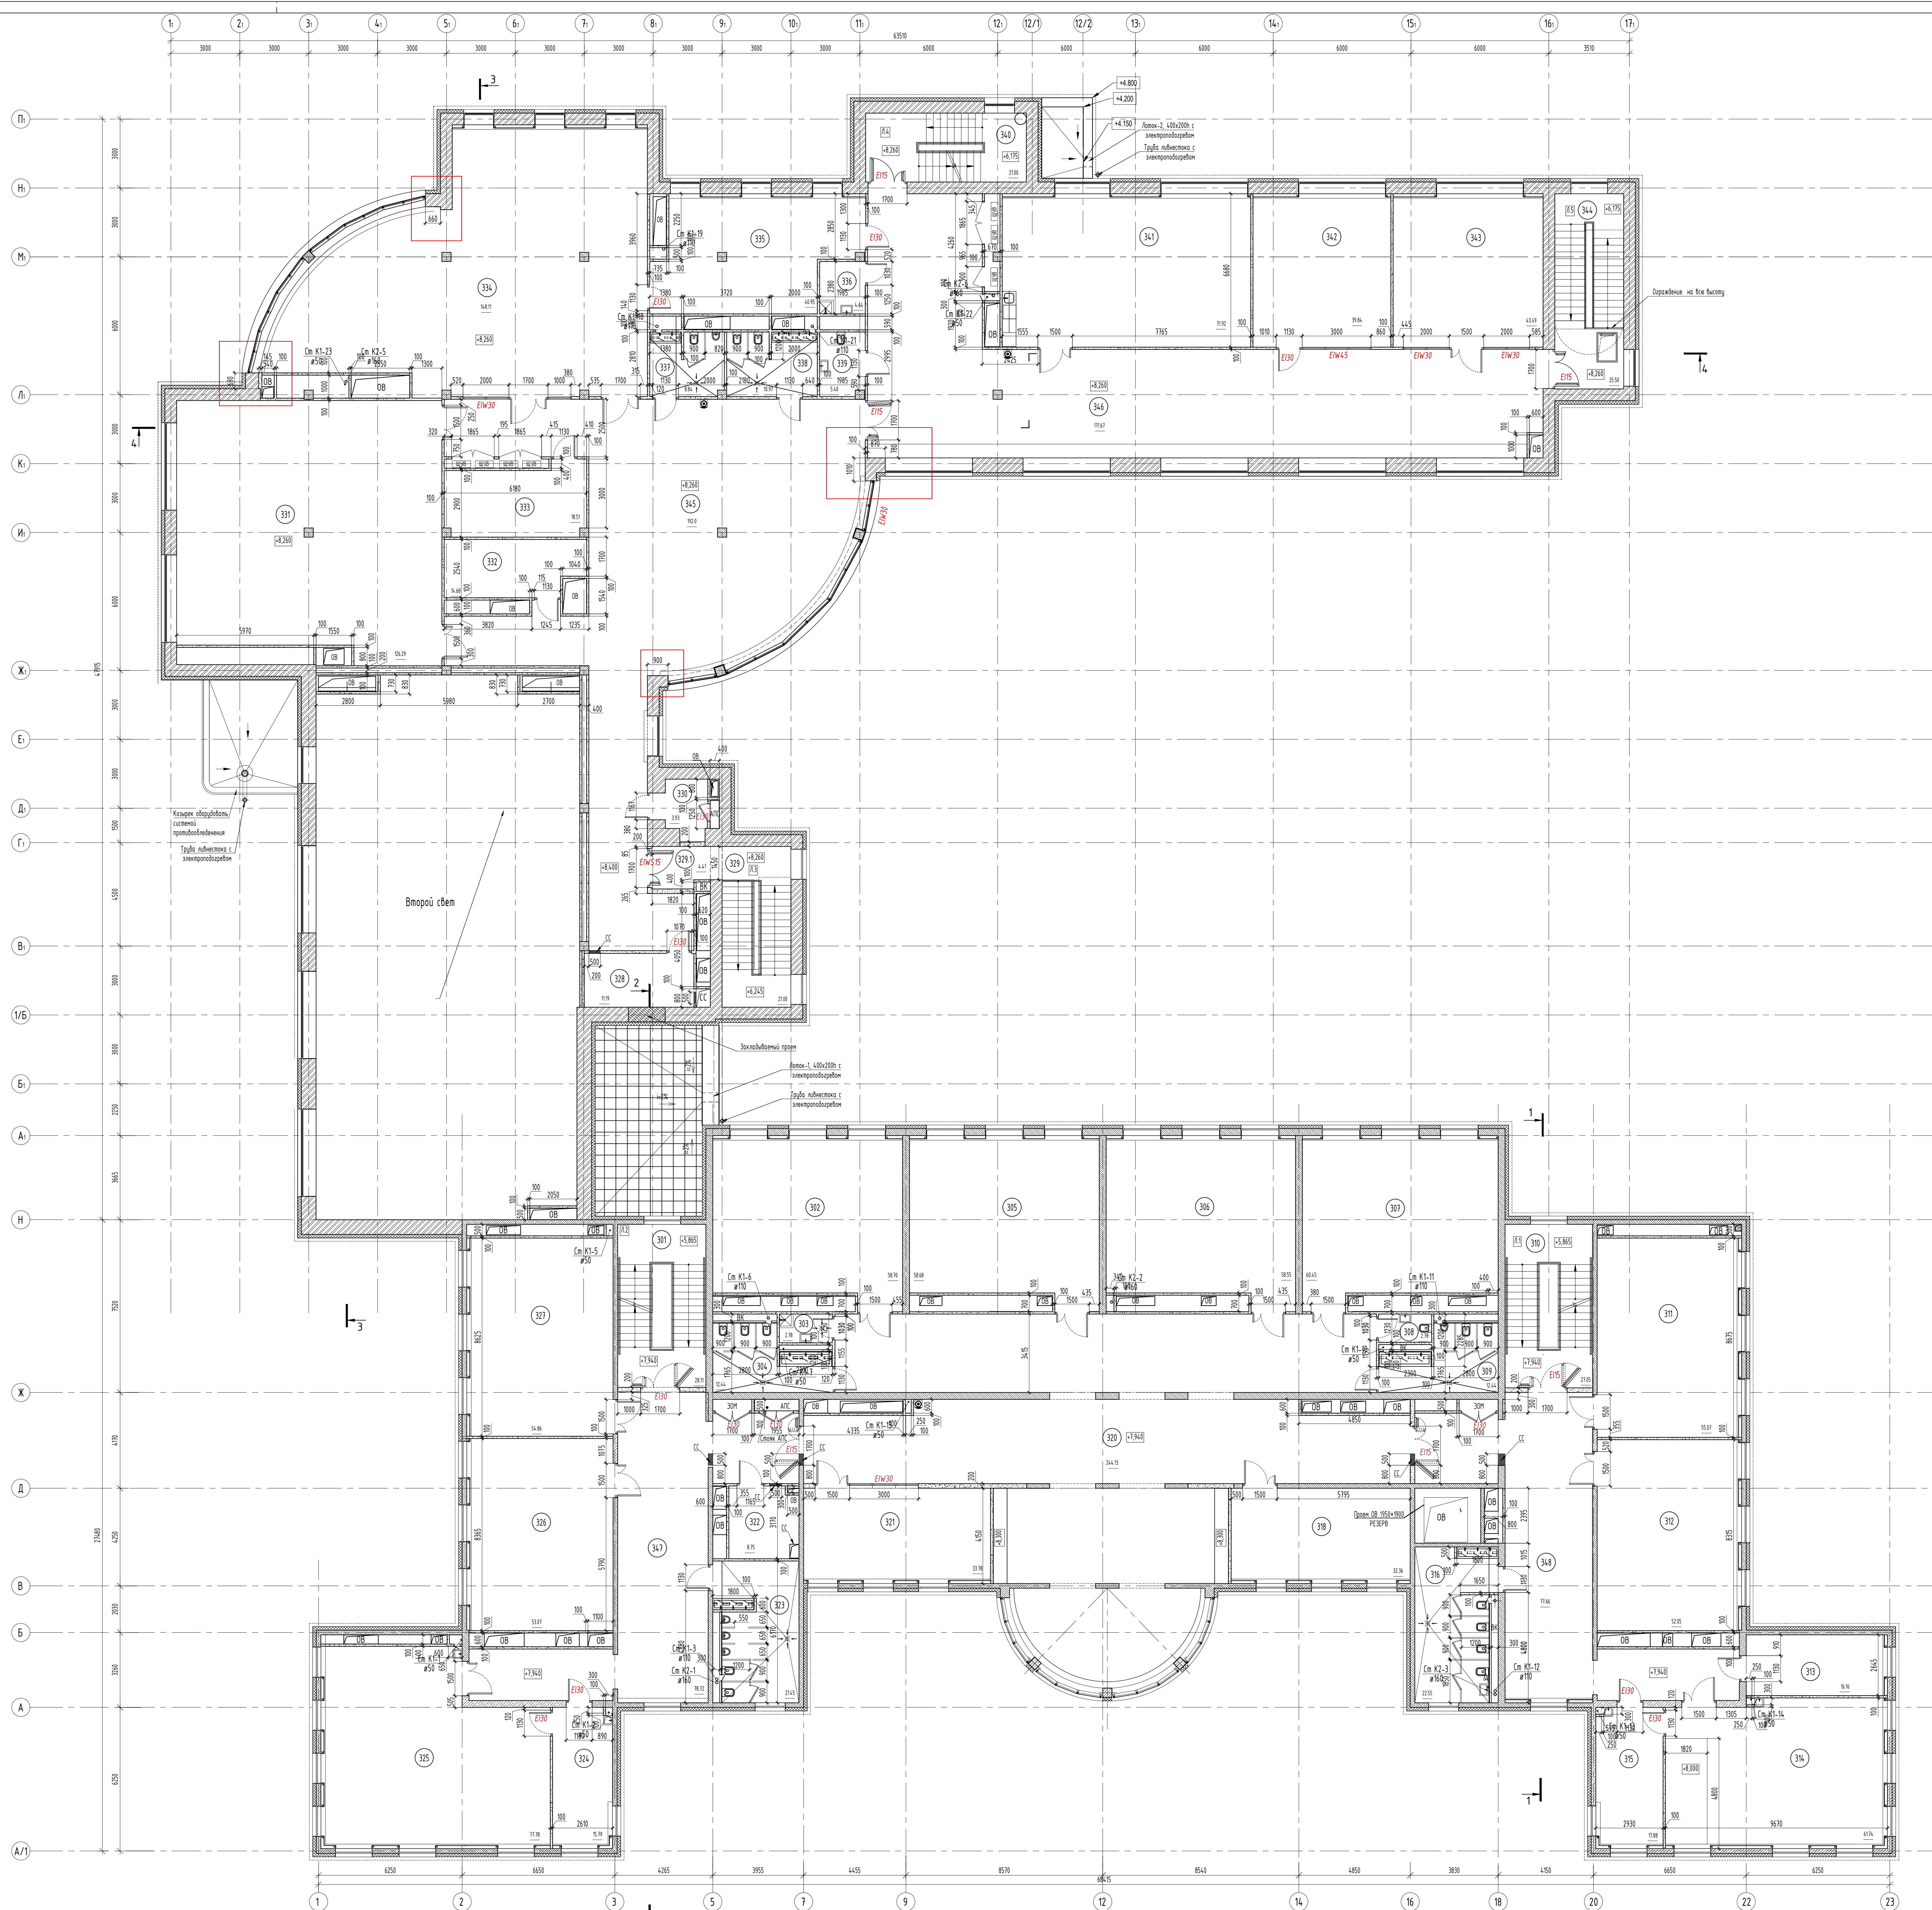

Экспликация помещений 3-го этажа				
Номер помещения	Наименование	Площадь м2	Класс помещения	
301	Астеническая клетка Тип И2	28,82		
302	Коллектор русского языка и литературы	98,70		
303	ПЗИ	2,78	В4	
304	Сонярия для девочек (основная и старшая школа)	12,44		
305	Коллектор русского языка и литературы	58,68		
306	Коллектор математики	58,55		
307	Коллектор математики	60,45		
308	Сонярия для персонала	2,75		
309	Сонярия для мальчиков (основная и старшая школа)	12,44		
310	Астеническая клетка [И1]	27,05		
311	Коллектор географии	55,07		
312	Универсальный учебный кабинет	56,05		
313	Коллектор для индивидуальных занятий, 8 п.ч с педсоветом-психологом	9,16		
314	Учебный кабинет для изучения естественных физика	61,36		
315	Астеническая клетка физики	18,02	В3	
316	Сонярия для девочек с компьютерной техникой (основная и старшая школа)	23,25		
317	Подсобное помещение	6,66	В4	
318	Коллектор иностранного языка (основная и старшая школа)	32,34		
320	Коридор с рекреацией	24,19		
321	Коллектор иностранного языка (основная и старшая школа)	33,78		
322	Помещение связи	8,75	В4	
323	Сонярия для мальчиков (основная и старшая школа)	21,73		
324	Астеническая клетка биологии	15,93	В3	
325	Учебный кабинет для изучения естественных биология с БЗР	51,07		
326	Универсальный учебный кабинет	57,88		
328	Коллектор типичный тип 1	56,86		
329	Коридор	11,19	В3	
329	Астеническая клетка [И1]	21,00		
329.1	Тендер	4,41		
330	Тех. помещение	3,93	В4	
331	Универсальное помещение с возможностью организации административных дел (интерактор)	125,19		
332	Роздебальня	14,45		
333	Роздебальня	16,56		
334	Мультимедийный информационный библиотечный центр с зонами для индивидуальных занятий	52,15		
335	Мультимедийный информационный библиотечный центр (экранный [экраны] фон) и выдох книг	41,45	В3	
336	ПЗИ	4,44	В4	
337	Сонярия для мальчиков (основная и старшая школа)	8,84		
338	Сонярия для девочек (основная и старшая школа)	10,97		
339	Сонярия для персонала	56,40		
340	Астеническая клетка [И1]	21,00		
341	Кабинет с рабочим пространством для учителя Тип 1 (основная и старшая школа)	71,92		
342	Универсальное помещение с возможностью организации мультимедиа	39,84	В3	
343	Помещение музея	43,49		
344	Астеническая клетка [И1]	25,50		
345	Коридор и рекреация (основная и старшая школа)	192,00		
346	Коридор и рекреация (основная и старшая школа)	178,67		
347	Коридор	78,72		
348	Коридор	77,66		
	Всего	2245,1		

УСЛОВНЫЕ ОБОЗНАЧЕНИЯ

- [illegible]

1. Возможность устройства проемов в несущих стенах будет уточняться в проекте.
Размер и расположение вентиляционных шахт будет уточнен в проекте.
2. Шахты предназначены для прокладки инженерных коммуникаций и стожков ИВК, СС, ЗОМ, обору́дываемые лючками для обслуживания.
3. * категорирование по взрывопожарной опасности данных помещений выполнять на этапе проектирования.
4. Марки ограждений смотреть альбом 16-25/1 -П-АР лист 61

№ 100-П/С

16-25/Г - П-АР

Капитальный ремонт объекта "ТБОУ Школа № 429 ("Соколиная гора") расположенного по адресу: г Москва, ул Соколовской горы 5-й д 1/в

Архитектурно-планировочные решения

Страница

Лист

Листов


Р

Ис. номер: Губарева

Дир. Морозова


Листы 3 знака, М1000

 АЗУРИТ

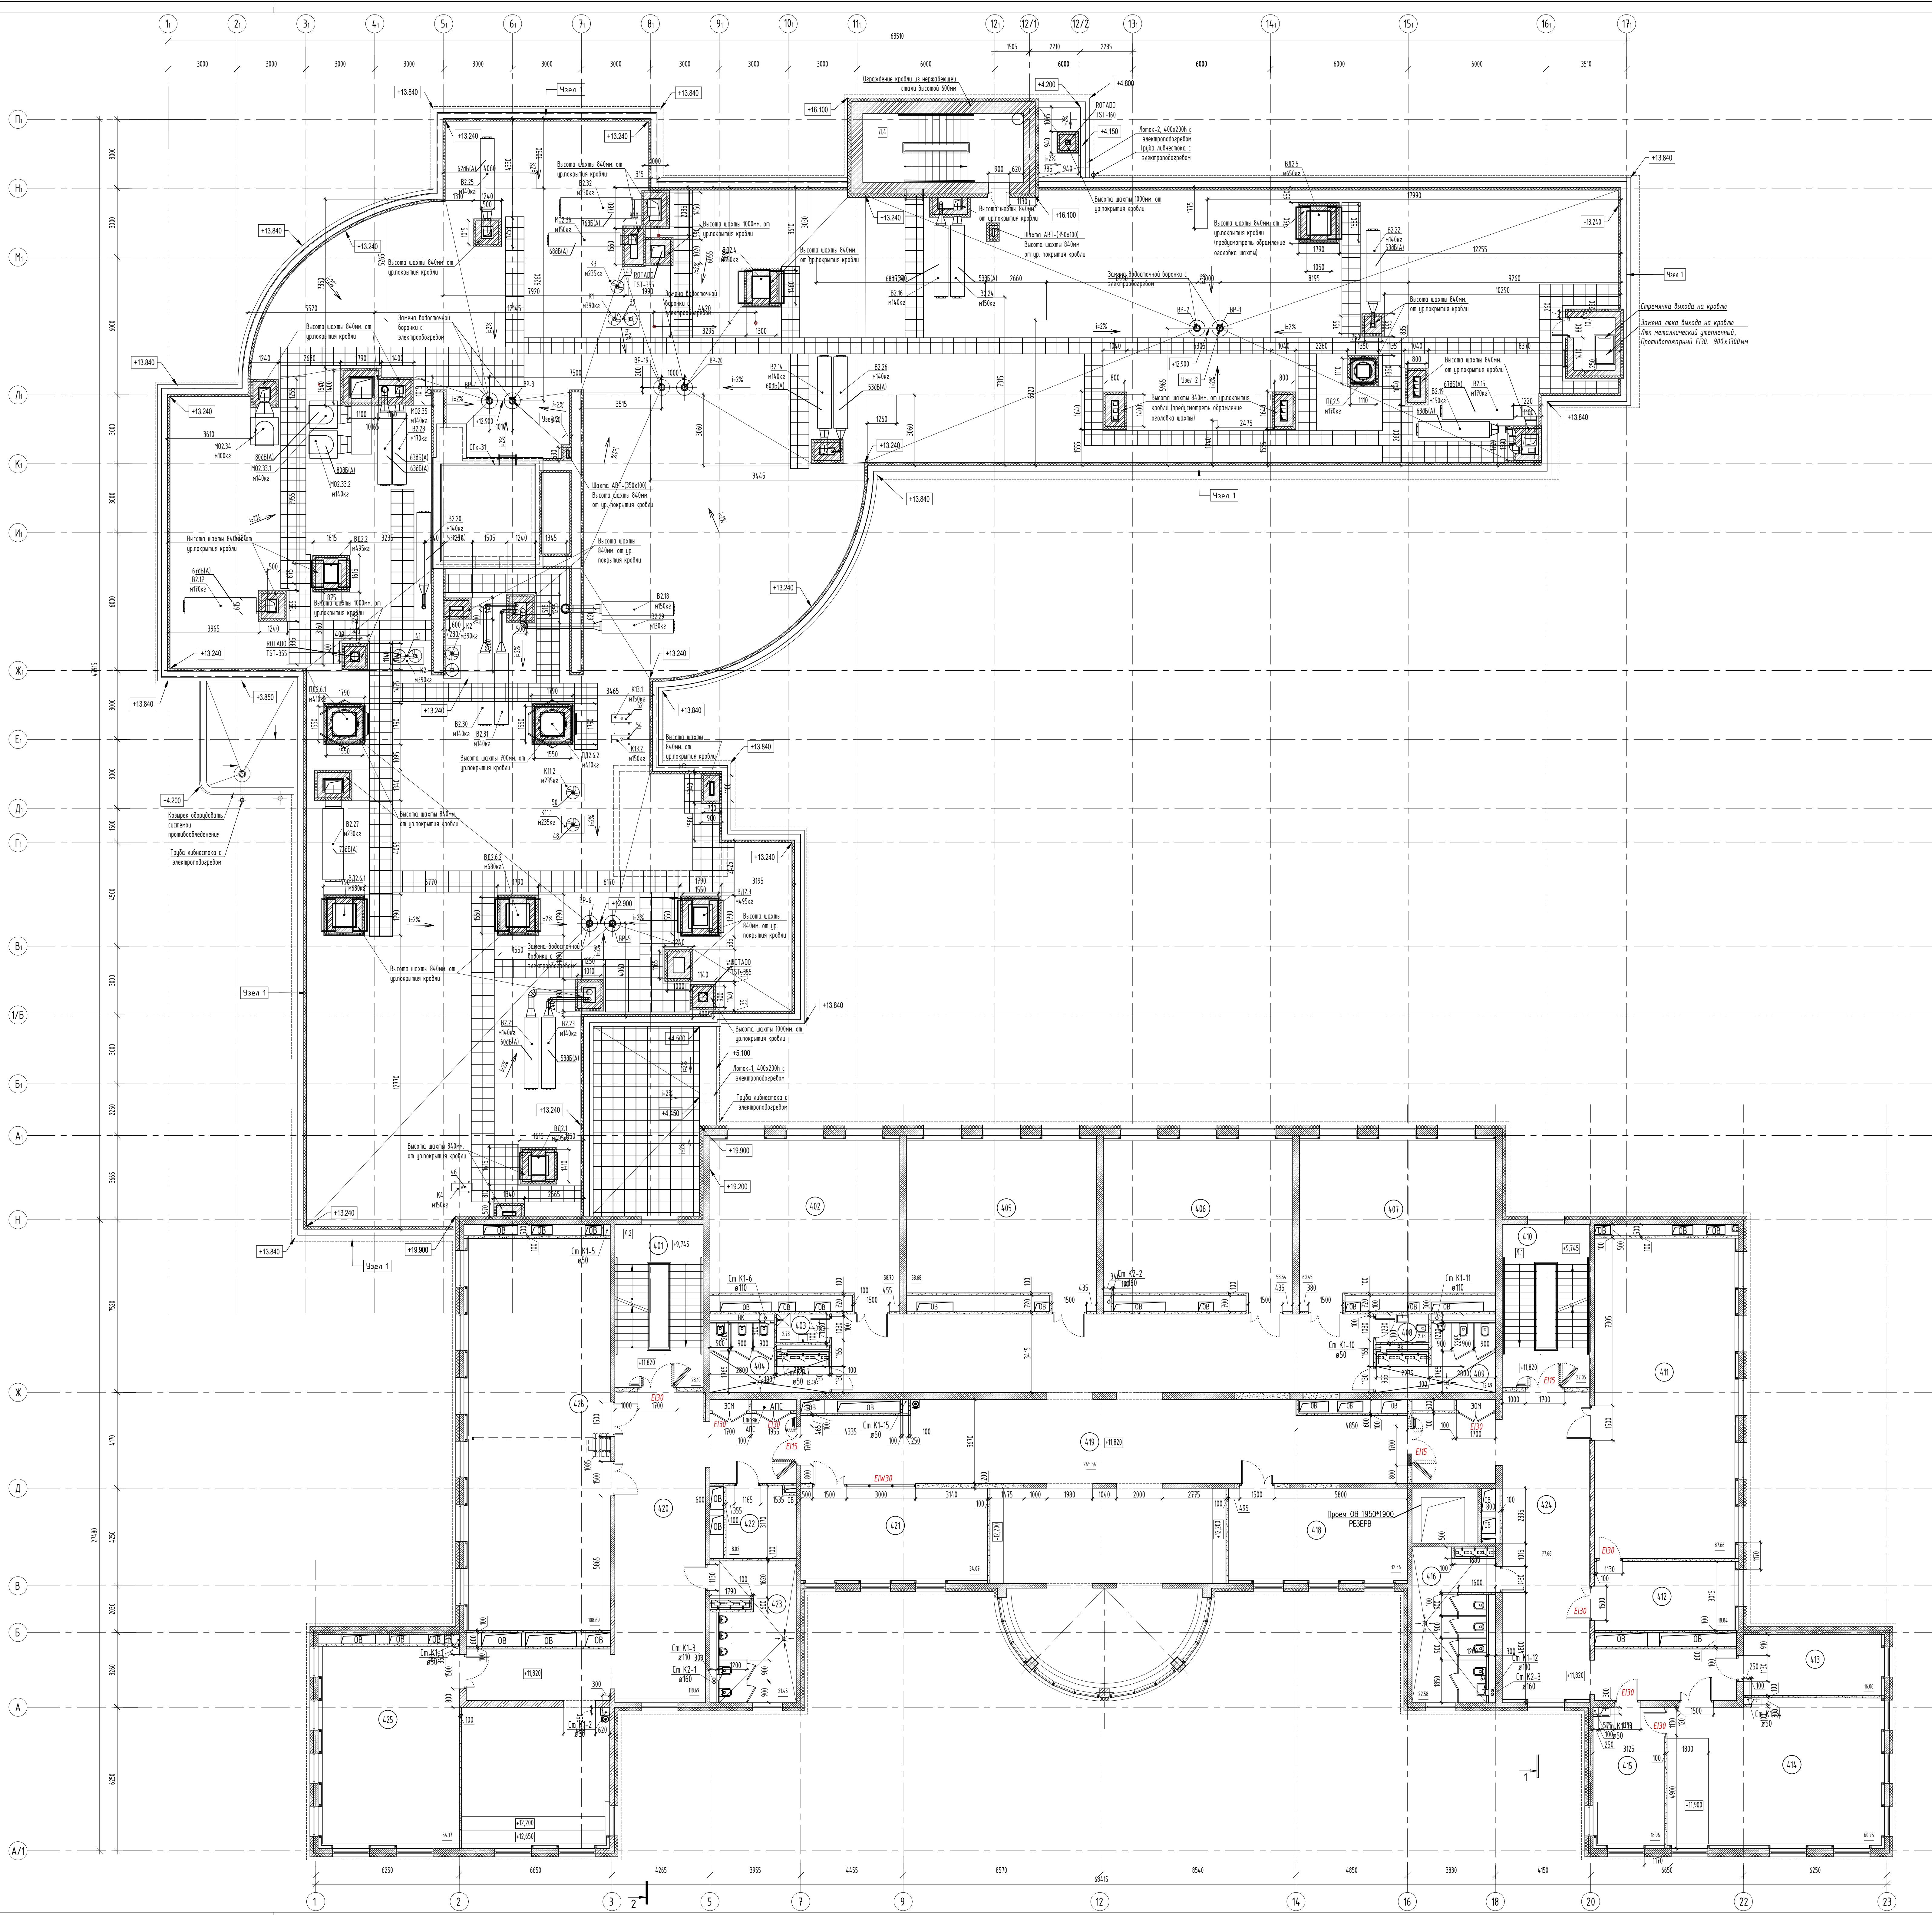





Экспликация помещений 4-20 этажа			
Номер помеще-ния	Наименование	Площадь, м2	Кол. помеще-ния
401	Лестничная клетка Тип Н2	28.81	
402	Кабинет русского языка и литературы	58.70	
403	ПМ	2.78	В4
404	Санитар для девочек (основная и старшая школа)	12.49	
405	Кабинет русского языка и литературы	58.68	
406	Кабинет математики	58.54	
407	Кабинет математики	60.45	
408	Санитар для персонала	2.78	
409	Санитар для мальчиков (основная и старшая школа)	12.49	
410	Лестничная клетка (ЛП)	26.98	
411	Кабинет информационных технологий	87.66	
412	Лаборантская при кабинете информационных технологий	18.84	В3
413	Административный кабинет тип 1 (основная и старшая школа)	16.03	
414	Учебные кабинеты для изучения естественных наук	60.75	
415	Лаборантская кабинета химии	18.96	В3
416	Санитар для девочек с комнатой личной гигиены (основная и старшая школа)	22.56	
417	Подсобное помещение	7.30	В4
418	Кабинет иностранного языка (основная и старшая школа)	32.36	
419	Коридор с рекреацией	245.54	
420	Коридор с рекреацией	108.69	
421	Кабинет иностранного языка (основная и старшая школа)	34.07	
422	Помещение связи	8.02	В4
423	Санитар для мальчиков (основная и старшая школа)	21.45	
424	Коридор	77.66	
425	Кабинет истории Тип 1	54.17	
426	Кабинет информатики с возможностью деления трансформированной перегородкой на два помещения	108.69	
427	Лестничная клетка (ЛП)	21.00	
428	Помещение выхода на крыльцо	4.18	
Всего		1276.5	

- УСЛОВНЫЕ ОБОЗНАЧЕНИЯ**
- Существующие материалы и/или стены
 - Замена перегородки из газобетонных блоков 1/625/250/100/050/05.0 по ГОСТ Р 7552-2002, толщиной 100мм на клею с армированием базальтовой сеткой, оштукатуренная
 - Замена перегородки из газобетонных блоков 1/625/250/100/050/05.0 по ГОСТ Р 7552-2002, толщиной 200мм на клею с армированием базальтовой сеткой, оштукатуренная
 - Замена перегородки из акриловых одностронне обусловленные на все высоту этажа толщиной 10мм
 - Замена перегородки из акриловых одностронне обусловленные во ш. раковин толщиной 10мм
 - Замена осветленные перегородки
 - Замена перегородки сантехническая (влагостойкая) с дверью и необходимой фурнитурой
 - Номер помещения по экспликации
 - Отметка уровня пола этажа
 - Маркировка геометрии помещений, дверей, окон, перегородок
1. Возможность устройства проемов в несущих стенах будет уточняться в проекте.
Размер и расположение вентиляционных шахт будет уточнен в проекте.
2. Шахты предназначены для прокладки инженерных коммуникаций и стоков (ВК, СС, 30М), оборудуются лестницами для обслуживания.
3. * категоризация по взрывопожарной опасности данных помещений выполнять на этапе проектирования.
4. Марки ограждений смотреть отбтом 15-25/Г-П-АР лист 61

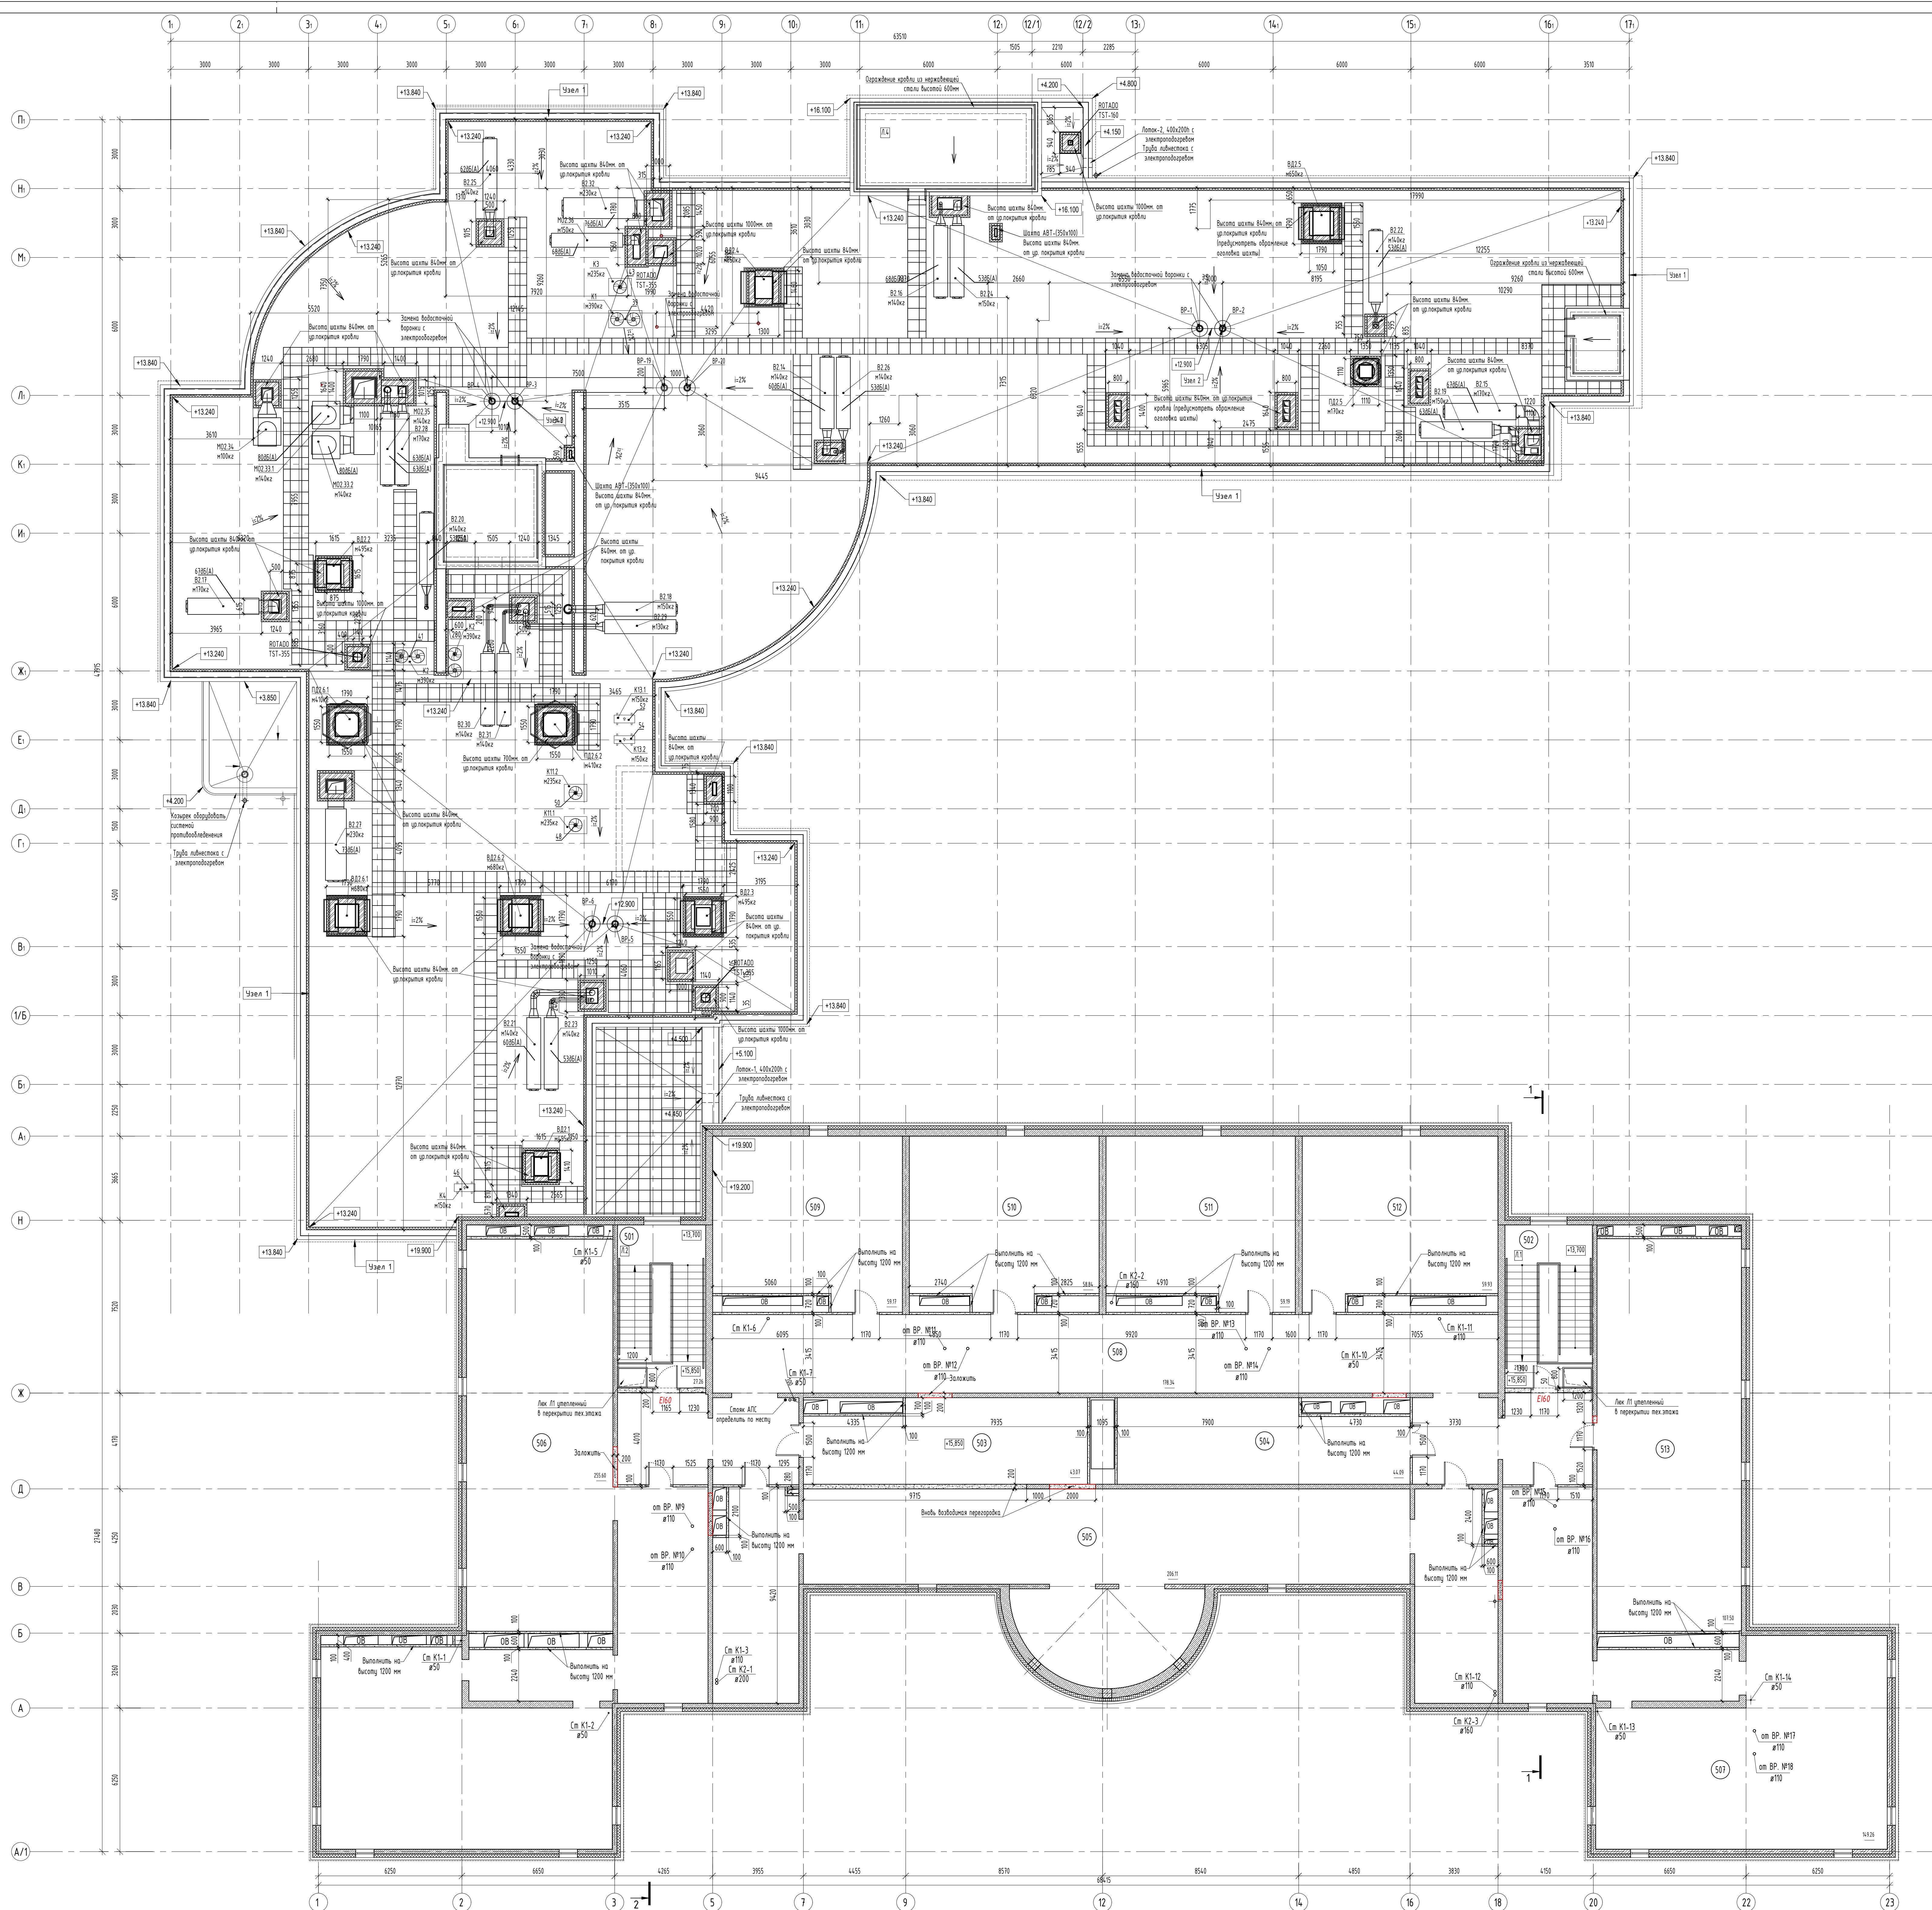

Экспликация помещений технического этажа			
Номер помещения	Наименование	Площадь м2	Кол. помещений
501	Лесничная клетка Тип Н2	27,26	
502	Лесничная клетка Тип Л1	27,05	
503	Вентилятора 1	43,07	83
504	Вентилятора 2	44,09	83
505	Техническое помещение	206,11	83
506	Техническое помещение	155,65	83

УСЛОВНЫЕ ОБОЗНАЧЕНИЯ

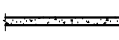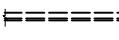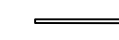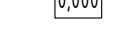
- | | |
|---|--|
|  | - Штукатурка гипсовая на кирпичных стенах |
|  | - Замена перегородки из газобетонных блоков |
|  | 1/1625/25x100/ГОСН/85,5 по ГОСТ Р 76522-2002, толщиной 100мм на клее с армированием базальтовой сеткой, опукатуривания |
|  | - Замена перегородки из газобетонных блоков |
|  | 1/1625/25x100/ГОСН/85,5 по ГОСТ Р 76522-2002, толщиной 200мм на клее с армированием базальтовой сеткой, опукатуривания |
|  | - Замена перегородки из опилочно гипсовитонных дублированных на все высоту помещения 100мм |
|  | - Замена перегородки из опилочно односторонняя дублированная до высоты потолочной 100мм |
|  | - Замена откосов перегородки |
|  | - Замена перегородки опилочечной (полостной) с дверью и напольной фурнитурой |
|  | 201 |
|  | - Номер помещения на этикетке |
|  | - Отметка уровня пола этажа |
|  | - Маркировка оконных проемов, замена дверей, окон, перегородок, |

1. Возможность устройства проемов в несущих стенах будет уточняться в проекте.
Размер и расположение вентиляционных шахт будет уточнен в проекте.
2. Шахты предназначены для прокладки инженерных коммуникаций и стояков (ВК, СС, ЗОМ)
оборудуются личниками для обслуживания.
3. ★ категорирование по взрывопожарной опасности данных помещений выполнить на этапе проектирования.
4. Марки ограждений смотреть альбом 16-25/Г-П-АР лист 61


					16-25/П -П-АР		
					Капитальный ремонт объекта "ГБОУ Школа № 429 "Скоковская гора",		
					расположенного по адресу: г.Москва, ул. Скоковской горы 5-в, д.14		
Изм.	Кол.л.	Лист	№ док.	Подпись	Дата		
Разработ.		Литовская			2020.07.07		
Архитектурно-планировочные решения						Станд.	Лист
							Листов
							Р
И. контро.		Григорьева			2020.07.07		
Н. проект.		Малыгина			2020.07.07		
Лист тех.эпизода М1100						АЗУРИТ	

Экспликация помещений кровли

Номер помещения	Назначение	Площадь м ²	Кол. помещений
601	Помещение выхода на кровлю	4,19	
602	Помещение выхода на кровлю	5,19	
Всего		4,2	

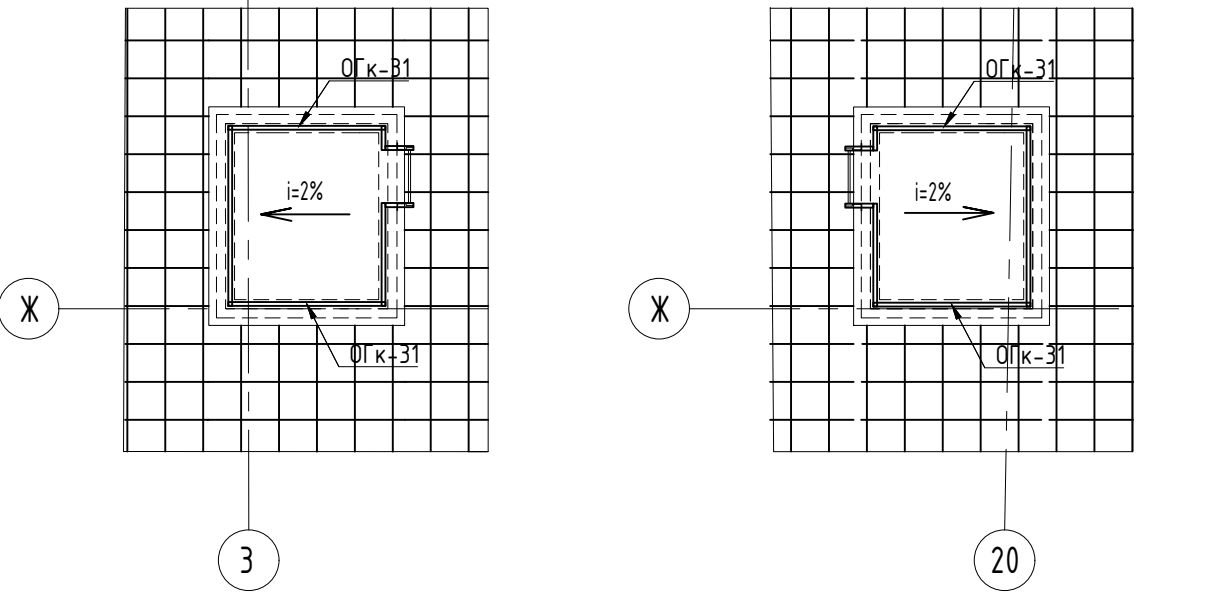


Паралет кирпичный







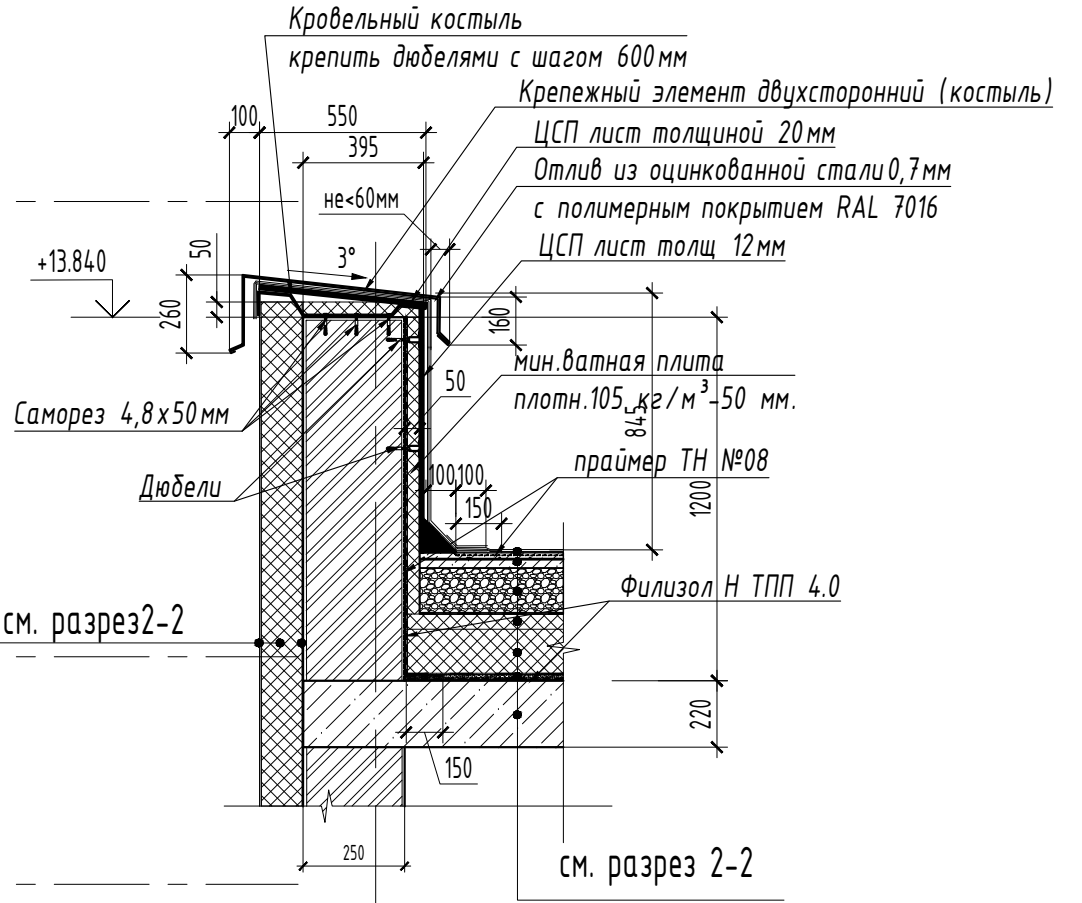


Устройство водоотведения через паралет кирпичный

Паралет из железобетона

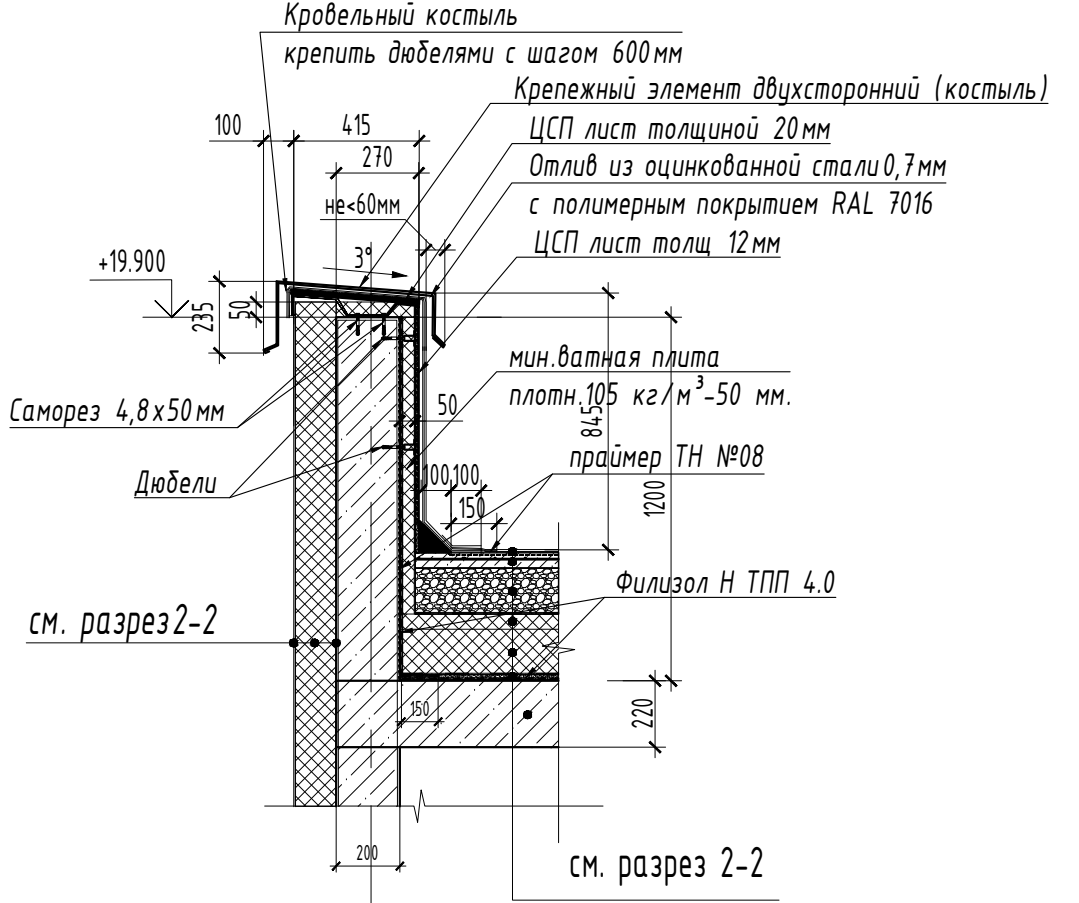

Устройство водоотведения через паралет железобетонный

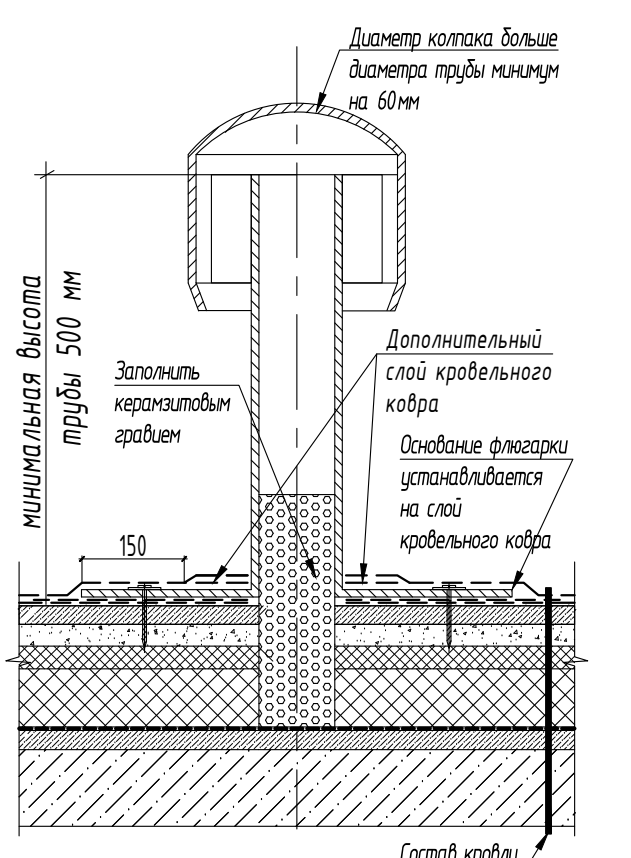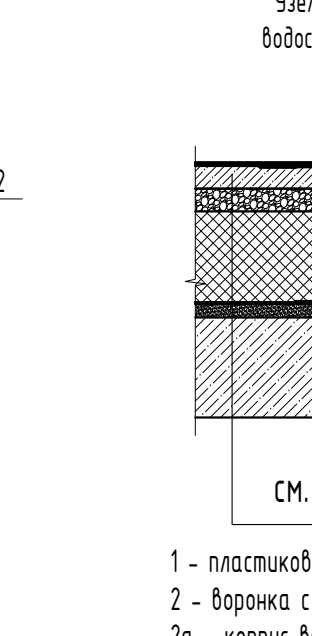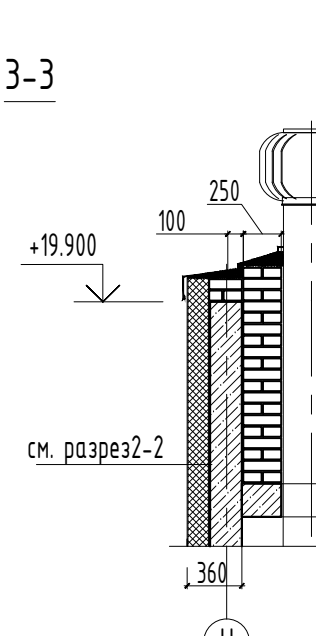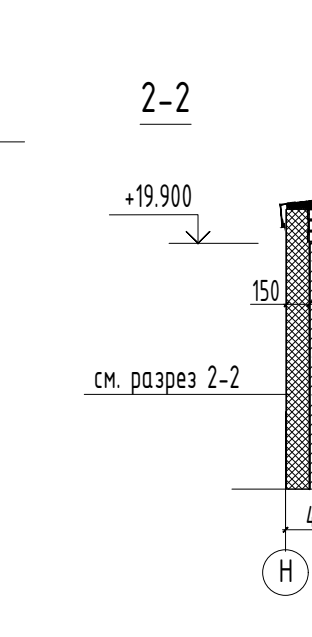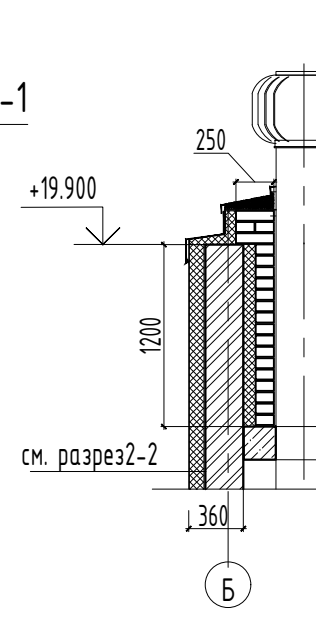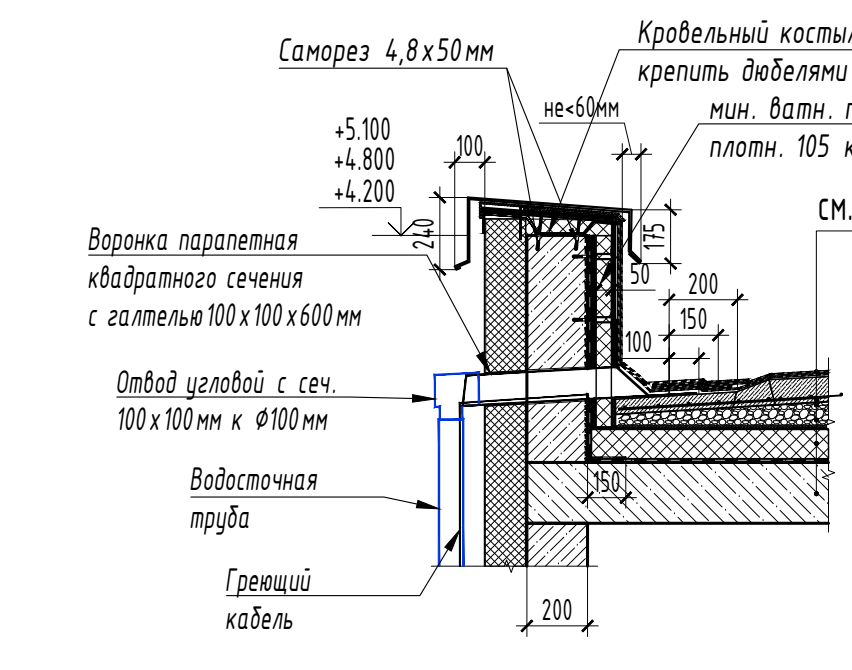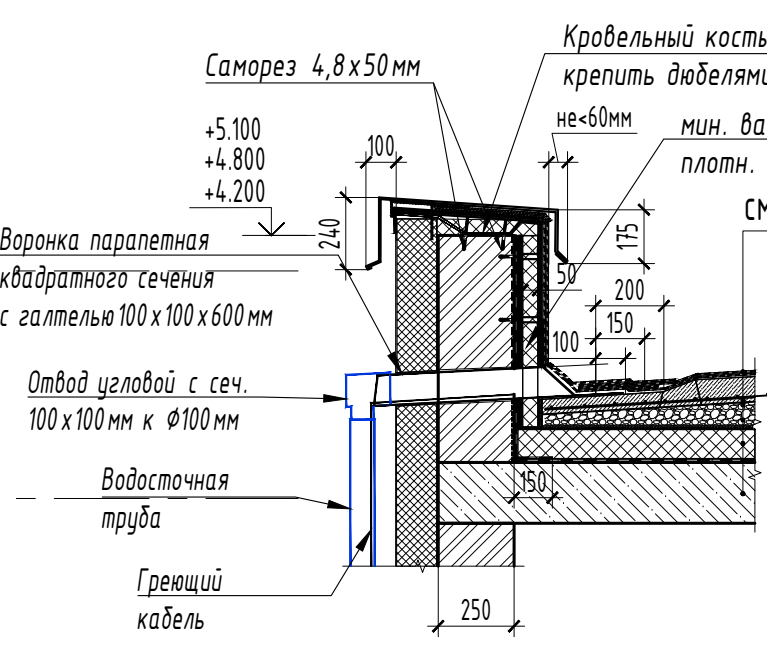

УСЛОВНЫЕ ОБОЗНАЧЕНИЯ

- Водосточная воронка (внутренний организованного водостока)
- Направление ската кровли к внутреннему организованному водостоку
- Бетонная протекторная плита 500х500х50 с покрытием против скольжения по выходящей на кровлю
- Направление осязательности элементов кровли, окон, перегородок
- Панель кровли
- Марка фановой трубы

15-25/1-П-АР			
Капитальный ремонт объекта "ГБОУ Школа № 429 "Соколиная гора", расположенного по адресу: г. Москва, ул. Соколиной горы 5-я, д. 14			
Им. проект	Лист	№ 1	Дата
Разраб.	Лист	№ 1	Дата
Архитектурно-планировочные решения			
И. номер	Губарев	Лист	№ 1
Гип	Наркова	Лист	№ 1
План кровли М1:100			
АЗУРИТ			