



Проектный план трассы КЛ-0.4кВ

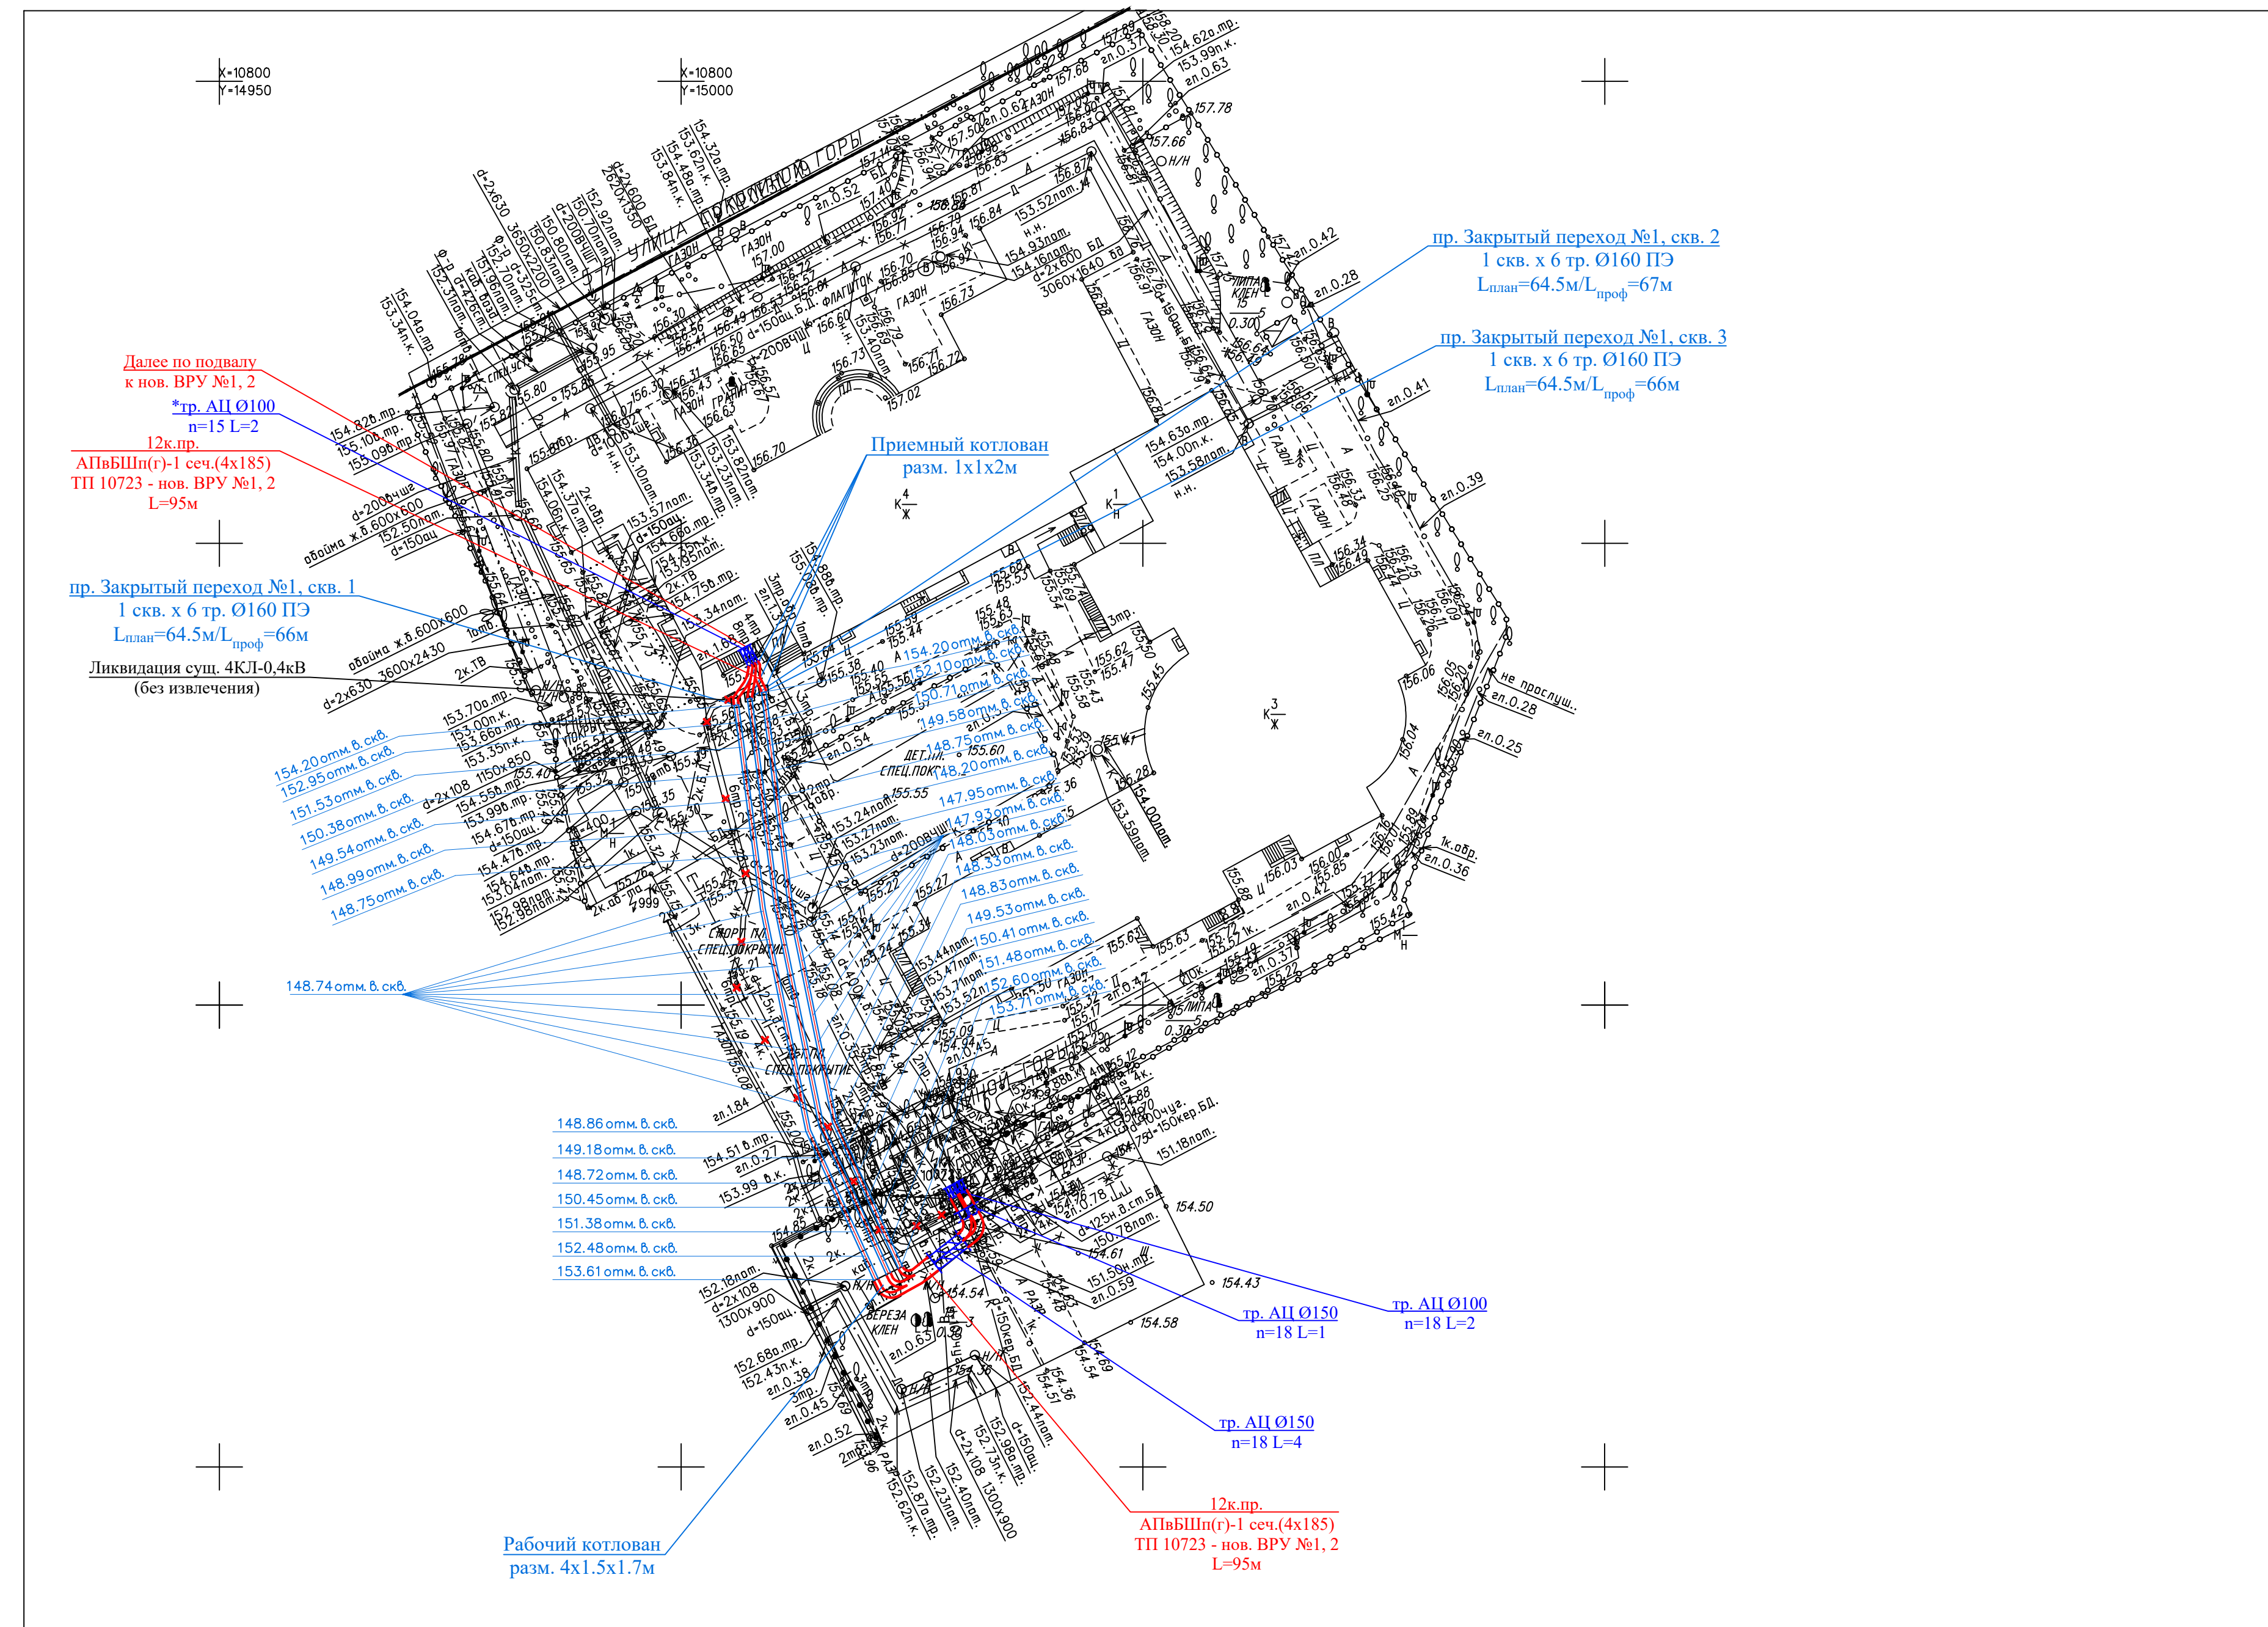


*Примечание – закладные трубы в здание школы монтируются силами заявителя.

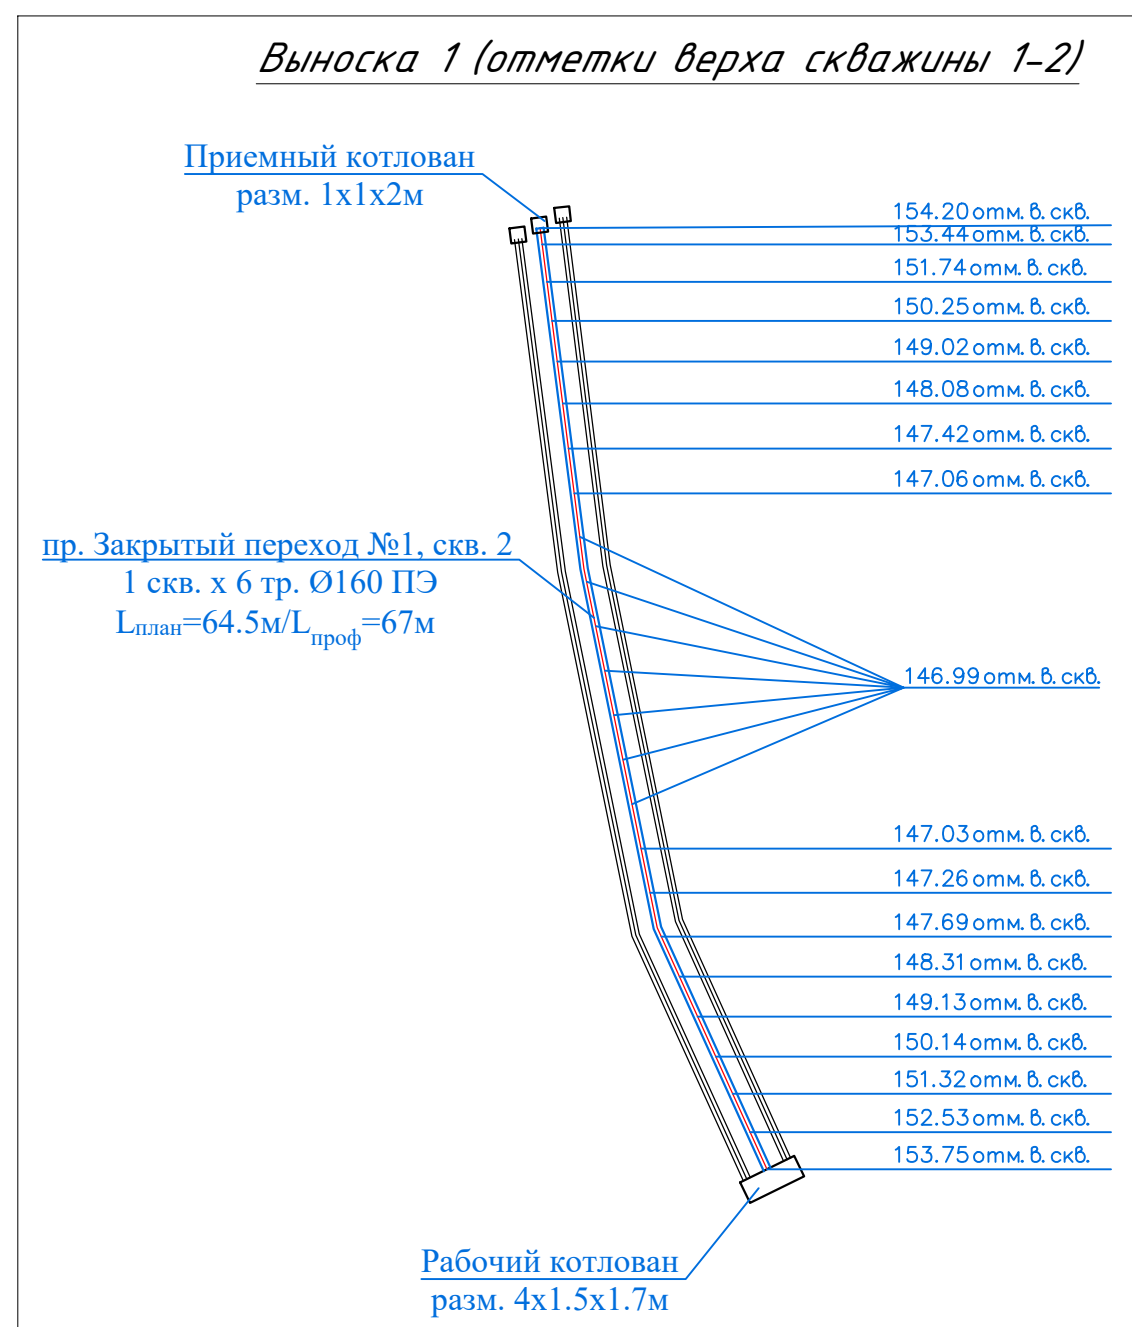

Условные обозначения

№п/п	Изображение	Обозначение
1		Проектируемая КЛ-0,4кВ
2		Проектируемая труба
3		ГНБ

Разрез траншеи

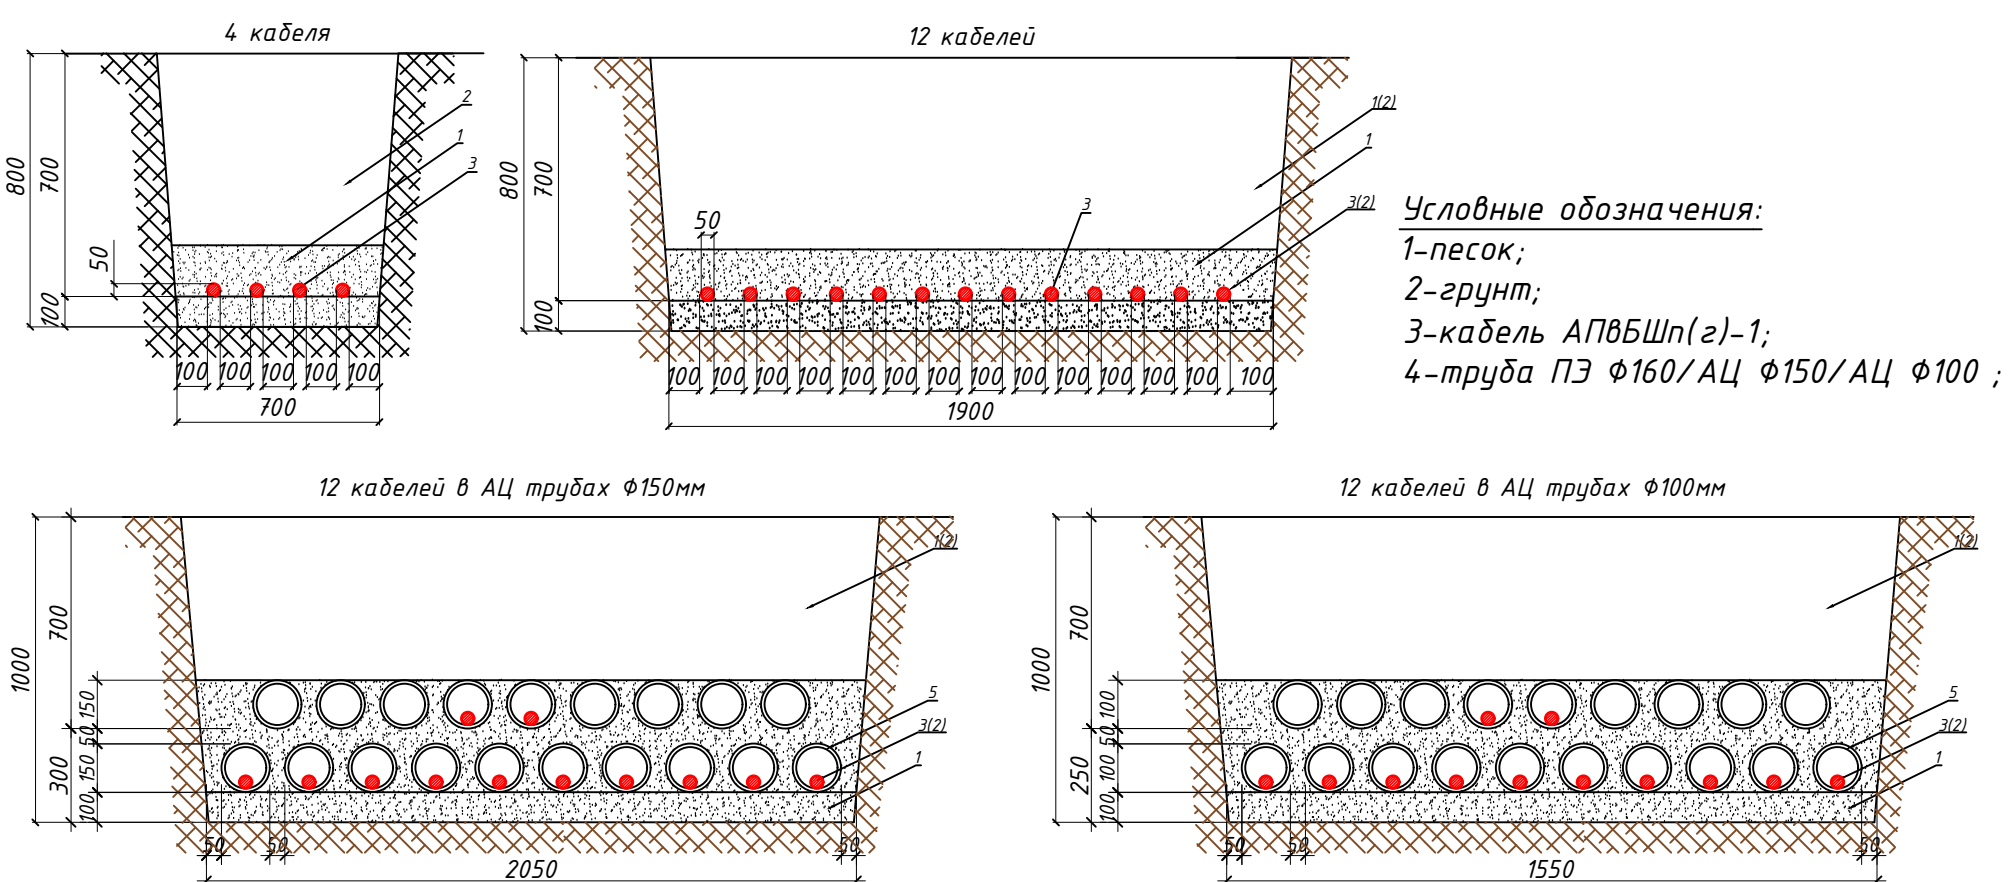

Условные обозначения:
1-песок;
2-грунт;
3-кабель АПВБШп(г)-1;
4-труба ПЗ $\Phi 160$ /АЦ $\Phi 150$ /АЦ $\Phi 100$;

Выводы по эксперименту КНД, 4 КВ
ТЧ 4.28.00.131833/102.

1. Проверить ГНБ совместить с инженером
2. Заказать ил в ВРУ совместить с инженером.
3. По итогам работы представить ГНО, ГНП, выдать представителю

82 ррр.

Финансирование 08.26

Филиал ПАО «Россети»
- М. 05.08.26
Управление капитальных вложений
Восточного района
16 ремонтно-эксплуатационного отделения -
Заместитель начальника
начальник ремонтно-эксплуатационного
района
П.Н. Стасюк

Проект выполнен на инженерно-топографическом плане,
снятом в электронном виде на основании заказов
№ 3/ДО-26/00006, 3/3421-26.
ООО "ЕВРОСТРОЙ" подтверждает полное соответствие данной
геологической оригиналу, выполненному Мосгоргеостром.

ГИП /Жердев Г.А./

Копии всех согласований верны.

ГИП  /Жердев Г.А./

ЛИНИИ ГРАДОСТРОИТЕЛЬНОГО РЕГУЛИРОВАНИЯ НАНЕСЕНЫ ПО СОСТОЯНИЮ
НА 26.03.26

ПРОЕКТИРОВАНИЕ ВЫПОЛНИТЬ В УВЯЗКЕ С СУЩЕСТВУЮЩИМИ ОТМЕТКАМИ

При возникновении вопросов к инженерно-топографическому плану обращаться по электронной почте: consultation_PK@mngt.ru. Если в процессе проведения земляных работ выявляются несоответствия фактического расположения действующих инженерных коммуникаций, согласно п. 2.5.7 Постановления Правительства Москвы от 19.05.2015 № 299-ПП «Об утверждении Правил проведения земляных работ, установив временных ограничений, размещения земляных объектов в городе, а также требований к качеству производства работ представителями проектной организации, заказчика, эксплуатирующих организаций подземных коммуникаций и ГБУ «Мосгоргеотрест».

М 1:500, высота сечения рельефа 0.5м

система координат: Московская; система высот: Московская

						ЗД-26/00006 - ИГДИ-Г
						Наименование объекта: Земельные участки образовательных организаций, подведомственных Департаменту образования и науки города Москвы
Изм.	Колуч.	Лист	№ док.	Подпись	Дата	Заказчик: ДОИМ
Разработан						Местоположение (адрес) объекта: г. Москва, ул. 5-я Сокольническая, вл. 14 (77.03.0004007-89), БУФУ Школа № 429
Полевые работы	Хомеников П. В.			01.03.26		Стадия
Намерал. работы	Ягольникова М. В.			01.03.26		Лист
ЛРП (Пр.лик.)	Народован А. А.			01.03.26		И
Н.контр.	Алимова Л. И.			01.03.26		Листов
						1
						ИНЖЕНЕРНО-ТОПОГРАФИЧЕСКИЙ ПЛАН (М 1:500)
						3/3421-26 - ИГДИ-Г
						Наименование объекта: Строительство 12КЛ-0,4кВ от ТП-100,4кВ № 10723 до ВРУ-0,4кВ № 13 Заявителя, в т.ч. ПИР: г.Москва, 5-я ул.Сокольнической Горы, д.14
Изм.	Кол.уч.	Лист	№ док.	Подпись	Дата	Заказчик: ООО "Евротест"
Разработан						Местоположение (адрес) объекта: г. Москва, 5-я ул.Сокольнической Горы, д. 14
Полевые работы	Хомеников П. В.			08.08.26		Стадия
Намерал. работы	Матвеевичко Е. В.			08.08.26		Лист
ЛРП (Пр.лик.)	Народован А. А.			08.08.26		И
Н.контр.	Алимова Л. И.			08.08.26		Листов
						1
						ИНЖЕНЕРНО-ТОПОГРАФИЧЕСКИЙ ПЛАН (М 1:500)
						Заказчик: ПАО "Россети - Московский регион"
						Шифр: 361550-ТКР.ЭС
						Строительство 12КЛ-0,4кВ от ТП-10/0,4кВ № 10723 до ВРУ-0,4кВ № 12 Заявителя, в м.ч. ПИР: г. Москва, 5-я ул. Сокольнической Горы, д.14
Изм.	Колуч.	Лист	№ док.	Подп.	Дата	Стадия
Разраб.	Курганкин			08.26		Лист
ГИП	Жердев Г. А.			08.26		Листов
						Р
						1
						1
						План трассы КЛ-0,4кВ М 1:500
Н.контроль	Моисеева Т.			08.26		