


Тех. этаж

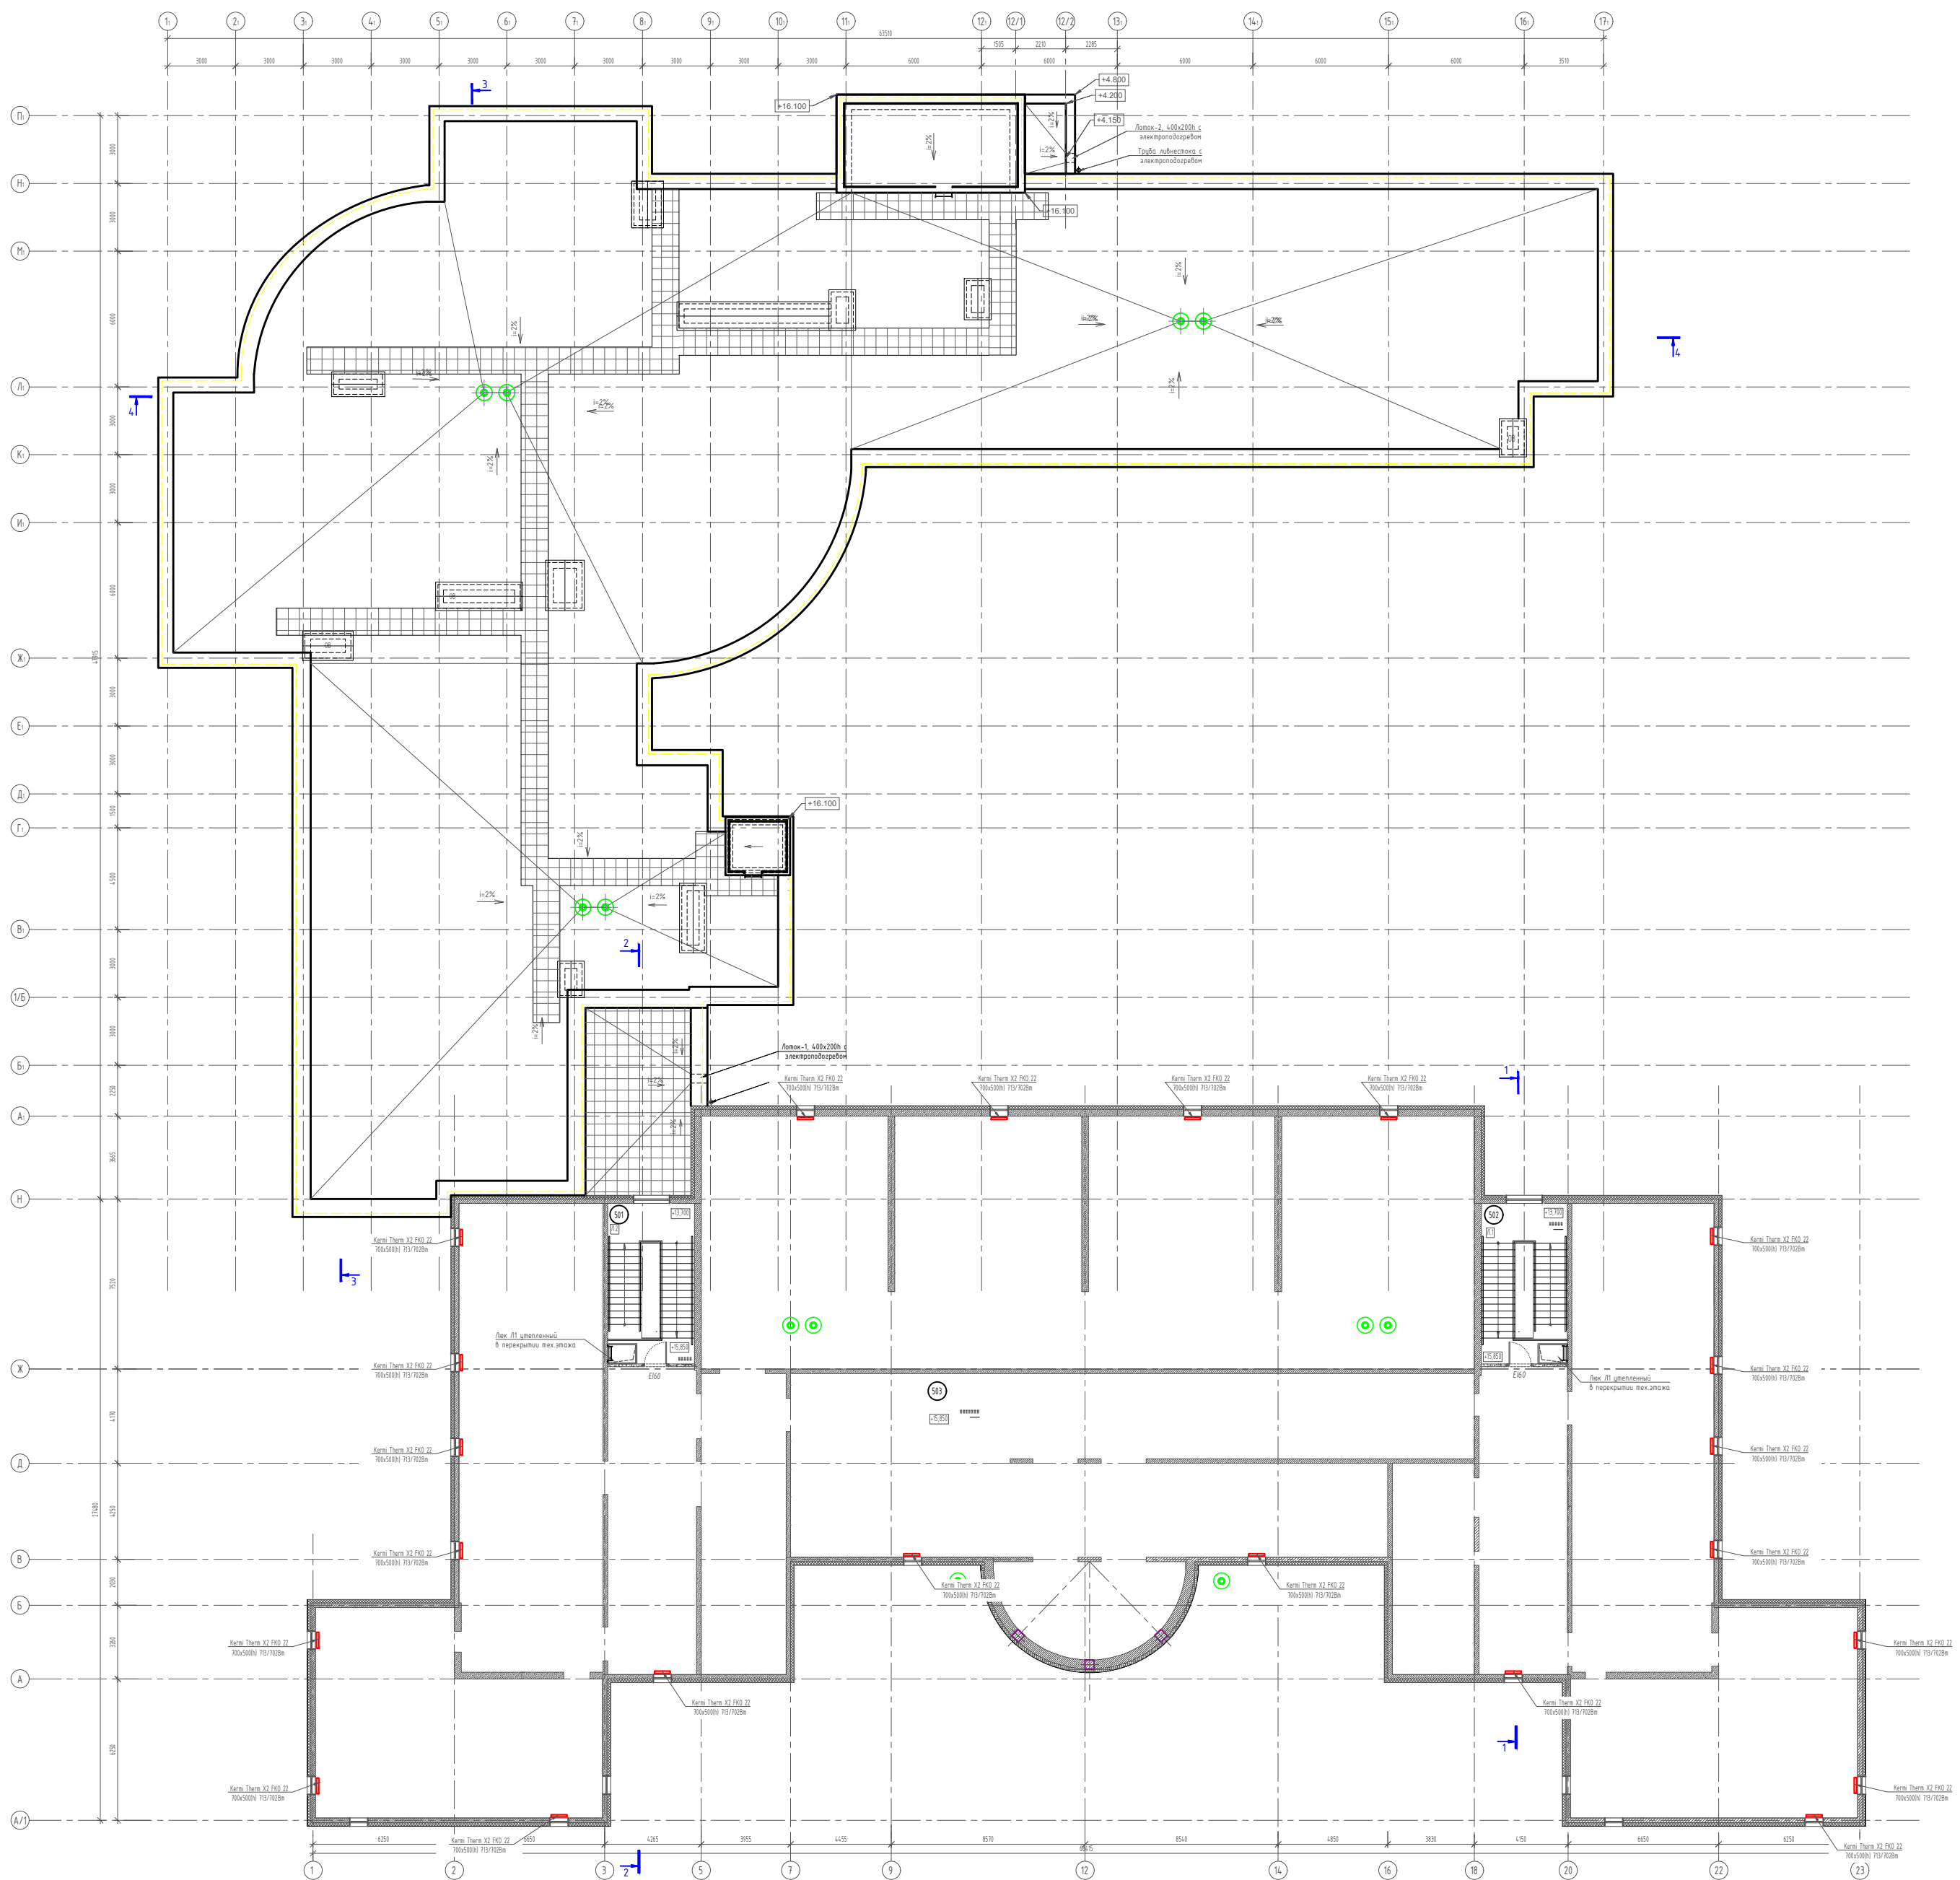

Экспликац	
Номер поме- щения	
501	Лестничная кл
502	Лестничная кл
503	Техническое п

201

E30/EI30/ETk

±0,000