



АЗУРИТ

ООО ПСК «Азурит»
ИНН: 7722762829
Рег. № члена СРО
№ П-163-007722762829-0240
от 23.04.2019г. СРО АП «АПП»

Тел: 8 (495) 724-53-47
e-mail: info@psk-azurit.ru

Экз. №

Заказчик: "АНО «ОЭК Стройтрест»"

**Капитальный ремонт общеобразовательного учреждения
(ГБОУ «Школа № 429»), расположенного по адресу:
г. Москва, 5-ая ул. Соколиной Горы д.14
1 этап**

ПРОЕКТНАЯ ДОКУМЕНТАЦИЯ

**Раздел 5 "Сведения об инженерном оборудовании, о сетях
и системах инженерно-технического обеспечения"**

Подраздел 5 «Сети связи»

Часть 10. Система двухсторонней связи

1 этап

16-25/Г-П – ИОС5.10

Том 5.5.10

Изм.	№ док.	Подп.	Дата



АЗУРИТ

ООО ПСК «Азурит»
ИНН: 7722762829
Рег. № члена СРО
№ П-163-007722762829-0240
от 23.04.2019г. СРО АП «АПП»

Тел: 8 (495) 724-53-47
e-mail: info@psk-azurit.ru

Экз. №

Заказчик: "АНО «ОЭК Стройтрест»"

**Капитальный ремонт общеобразовательного учреждения
(ГБОУ «Школа № 429»), расположенного по адресу:
г. Москва, 5-ая ул. Соколиной Горы д.14
1 этап**

ПРОЕКТНАЯ ДОКУМЕНТАЦИЯ

**Раздел 5 "Сведения об инженерном оборудовании, о сетях
и системах инженерно-технического обеспечения"**

Подраздел 5 «Сети связи»

Часть 10. Система двухсторонней связи

1 этап

16-25/Г-П – ИОС5.10

Том 5.5.10

Технический директор –
главный инженер
Главный инженер проекта



Н.А. Губарев

Н.В. Маркова

Изм.	№ док.	Подп.	Дата

Содержание тома

Обозначение	Наименование	Примечание
16-25/Г -П-ИОС5.10-С	Содержание тома	3
16-25/Г -ИОС5.10-ТЧ	Текстовая часть	4
16-25/Г -ИОС5.10-ГЧ	Графическая часть	9
Прилагаемые материалы		
16-25/Г -П-ИОС5.10.СО	Спецификация оборудования, изделий и материалов	
	Общее количество листов	14

Согласовано		

Взам. инв. №	
Подп. и дата	
Инв. № подл.	

						16-25/Г -П-ИОС5.10-С			
Изм.	Кол.уч.	Лист	№ док.	Подп.	Дата				
Разработал	Сошников		29.05.26	СОДЕРЖАНИЕ ТОМА			Стадия	Лист	Листов
Проверил	Поляков		29.05.26				П	3	13
Н. контр.	Воробьев		29.05.26				 АЗУРИТ		
ГИП	Маркова		29.05.26						

Текстовая часть

Ведомость документов графической части

Обозначение	Наименование	Примечание
429-26-П-ИОС5.10-ГЧ	Принципиальная схема	
429-26-П-ИОС5.10-ГЧ	Уровень подвала. План расположения оборудования	
429-26-П-ИОС5.10-ГЧ	1й-этаж. План расположения оборудования	
429-26-П-ИОС5.10-ГЧ	2й-этаж. План расположения оборудования	
429-26-П-ИОС5.10-ГЧ	3й-этаж. План расположения оборудования	
429-26-П-ИОС5.10-ГЧ	4й-этаж. План расположения оборудования	

Согласовано		

Взам. инв. №	

Подп. и дата	

Инв. № подл.	

						16-25/Г -П-ИОС5.10-ТЧ		
Изм.	Кол.уч.	Лист	№ док.	Подп.	Дата	ТЕКСТОВАЯ ЧАСТЬ		
Разработал	Сошников				01.06.26			
Проверил	Поляков				01.06.26			
Н. контр.	Воробьев				01.06.26			
ГИП	Маркова				01.06.26			
						Стадия	Лист	Листов
						П	1	6
						 АЗУРИТ		

Содержание

1	Общие сведения	3
1.1	Общие указания	3
1.2	Перечень нормативно-технической документации	3
2	Вызывная сигнализация для мгн	3
2.1	Состав и размещение оборудования	3
2.2	Алгоритм работы вызывной сигнализации для МГН	4
2.3	Кабельные изделия:	4
3	Электропитание	5
4	Заземление	4
5	Режим работы проектируемой системы	5
6	Перечень допускаемых сокращений слов	5

Инв. № подл.	Подп. и дата	Взам. инв. №							Лист
									2
			Изм.	Кол.уч.	Лист	№ док.	Подпись	Дата	16-25/Г -П-26-П-ИОС5.10-ТЧ

1 Общие сведения

1.1 Общие указания

Проектная документация разработана на основании технического задания на проектирование, архитектурного проекта и смежных инженерных разделов.

Инженерные решения, разработанные на стадии проектной документации, соответствуют выданным техническим условиям, требованиям действующих технических регламентов, стандартов, сводов правил, а также противопожарных требований.

Оборудование, приведенное в данном разделе, подлежит замене исключительно при идентичных технических и габаритных параметрах заменяемого оборудования и только при согласовании с Заказчиком.

1.2 Перечень нормативно-технической документации

Проектная документация разработана на основании следующих документов:

- Федеральный закон от 30.12.2009 г. N 384-ФЗ. Технический регламент о безопасности зданий и сооружений;
- Постановление Правительства Российской Федерации от 16.02.2008 г. № 87. О составе разделов проектной документации и требованиях к их содержанию.;
- ГОСТ Р 21.101-2020 Основные требования к проектной и рабочей документации;
- ГОСТ Р 31565-2012 Кабельные изделия. Требования пожарной безопасности;
- ПУЭ. Правила устройства электроустановок. Издание 7, 2009г.
- СП 118.13330.2022 Общественные здания и сооружения;
- СП 59.13330.2016 Доступность зданий и сооружений для маломобильных групп населения. Актуализированная редакция СНиП 35-01-2001
- СП134.13330.2022 Системы электросвязи зданий и сооружения. Основные положения проектирования

2 Вызывная сигнализация для мгно

2.1 Состав и размещение оборудования.

Вызывная сигнализация для МГН предусматривается:

На 1 этаже:

- перед пандусом предусматривается установка переговорного устройства GC-2001P4;
- в санузле для МГН 103 предусматривается установка переговорного устройства GC-2001W3, проводной кнопки экстренного вызова со шнуром и

Взам. инв. №	Подп. и дата	Инв. № подл.							Лист	
										3
Изм.	Кол.уч.	Лист	№ док.	Подпись	Дата	16-25/Г -П-26-П-ИОС5.10-ТЧ				

ручкой GC-0423W1, устройства сброса GC-0421W1 и сигнальной лампы GC-0611W4 (со стороны коридора и в нутри помещения).

Пульт селекторной связи GC-1036F4 устанавливается в помещении охраны 122.

Источник бесперебойного питания ББП-50 устанавливается в вестибюле 102.

Для обеспечения двухсторонней связи на объекте предусматривается установка переговорного устройства GC-2001P4 у основных и эвакуационных выходов 1-го этажа.

В местах массового прибывания людей на объекте предусматривается установка переговорного устройства GC-2001W3 у входов в помещение.

2.2 Алгоритм работы вызывной сигнализации для МГН

В случае экстренной ситуации в санузле (например падение инвалида на пол) он тянет за ручку кнопки GC-0423W1, тем самым посылая вызов на пульт дежурного GC-1006D5. При послыке вызова, сигнальная лампа GC-0611W4 начинает мигать красным цветом и подавать звуковой сигнал.

На пульте дежурного персонала раздается вызов и после установки двухсторонней голосовой связи между пультом и абонентским устройством GC-2001W3, сигнальная лампа перестает подавать звуковые сигналы и меняет цвет свечения на зеленый. Установив голосовую связь, дежурный может выяснить причину вызова и предпринять необходимые действия для устранения этой ситуации.

После разрыва соединения сигнальная лампа гаснет. Если же, после послыки сигнала о помощи инвалидом, обслуживающий персонал сразу пришел в туалетную комнату, то он нажимает кнопку сброса GC-0421W1, тем самым сбрасывая поступивший вызов из данного санузла, и может приступить к оказанию помощи инвалиду.

В случае, если инвалиду нужна помощь на входе в корпус, он нажимает на кнопку вызова, расположенную на переговорном устройстве GC-2001P4, тем самым посылая вызов на пульт GC-1006D5. После ответа дежурного, инвалид может объяснить какая помощь ему требуется, чтобы дежурный мог оказать помощь инвалиду.

2.3 Кабельные изделия:

Кабели системы двухсторонней связи выполняются кабелями с медными жилами и прокладываются отдельно от всех силовых, осветительных кабелей и проводов.

Кабельные трассы системы двухсторонней связи прокладываются в металлических листовых перфорированных лотках системы СКС. Опуски с лотков выполняются в гофрированных трубах ПВХ соответствующего диаметра, не распространяющих горение.

Для выполнения требований Федерального закона от 22.07.2008 №123-ФЗ и ГОСТ 31565—2012 проектом предусмотрен кабель с медными жилами с индексом нг (А)-LSLTx.

Прокладка кабеля выполнена в лотках и гофрированных трубах скрыто за подвесными потолками и открыто по потолкам в технических помещениях.

Кабели связи прокладываются отдельно от всех силовых, осветительных кабелей и проводов.

Проходы кабелей через стены и перегородки выполняются в отрезках стальных труб при одиночной прокладке, зазоры между кабелями и кабелепроводами заделываются при помощи огнеупорного раствора, не снижающего предел огнестойкости пересекаемой преграды, а в местах пересечения противопожарных преград группами кабелей предусмотрены

Изн. № подл.	Подп. и дата	Взам. инв. №							Лист
Изм.	Кол.уч.	Лист	№ док.	Подпись	Дата	16-25/Г -П-26-П-ИОС5.10-ТЧ			4

огнестойкие кабельные проходки. Концы коробов, крышек, труб и др. защищаются от заусенцев.

3 Электропитание

Электроснабжение систем предусмотрено по I категории надежности ПУЭ от независимых источников с устройством автоматического ввода резерва (АВР) между ними. Питание технических средств системы предусмотрено от отдельных щитов, запитанных напрямую с ГРЩ. Электроснабжение систем предусматривается разделом ИОС1.1 (электроснабжение)

Для электроснабжения приборов систем связи применяются источники бесперебойного питания. Емкость герметизированных аккумуляторных батарей, позволяющих поддерживать работоспособность системы при отключении электропитания объекта в дежурном режиме в течении 15 минут, определить на этапе разработки Рабочей документации.

4 Заземление

Предусмотренные проектом элементы электротехнического оборудования удовлетворяют требованиям ГОСТ 12.2.007.0-75 по способу защиты человека от поражения электрическим током.

Защитное заземление и зануление проектируемого электрооборудования и возводимых конструкций выполняется в соответствии с требованиями ПУЭ, СП 76.13330.2016, ГОСТ 12.1.030 -81 и технической документацией завода-изготовителя.

Присоединение заземляющих и нулевых защитных проводников к частям электрооборудования должно быть выполнено сваркой или болтовым соединением.

Для обеспечения безопасности эксплуатации системы предусмотреть выполнение защитного заземления от ГРЩ здания или от групповых щитков.

5 Режим работы проектируемой системы

Режим работы проектируемого оборудования - круглосуточный.

6 Перечень допускаемых сокращений слов

Приложение А(справочное). Перечень допускаемых сокращений слов.
Таблица А1.

Полное наименование	Сокращение
Автоматизированное рабочее место	АРМ
Структурированная кабельная система	СКС

Взам. инв. №	
Подп. и дата	
Инв. № подл.	

						16-25/Г -П-26-П-ИОС5.10-ТЧ	Лист 5
Изм.	Кол.уч.	Лист	№ док.	Подпись	Дата		


Рабочая документация	РД
Система двухсторонней связи	СДС
Маломобильные группы населения	МГН
Персональный компьютер	ПК
Программное обеспечение	ПО
Локальная вычислительная сеть	ЛВС
Операционная система	ОС

Инов. № подл.	Подп. и дата	Взам. инв. №

Изм.	Кол.уч.	Лист	№ док.	Подпись	Дата

16-25/Г -П-26-П-ИОС5.10-ТЧ

Согласовано					
Изм. № подл.	Взам. инв. №	Подп. и дата			

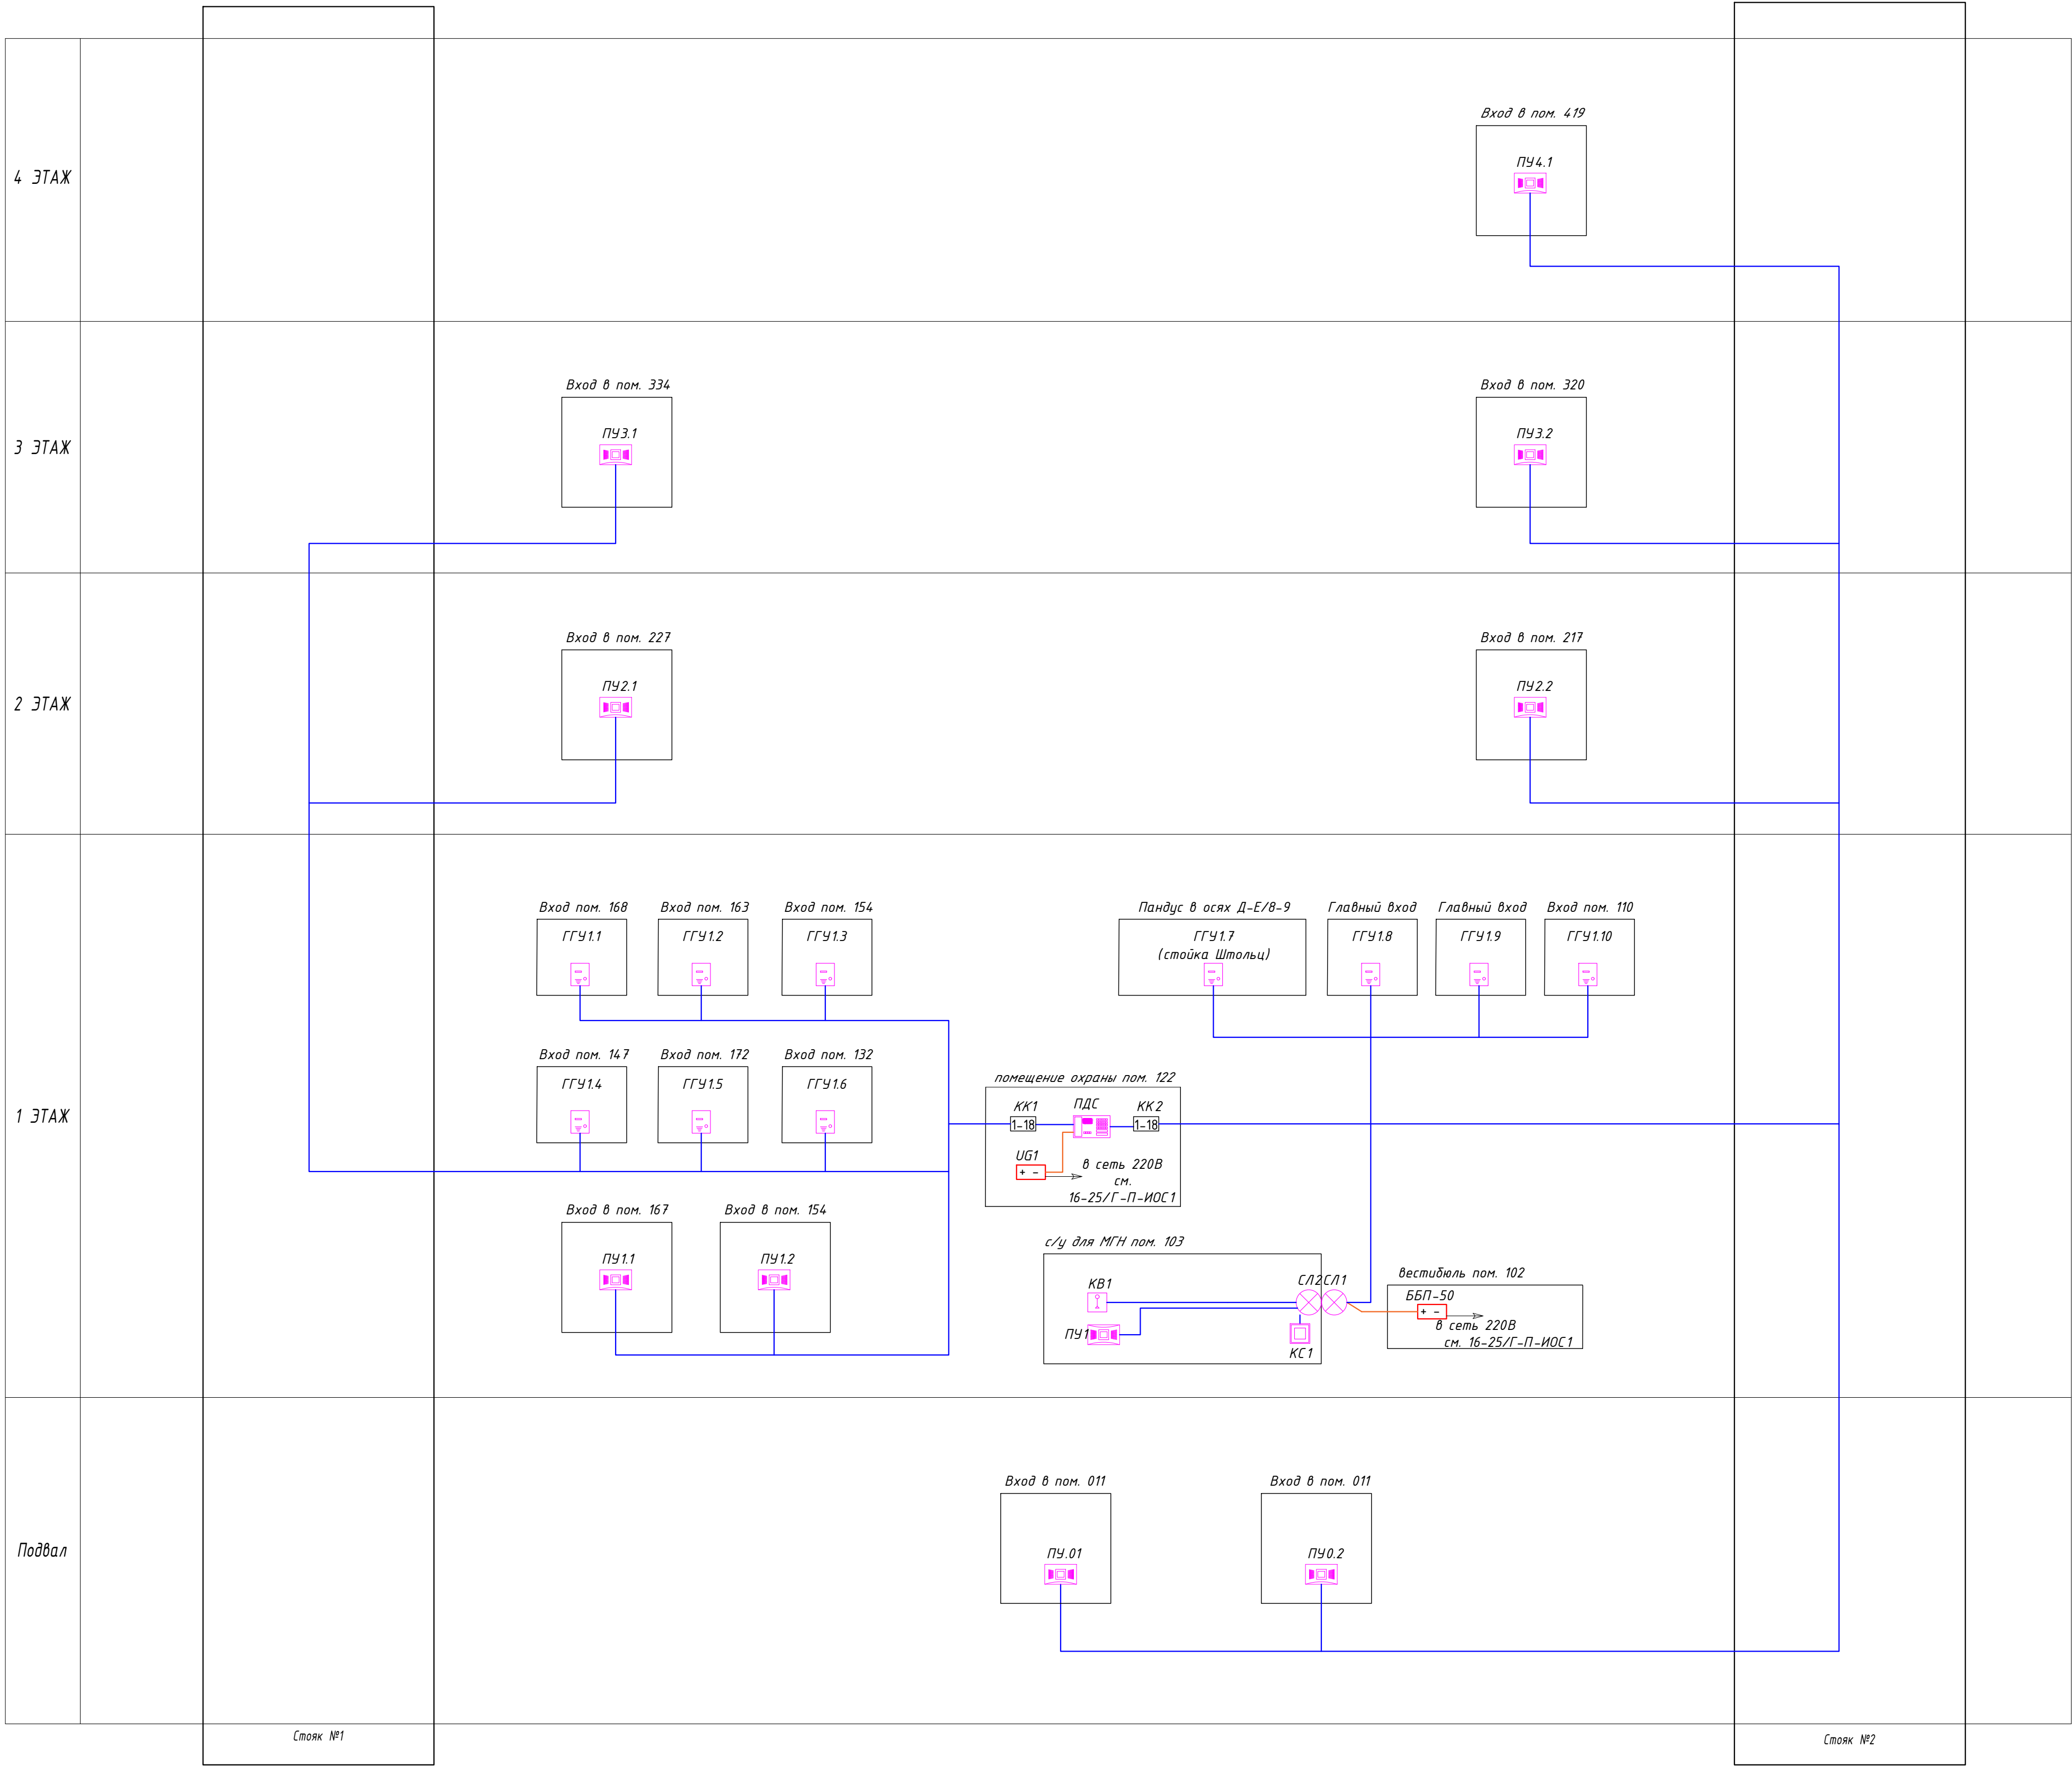

- Условные обозначения:
- пульт диспетчерской связи на 24 абонентов ГС-1036F4 (ПДС)
 - громкоговорящее переговорное устройство ГС-2001Р4 (ГГУ) с указанием порядкового номера
 - переговорное устройство ГС-2001W3 (ГГУ) с указанием порядкового номера
 - сигнальная лампа ГС-061W4 (СЛ) с указанием порядкового номера
 - кнопка сброса ГС-0421W1 (КС) с указанием порядкового номера
 - кнопка вызова со шнуром ГС-0423W1 (КВ) с указанием порядкового номера
 - блок питания ББП-50 (ББП-50)
 - кабель КПСВВнг(А)-LSLTx 1x2x0,5
 - кабель питания ВВГнг(А)-LSLTx 1x2x1,5

						16-25/Г-П-ИОС 5.10-ГЧ			
						Капитальный ремонт общеобразовательного учреждения (ГБОУ «Школа № 429»), расположенного по адресу: г. Москва, 5-ая ул. Соколиной Горы д.14 1 этап			
Изм.	Кол.ч.	Лист	№ док.	Подп.	Дата	Часть 10. Система двусторонней связи	Стадия	Лист	Листов
Разраб.		Сошников			05.26		П	1	6
Проверил		Поляков			05.26				
						Принципиальная схема	 АЗУРИТ		
Н. контр.		Воробьев			05.26				
ГИП		Маркова			05.26				

Копировал

Номер помещения	Наименование	Площадь м2	Категория
001	ИТП	66,06	д
002	Венткамера с форканерой	71,36	в3
004	Водомерный узел и насосная	1130	д
005	Венткамера	28,40	в3
006	Венткамера	198,07	в3
007	Венткамера	138,94	в3
008	Техническое помещение для прокладки инженерных коммуникаций	974,84	в3
009	Венткамера	64,68	в3
010	Венткамера	64,96	в3
011	Защитное помещение гражданской обороны	249,34	д
012	Коридор	50,95	д
013	Санузел женский	10,88	д
014	Санузел мужской	4,45	д
015	Коридор	2,108	д
016	Узел ввода электрических сетей	570,70	в4
017	Коридор	39,60	д
		2047,4	
		Всего	


Номер помещения	Наименование	Площадь м2	Категория
001	ИТП	66,06	д
002	Венткамера с форканерой	71,36	в3
004	Водомерный узел и насосная	1130	д
005	Венткамера	28,40	в3
006	Венткамера	198,07	в3
007	Венткамера	138,94	в3
008	Техническое помещение для прокладки инженерных коммуникаций	974,84	в3
009	Венткамера	64,68	в3
010	Венткамера	64,96	в3
011	Защитное помещение гражданской обороны	249,34	д
012	Коридор	50,95	д
013	Санузел женский	10,88	д
014	Санузел мужской	4,45	д
015	Коридор	2,108	д
016	Узел ввода электрических сетей	5,70	в4
017	Коридор	39,60	д
		2047,4	
		Всего	

1. Места размещения оборудования систем дымовых газов показаны условно. Точное местонахождение оборудования определить при монтаже с учетом архитектурных решений, расстояний оборудования, дверных проемов, зон доступности ГИ и удобства эксплуатации.

2. Громкоговорящие переводные устройства ГС-200/1 и ГС-200/1ПЗ устанавливаются в местах вызова помощи сестры эрготехнической части проекта.


3. Оптику к оборудованию выполнять скрыто за отделочными материалами или в гофрированной трубке в кабель-канал, выполненный пологой или опускной возможности скрытой прокладки, например по штукатурке, кирпичным или бетонным стенам, и при соединении с Заказчиком.

						16-25/ГЧ - П.-ИОС С-10-ГЧ							
						Капитальный ремонт общеобразовательного учреждения ("БОУ "Школа № 428"), расположенного по адресу: г. Москва, 5-я ул. Соколиной Гори д.4 кп 1 шт.							
Изв.	Контр.	Лист	Мфдо	Подг.	Дат						Стадия	Лист	Листов
Разработчик		Соколовский			05.26						P		
Проектировщик		Полынов			05.26							2	
						Часть 10. Система двухсторонней связи							
N контр.		Варварова			05.26								
ГИП		Маркова			05.26								
						План размещения оборудования и кабельных трасс в подвале.							
						 AZURIT							

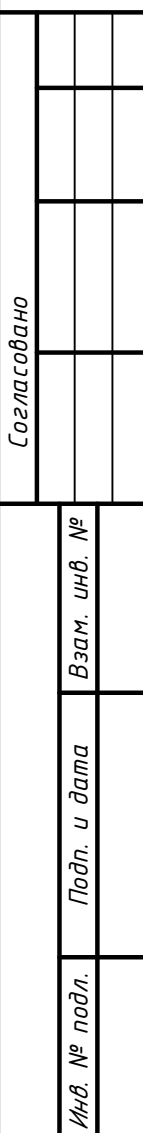

Номер помещения	Наименование	Площадь м2	Кат. помещения
101	Танбур	35,02	
102	Коридор с рекреацией	277,54	
103	Санузел для МН	5,23	
104	Административный кабинет тип 1 (начальная школа)	25,91	
106	Санузел для девочек (начальная школа)	23,25	
107	Гардеробная для обучающихся (основная и старшая школа)	97,54	
108	Гардеробная для обучающихся (основная и старшая школа)	35,25	
109	Гардеробная для обучающихся (начальная школа)	57,49	
110	Лестничная клетка (Л1)	24,50	
111	Коридор	77,66	
112	Санузел для мальчиков (начальная школа)	12,44	
113	Санузел для персонала	2,78	
114	Учебные кабинеты (начальная школа)	60,20	
115	Учебные кабинеты (начальная школа)	58,33	
117	Учебные кабинеты (начальная школа)	58,22	
118	ПУИ	2,78	В4
119	Санузел для девочек (начальная школа)	12,44	
120	Коридор с рекреацией (основная и старшая школа)	95,10	
122	Комната охраны (с диспетчерским пунктом)	23,43	
123	Гардеробная комната (для учителей)	9,86	
124	Помещение связи	9,47	В4
125	Санузел для мальчиков (начальная школа)	21,73	
127	Учебные кабинеты (начальная школа)	57,26	
128	Учебные кабинеты (начальная школа)	53,71	
129	Учебные кабинеты (начальная школа)	58,81	
130	Коридор с рекреацией	117,57	
131	Лестничная клетка Тип N2	27,18	
132	Вестибюль	4,20,02	
133	Электрощитовая	16,16	В3
134	Место для приготовления дезинфицирующих растворов и хранения уборочного инвентаря, предназначенных для помещений медико-социального назначения	7,64	В4
134.1	Туалет медпункта	4,31	
135	Кабинет врача	27,00	
136	Процедурный (прибавочный) кабинет	20,80	
137	Коридор	26,63	
138	Комната инструктора	12,07	
138.1	Санузел с душем	7,03	
139	ПУИ	6,79	В4
140	Санузел для персонала	3,27	
141	Помещение связи	12,01	В3
142	Помещение для персонала	11,87	
142.1	Санузел для персонала	2,01	
142.2	Душевая	2,82	
143	ПУИ	4,85	В4
144	Помещение для временного хранения пищевых отходов	6,01	В4
145	Кладовая и моечная оборотной тары	6,92	В4
146	Загрузочный цех	74,5	В4
147	Коридор	28,66	
147.1	Помещение с холодильным оборудованием	26,78	
148	Кладовая сухих продуктов	10,93	В3
149	Дозаготовительный цех	15,16	В3
150	Горячий цех	39,25	В3
151	Моечная для кухонной посуды	9,75	Д
152	Моечная для столовой посуды	34,78	Д
152.1	Предмоечная	5,48	Д
153	Холодный цех	15,96	В3
154	Обеденный зал	178,91	
155	Раздевальная	11,10	
156	Санузел	2,40	
157	Санузел	2,48	
158	Душевые	4,15	
159	Душевые	8,16	
160	Санузел для мальчиков	4,71	
161	Санузел для девочек	9,76	
162	Раздевальная	17,10	
163	Лестничная клетка (Л1)	21,00	
164	Техническое помещение	4,16	В4
165	Складная	21,21	В3
166	ПУИ	4,30	В4
167	Универсальный спортивный зал	270,82	
168	Лестничная клетка (Л1)	25,50	
169	Коридор и рекреация (основная и старшая школа)	281,24	
171	Тех. помещение	3,93	В4
172	Лестничная клетка (Л1)	21,00	
172.1	Танбур	4,48	
173	Электрощитовая	17,34	В3
Всего		2688,9	

							N-237/P.-П.ИССС.10/Г
							Выполнены ремонт общедомового хозяйства учреждения (ТОУ) «Школа № 69», расположенного по адресу г. Москва, 5-я ул. Иссоски Гари 3а и 1 этаж.
Инз.	Контр.	Лист	Модуль	Дата	Подп.	Всего	
Разработчик	Соинский	08	05.26				Стандарт Лист Листов
Проверщик	Любимов	08	05.28				п з
M. контр.	Бородавко	08	05.26				Часть 10. Система двухсторонней связи План расположения оборудования и кабельных трасс на 1 этаже
K. контр.	Михайлов	08	05.26				AZURIT

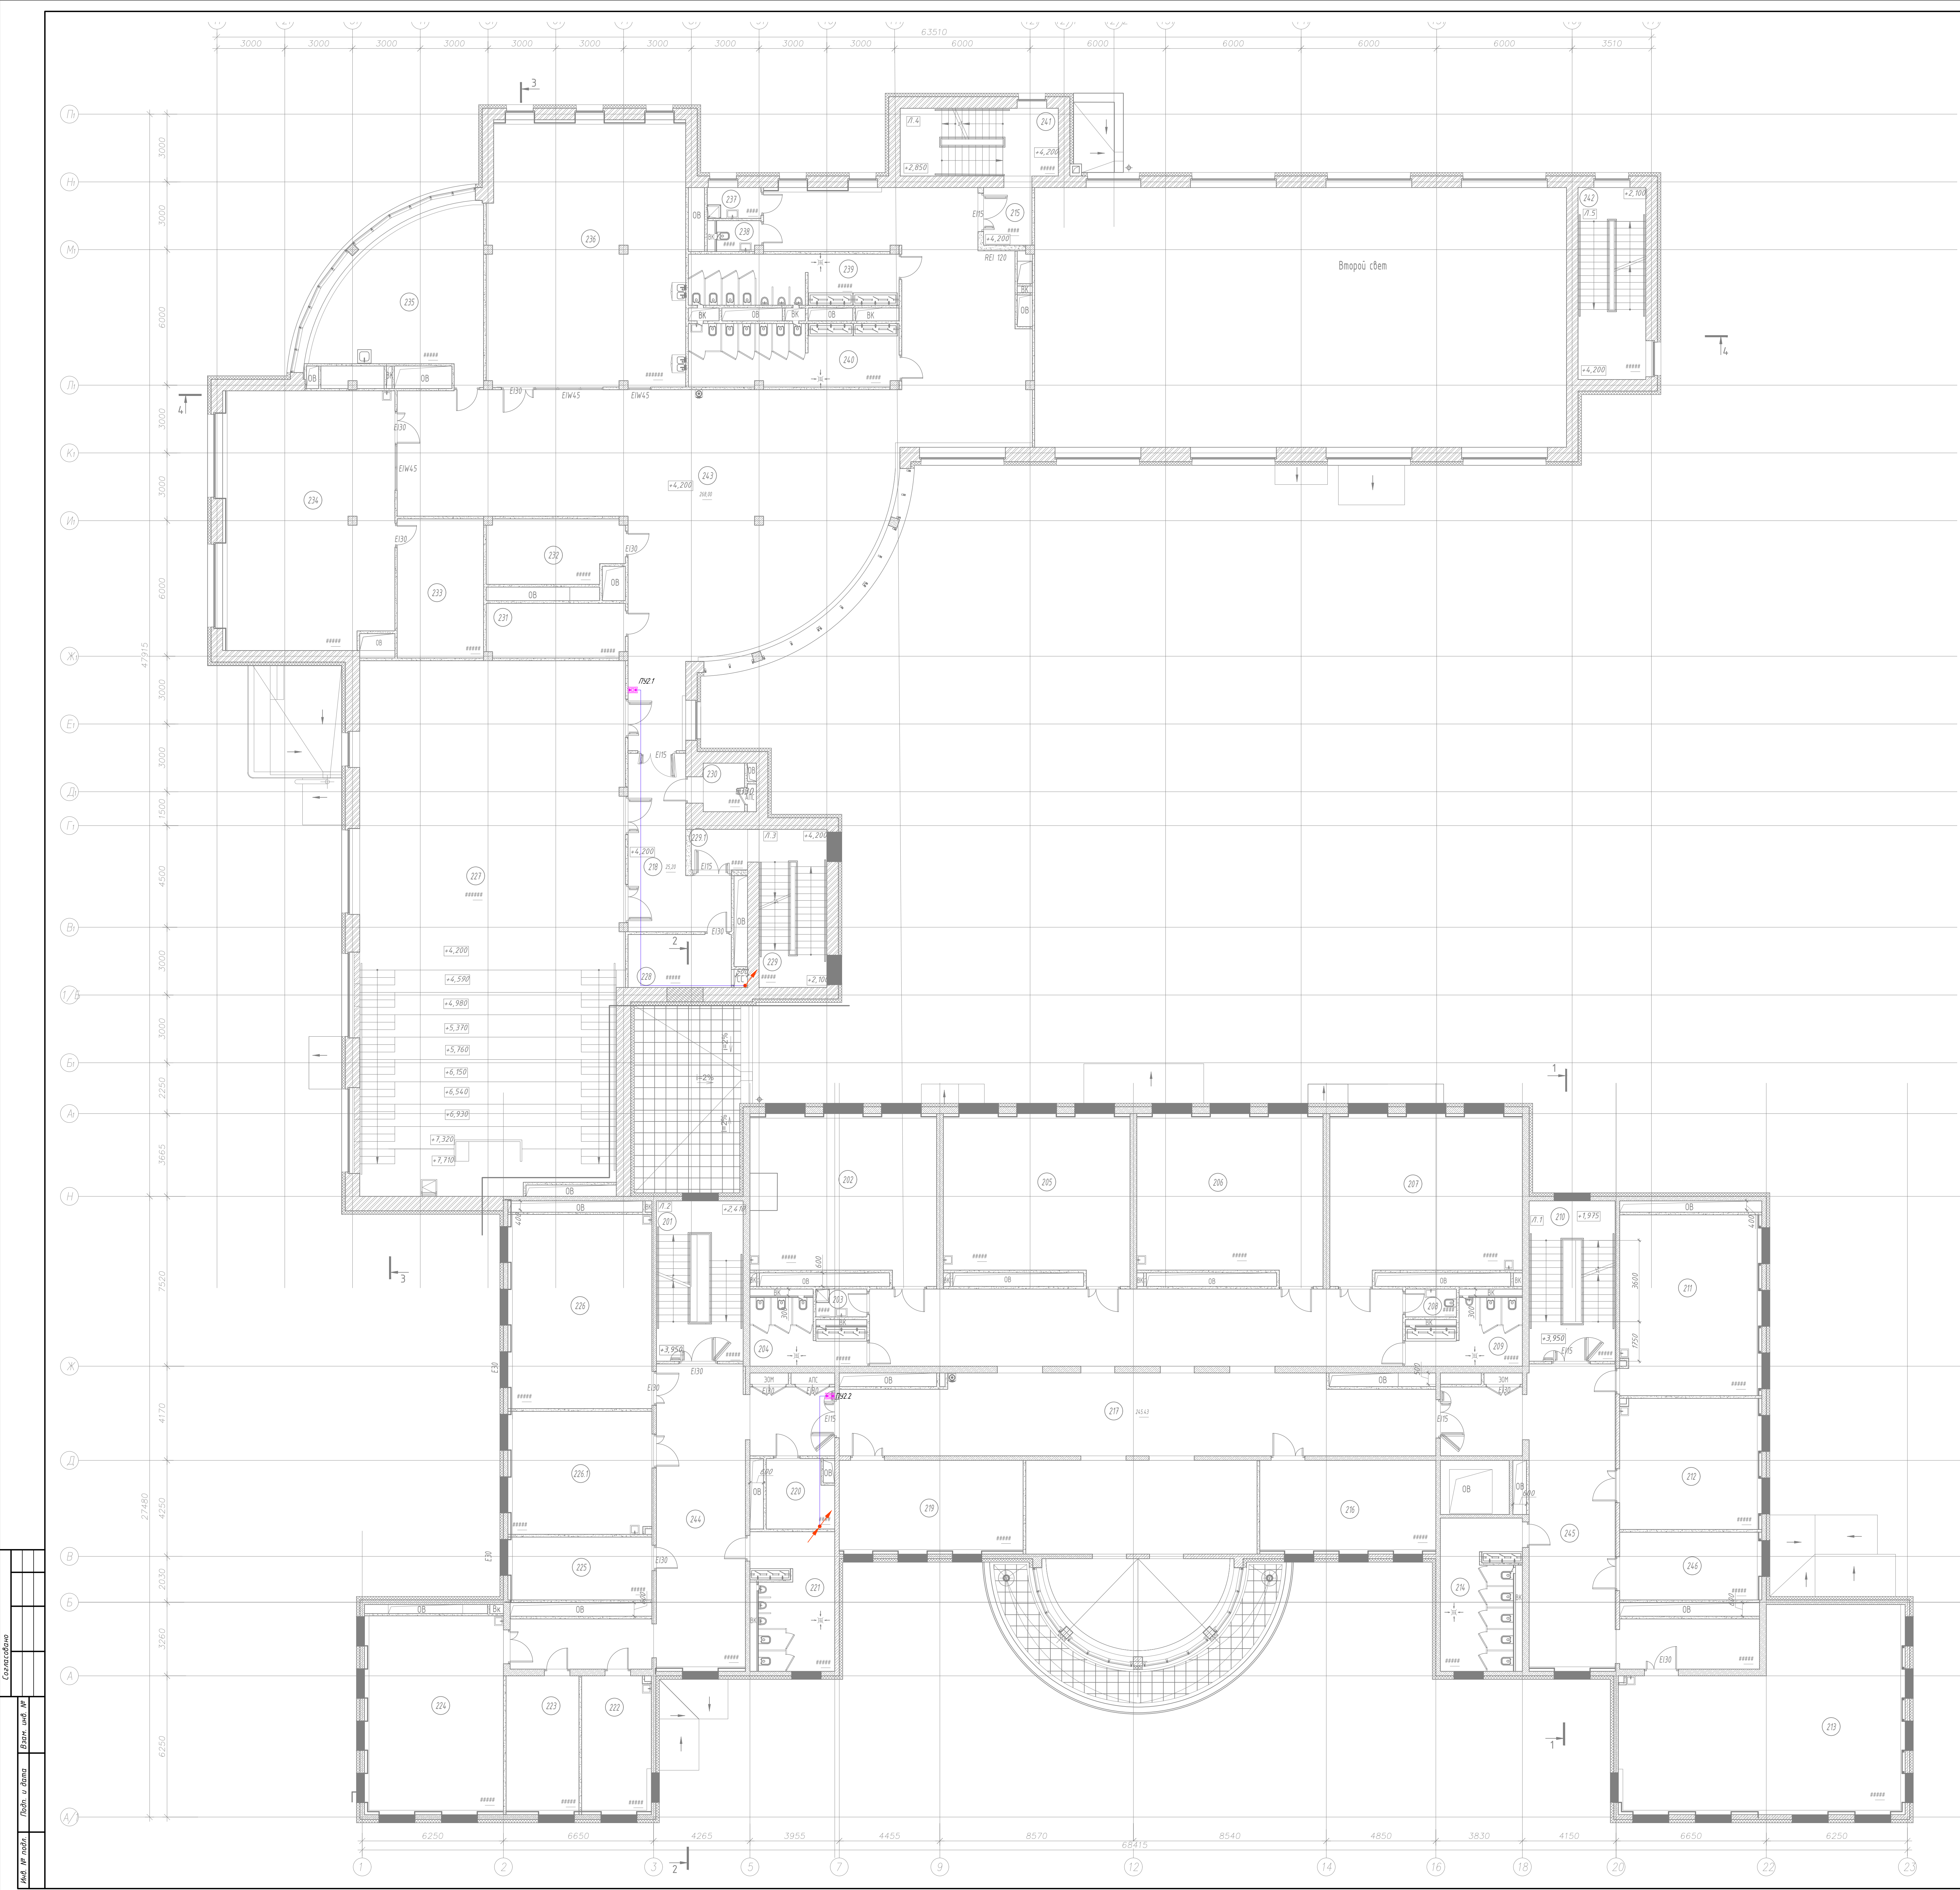


Экспликация помещений 2-го этажа

Номер помещения	Наименование	Площадь м2	Кат. помещен
201	Лестничная клетка Тип М2	28,82	
202	Учебные кабинеты (начальная школа)	58,70	
203	ПУИ	2,78	В4
204	Санузел для девочек (начальная школа)	12,73	
205	Учебные кабинеты (начальная школа)	58,68	
206	Учебные кабинеты (начальная школа)	58,54	
207	Учебные кабинеты (начальная школа)	60,45	
208	Санузел для персонала	2,79	
209	Санузел для мальчиков (начальная школа)	12,44	
210	Лестничная клетка (Л1)	27,05	
211	Учебные кабинеты (начальная школа)	50,17	
212	Кабинет иностранного языка (начальная школа)	36,51	
213	Лабораторно-исследовательский комплекс для изучения естествознания тип 1	97,02	В3
214	Санузел для девочек (начальная школа)	23,25	
215	Танбур	5,46	
216	Кабинет для индивидуальных занятий с малой группой	32,35	
217	Коридор с рекреацией (начальная школа)	245,43	
218	Коридор	25,20	
219	Кабинет для индивидуальных занятий с малой группой	33,78	
220	Помещение связи	8,75	В4
221	Санузел для мальчиков (начальная школа)	21,45	
222	Кабинет для индивидуальных занятий, в т.ч. с учителями-логопедами	18,97	
223	Кабинет для индивидуальных занятий, в т.ч. с коррекционным педагогом	19,22	
224	Учебные кабинеты (начальная школа)	54,17	
225	Кладовая инвентаря творческой мастерской	17,75	В3
226	Творческая мастерская	54,82	В3
226.1	Кабинет иностранного языка (начальная школа)	34,58	
227	Многофункциональное пространство с функцией актового зала (с эстрадой в уровне пола)	272,39	
228	Кроссовая	10,12	В3
229	Лестничная клетка (Л1)	21,00	
229.1	Танбур	4,48	
230	Тех. помещение	3,93	В4
231	Артистическая	14,75	
232	Кладовая инвентаря	16,65	В3
233	Кладовая кабинета материальной технологии	23,55	В3
234	Кабинет материальной технологии тип 2	86,25	В3
235	Кабинет с рабочим пространством для учителей тип 1 (начальная школа)	44,43	
236	Кабинет материальной технологии тип 1	102,78	В3
237	ПУИ	3,24	В4
238	Санузел для персонала	2,56	
239	Санузел для мальчиков (основная и старшая школа)	20,92	
240	Санузел для девочек с комнатой личной гигиены (основная и старшая школа)	25,84	
241	Лестничная клетка (Л1)	21,00	
242	Лестничная клетка (Л1)	25,50	
243	Коридор и рекреация (основная и старшая школа)	268,00	
244	Коридор	78,72	
245	Коридор	77,66	
246	Административный кабинет	18,87	
	Всего	2245,1	

Примечания:


1. Места размещения оборудования системы двусторонней связи показаны условно. Точное местоположение оборудования определить при монтаже с учетом архитектурных решений, расстояний, оборудования, фактических проемов, зон доступности МТМ и удобства эксплуатации.
2. Громкоговорящие переговорные устройства ГС-200Р4 и ГС-200М3 устанавливать в местах выхода помощи соседних графических частей проекта.
3. Трубки и оборудование выполнять герметично из негорючих материалов или в гофрированной трубе. Прокладку в кабель-канале выполнять только при отсутствии возможности скрытой прокладки, например по штукатурным, кирпичным или бетонным стенам, и при согласовании с Заказчиком.

				16-25/Г-П-МОС.10-ГЧ			
				Капитальный ремонт общеобразовательного учреждения (ГБОУ «Школа № 429»), расположенного по адресу: г. Москва, 5-ая ул. Соколиной Гory, д.14, 1 этаж			
Изм.	Вкл. в Лист	Монтаж	Лист	Дата	Страница	Лист	Листов
Разработчик	Составитель	Проверка	Получатель	05.26	05.26	05.26	05.26
Н. инициатор				Часть 10. Система двусторонней связи			
Ген. директор				План расположения оборудования и кабельных трасс на 2 этаже			
М. инициатор				Копировать			
				Формат А0			

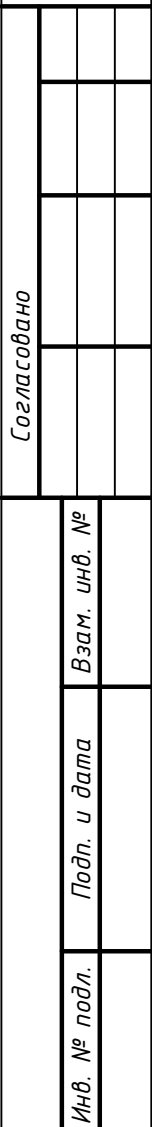

Номер помещения	Наименование	Площадь, м ²	Категория назначения
301	Лестничная клетка Тип Н2	28,82	
302	Кабинет русского языка и литературы	58,70	
303	Пси	2,78	В4
304	Санузлы для девочек (основная и старшая школа)	12,44	
305	Кабинет русского языка и литературы	58,68	
306	Кабинет математики	58,55	
307	Кабинет математики	60,45	
308	Санузлы для персонала	2,75	
309	Санузлы для мальчиков (основная и старшая школа)	12,44	
310	Лестничная клетка (Л1)	27,00	
311	Кабинет географии	55,07	
312	Универсальный учебный кабинет	56,05	
313	Кабинет для индивидуальных занятий, в т.ч. с педагогом-психологом	16,16	
314	Учебный кабинет для изучения естественной физики	61,36	
315	Лабораторная кабинета физики	18,02	В3
316	Санузлы для девочек с контингентом легкой степени (основная и старшая школа)	13,25	
317	подсобное помещение	6,64	В4
318	Кабинет иностранного языка (основная и старшая школа)	32,36	
320	Коридор с рекреацией	244,13	
321	Кабинет иностранного языка (основная и старшая школа)	33,78	
322	Помещение связи	8,75	В4
323	Санузлы для мальчиков (основная и старшая школа)	21,73	
324	Лабораторная кабинета биологии	15,93	В3
325	Учебный кабинет для изучения естественной: биология + ОБЗР	77,07	
326	Универсальный учебный кабинет	53,78	
327	Кабинет истории тип 1	54,86	
328	Кроссова	10,72	В3
329	Лестничная клетка (Л1)	21,00	
329.1	Тандыр	4,48	
330	Тех. помещение	3,93	
331	Универсальное помещение с возможностью организации гимнастического зала (хореография)	125,19	
332	Раздевальная	14,45	
333	Раздевальная	17,63	
334	Мультифункциональный информационный библиотечный центр с зоной для индивидуальных занятий	152,15	
335	Мультифункциональный информационный библиотечный центр (хранение (эксперим. фонд) и выдачи книги)	41,15	В3
336	Пси	4,44	В4
337	Санузлы для мальчиков (основная и старшая школа)	8,84	
338	Санузлы для девочек (основная и старшая школа)	10,97	
339	Санузлы для персонала	5,40	
340	Лестничная клетка (Л1)	21,00	
340.1	Тандыр	2,00	
341	Кабинет с рабочим пространством для учителей Тип 1 (основная и старшая школа)	71,92	
342	Универсальное помещение с возможностью организации Медицентра	39,84	В3
343	Помещение туалета	43,49	
344	Лестничная клетка (Л1)	25,50	
345	Коридор с рекреация (основная и старшая школа)	195,20	
346	Коридор с рекреация (основная и старшая школа)	169,67	
347	Коридор	78,72	
348	Коридор	77,66	
	Всего	2210,1	

						10-25/Г.-П.ИОС.5-10-ГЧ						
							Капитальный ремонт общеобразовательного учреждения (ГБОУ «Школа № 429»), расположенного по адресу: с. Москва, 5-ая ул. Соколовой Гари д.14 1этап					
Изм.	Кач.ч	Листы	№док	Подп.	Дата			Стадия	Лист	Листов		
Разобр.		Сошкин		Ю.	05.26							
Проверить		Половин		Ю.	05.26							
							Часть 10. Система двусторонней связи					
							П		5			
Н. контро.		Морозов		Ю.		План расположения оборудования и кабельных трасс на 3 этаже						
Генд.		Морозов		Ю.	05.26							

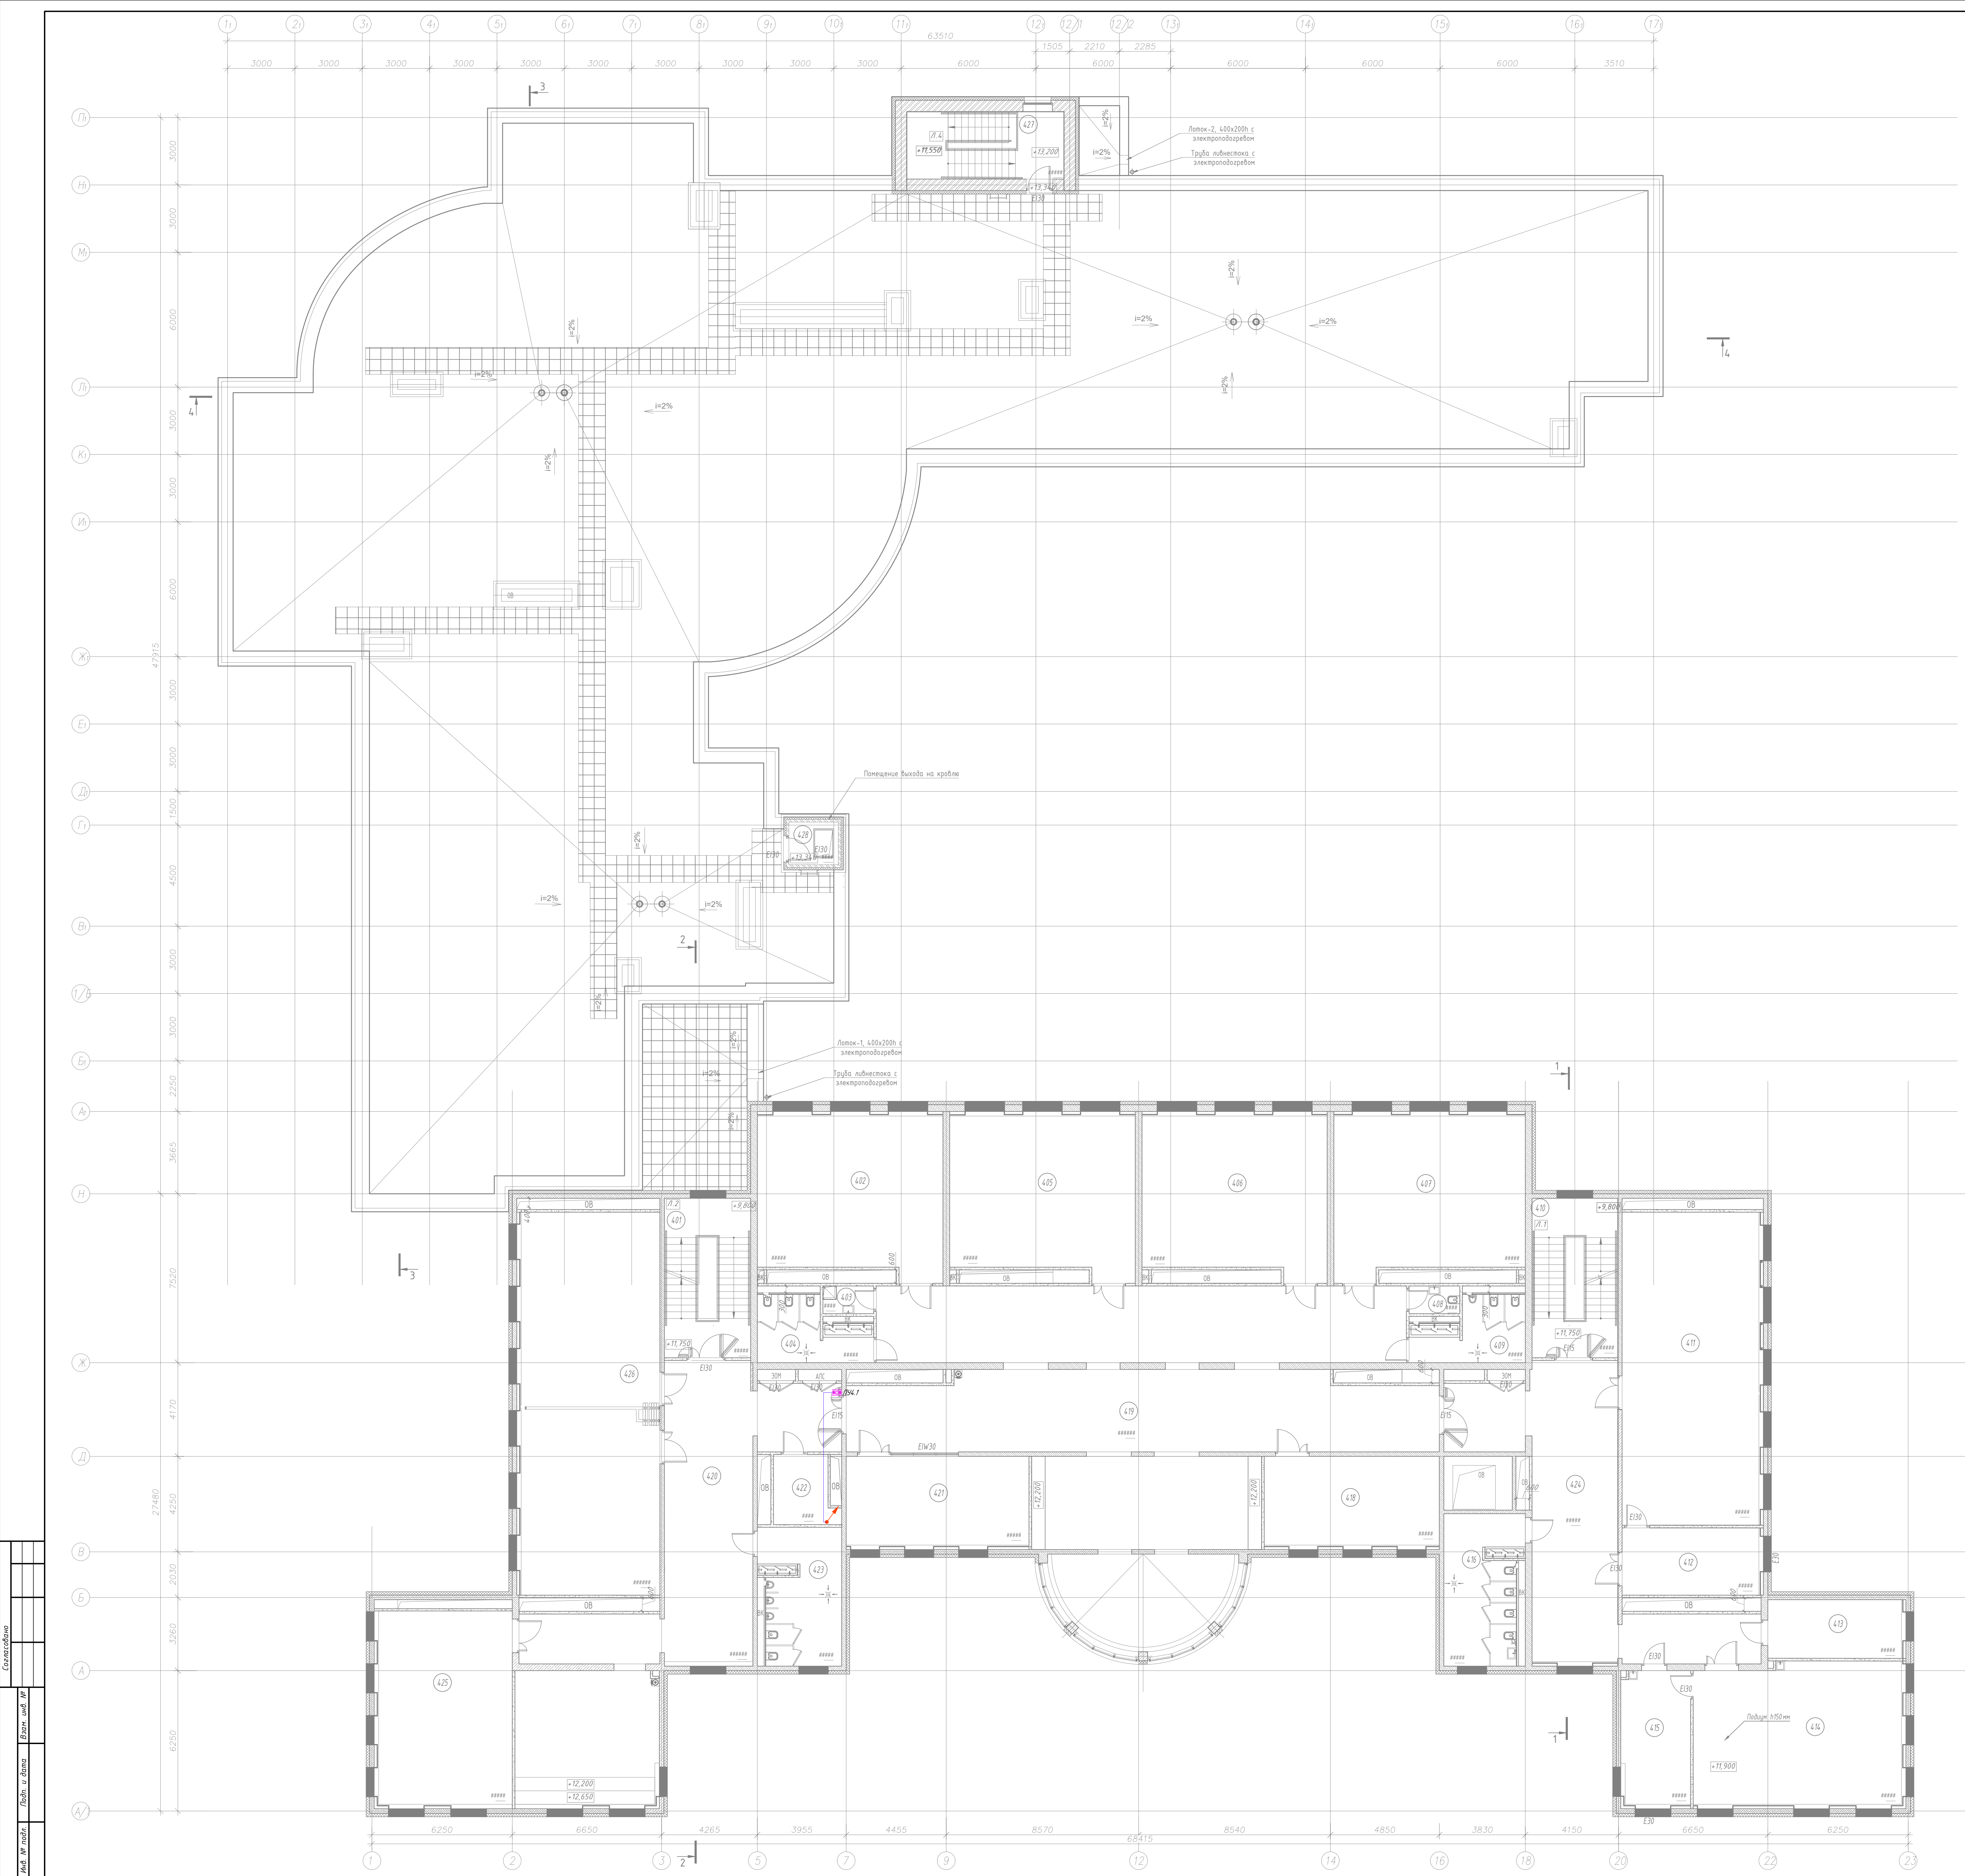

Экспликация помещений 4-го этажа

Номер помещения	Наименование	Площадь, м ²	Кат. помещения
401	Лестничная клетка Тип Н2	28.81	
402	Кабинет русского языка и литературы	58.70	
403	ПУИ	2.78	В4
404	Санузел для девочек (основная и старшая школа)	12.49	
405	Кабинет русского языка и литературы	58.68	
406	Кабинет математики	58.54	
407	Кабинет математики	60.45	
408	Санузел для персонала	2.78	
409	Санузел для мальчиков (основная и старшая школа)	12.49	
410	Лестничная клетка (Л1)	26.98	
411	Кабинет информационных технологий	87.66	
412	Лаборантская при кабинете информационных технологий	18.84	В3
413	Административный кабинет тип 1 (основная и старшая школа)	16.03	
414	Учебные кабинеты для изучения естественных наук: химия	60.75	
415	Лаборантская кабинета химии	18.96	В3
416	Санузел для девочек с комнатой личной гигиены (основная и старшая школа)	22.56	
417	Подсобное помещение	7.30	В4
418	Кабинет иностранного языка (основная и старшая школа)	32.36	
419	Коридор с рекреацией	245.54	
420	Коридор с рекреацией	118.69	
421	Кабинет иностранного языка (основная и старшая школа)	34.07	
422	Помещение (б/у)	8.02	В4
423	Санузел для мальчиков (основная и старшая школа)	21.45	
424	Коридор	77.66	
425	Кабинет истории Тип 1	54.17	
426	Кабинет информатики с возможностью деления трансформируемой перегородкой на два помещения	108.69	
427	Лестничная клетка (Л1)	21.00	
428	Помещение выхода на крышу	4.18	
	Всего	1216.5	

Примечания:

- 1 Место размещения оборудования системы двусторонней связи показано условно. Точное местоположение оборудования определить при монтаже с учетом архитектурных решений, расположения оборудования, открытия арочных, тон доступа МЭИ и удобства эксплуатации.
- 2 Громкоговорящие переговорные устройства ГС-200Р4 и ГС-200И4 устанавливать в местах выхода помещений согласно графической части проекта.
- 3 Опуски к оборудованию выполнять скрыто по отделочным материалам или в завершенной трубе. Прокладку в кабель-канале выполнять только при отсутствии возможности скрытой прокладки, например по штукатурным, кирпичным или бетонным стенам, и при согласовании с Заказчиком.

				16-25/Г-П-ИОС.10-ГЧ			
				Капитальный ремонт общеобразовательного учреждения (ГБОУ «Школа № 429»), расположенного по адресу: г. Москва, 5-ая ул. Соколиной Горы д.14 1 этаж			
Мин. Кол. Лист	Мин. Лист	Лист	Дата	Страниц	Лист	Листов	
Разработчик	Составитель	25	05.26	п	6		
Проверил	Полковник	25	05.26				
Н. контр. Водовед				План расположения оборудования и кабельных трасс на 4 этаже			
ГМП				Маслова			
				Формат А0			

Согласовано:

Изм. Кол.уч. Лист № Подпись Дата Разработал Сошников Проверил Поляков Н.Контр. Воробьев ГИП Марков Взам. инв. № Подпись и дата Инв. № подл.	Позиция	Наименование и техническая характеристика	Тип, марка, обозначение документа, опросного листа	Код оборудования, изделия, материала	Завод-изготовитель	Единица измерения	Кол-во	Масса единицы, кг	Примечание	
		Оборудование								
		Источник бесперебойного питания 12В/5А	ББП-50 исп.1		СКБ Телси	шт.	1			
		Пульт селекторной связи на 24 абонента	GC-1036F4		СКБ Телси	шт.	1			
		Источник вторичного электропитания	ИВЭПР 24/2,5 RS-R3 2x17 БР		ООО "Рубеж"	шт.	1			
		Аккумулятор герметичный свинцово-кислотный 12В/17Ач	Delta DTM 1217 L		ООО "Рубеж"	шт.	2			
		Сигнальная лампа	GC-0611W4		СКБ Телси	шт.	2			
		Кнопка сброса	GC-0421W1		СКБ Телси	шт.	1			
		Переговорное устройство	GC-2001W3		СКБ Телси	шт.	10			
		Переговорное устройство	GC-2001P4		СКБ Телси	шт.	10			
		Проводная влагозащищенная кнопка со шнуром	GC-0423W1		СКБ Телси	шт.	1			
		Аккумулятор 12В,7А/ч			СКБ Телси	шт.	1			
		Стойка Штольц для крепления антивандальной кнопки вызова помощи, сталь			Тифлоцентр Вертикаль	шт.	1			
		Табличка тактильная с пиктограммой "SOS" красный фон, 150x150мм.	MP-010R1		СКБ Телси	шт.	1			
		Табличка тактильная с пиктограммой "SOS с трубкой" красный фон,150x150 мм	MP-010R2		СКБ Телси	шт.	19			
		Табличка тактильная с пиктограммой "Инвалид" синий фон 150x150 мм.	MP-010B1		СКБ Телси	шт.	1			
		Кабели								
		ОКЛ-труба гофрированная негорючая D20 ПВХ с зондом (легкая), кабель КПСнг(А)-FRLSLTx 1x2x0,5, мет. скобы, крепеж	ОКЛ СегментЛайн-ГФ		Сегмент-Энерго	м	1100			
		ОКЛ-труба гофрированная негорючая D20 ПВХ с зондом (легкая), кабель ВВГнг(А)- FRLSLTx 2x1,5, мет. скобы, крепеж	ОКЛ СегментЛайн-ГФ		Сегмент-Энерго	м	10			
		ОКЛ-труба гофрированная негорючая D20 ПВХ с зондом (легкая), кабель КПСнг(А)-FRLSLTx 1x2x1,0, мет. скобы, крепеж	ОКЛ СегментЛайн-ГФ		Сегмент-Энерго	м	10			
		Материалы								
		Труба жесткая оцинкованная ø32x1,2x3000 мм	6008-32L3		ДКС	шт	1			
		Огнезащитный терморасширяющийся герметик ОГНЕЗА-ГТ 3 кг	ОГНЕЗА-ГТ		ОГНЕЗА	шт	1			
	Изм. Кол.уч. Лист № Подпись Дата Разработал Сошников Проверил Поляков Н.Контр. Воробьев ГИП Марков 06.26 06.26 06.26 06.26 16-25/Г-П-ИОС5.10.СО Капитальный ремонт общеобразовательного учреждения (ГБОУ «Школа № 429»), расположенного по адресу: г. Москва, ул. Соколиной Горы, д.14, 1 этап Часть 10. Система двухсторонней связи Стадия Лист Листов П 1 1 Спецификация оборудования, изделий и материалов 									