


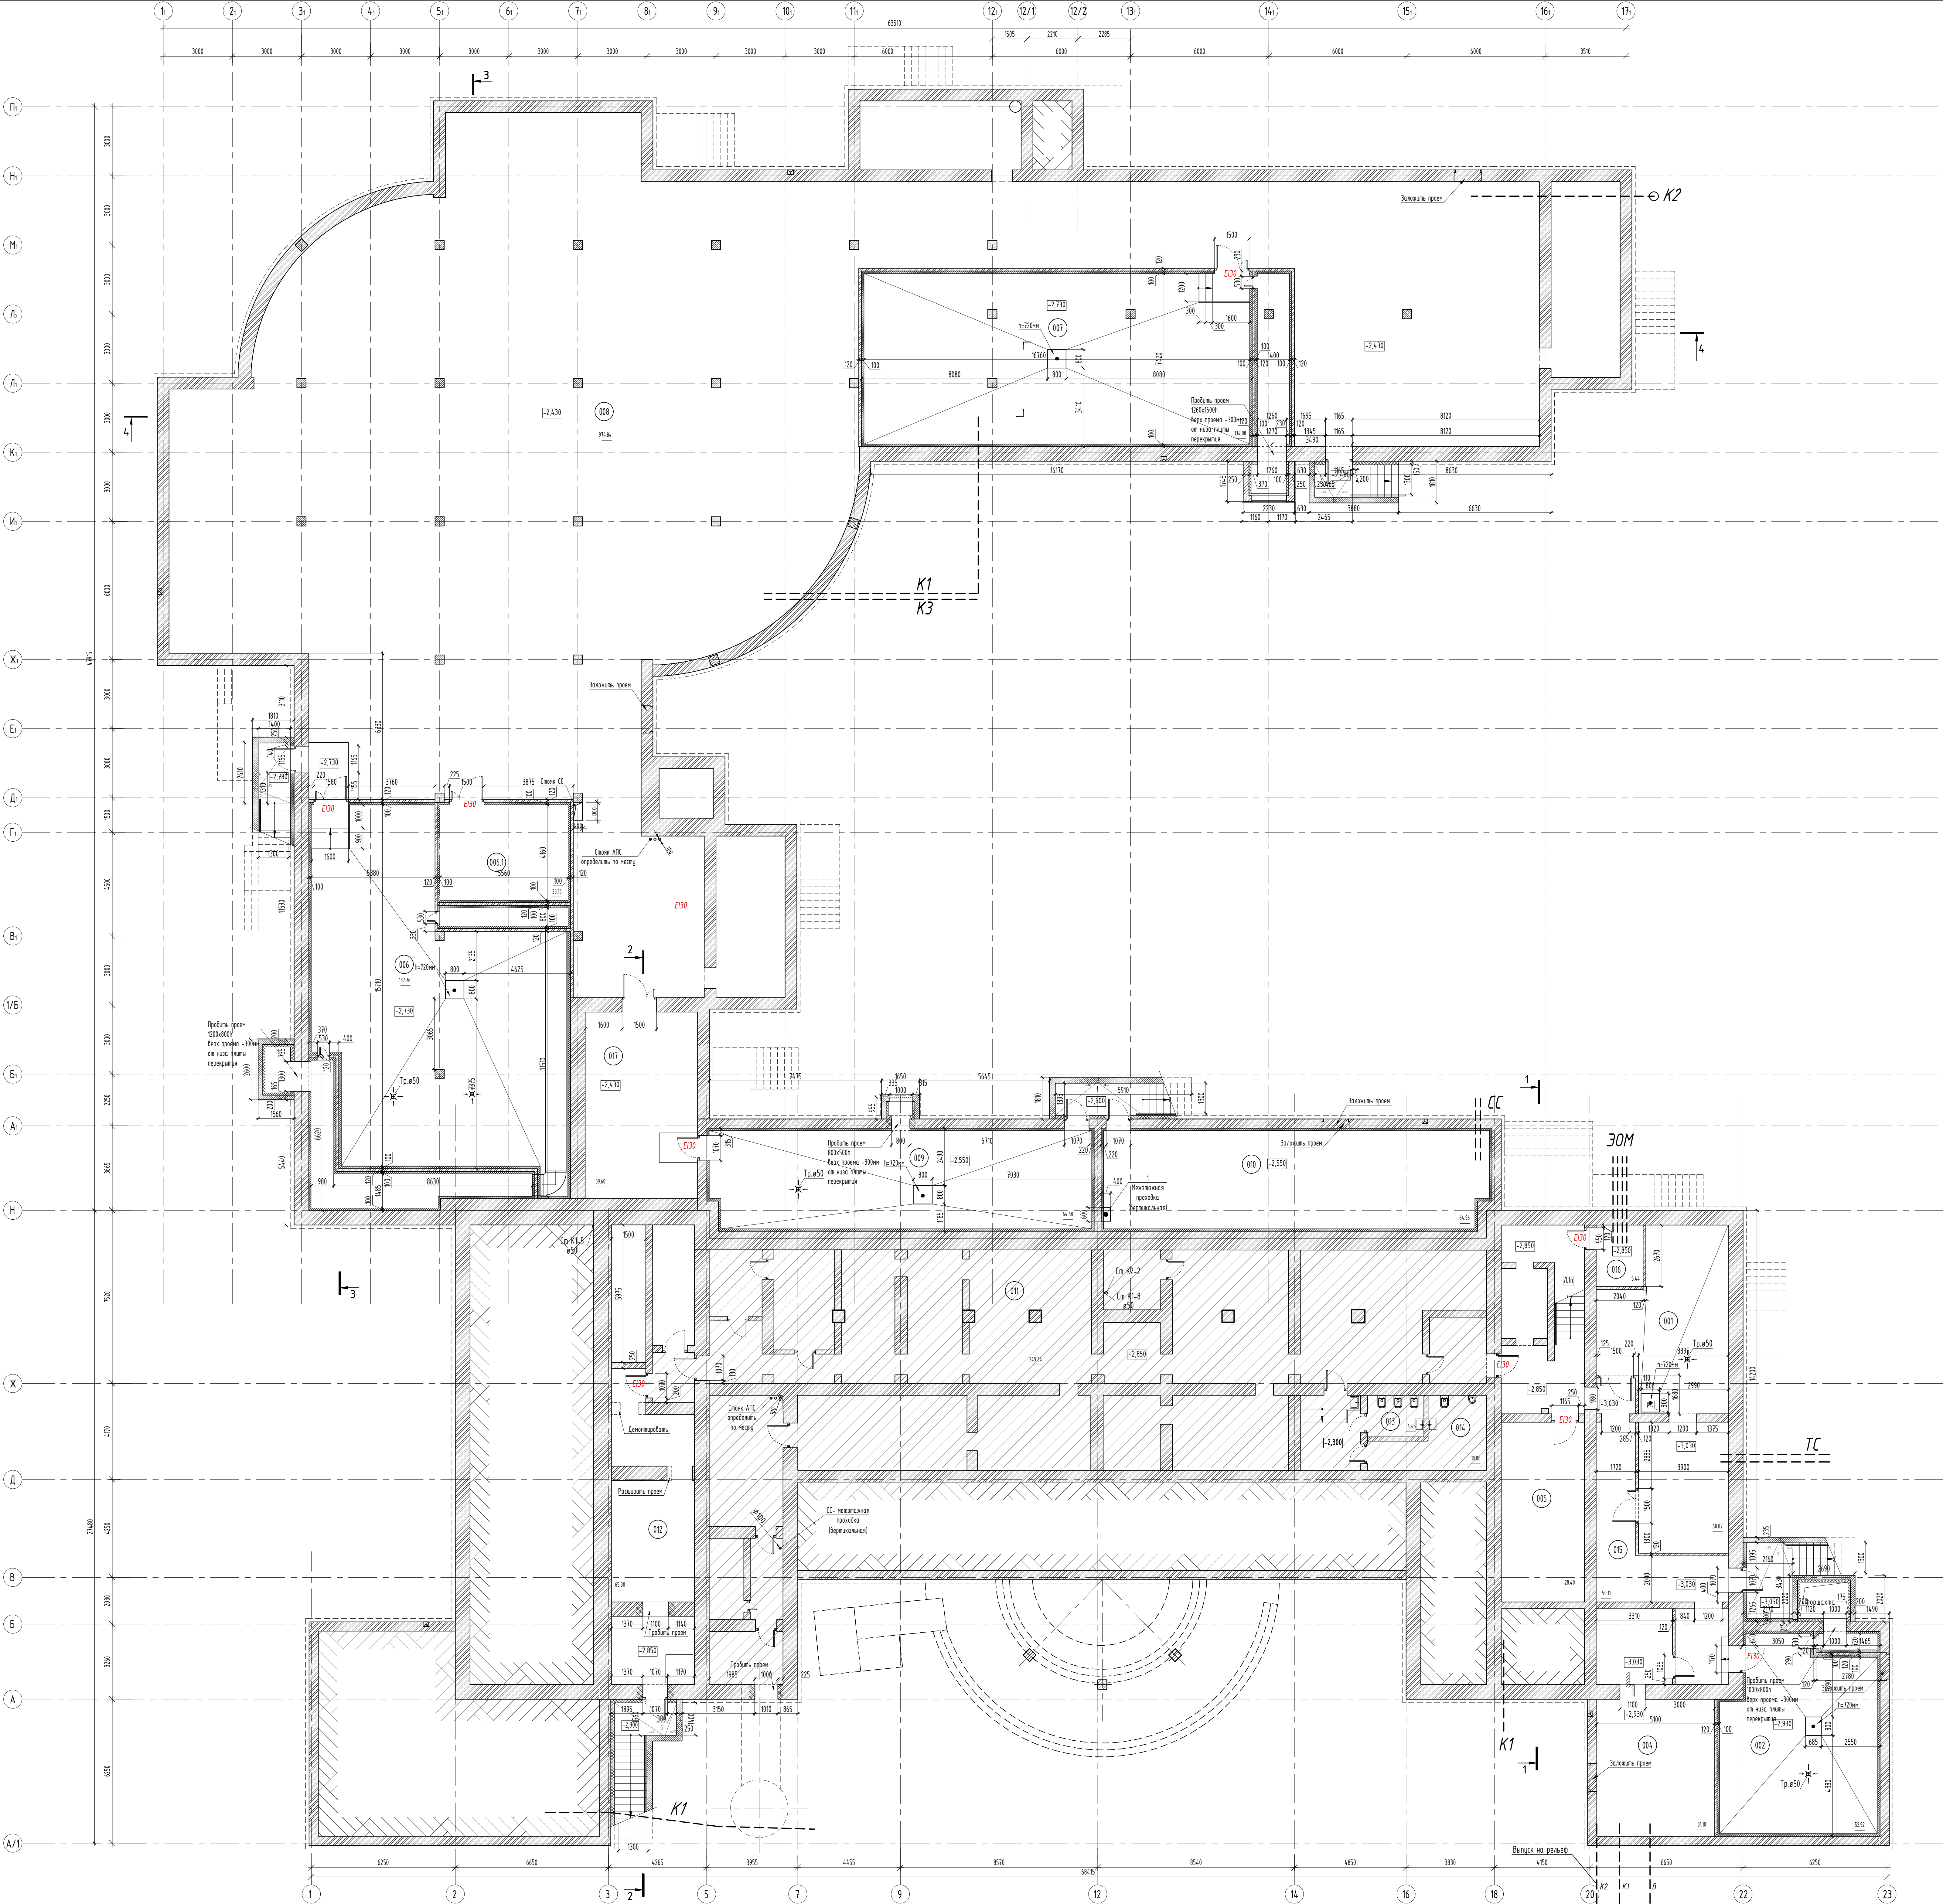


Экспликация помещений подвала

Номер помещения	Наименование	Площадь м2	Кот. помещ.
001	ИТП	60.07	Д
002	Вентилятор с формальдегидом	52.92	В3
004	Водомерный узел и насосная	41.24	Д
005	Техническое помещение	28.40	Д
006	Вентилятор	137.76	В3
006.1	Вентилятор систем приточной приточной вентиляции	23.13	Д
007	Вентилятор	138.94	В3
008	Техническое помещение для прокладки инженерных коммуникаций	974.84	В3
009	Вентилятор	64.68	В3
010	Техническое помещение	64.96	Д
011	Защитное помещение гражданской обороны	249.34	Д
012	Коридор	50.95	
013	Санузел женский	10.88	
014	Санузел мужской	4.45	
015	Коридор	50.11	
016	Узел ввода электрических сетей	5.44	В4
017	Коридор	39.60	
Всего		1997.7	

УСЛОВНЫЕ ОБОЗНАЧЕНИЯ

- Существующие стены из полнотелого керамического кирпича
- Замена существующих стен из полнотелого кирпича
- Замена существующих стен из полнотелого кирпича толщиной 100мм и 250 мм
- Номер помещения по экспликации
- Маркировка оконности замененных дверей
- Плитка полов
- Помещение ГО ЧС
- Пути эвакуации

- Возможность устройства проемов в несущих стенах будет уточняться в проекте. Размер и расположение вентиляционных шахт будет уточнен в проекте.
- Шахты предназначены для прокладки инженерных коммуникаций и стоек (ВК, СТ, ЗОМ), оборудуются лестницами для обслуживания.
- Ж - категорирование по взрывопожарной опасности данных помещений выполняется на этапе проектирования.
- Марки проемов см. альбом 16-25/Г-П-АР лист 61

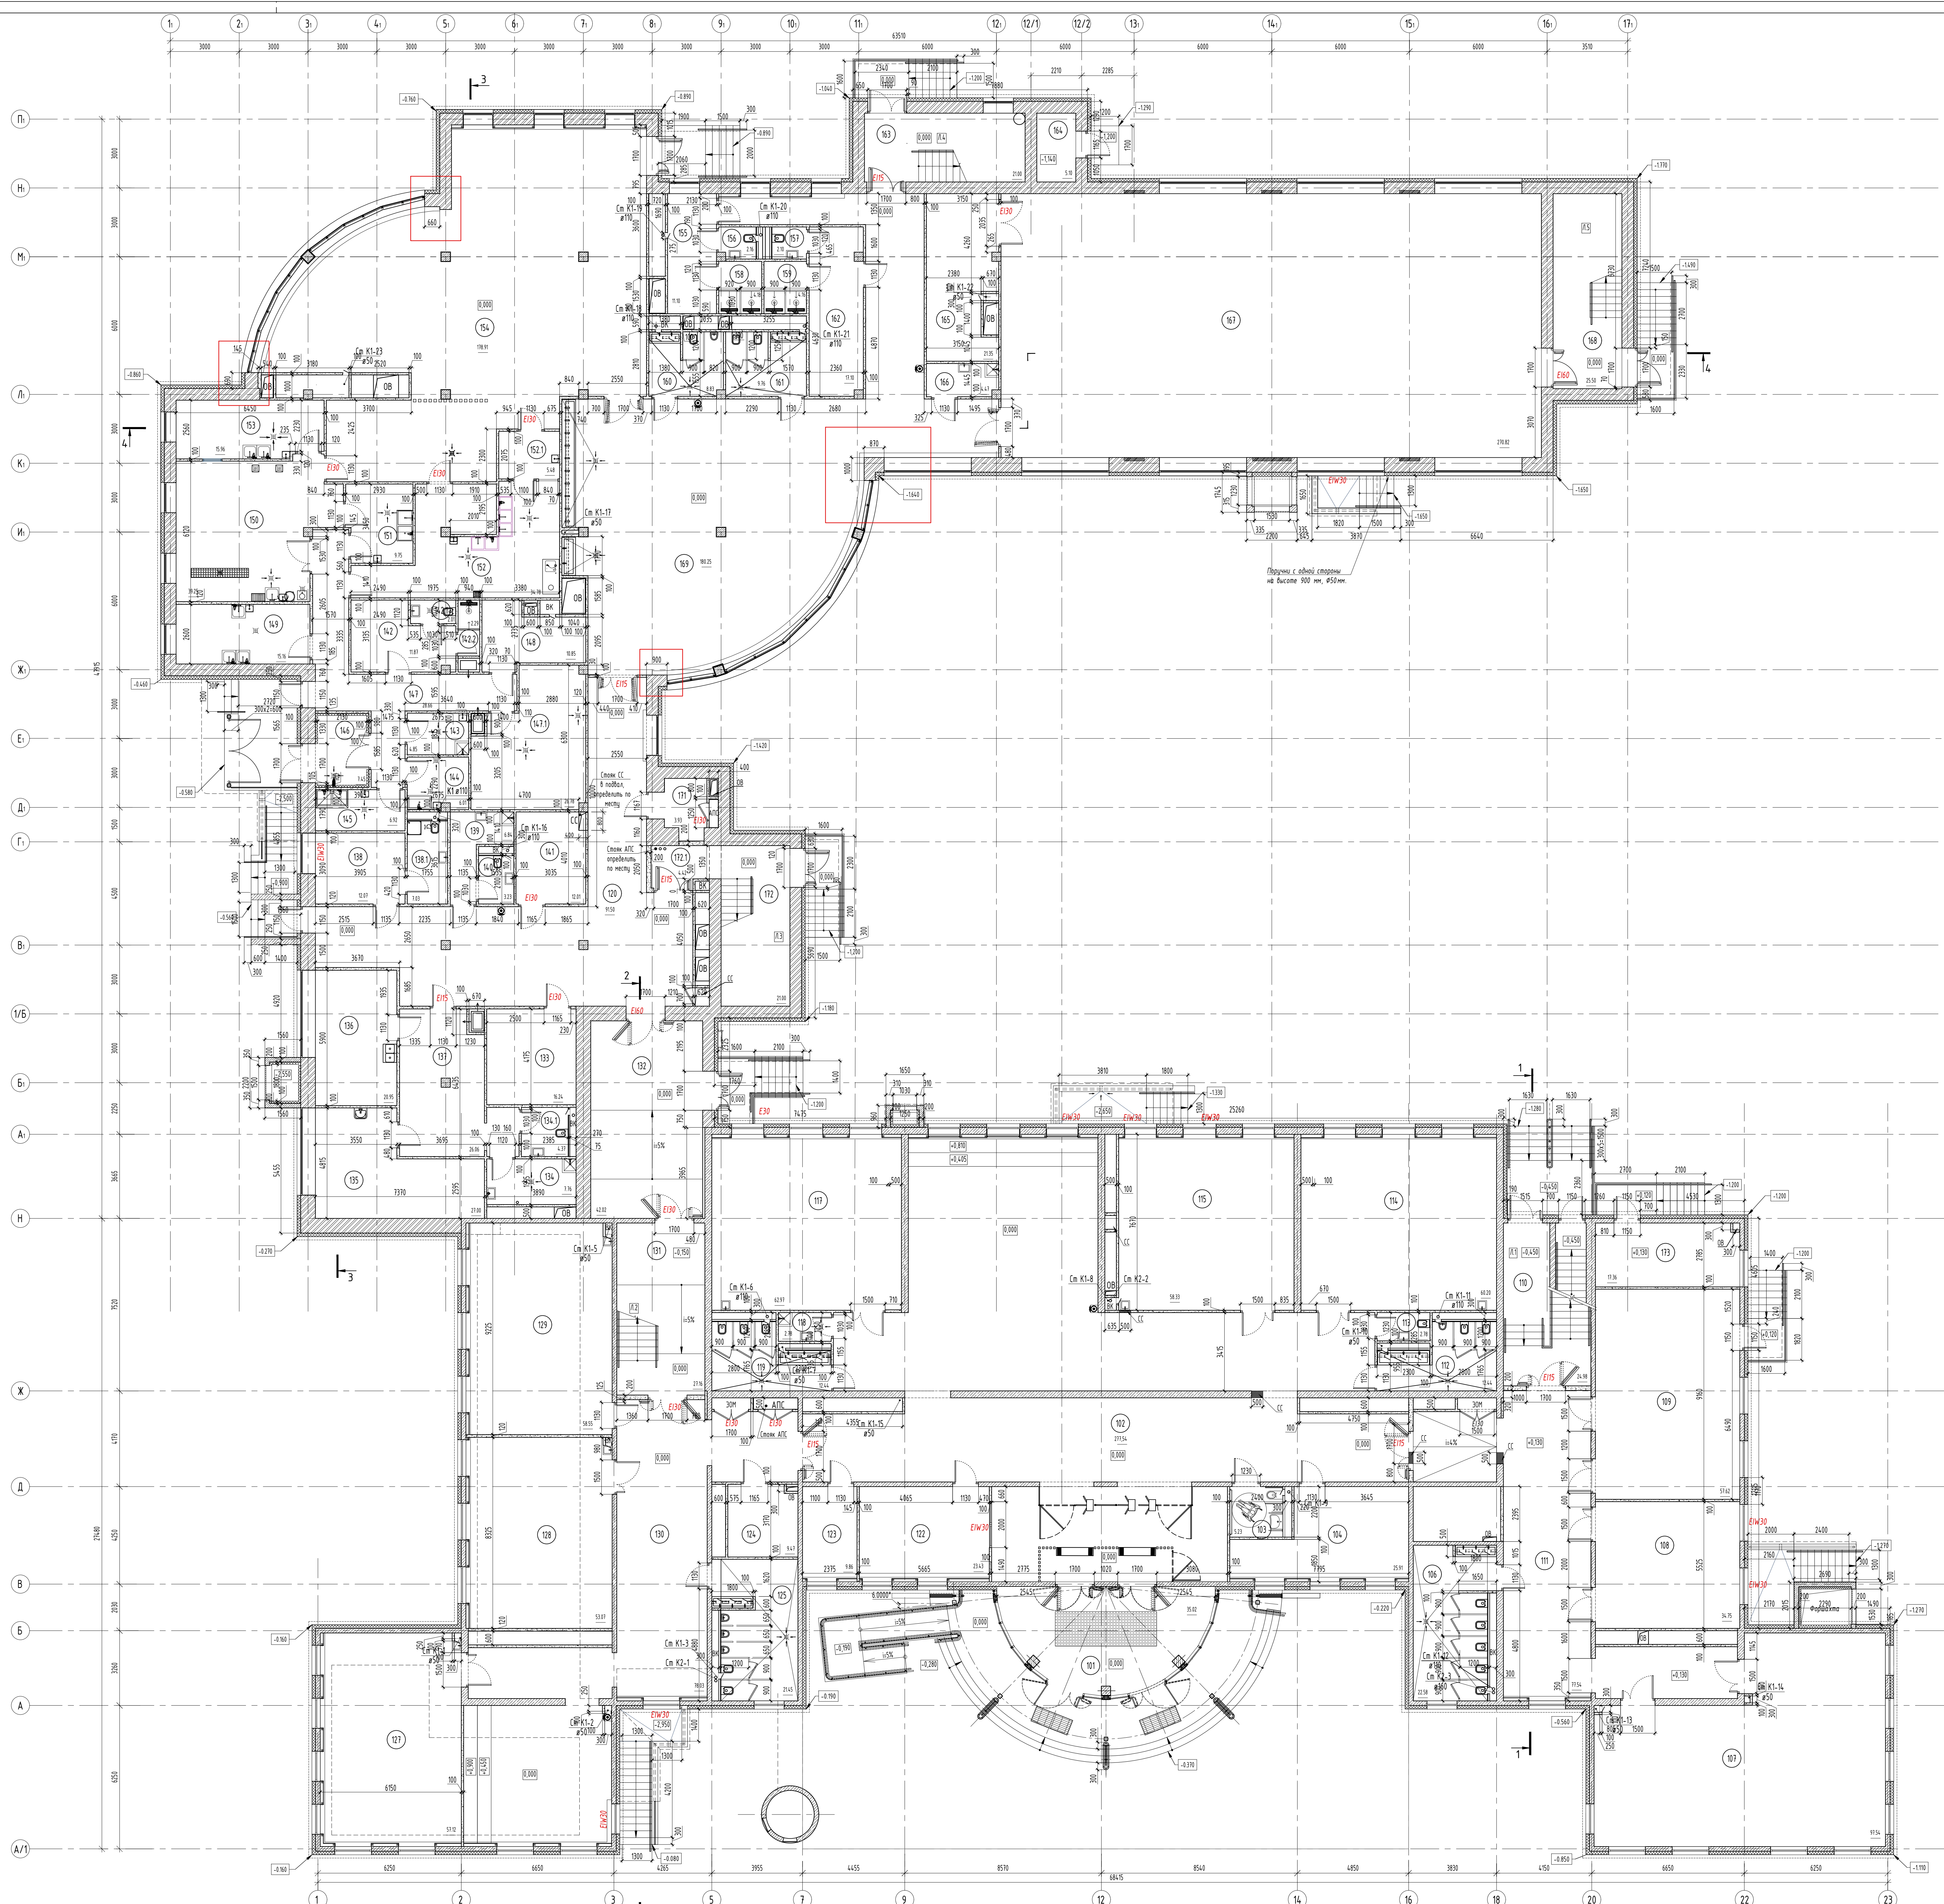


Код по-мещения	Наименование	Площадь м2	Кол-во помещений
101	Танцдр	35.02	
102	Коридор с рекреацией	277.54	
103	Санитар для МН	5.33	
104	Административный кабинет тип 1 (начальная школа)	25.91	
105	Санитар для девочек (начальная школа)	23.25	
107	Гардеробная для обучающихся (основная и старшая школа)	97.54	
108	Гардеробная для обучающихся (основная и старшая школа)	34.75	
109	Гардеробная для обучающихся (начальная школа)	57.62	
110	Лестничная клетка (ЛК)	24.50	
111	Коридор	17.54	
112	Санитар для мальчиков (начальная школа)	12.44	
113	Санитар для персонала	2.79	
114	Учебные кабинеты (начальная школа)	65.12	
115	Учебные кабинеты (начальная школа)	58.33	
117	Учебные кабинеты (начальная школа)	62.97	
118	ПСИ	9.47	84
119	Санитар для девочек (начальная школа)	12.44	
120	Коридор с рекреацией (основная и старшая школа)	91.50	
122	Компьютерная (с компьютерными пунктами)	23.43	
123	Гардеробная комната (для учителей)	9.86	
124	Помещение связи	9.47	84
125	Санитар для мальчиков (начальная школа)	21.73	
127	Учебные кабинеты (начальная школа)	57.26	
128	Учебные кабинеты (начальная школа)	53.71	
129	Учебные кабинеты (начальная школа)	58.81	
130	Коридор с рекреацией	117.57	
131	Лестничная клетка Тип И2	27.38	
132	Вестибюль	16.22	
133	Электрощитовая	42.94	
134	Имеется для предоставления дезинфекционных растворов и средств для обработки одежды, предназначенных для помещений медицинского назначения	7.76	84
134.1	Туалет男	4.31	
135	Кабинет физика	23.00	
136	Процедурный (пробирочный) кабинет	20.88	
137	Коридор	28.06	
138	Комната инструктора	12.87	
138.1	Санитар с душем	7.83	
139	ПСИ	6.79	84
140	Санитар для персонала	3.27	
141	Помещение связи	11.07	83
142	Помещение для персонала	12.61	
142.1	Санитар для персонала	2.01	
142.2	Душевая	2.29	
143	ПСИ	4.95	84
144	Помещение для временного хранения пищевых отходов	6.01	84
145	Кабинет с мясницкой оборотной тары	9.62	84
146	Защитный щит	7.45	84
147	Коридор	28.66	
147.1	Помещение с холодильным оборудованием	26.78	83
148	Кабинет сушки продуктов	10.85	83
149	Дезинфекционный щит	15.16	83
150	Горячий душ	39.25	83
151	Мясницкая для кухонной посуды	9.75	д
152	Мясницкая для столовой посуды	34.48	д
152.1	Предмечная	5.46	д
153	Холодный щит	15.98	83
154	Обеденный зал	118.91	
155	Раздевальня для мальчиков	17.50	
156	Санитар для мальчиков	2.16	
157	Санитар для девочек	2.30	
158	Душевые для мальчиков	4.15	
159	Душевые для девочек	4.76	
160	Санитар для мальчиков	8.71	
161	Санитар для девочек	9.76	
162	Раздевальня для девочек	21.00	
163	Лестничная клетка (ЛК)	17.00	
164	Техническое помещение	5.10	84
165	Сараи	21.35	83
166	ПСИ	4.47	84
167	Универсальный спортивный зал	270.82	
168	Лестничная клетка (ЛК)	25.50	
169	Коридор с рекреацией (основная и старшая школа)	281.24	
171	Тех. помещение	3.93	84
172	Лестничная клетка (ЛК)	21.00	
172.1	Танцдр	4.42	
173	Электрощитовая	17.36	83
Всего		2676.1	

- - Шлифовка мыльная ж/б стемы
- - Замачивание перекладины из газобетонных блоков
L/25x25x250/050/Б5 по ГОСТ Р 19512-2012, толщиной 100мм на клею с армированием базальтовым сеткой, опущенной
- - Замачивание перекладины из газобетонных блоков
L/25x25x250/050/Б5 по ГОСТ Р 19512-2012, толщиной 200мм на клею с армированием базальтовым сеткой, опущенной
- - Замачивание перекладины по технологии изготовления двутавровой балки толщиной 100мм
- - Замачивание перекладины из экоблоков односторонней двутавровой толщиной 100мм
- - Замачивание ослепленных перекладин
- - Замачивание перекладины симметричной (Нормоспектр) с обшивкой с необходимой фурнитурой
- - Темпер. понижения по эксплуатации
- - Отметка уровня пола этакса
- - Маркировка сантехнической арматуры дверей, окон, перегородок;

1. Возможность устройства проемов в несущих стенах будет уточняться в проекте.
2. Размер и расположение вентиляционных шахт будет уточнен в проекте.
3. Шахты предназначение для прокладки инженерных коммуникаций и стоек (ВК, СС, ЗОМ), оборудуются лючками для обслуживания.
4. ★ категорирование по взрывопожарной опасности данных помещений выполнить на этапе проектирования.
4. Марки ограждений смотреть альбом 16-ЗС/Г-П-АР лист 61

[illegible]

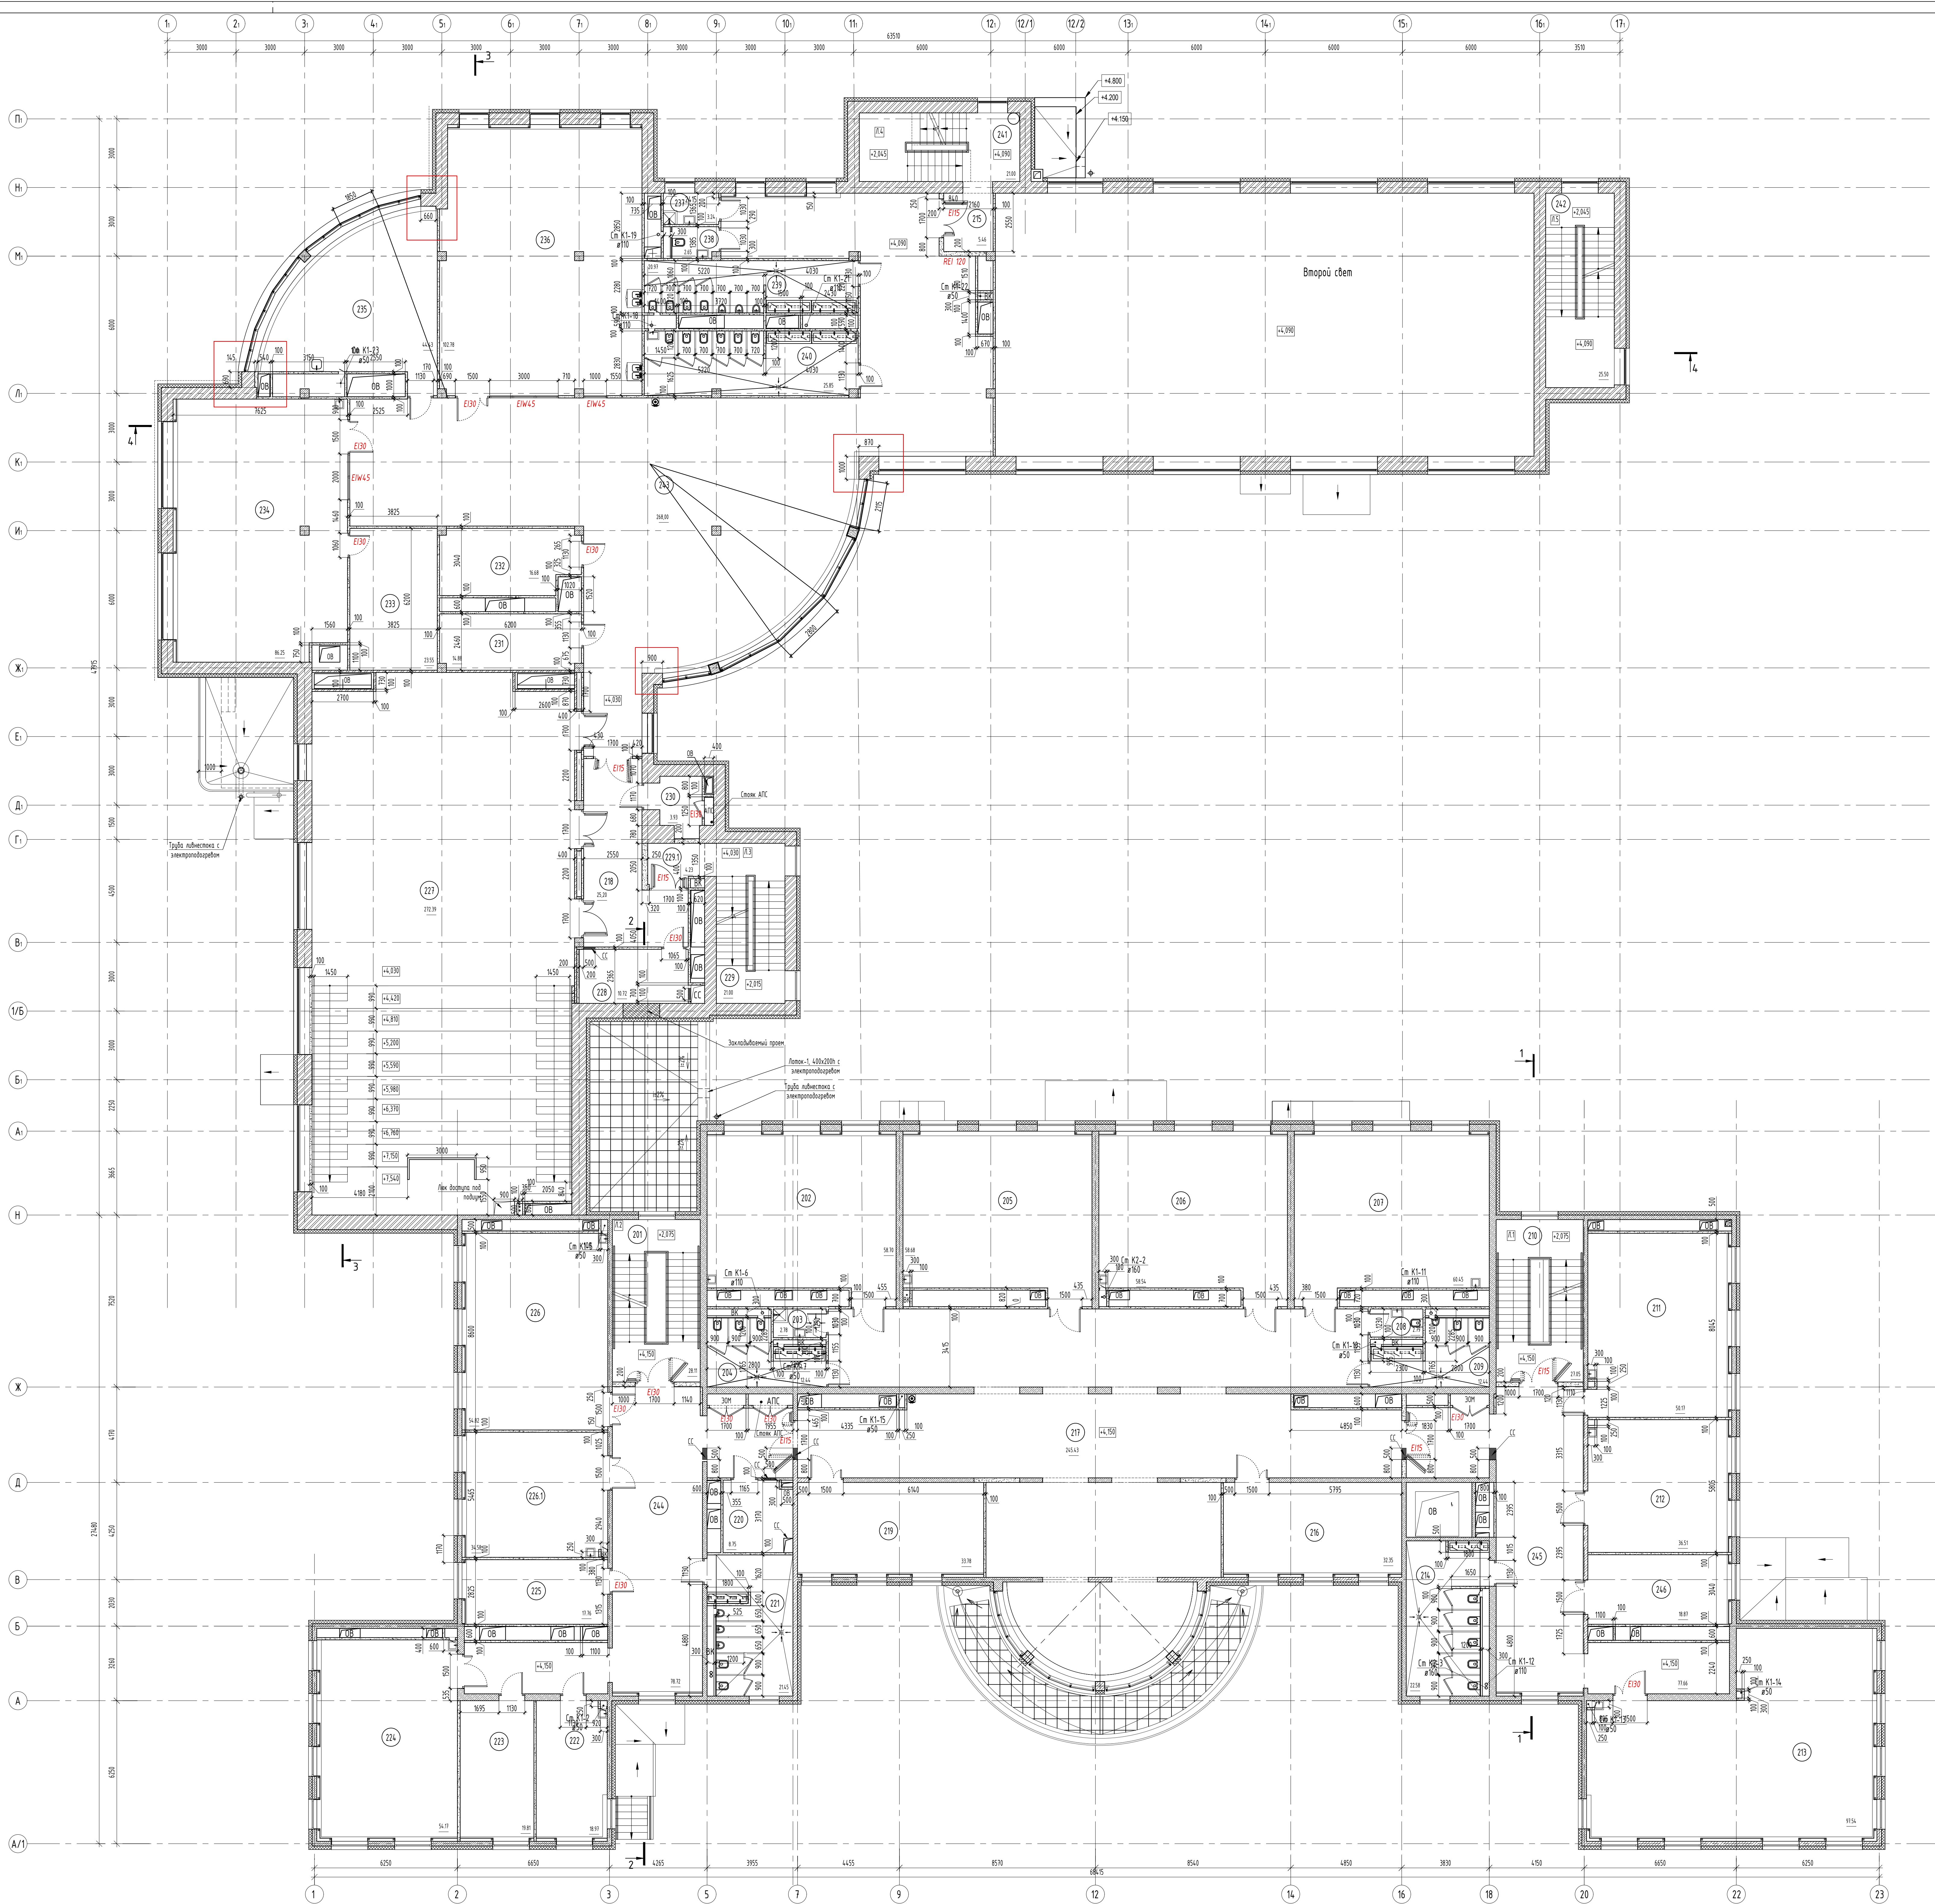

Экспликация помещений 2-го этажа


Номер помещения	Наименование	Площадь, м2	Кат. помещ.
201	Лестничная клетка Тип Н2	28,82	
202	Учебные кабинеты (начальная школа)	58,70	
203	ПНИ	2,78	В4
204	Санузел для девочек (начальная школа)	12,73	
205	Учебные кабинеты (начальная школа)	58,68	
206	Учебные кабинеты (начальная школа)	58,54	
207	Учебные кабинеты (начальная школа)	60,45	
208	Санузел для персонала	2,79	
209	Санузел для мальчиков (начальная школа)	12,44	
210	Лестничная клетка (ЛП)	27,05	
211	Учебные кабинеты (начальная школа)	50,17	
212	Кабинет иностранного языка (начальная школа)	36,51	
213	Лабораторно-исследовательский комплекс для изучения астрономии (п.п.)	97,02	В3
214	Санузел для девочек (начальная школа)	23,25	
215	Танцев	5,46	
216	Кабинет для индивидуальных занятий с малой группой	32,35	
217	Коридор с рекреацией (начальная школа)	245,43	
218	Коридор	25,20	
219	Кабинет для индивидуальных занятий с малой группой	33,78	
220	Помещение связи	8,75	В4
221	Санузел для мальчиков (начальная школа)	21,45	
222	Кабинет для индивидуальных занятий, в т.ч. с коррекционным педагогом	18,97	
223	Кабинет для индивидуальных занятий, в т.ч. с коррекционным педагогом	19,22	
224	Учебные кабинеты (начальная школа)	54,17	
225	Классовая инвентарь творческой мастерской	11,75	В3
226	Творческая мастерская	54,82	В3
226.1	Кабинет иностранного языка (начальная школа)	34,58	
227	Многофункциональное пространство с функцией актового зала (с эстрадой в уровне пола)	272,39	
228	Классовая	10,72	В3
229	Лестничная клетка (ЛП)	21,00	
229.1	Танцев	4,23	
230	Тех. помещение	3,93	В4
231	Архитектурная	14,75	
232	Классовая инвентарь	16,65	В3
233	Классовая инвентарь материальной технологии	23,55	В3
234	Кабинет материальной технологии тип 2	86,25	В3
235	Кабинет с рабочим пространством для учителей тип 1 (начальная школа)	44,43	
236	Кабинет материальной технологии тип 1	102,78	В3
237	ПНИ	3,24	В4
238	Санузел для персонала	2,65	
239	Санузел для мальчиков (основная и старшая школа)	20,97	
240	Санузел для девочек с комнатой личной гигиены (основная и старшая школа)	25,85	
241	Лестничная клетка (ЛП)	21,00	
242	Лестничная клетка (ЛП)	25,50	
243	Коридор и рекреация (основная и старшая школа)	268,00	
244	Коридор	78,72	
245	Коридор	77,66	
246	Административный кабинет	18,87	
Всего		2245,0	

УСЛОВНЫЕ ОБОЗНАЧЕНИЯ

- Существующие монолитные и/б стены
- Заменяемые перегородки из газобетонных блоков 1/4x25x250/100/500/85,0 по ГОСТ Р 76522-2022, толщиной 100мм на клею с армированием базальтовой сеткой, опущенными
- Заменяемые перегородки из газобетонных блоков 1/4x25x250/100/500/85,0 по ГОСТ Р 76522-2022, толщиной 200мм на клею с армированием базальтовой сеткой, опущенными
- Заменяемые перегородки из акрилового одностроннего двустороннего дощ. раковины толщиной 100мм
- Заменяемые перегородки из акрилового одностроннего двустороннего дощ. раковины толщиной 100мм
- Заменяемые перегородки
- Заменяемые перегородки синтетическая (пластиковая) с дверью и необходимой фурнитурой
- Номер помещения по экспликации
- Отметка уровня пола этажа
- Маркировка оконных проемов, дверей, окон, перегородок

- Возможность устройства проемов в несущих стенах будет уточняться в проекте. Размер и расположение вентиляционных шахт будет уточнен в проекте.
- Шахты предназначены для прокладки инженерных коммуникаций и стояков (ВК, СТ, ЭОМ), оборудуются лестницами для обслуживания.
- Жиромаркировка по взрывопожарной опасности данных помещений выполняется на этапе проектирования.
- Марки горизонтальной сети 16-25/Г-П-АР лист 61

16-25/Г-П-АР				
Капитальный ремонт объекта "ГБОУ Школа № 429 "Соколовая гора", расположенного по адресу: г. Москва, ул. Соколовой горы 5-я, д. 14				
Им. Разраб.	Лист	№ д.н.	Подпись	Дата
Архитектура-планировочные решения	Стандарт	Лист	Листов	
И. комп.	Губарева	И. комп.	Губарева	
Гипс	Маркова	Гипс	Маркова	
Лист 2 из 3. М1:100				
АЗУРИТ				

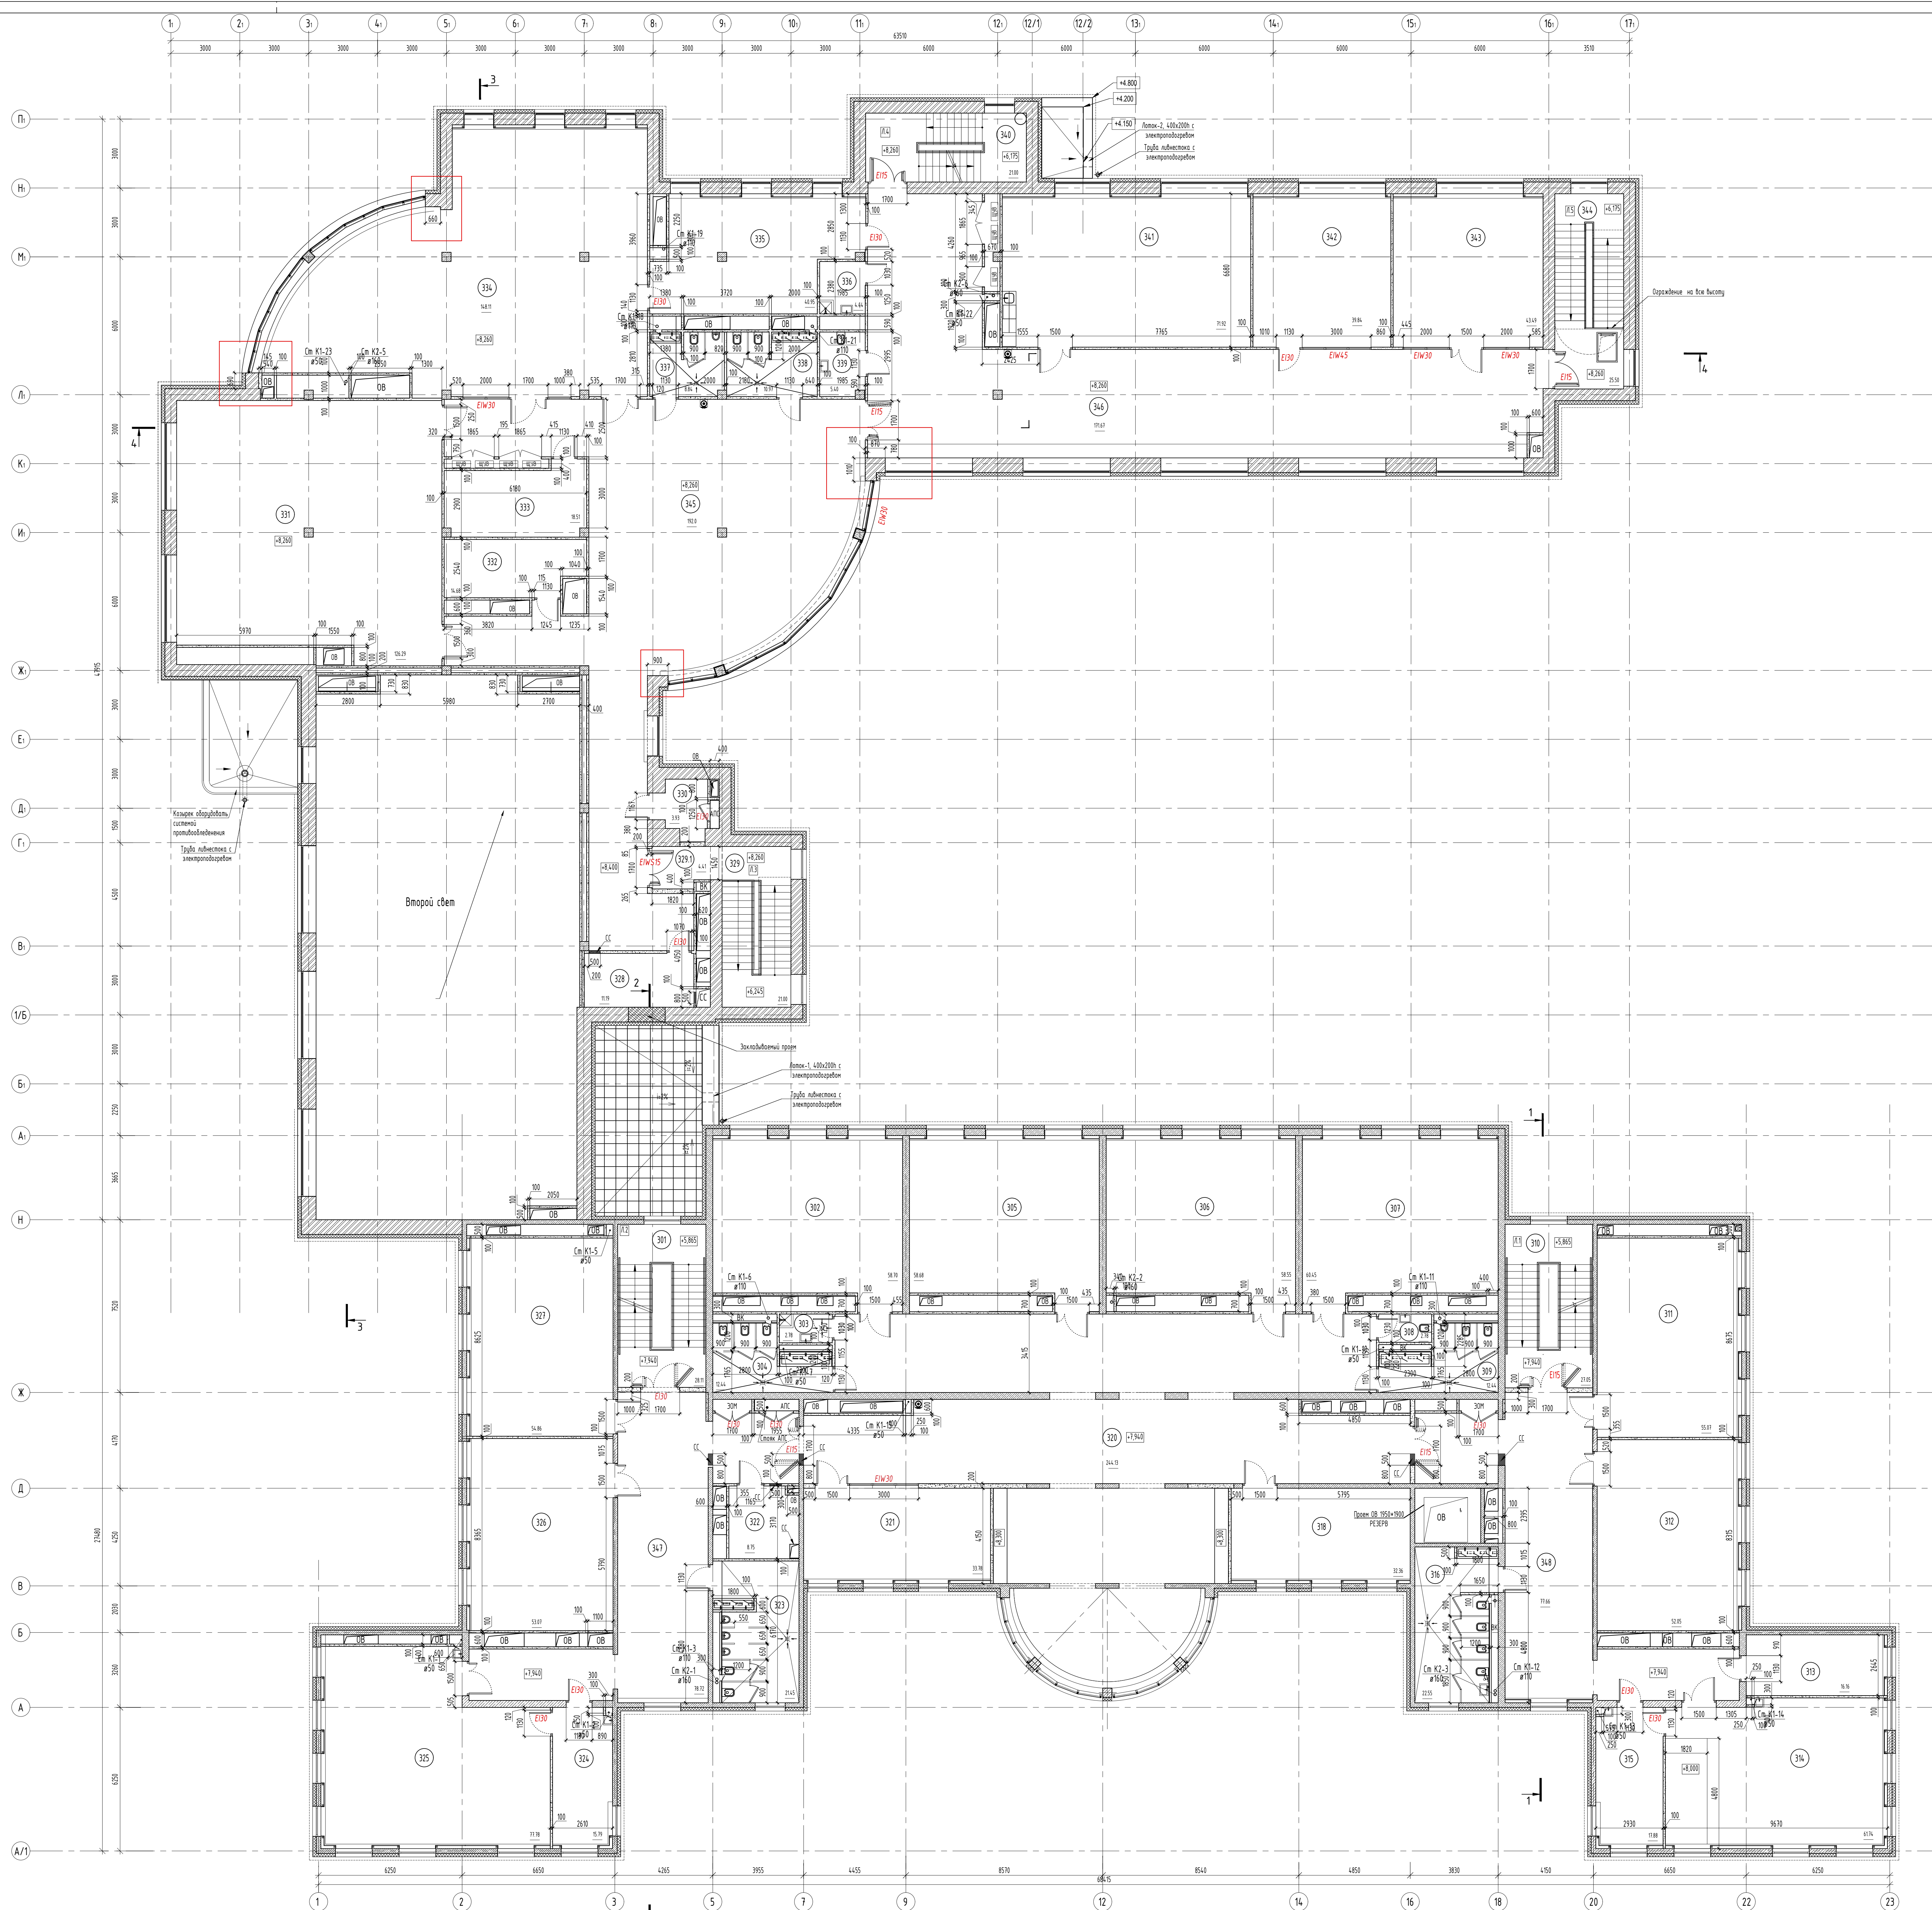

Экспликация помещений 3-го этажа				
Номер помещения	Наименование	Площадь м2	Класс помещения	
301	Астеническая клетка Тип И2	28,82		
302	Кабинет русского языка и литературы	98,70		
303	Псих	2,78	В4	
304	Сонетная для девочек (основная и старшая школа)	12,44		
305	Кабинет русского языка и литературы	58,68		
306	Кабинет математики	58,55		
307	Кабинет математики	60,45		
308	Сонетная для персонала	2,75		
309	Сонетная для мальчиков (основная и старшая школа)	12,44		
310	Астеническая клетка [И1]	27,05		
311	Кабинет географии	55,07		
312	Учебный кабинет учебной кабинеты	56,05		
313	Кабинет для индивидуальных занятий, 8 п.ч с психологом-психологом	9,16		
314	Учебный кабинет для изучения естественных физика	61,36		
315	Астеническая клетка физики	18,02	В3	
316	Сонетная для девочек с компьютерной техникой (основная и старшая школа)	23,25		
317	Подсобное помещение	6,66	В4	
318	Кабинет иностранного языка (основная и старшая школа)	32,34		
320	Коридор с рекреацией	24,19		
321	Кабинет иностранного языка (основная и старшая школа)	33,78		
322	Помещение связи	8,75	В4	
323	Сонетная для мальчиков (основная и старшая школа)	21,73		
324	Астеническая клетка биологии	15,93	В3	
325	Учебный кабинет для изучения естественных биологии + БЗР	51,07		
326	Учебный кабинет учебной кабинеты	17,38		
328	Кабинет типовой тип 1	56,86		
329	Коридор	11,19	В3	
329	Астеническая клетка [И1]	21,00		
329.1	Тендер	4,41		
330	Тех. помещение	3,93	В4	
331	Учебно-исследовательское помещение с возможностью организации административных услуг (интерактор)	125,19		
332	Роздебальня	14,45		
333	Роздебальня	16,56		
334	Модернизационный информационный библиотечный центр с зонами для индивидуальных занятий	52,15		
335	Модернизационный информационный библиотечный центр (зонация (экраны) фонды и выданы книг)	41,45	В3	
336	Псих	4,74	В4	
337	Сонетная для мальчиков (основная и старшая школа)	8,84		
338	Сонетная для девочек (основная и старшая школа)	10,97		
339	Сонетная для персонала	5,40		
340	Астеническая клетка [И1]	21,00		
341	Кабинет с рабочим пространством для учителей Тип 1 (основная и старшая школа)	71,92		
342	Учебно-исследовательское помещение с возможностью организации исследований	39,84	В3	
343	Помещение музея	43,49		
344	Астеническая клетка [И1]	25,50		
345	Коридор и рекреация (основная и старшая школа)	192,00		
346	Коридор и рекреация (основная и старшая школа)	178,67		
347	Коридор	78,72		
348	Коридор	77,66		
	Всего	2245,1		

УСЛОВНЫЕ ОБОЗНАЧЕНИЯ

- Сдвигнутые молотки и/или стволы
 - Заменяемые переключатели из заготовленных блоков
 - 1/625x25x100/0500/0,95 по ГОСТ Р 76322-2022, толщиной 100мм на клею с армированием базальтовой сеткой, выпущенные
 - Заменяемые переключатели из заготовленных блоков
 - 1/625x25x100/0500/0,95 по ГОСТ Р 76322-2022, толщиной 200мм на клею с армированием базальтовой сеткой, выпущенные
 - Заменяемые переключатели из односторонне односторонние двусторонние на все типы, эласто толщиной 100мм
 - Заменяемые переключатели из односторонне односторонние двусторонние до 30 раз, толщиной 100мм
 - Заменяемые односторонние переключатели
 - Заменяемые переключатели самонапряжения (Автоматической) с дверью и необходимой фурнитурой
- 201


- Нормы поставки на эксплуатацию

- Отметка уровня пола эстака

- Маркировка единичности заменяемых дверей, окон, переключателей
- ЕМ/ЕВ/ЕВ-М

1. Возможность устройства проемов в несущих стенах будет уточняться в проекте.
Размер и расположение вентиляционных шахт будет уточнен в проекте.
2. Шахты предназначены для прокладки инженерных коммуникаций и стожков ИВК, СС, ЗОМ, оборудованы лючками для обслуживания.
3. * категорирование по взрывопожарной опасности данных помещений выполнять на этапе проектирования.
4. Марки ограждений смотреть альбом 16-25/1 -П-АР лист 61

ИВ-100-105-10					
16-25/П-П-АР					
Капитальный ремонт объекта "БЭУ Школа № 429 "Сосновка город", расположенного по адресу: г. Москва, ул. Сосновкой шоссе 5-й д. 4, А.					
Архитектура-планировочные решения					
План 3 этажа, М:1:100					

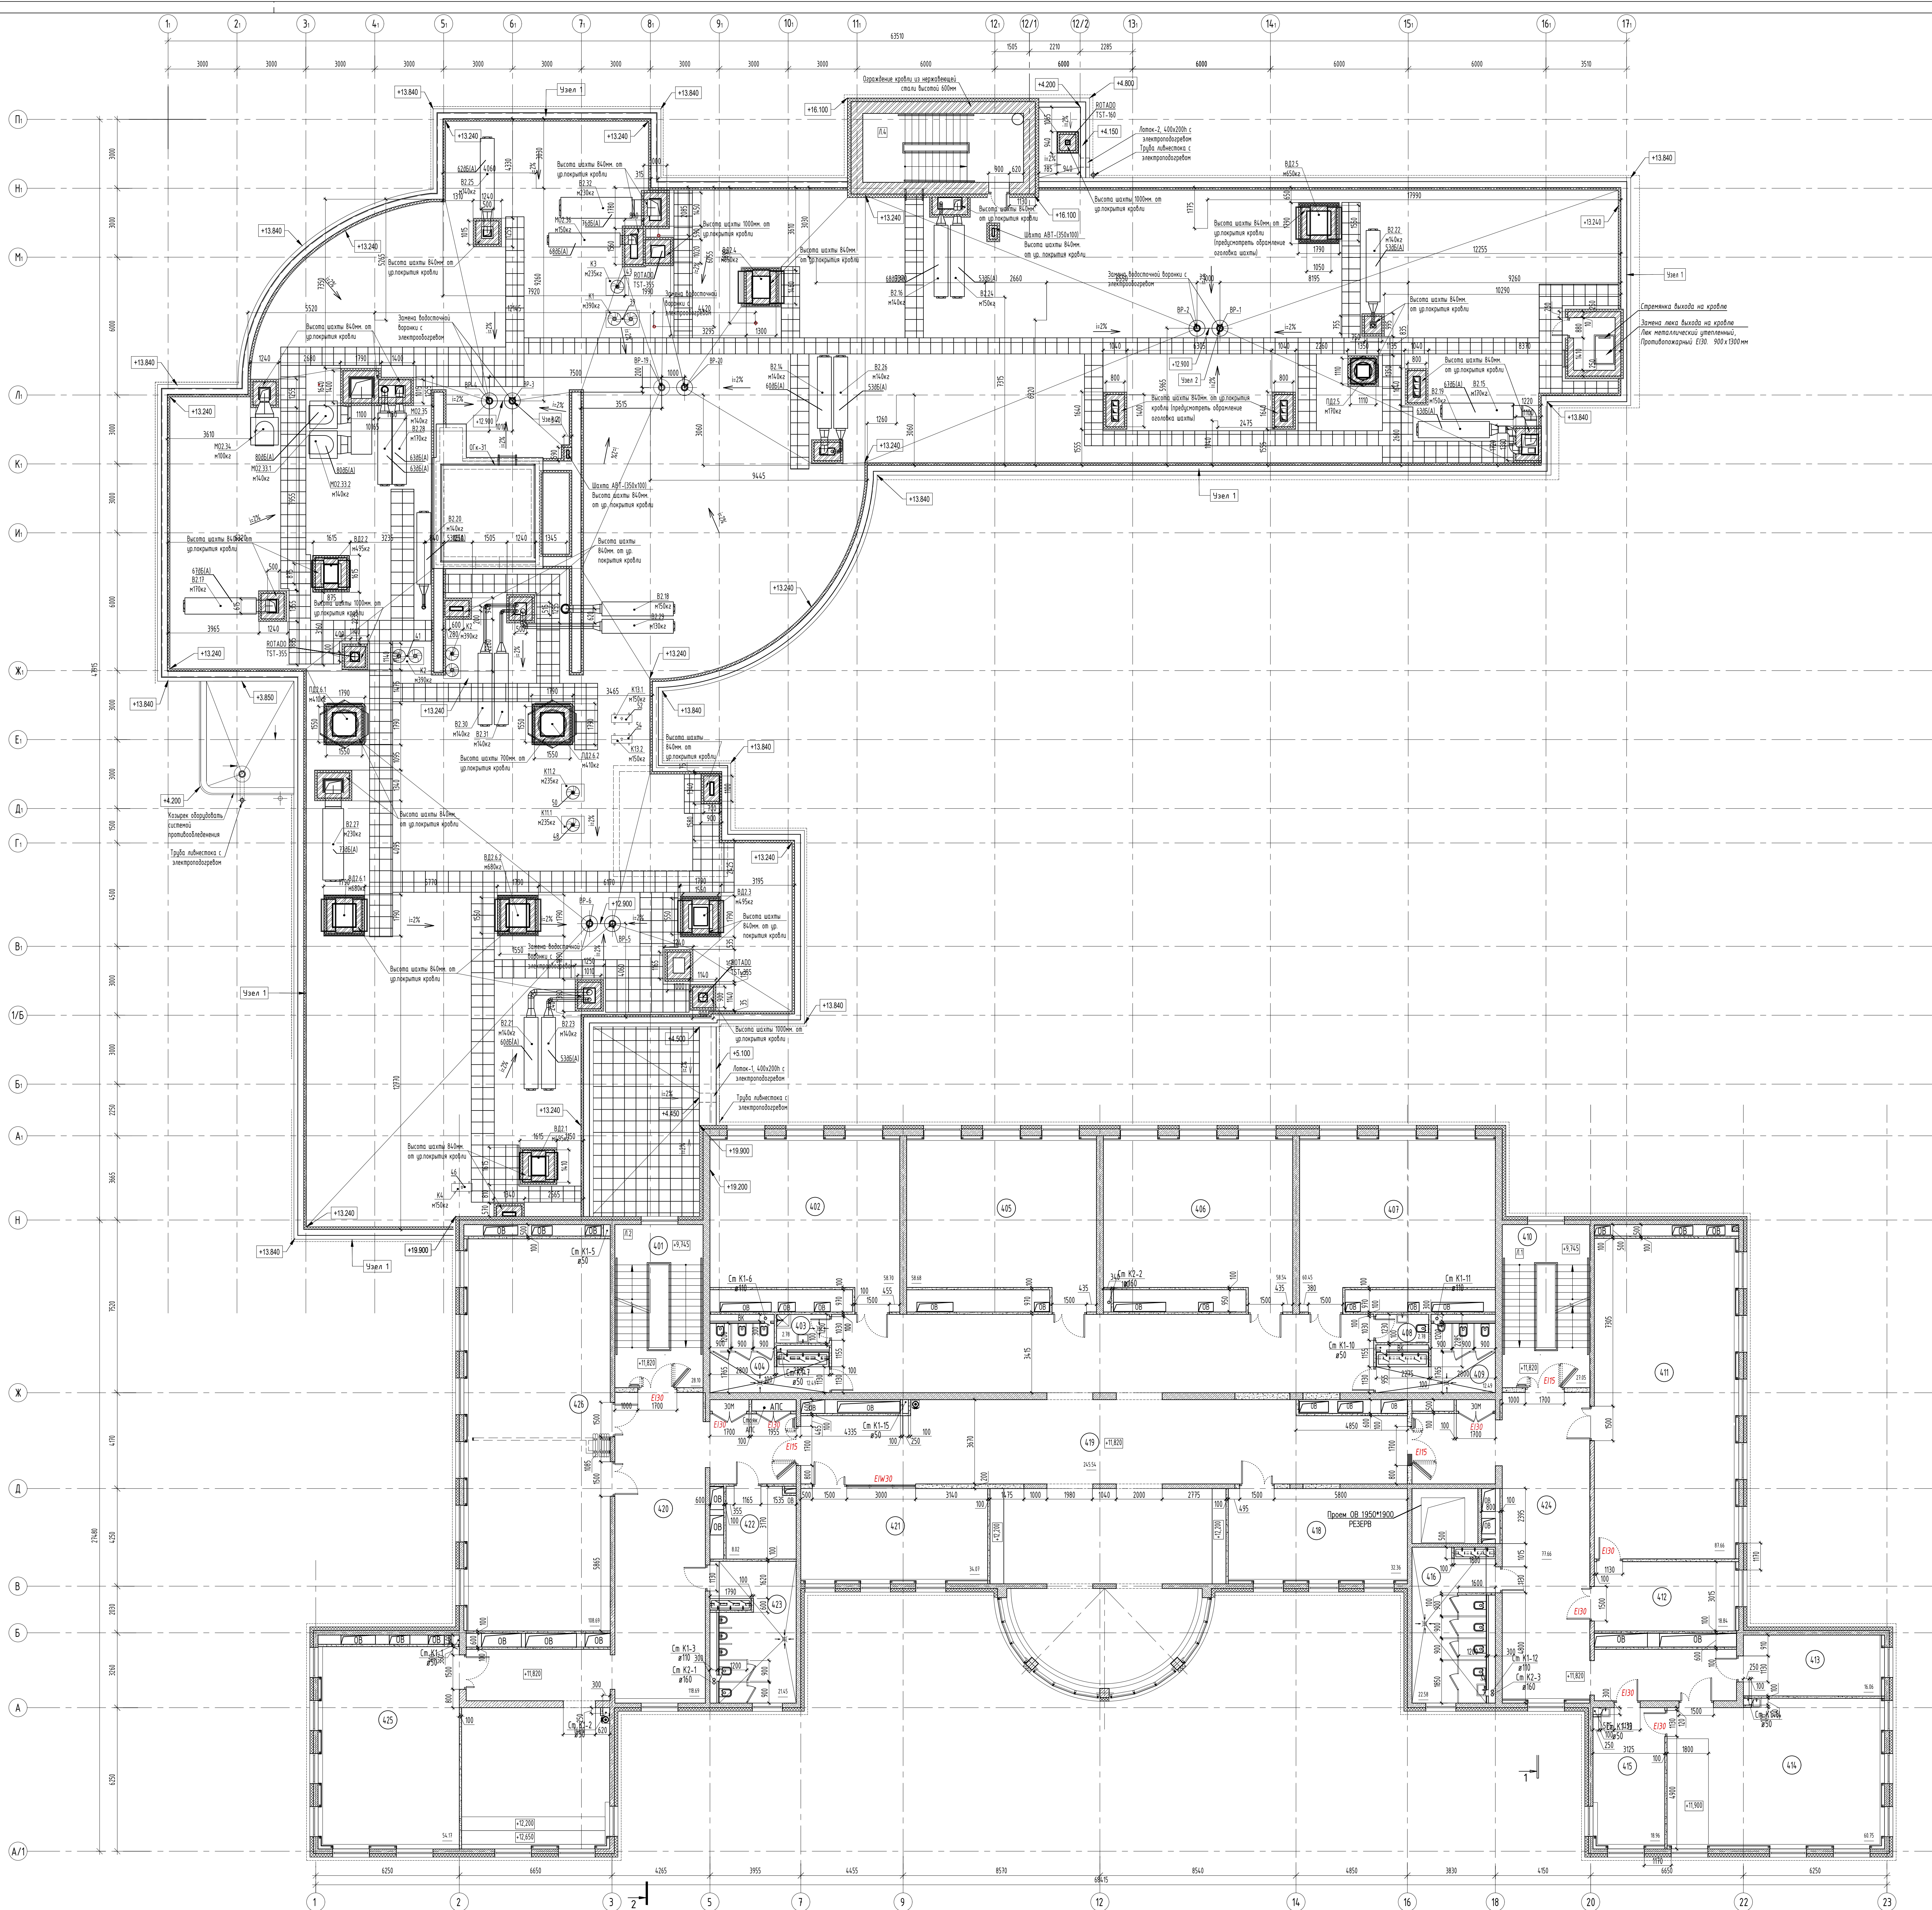

Номер помещения	Наименование	Площадь, м ²	Комплектация
401	Лестничная клетка Тип ИЭ	28,81	
402	Кабинет русского языка и литературы	58,70	
403	ФИ	2,78	84
404	Специал. для девочек (использия и старшая школа)	12,49	
405	Кабинет русского языка и литературы	58,68	
406	Кабинет математики	58,54	
407	Кабинет математики	60,45	
408	Специал. для парикюла	2,78	
409	Специал. для мальчиков (использия и старшая школа)	12,49	
410	Лестничная клетка (ЛП)	26,38	
411	Кабинет информационных технологий	87,86	
412	Лабюриатория при кабинете информационных технологий	18,64	83
413	Административный кабинет тип 1 (использия и старшая школа)	16,03	
414	Чтальные кабинеты для изучения естественных наук	60,75	
415	Лабюриаторная кабинет химии	18,96	83
416	Специал. для девочек с комюнальной личной гигиены (использия и старшая школа)	22,56	
417	Подсобные помещения	7,30	84
418	Кабинет иностранного языка (использия и старшая школа)	32,36	
419	Коридор с раздевалкой	24,54	
420	Коридор с раздевалкой	118,69	
421	Кабинет иностранного языка (использия и старшая школа)	34,07	
422	Помещения связи	8,02	84
423	Специал. для мальчиков (использия и старшая школа)	21,45	
424	Коридор	77,66	
425	Кабинет истории Тип 1	54,17	
426	Кабинет информатики с возможностью деления трансформирюющей переработкой на два помещения	110,69	
427	Лестничная клетка (ЛП)	28,81	
428	Помещения выхода на крыло	4,78	
Всего		1296,5	

[illegible]

1. Возможность устройства проемов в несущих стенах будет уточняться в проекте.
Размер и расположение вентиляционных шахт будет уточнен в проекте.
2. Шахты предназначены для прокладки инженерных коммуникаций и стожков ВК, СС, ЗОМ, оборудуются лестницами для обслуживания.
3. ★ категорирование по взрывопожарной опасности данных помещений выполнить на этапе проектирования.
4. Марки ограждений смотреть альбом 16-25/Г-П-АР лист 61

						16-25/П -П-АР		
						Капитальный ремонт объекта "ТБОУ Школа № 429 "Скоковская гора", расположенного по адресу: г.Москва, ул. Скоковской горы 5-в, д.14		
Изм.	Кол. л.	Лист	№ док.	Подпись	Дата			
Разработ.		Литовских			2020.07.07			
						Архитектурно-планировочные решения		
						Станд.	Лист	Листов
							Р	
И. контро.		Григорьев			2020.07.07			
Н. спет.					2020.07.07			
						Лист 4 из 4, всего М1000		
						 АЗУРИТ		



Номер помещения	Наименование	Площадь м2	Кол-во помещений
501	Лестничная клетка Тип Н2	27,26	
502	Лестничная клетка Тип Л1	27,05	
503	Венткамера 1	43,07	83
504	Венткамера 2	44,09	83
505	Техническое помещение	206,11	
506	Техническая планировка	155,65	83

УСЛОВНЫЕ ОБОЗНАЧЕНИЯ

- | | |
|---|---|
|  | <ul style="list-style-type: none"> - Сущестующие монтажные и/ли стены -Зачемнения переборщи из неабогоненных бляков -1/4х25х100/150/85/0 по ГЦИ Р 1652-2022, полноты 100мм на клею с сирогорением фольгистой сеткой, опукатуренной |
|  | <ul style="list-style-type: none"> -Зачемнения переборщи из неабогоненных бляков -1/4х25х100/150/85/0 по ГЦИ Р 1652-2022, полноты 100мм на клею с сирогорением фольгистой сеткой, опукатуренной -Зачемнения переборщи из ополоненных односторонне двусторонне на все высту пытки полноты 100мм |
|  | <ul style="list-style-type: none"> -Зачемнения переборщи из ополоненных односторонне двусторонне на все высту пытки полноты 100мм -Зачемнения опукатуренные переборщи |
|  | <ul style="list-style-type: none"> -Зачемнения переборщи сантехнические (вызгоствосили) с (варены с изобогоненной функцией) |
|  | <ul style="list-style-type: none"> -Номер помещения по экспликации |
|  | <ul style="list-style-type: none"> -Зачемнения уровни пола эписки |
|  | <ul style="list-style-type: none"> -Натуральная известности зачемнения двери, окон, переборщи |

1. Возможность устройства проемов в несущих стенах будет уточняться в проекте.
- Размер и расположение вентиляционных шахт будет уточнен в проекте.
- Шахты предназначенные для прокладки инженерных коммуникаций и стоек (ВК, СВ, ЗОМ) оборудуются личинки для обслуживания.
2. **★** категорирование по взрывопожарной опасности данных помещений выполнить на этапе проектирования.
3. Марки ограждений смотреть альбом 16-25/Г-П-АР лист 61

						16-25/Г-П-АР		
						Капитальный ремонт объекта "ГБОУ Школа № 429 "Соколиная гора", расположенного по адресу: г. Москва, ул. Соколиная гора, д. 5-я, 8/1		
Изм	Кол-во	Лист	№ док	Подпись	Дата			
Разобр		Листа		<i>[Подпись]</i>	2020.07.01			
						Архитектурно-планировочные решения		
						Стандарт	Лист	
						р		
И. контр.	Губарева			<i>[Подпись]</i>	2020.07.01	План тех. этажа. М1:100		
Гип	Морозова			<i>[Подпись]</i>	2020.07.01	 АЗУРИ		

