# Общие указания. Ведомость отделки помещений

## Ведомость отделки помещений (вариант Б)

| Пом. | Элемент | Отделка / состав (снизу вверх или от основания) | Цвет / материал | Кол-во | Смета ред.3 |
|---|---|---|---|---|---|
| 9.2.5 | Пол | Фальшпол 600×600 — восстановить по уровню (перепад ≤ 1 мм на 2 м) → ковролин рулонный (ширина рулона 4 м), ОДНИМ ОТРЕЗОМ без швов, на клей-фиксатор; ворс — к окну | графит, петлевой ворс | 11,31 м² | п. 3, 4 |
| 9.2.6 | Пол | Фальшпол — по уровню → кварцвинил 43 кл., замковый, 600×600, с подложкой по рекомендации производителя | «светлый камень» | 3,75 м² | п. 3, 5 |
| обе | Плинтус | Скрытый (теневой) алюм. плинтус h 60 с LED-лентой 2700 K; монтаж ДО шпаклёвки, в одной плоскости со стеной | анод. графит | по факту | п. 6 |
| обе | Стены | Дошивка ГКЛВ (по месту) → грунт → выравнивание → шпаклёвка Q4 → стеклохолст → грунт → окраска износостойкой моющейся краской 1 кл., 2 слоя, до перекрытия (H ≈ 3,5 м) | NCS S 1505-Y40R (тёплый беж), мат | 61,36 м² | п. 2, 7–11 |
| 9.2.5 | Акцент | Ламели МДФ шпон дуб 196 мм, шов 4 мм, на скрытом крепеже (клямеры по рейкам 20 мм); Ст.1, за диваном, 2000×2500 | шпон дуб, масло-воск «медовый» | 5,0 м² | п. 12 |
| 9.2.5 | Акустика | Панели ПЭТ-войлок 12 мм на клей/кляммеры: Ст.5 у окна 950×2250 + Ст.5 над шкафом 1400×1000 | графит | 4,0 м² | п. 13 |
| 9.2.6 | Рейка | Подложка МДФ 10 мм (окраска графит) → рейка МДФ шпон дуб 30×20, шаг 50; снизу LED-профиль; Ст.3 над фартуком | шпон дуб «медовый» | 2,1 м² | новая (ред.3) |
| 9.2.6 | Фартук | Кварцевый агломерат 12 мм, из одной партии со столешницей, вырезы под 2 розетки (h 1100) | светлый кварц | 0,63 м² | п. 44 (изделие) |
| обе | Откосы | Окна ОК-1 и над стеклянной перегородкой: грунт → выравнивание → Q4 → стеклохолст → окраска | как стены | 9,94 мп | п. 14–18 |
| обе | Потолок | ОТКРЫТЫЙ. Обеспылить, грунт, окраска потолка и ВСЕХ инженерных систем (трубы, короба, подвесы) краской матовой, 2 слоя, краскопультом. Спринклеры и датчики — НЕ окрашивать (заклеить) | RAL 7021 (чёрно-серый), мат | 15,51 м² | п. 19, 20 |

## Примечания

1. Альбом выполнен по модели (этажный план + видеофиксация) и смете ред.3. Размеры — проверить контрольным обмером до начала работ.
2. Высота стен до перекрытия H ≈ 3500 мм (по смете ред.2, площадь окраски 69,36 м²) — уточнить. Потолок открытый, без подвесных систем.
3. Порядок работ: электромонтаж и закладные → дошивка ГКЛВ → плинтус скрытый (каркас) → стены до Q4 → окраска потолка/инженерки → стеклохолст и окраска стен → фальшпол → покрытия пола → акцент/акустика/рейка → мебель.
4. Окраска потолка — ДО финишной окраски стен; стык потолок/стена — малярная лента, ровная линия на отметке перекрытия.
5. Выкраски стен и потолка (не менее А4) согласовать с заказчиком на месте при дневном и искусственном свете.
6. Цвета — по листу 9 (колористика); шпон акцента и рейки — один оттенок, образцы утвердить до заказа.
7. Существующий ЩР (Ст.1) — не закрывать отделкой и мебелью; сохранить свободный доступ.
8. 9.2.6 — без водоснабжения и канализации (требование УК).

Состав альбома: 1 Общие указания · 2 Полы · 3 Потолок и свет · 4 Развёртки 9.2.5 · 5 Развёртки 9.2.6 · 6 Узлы · 7 Мебель · 8 Электрика · 9 Колористика · 10 Ключевые размеры

**ООО «Матрёшка Проект»**

ГИП Толубец Д.

Разраб.

Дата: 28.10.2026


ИНТЦ МГУ «Воробьёвы горы», Образовательный кластер, 10 этаж, отм. +39.600

Ремонт помещений 9.2.5 «Рабочая зона», 9.2.6 «Кофе-поинт»

**Общие указания. Ведомость отделки помещений**

| Масштаб — | Стадия | Лист | Листов |
|---|---|---|---|
| | Р | 1 | 10 |

# План полов. Раскладка покрытий

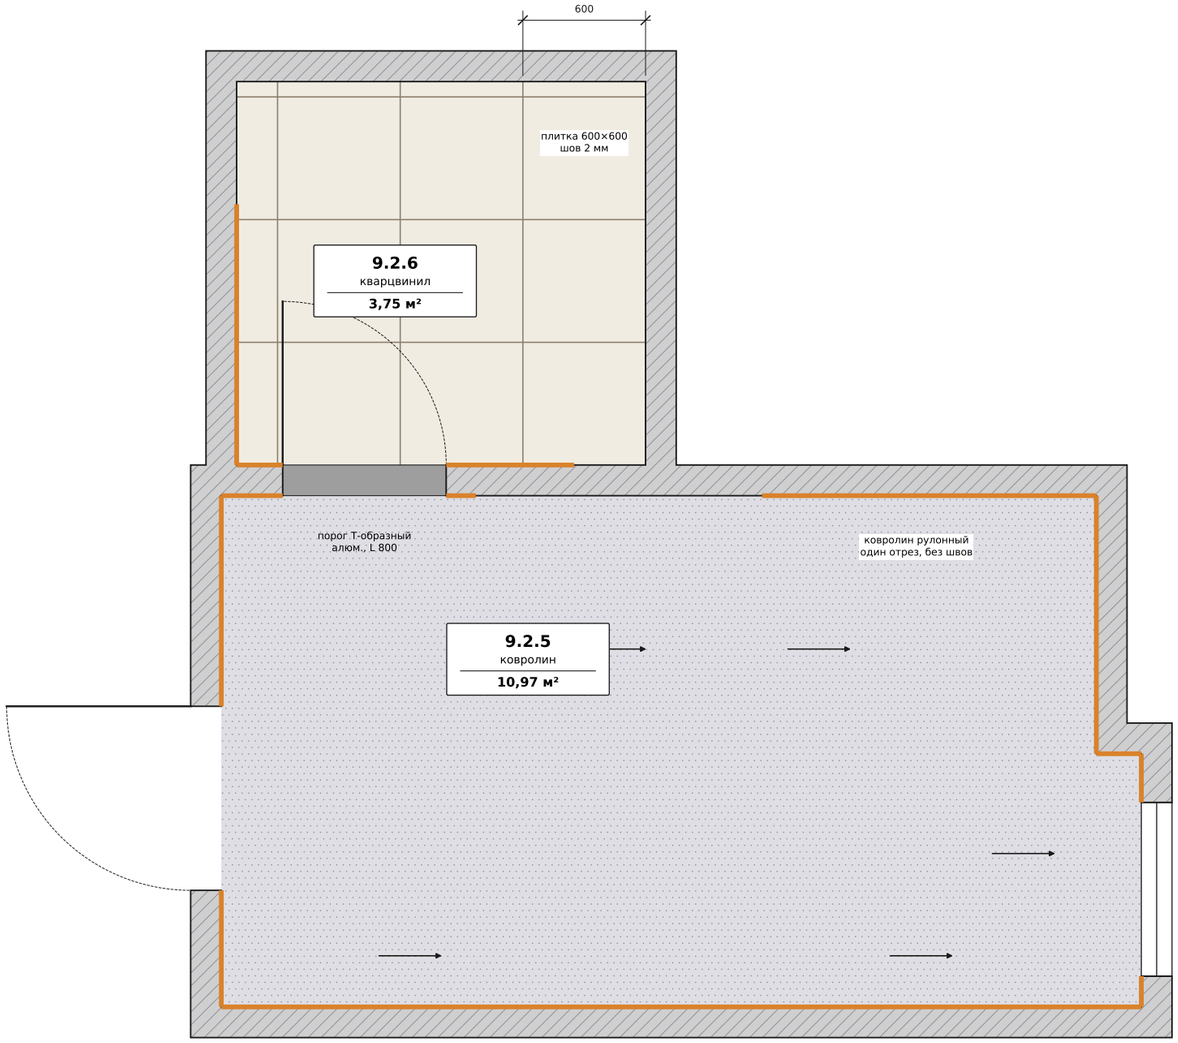


## Экспликация полов

| Тип | Покрытие | Монтаж | м² |
|---|---|---|---|
| Т1 | Ковролин рулонный, петля, графит, 33 кл., рулон 4 м | один отрез, клей-фиксатор | 11,31 |
| Т2 | Кварцвинил 43 кл., замковый, 600×600 | плавающий, с подложкой | 3,75 |
| — | Фальшпол: восстановить по уровню | Δ ≤ 1 мм / 2 м | 15,51 |


скрытый плинтус h 60 с LED (узел У1)

## Примечания

1. Ковролин 9.2.5 — один отрез из рулона 4 м (помещение 4,5×2,5 м укладывается без швов): отрез ≈ 4,7×4,0 м, подрезка по месту.
2. Направление ворса — к окну (стрелки). Перед укладкой — акклиматизация рулона в помещении не менее 24 ч.
3. Кварцвинил 9.2.6 — раскладка от оси двери Д1.2.3*; подрезка у стен ≥ 200 мм.
4. Порог-переход в проёме Д1.2.3* — в одном уровне, перепад покрытий ≤ 2 мм (узел У4).
5. Плинтус — по всем свободным стенам; за шкафом-купе и под кухней 9.2.6 не выполняется.
6. Под столом руководителя — напольный лючок (см. лист 8): вырез в фальшполу и ковролине по месту.

| | |
|---|---|
| **ООО «Матрёшка Проект»** | ИНТЦ МГУ «Воробьёвы горы», Образовательный кластер, 10 этаж, отм. +39.600 |
| ГИП Толубец Д. | Ремонт помещений 9.2.5 «Рабочая зона», 9.2.6 «Кофе-поинт» |
| Разраб. | **План полов. Раскладка покрытий** |
| Дата: 28.10.2026 | Масштаб 1:30 · Стадия: Р · Лист: 2 · Листов: 10 |

# План потолка (открытый) и освещения

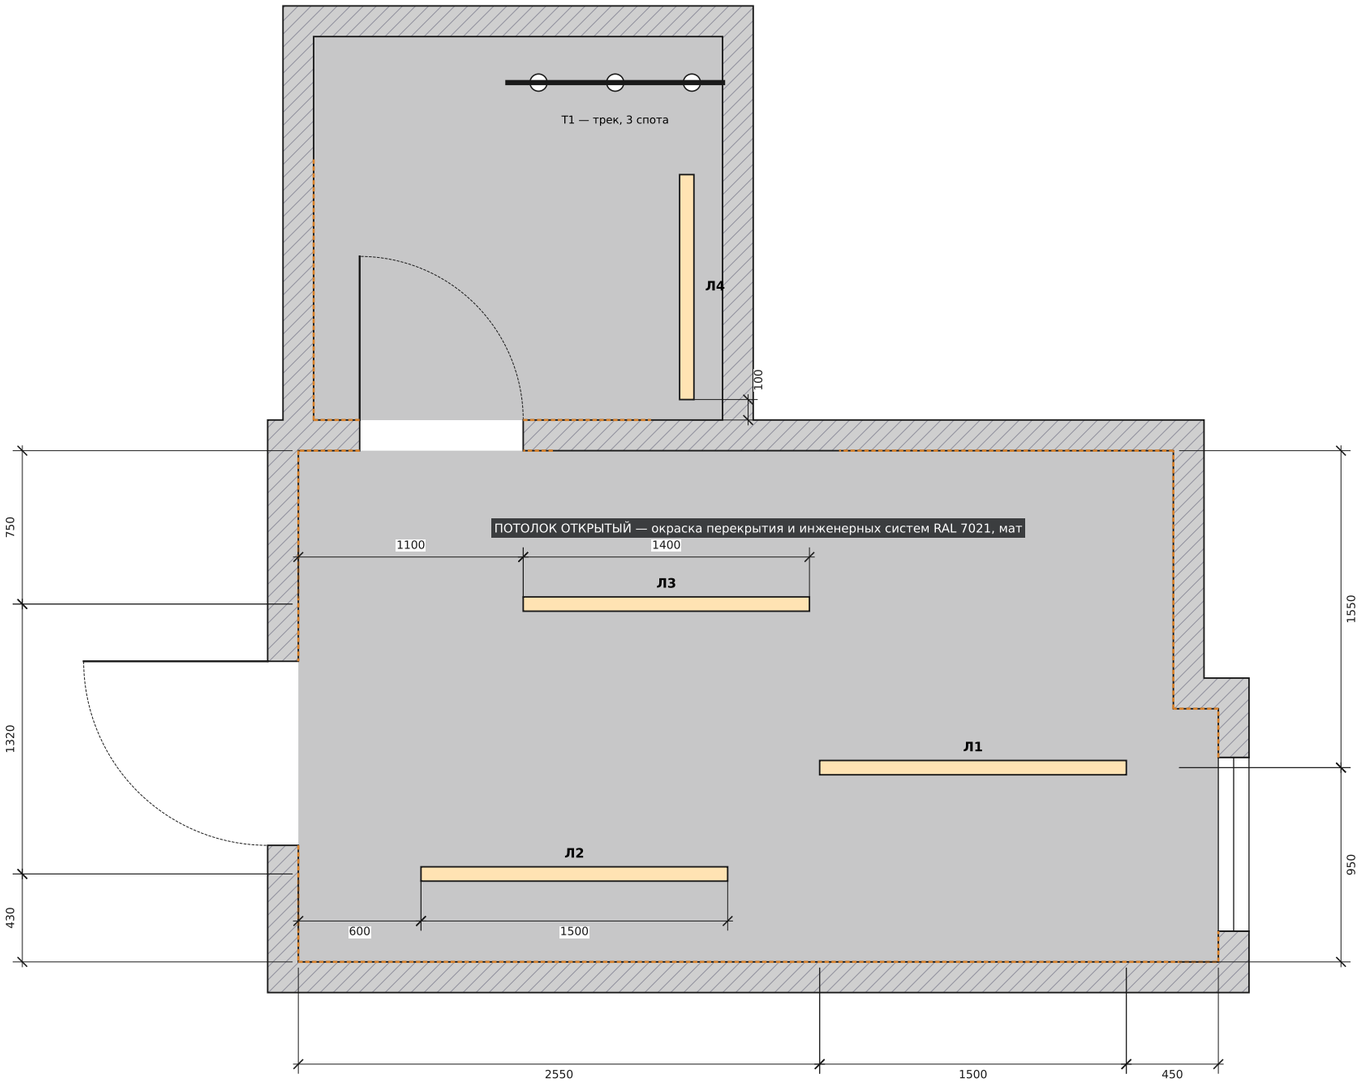


## Спецификация освещения (смета п. 24, 25)

| Марка | Светильник | Монтаж | Кол. |
|---|---|---|---|
| Л1–Л3 | Линейный подвесной LED, диммируемый, L 1500 | низ на отм. +2,500 | 3 |
| Л4 | Линейный подвесной LED, диммируемый, L 1100 (над стойкой) | низ на отм. +2,300 | 1 |
| Т1 | Трек-шина 1 м + 3 поворотных спота, 3000 K | на перекрытии / подвес | 1 компл |
| С3 | LED-лента 2700 K в скрытом плинтусе | h 0–60 | по факту |
| С4 | LED-профиль под реечной панелью 9.2.6 | отм. +1,500 | 1,05 м |


## Примечания

1. Окраска потолка и инженерки — до монтажа светильников; подвесы светильников — тросовые, в цвет потолка.
2. Высоту подвеса Л1 над столом руководителя уточнить по месту (900–1100 мм от столешницы).
3. Управление: у входа — Л1–Л3 (диммер, 2 канала) + С3; в 9.2.6 у двери — Л4/Т1 + С4.
4. Блоки питания и драйверы — в доступном месте (на перекрытии, с маркировкой).
5. Спринклеры, датчики АПС и оповещатели — не перекрывать светильниками и треком (≥ 0,5 м).

| | |
|---|---|
| **ООО «Матрёшка Проект»** | ИНТЦ МГУ «Воробьёвы горы», Образовательный кластер, 10 этаж, отм. +39.600 |
| ГИП Толубец Д. | Ремонт помещений 9.2.5 «Рабочая зона», 9.2.6 «Кофе-поинт» |
| Разраб. | **План потолка (открытый) и освещения** |
| Дата: 28.10.2026 | Масштаб 1:30 · Стадия: Р · Лист: 3 · Листов: 10 |


# Развёртки стен пом. 9.2.5 (отделка)

### Ст.1 — у шахт ОВ/ВК, щит

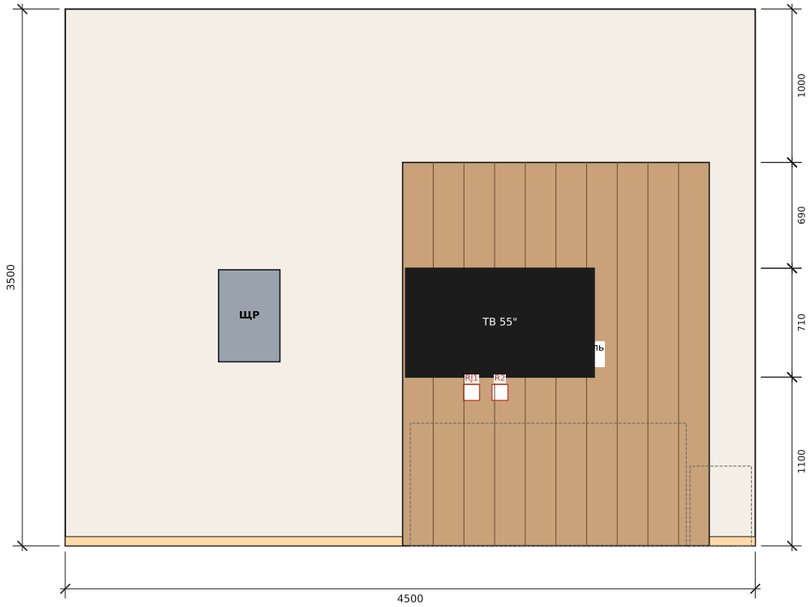



Окраска: 4.50×3.50 − 5.00 = 10.75 м²

### Ст.2 — окно ОК-1

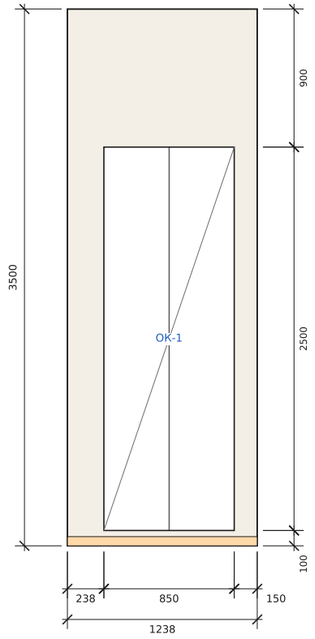



Окраска:
1.24×3.50 − 2.12
= 2.21 м²

### Ст.3 — уступ

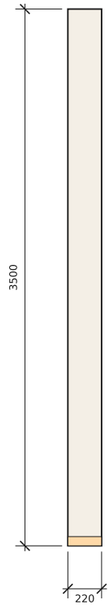



Окраска:
0.22×3.50 − 0.00
= 0.77 м²

### Ст.4 — радиатор

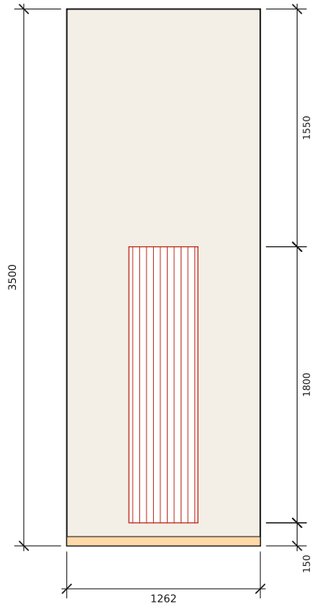



Окраска:
1.26×3.50 − 0.00
= 4.42 м²

### Ст.5 — шкаф, МФУ, дверь Д1.2.3*

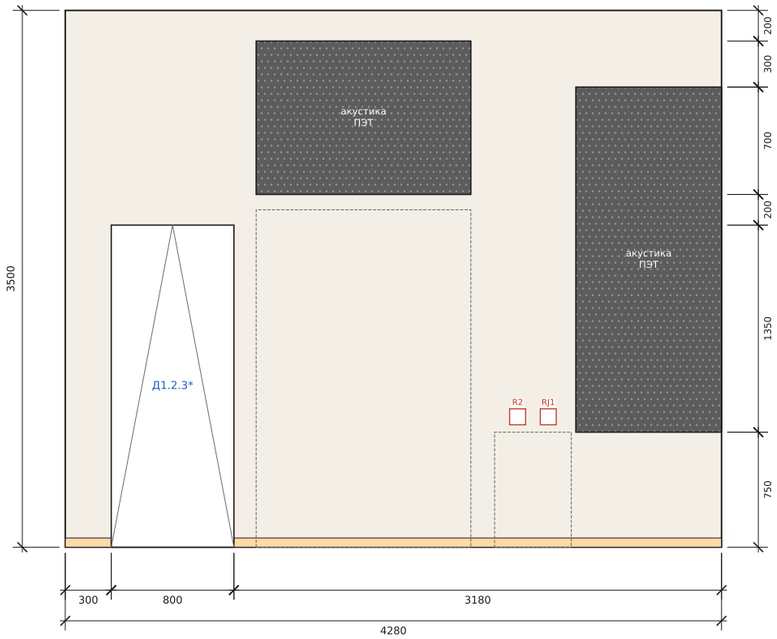


Окраска: 4.28×3.50 − 5.22 = 9.76 м²

### Ст.6 — вход, вешалка

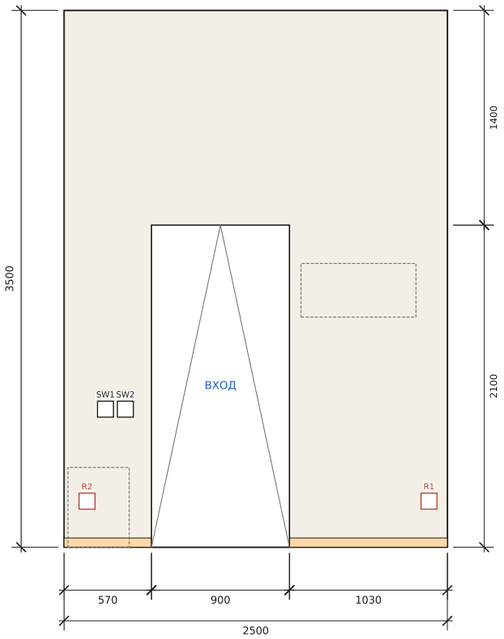


Окраска: 2.50×3.50 − 1.89 = 6.86 м²

## Отделка стен 9.2.5

| Элемент | Расположение |
|---|---|
| Окраска (S 1505-Y40R) | стены до перекрытия, за вычетом акцента/акустики |
| Акцент шпон | Ст.1: 2000×2500, низ 0 |
| Акустика ПЭТ | Ст.5: у окна 950×2250, низ 750; над шкафом 1400×1000, низ 2300 |
| Плинтус LED | h 60, все свободные участки |
| ТВ 55" | Ст.1 на акценте, низ 1100; закладная + R2/RJ45 за ТВ h 1000 |
| Радиатор | Ст.4, вертикальный 450×1800, низ 150 |
| ЩР | Ст.1, x 1000 от левого края (уточнить) |

## Примечания

1. Развёртки — вид изнутри; размеры по горизонтали — слева направо.
2. Площади под рисунками — для контроля; в смете — по ред.2/ред.3.

**ООО «Матрёшка Проект»**

ГИП Толубец Д.

Разраб.

Дата: 28.10.2026

ИНТЦ МГУ «Воробьёвы горы», Образовательный кластер, 10 этаж, отм. +39.600


Ремонт помещений 9.2.5 «Рабочая зона», 9.2.6 «Кофе-поинт»

**Развёртки стен пом. 9.2.5 (отделка)**

| Масштаб 1:40 | Стадия | Лист | Листов |
|---|---|---|---|
| | Р | 4 | 10 |


# Развёртки стен пом. 9.2.6 (отделка)

**Ст.1 — дверь Д1.2.3***

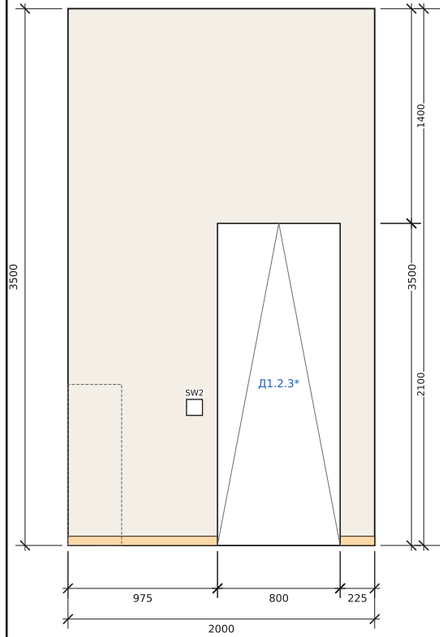



Окраска: 2.00×3.50 − 1.68 = 5.32 м²

**Ст.2 — барная стойка**

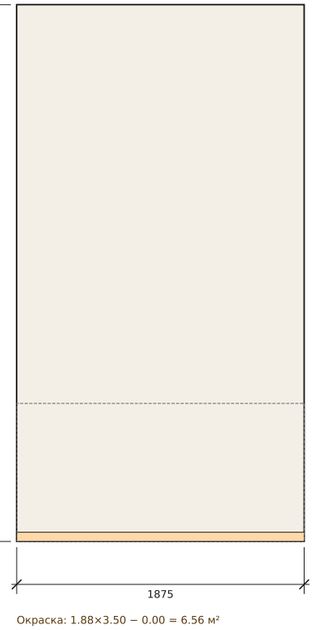



Окраска: 1.88×3.50 − 0.00 = 6.56 м²

**Ст.3 — столешница, рейка**

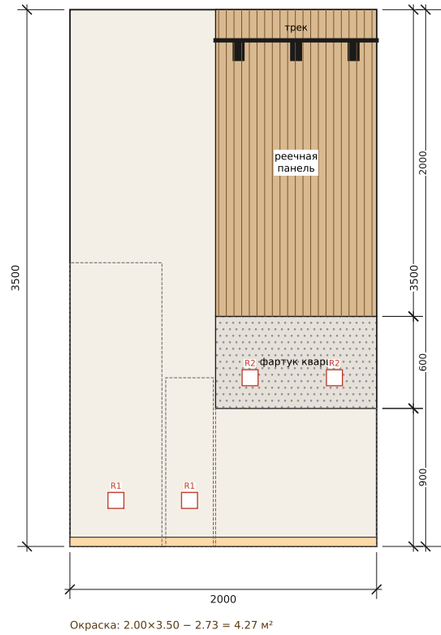


Окраска: 2.00×3.50 − 2.73 = 4.27 м²

**Ст.4 — холодильник**

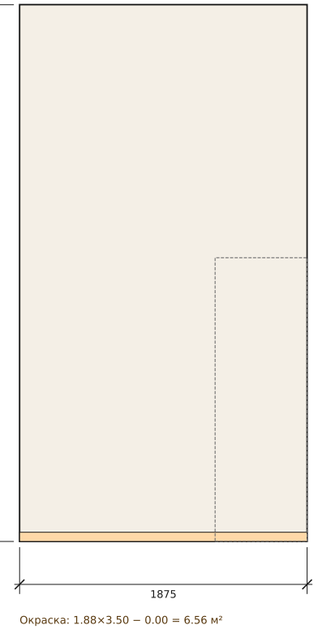


Окраска: 1.88×3.50 − 0.00 = 6.56 м²

## Отделка стен 9.2.6

| Элемент | Расположение |
|---|---|
| Окраска | S 1505-Y40R, до перекрытия |
| Фартук | кварц 12 мм, 1050×600, низ 900 |
| Реечная панель | 1050×2000, низ 1500, до перекрытия |
| LED C4 | под рейкой, отм. +1,500 |
| Трек T1 | над столешницей, на перекрытии |

## Примечания


1. Розетки R2 над столешницей — в фартуке (вырезы по месту, после монтажа столешницы).
2. Окраска за холодильником и кулером — выполняется.
3. Рейку торцевать по факту высоты перекрытия; верхний торец — с зазором 10 мм (теневой).

| | | | | |
|---|---|---|---|---|
| **ООО «Матрёшка Проект»** | ИНТЦ МГУ «Воробьёвы горы», Образовательный кластер, 10 этаж, отм. +39.600 | | | |
| ГИП Толубец Д. | Ремонт помещений 9.2.5 «Рабочая зона», 9.2.6 «Кофе-поинт» | | | |
| Разраб. | **Развёртки стен пом. 9.2.6 (отделка)** | | | |
| Дата: 28.10.2026 | Масштаб 1:40 | Стадия: Р | Лист: 5 | Листов: 10 |

# Узлы отделки

## У1 Скрытый плинтус с LED


М 1:5

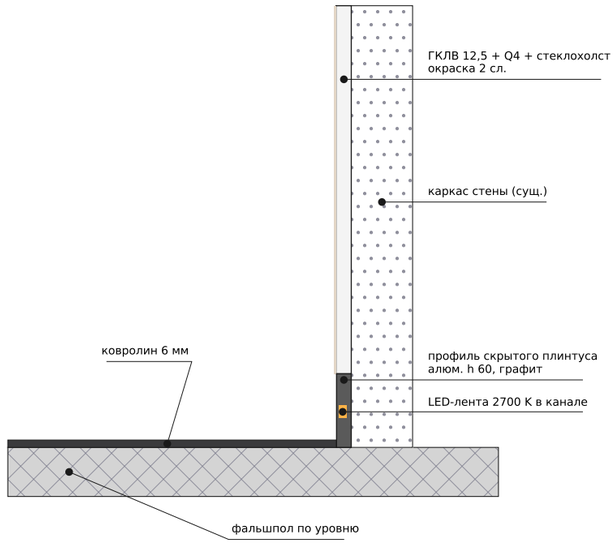


Профиль крепится к каркасу до шпаклёвки. Лицевая полка — в плоскости чистовой стены; зазор до ковролина 2–3 мм.

## У2 Акцентная панель, шпон дуб


М 1:5

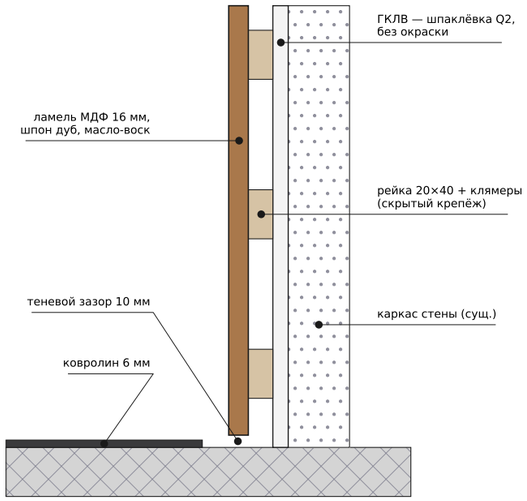


Ламели 196 мм, V-шов 4 мм. Верх — алюм. торцевой профиль на отм. +2,500; торцы ламелей — кромка шпоном.

## У3 Рейка, LED, фартук (9.2.6)


М 1:5

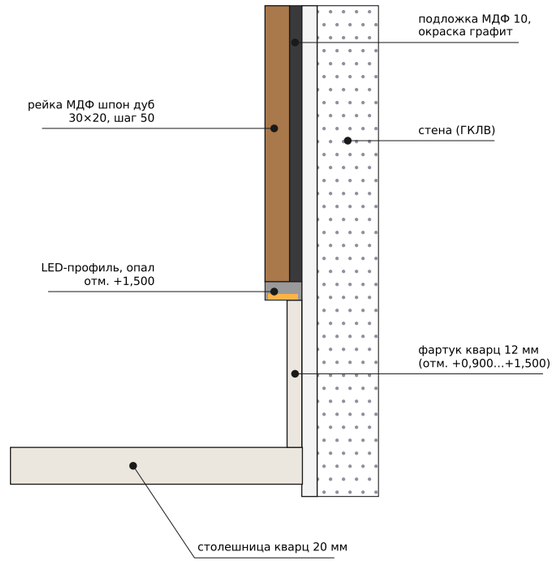


Рейка торцуется по факту высоты; верхний торец — теневой зазор 10 мм до перекрытия. Фартук и столешница — из одной партии.

## У4 Стык покрытий в проёме Д1.2.3*


М 1:2

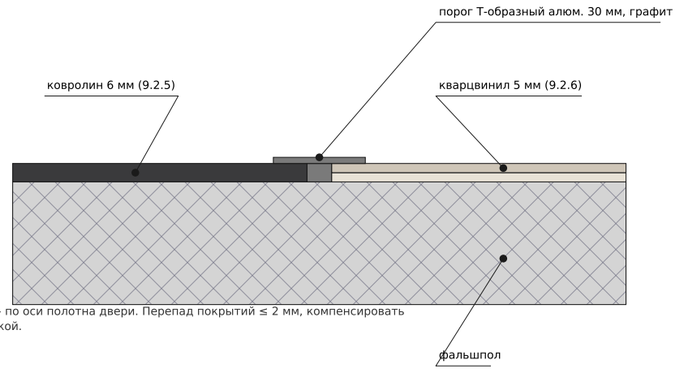


Порог — по оси полотна двери. Перепад покрытий ≤ 2 мм, компенсировать подложкой.

## У5 Акустическая панель ПЭТ


М 1:5

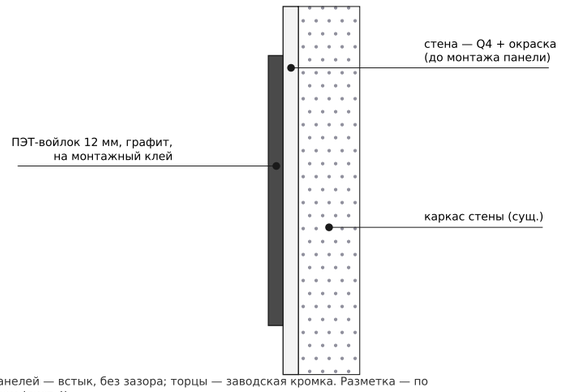


Стыки панелей — встык, без зазора; торцы — заводская кромка. Разметка — по развёрткам (лист 4).

## У6 Откос окна ОК-1 (план)


М 1:5

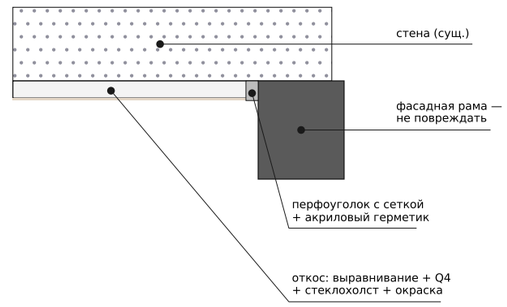


Глубина откоса ≈ 200 мм (уточнить). Примыкание к раме — герметик в цвет откоса.

| | |
|---|---|
| **ООО «Матрёшка Проект»** | ИНТЦ МГУ «Воробьёвы горы», Образовательный кластер, 10 этаж, отм. +39.600 |
| ГИП Толубец Д. | Ремонт помещений 9.2.5 «Рабочая зона», 9.2.6 «Кофе-поинт» |
| Разраб. | **Узлы отделки** |
| Дата: 28.10.2026 | Масштаб 1:5; 1:2 — Стадия: Р — Лист: 6 — Листов: 10 |

# План расстановки мебели (вариант Б)

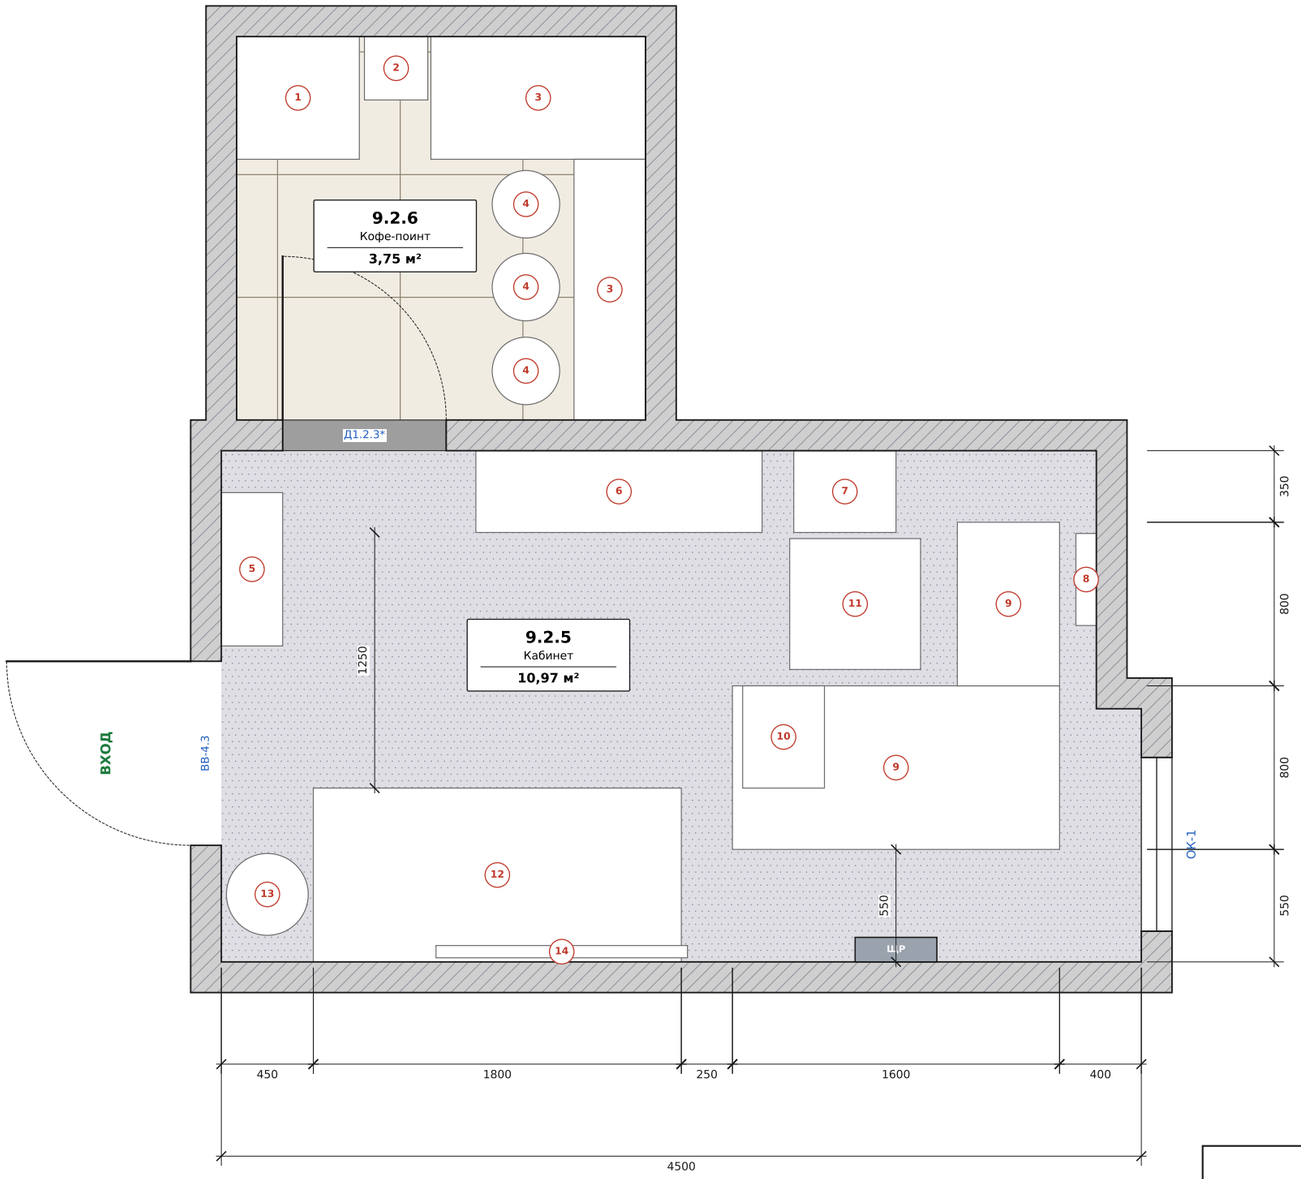


шахты ОВ / ВК (по проекту)

## Спецификация мебели (вариант Б)


| Поз. | Наименование | Характеристика / материал | Кол. |
|---|---|---|---|
| 1 | Холодильник отдельностоящий | 600×600, h≈1850, No Frost, нерж./графит, класс A+ | 1 |
| 2 | Кулер напольный | 310×310,<br>нагрев/охлаждение, нижняя загрузка или пурифайер | 1 |
| 3 | Столешница + барная стойка, Г-образная | кварцевый агломерат 20 мм,<br>h=900/1050; фартук кварц 1050×600 — в комплекте изделия | 1 |
| 3а | Нижние модули кухни (под столешницу) | 1050×600,<br>h=870, корпус ЛДСП, фасады МДФ шпон/плёнка «дуб», push-to-open, цоколь графит | 1 |
| 3б | Корпус барной стойки | 1275×330, h=1010, ЛДСП/МДФ «дуб» (каркас под кварц) | 1 |
| 4 | Табурет барный | Ø330,<br>h сиденья 750, опора металл графит, обивка ткань/экокожа терракота | 3 |
| 5 | Вешалка настенная с полкой | 750×300, реечная панель дуб + 5 крючков графит | 1 |
| 6 | Шкаф для документов, двери-купе | 1400×400,<br>h=2200, ЛДСП Egger «дуб», профиль графит; встроенный | 1 |
| 7 | Тумба под МФУ | 500×400, h=750, ЛДСП «дуб», 1 полка + ящик | 1 |
| 8 | Радиатор трубчатый с термоголовкой | вертикальный 450×1800,<br>белый RAL 9016 — по проекту ОВ после согласования с УК | 1 |
| 9 | Стол руководителя Г-образный | основной 1600×800 + приставка 800×500 с подвесной тумбой,<br>шпон дуб / ЛДСП «дуб», опоры-панели, кабель-канал | 1 |
| 10 | Тумба приставная с замком | 400×500, h=600, 3 ящика, «дуб», на колёсах | 1 |
| 11 | Кресло руководителя | экокожа/кожа беж,<br>механизм мультиблок, крестовина алюм. графит | 1 |
| 12 | Диван двухместный | 1800×850,<br>h 800, ткань рогожка/букле беж, ножки металл графит, 2 декор. подушки | 1 |
| 13 | Столик приставной | Ø400, h 520, металл графит + столешница шпон дуб | 1 |
| 14 | Телевизор 55" 4K + кронштейн поворотный | на акцентной стене,<br>низ ТВ 1100, разворот к столу/дивану | 1 |

### Примечания

1. Директор сидит лицом к стене ОВ/ВК, окно — слева (естественный свет слева, СанПиН).
2. Перед ЩР (Ст.1) между столом и стеной остаётся 550 мм — привязку щита уточнить; при необходимости сместить стол.
3. Диван — у акцентной стены; посетители — на диване.

| | | | | |
|---|---|---|---|---|
| **ООО «Матрёшка Проект»** | | ИНТЦ МГУ «Воробьёвы горы», Образовательный кластер, 10 этаж, отм. +39.600 | | |
| ГИП Толубец Д. | | Ремонт помещений 9.2.5 «Рабочая зона», 9.2.6 «Кофе-поинт» | | |
| Разраб. | | **План расстановки мебели (вариант Б)** | | |
| Дата: 28.10.2026 | | Масштаб 1:30 | Стадия: Р | Лист: 7 / Листов: 10 |

# Розетки, выключатели, лючок (вариант Б)

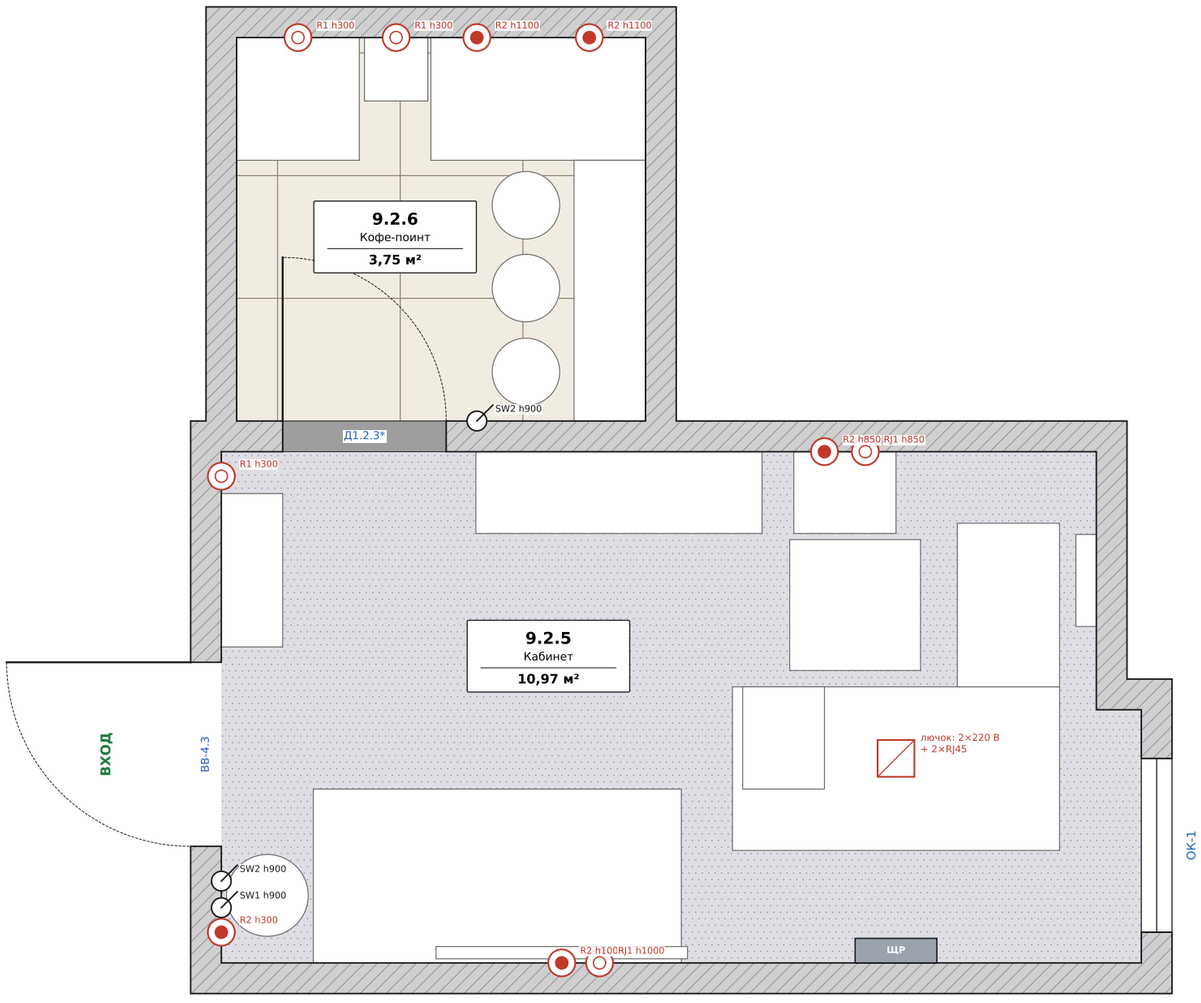


## Электроустановочные изделия (вар. Б)

| Обозн. | Наименование | Кол. |
|---|---|---|
| FB | Лючок напольный (2×220 В + 2×RJ45) в фальшпол | 1 |
| R2 | Розетка двойная 220 В с заземлением, 16 А | 5 |
| R1 | Розетка одинарная 220 В с заземлением, 16 А | 3 |
| RJ1 | Розетка компьютерная 1×RJ45 Cat.6 | 2 |
| SW2 | Выключатель двухклавишный 10 А | 2 |
| SW1 | Выключатель одноклавишный 10 А | 1 |

## Примечания

1. h — до низа коробки от чистого пола, мм.
2. Питание — от существующего ЩР; 9.2.6 — отдельная группа с УЗО 30 мА (смета п. 30).
3. Лючок — под столом руководителя, кабель в фальшполу (до укладки ковролина).
4. Выключатели у входа: диммер Л1–Л3 (2-клав.) + LED-плинтус; в 9.2.6 — Л4/трек + LED рейки.

шахты ОВ / ВК (по проекту)

| | | | | |
|---|---|---|---|---|
| **ООО «Матрёшка Проект»** | | ИНТЦ МГУ «Воробьёвы горы», Образовательный кластер, 10 этаж, отм. +39.600 | | |
| ГИП | Толубец Д. | Ремонт помещений 9.2.5 «Рабочая зона», 9.2.6 «Кофе-поинт» | | |
| Разраб. | | **Розетки, выключатели, лючок (вариант Б)** | | |
| Дата: 28.10.2026 | | Масштаб 1:30 | Стадия: Р | Лист: 8 / Листов: 10 |

# Колористика и материалы

**Стены — окраска**

NCS S 1505-Y40R, матовая, моющаяся 1 кл.

где: 9.2.5, 9.2.6

смета: п. 11

**Потолок и инженерка**

RAL 7021, матовая

где: 9.2.5, 9.2.6

смета: п. 20

**Ковролин**

графит, петлевой ворс, рулон 4 м

где: 9.2.5

смета: п. 4

**Кварцвинил**

«светлый камень» 600×600

где: 9.2.6

смета: п. 5

**Шпон дуб**

масло-воск, тон «медовый» — акцент, рейка, мебель

где: 9.2.5, 9.2.6

смета: п. 12, 41, 44

**Акустика ПЭТ**

графит 12 мм

где: 9.2.5

смета: п. 13

**Кварц**

светлый тёплый — столешница, фартук

где: 9.2.6

смета: п. 44

**Диван**

рогожка/букле беж

где: 9.2.5

смета: вар. Б

**Кресло руководителя**

кожа/экокожа карамель

где: 9.2.5

смета: вар. Б

**Табуреты**

терракота

где: 9.2.6

смета: п. 45

**Металл**

RAL 7021 — опоры, ручки, профили

где: обе

смета: —

**Свет**

2700–3000 K, Ra > 90


где: обе

смета: п. 6, 24, 25

Цвета на экране/печати — ориентировочные. Окончательно — по веерам NCS/RAL и физическим образцам, утверждённым заказчиком.

| | |
|---|---|
| **ООО «Матрёшка Проект»** | ИНТЦ МГУ «Воробьёвы горы», Образовательный кластер, 10 этаж, отм. +39.600 |
| ГИП Толубец Д. | Ремонт помещений 9.2.5 «Рабочая зона», 9.2.6 «Кофе-поинт» |
| Разраб. | **Колористика и материалы** |
| Дата: 28.10.2026 | Масштаб — · Стадия: Р · Лист: 9 · Листов: 10 |

# Ключевые размеры для разметки

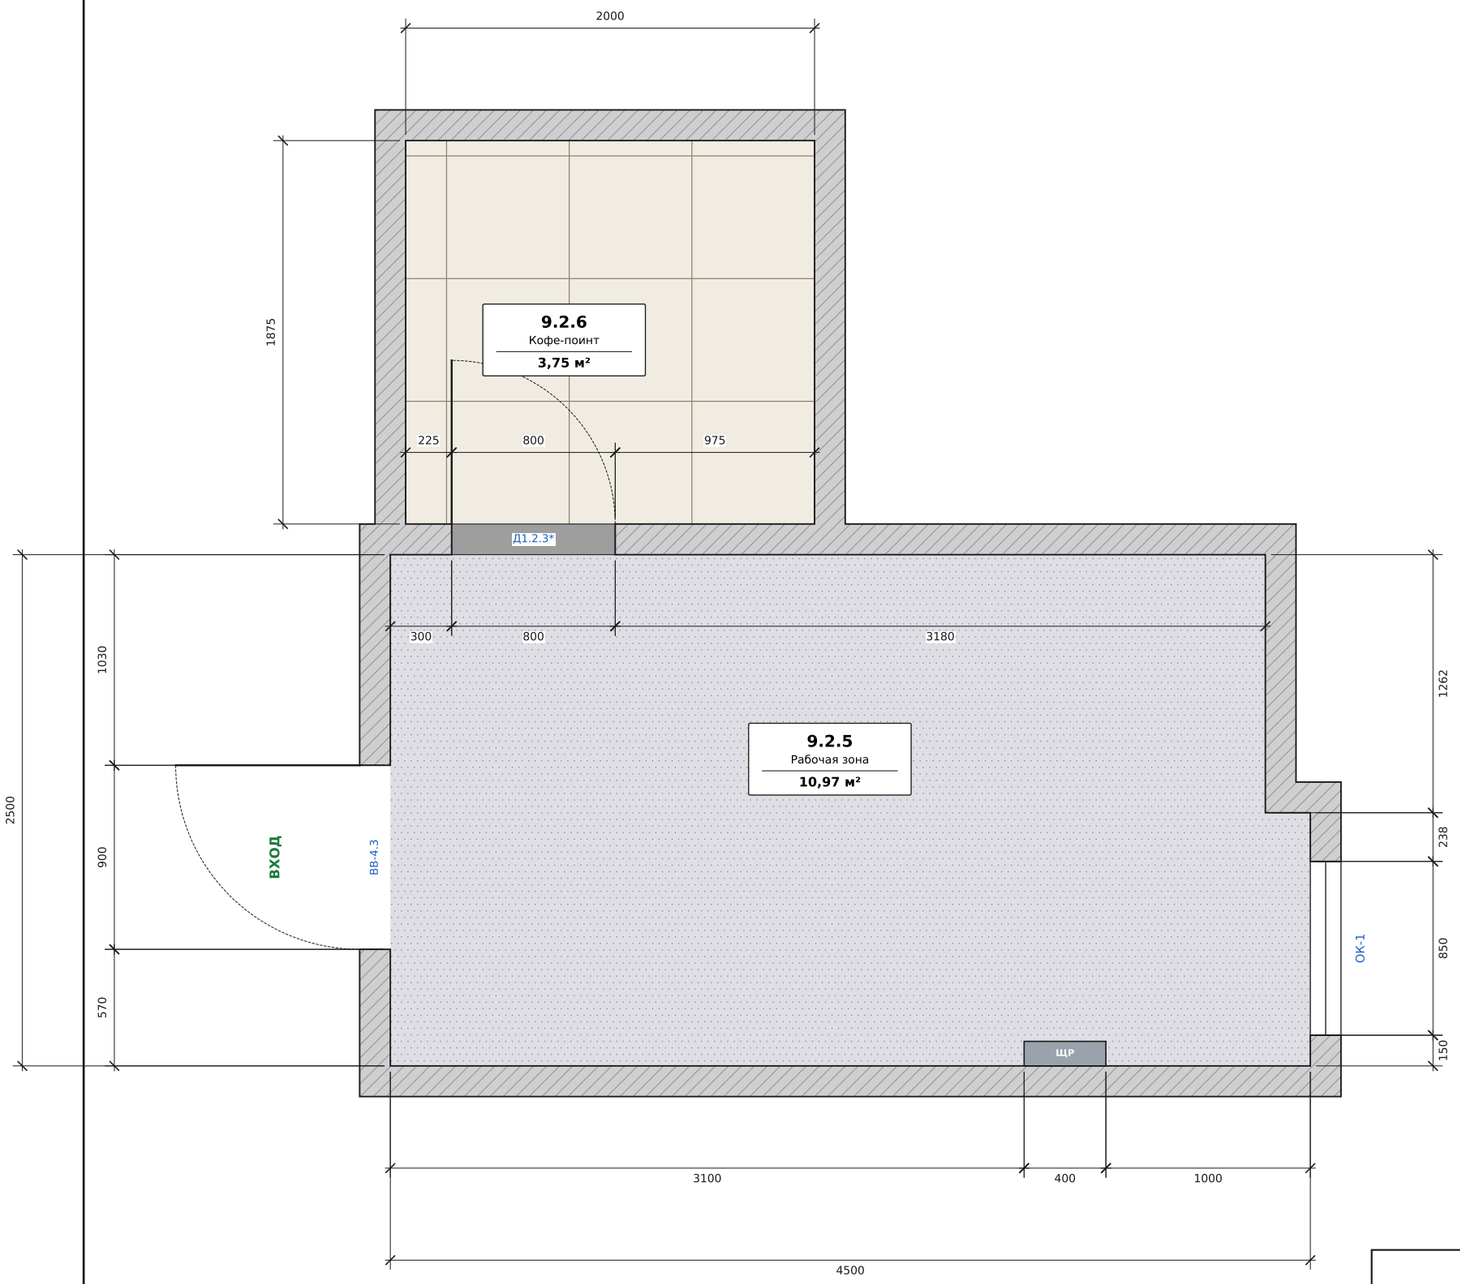


## Основные данные

| Параметр | Значение, мм |
|---|---|
| Высота стен до перекрытия | ≈ 3500 (уточнить) |
| Окно ОК-1 | ≈ 850×2500, низ 100 |
| Двери ВВ-4.3 / Д1.2.3* | 900×2100 / 800×2100 |
| ЩР | 400×600, низ 1200 (по видео) |
| Отметка этажа | +39.600 |

## Примечания

1. Все размеры — проверить контрольным обмером до начала работ и до заказа мебели.
2. Площади по смете: 9.2.5 — 11,31 м², 9.2.6 — 3,75 м²; по модели 9.2.5 — 10,97 м² (уступ фасада).

шахты ОВ / ВК (по проекту)

**ООО «Матрёшка Проект»**

ГИП Толубец Д.

Разраб.

Дата: 28.10.2026

ИНТЦ МГУ «Воробьёвы горы», Образовательный кластер, 10 этаж, отм. +39.600

Ремонт помещений 9.2.5 «Рабочая зона», 9.2.6 «Кофе-поинт»

**Ключевые размеры для разметки**

| Масштаб 1:30 | Стадия | Лист | Листов |
|---|---|---|---|
| | Р | 10 | 10 |