


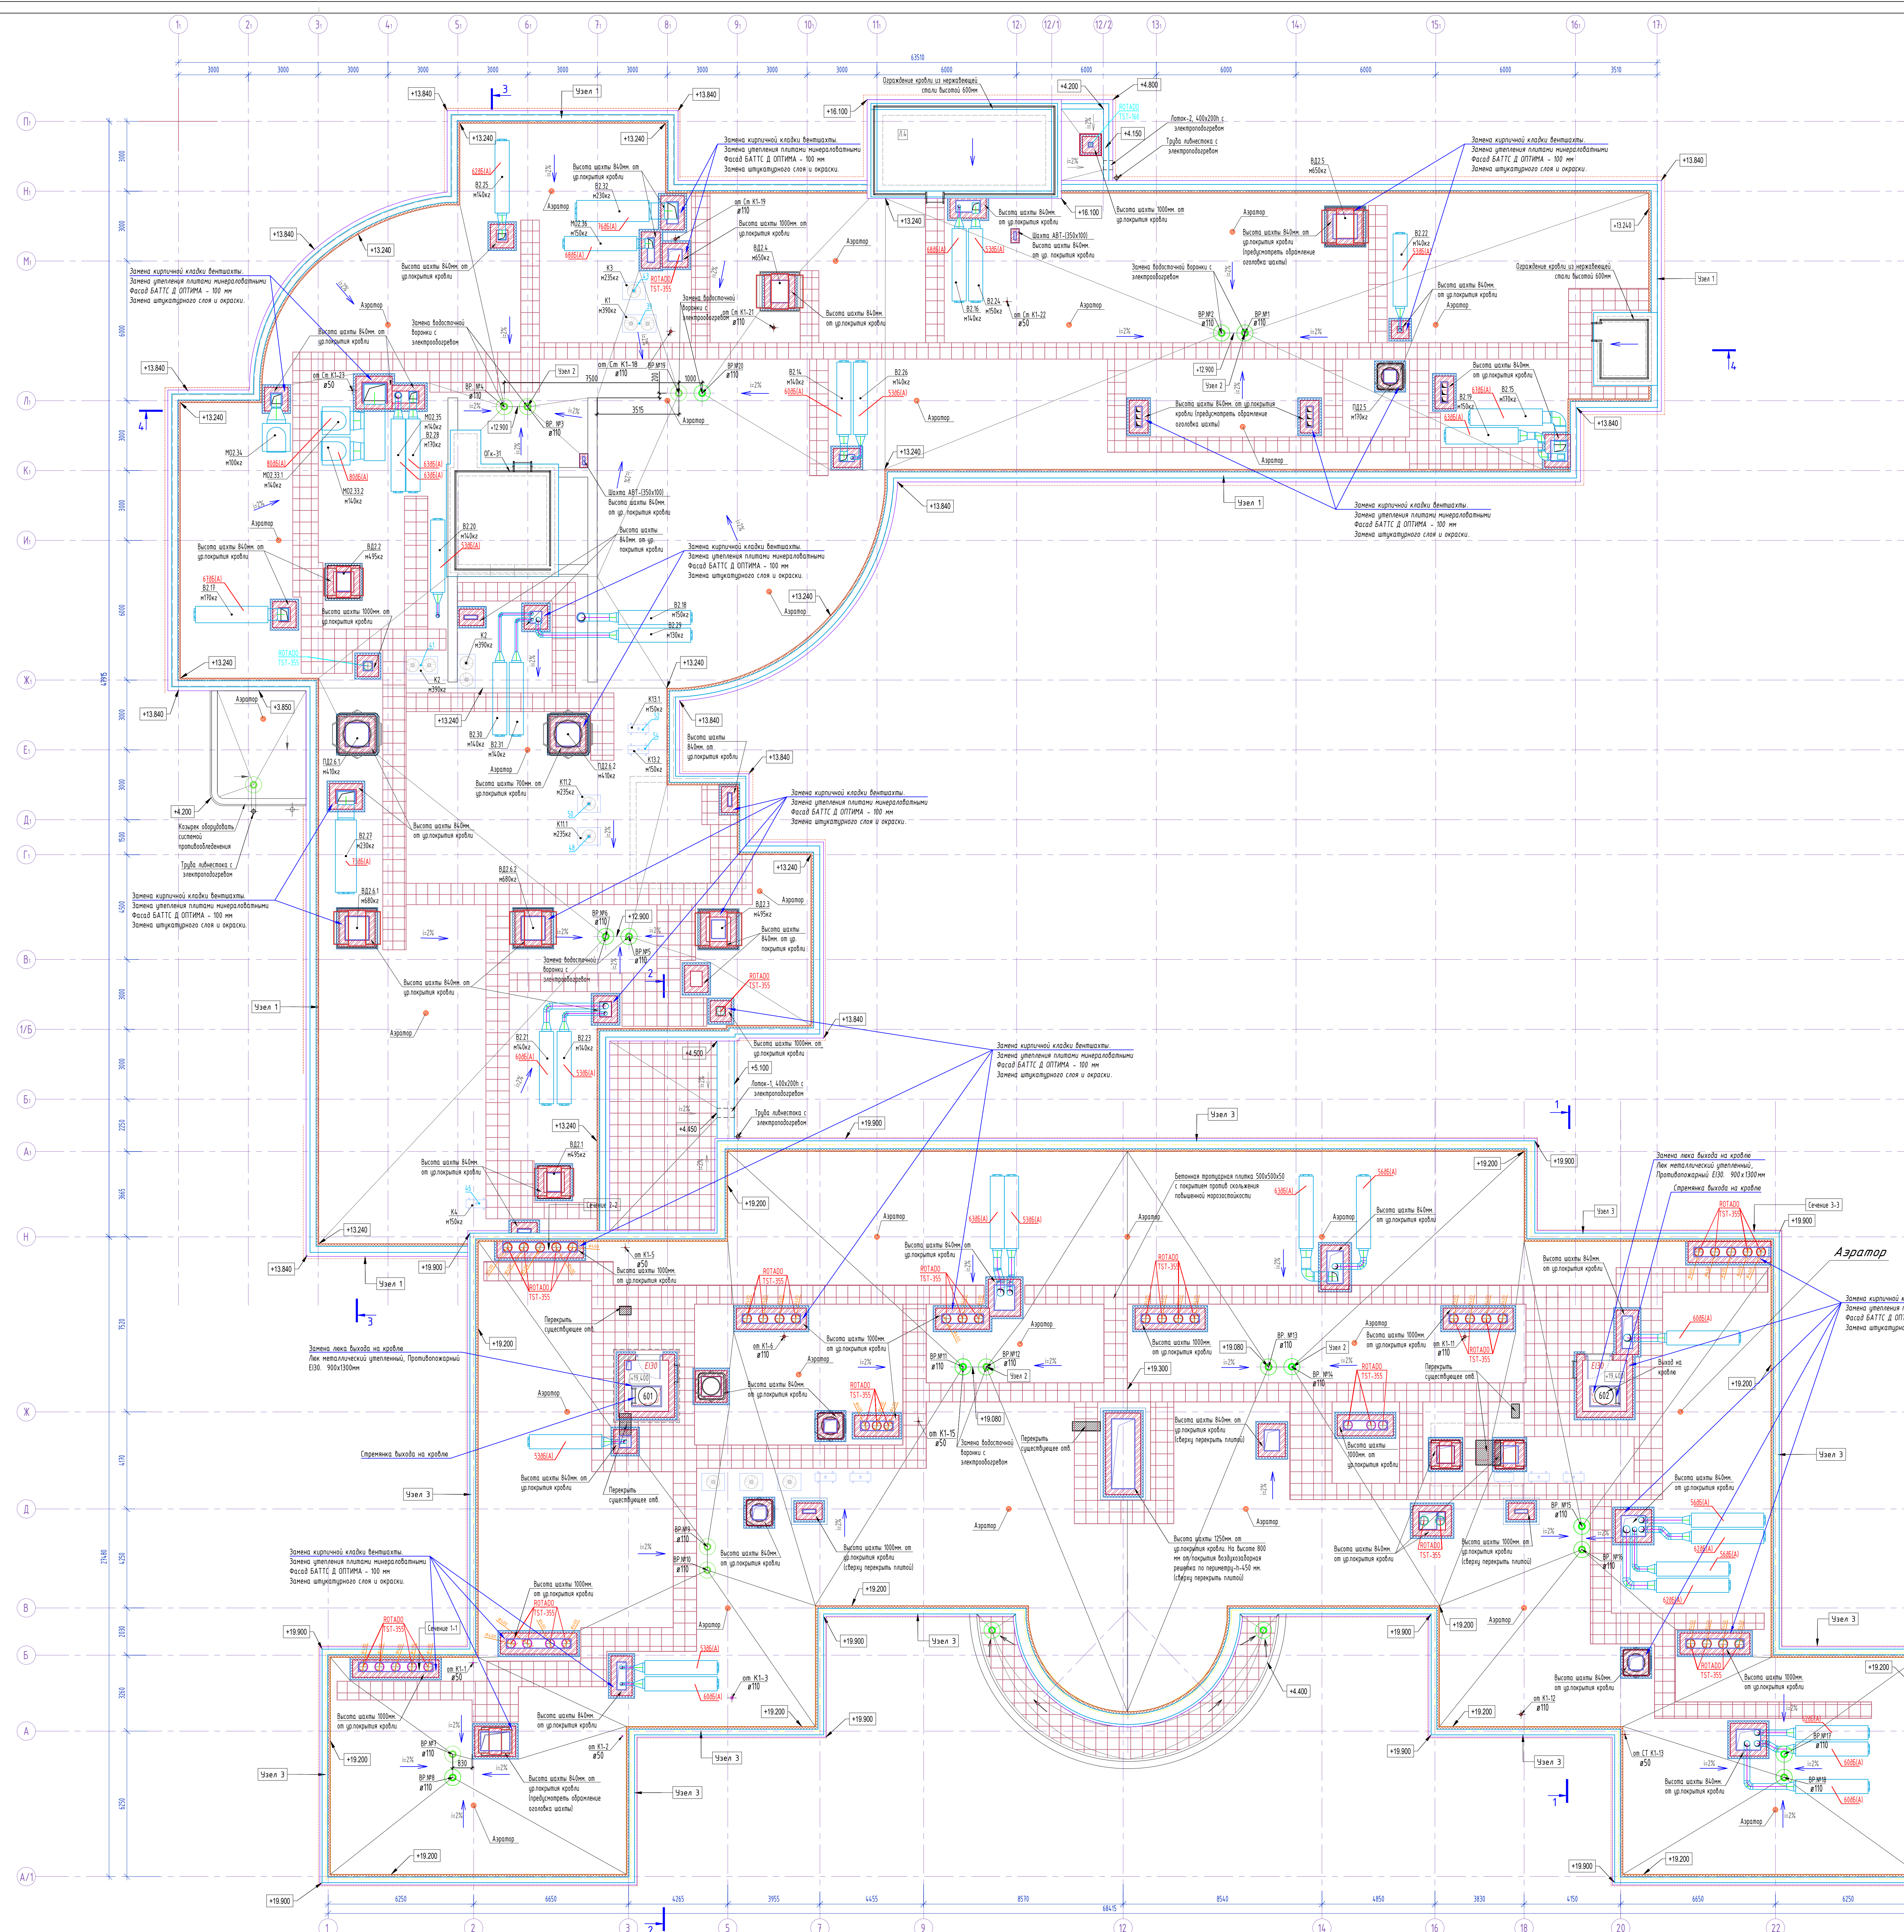


План кровли


Экспликация помещений кровли

Номер помещения	Наименование	Площадь м ²	Кол. помещений
601	Помещение выхода на кровлю	4.19	
602	Помещение выхода на кровлю	5.19	
	Всего	4.2	


Фрагмент плана кровли в осях "З/Ж"

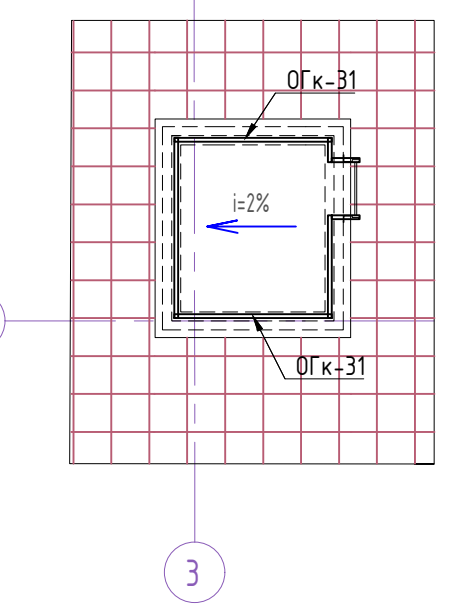

Фрагмент плана кровли в осях "20/Ж"

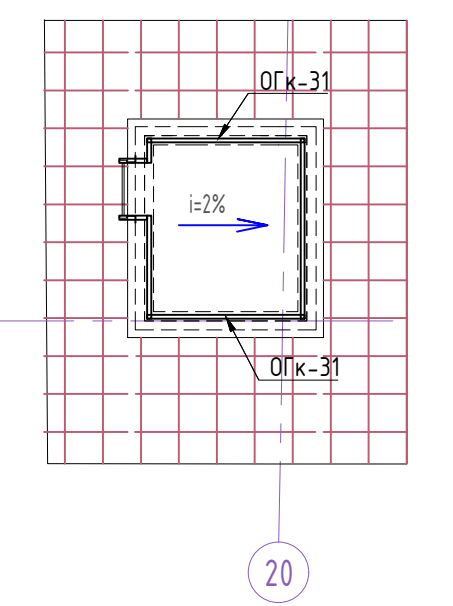


Паралет кирпичный


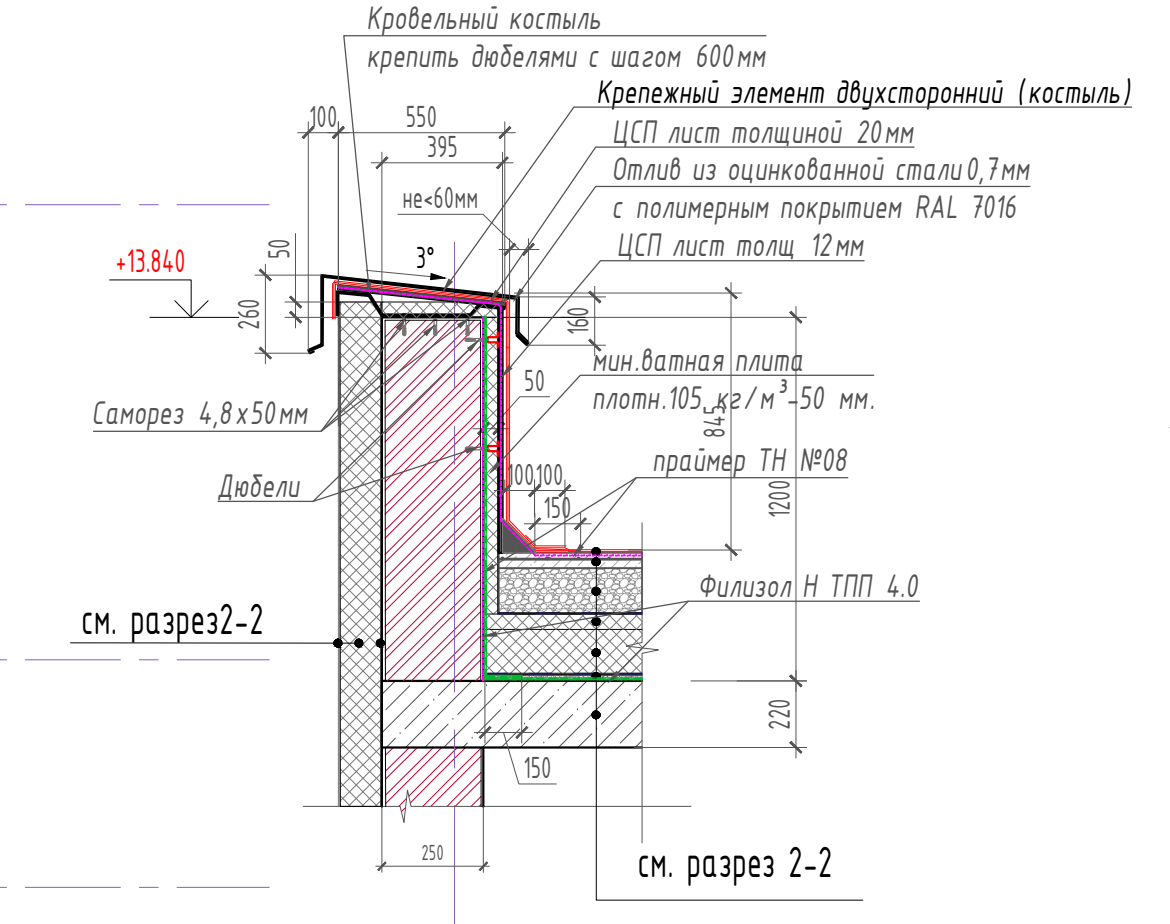


Устройство водоотведения через паралет кирпичный


Паралет из железобетона

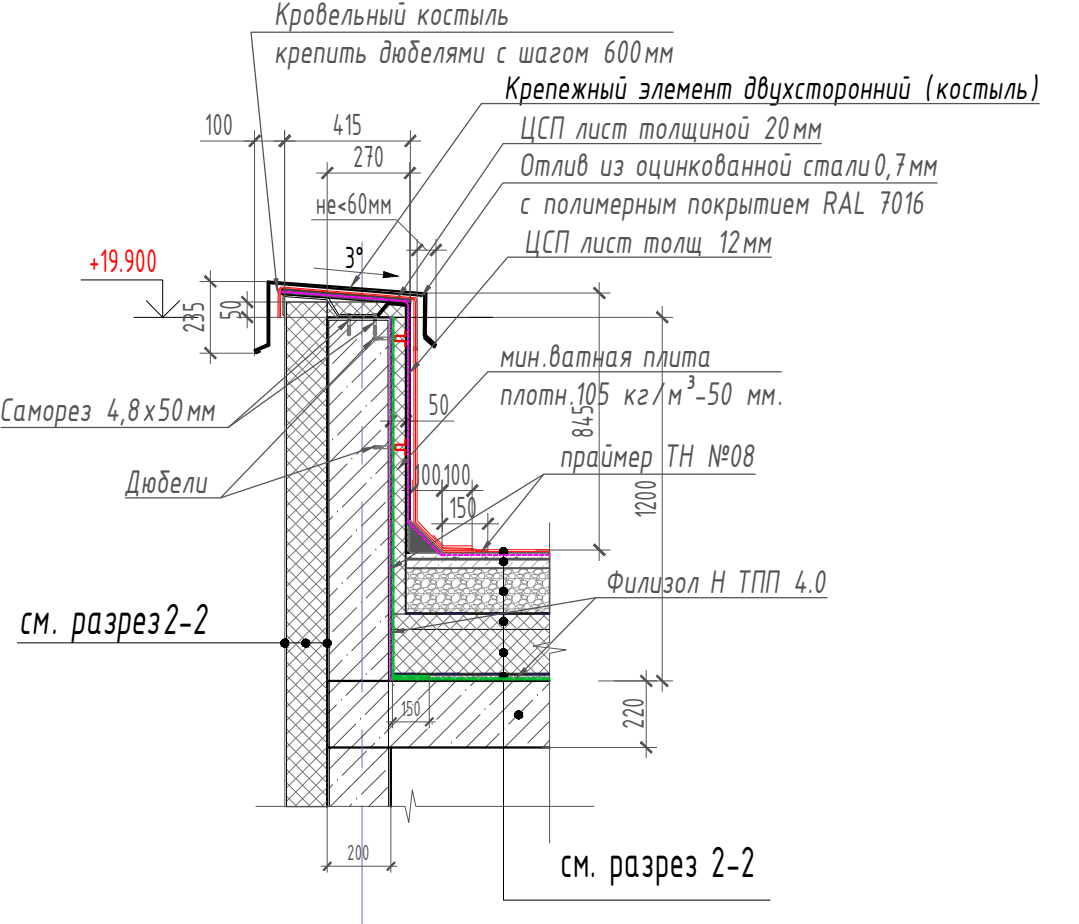


Устройство водоотведения через паралет железобетонный

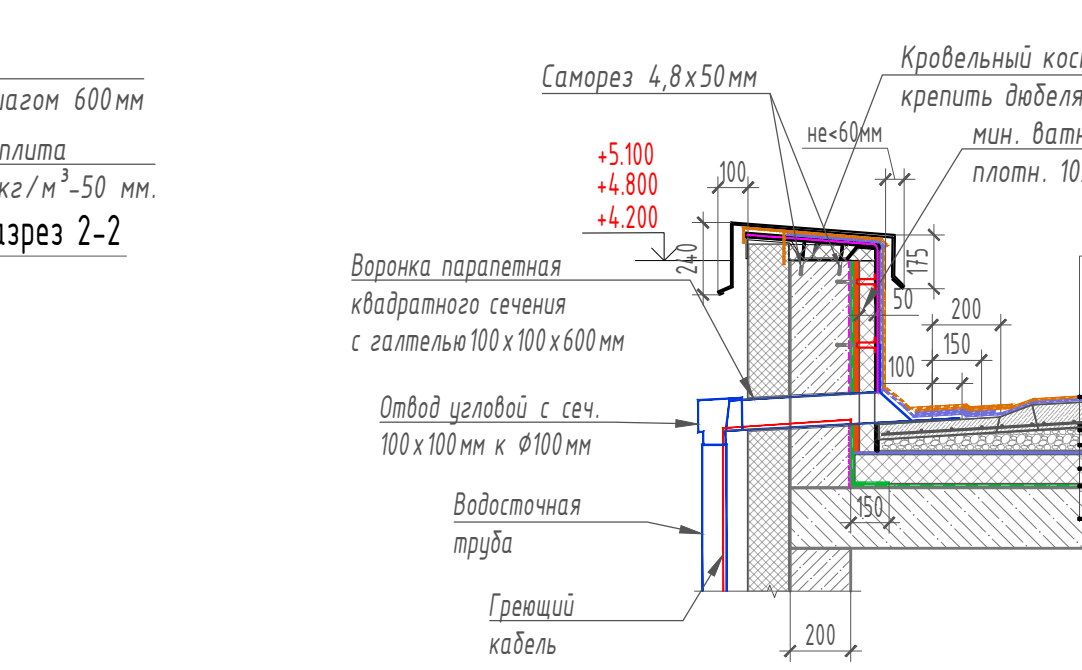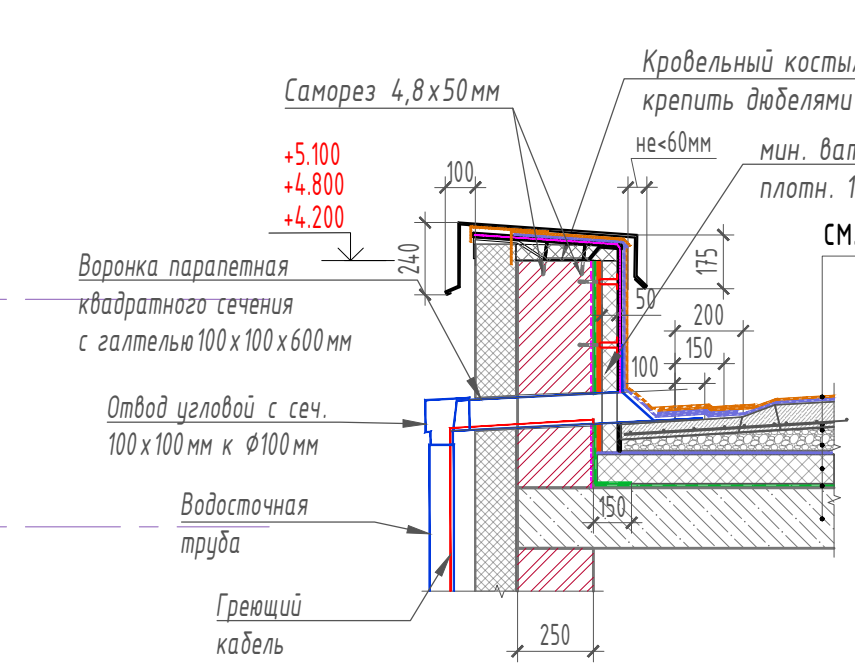


1-1

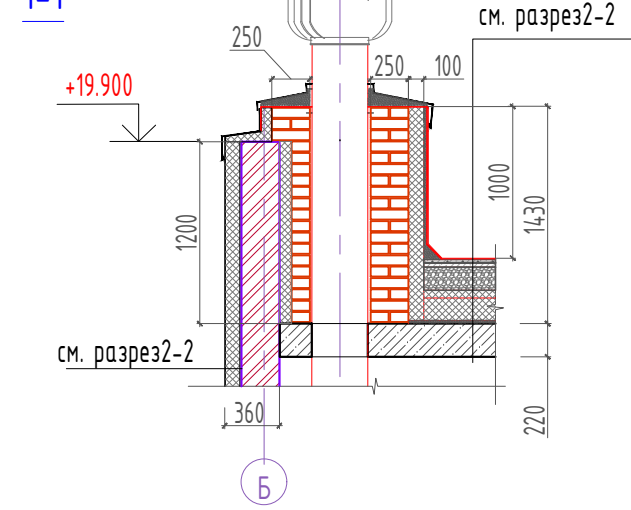



2-2

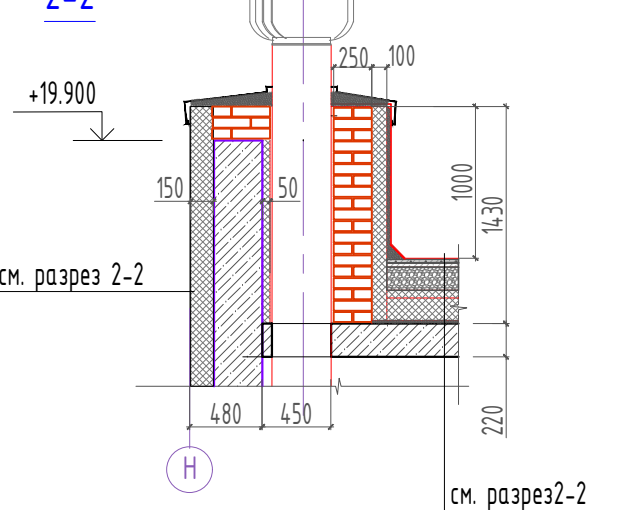

3-3

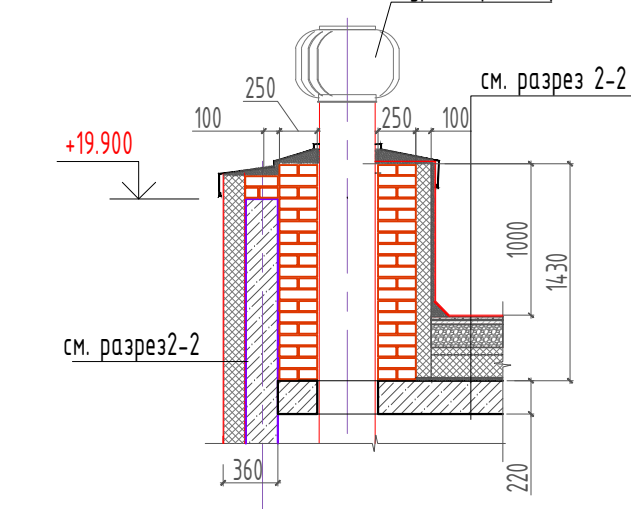

Узел 3

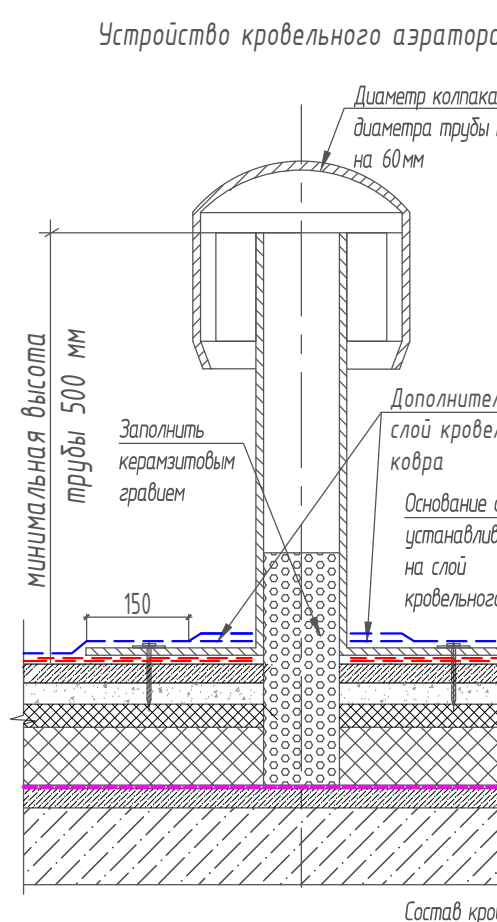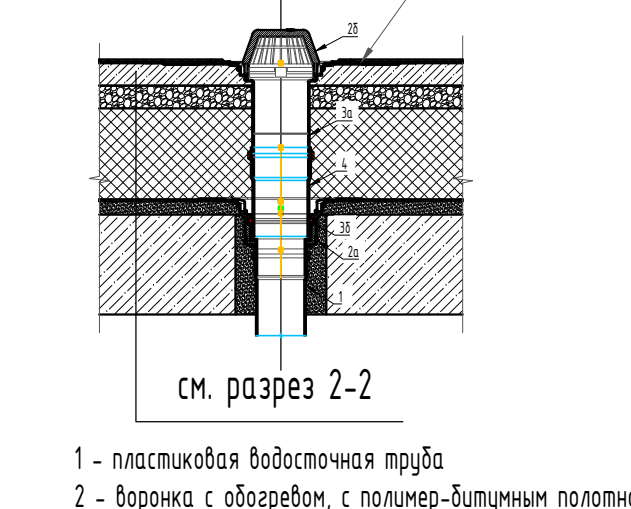

УСЛОВНЫЕ ОБОЗНАЧЕНИЯ

- Водосточная воронка (внутренний дренажный водосток)
- Направление ската кровли к выпуклому/ограниченному водостоку
- Базовая структурная линия 50х50х50 с покрытием проф. склеивания повышенной морозостойкости
- Маркировка геометрии элементов кровли, стен, перегородок
- Отметка уровня кровли
- Марка фановой трубы

ПРИМЕЧАНИЕ:
1. За условную отметку 0.000 принята отметка уровня чистого пола 1 этажа.
2. Шпалы предназначены для прокладки инженерных коммуникаций и стоек (БК, СТ, ЗМ, ЗМ), оборудуются лямками для обслуживания.

					16-25/Г-П-АР			
					Капитальный ремонт объекта "ГБОУ Школа № 429 "Скопальная гора", расположенного по адресу: г.Москва, ул. Скопальной горы 5-я, д.14.			
Изм.	Коп. экз.	Лист	№ док.	Подпись	Дата	Состав	Лист	Листов
Разработ		Авт.авт.			2020.08.04	П	13	
					Объемно-планировочные и архитектурные решения			
И. контр.	Г. ур. авт.	Л. авт.	П. авт.	Д. авт.	С. авт.	Л. авт.	Л. авт.	Л. авт.
Н. контр.	Г. ур. авт.	Л. авт.	П. авт.	Д. авт.	С. авт.	Л. авт.	Л. авт.	Л. авт.
Гит		Начальник			2020.08.04	План кровли. М1:100		
					 AZURIT			