


Сметная					
Изм.	Кол-во	Лист	№ док.	Подпись	Дата
Разраб.	Липавская	2026.07.07			
И. контр.	Губарева	2026.07.07			
ГИП	Маркова	2026.07.07			

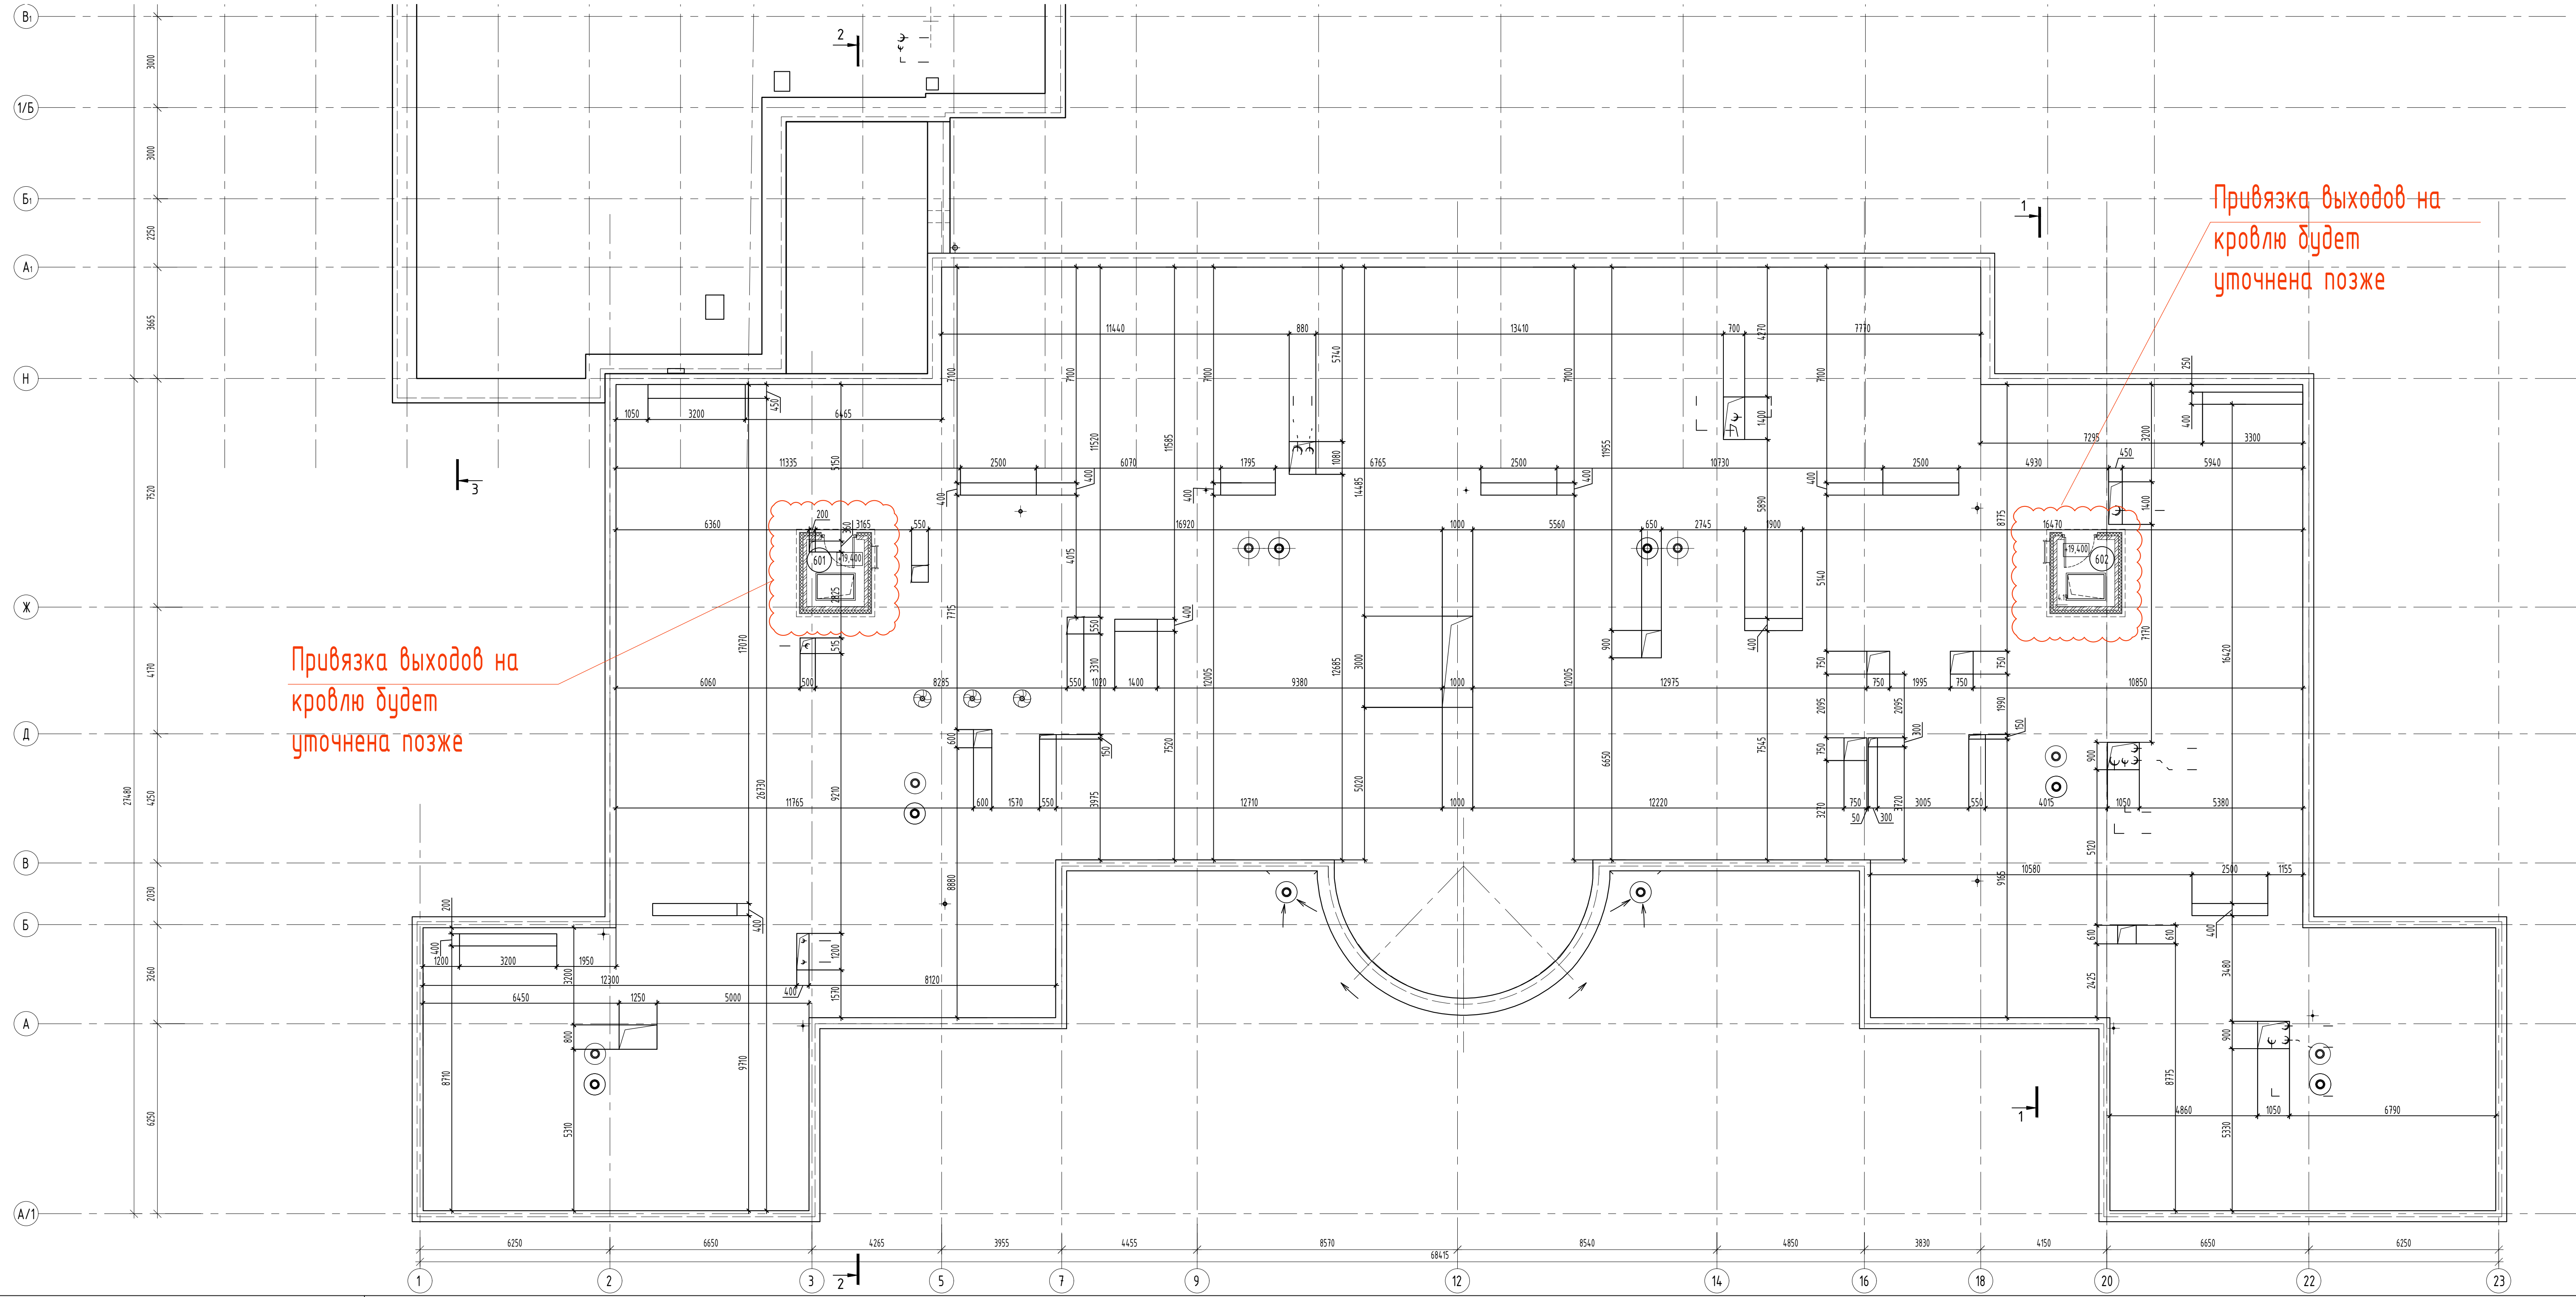

1-1

2-2

3-3

Понижение уровня гидроизоляции

УСЛОВНЫЕ ОБОЗНАЧЕНИЯ

- Водосточная воронка (внутренний организованный водосток)
- Направление ската кровли к внутреннему организованному водостоку
- Бетонная тротуарная плита 500x500x50 с покрытием против скольжения повышенной морозостойкости
- Маркировка огнестойкости заменяемых дверей, окон, перегородок
- Отметка уровня кровли
- Марка фановой трубы

1. Возможность устройства проемов в несущих стенах будет уточняться в проекте.
Размер и расположение вентиляционных шахт будет уточнен в проекте.

2. Шахты предназначенные для прокладки инженерных коммуникаций и стояков (ВК, СС, ЗОМ), оборудуются лючками для обслуживания.

3. * категорирование по взрывопожарной опасности данных помещений выполнить на этапе проектирования.

4. Марки ограждений смотреть альбом 16-25/Г-П-АР лист 61

Изм.	Кол-во	Лист	№ док.	Подпись	Дата
Разраб.	Липавская	2026.07.07			
И. контр.	Губарева	2026.07.07			
ГИП	Маркова	2026.07.07			

16-25/Г-П-АР

Капитальный ремонт объекта "ГБОУ Школа № 429 "Соколиная гора", расположенного по адресу: г.Москва, ул. Соколиной горы 5-я, д.14

Архитектурно-планировочные решения

Стадия Лист Листов

Р

План кровли. М1:100

АЗУРИТ

ФОРМАТ А0