





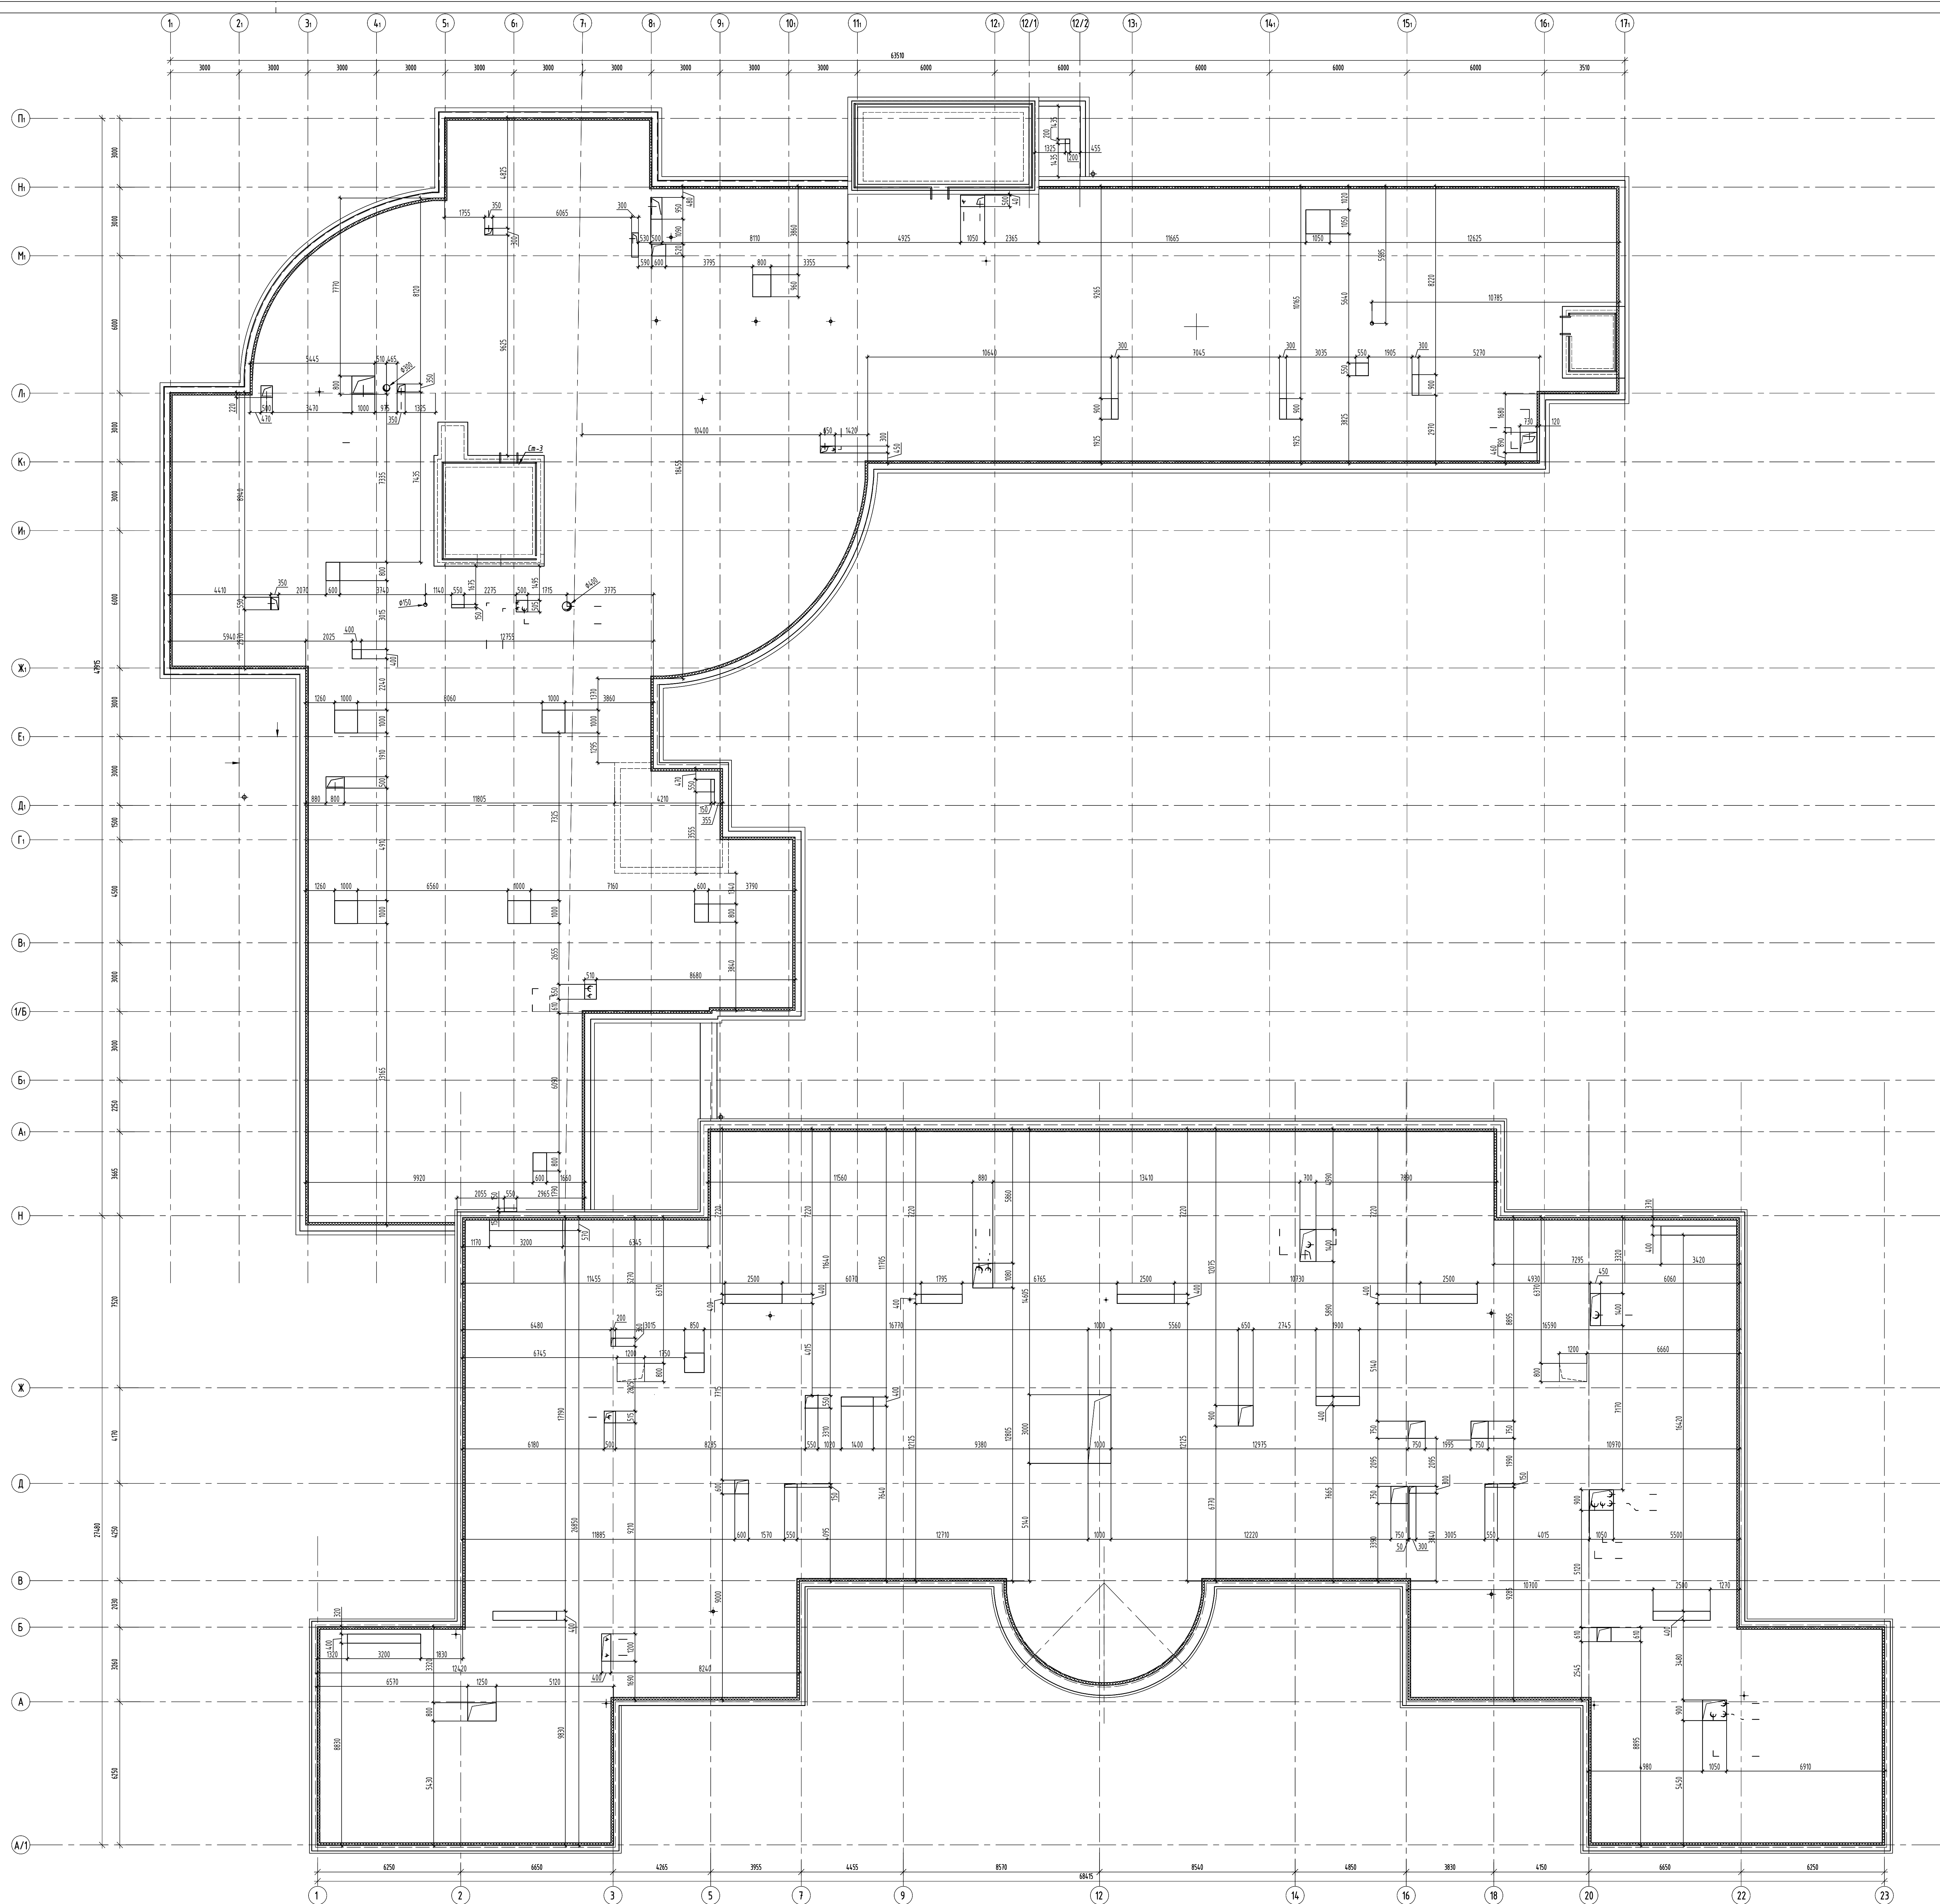


Номер помещения	Наименование	Площадь м2	Кол. помещений
601	Помещение выхода на кровлю	4.19	
602	Помещение выхода на кровлю	5.19	
	Всего	4.2	

Фрагмент плана кровли в осях
20/Ж

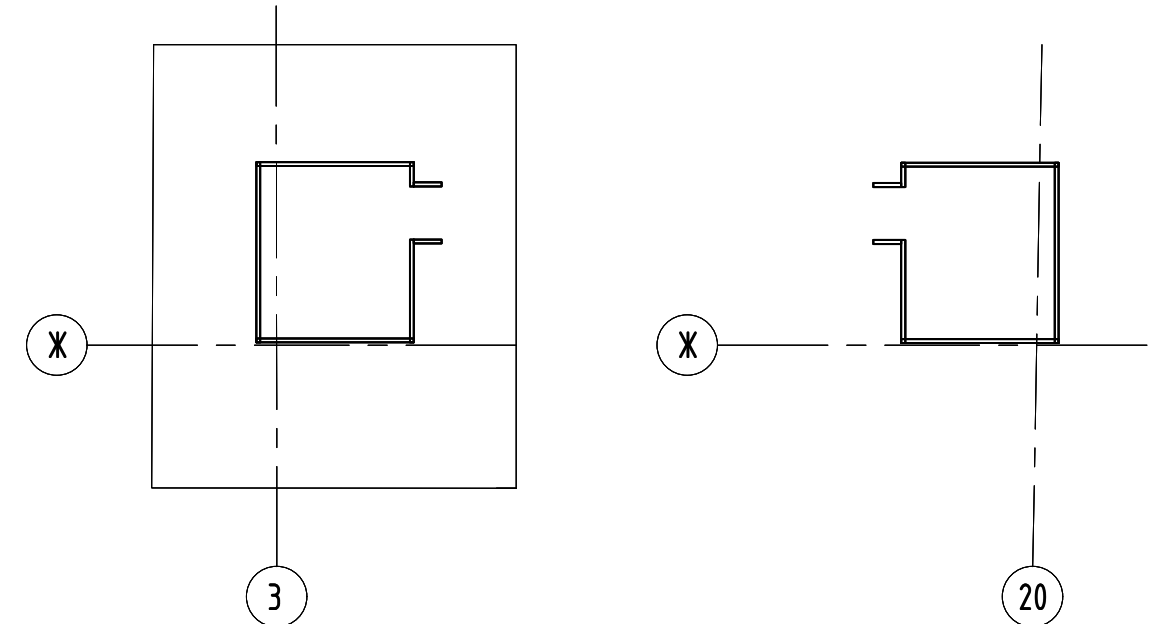

Паралел кургачный.

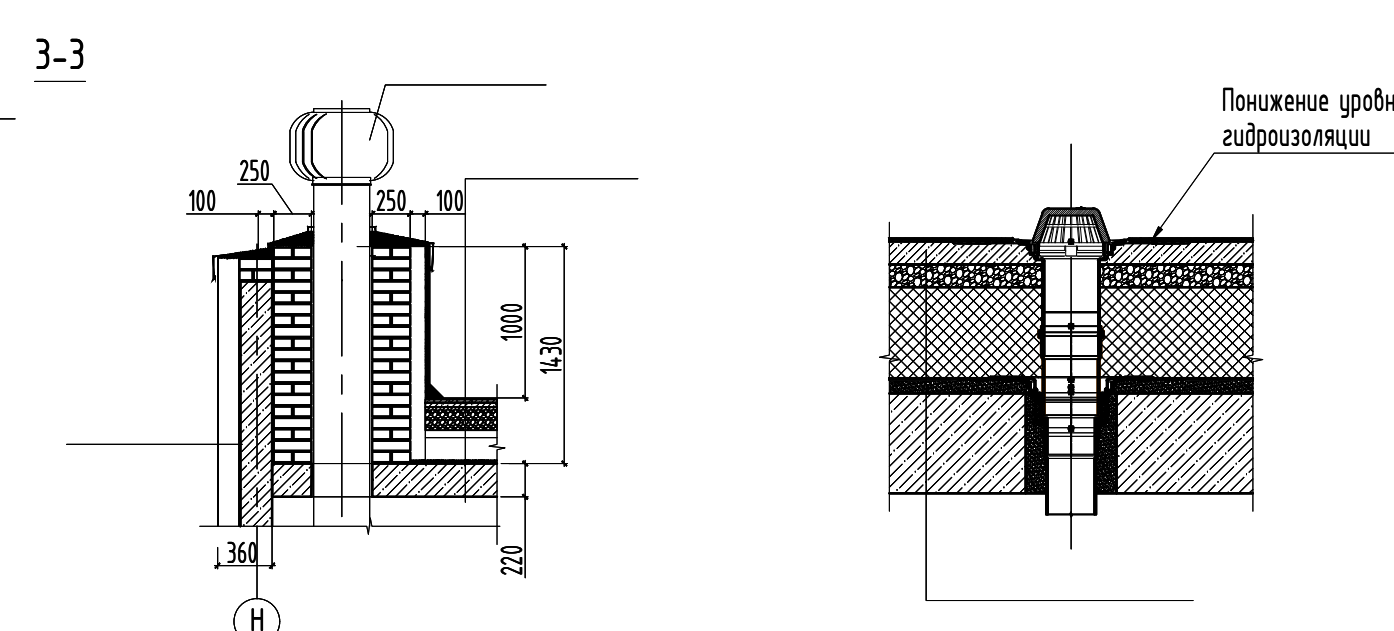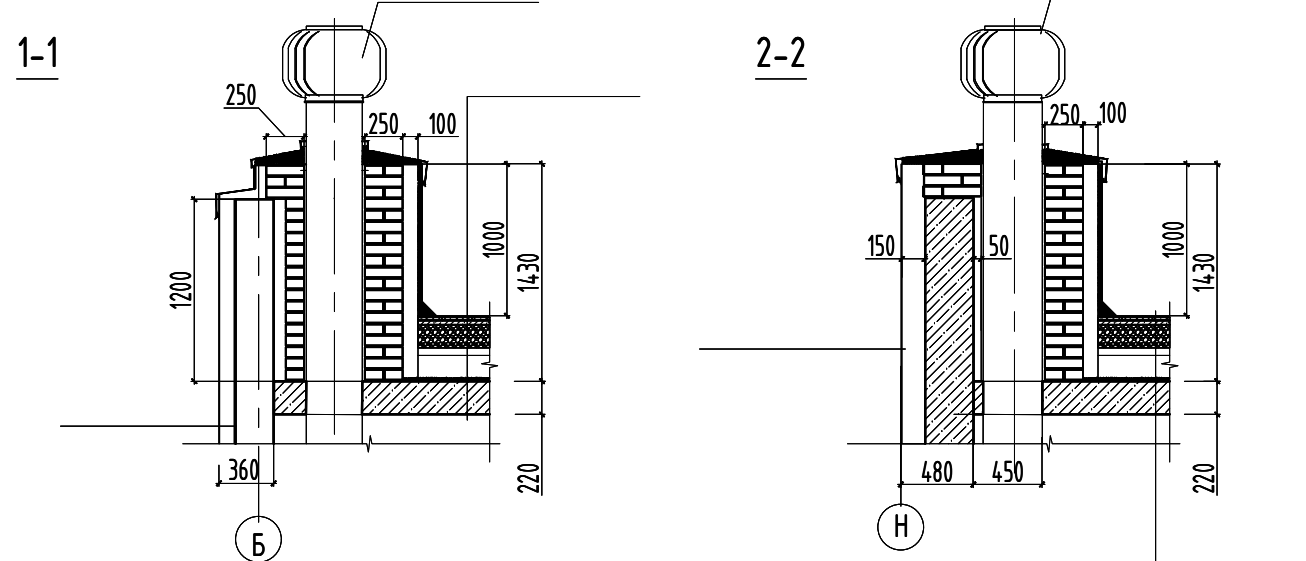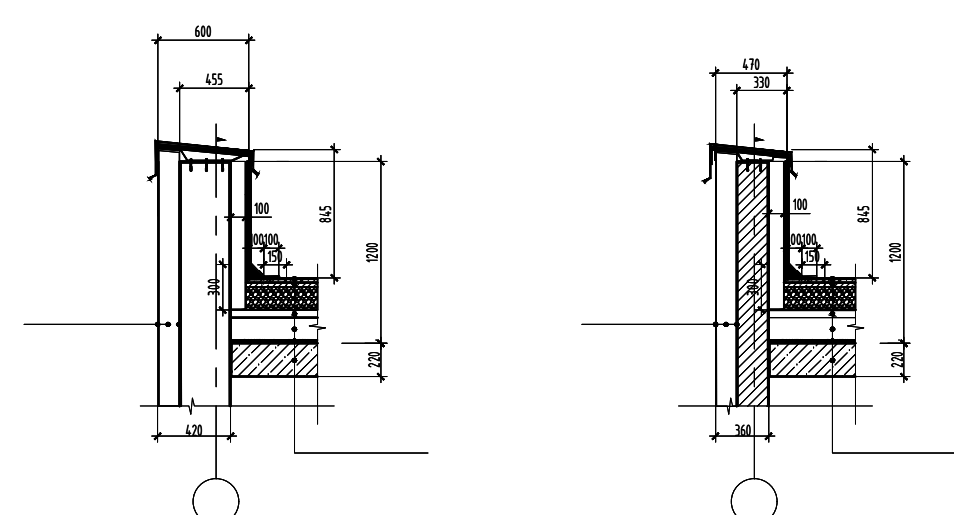

	-Водосточная воронка (внутренний организованный водосток)
	-Направление ската кровли к внутреннему организованному водостоку
	-Бетонная прутяжная плита 500х500х50 с покрытием против скольжения повышенной износостойкости
	-Маркировка осязательности замечания дверей, окон, перегородок
	-Ометка уровня кровли
	-Марка фактовой пробы

E30/E130/E1W30

1. Возможность устройства проемов в несущих стенах будет уточняться в проекте.
Размер и расположение вентиляционных шахт будет уточнен в проекте.
2. Шахты предназначение для прокладки инженерных коммуникаций и стояков (ВК, СС, ЗОМ), оборудуются личиками для обслуживания.
3. ★ категорирование по взрывопожарной опасности данных помещений выполнить на этапе проектирования.
4. Марки ограждений смотреть альбом 16-25/Г-1-АР лист 61

					16-25/Г-П-АР		
					Капитальный ремонт объекта "БОУ Школа № 429 "Семиланная зора", расположенного по адресу: г.Москва, ул. Семиланской горы 5-я, 8/16		
					Архитектура-планировочные решения		
					Сводка	Лист	Листов
					р		
И. комп.	Губарева			2020.03.08	План кровли. М:100		
ГМТ	Михайлова			2020.03.08			
					 AZURIT		