


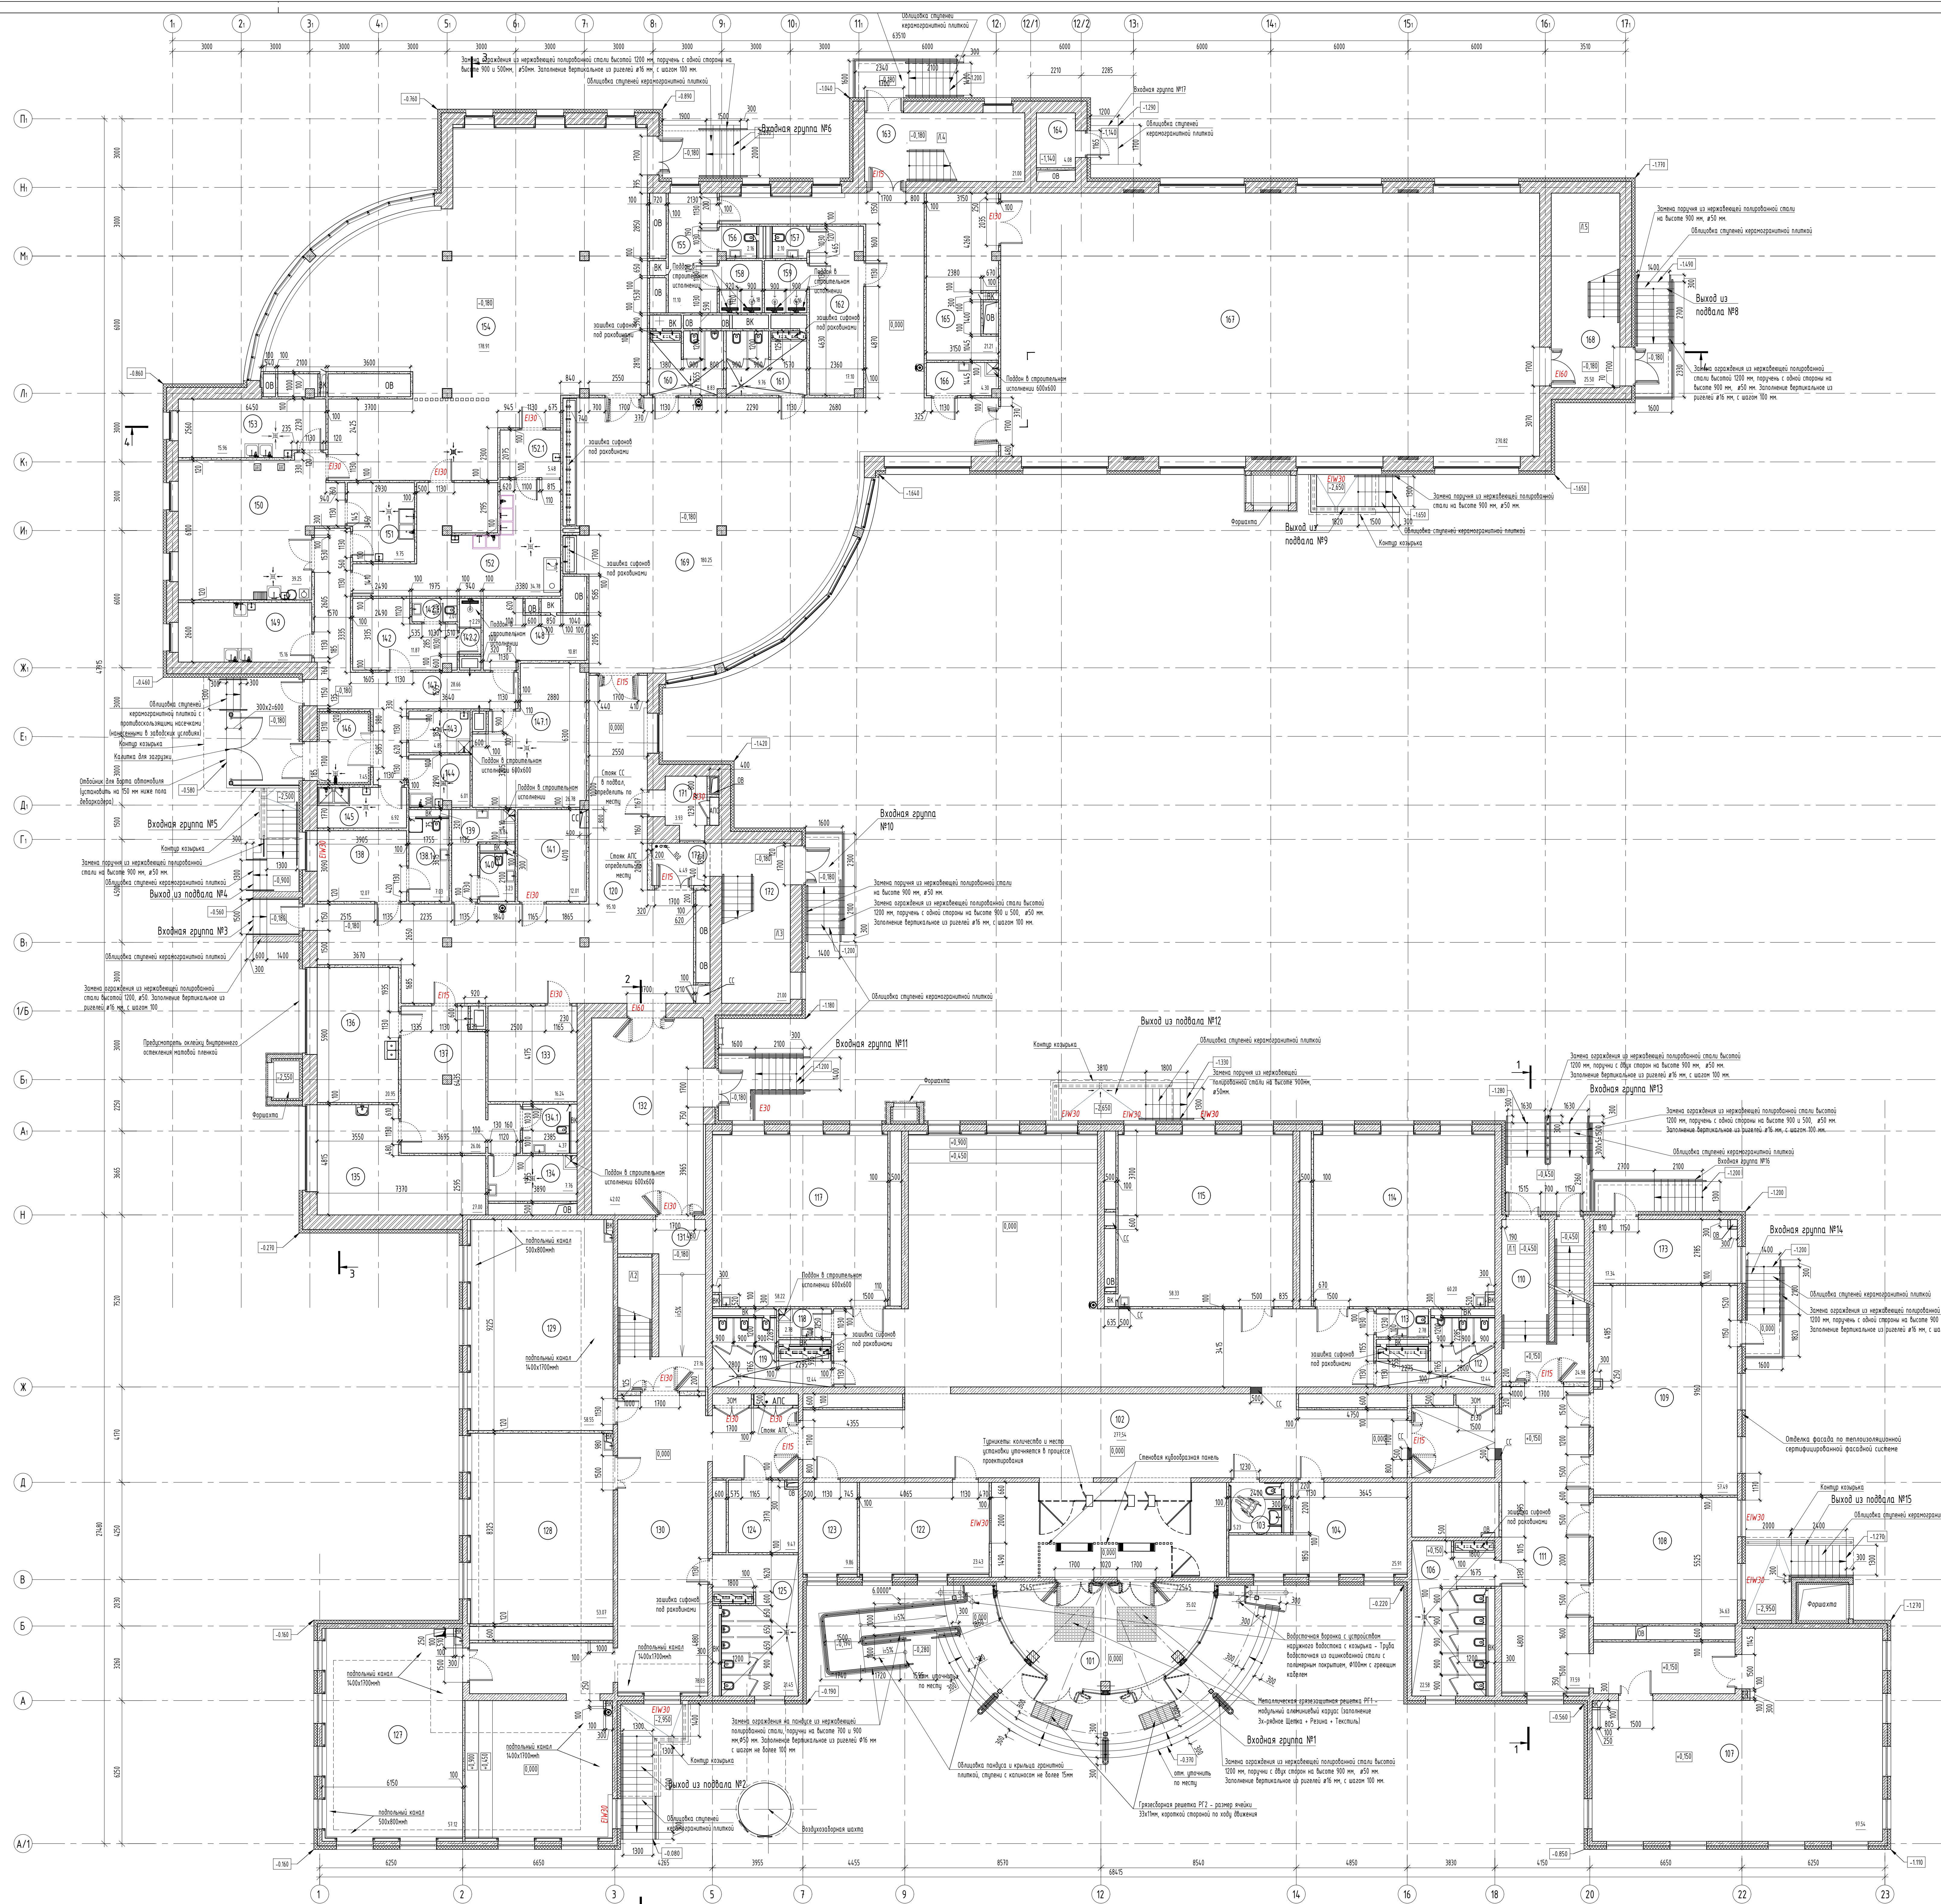


Номер помещения	Наименование	Площадь, м ²	Кол-во помещений
101	Танбур	35,02	
102	Коридор с перегородкой	27,54	
103	Санитар для МН	5,23	
104	Амбиспортивный кабинет тип 1 (начальная школа)	52,91	
106	Санитар для девочек (начальная школа)	23,25	
107	Гардеробная для обучающихся (основная и старшая школа)	97,54	
108	Гардеробная для обучающихся (основная и старшая школа)	35,25	
109	Гардеробная для обучающихся (начальная школа)	574,69	
110	Лестничная клетка (ЛК)	24,50	
111	Коридор	77,66	
112	Санитар для мальчиков (начальная школа)	12,44	
113	Санитар для персонала	2,78	
114	Учебные кабинеты (начальная школа)	60,20	
115	Учебные кабинеты (начальная школа)	58,33	
117	Учебные кабинеты (начальная школа)	58,62	
118	ПСИ	12,78	84
119	Санитар для девочек (начальная школа)	22,44	
120	Коридор с перегородкой (основная и старшая школа)	25,10	
122	Комната охраны (с диспетчерской турпункта)	93,43	
123	Гардеробная комната (для учителей)	9,86	
124	Помещение связи	9,47	84
125	Санитар для мальчиков (начальная школа)	21,93	
127	Учебные кабинеты (начальная школа)	57,26	
128	Учебные кабинеты (начальная школа)	53,31	
129	Учебные кабинеты (начальная школа)	58,81	
130	Коридор с перегородкой	115,57	
131	Лестничная клетка Тип П2	27,78	
132	Вестибюль	42,02	
133	Электрощитовая	16,24	83
134	Место для противопожарной дезинфицирующей распылатор и хранения (форменные шлемы, предельные значения для помещений) медико-санитарного назначения	7,36	84
134.1	Углубленная мебель	1,71	
135	Кабинет врача	27,00	
136	Процедурный (профилактический) кабинет	20,88	
137	Коридор	26,06	
138	Комната инструктора	12,87	
138.1	Санитар с душем	7,03	
139	ПСИ	6,79	84
140	Санитар для персонала	3,27	
141	Помещение связи	12,01	83
142	Помещение для персонала	11,89	
142.1	Санитар для персонала	2,09	
142.2	Душевая	2,29	
143	ПСИ	4,85	84
144	Помещение для временного хранения пахучих отходов	6,01	84
145	Кабинет и моечная обуви (пары)	6,92	84
146	Защитный щит	4,15	84
147	Коридор	28,66	
147.1	Помещение с холодильным оборудованием	26,78	83
148	Кабинет сушки предметов	10,81	83
149	Дезинфекционный щит	15,15	83
150	Горячий щит	39,26	83
151	Моечная для кухонной посуды	9,75	д
152	Моечная для столовой посуды	34,78	д
152.1	Предмоечная	5,48	д
153	Холодный щит	15,96	83
154	Общественный зал	118,91	
155	Раздевальня для мальчиков	10,30	
156	Санитар для мальчиков	2,36	
157	Санитар для девочек	2,10	
158	Душевые для мальчиков	4,75	
159	Душевые для девочек	4,15	
160	Санитар для мальчиков	8,71	
161	Санитар для девочек	9,76	
162	Раздевальня для девочек	11,30	
163	Лестничная клетка (ЛК)	21,00	
164	Техническое помещение	4,16	84
165	Сараи	21,21	83
166	ПСИ	4,20	84
167	Универсальный спортивный зал	278,82	
168	Лестничная клетка (ЛК)	25,50	
169	Коридор с перегородкой (основная и старшая школа)	281,24	
171	Тех. помещение	3,33	84
172	Лестничная клетка (ЛК)	21,00	
172.1	Танбур	4,48	
173	Электрощитовая	17,34	83
Всего		2667,3	

- Существующие монтажные х/б стены
- Замена перерезки из заготовочных блоков В/Б/С/250х100х100/В/Б/С по ГОСТ Р 10522-02, поли на клею с приращением базальной сеткой, сетку
- Замена перерезки из заготовочных блоков В/Б/С/250х100х100/В/Б/С по ГОСТ Р 10522-02, поли на клею с приращением базальной сеткой, сетку
- Замена перерезки из скарпелени односторонней толщиной 100мм
- Замена перерезки из скарпелени односторонней толщиной 100мм
- Замена остекленные перерезки
- Замена перерезки синтетическая (волоконная) с обрешеткой и необходимой фурнитурой

1. Возможность устройства проемов в несущих стенах будет уточняться в проекте.
2. Размер и расположение вентиляционных шахт будет уточнен в проекте.
3. Шахты предначиненные для прокладки инженерных коммуникаций и стоек ЛВК, СС, ЗОН оборудуются лючками для обслуживания.
4. ★ категорирование по взрывопожарной опасности данных помещений выполнить на этапе проектирования.
4. Марки ограждений смотреть альбом 16-25/Г-П-АР лист 61

						16-25/Г-П-АР								
						Капитальный ремонт объекта "ГБОУ Школа № 429 "Соколовая гора", расположенного по адресу: г.Москва, ул. Соколовой горы 5-в, д.14								
						Архитектурно-планировочные решения								
						<table><tr><td>Статус</td><td>Лист</td><td>Листов</td></tr><tr><td>Р</td><td></td><td></td></tr></table>			Статус	Лист	Листов	Р		
Статус	Лист	Листов												
Р														
И.м.	А.м.д.	Лист	№ док	Подпись	Дата									
Разреш.	Литовская				02.06.07									
И.м. контр.	Губарева				06.06.07									
Гипр.	Маркова				06.06.07									
						Лист 1 из 1. М.100								
						 АЗУРИТ								

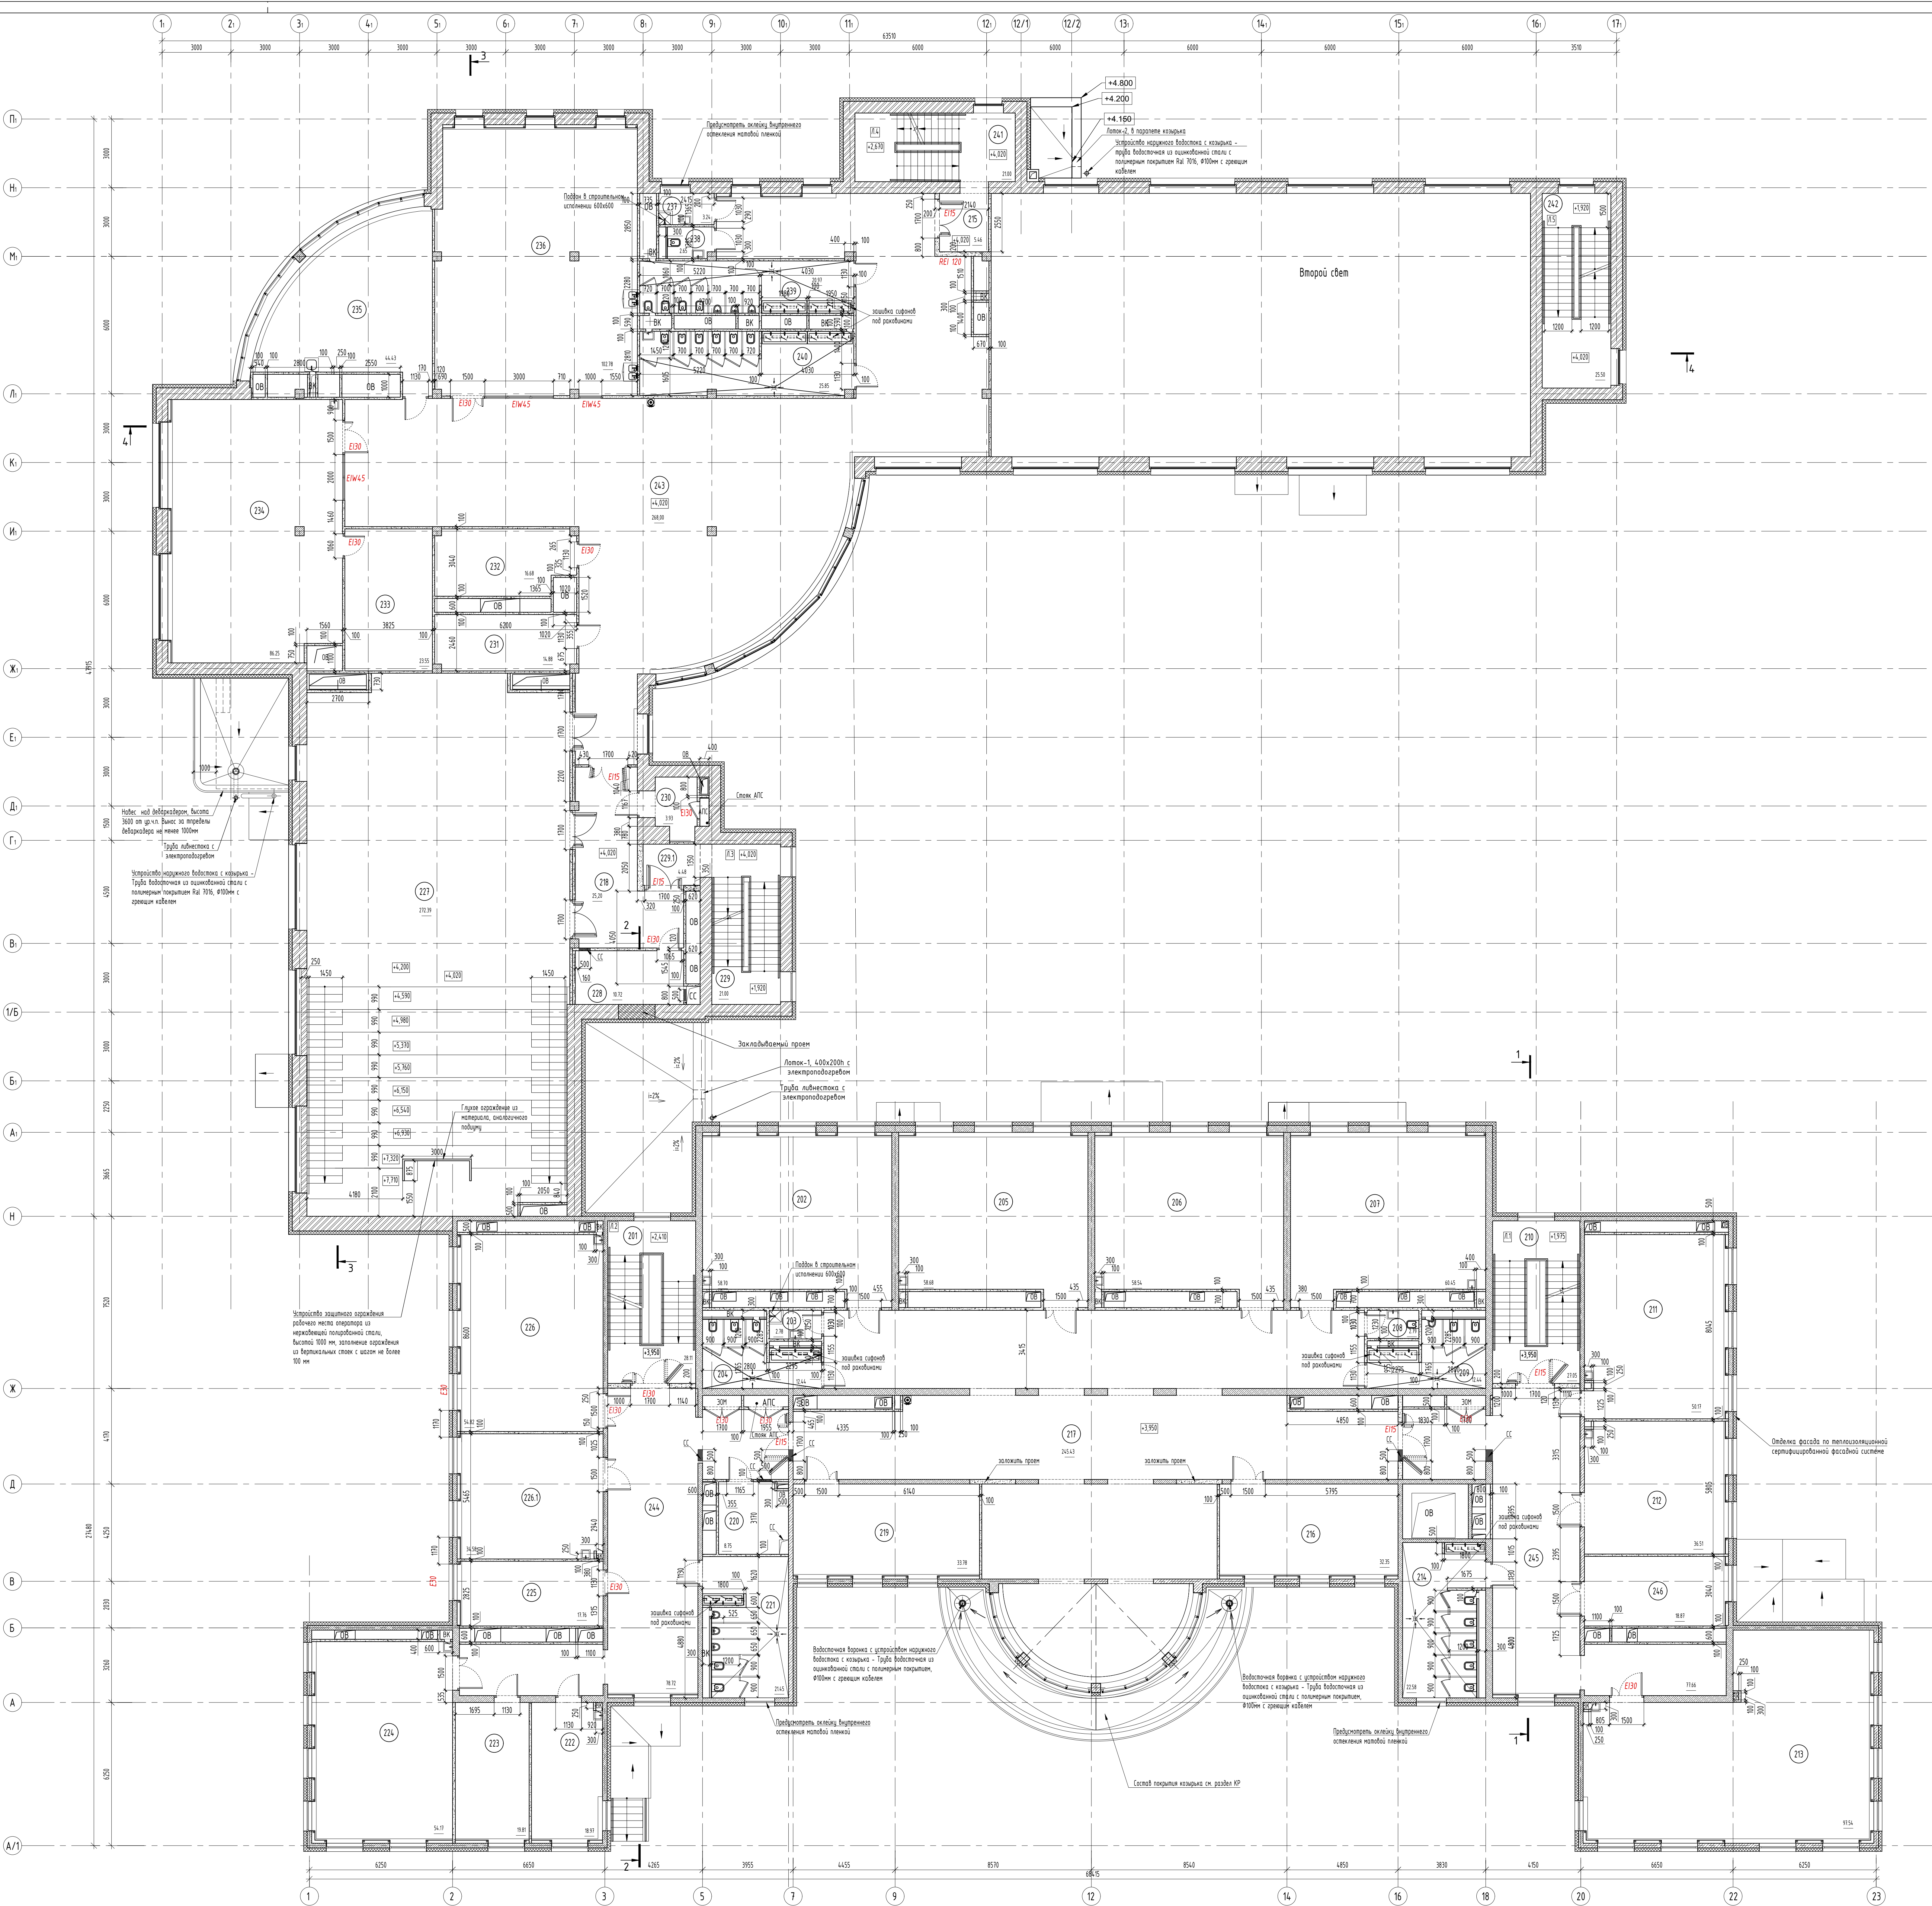


Экспликация помещений 2-го этажа

Номер помещения	Наименование	Площадь, м2	Кол. помещ.
201	Лестничная клетка Тип Н2	28,82	
202	Учебные кабинеты (начальная школа)	58,70	
203	ПМ	2,78	В4
204	Санузел для девочек (начальная школа)	12,73	
205	Учебные кабинеты (начальная школа)	58,68	
206	Учебные кабинеты (начальная школа)	58,54	
207	Учебные кабинеты (начальная школа)	60,45	
208	Санузел для персонала	2,79	
209	Санузел для мальчиков (начальная школа)	12,44	
210	Лестничная клетка (ЛП)	27,05	
211	Учебные кабинеты (начальная школа)	50,17	
212	Кабинет иностранного языка (начальная школа)	36,51	
213	Лабораторно-исследовательский комплекс для изучения астрономии (п.п.)	97,02	В3
214	Санузел для девочек (начальная школа)	23,25	
215	Танцевальный зал	5,46	
216	Кабинет для индивидуальных занятий с малой группой	32,35	
217	Коридор с рекреацией (начальная школа)	245,43	
218	Коридор	25,20	
219	Кабинет для индивидуальных занятий с малой группой	33,78	
220	Помещение связи	8,75	В4
221	Санузел для мальчиков (начальная школа)	21,45	
222	Кабинет для индивидуальных занятий, в т.ч. с коррекционными педагогами	18,97	
223	Кабинет для индивидуальных занятий, в т.ч. с коррекционными педагогами	19,22	
224	Учебные кабинеты (начальная школа)	54,17	
225	Классовый кабинет творческой мастерской	11,75	В3
226	Творческая мастерская	54,82	В3
226.1	Кабинет иностранного языка (начальная школа)	34,58	
227	Многофункциональное пространство с функцией актового зала (с эстрадой в уровне пола)	272,39	
228	Классовый кабинет	10,72	В3
229	Лестничная клетка (ЛП)	21,00	
229.1	Танцевальный зал	4,48	
230	Тех. помещение	3,93	В4
231	Архитектурная	14,75	
232	Классовый кабинет	16,65	В3
233	Кабинет материальной технологии тип 2	23,55	В3
234	Кабинет с рабочим пространством для учителей тип 1 (начальная школа)	86,25	В3
235	Кабинет с рабочим пространством для учителей тип 1 (начальная школа)	44,43	
236	Кабинет материальной технологии тип 1	102,78	В3
237	ПМ	3,24	В4
238	Санузел для персонала	2,65	
239	Санузел для мальчиков (основная и старшая школа)	20,97	
240	Санузел для девочек (основная и старшая школа)	25,85	
241	Лестничная клетка (ЛП)	21,00	
242	Лестничная клетка (ЛП)	25,50	
243	Коридор и рекреация (основная и старшая школа)	268,00	
244	Коридор	78,72	
245	Коридор	77,66	
246	Административный кабинет	18,87	
	Всего	2245,3	

УСЛОВНЫЕ ОБОЗНАЧЕНИЯ

- Существующие материалы и/или стены
- Замена перегородки из газобетонных блоков 1/625x250x100/1500/85,0 по ГОСТ Р 76522-2022, толщиной 100мм на клею с армированием базальтовой сеткой, оштукатуренная
- Замена перегородки из газобетонных блоков 1/625x250x100/1500/85,0 по ГОСТ Р 76522-2022, толщиной 200мм на клею с армированием базальтовой сеткой, оштукатуренная
- Замена перегородки из гипсокартона однослойное оштукатуренное на все высоту этажа толщиной 100мм
- Замена перегородки из гипсокартона однослойное оштукатуренное до 2х раковин толщиной 100мм
- Замена оштукатуренная перегородка
- Замена перегородки синтетическая (пластиковая) с дверью и необходимой фурнитурой
- Номер помещения по экспликации
- Отметка уровня пола этажа
- Маркировка оконных проемов, дверей, окон, перегородок

- Возможность устройства проемов в несущих стенах будет уточняться в проекте.
- Размер и расположение вентиляционных шахт будет уточнен в проекте.
- Шахты предназначены для прокладки инженерных коммуникаций и стояков (ВК, Ц, ЗОМ), оборудуются лестницами для обслуживания.
- Ж. категоризирование по взрывопожарной опасности данных помещений выполняется на этапе проектирования.
- Марки проемов см. альбом 16-25/Г-П-АР лист 61

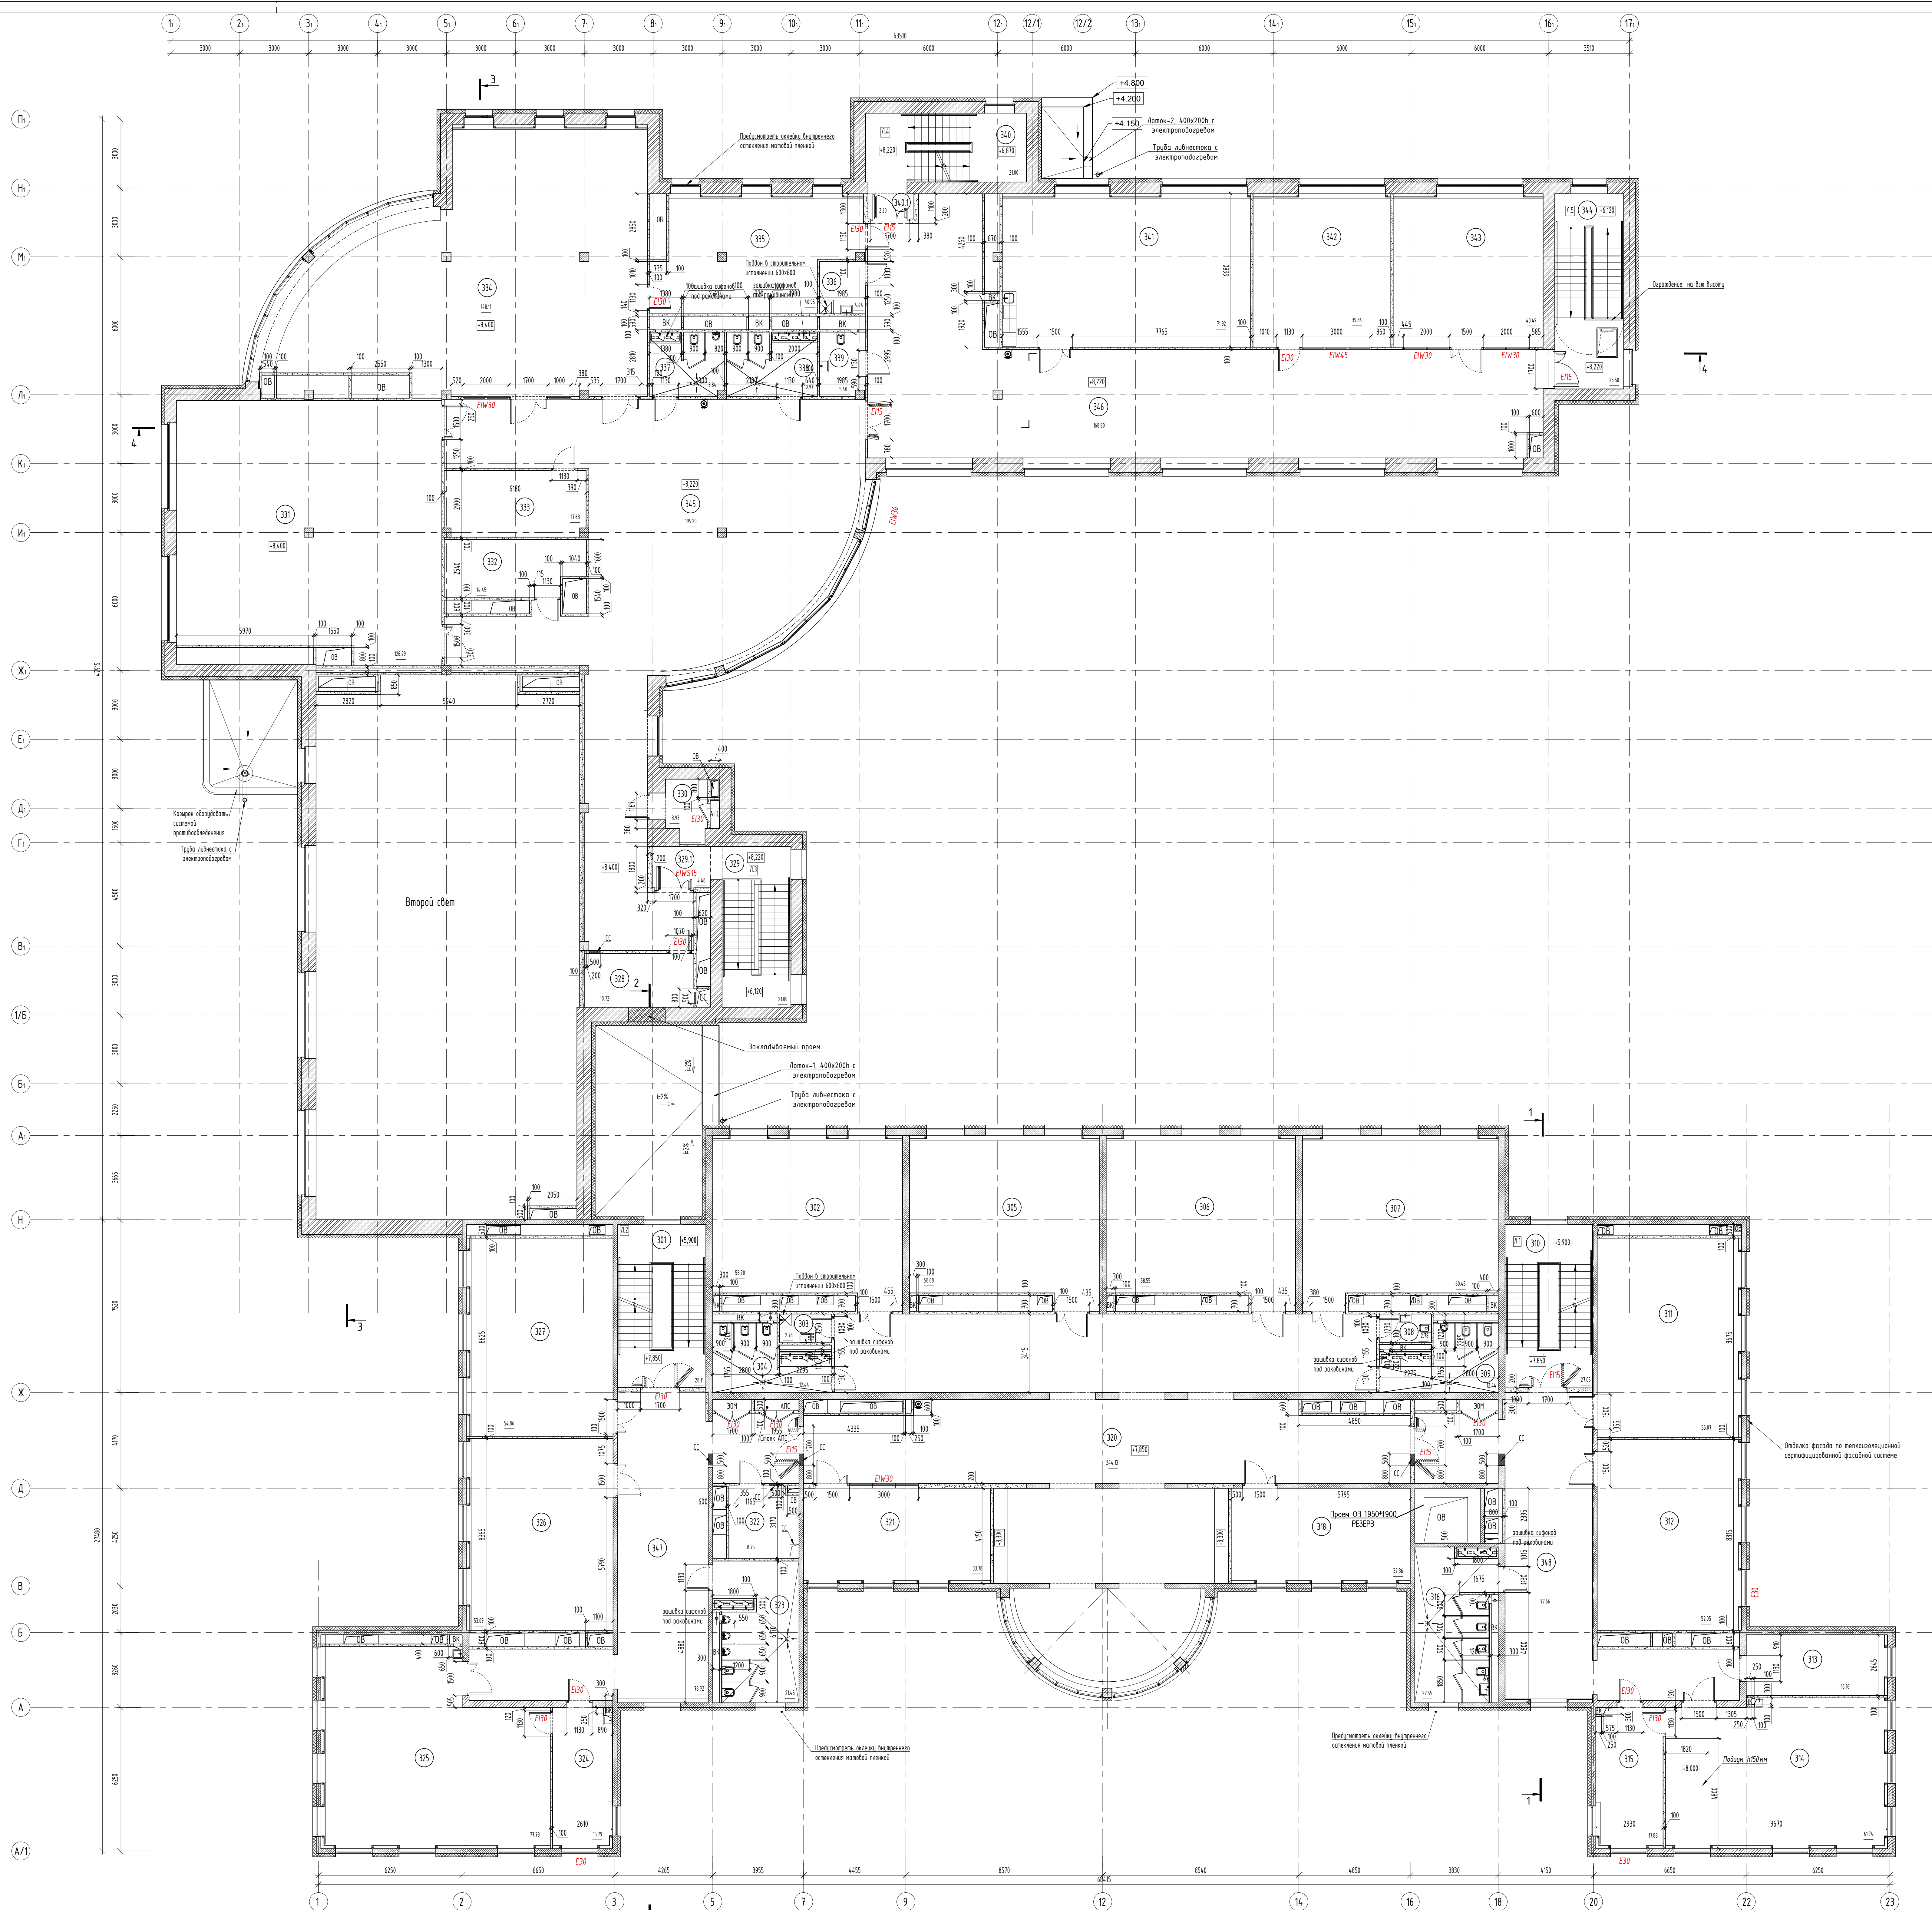

Экспликация помещений 3-го этажа				
Номер помещения	Наименование	Площадь, м2	Кол. помещ.	
301	Астеническая клетка Тит И2	18,82		
302	Кабинет русского языка и литературы	18,70		
303	Псих	2,78		В4
304	Секция для девочек (основная и старшая школа)	12,44		
305	Кабинет русского языка и литературы	59,08		
306	Кабинет математики	58,55		
307	Кабинет математики	60,45		
308	Секция для персонала	2,75		
309	Секция для мальчиков (основная и старшая школа)	12,44		
310	Астеническая клетка I	27,05		
311	Кабинет географии	55,07		
312	Универсальный учебный кабинет	56,05		
313	Кабинет для индивидуальных занятий, 8 в.ч. с психологом-психологом	16,16		
314	Учебный кабинет для изучения естественных физика	61,02		
315	Астеническая клетка физика	18,82		В3
316	Секция для девочек с комнатой личной гигиены (основная и старшая школа)	23,25		
317	Подсобное помещение	2,64		В4
318	Кабинет иностранного языка (основная и старшая школа)	66,36		
320	Коридор с рекреацией	244,13		
321	Кабинет иностранного языка (основная и старшая школа)	13,78		
322	Помещение связи	2,75		В4
323	Секция для мальчиков (основная и старшая школа)	11,73		
324	Астеническая клетка биология	15,93		В3
325	Учебный кабинет для изучения естественных: биология + ОБЗР	17,78		
326	Универсальный учебный кабинет	53,07		
327	Кабинет истории тип 1	54,86		
328	Коридор	10,72		В3
329	Астеническая клетка I/II	21,08		
329.1	Томбоу	4,40		
330	Тех. помещение	2,93		В4
331	Универсальное помещение с возможностью организации административного зала (конференции)	125,19		
332	Раздевальня	14,45		
333	Раздевальня	17,63		
334	Медиаинформационный информационный библиотечный центр : зона для индивидуальных занятий	52,15		
335	Медиаинформационный информационный библиотечный центр :проекции (экраны) фото и видео кино	41,15		В3
336	Псих	4,44		В4
337	Секция для мальчиков (основная и старшая школа)	8,84		
338	Секция для девочек (основная и старшая школа)	10,97		
339	Секция для персонала	5,40		
340	Астеническая клетка I/II	21,08		
340.1	Томбоу	2,20		
341	Кабинет с рабочим пространством для учителей Тип 1 (основная и старшая школа)	39,94		
342	Универсальное помещение с возможностью организации Мультимедиа	71,82		В3
343	Помещение музея	43,49		
344	Астеническая клетка I/II	25,50		
345	Коридор и рекреация (основная и старшая школа)	195,20		
346	Коридор и рекреация (основная и старшая школа)	168,80		
347	Коридор	18,72		
348	Коридор	77,66		
	Всего	2246,3		

УСЛОВНЫЕ ОБОЗНАЧЕНИЯ

- Сдвигнутые молотки и/или стволы
 - Замена перекосы из газобетонных блоков
 - 1/625x25x100/1050/8/5 по ГОСТ Р 76232-2022, толщину 100мм на клею с армированием базальтовой сеткой, штукатурке
 - Замена перекосы из газобетонных блоков
 - 1/625x25x100/1050/8/5 по ГОСТ Р 76232-2022, толщину 200мм на клею с армированием базальтовой сеткой, штукатурке
 - Замена перекосы из кирпича однослойного двухслойного на все фасады, этаж по толщине 100мм
 - Замена перекосы из кирпича однослойного двухслойного до 3х раз по толщине 100мм
 - Замена перекосы оштукатуренных перекосы
 - Замена перекосы цементно-песчаной (гипсокартонной) с дверью и необходимой фурнитурой
- 201

— Номер помещения по эксплуатации

— Отметка уровня пола этажа

— Маркировка единичности записей: дверей, окон, перегородок
- EM/EM/EM

1. Возможность устройства проемов в несущих стенах будет уточняться в проекте.
Размер и расположение вентиляционных шахт будет уточнен в проекте.
2. Шахты предназначенные для прокладки инженерных коммуникаций и стоек ИВК, СВ, ЗОМ, оборудуются лючками для обслуживания.
3. * категорирование по взрывопожарной опасности данных помещений выполнять на этапе проектирования.
4. Марки ограждений смотреть альбом 16-25/1 -П-АР лист 61

					16-25/Т-П-АР	
					Капитальный ремонт объекта "ТБОУ Школа № 429 "Скоkelная гора", расположенного по адресу: г.Москва, ул. Скоkelной горы 5-А, 8/А	
Имя	Кол.ку	Лист	№Фол.	Подпись	Дата	
Разработ		Литовская		<i>[Подпись]</i>	16.06.2018	
					Архитектурно-планировочные решения	
					Страница	Лист
					р	8
№ киндер	Гербарь				16.06.2018	
Гипс	Морозов		<i>[Подпись]</i>		16.06.2018	
					План 3 этажа, М1:100	
					 АЗУРИТ	

