


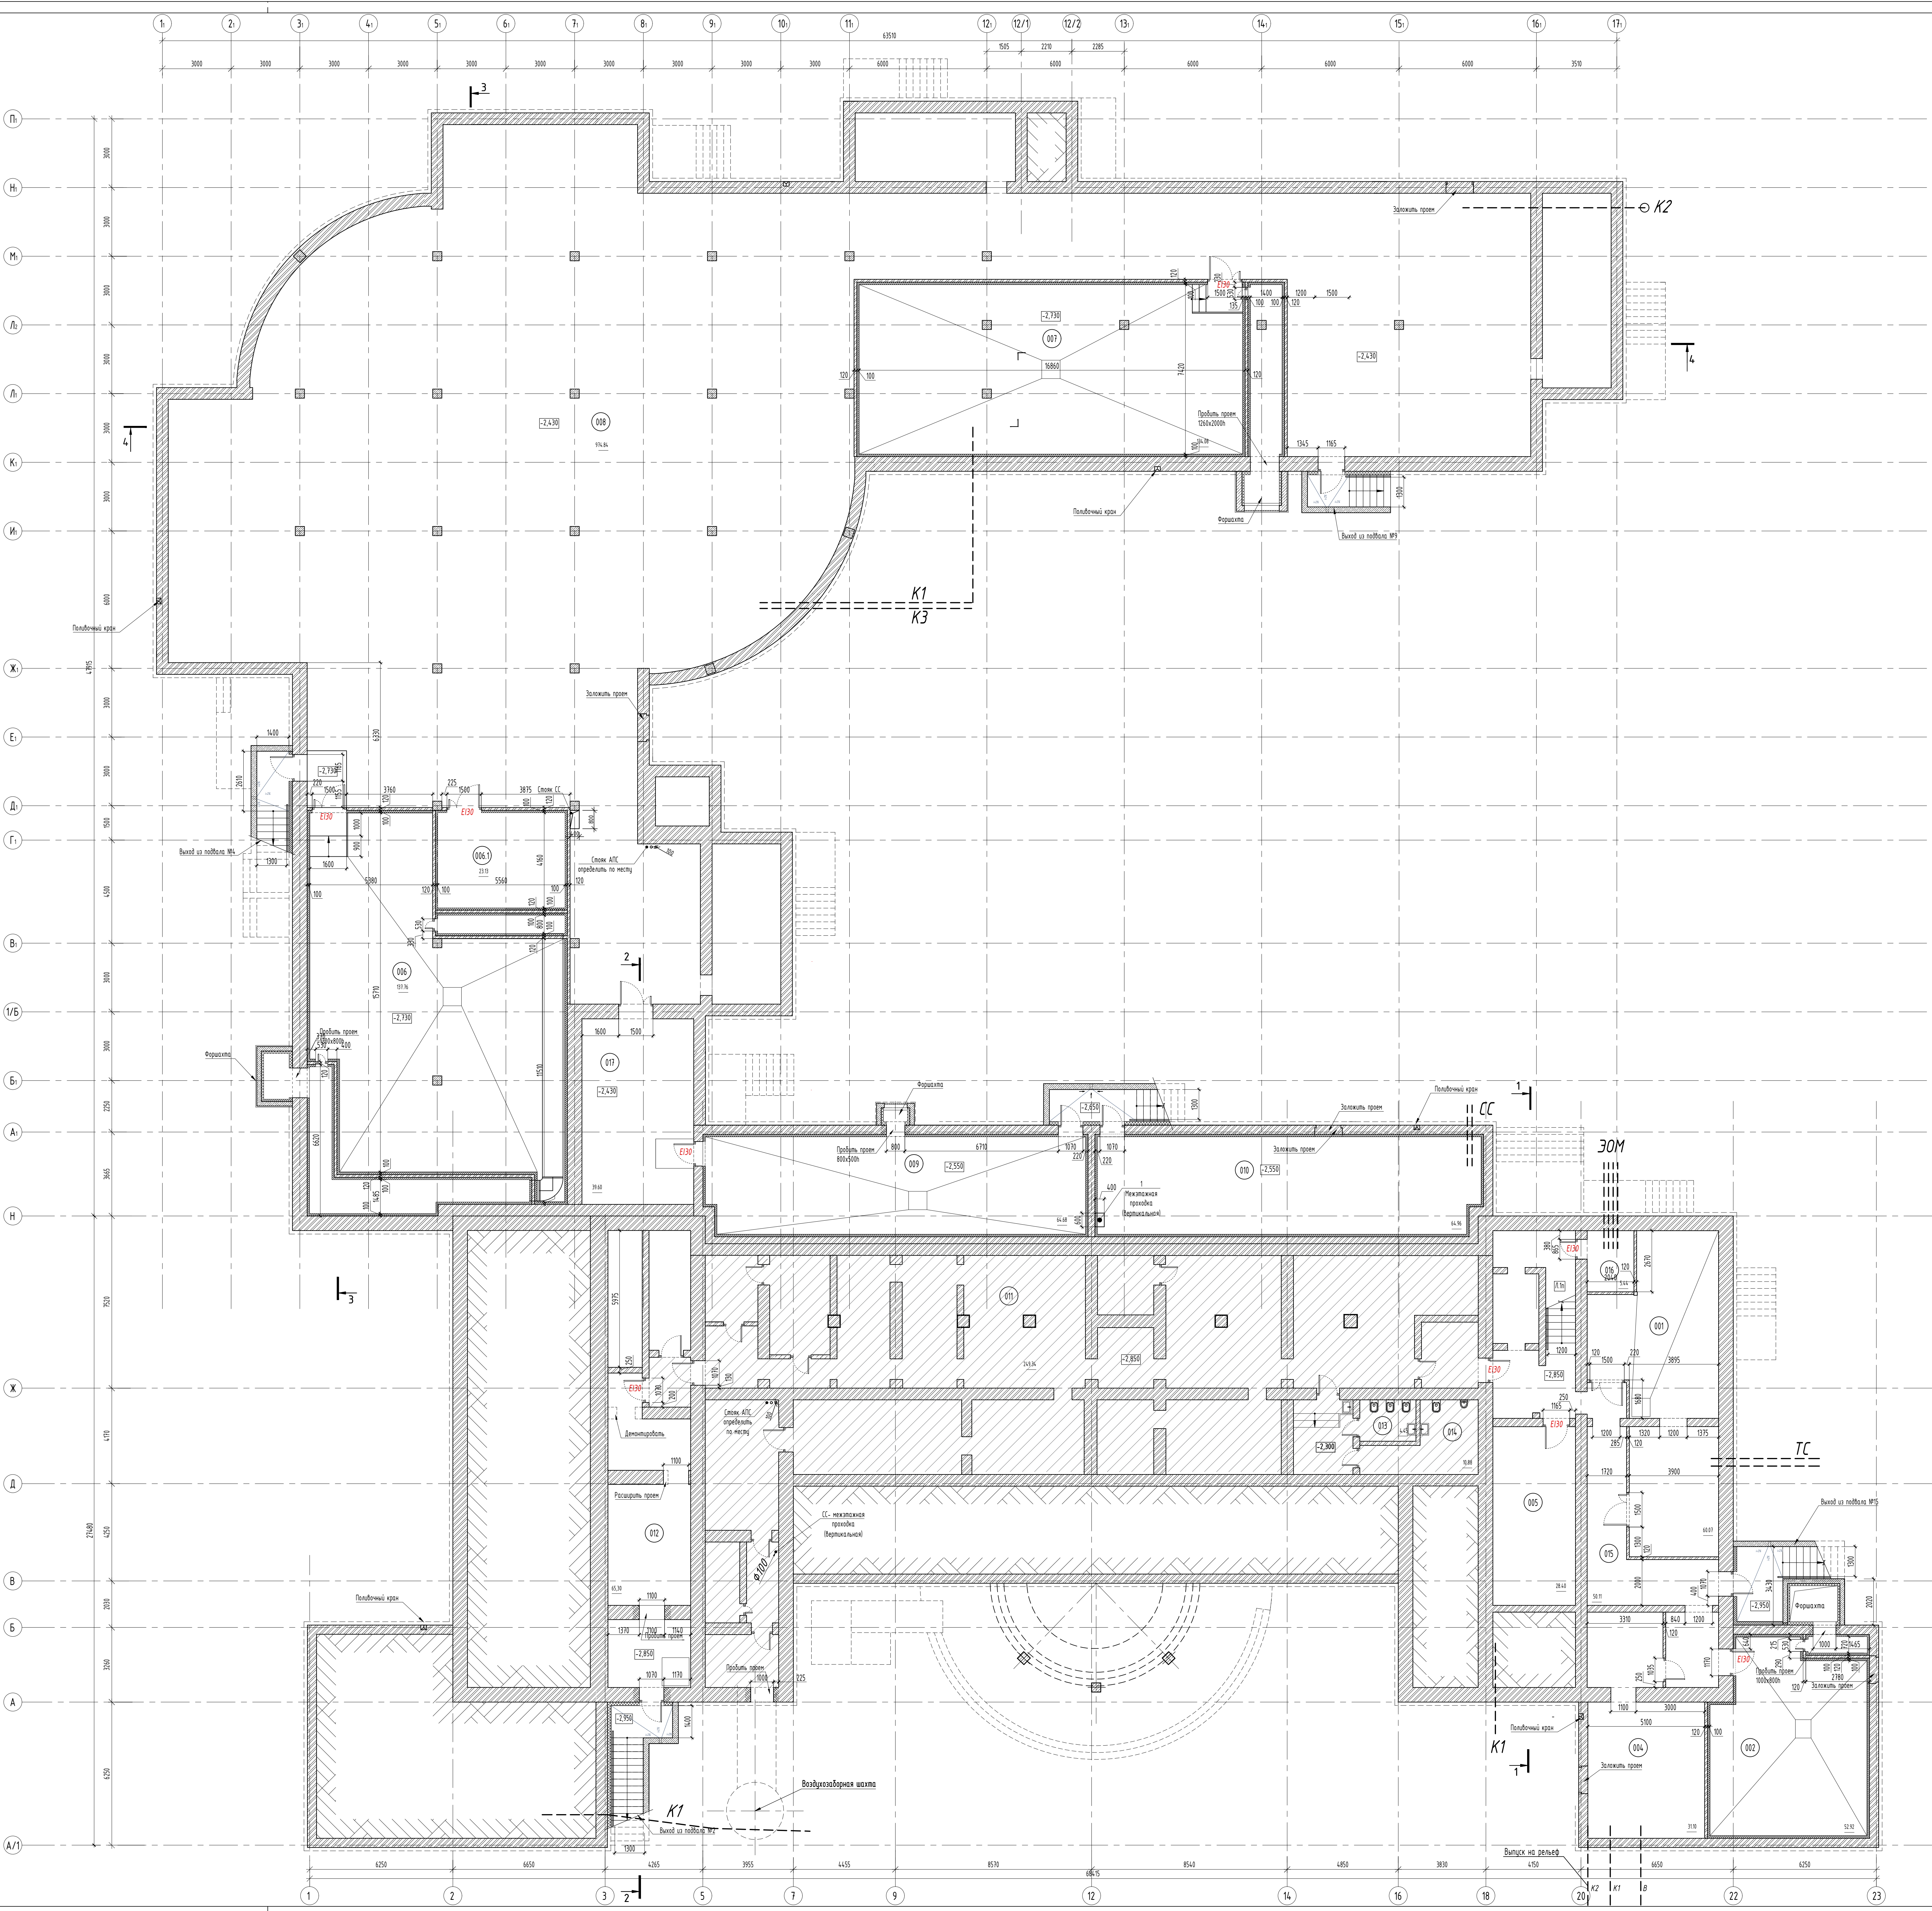

Экспликация помещений подвала

Номер помещения	Наименование	Площадь м2	Кот. помещ.
001	ИТП	60.07	Д
002	Вентилятор с форскамерой	52.92	В3
004	Водомерный узел и насосная	41.24	Д
005	Техническое помещение	28.40	Д
006	Вентилятор	197.76	В3
006.1	Вентилятор систем приточной приточной вентиляции	23.13	Д
007	Вентилятор	138.94	В3
008	Техническое помещение для прокладки инженерных коммуникаций	974.84	В3
009	Вентилятор	64.68	В3
010	Техническое помещение	64.96	Д
011	Защитное помещение гражданской обороны	249.34	Д
012	Коридор	50.95	
013	Санузел женский	18.88	
014	Санузел мужской	4.45	
015	Коридор	50.11	
016	Узел ввода электрических сетей	5.44	В4
017	Коридор	39.60	
Всего		1997.7	

- УСЛОВНЫЕ ОБОЗНАЧЕНИЯ
- Существующие стены из полнотелого керамического кирпича
 - Значения номинальные Ж/Б стены
 - Значения периметры из полнотелого кирпича толщиной 100мм и 250 мм
 - Номер помещения по экспликации
 - Маркировка геометрии значимых дверей
 - Ометка уровня пола этажа
 - Помещения ГО ЧС
 - Пути эвакуации

- Возможность устройства проемов в несущих стенах будет уточняться в проекте. Размер и расположение вентиляционных шахт будет уточнен в проекте.
- Шахты предназначены для прокладки инженерных коммуникаций и стоек (ВК, СТ, ЗОМ), оборудуются лестницами для обслуживания.
- Ж - категорирование по взрывопожарной опасности данных помещений выполняется на этапе проектирования.
- Марки ограждений смотреть альбом 16-25/Г-П-АР лист 61