


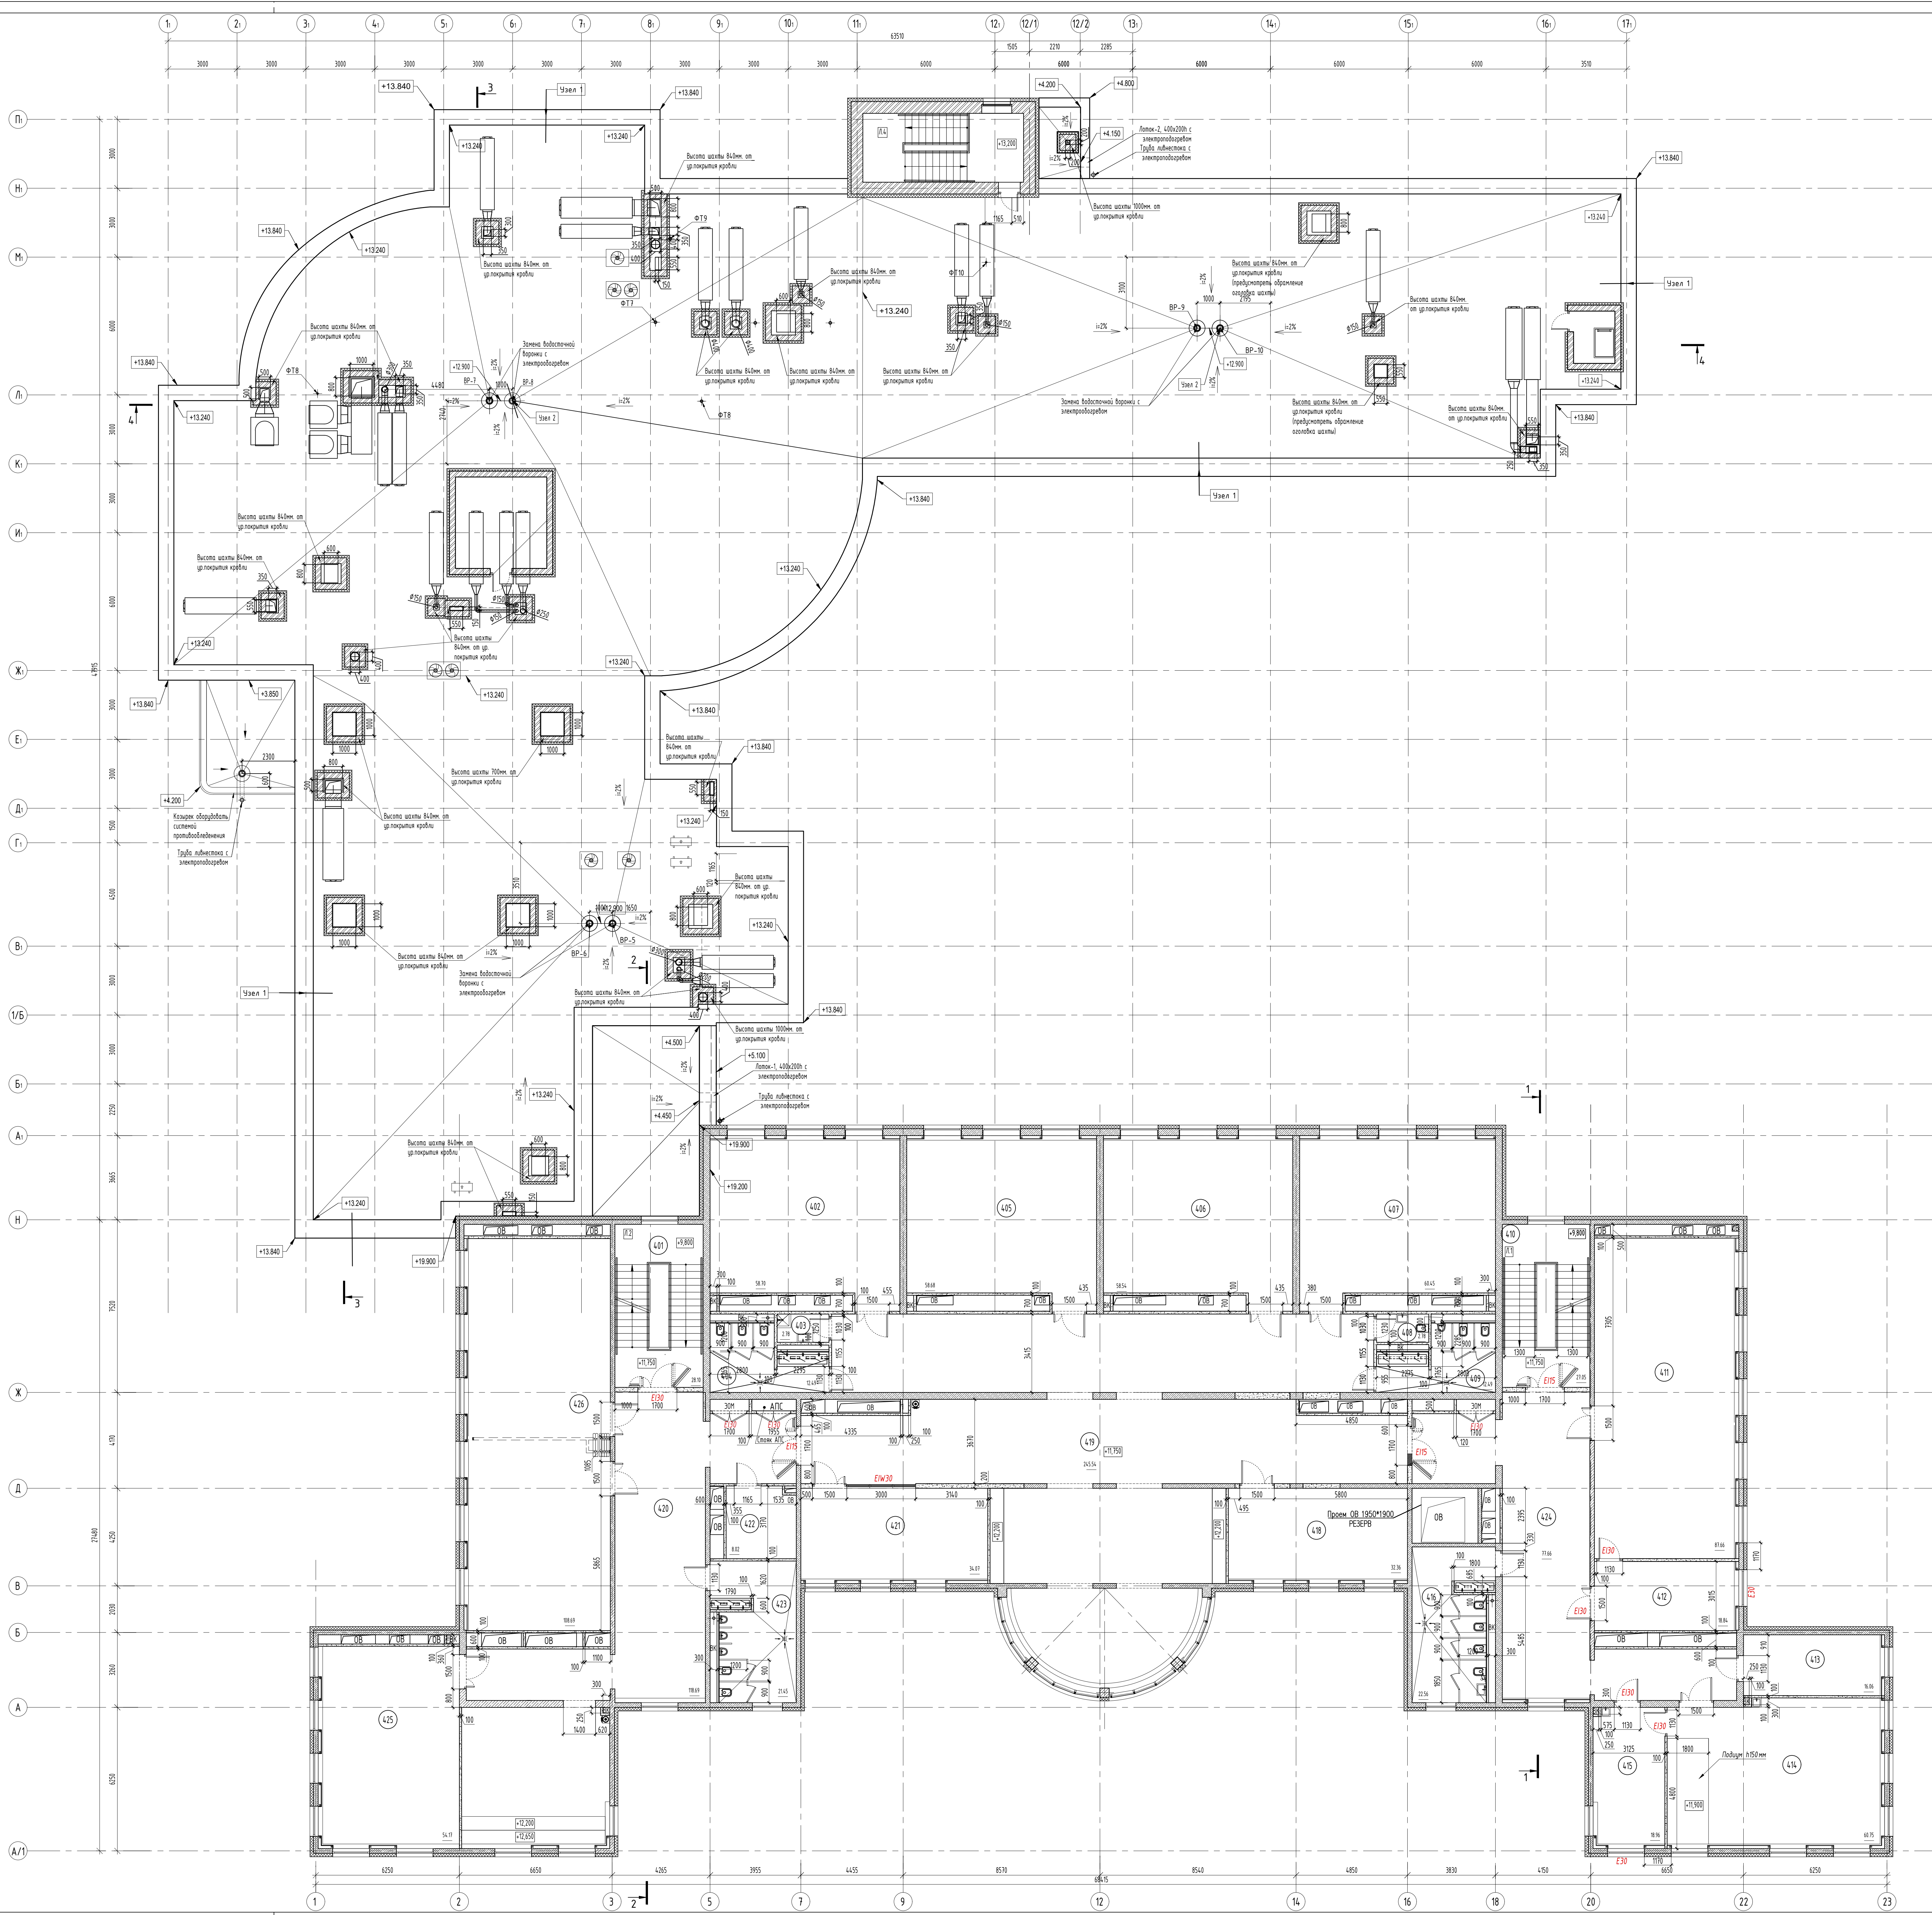

Экспликация помещений 4-го этажа			
Номер помещения	Наименование	Площадь, м2	Кол. помещ.
401	Лестничная клетка Тип Н2	28.81	
402	Кабинет русского языка и литературы	58.10	
403	ПМ	2.18	В4
404	Санузел для девочек (основная и старшая школа)	12.49	
405	Кабинет русского языка и литературы	58.68	
406	Кабинет математики	58.54	
407	Кабинет математики	60.45	
408	Санузел для персонала	2.78	
409	Санузел для мальчиков (основная и старшая школа)	12.49	
410	Лестничная клетка (ЛП)	26.98	
411	Кабинет информационных технологий	87.66	
412	Лаборантская при кабинете информационных технологий	18.84	В3
413	Административный кабинет тип 1 (основная и старшая школа)	16.03	
414	Учебные кабинеты для изучения естественных наук	60.75	
415	Лаборантская кабинета химии	18.96	В3
416	Санузел для девочек с комнатой личной гигиены (основная и старшая школа)	22.56	
417	Подсобное помещение	7.30	В4
418	Кабинет иностранного языка (основная и старшая школа)	32.36	
419	Коридор с рекреацией	245.54	
420	Коридор с рекреацией	108.69	
421	Кабинет иностранного языка (основная и старшая школа)	34.07	
422	Помещение связи	8.02	В4
423	Санузел для мальчиков (основная и старшая школа)	21.45	
424	Коридор	77.66	
425	Кабинет истории Тип 1	54.17	
426	Кабинет информатики с возможностью деления трансформированной перегородкой на два помещения	108.69	
427	Лестничная клетка (ЛП)	21.00	
428	Помещение выхода на крышу	4.18	
Всего		1276.5	

- УСЛОВНЫЕ ОБОЗНАЧЕНИЯ**
- Существующие материалы и/или стены
 - Замена перегородки из газобетонных блоков 1/625x250x100/050/0 по ГОСТ Р 7552-2012, толщиной 100мм на клею с армированием базальтовой сеткой, оштукатуренная
 - Замена перегородки из газобетонных блоков 1/625x250x100/050/050 по ГОСТ Р 7552-2012, толщиной 200мм на клею с армированием базальтовой сеткой, оштукатуренная
 - Замена перегородки из акриловых одностронне обшитых на все высоту этажа толщиной 10мм
 - Замена перегородки из акриловых односторонне обшитых во ш. раковин толщиной 10мм
 - Замена остекление перегородки
 - Замена перегородки сантехническая (вместо старой) с дверью и необходимой фурнитурой
 - Номер помещения по экспликации
 - Отметка уровня пола этажа
 - Маркировка геометрии помещений, окон, перегородок
1. Возможность устройства проемов в несущих стенах будет уточняться в проекте.
2. Размеры и расположение вентиляционных шахт будет уточнен в проекте.
3. Шахты предназначены для прокладки инженерных коммуникаций и стояков (ВК, СС, ЗОМ), оборудуются лестницами для обслуживания.
4. Маркировка геометрии помещений, окон, перегородок.