


План кровли

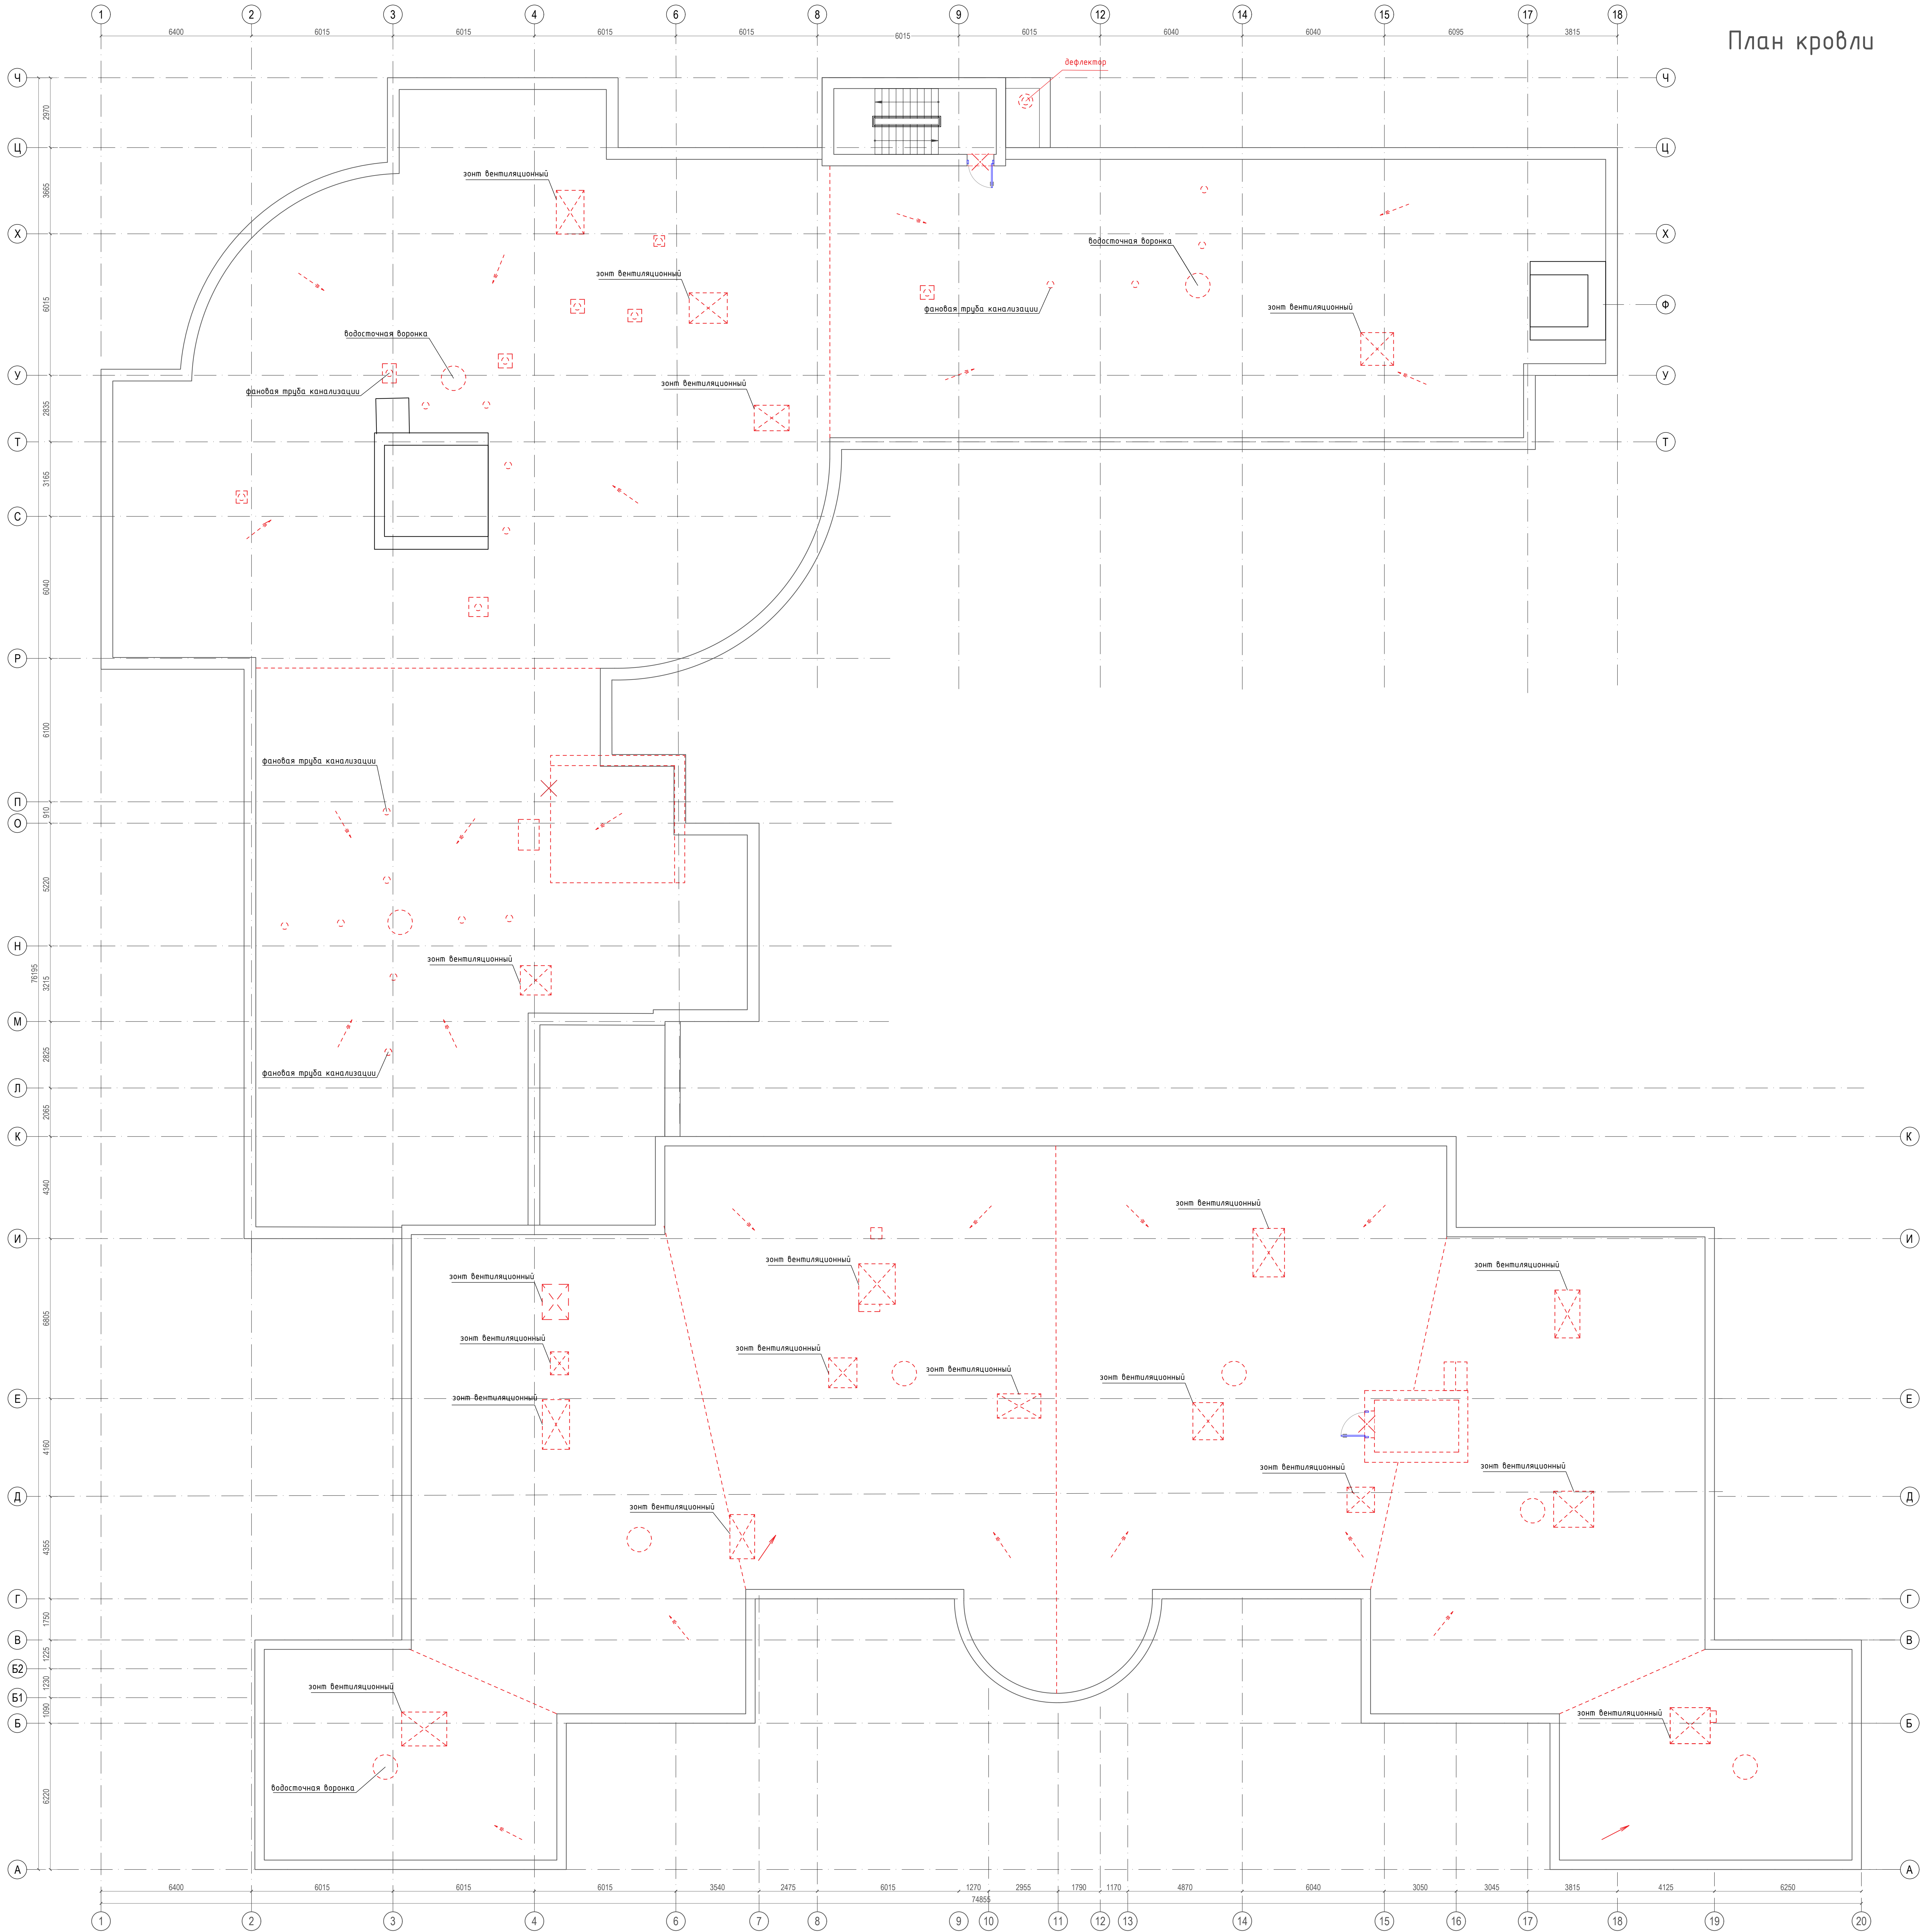

Условные обозначения

- демонтаж кровельных настилов
- демонтаж дверей

						18-25/Г-П-АР		
						Капитальный ремонт общеобразовательного учреждения (ГБОУ "Школа №429"), расположенного по адресу: г. Москва, 5-ая ул. Соколиной Горы, д.14		
Им.	Кол. рч.	Лист	№ док.	Подпись	Дата	Архитектурно-планировочные решения		
Разраб.			Наблюдатель		2020.05	Степан	Лист	Листов
ГАП			Алалыкина		2020.05	П	7	
И. контр.			Губарева		2020.05	План демонтажа кровли. М1:100		
Гип			Маркова		2020.05	АЗУРИТ		