


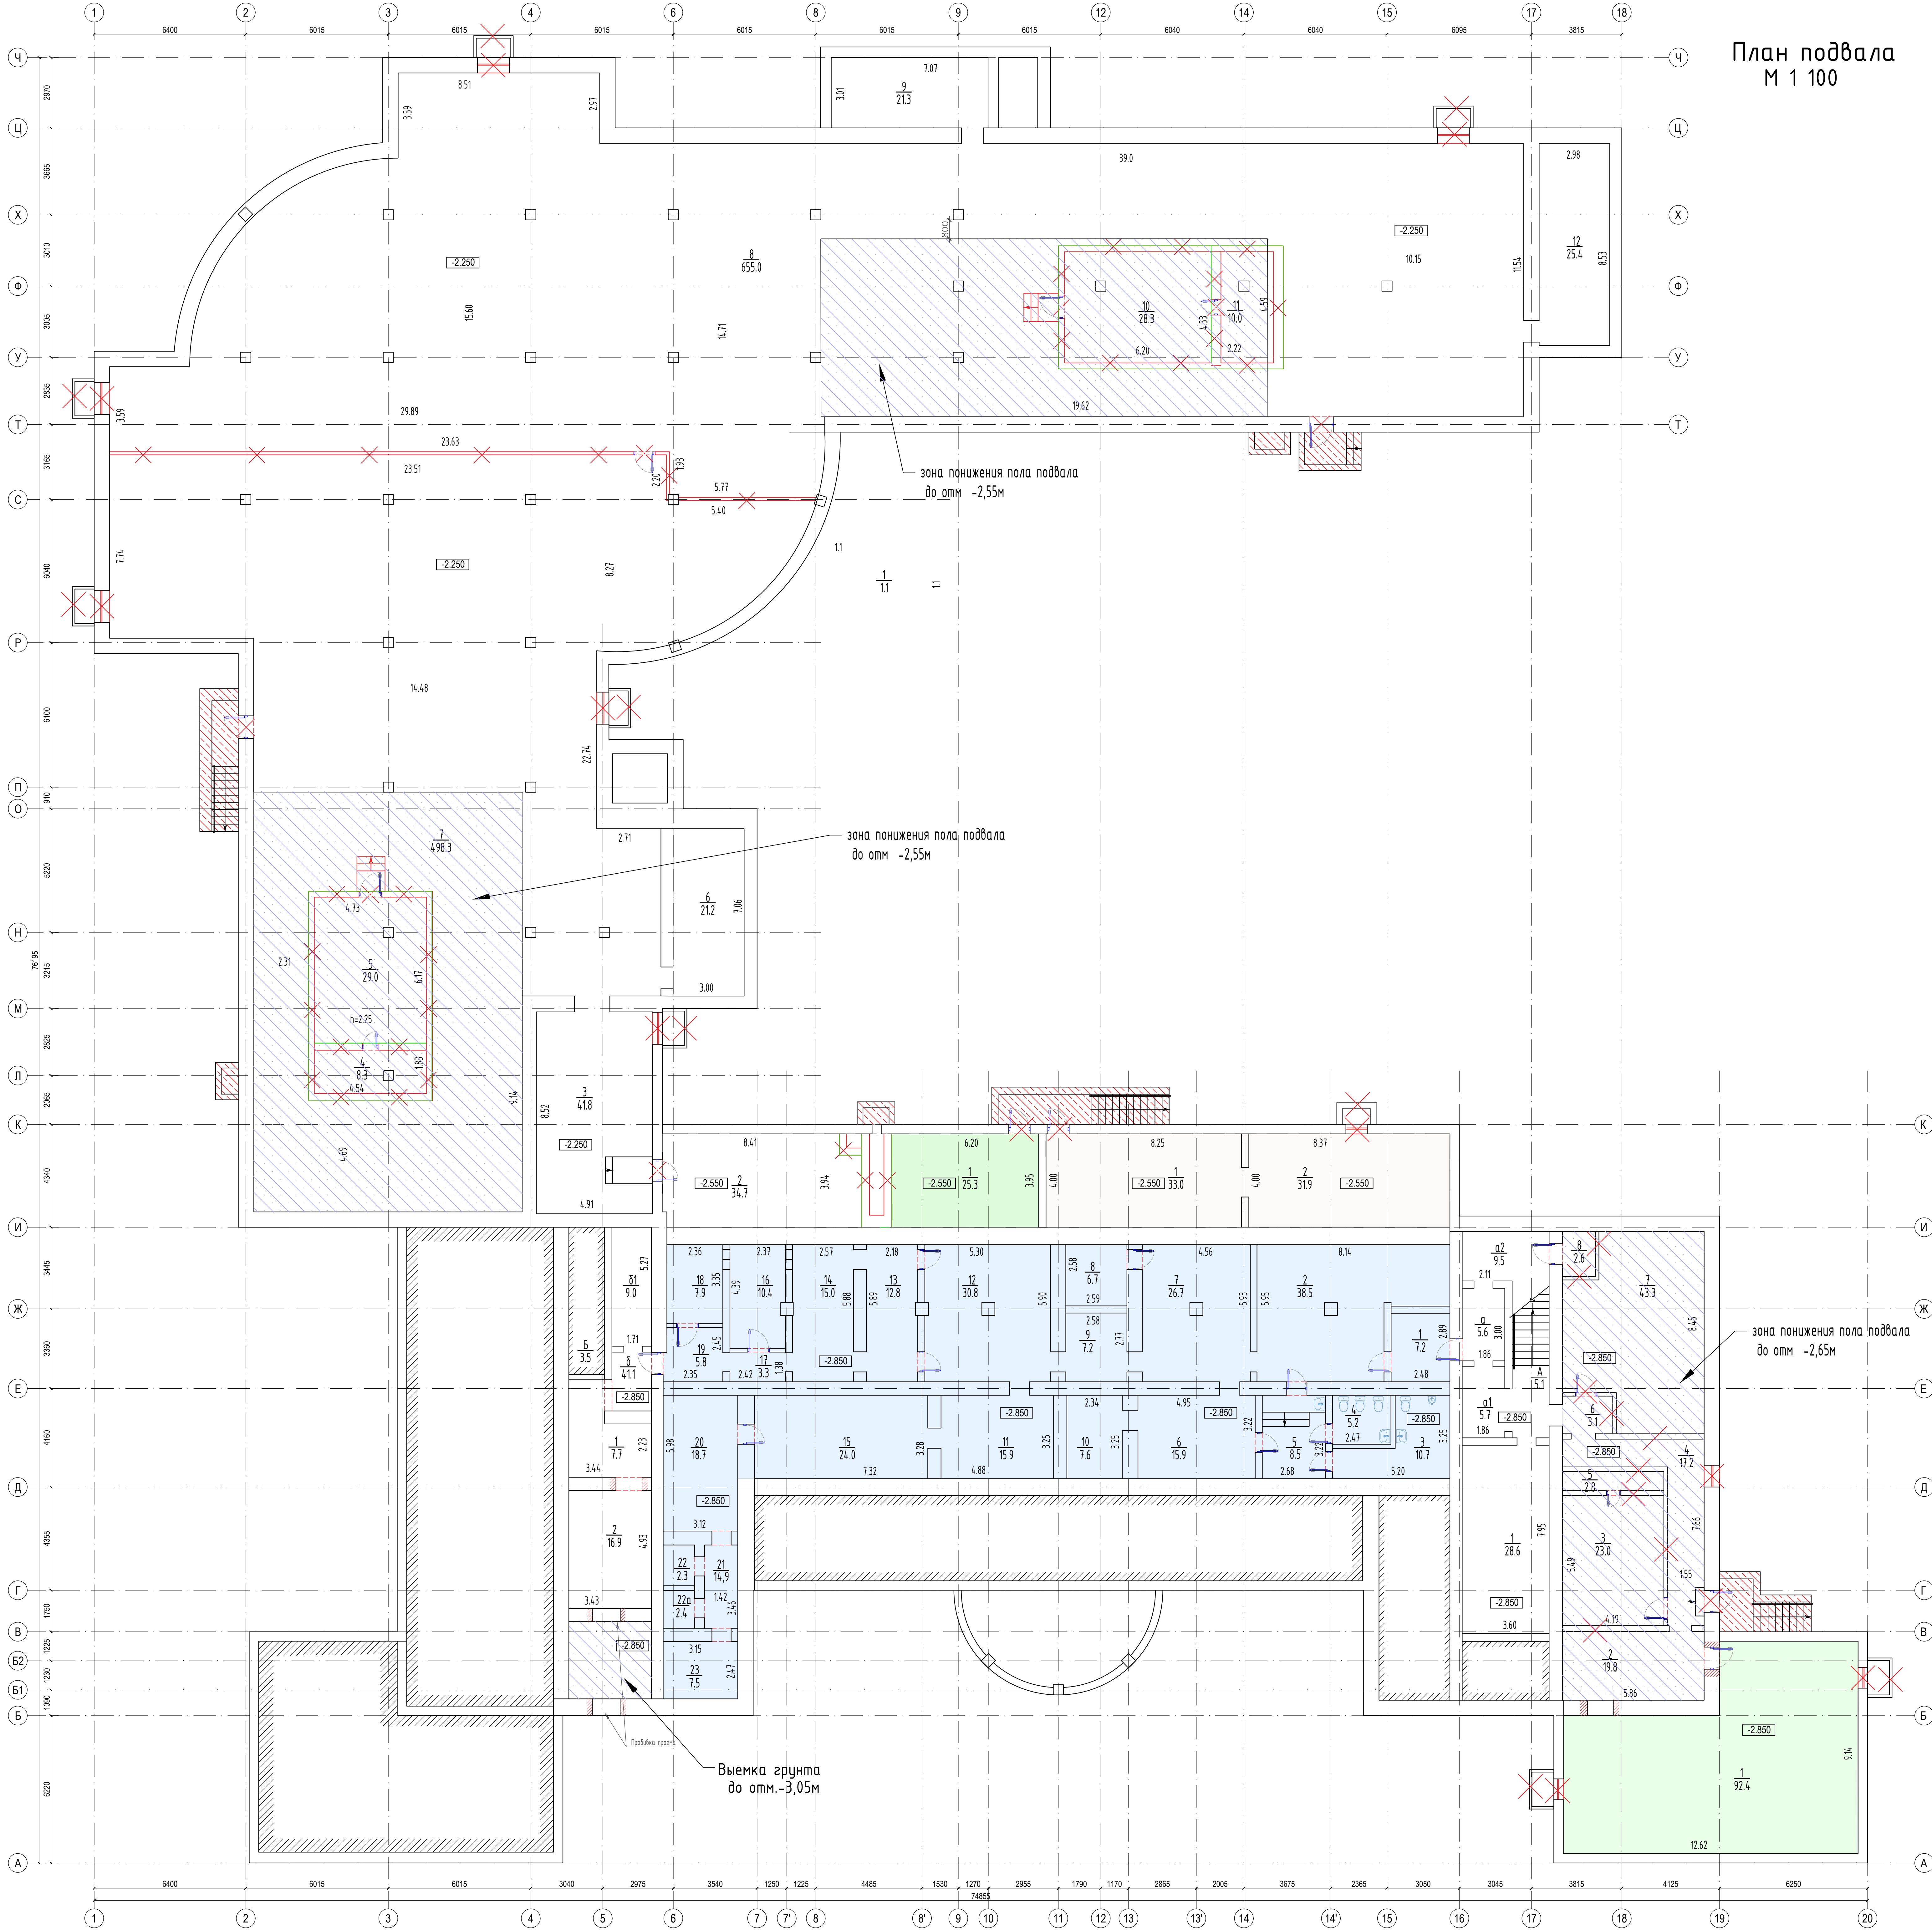

План подвала
М 1 100

Экспликация помещений подвала		
Номер помещения	Наименование	Площадь, м2
1	Водонагревательная	92.4
2	Помещение техническое	19.8
3	Вентиляторная	23.0
4	Коридор	17.2
5	Вентиляторная	2.8
6	Коридор	3.1
7	Бойлерная	43.3
8	Помещение подсобное	2.6
Всего		204.2
А	Клетка лестничная	5.1
а	Коридор	5.6
а1	Коридор	5.1
а2	Коридор	9.5
Б	Клетка лестничная	3.5
Б	Коридор	4.1
В1	Помещение подсобное	9.0
Всего		42.5
1	Помещение специальное	7.2
2	Помещение специальное	38.5
3	Санузел	10.7
4	Санузел	5.2
5	Коридор	8.5
6	Помещение специальное	15.9
7	Помещение специальное	26.7
8	Помещение специальное	6.7
9	Помещение специальное	7.2
10	Помещение специальное	7.6
11	Помещение специальное	15.9
12	Помещение специальное	30.8
13	Помещение специальное	12.8
14	Помещение специальное	15.0
15	Помещение специальное	24.0
16	Помещение специальное	10.4
17	Коридор	3.3
18	Помещение специальное	7.9
19	Коридор	5.8
20	Помещение специальное	18.7
21	Помещение специальное	4.9
22	Шахта вентиляционная	2.3
22а	Шахта вентиляционная	2.4
23	Помещение специальное	7.5
Всего		295.9
1	Помещение техническое	28.6
Всего		28.6
1	Помещение техническое	25.3
Всего		25.3
1	Помещение техническое	33.0
2	Помещение техническое	31.9
Всего		64.9
1	Коридор	7.7
2	Помещение техническое	16.9
Всего		24.6

Экспликация помещений техподполья		
Номер помещения	Наименование	Площадь, м2
1	Вентиляторная	1.9
2	Вентиляторная	34.7
3	Подполье техническое	4.18
4	Вентиляторная	8.3
5	Вентиляторная	29.0
6	Подполье техническое	21.2
7	Подполье техническое	498.3
8	Подполье техническое	655.0
9	Подполье техническое	21.3
10	Вентиляторная	28.3
11	Вентиляторная	10.0
12	Подполье техническое	25.4
Всего		1375.2

- Условные обозначения:
- сохраняемые несущие конструкции
 - демонтаж оконных блоков
 - демонтаж витражей
 - демонтаж внутренних витражей и окон
 - демонтаж перегородок
 - демонтаж дверных блоков
 - разбираемые конструкции
 - демонтаж стенок под проем
 - демонтаж лифта
 - пробивка проема