


План подвала

Имя	Кол-во	Лист	№ док.	Подпись	Дата
Разработчик					
ГЛАВ					
Н. контр.					
Ген. дир.					

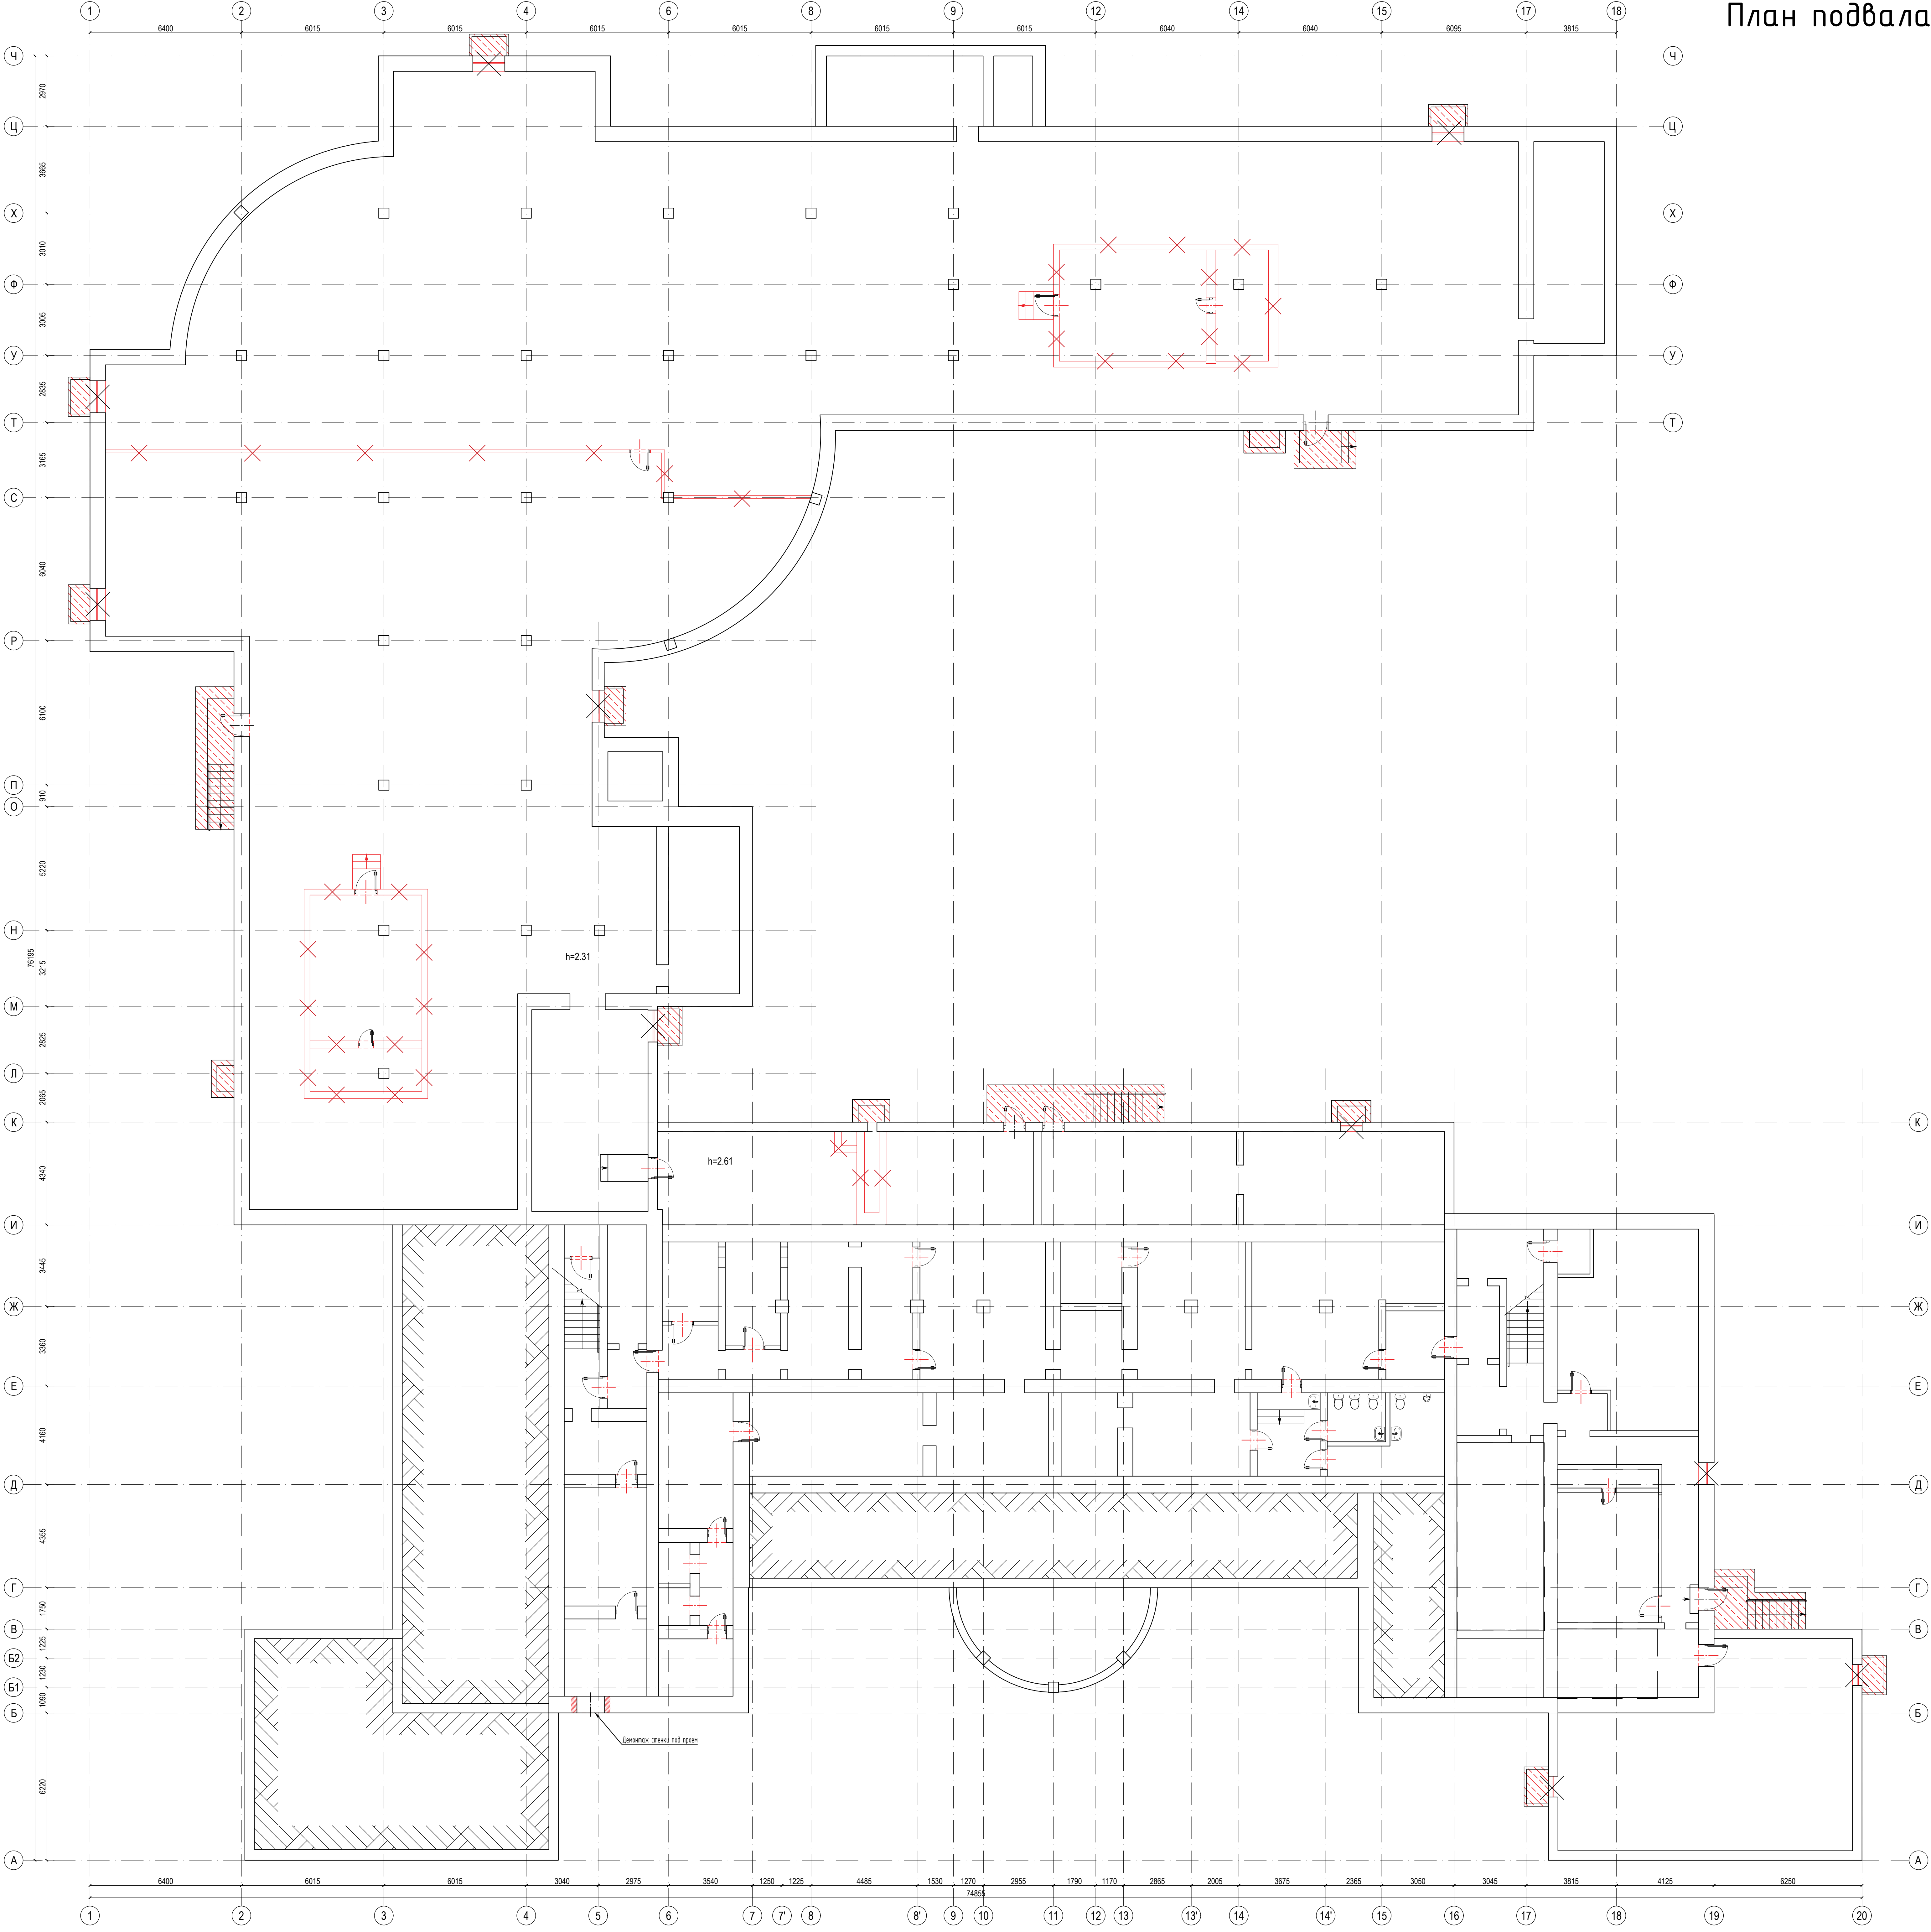

Условные обозначения:

- сохраняемые несущие конструкции
- демонтаж витражей
- демонтаж оконных блоков
- демонтаж внутренних окон и витражей
- демонтаж перегородок
- демонтаж внутренних дверных блоков
- демонтаж наружных дверных блоков
- разбираемые конструкции
- демонтаж стенки под проем

						16-25/Г-П-АР		
Капитальный ремонт общеобразовательного учреждения (ГБОУ "Школа №429"), расположенного по адресу: г.Москва, 5-ая ул.Соколиной Горы, д.14								
Архитектурно-планировочные решения						Склад	Лист	Листов
						П	1	
И. контр.	Губарева	2024.04				План демонтажа подвала №1/00		
Ген. дир.	Маркова	2024.04				АЗУРИТ		
						ФОРМАТ А2		