


План 1 этажа

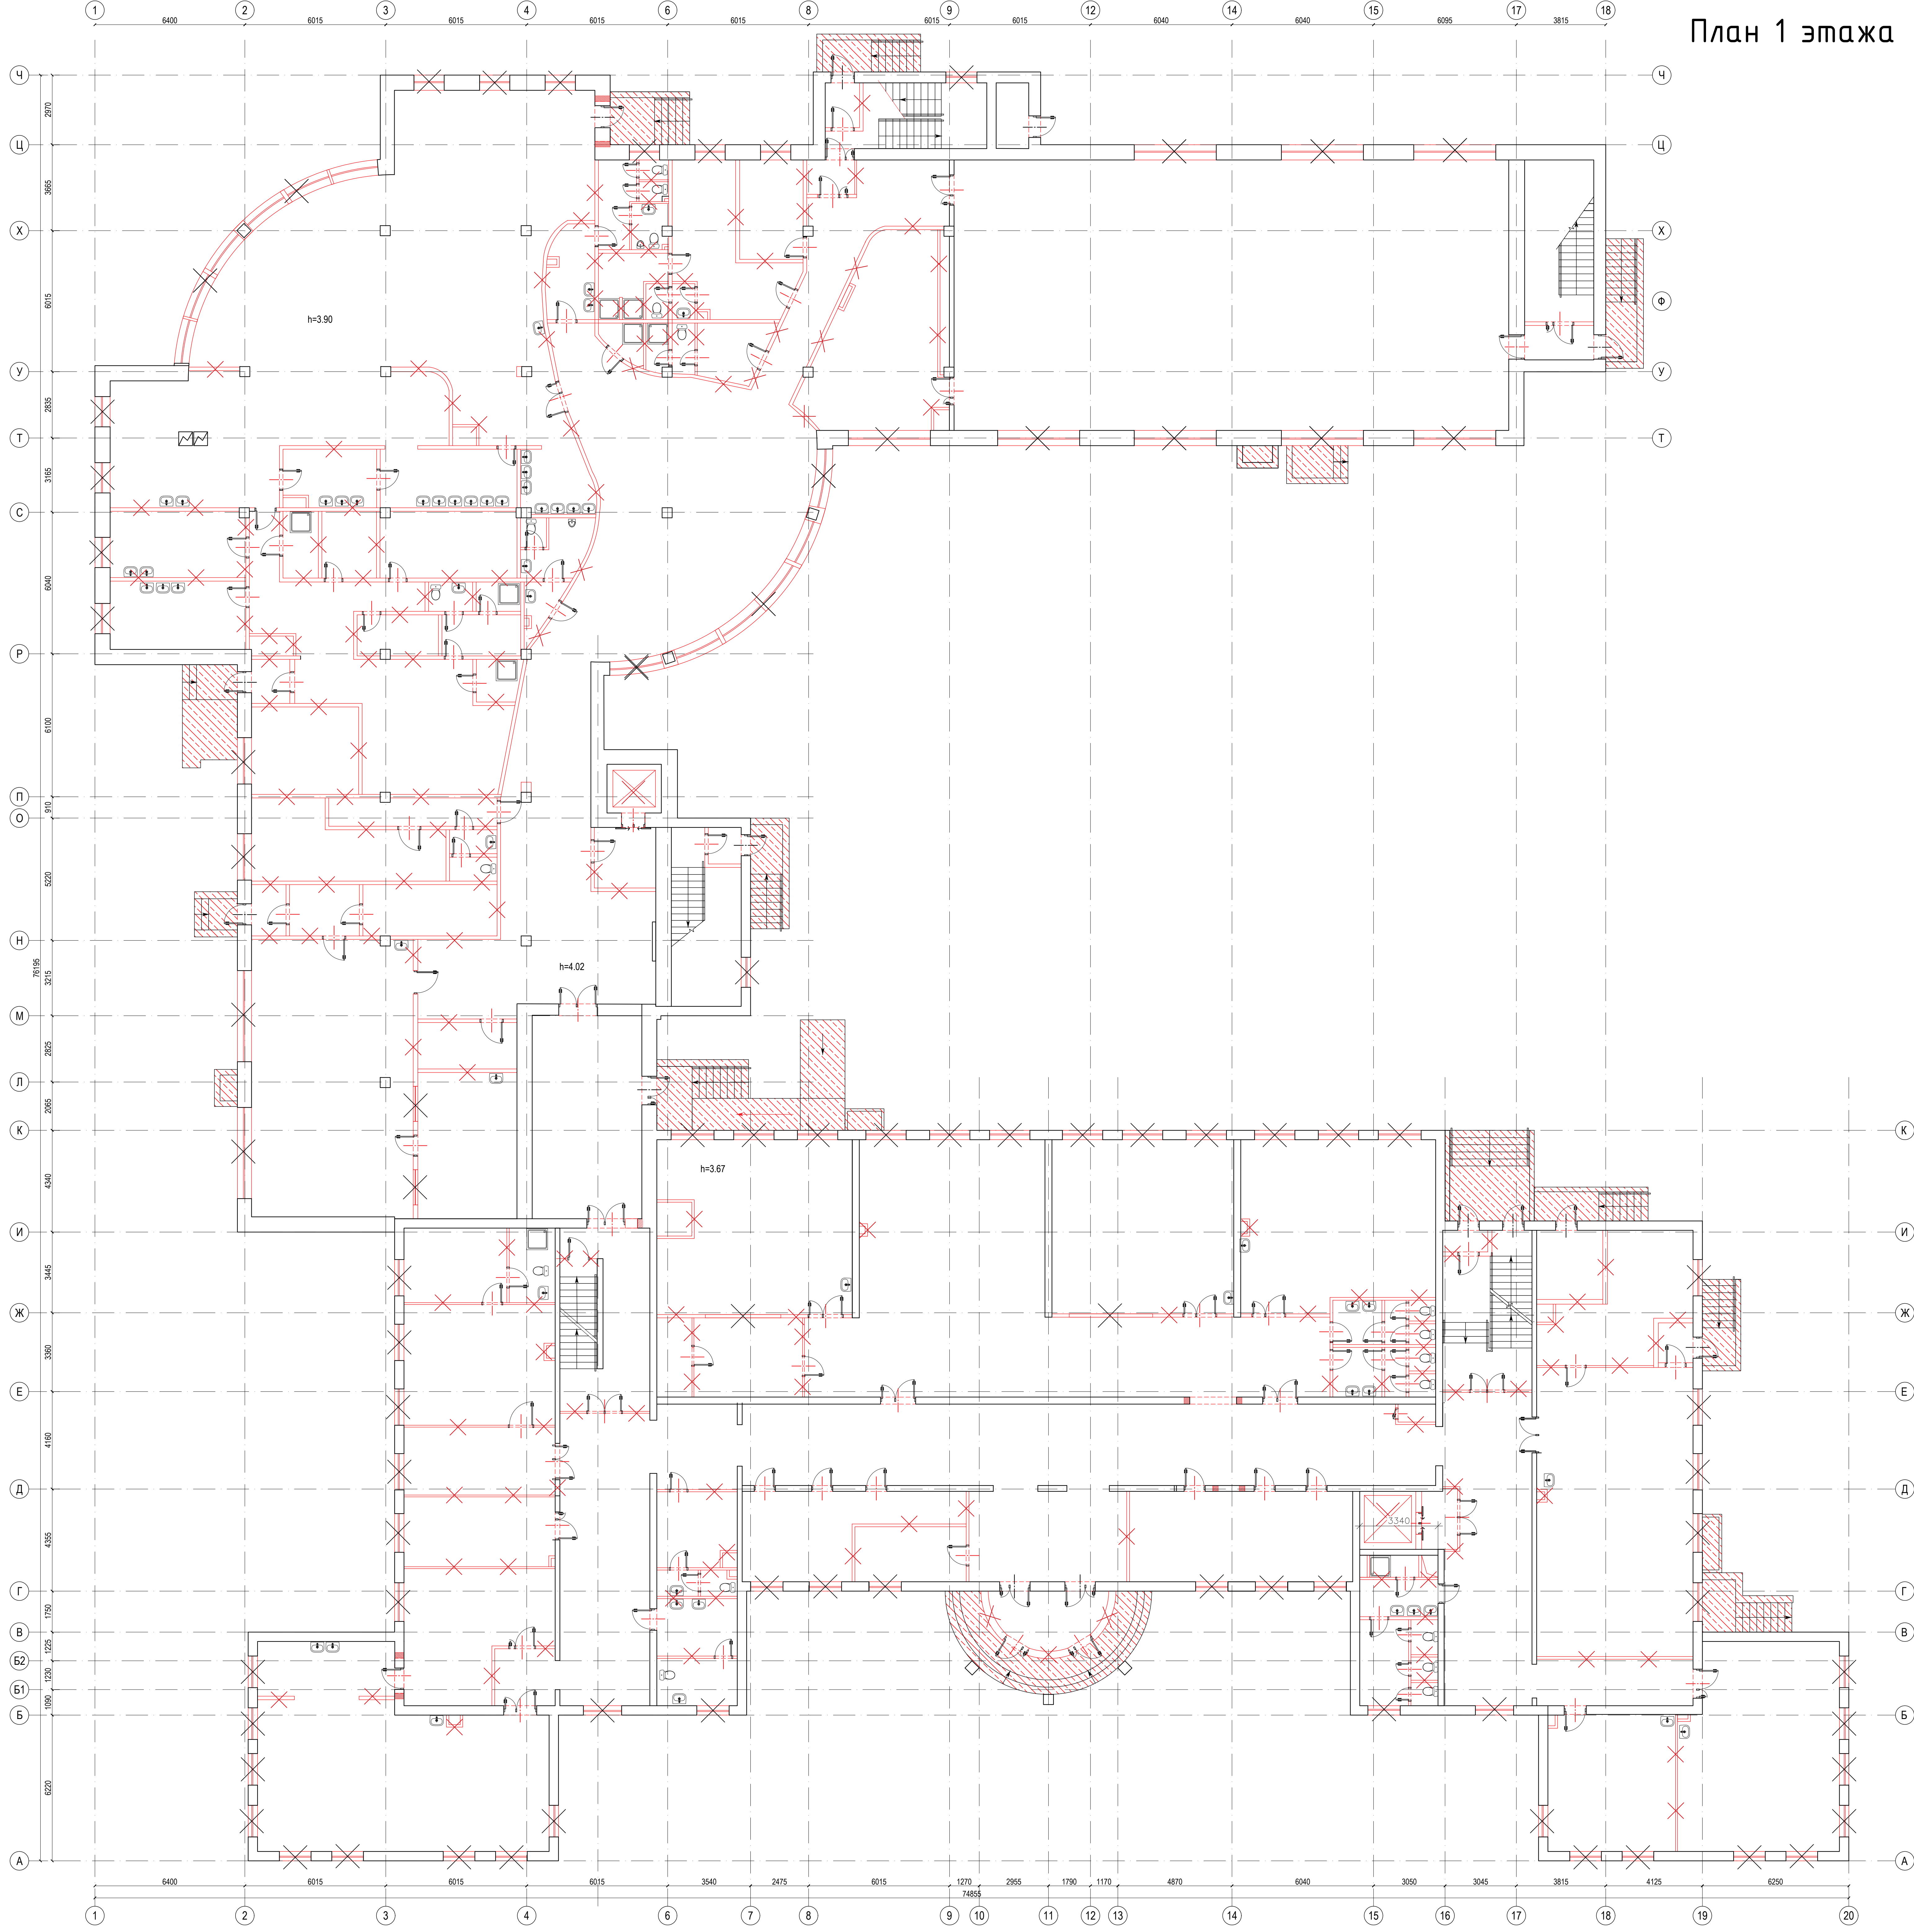

- Условные обозначения:
- сохраняемые несущие конструкции
 - демонтаж витражей
 - демонтаж оконных блоков
 - демонтаж внутренних окон и витражей
 - демонтаж перегородок
 - демонтаж внутренних дверных блоков
 - демонтаж наружных дверных блоков
 - разбираемые конструкции
 - демонтаж стенки под проем
 - демонтаж лифта

Имя	Кол-во	Лист	№ доку	Подпись	Дата
Разработ	Надзор	Проект	Исполн	Смет	Исх
ГЛАВ	Литература	Смет	Исх	Смет	Исх
Н. контр.	Губарева	Смет	Исх	Смет	Исх
Ген.пр.	Маринова	Смет	Исх	Смет	Исх

16-25/Г-П-АР					
Капитальный ремонт общеобразовательного учреждения (ГБОУ "Школа №429"), расположенного по адресу: г.Москва, 5-ая ул.Соколиной Горы, д.14					
Архитектура-планопроектные решения					
Имя	Кол-во	Лист	№ доку	Подпись	Дата
Разработ	Надзор	Проект	Исполн	Смет	Исх
ГЛАВ	Литература	Смет	Исх	Смет	Исх
Н. контр.	Губарева	Смет	Исх	Смет	Исх
Ген.пр.	Маринова	Смет	Исх	Смет	Исх