


План 4 этажа

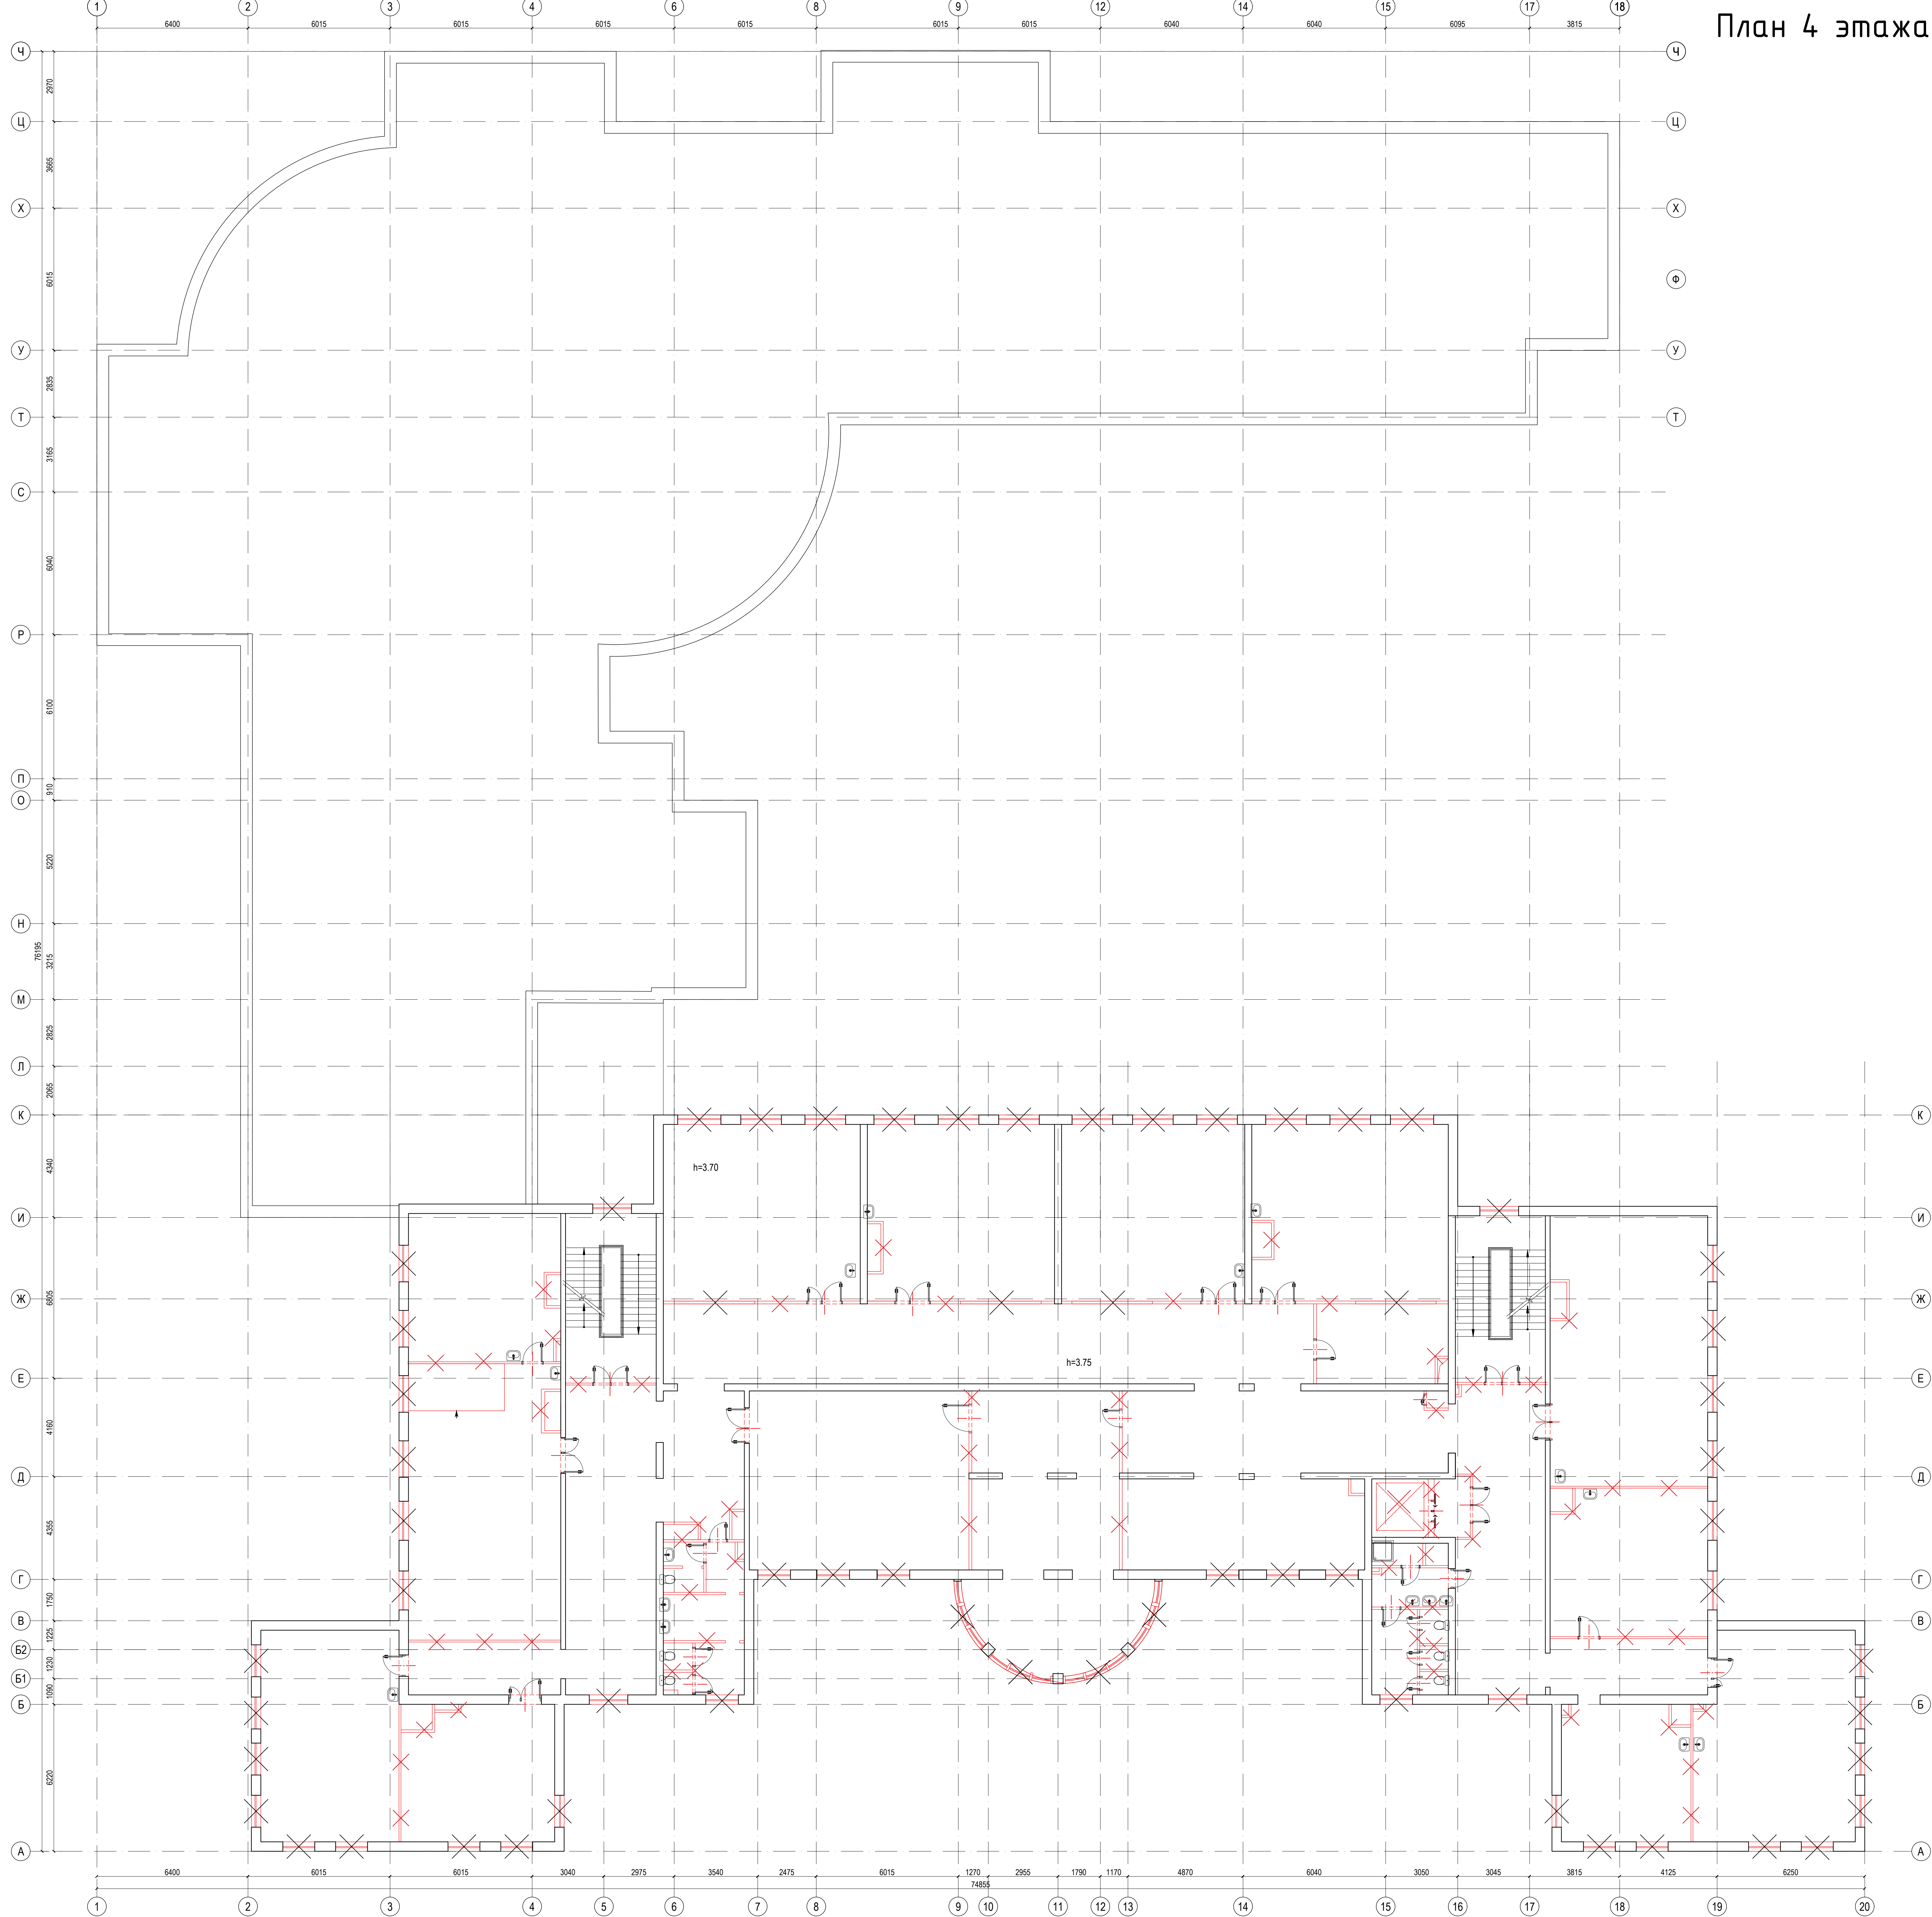

- Условные обозначения:
- сохраняемые несущие конструкции
 - демонтаж витражей
 - демонтаж оконных блоков
 - демонтаж внутренних окон и витражей
 - демонтаж перегородок
 - демонтаж внутренних дверных блоков
 - демонтаж наружных дверных блоков
 - разбираемые конструкции
 - демонтаж стенки под проем
 - демонтаж лифта