


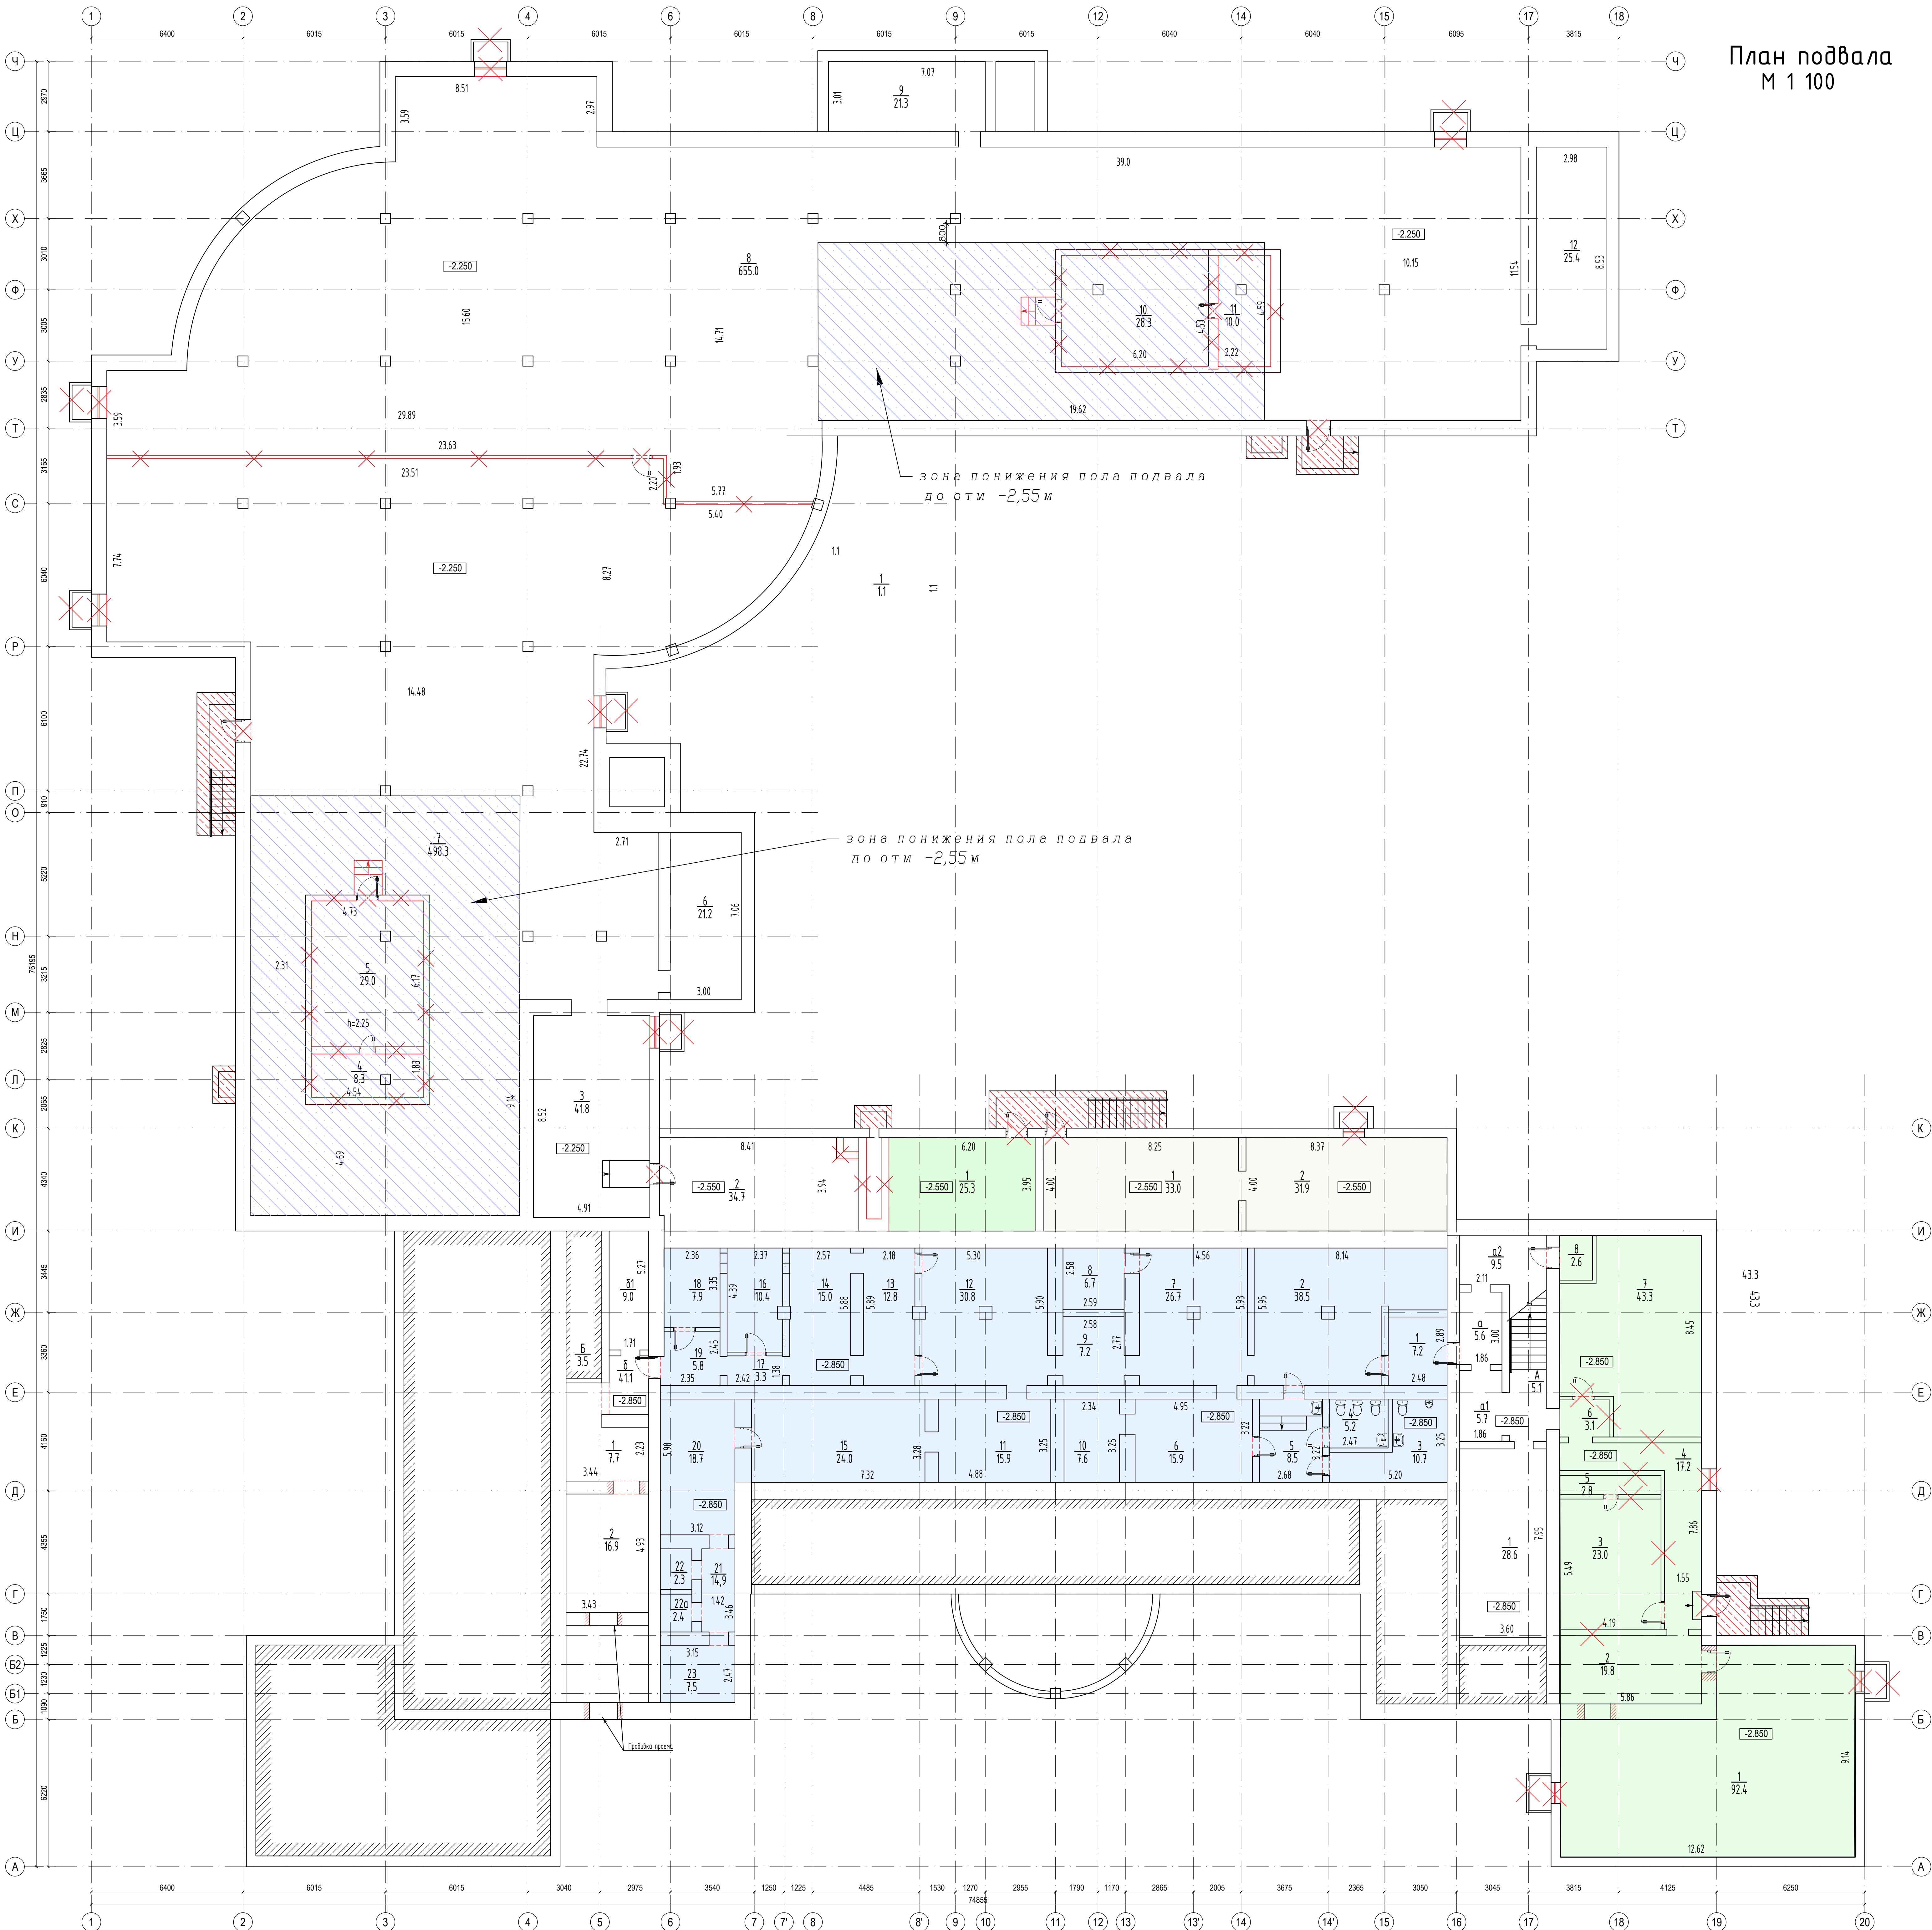


План подвала
М 1 100

Экспликация помещений подвала		
Номер помеще-ния	Наименование	Площадь, м2
1	Водонагревательная	92.4
2	Помещение техническое	19.8
3	Вентиляторная	23.0
4	Коридор	17.2
5	Вентиляторная	2.8
6	Коридор	3.1
7	Бойлерная	43.3
8	Помещение подсобное	2.6
Всего		204.2
А	Клетка лестничная	5.1
а	Коридор	5.6
а1	Коридор	5.1
а2	Коридор	9.5
Б	Клетка лестничная	3.5
Б	Коридор	4.1
В1	Помещение подсобное	9.0
Всего		42.5
1	Помещение специальное	7.2
2	Помещение специальное	38.5
3	Санузел	10.7
4	Санузел	5.2
5	Коридор	8.5
6	Помещение специальное	15.9
7	Помещение специальное	26.7
8	Помещение специальное	6.7
9	Помещение специальное	7.2
10	Помещение специальное	7.6
11	Помещение специальное	15.9
12	Помещение специальное	30.8
13	Помещение специальное	12.8
14	Помещение специальное	15.0
15	Помещение специальное	24.0
16	Помещение специальное	10.4
17	Коридор	3.3
18	Помещение специальное	7.9
19	Коридор	5.8
20	Помещение специальное	18.7
21	Помещение специальное	4.9
22	Шоха вентиляционная	2.3
22а	Шоха вентиляционная	2.4
23	Помещение специальное	7.5
Всего		295.9
1	Помещение техническое	28.6
Всего		28.6
1	Помещение техническое	25.3
Всего		25.3
1	Помещение техническое	33.0
2	Помещение техническое	31.9
Всего		64.9
1	Коридор	7.7
2	Помещение техническое	16.9
Всего		24.6

Экспликация помещений техподполья		
Номер помеще-ния	Наименование	Площадь, м2
1	Вентиляторная	1.9
2	Вентиляторная	34.7
3	Подполье техническое	41.8
4	Вентиляторная	8.3
5	Вентиляторная	29.0
6	Подполье техническое	21.2
7	Подполье техническое	498.3
8	Подполье техническое	655.0
9	Подполье техническое	21.3
10	Вентиляторная	28.3
11	Вентиляторная	10.0
12	Подполье техническое	25.4
Всего		1375.2

- Условные обозначения:
- сохраняемые несущие конструкции
 - демонтаж оконных блоков
 - демонтаж витражей
 - демонтаж внутренних витражей и окон
 - демонтаж перегородок
 - демонтаж дверных блоков
 - разбираемые конструкции
 - демонтаж стенок под проем
 - демонтаж лифта
 - пробивка проема


План 1 этажа

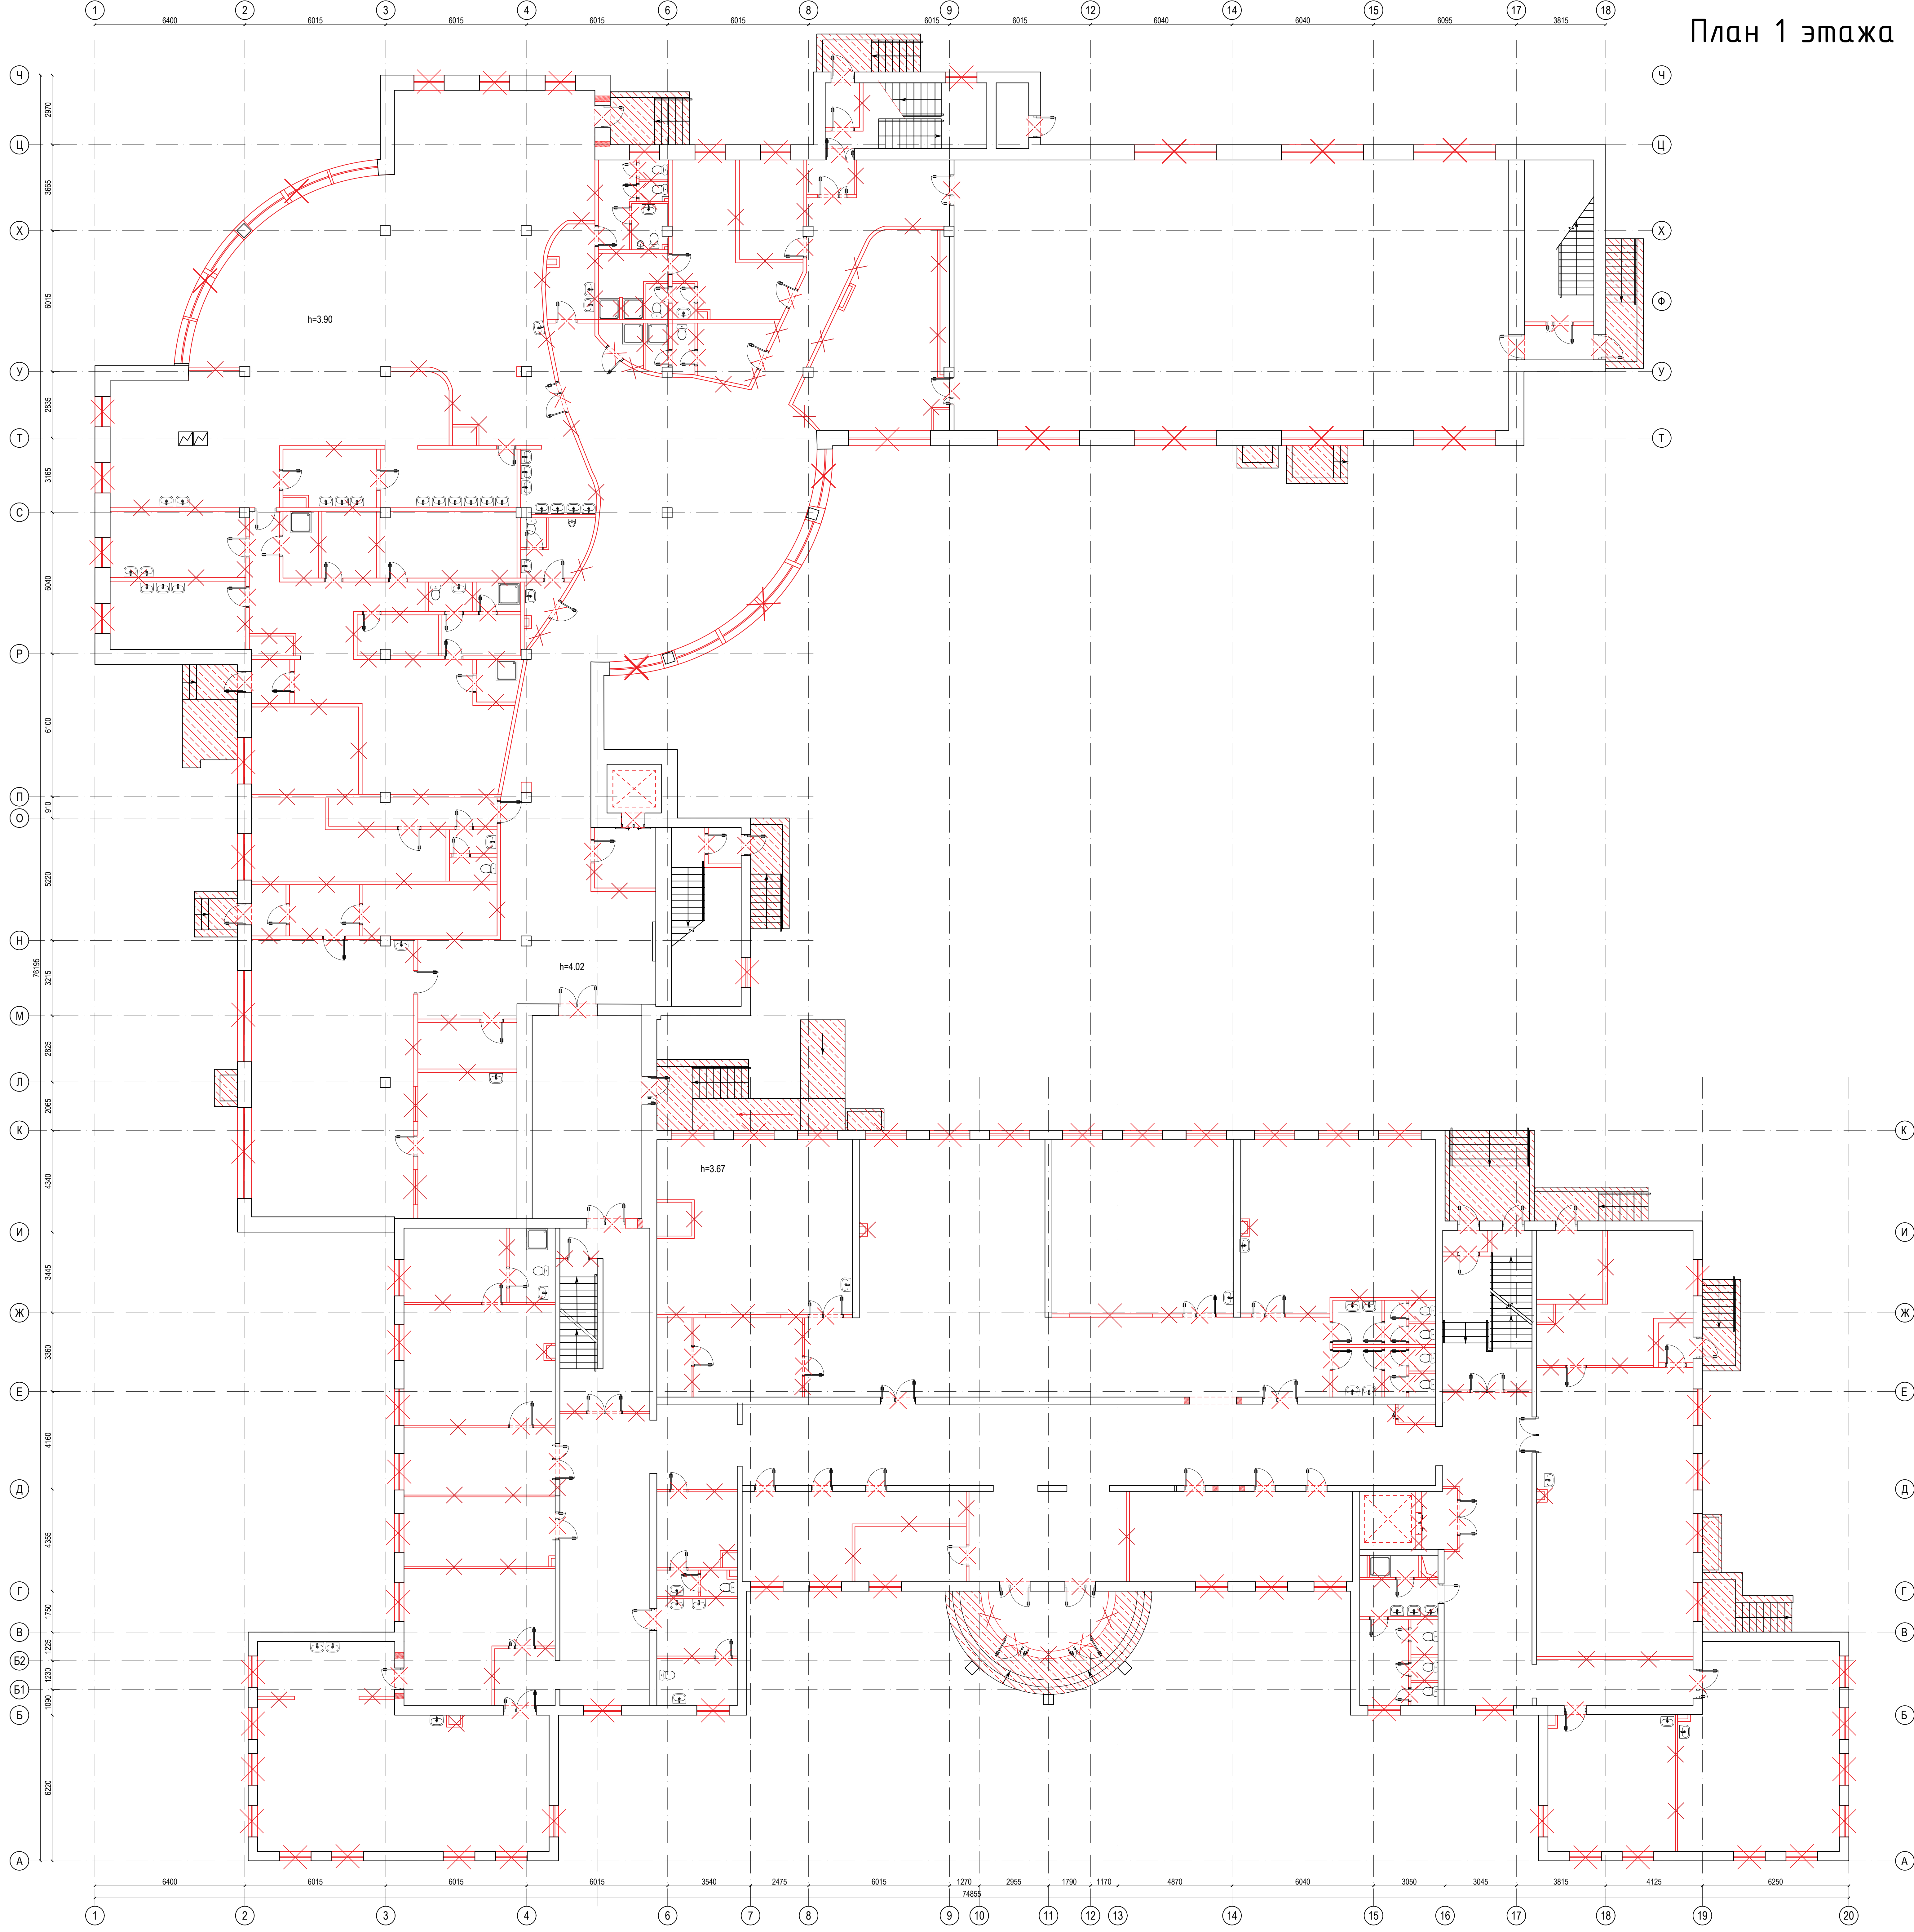


Условные обозначения:

- сохраняемые несущие конструкции
- демонтаж оконных блоков
- демонтаж перегородок
- демонтаж дверных блоков
- демонтаж внутренних перегородок и окон
- демонтаж перегородок
- демонтаж дверных блоков
- разбираемые конструкции
- демонтаж стенки под проем
- демонтаж лифта

										16-25/Г-П-АР		
										Капитальный ремонт общеобразовательного учреждения (ГБОУ "Школа №4297", расположенного по адресу: г.Москва, 5-ая ул.Соколиной Горы, д.14)		
										Архитектура-планировочные решения		
										П	2	Листов
										План демонтажа 1 этажа. М 1:100		
										АЗУРИТ		
										ФОРМАТ А0		

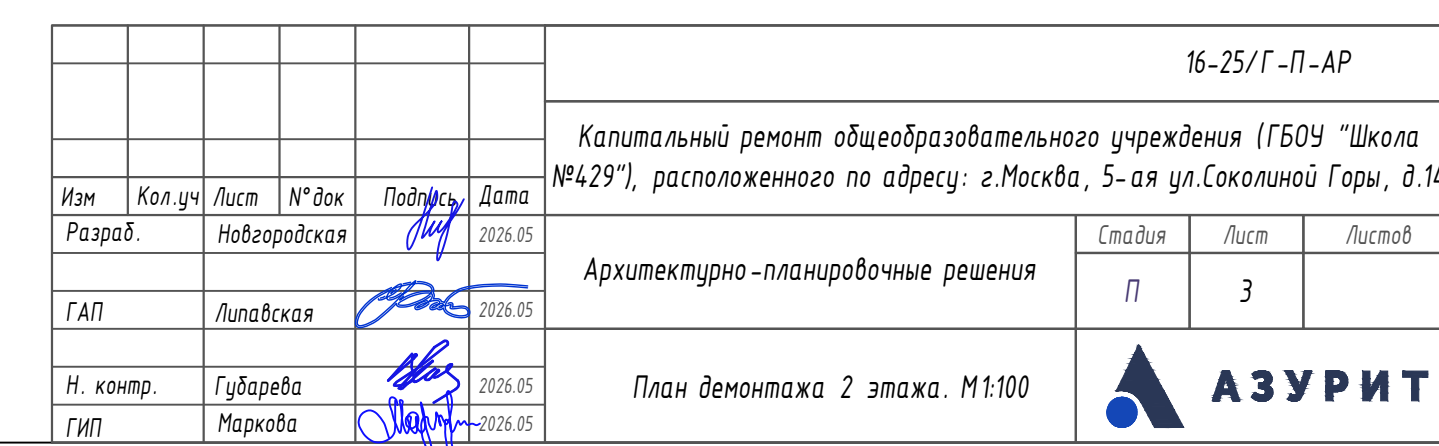

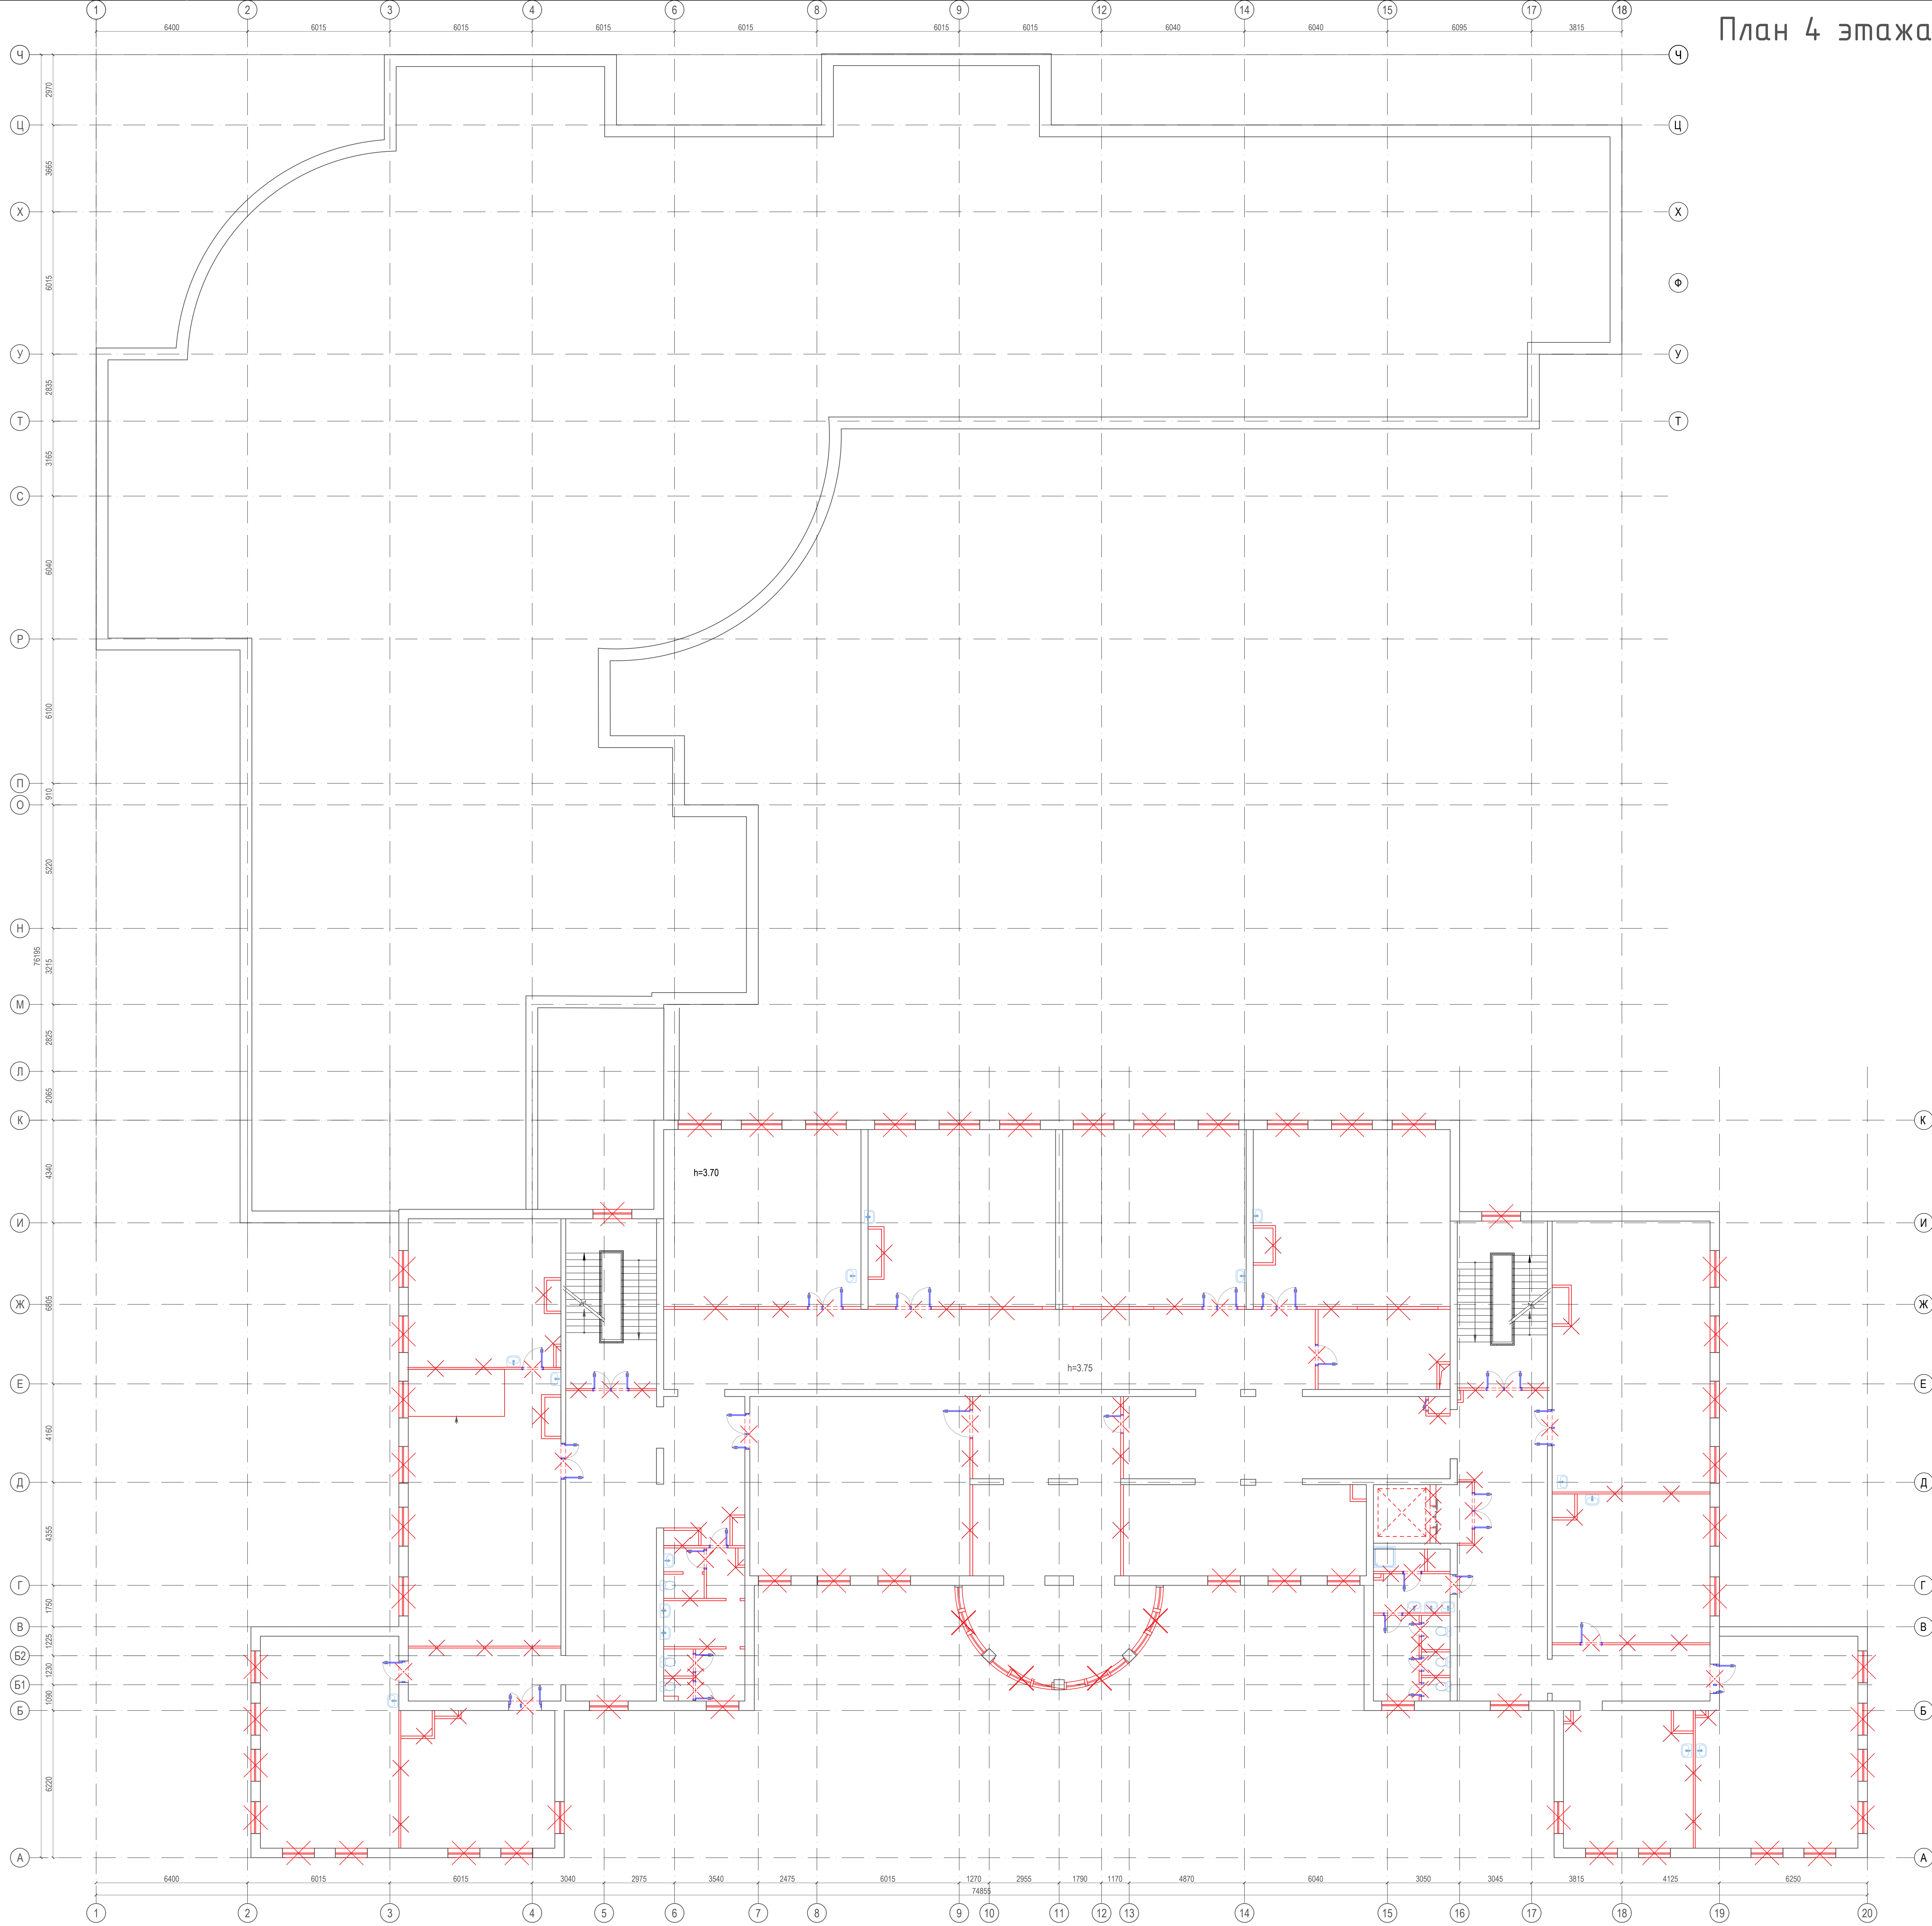


Условные обозначения:

- сохраняемые несущие конструкции
- демонтаж оконных блоков
- демонтаж витражей
- демонтаж внутренних витражей и окон
- демонтаж перегородок
- демонтаж дверных блоков
- разбираемые конструкции
- демонтаж стенки под проем
- демонтаж лифта


						18-25/Г-П-АР		
						Капитальный ремонт общеобразовательного учреждения (ГБОУ "Школа №429"), расположенного по адресу: г. Москва, 5-ая ул. Соколиной Горы, д.14		
Изм.	Кол. изм.	Лист	№ док.	Подпись	Дата	Архитектурно-планировочные решения		
Разраб.		Наблюдатель			2020.05	Степан	Лист	Листов
ГАП		Алаловская			2020.05	П	5	
И. контр.		Губарева			2020.05	План демонтажа 4 этажа. М1:100		
Гип		Маркова			2020.05	АЗУРИТ		

План техэтажа

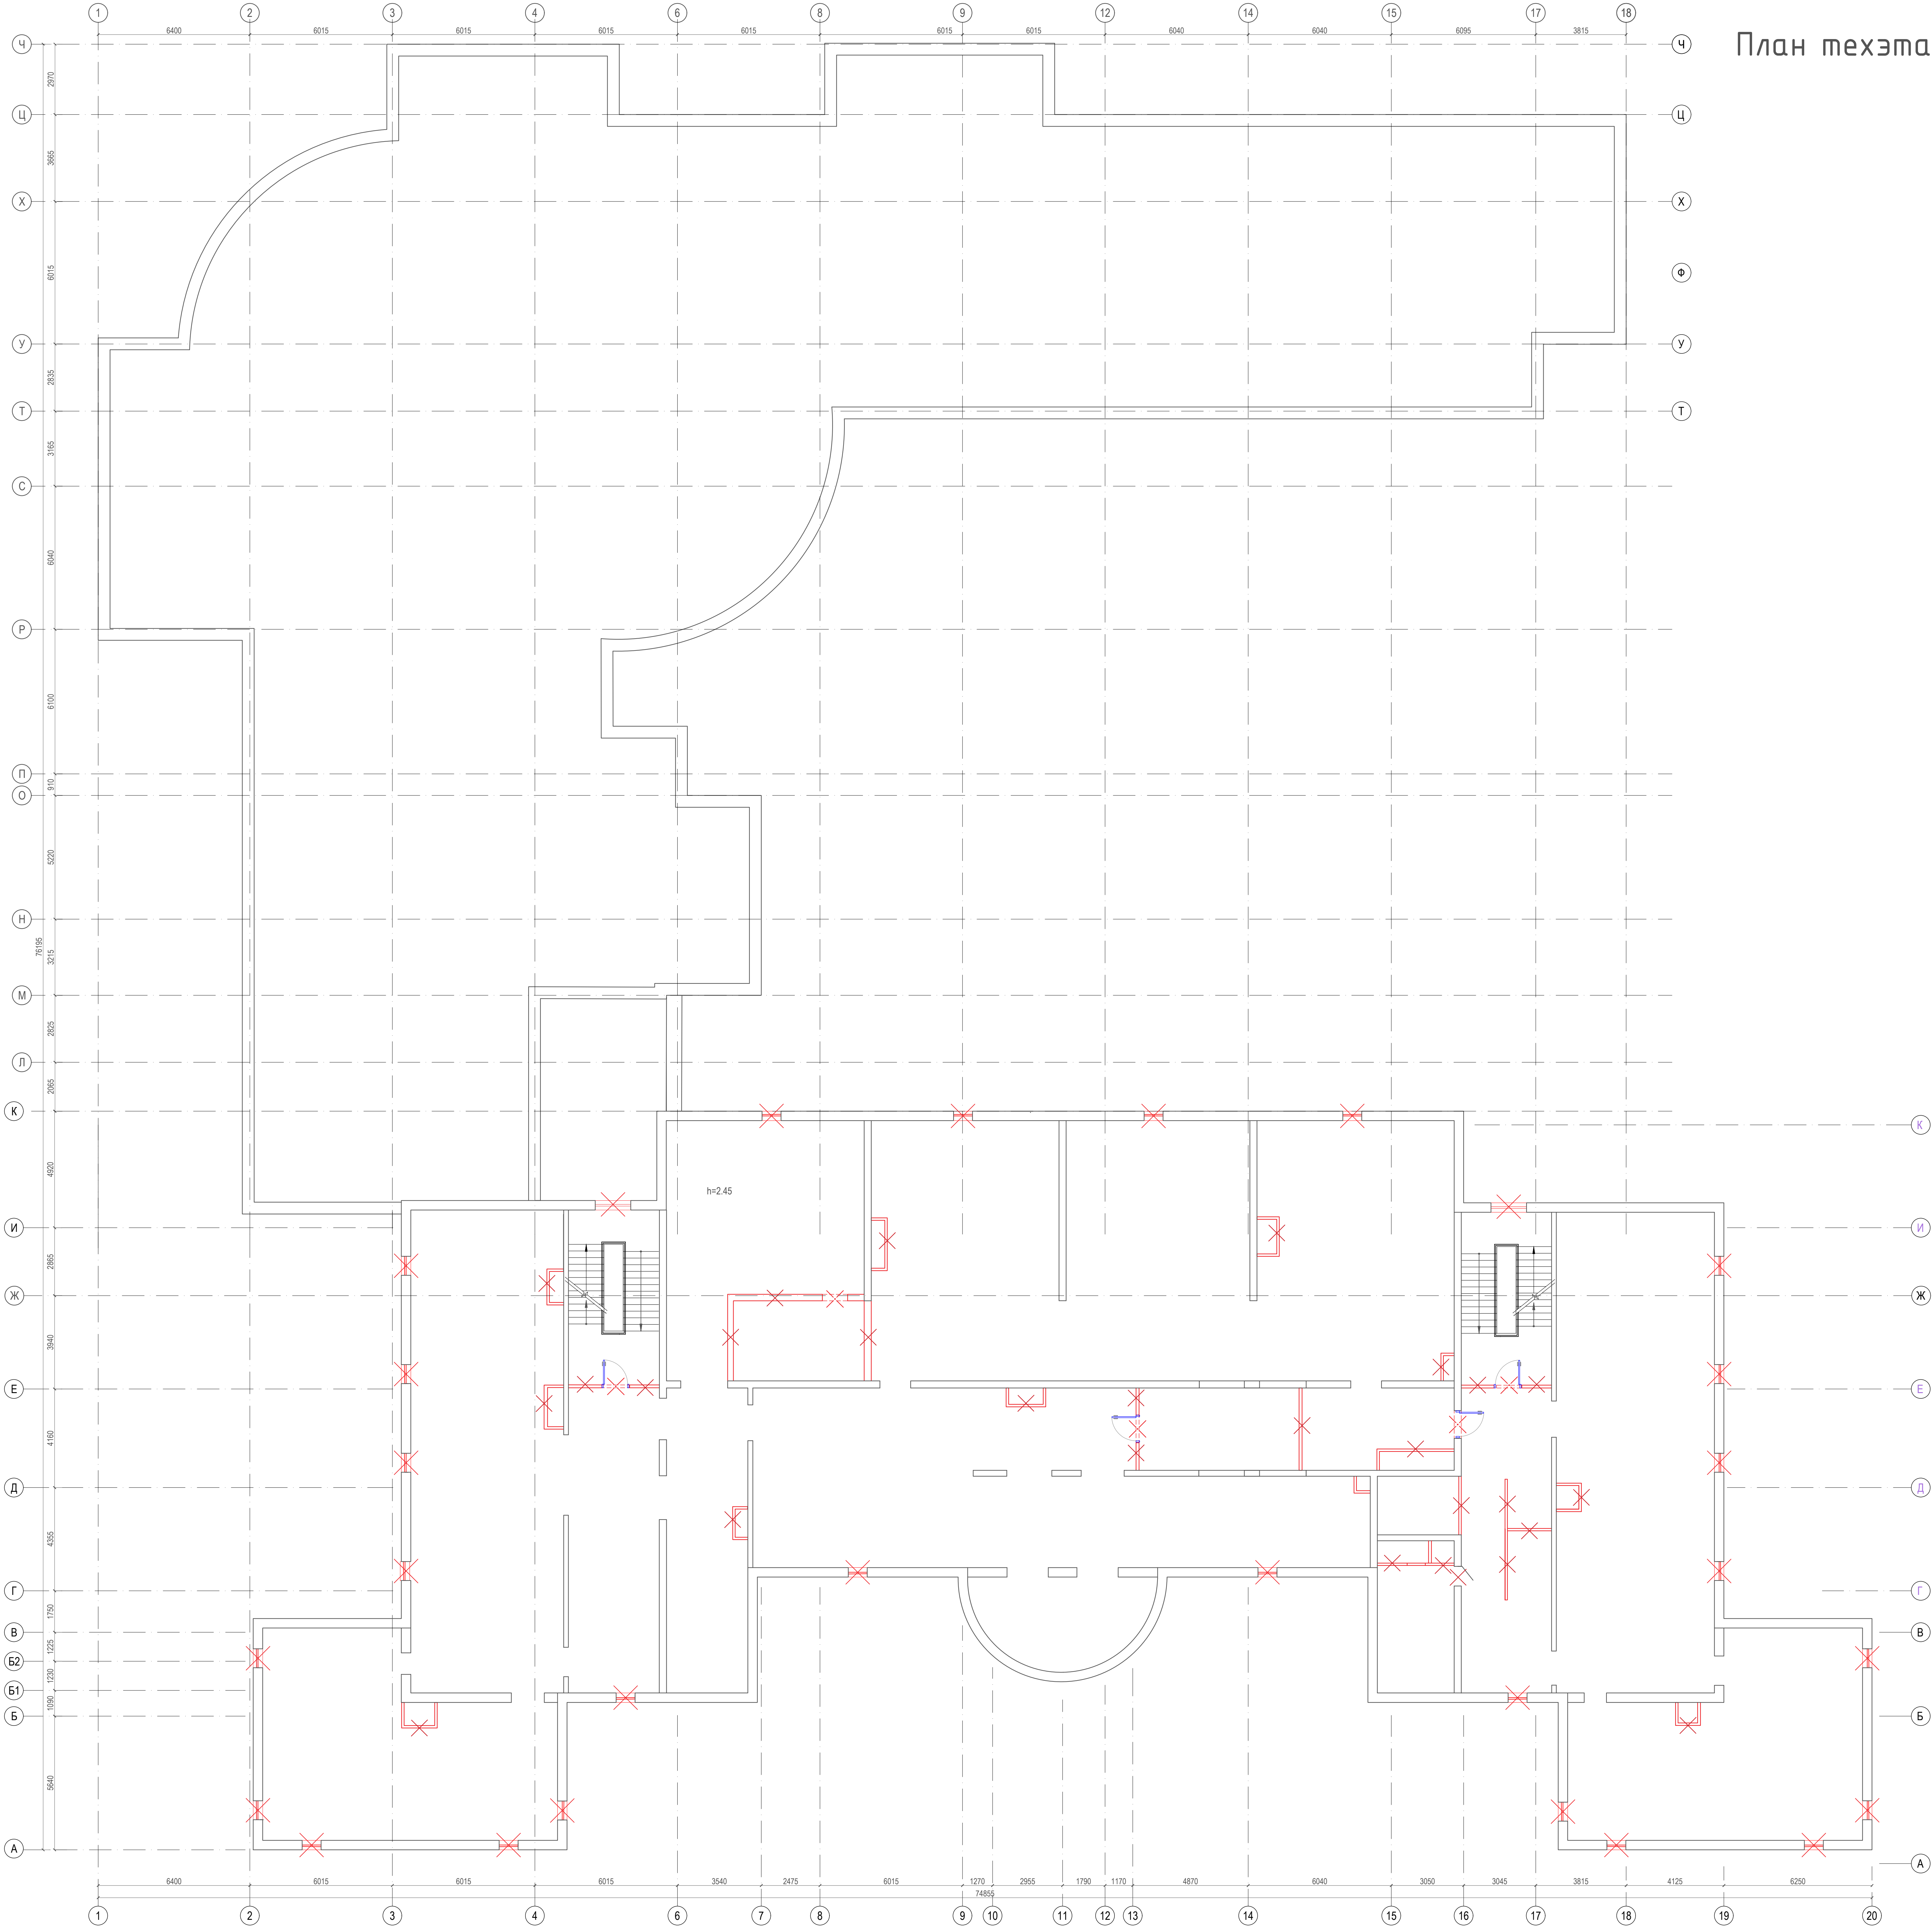

- Условные обозначения:
- сохраняемые несущие конструкции
 - демонтаж оконных блоков
 - демонтаж витражей
 - демонтаж внутренних витражей и окон
 - демонтаж перегородок
 - демонтаж дверных блоков

План кровли

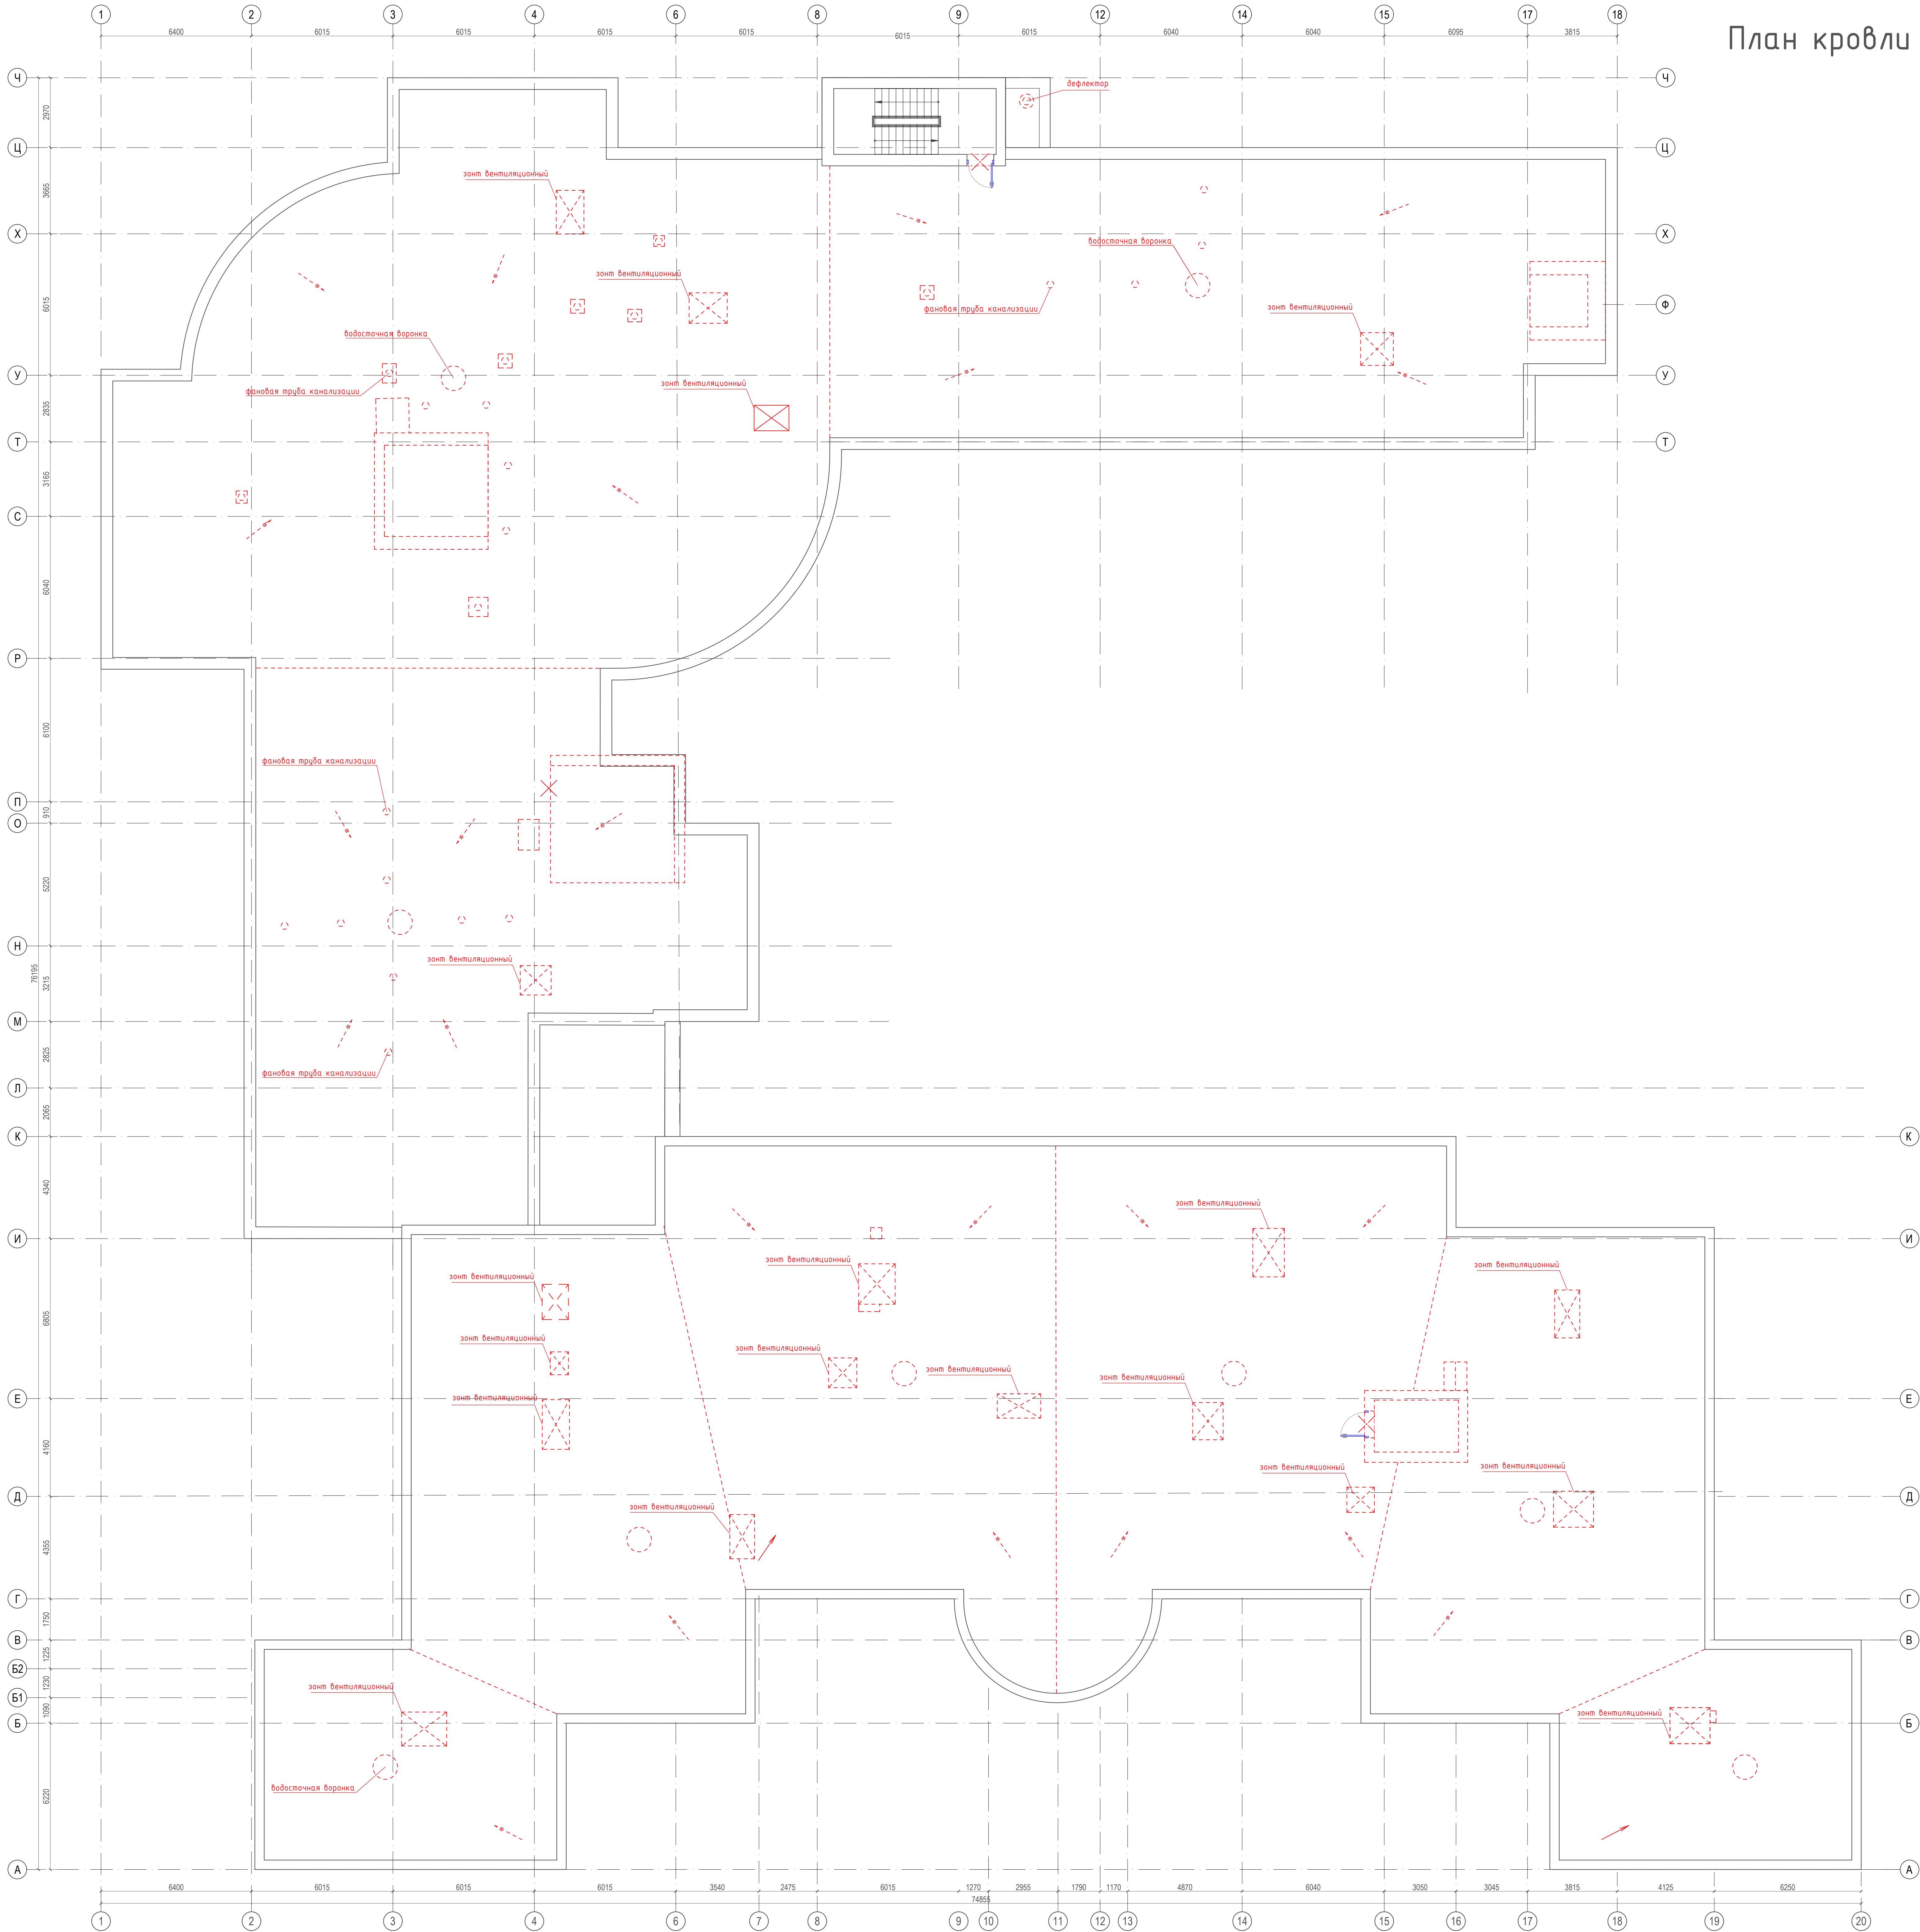

Условные обозначения

- демонтаж кровельных настилов
- демонтаж дверей

						18-25/Г-П-АР		
						Капитальный ремонт общеобразовательного учреждения (ГБОУ "Школа №429"), расположенного по адресу: г. Москва, 5-ая ул. Соколиной Горы, д.14		
Изм.	Кол. изм.	Лист	№ док.	Подпись	Дата	Архитектурно-планировочные решения		
Разраб.			Наблюдатель		2020.05	Степан	Лист	Листов
ГАП			Алалмазя		2020.05	П	7	
И. контр.			Губарева		2020.05	План демонтажа кровли. М1:100		
Гип			Маркова		2020.05	АЗУРИТ		

ВЕДОМОСТЬ ВНУТРЕННИХ ДЕМОНТАЖНЫХ РАБОТ											
N/пп	Наименование работ	Ед.изм.	подвал	1 этаж	2 этаж	3 этаж	4 этаж	тех. этаж	крыша	ВСЕГО	ПРИМЕЧАНИЕ
1	Очистка несущих стен помещений от штукатурного слоя	м²	1509.0	3295.0	3058.0	3078.0	2054.0	1726.0	-	14720.0	
	Площадь стен помещения ГО		1162.0	-	-	-	-	-	-	1162.0	
2	Демонтаж керамической плитки с существующих несущих стен	м²	-	285.0	83.0	83.0	74.0	-	-	525.0	
	Демонтаж напольного плитинуса ПВХ		п.м	-	388.0	960.0	863.0	600.0	-	-	2811.0
	Демонтаж напольного плитинуса деревянного	п.м	-	65.0	-	146.0	-	-	-	211.0	
	Демонтаж напольного плитинуса керамогранитного h=100мм		п.м	-	700.0	121.0	121.0	72.0	50.0	-	1064.0
3	Демонтаж напольного покрытия - линолеум	м²	-	565.0	1869.0	2164.7	1116.0	-	-	5714.7	
	Демонтаж напольного покрытия - керамогранитная плитка		м²	659.0	1542.5	128.0	106.0	76.0	-	-	2511.5
	Демонтаж напольного покрытия - керамогранитная плитка (лестн. клетки)	м²	11.5	195.0	146.0	146.0	89.0	61.0	-	648.5	
	Демонтаж напольного покрытия - деревянный пол, паркет		м²	-	272.0	-	185.0	-	-	-	457.0
	Демонтаж армированной цем. песч. стяжки толщиной 60мм	м²	670.5	2379.5	1997.0	2455.0	1192.0	-	-	8694.0	
	Демонтаж подвесных потолков типа Армстронг		м³	40.2	142.8	119.8	147.3	71.5	-	-	521.6
4	Демонтаж подвесных потолков типа Армстронг	м²	-	387.1	946.0	847.0	792.3	-	-	2972.4	
	Демонтаж речного металлического потолка		м²	-	198.1	121.2	97.0	72.0	-	-	488.3
	Демонтаж потолка из алюминиевых панелей	м²	-	78.8	-	-	-	-	-	78.8	
	Очистка потолков от клеевой покраски		м²	-	1868.2	1278.0	1655.2	600.0	-	-	5401.4
	Очистка потолков от побелки	м²	656.0	-	-	-	-	-	-	656.0	
	Подоконники										
5	Демонтаж подоконных досок	п.п	7.3	97.3	102.4	100.8	84.3	31.5	-	423.6	
	Длина доски 1210х500мм		шт.	6	-	-	-	-	26	-	32
	Длина доски 1310х500мм	шт.	-	30	29	29	19	-	-	107	
	Длина доски 1600х500мм		шт.	-	23	27	26	24	-	-	100
	Длина доски 1770х500мм	шт.	-	12	12	12	12	-	-	48	
	Длина доски 2700х500мм		шт.	-	-	1	1	-	-	-	2
6	Очистка внутренних оконных откосов	м²	2.9	159.4	159.4	159.4	79.4	12.5	-	573.0	
			п.м	19.2	665.7	665.7	665.7	332.9	83.2	-	2432.4
7	Демонтаж перегородок	м³	-	50.3	40.4	44.8	27.6	15.4	-	179	
	Демонтаж перегородок из газобетона толщиной 100мм.		м³	25.8	201.7	141.8	156.6	47.5	18.5	-	592
	Демонтаж зашивки инженерных коммуникаций листами влагостойкого гипсокартона в 2 слоя с одной стороны	м²	-	107.3	74.4	68.8	70.3	-	-	321	
	Сантехнические перегородки										
8	Перегородака сантехническая (СП-1) в составе с дверью 1шт. 950х2300(н)мм, 150мм от у.ч.л. высотой 2150ш	шт.	-	1	-	1	-	-	-	2	
	Перегородака сантехническая(СП-2) в составе с дверью 2шт. 1850х2300(н)мм, 150мм от у.ч.л. высотой 2150		м²	-	2.0	-	2.0	-	-	-	4.0
	Перегородака сантехническая(СП-2) в составе с дверью 2шт. 1850х2300(н)мм, 150мм от у.ч.л. высотой 2150	шт.	-	1	1	1	1	-	-	4	
	Перегородака сантехническая(СП-2.1) в составе с дверью 2шт. 1850х2300(н)мм, 150мм от у.ч.л. высотой 2150		м²	-	4.0	4.0	4.0	4.0	-	-	16.0
	Перегородака сантехническая(СП-2.1) в составе с дверью 2шт. 1850х2300(н)мм, 150мм от у.ч.л. высотой 2150	шт.	-	2	1	2	1	-	-	6	
	Перегородака сантехническая (СП-3) в составе с дверью 3шт. 2800х2300(н)мм, 150мм от у.ч.л. высотой 2150		м²	-	8.0	4.0	8.0	4.0	-	-	24.0
	Перегородака сантехническая (СП-3) в составе с дверью 3шт. 2800х2300(н)мм, 150мм от у.ч.л. высотой 2150	шт.	-	1	1	1	1	-	-	4	
	Перегородака сантехническая (СП-4) в составе с дверью 4шт. 3000х2300(н)мм, 150мм от у.ч.л. высотой 2150		м²	-	6.0	6.0	6.0	6.0	-	-	24.0
	Перегородака сантехническая (СП-4) в составе с дверью 4шт. 3000х2300(н)мм, 150мм от у.ч.л. высотой 2150	шт.	-	-	1	-	-	-	-	1	
	Перегородака сантехническая (СП-5) в составе с дверью 5шт. 4800х2300(н)мм, 150мм от у.ч.л. высотой 2150		м²	-	10.3	10.3	-	-	-	-	20.6
	Перегородака сантехническая (СП-6) в составе с дверью 6шт. 5180х2300(н)мм, 150мм от у.ч.л. высотой 2150	шт.	-	-	1	-	-	-	-	1	
	Перегородака сантехническая (СП-7) в составе с дверью 7шт. 4700х2300(н)мм, 150мм от у.ч.л. высотой 2150		м²	-	11.1	-	-	-	-	-	11.1
	Перегородака сантехническая (СП-7) в составе с дверью 7шт. 4700х2300(н)мм, 150мм от у.ч.л. высотой 2150	шт.	-	-	-	1	1	-	-	2	
	Перегородака сантехническая (СП-8) в душевых 1100х2300(н)мм, 150мм от у.ч.л. высотой 2150		м²	-	-	-	10.1	10.1	-	-	20.2
	Перегородака сантехническая (СП-8) в душевых 1100х2300(н)мм, 150мм от у.ч.л. высотой 2150	шт.	-	2	-	-	-	-	-	2	
	Перегородака сантехническая (СП-9) 550х2300(н)мм, 150мм от у.ч.л. высотой 2150		м²	-	4.7	-	-	-	-	-	4.7
	Перегородака сантехническая (СП-9) 550х2300(н)мм, 150мм от у.ч.л. высотой 2150	шт.	-	2	4	2	2	-	-	10	
	Перегородака сантехническая (СП-10) 1150х2300(н)мм, 150мм от у.ч.л. высотой 2150		м²	-	2.4	4.8	2.4	2.4	-	-	12.0
	Перегородака сантехническая (СП-10) 1150х2300(н)мм, 150мм от у.ч.л. высотой 2150	шт.	-	4	8	3	3	-	-	18	
	Перегородака сантехническая (СП-11) 1200х2300(н)мм, 150мм от у.ч.л. высотой 2150		м²	-	9.9	19.8	7.4	7.4	-	-	44.5
	Перегородака сантехническая (СП-11) 1200х2300(н)мм, 150мм от у.ч.л. высотой 2150	шт.	-	8	11	8	6	-	-	33	
	Перегородака сантехническая (СП-11) 1200х2300(н)мм, 150мм от у.ч.л. высотой 2150		м²	-	20.6	28.4	20.6	15.5	-	-	85.1
9	Трансформируемая перегородка (ПТ-1) 6370х2450мм по направляющим профилям в полу и потолке, вес не более 100кг/м2, с заполнением звукоизоляционными панелями	шт.	-	-	-	-	1	-	-	1	
	Перегородака 4470х3940ш из панели стеновой кубообразной 80х80мм Pergafen Pergola 6/2-4, с шагом 160мм, толщина металла 2-3мм, текстура светлое дерево, группа горючести НГ или аналог		м.п	-	110.3	-	-	-	-	-	110.3
	Перегородака 4610х3670ш из панели стеновой кубообразной 80х80мм Pergafen Pergola 6/2-4, с шагом 160мм, толщина металла 2-3мм, текстура светлое дерево, группа горючести НГ или аналог	м.п	-	99.1	-	-	-	-	-	99.1	
	Экран (Э-3) толщ. 150 мм, изст на отк. 2 м от у.ч.л. Незеркач. плита 2-го слоя -125мм Минеральная плита 40кг/куб.м 1спой-50мм Незеркач. плита 2-го слоя -125 мм Каркас - стальной профиль ПС 100/50		м2	-	60.0	-	-	-	-	-	60.0
11	Перемычки	шт.	3	7	4	3	2	2	-	21	
	Тип ПР-1 L110х110х8 мм, L=1400 мм		шт.	-	31	8	12	4	-	-	55
	Тип ПР-2 L110х110х8 мм, L=1500 мм	шт.	-	4	2	2	1	-	-	9	
	Тип ПР-3 L110х110х8 мм, L=1600 мм		шт.	2	3	8	8	4	-	-	25
	Тип ПР-4 L110х110х8 мм, L=1900 мм	шт.	-	7	7	5	2	-	-	21	
	Тип ПР-5 L110х110х8 мм, L=2200 мм		шт.	-	1	-	-	-	-	-	1

	Подоконники										
ПД-1	Подоконник: Доска из березовой фанеры толщ. не менее 24мм, заоблачивание края, отшлифованная поверхность, технические зазоры, ПТХ обработка КМО, Спаль-Комплексы, НТК "Олимп" *	м²	-	41.2	54.8	55.6	31.3	-	-	182.9	
	Экран для радиаторов высотой 900мм из МДФ: толщина фасада 12мм, каркас из фанеры 15мм, окрашен матовым лаком с двух сторон, цвет фасада - белая матовая эмаль	п.м	-	146.0	241.5	244.4	150.0	-	-	781.9	
ПД-2	Подоконник керамогранитный, цвет "голд камень", поверхность матовая, обработка ректифицированная, зазоры в цвет плитки, 600х450х15мм, Керага Magazzi ПРО ЛАЙН (СТОН СЕРЫЙ СВЕТЛЫЙ НАТУРАЛЬНЫЙ) 004x10200	м²	-	1.0	3.1	3.1	0.9	0.5	-	8.6	
	Подоконник керамогранитный, цвет "голд камень", поверхность матовая, обработка ректифицированная, зазоры в цвет плитки, цоколя Г-образный в строенном исполнении, 600х400х9 мм, Керага Magazzi Фьюжн Пепельный (светлый обрезной) DL6007200, Керага Magazzi Про Стон серый светлый обрезной 004x10200	м²	-	0.4	0.8	0.4	0.4	-	-	2.0	
ПД-3	Подоконник керамогранитный, цвет "голд камень", поверхность матовая, обработка ректифицированная, зазоры в цвет плитки, цоколя Г-образный в строенном исполнении, 600х400х9 мм, Керага Magazzi Фьюжн Пепельный (светлый обрезной) DL6007200, Керага Magazzi Про Стон серый светлый обрезной 004x10200	м²	-	20.2	5.9	2.5	-	-	-	28.6	
	Подоконник керамогранитный, цвет "голд камень", поверхность матовая, обработка ректифицированная, зазоры в цвет плитки, цоколя Г-образный в строенном исполнении, 600х400х9 мм, Керага Magazzi Фьюжн Пепельный (светлый обрезной) DL6007200, Керага Magazzi Про Стон серый светлый обрезной 004x10200	м²	-	20.2	5.9	2.5	-	-	-	28.6	
ПД-5	Подоконник керамогранитный, цвет "голд камень", поверхность матовая, обработка ректифицированная, зазоры в цвет плитки, цоколя Г-образный в строенном исполнении, 600х400х9 мм, Керага Magazzi Фьюжн Пепельный (светлый обрезной) DL6007200, Керага Magazzi Про Стон серый светлый обрезной 004x10200	м²	1.5	-	0.8	0.7	-	3.3	-	6.3	
	Подоконник керамогранитный, цвет "голд камень", поверхность матовая, обработка ректифицированная, зазоры в цвет плитки, цоколя Г-образный в строенном исполнении, 600х400х9 мм, Керага Magazzi Фьюжн Пепельный (светлый обрезной) DL6007200, Керага Magazzi Про Стон серый светлый обрезной 004x10200	м²	1.5	-	0.8	0.7	-	3.3	-	6.3	
ПД-7	Подоконник: Доска из березовой фанеры толщ. не менее 24мм, заоблачивание края, отшлифованная поверхность, технические зазоры, ПТХ обработка КМО, Спаль-Комплексы, НТК "Олимп" *	м²	-	-	-	17.2	-	-	-	17.2	
	Экран для радиаторов высотой 450мм из МДФ: толщина фасада 12мм, каркас из фанеры 15мм, окрашен матовым лаком с двух сторон, цвет фасада - белая матовая эмаль	п.м	-	-	-	28.7	-	-	-	28.7	
13	Подоконник										
ПД-7	Подоконник: Доска из березовой фанеры толщ. не менее 24мм, заоблачивание края, отшлифованная поверхность, технические зазоры, ПТХ обработка КМО, Спаль-Комплексы, НТК "Олимп" *	м²	-	7.5	-	-	7.5	-	-	15.0	
	Экран для радиаторов высотой 450мм из МДФ: толщина фасада 12мм, каркас из фанеры 15мм, окрашен матовым лаком с двух сторон, цвет фасада - белая матовая эмаль	п.м	-	12.4	-	-	12.4	-	-	24.8	
ПД-7	Подоконник: Доска из березовой фанеры толщ. не менее 24мм, заоблачивание края, отшлифованная поверхность, технические зазоры, ПТХ обработка КМО, Спаль-Комплексы, НТК "Олимп" *	м²	-	-	-	5.0	5.0	-	-	10.0	
	Экран для радиаторов высотой 450мм из МДФ: толщина фасада 12мм, каркас из фанеры 15мм, окрашен матовым лаком с двух сторон, цвет фасада - белая матовая эмаль	п.м	-	-	-	8.3	8.3	-	-	16.6	
ПД-8	Подоконник: Доска из березовой фанеры толщ. не менее 24мм, заоблачивание края, отшлифованная поверхность, технические зазоры, ПТХ обработка КМО, Спаль-Комплексы, НТК "Олимп" *	м²	-	-	-	8.3	8.3	-	-	16.6	
	Экран для радиаторов высотой 450мм из МДФ: толщина фасада 12мм, каркас из фанеры 15мм, окрашен матовым лаком с двух сторон, цвет фасада - белая матовая эмаль	п.м	-	-	-	1.0	1.0	-	-	2.0	
14	Спецификация подоконных доборов и экранов радиаторов										
15	Демонтаж внутренних оконных блоков из деревянных материалов	шт.	-	2	-	-	-	-	-	2	
16	Демонтаж внутренних дверных блоков	шт.	-	13.0	-	-	-	-	-	13.0	
Д-1	Дверь одностворчатая глухая композиционная из ПВХ 1033x2200h	шт.	-	1	-	-	-	-	-	1	
	Д-1п	шт.	-	2	-	-	-	-	-	2	
Д-2	Дверь одностворчатая глухая композиционная из ПВХ с отбойной пластиной на у.рук и ног. 1133x2200h	шт.	-	7	-	-	-	-	-	7	
	Д-2п	шт.	-	7	-	-	-	-	-	7	
Д-3	Дверь одностворчатая остекленная из алюминиевого профиля противопожарная EIW30(EIW15) с оклейкой мат. пленкой, 1130x2200h	шт.	-	2	2	2	2	-	-	8	
Д-3	Дверь одностворчатая остекленная из алюминиевого профиля с оклейкой матовой пленкой, 1130x2200h	шт.	-	4	1	4	1	-	-	10	
Д-4	Дверь одностворчатая остекленная из алюминиевого профиля с оклейкой матовой пленкой, 1130x2200h	шт.	-	9	5	5	2	-	-	21	
Д-4п	Дверь одностворчатая остекленная из алюминиевого профиля с оклейкой брон. матовой пленкой 1130x2200h	шт.	-	5	6	5	3	-	-	19	
Д-4,1п	Дверь одностворчатая остекленная из алюминиевого профиля с оклейкой брон. матовой пленкой 1130x2200h	шт.	-	1	-	-	-	-	-	1	
Д-5	Дверь одностворчатая остекленная из алюминиевого профиля с оклейкой мат. пленкой 1030x2200h	шт.	-	3	2	2	1	-	-	8	
Д-5п	Дверь одностворчатая остекленная из алюминиевого профиля с оклейкой мат. пленкой 1030x2200h	шт.	-	1	2	1	1	-	-	5	
Д-6	Дверь двустворчатая (полупотурная) остекленная из алюминиевого профиля 1500x2200h	шт.	-	5	9	8	8	-	-	30	
Д-6п	Дверь двустворчатая (полупотурная) остекленная из алюминиевого профиля 1500x2200h	шт.	-	6	2	6	2	-	-	16	
Д-7	Дверь двустворчатая (полупотурная) остекленная противопожарная EIW30 1700x2200h	шт.	-	-	-	-	-	-	-	-	
Д-7п	Дверь двустворчатая (полупотурная) остекленная противопожарная EIW30 1700x2200h	шт.	-	3	1	1	1	-	-	6	
Д-8	Дверь одностворчатая глухая композиционная из ПВХ 1,5мм 1133x2200h	шт.	-	1	-	-	-	-	-	1	
Д-8п	Дверь одностворчатая глухая композиционная из ПВХ 1,5мм 1133x2200h	шт.	-	1	-	-	-	-	-	1	
Д-9	Дверь одностворчатая металлопластиковая глухая 1667x2200h	шт.	1	2	2	2	1	-	-	8	
Д-9п	Дверь одностворчатая металлопластиковая глухая 1667x2200h	шт.	-	-	1	1	-	-	-	2	
Д-10	Дверь одностворчатая остекленная из алюминиевого профиля с оклейкой мат. пленкой 1230x2200h	шт.	-	1	-	-	-	-	-	1	
Д-11	Дверь одностворчатая (полупотурная) остекленная из алюминиевого профиля 1700x2200h	шт.	-	1	-	-	-	-	-	1	
Д-11п	Дверь одностворчатая (полупотурная) остекленная из алюминиевого профиля 1700x2200h	шт.	-	1	-	-	-	-	-	1	
Д-12	Дверь двустворчатая (полупотурная) остекленная противопожарная EIW15, 1700x2200h	шт.	-	5	4	4	1	-	-	14	
Д-12п	Дверь двустворчатая (полупотурная) остекленная противопожарная EIW15, 1700x2200h	шт.	-	2	2	3	2	-	-	9	
Д-13	Дверь полупотурная глухая композиционная с отбойной пластиной на у.рук и ног. 1584x2200h	шт.	-	1	-	-	-	-	-	1	
Д-13п	Дверь полупотурная глухая композиционная с отбойной пластиной на у.рук и ног. 1584x2200h	шт.	-	1	-	-	-	-	-	1	
Д-14	Дверь двустворчатая (полупотурная) остекленная противопожарная EIW30, 1500x2200h	шт.	-	-	1	-	-	-	-	2	
Д-14п	Дверь двустворчатая (полупотурная) остекленная противопожарная EIW30, 1500x2200h	шт.	-	-	-	-	-	-	-	-	
Д-15	Дверь одностворчатая металлопластиковая глухая 1667x2200h	шт.	-	2	-	-	-	1	-	3	
Д-15п	Дверь одностворчатая металлопластиковая глухая 1667x2200h	шт.	4	1	-	-	-	1	-	6	