

Российская Федерация
ООО "Шварцгрупп"

SCHWARTZ GROUP
intelligent office systems

ШК429

Рабочая документация
Светопрозрачные конструкции.
ПВХ и противопожарные окна.
5-ая ул. Соколиной Горы д.14

Заказчик: Общество с ограниченной
ответственностью «ГРАДИНВЕСТ»
Согласовано: _____

(Ф.И.О.)
Должность: _____
Подпись: _____
Дата: _____

Заказчик
Руководитель проекта
Инженер проекта

ГРАДИНВЕСТ
Ткаченко Евгений
Харитоновa Ирина

М.П.

Разработано: Общество с ограниченной
ответственностью «ШварцГрупп»

Согласовано: _____
(Ф.И.О.)
Должность: _____
Подпись: _____
Дата: _____

Москва
Август 2026

М.П.


Спецификация окон.

Наименов.	шир.	выс.	шт	цвет снаружи	цвет внутри	стеклопакет	моск. сетка	дет. замок	мех. Привод	эл. Привод	примечание	ширина проема (мин.)	высота проема (мин.)
ОК-1	1170*	1170*	3	Антрацит серый*	Антрацит серый*	СПД 40мм (4зак-14.Аг-4-14.Аг-4i.зак) -СМ1					СМ1	1200	1230
ОК-2	1270*	1170*	4	Антрацит серый*	Антрацит серый*	СПД 40мм (4зак-14.Аг-4-14.Аг-4i.зак) -СМ1	1	1			СМ1	1300	1230
ОК-3	1250	2140	61	Антрацит серый*	Антрацит серый*	СПД 40мм (4зак-14.Аг-4-14.Аг-4i.зак) -СМ1 СПД 40мм (4зак-14.Аг-4-12.Аг-6i.зак) -СМ4	1	2			СМ1- верх СМ4 -низ	1280	2200
ОК-3/1	1250	2140	1	Ral 7016 муар	Ral 7016 муар	СПД 42мм (6stg-14Аг-4i-12Аг-6зак)					Алюминий, Е30	1280	2200
ОК-3/2	1270	2140	9	Антрацит серый*	Антрацит серый*	СПД 40мм (4зак-14.Аг-4мат.-14.Аг-4i.зак) -СМ1 СПД 40мм (4зак-14.Аг-4мат.-12.Аг-6i.зак) -СМ4	1	2			СМ1- верх СМ4 -низ матовое стекло	1300	2200
ОК-3/3	1250	2140	2	Антрацит серый*	Антрацит серый*	СПД 40мм (4зак-14.Аг-4-14.Аг-4i.зак) -СМ1 СПД 40мм (4зак-14.Аг-4-12.Аг-6i.зак) -СМ4	1	2			СМ1- верх СМ4 -низ + броне пленка	1280	2200
ОК-3/4	1270	2140	29	Антрацит серый*	Антрацит серый*	СПД 40мм (4зак-14.Аг-4-14.Аг-4i.зак) -СМ1 СПД 40мм (4зак-14.Аг-4-12.Аг-6i.зак) -СМ4	1	2			СМ1- верх СМ4 -низ	1300	2200
ОК-4	1550	2140	72	Антрацит серый*	Антрацит серый*	СПД 40мм (4зак-14.Аг-4-14.Аг-4i.зак) -СМ1 СПД 40мм (4зак-14.Аг-4-12.Аг-6i.зак) -СМ4	1	2			СМ1- верх СМ4 -низ	1580	2200
ОК-4/1	1550	2140	11	Ral 7016 муар	Ral 7016 муар	СПД 42мм (6stg-14Аг-4i-12Аг-6зак)					Алюминий, Е30	1580	2200
ОК-4/1*	1740	2140	1	Ral 7016 муар	Ral 7016 муар	СПД 42мм (6stg-14Аг-4i-12Аг-6зак)					Алюминий, Е30	1770	2200
ОК-4/2	1270	2140	7	Антрацит серый*	Антрацит серый*	СПД 40мм (4зак-14.Аг-4-14.Аг-4i.зак) -СМ1 СПД 40мм (4зак-14.Аг-4-12.Аг-6i.зак) -СМ4	1	2			СМ1- верх СМ4 -низ	1300	2200
ОК-4/3	1550	2140	4	Антрацит серый*	Антрацит серый*	СПД 40мм (4зак-14.Аг-4-14.Аг-4i.зак) -СМ1 СПД 40мм (4зак-14.Аг-4-12.Аг-6i.зак) -СМ4	1	2			СМ1- верх СМ4 -низ	1580	2200
ОК-4/4	1730	2140	2	Антрацит серый*	Антрацит серый*	СПД 40мм (4зак-14.Аг-4-14.Аг-4i.зак) -СМ1 СПД 40мм (4зак-14.Аг-4-12.Аг-6i.зак) -СМ4	1	2			СМ1- верх СМ4 -низ	1760	2200
ОК-5	770	770	26	Антрацит серый*	Антрацит серый*	СПД 40мм (4зак-14.Аг-4-14.Аг-4i.зак) -СМ1					СМ1	800	800
ОК-6	1730	2140	3	Антрацит серый*	Антрацит серый*	СПД 40мм (4зак-14.Аг-4-14.Аг-4i.зак) -СМ1 СПД 40мм (4зак-14.Аг-4-12.Аг-6i.зак) -СМ4	1	2			СМ1- верх СМ4 -низ	1760	2200
ОК-7	1570	2140	40	Антрацит серый*	Антрацит серый*	СПД 40мм (4зак-14.Аг-4-14.Аг-4i.зак) -СМ1 СПД 40мм (4зак-14.Аг-4-12.Аг-6i.зак) -СМ4	1	2			СМ1- верх СМ4 -низ	1600	2200
ОК-7/1	1570	2140	4	Ral 7016 муар	Ral 7016 муар	СПД 42мм (6stg-14Аг-4i-12Аг-6зак)					Алюминий, Е30	1600	2200
ОК-7*	1570	2140	4	Антрацит серый*	Антрацит серый*	СПД 40мм (4зак-14.Аг-4-14.Аг-4i.зак) -СМ1 СПД 40мм (4зак-14.Аг-4-12.Аг-6i.зак) -СМ4	1	2			СМ1- верх СМ4 -низ	1600	2200
Итого			283				233	462	0	0			

★ - проектный размер.


						ШК429		
						5-ая ул. Соколиной Горы, д.14		
Изм.	Кол.уч	Лист	№ док.	Подпись	Дата	Спецификация заполнения оконных проемов.		Стадия
ГИП								Лист/Листов
Проверил	Ткаченко Евгений					РД		1/16
Разраб.	Харитоновна Ирина				18.08.2026			ООО "ШварцГрупп"
Н.контр.								

Плоск. 1-20 элжж

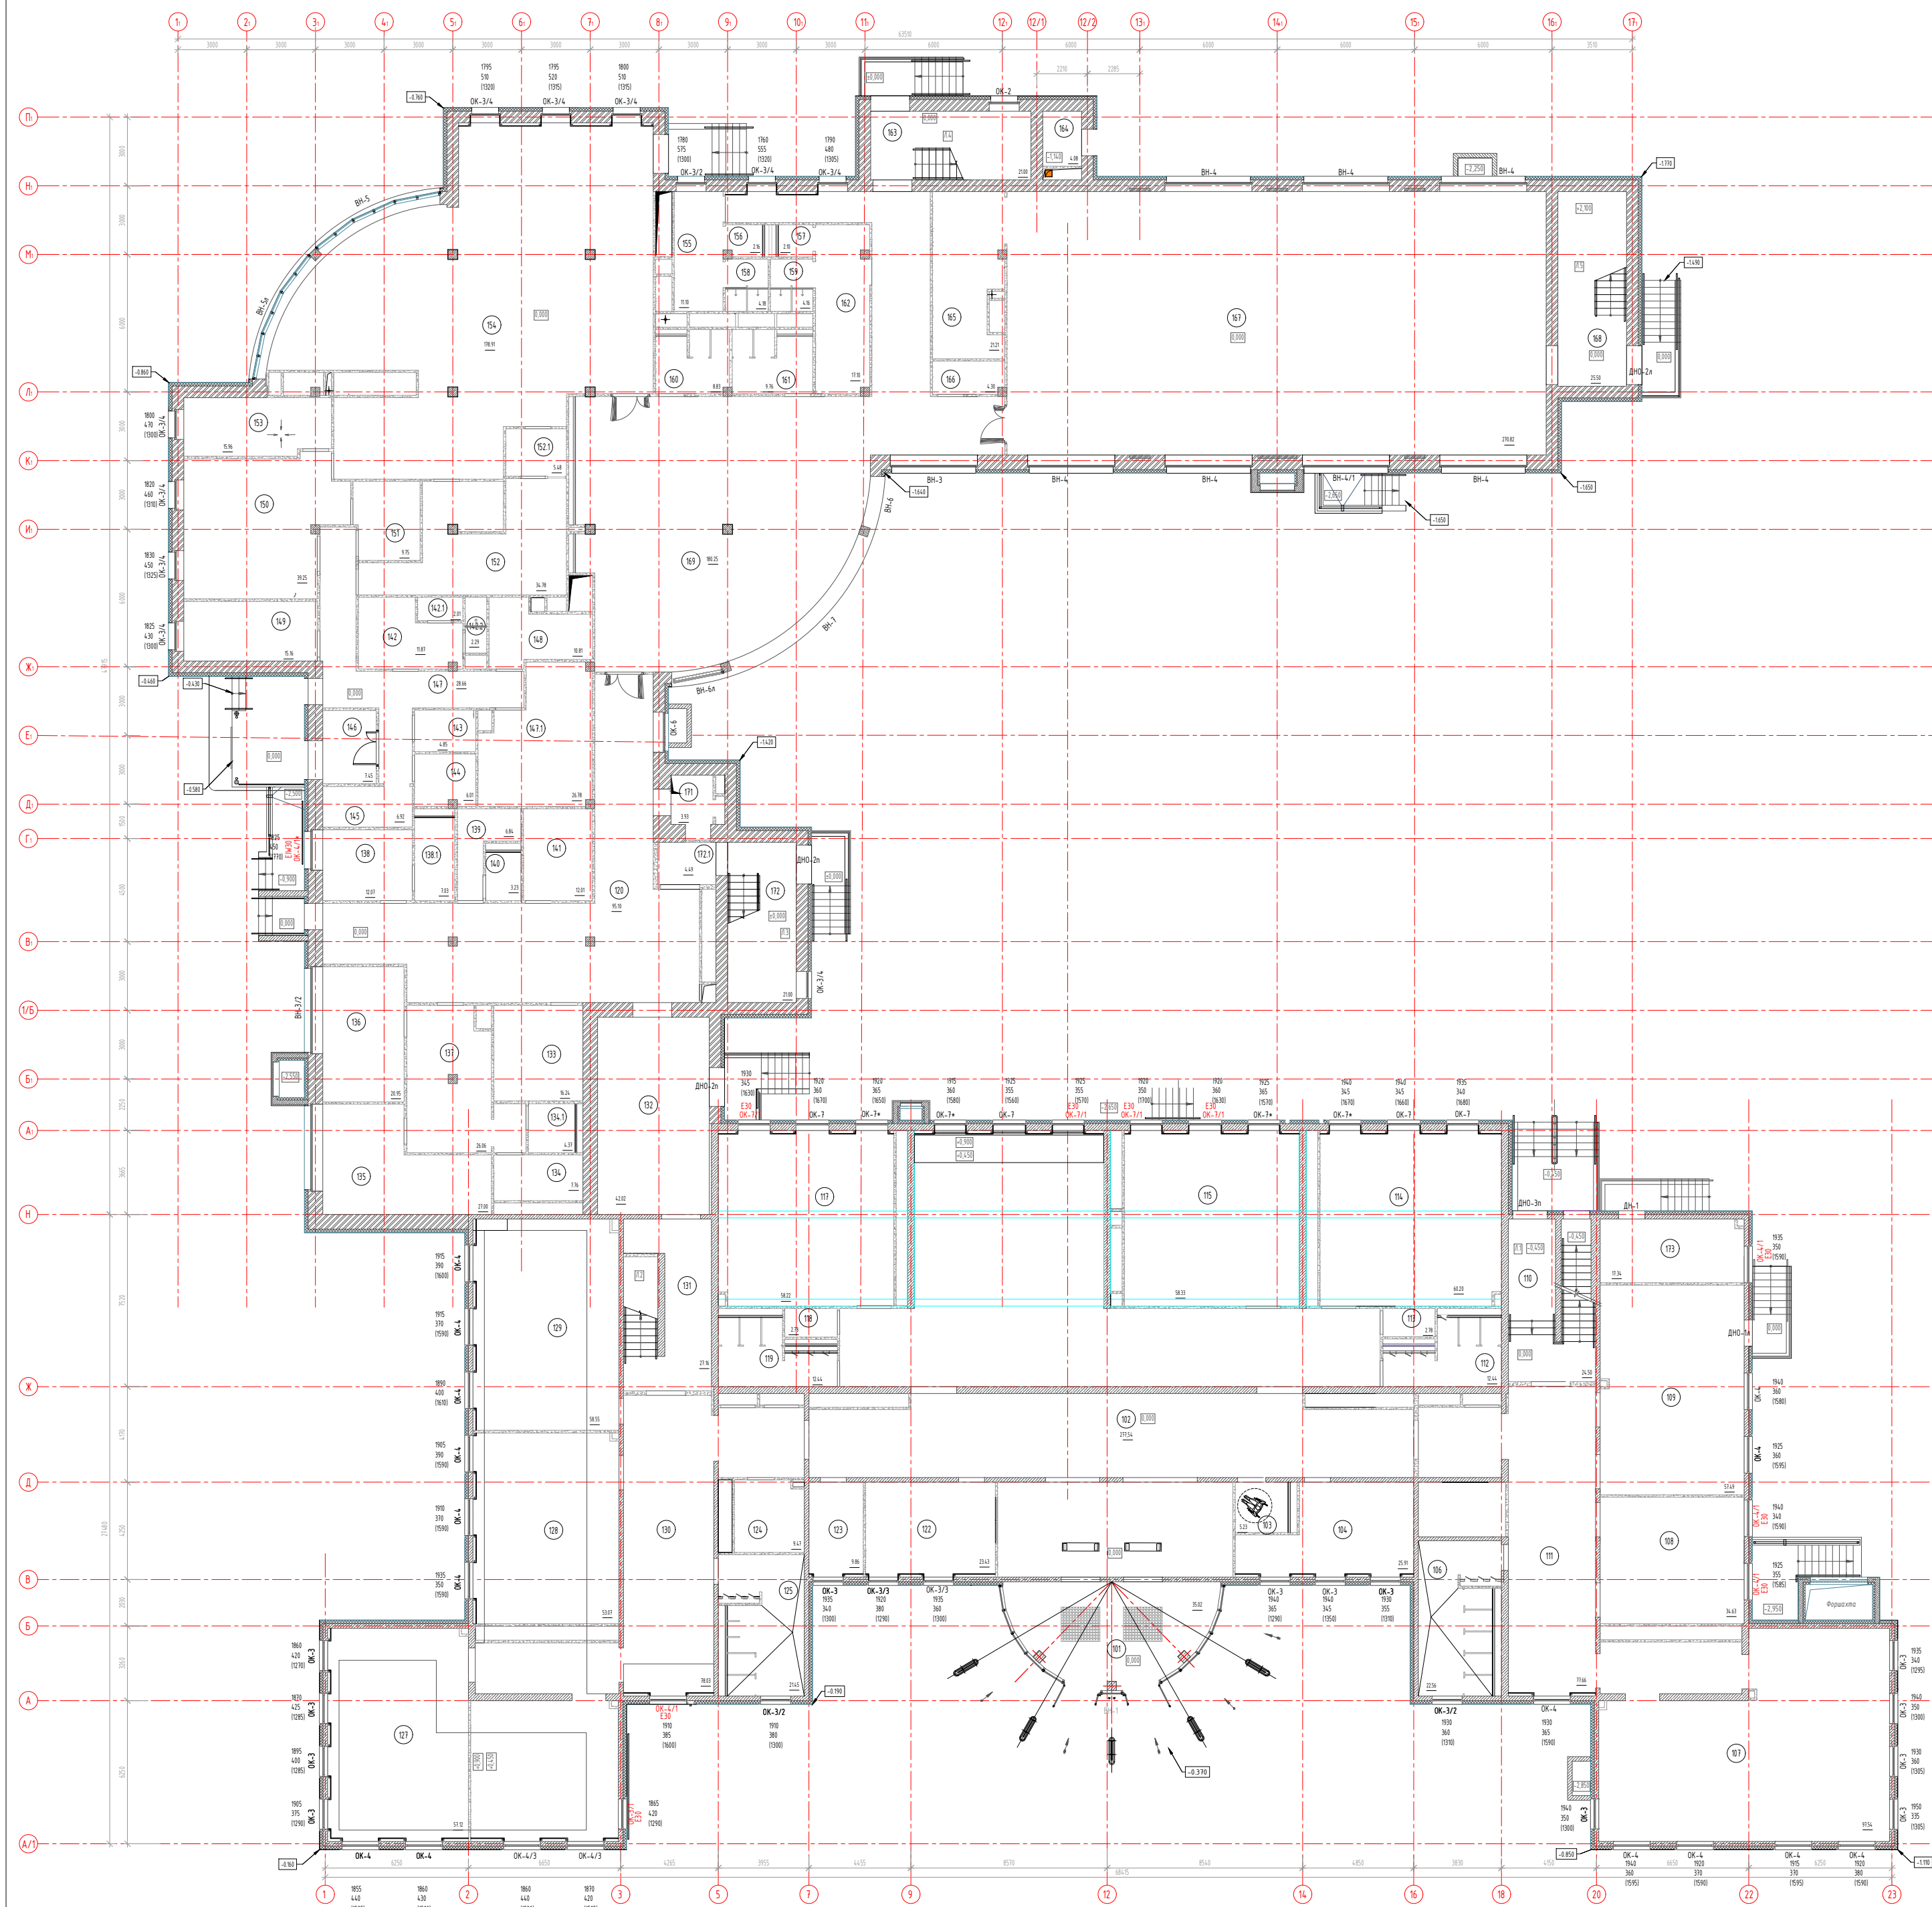


						ШК429		
						5-ая ул. Соколиной Горы, д.14		
Изм.	Кол.уч.	Лист	№ док.	Подпись	Дата			
ГИП Проверил Ткаченко Евгений						План 1-го этажа	Стадия	Лист/Листов
							РД	2/16
Разраб.	Харитоновна Ирина				18.08.2026		ООО "ШварцГрупп"	
Н.контр.								

План 2-го этажа

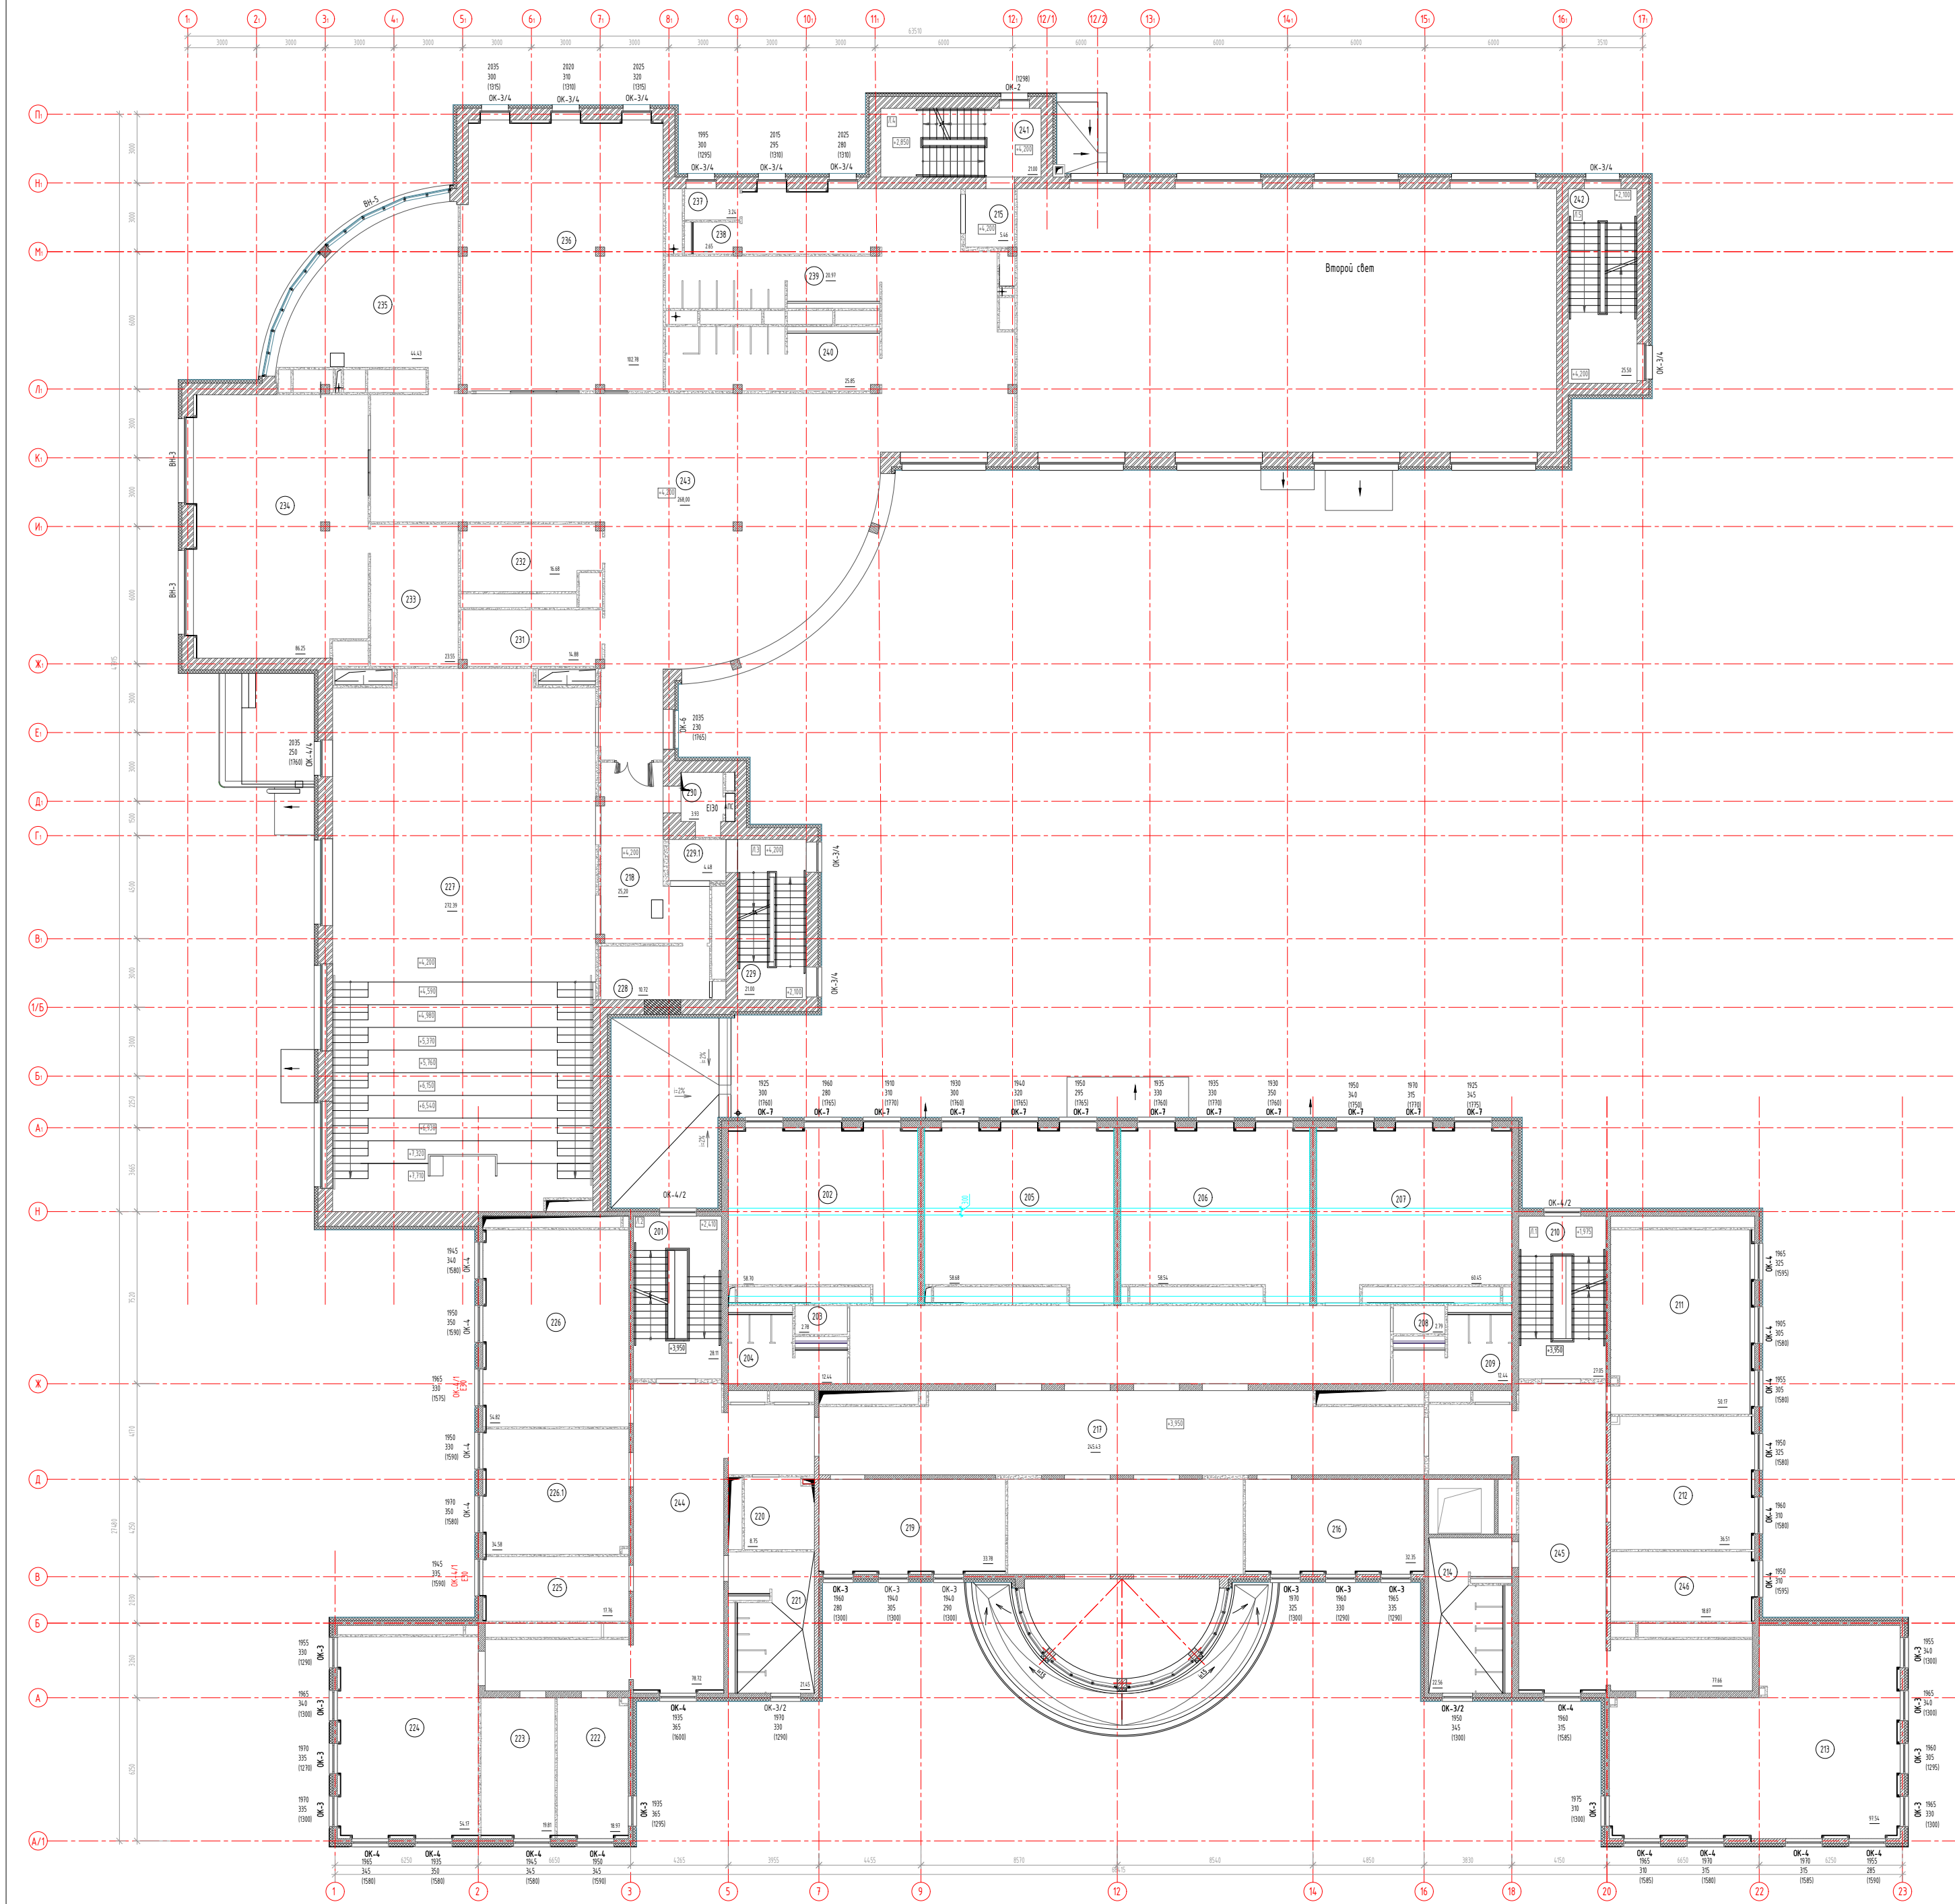


ШК429					
5-ая ул. Соколиной Горы, д.14					
Изм.	Кол.ч	Лист	№ док.	Подпись	Дата
Гип			План 2-го этажа		Стадия
Проверил			Ткаченко Евгений		РД
Разраб.			Харитонова Ирина		18.08.2026
Н.контр.					000 "ШварцГрупп"

План 3-го этажа

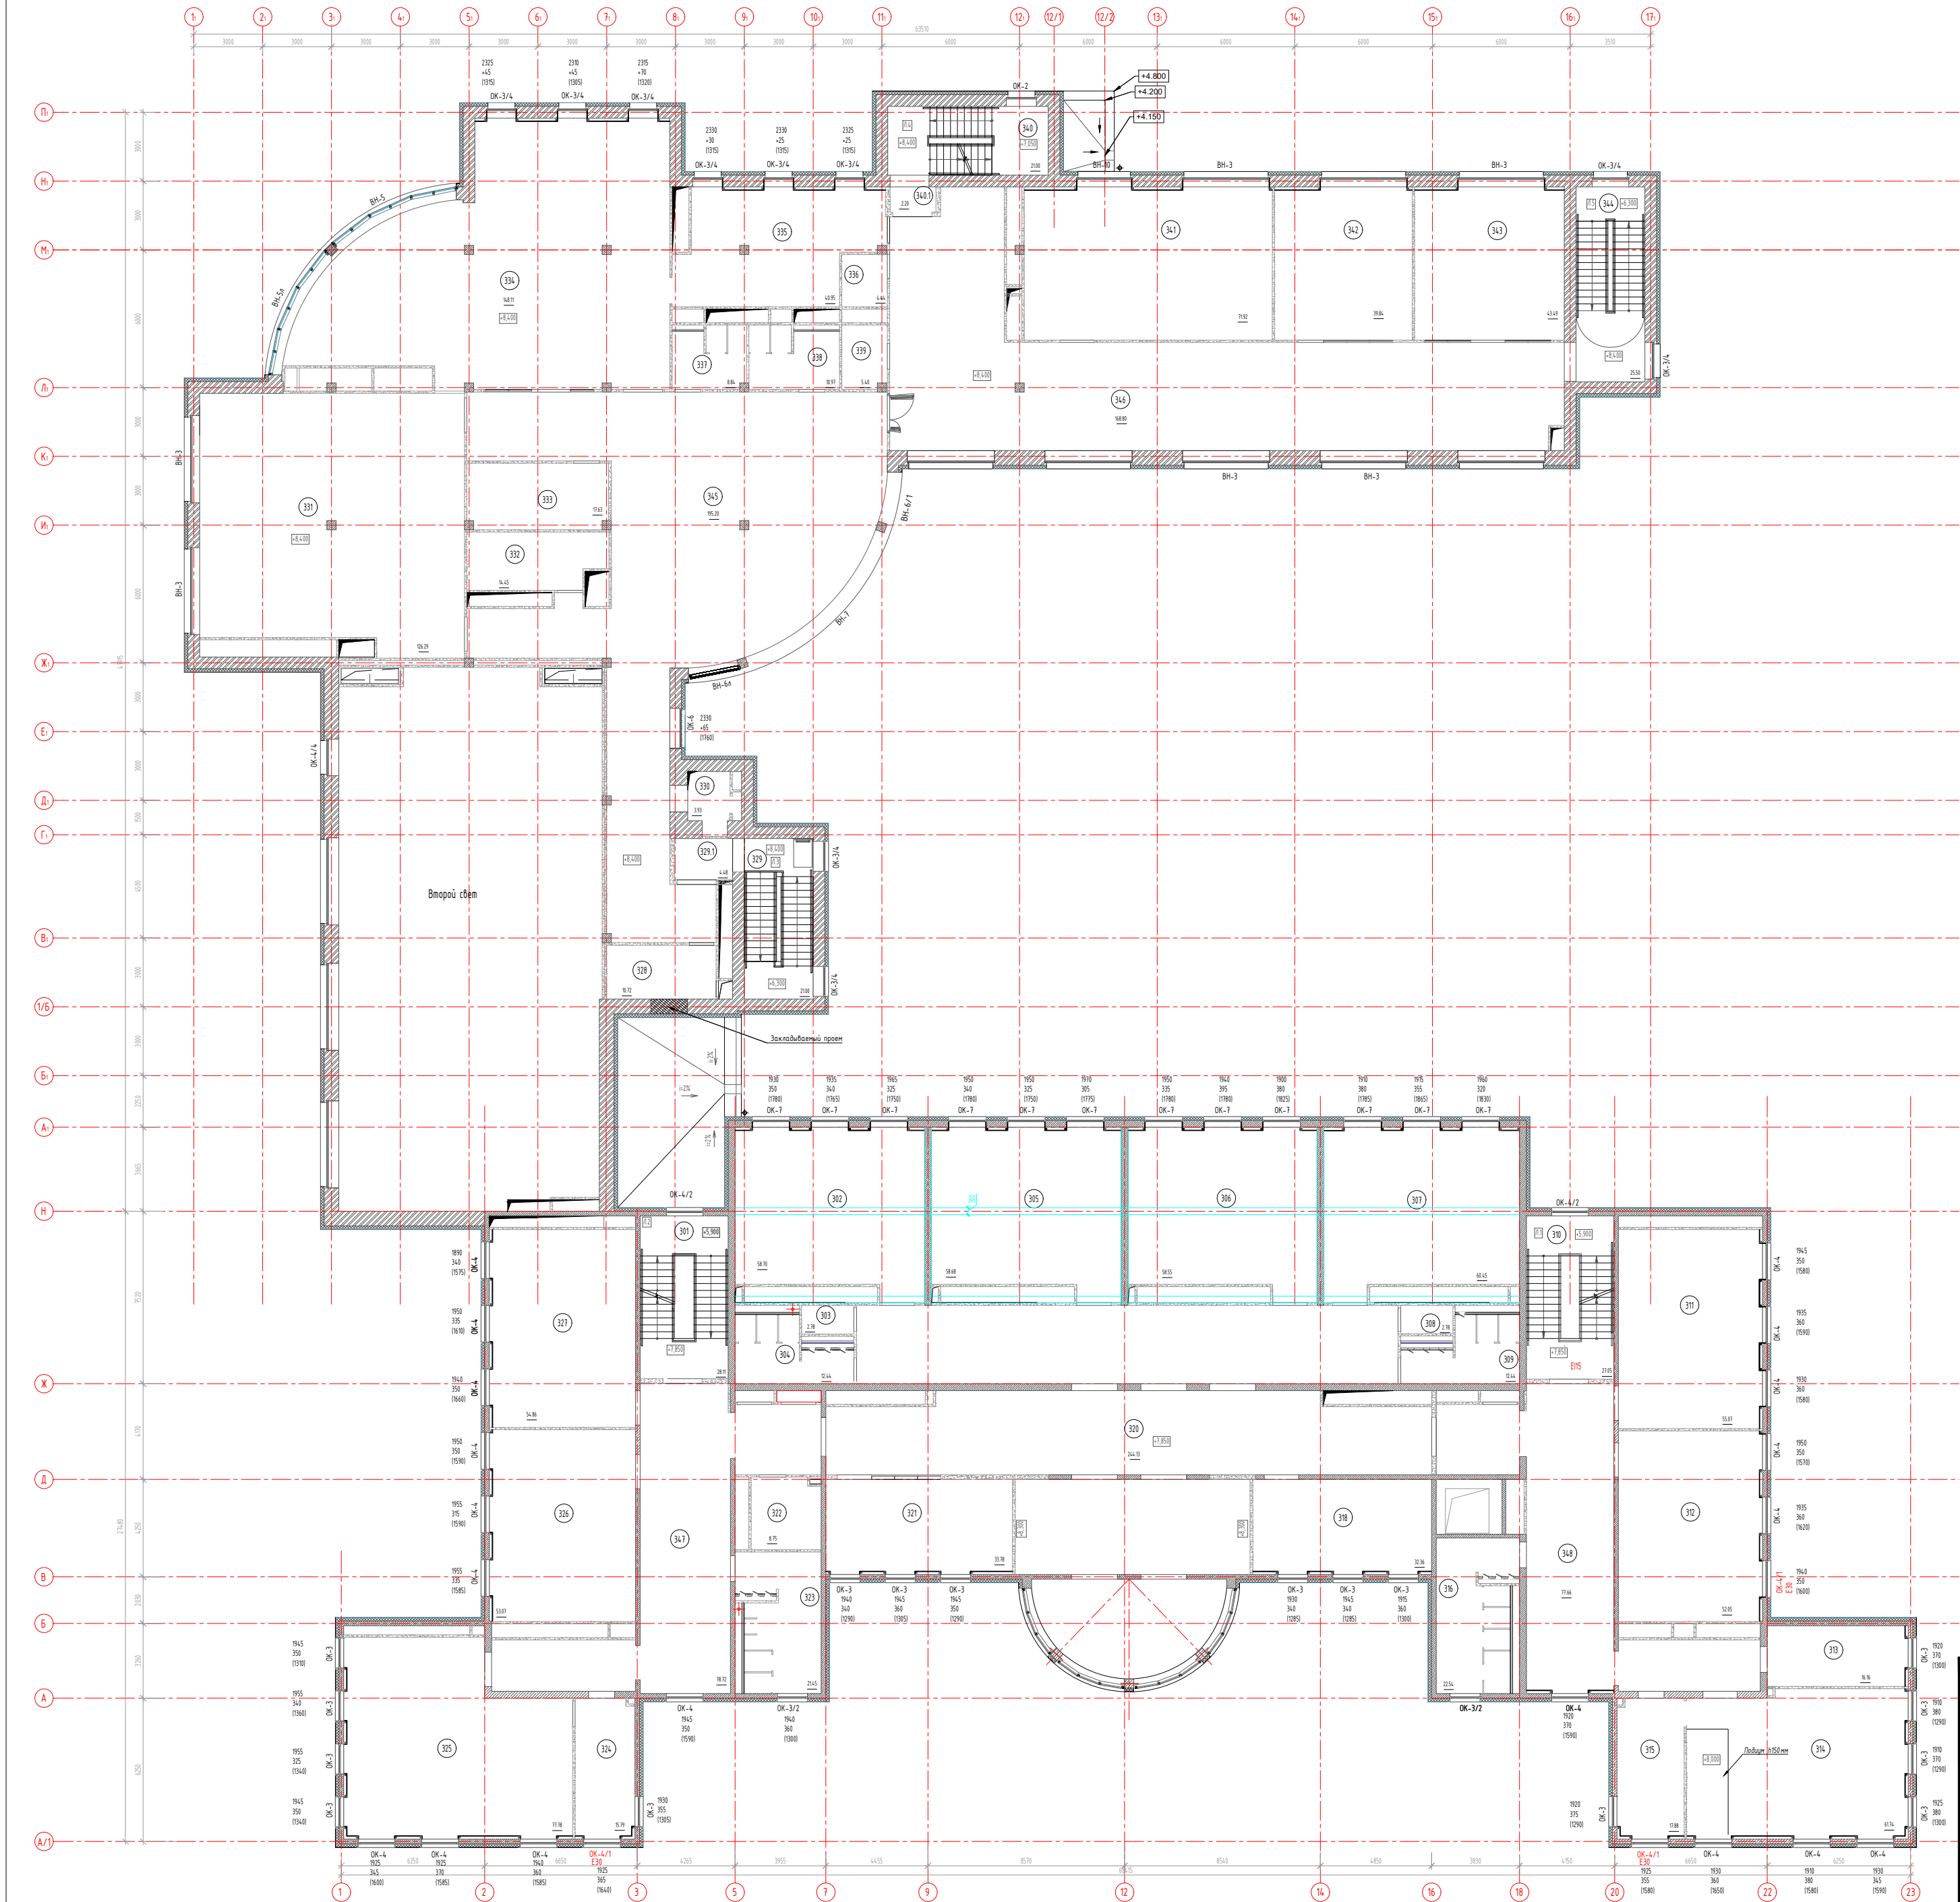


						ШК429		
						5-ая ул. Соколиной Горы, д.14		
Изм.	Кол.ч	Лист	№ док.	Подпись	Дата			
ГИП						План 3-го этажа		Стация
Проверил		Ткаченко Евгений						Лист/Листов
								РД
								4/16
Разраб.		Харитонова Ирина						ООО "ШварцГрупп"
Н.контр.						18.08.2026		

План 4-го этажа



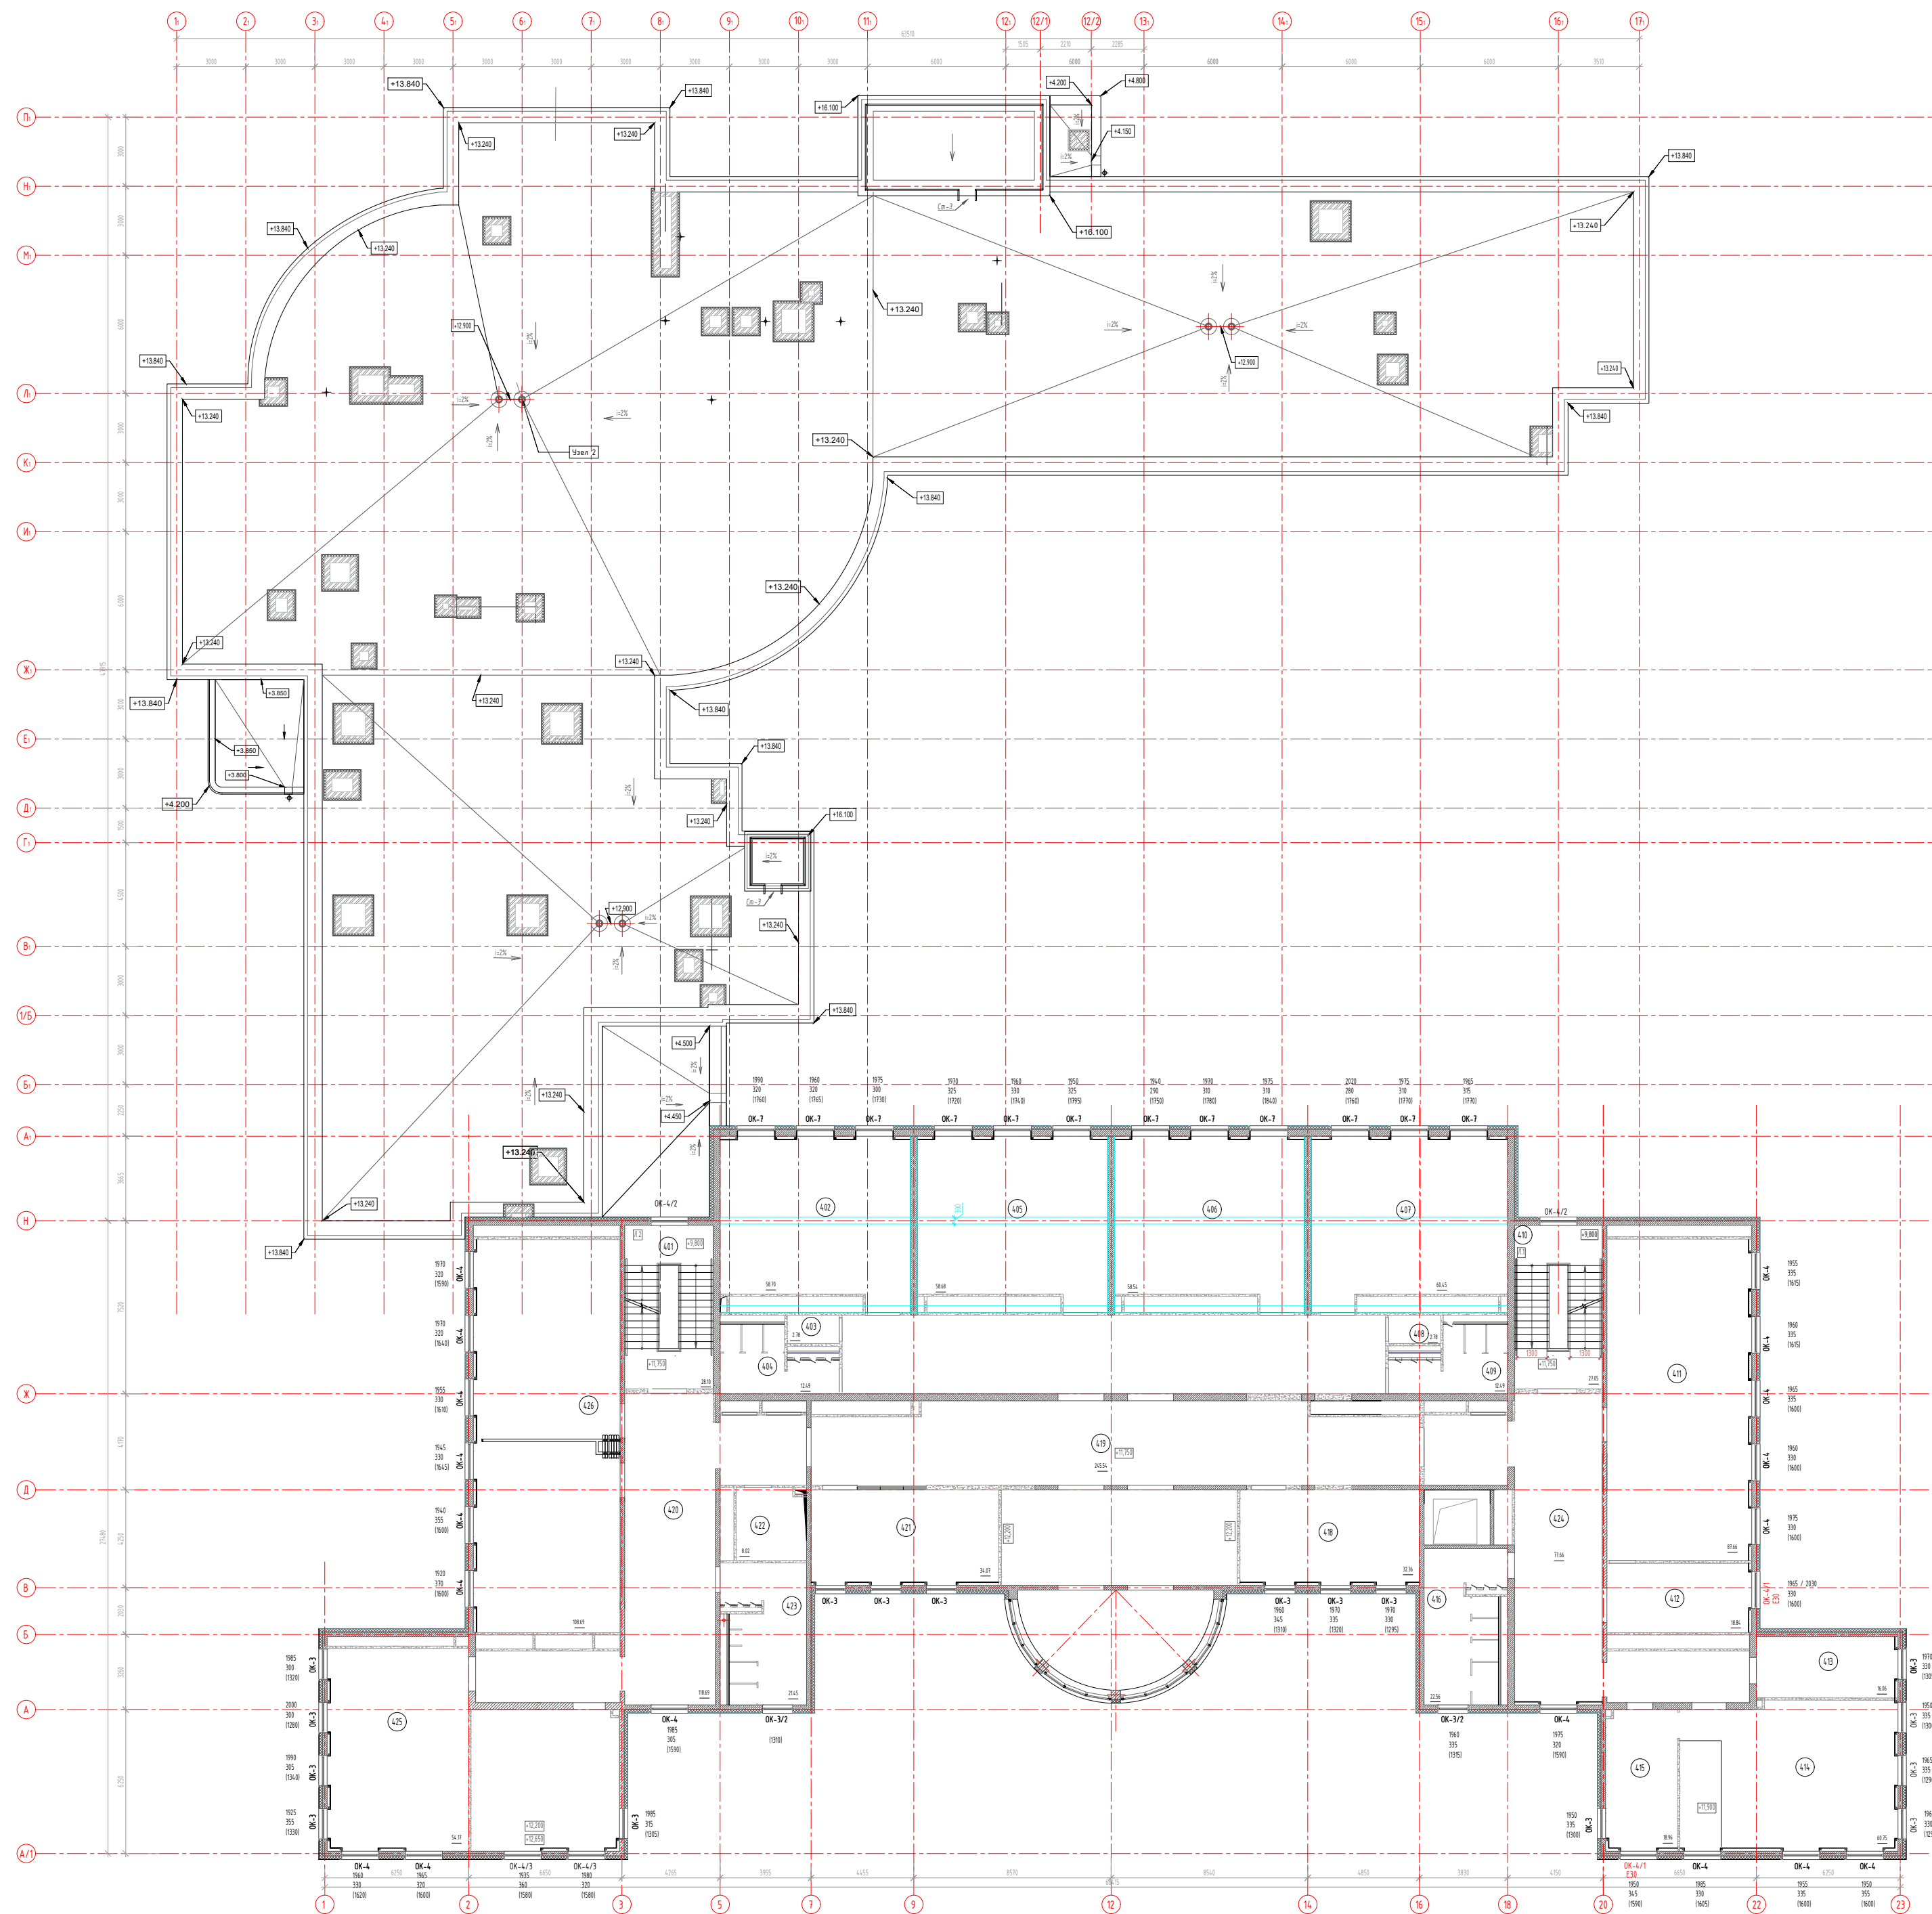


						ШК429		
						5-ая ул. Соколиной Горы, д.14		
Изм.	Кол.уч	Лист	№ док.	Подпись	Дата			
ГИП						План 4-го этажа	Стадия	Лист/Листов
Проверил		Ткаченко Евгений					РД	5/16
Разраб.		Харитонова Ирина			18.08.2026		ООО "ШварцГрупп"	
Н.контр.								


План тех. подполья

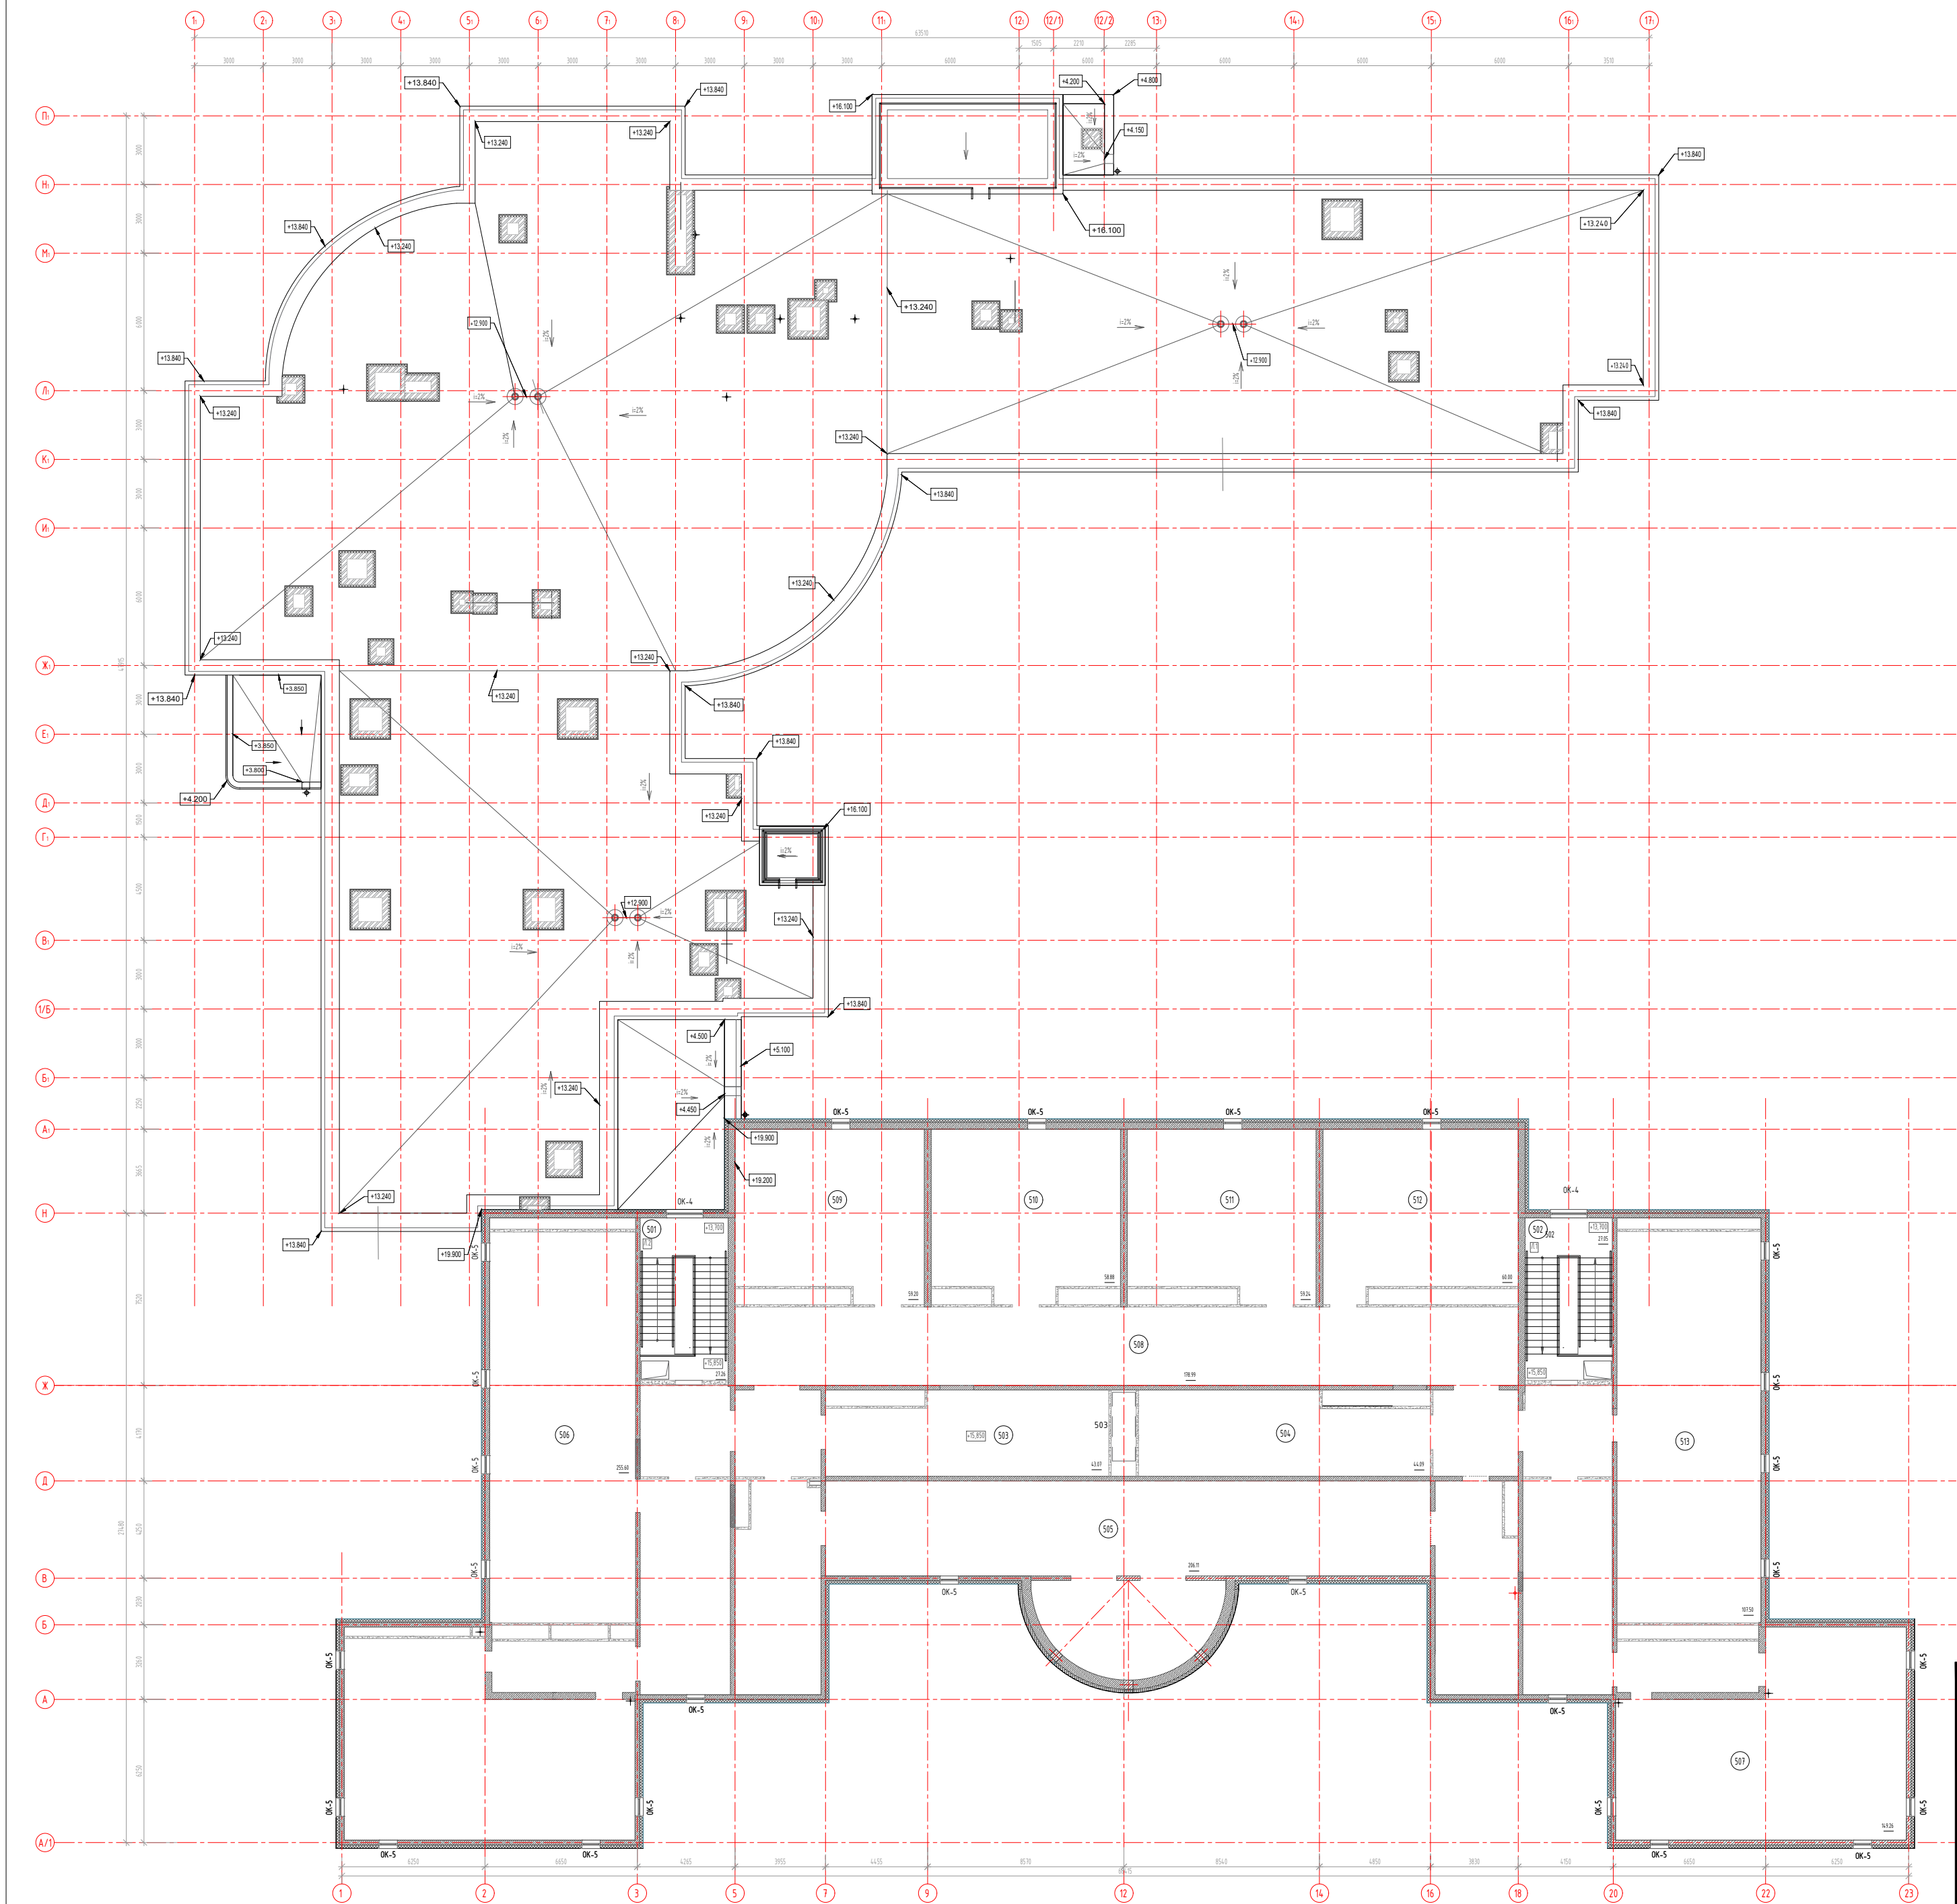


						ШК429
						5-ая ул. Соколиной Горы, д.14
Изм.	Кол.ч	Лист	№ док.	Подпись	Дата	План технического подполья
Гип						РД
Проверил	Ткаченко Евгений					6/16
Разраб.	Харитонова Ирина				18.08.2026	ООО "ШварцГрупп"
Н.контр.						

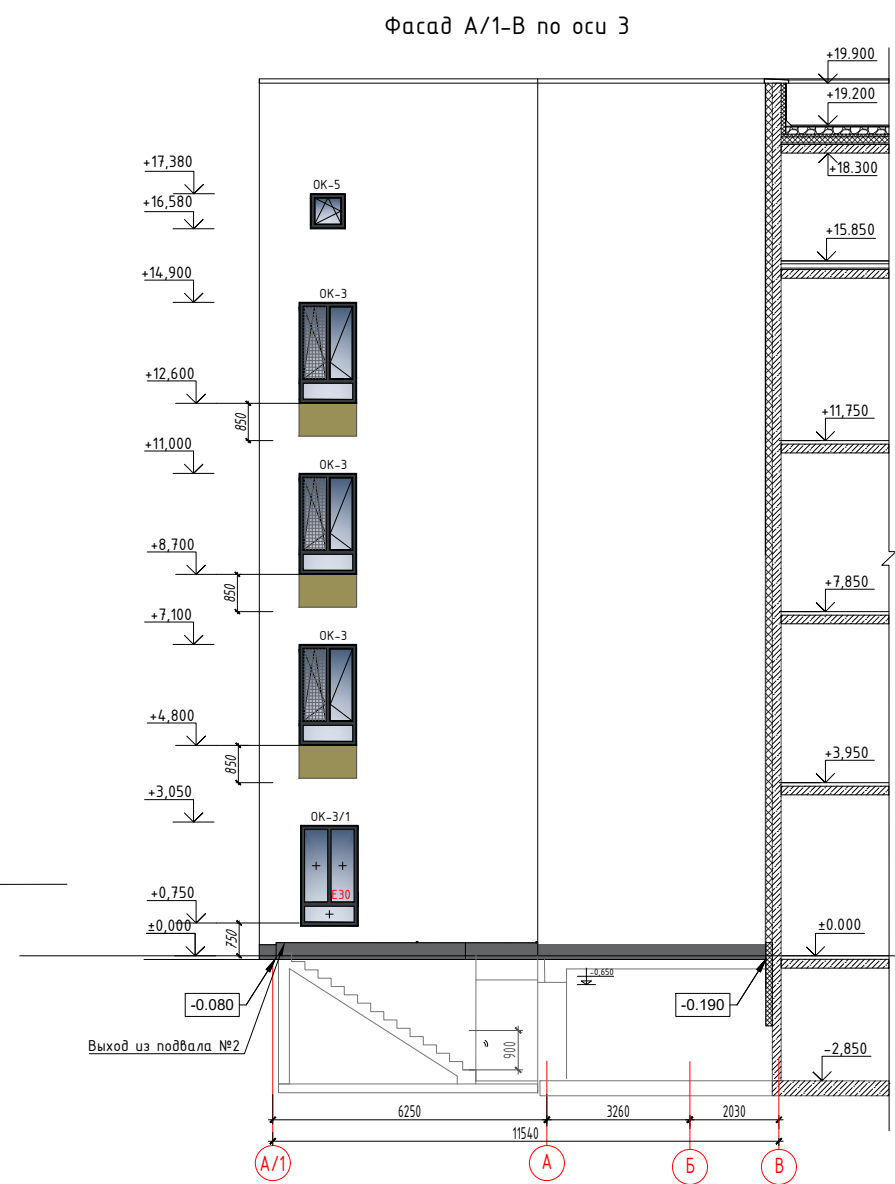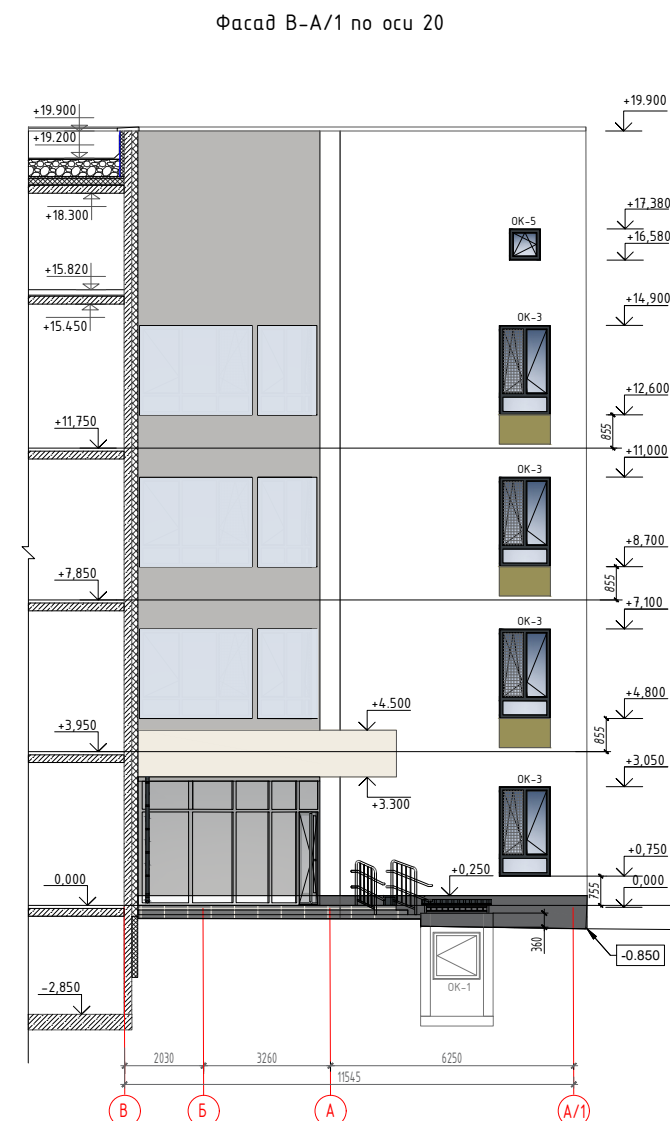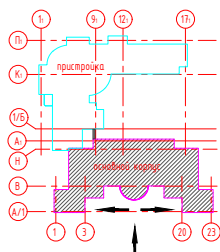

						ШК429
						5-ая ул. Соколиной Горы, д.14
Изм.	Кол.	лист	№ док.	Подпись	Дата	Фасад 1-23 по оси А/1, Фасад В-А/1 по оси 20, Фасад 17"1-1"1 по оси П1
ГИП	Проверил	Ткаченко Евгений				Стадия РД
Разраб.	Н.контр.	Харитонова Ирина			18.08.2026	Лист/Листов 7/16
						ООО "ШварцГрупп"

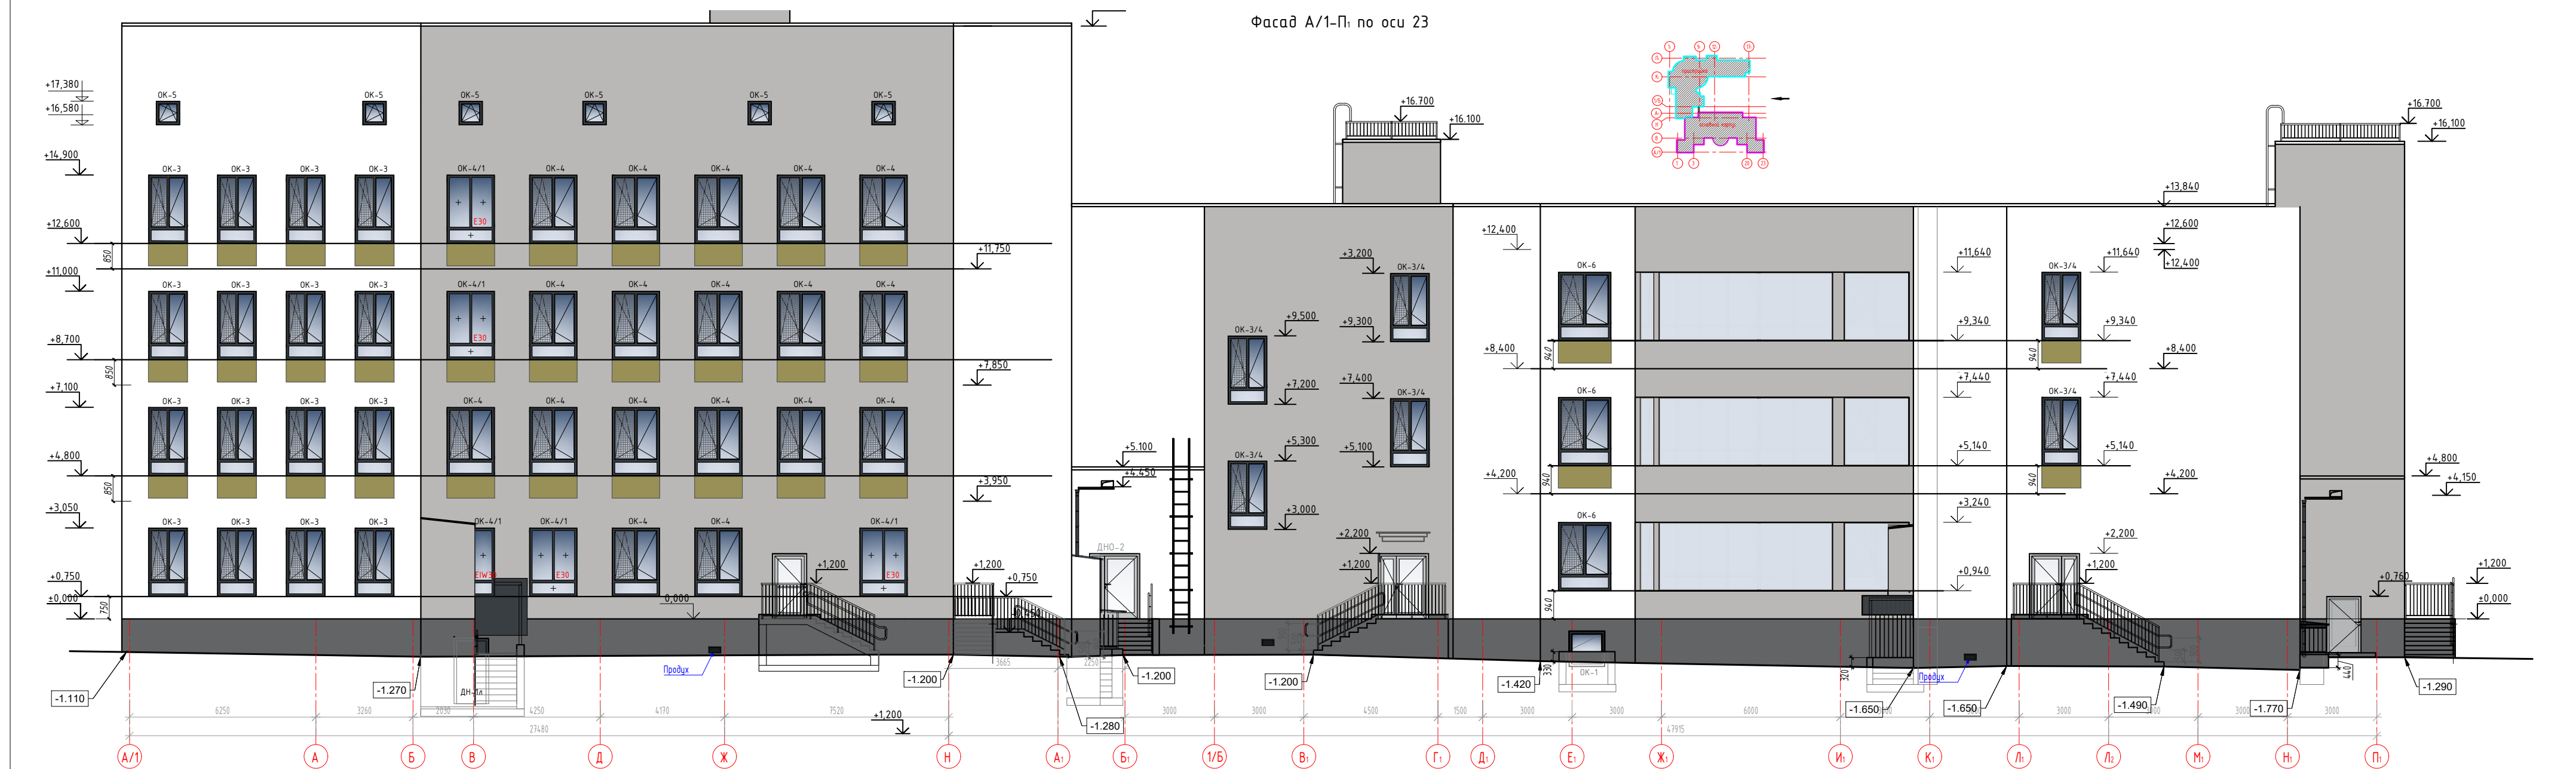

						ШК429	
						5-ая ул. Соколиной Горы, д.14	
Изм.	Колуч	Лист	№ док.	Подпись	Дата	Фасад П"1-А/1 по оси 1"1	Стадия
Гип	Проверил	Ткаченко Евгений				Фасад А/1-П"1 по оси 23	РД
Разраб.	Харитонова Ирина				18.08.2026		Лист/Листов
Н.контр.							8/16
						ООО "ШварцГрупп"	

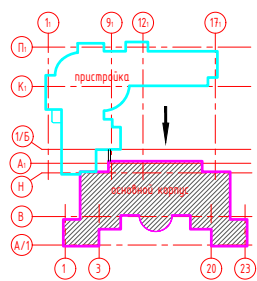


Фасад 23-3, по оси А1




						ШК429		
						5-ая ул. Соколиной Горы, д.14		
Изм.	Кол.уч.	Лист	№ док.	Подпись	Дата			
ГИП						Фасад 23-3"1 по оси А"1,	Стадия	Лист/Листов
Проверил	Ткаченко Евгений					Фасад А/1-В по оси 3	РД	9/16
Разраб.	Харитонова Ирина				18.08.2026			
Н.контр.						ООО "ШварцГрупп"		

1-й этаж
2-й этаж

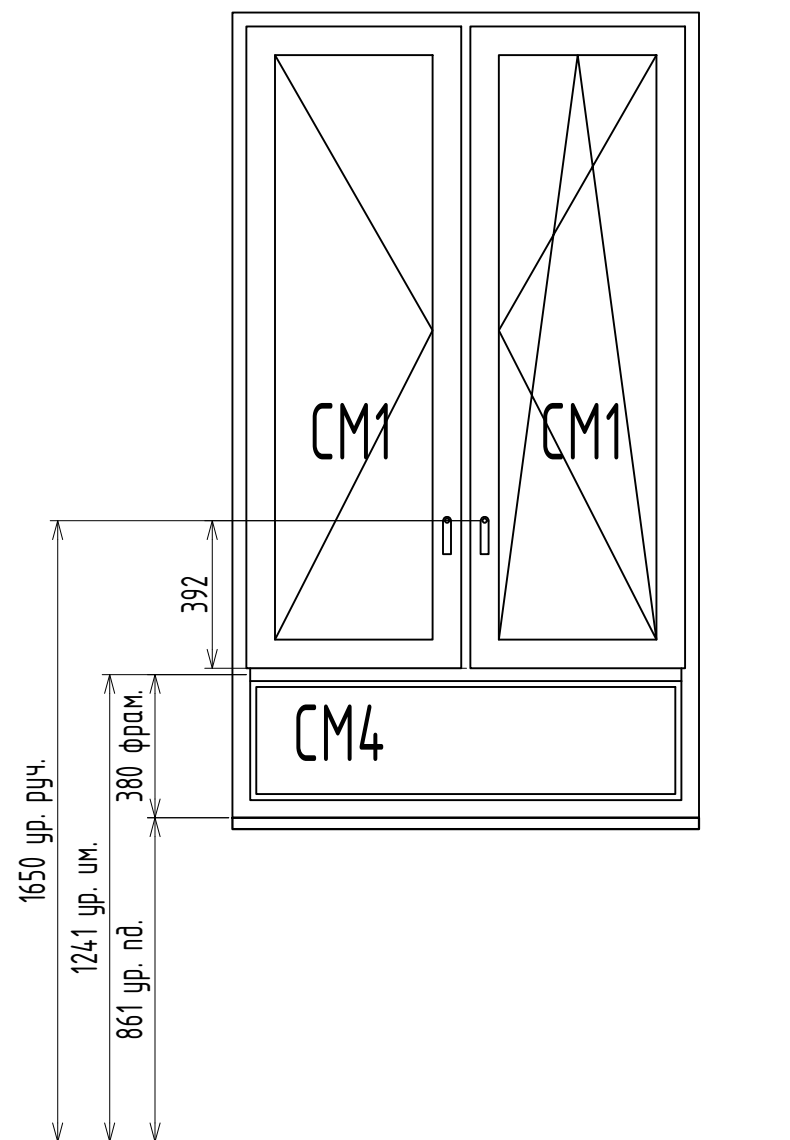


3-й этаж
4-й этаж

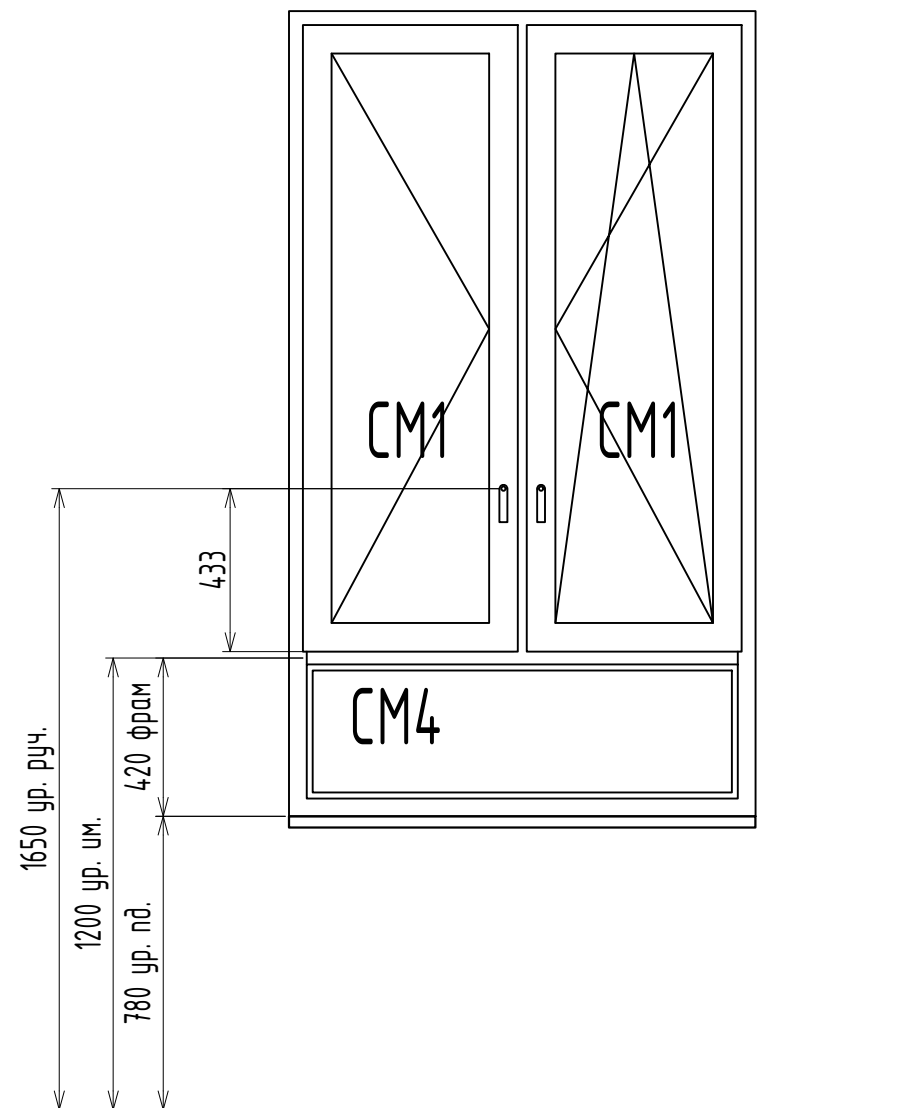


						ШК429		
						5-ая ул. Соколиной Горы, д.14		
Изм.	Кол.уч	Лист	N док.	Подпись	Дата	Схемы окон	Стадия	Лист/Листов
ГИП							РД	10/16
Проверил	Ткаченко Евгений						ООО "ШварцГрупп"	
Разраб.	Харитонова Ирина				18.08.2026			
Н.контр.								


Узел примыкания к вертикальному участку проема рамы огнестойкого оконного блока (вид сверху)

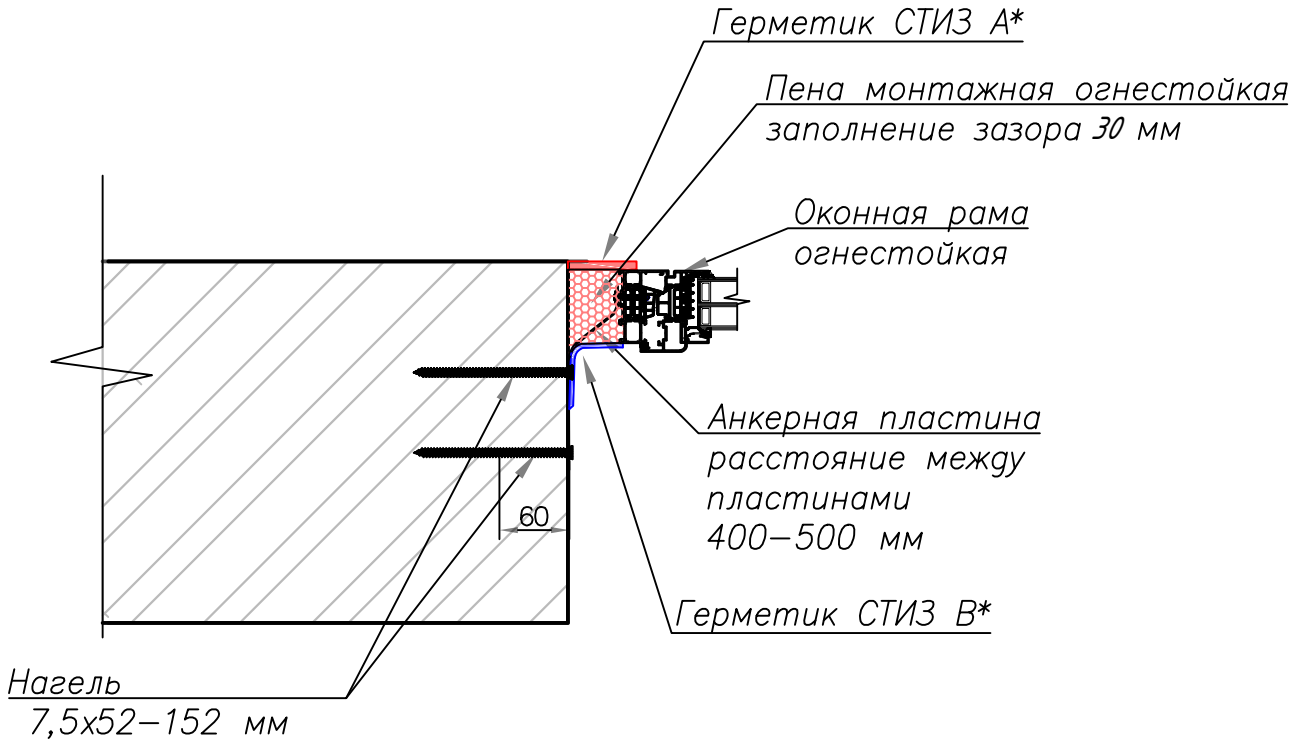

Узел примыкания к потолочному откоосу проема рамы огнестойкого оконного блока

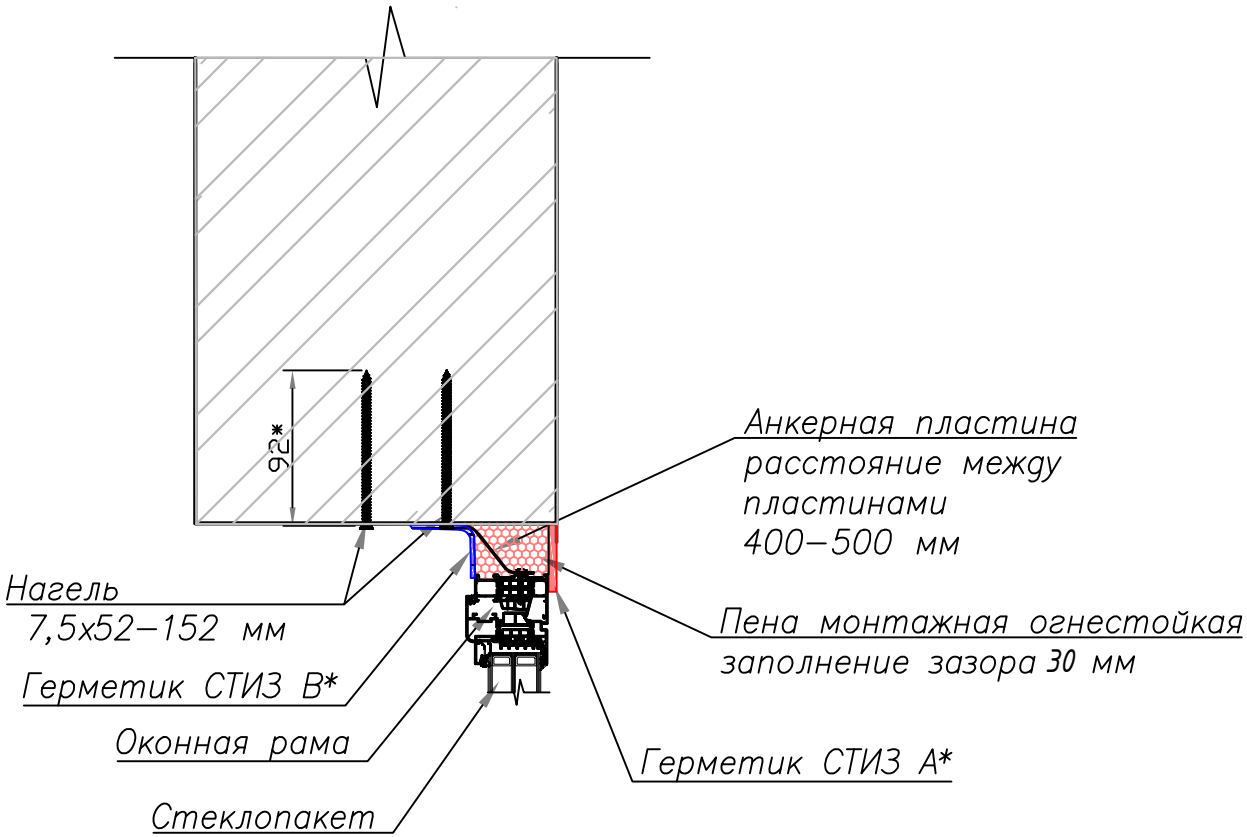

Узел примыкания к нижней части проема рамы огнестойкого оконного блока

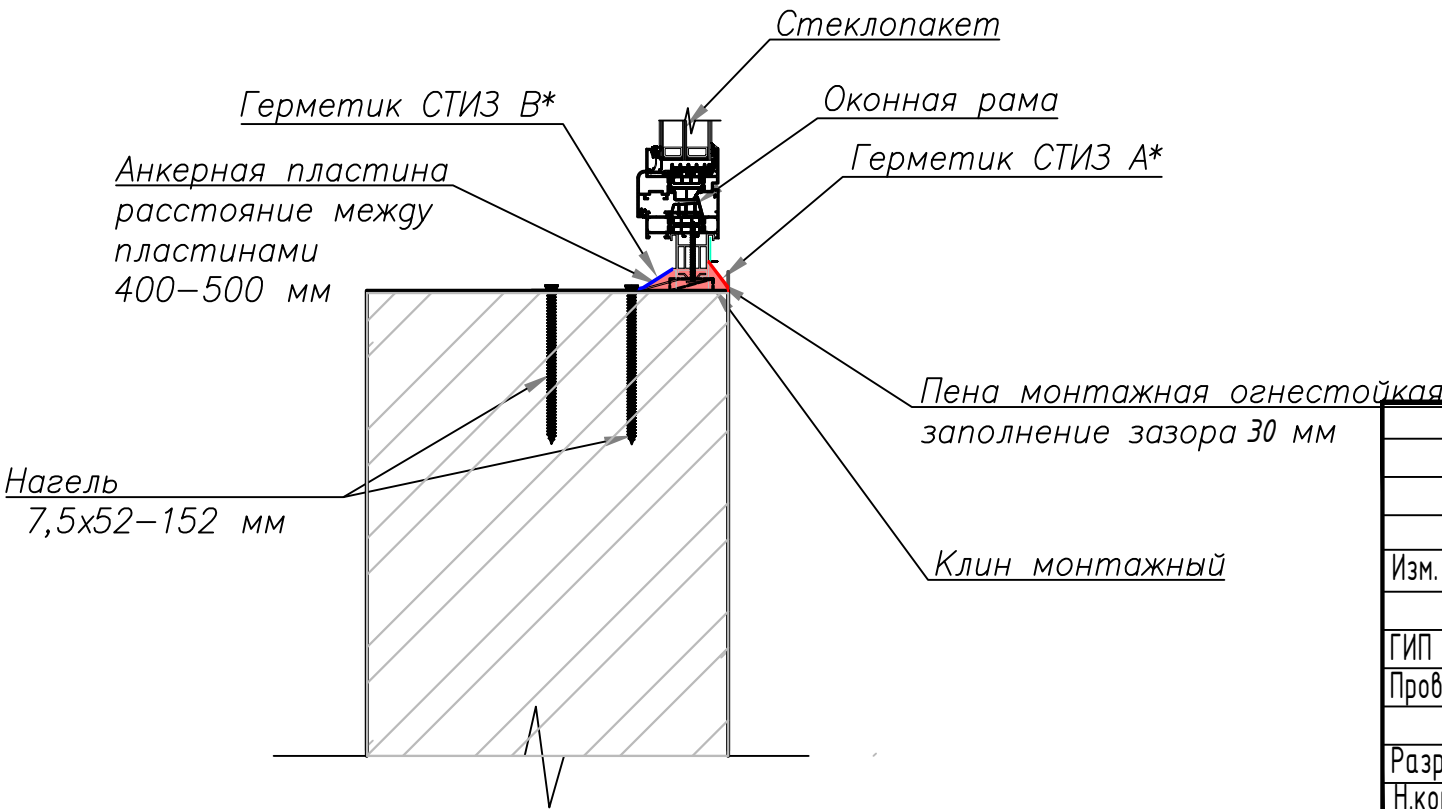

						ШК429		
						5-ая ул. Соколиной Горы, д.14		
Изм.	Кол.уч	Лист	N док.	Подпись	Дата	Монтажные узлы	Стадия	Лист/Листов
ГИП	Проверил	Ткаченко Евгений					РД	11/16
Разраб.	Н.контр.	Харитонова Ирина			18.08.2026	ООО "ШварцГрупп"		


Монтажные узлы вариант для основания кирпич

Дата


Подпись

М.П.


Крепление оконной рамы к вертикальным участкам проемов. Вариант 1 (вид сверху)

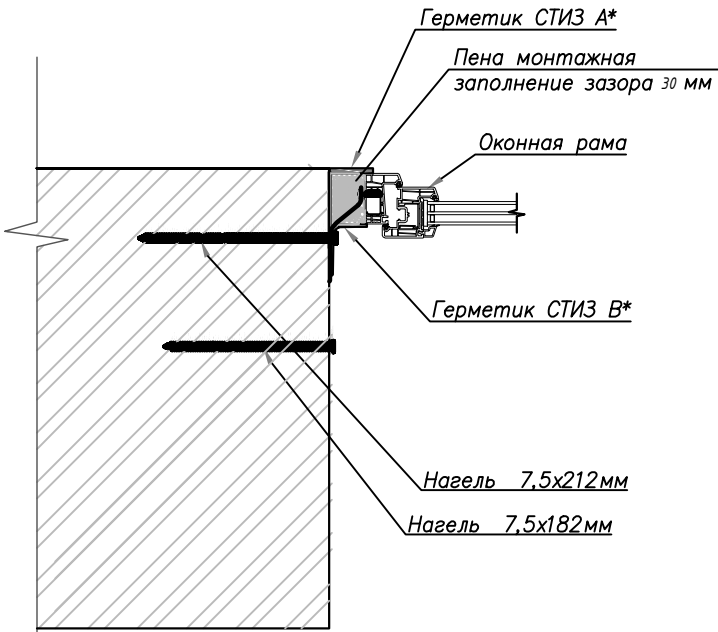


Крепление оконной рамы к вертикальным участкам проемов. Вариант 2 (вид сверху)

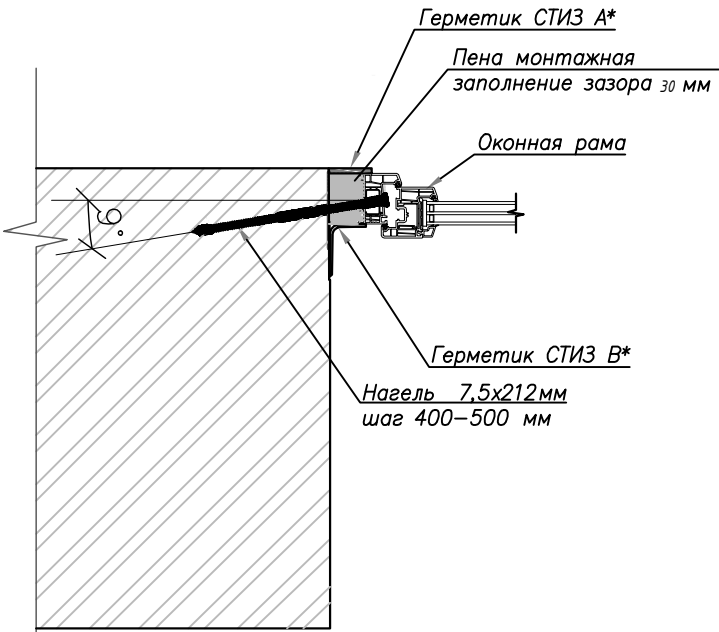


Крепление оконной рамы к перемычкам оконных проемов. Вариант 1 (вид сбоку)

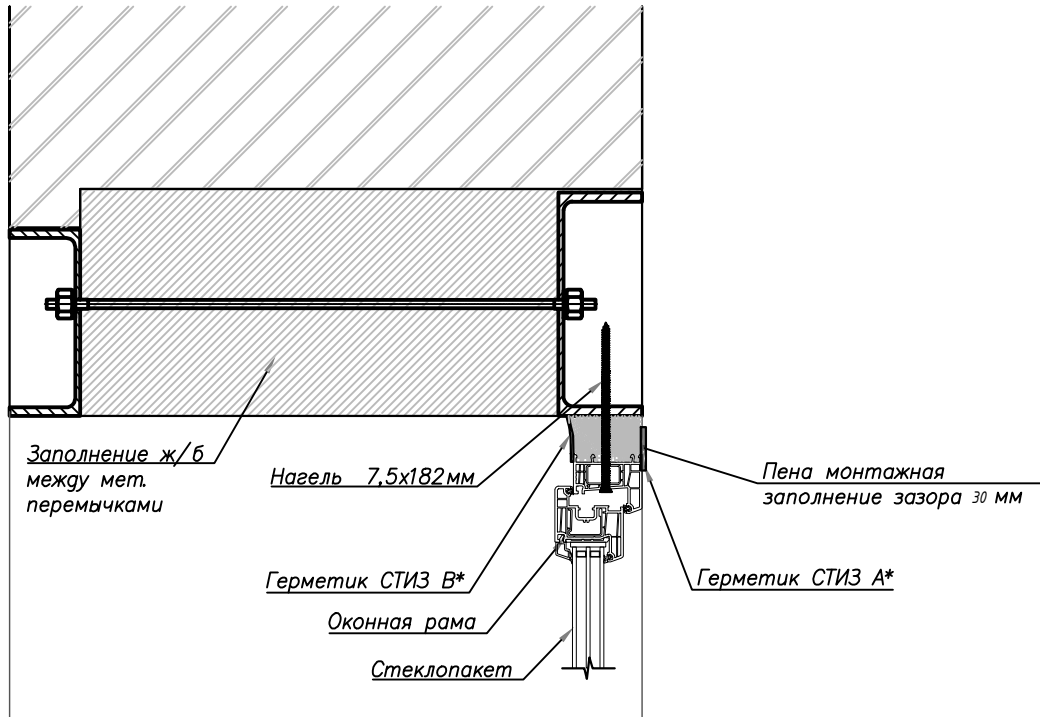


Крепление оконной рамы к перемычкам оконных проемов старой части школы. Вариант 2 (вид сбоку)

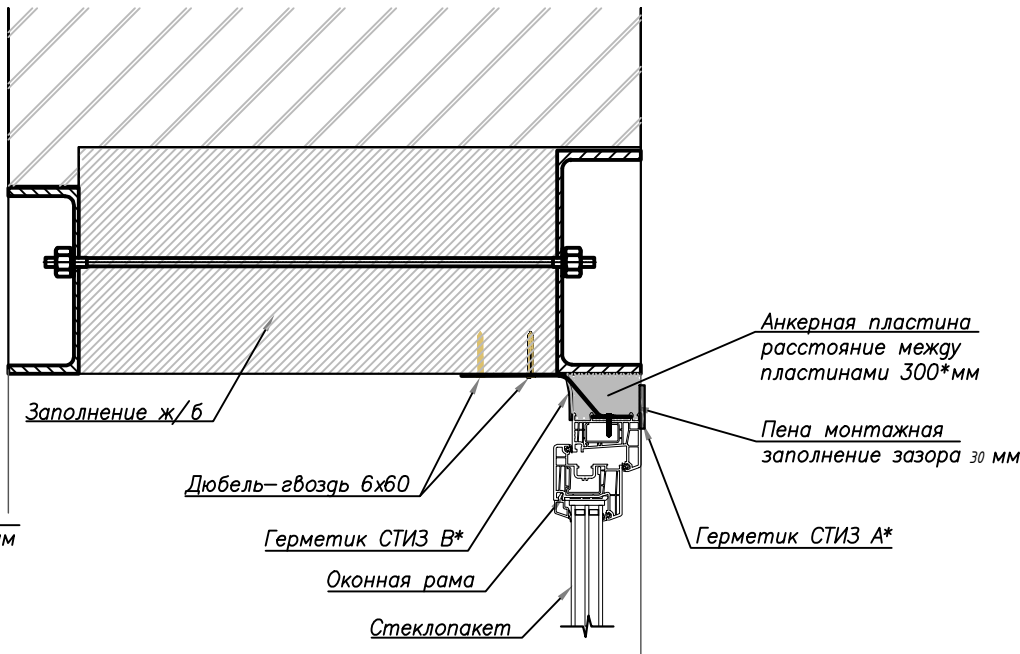

Крепление оконной рамы в нижней части проема

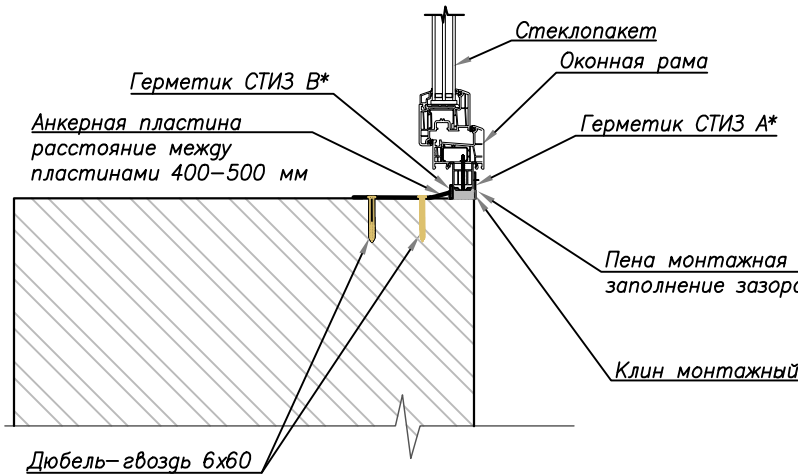

Крепление оконной рамы к перемычкам оконных проемов новой части школы.

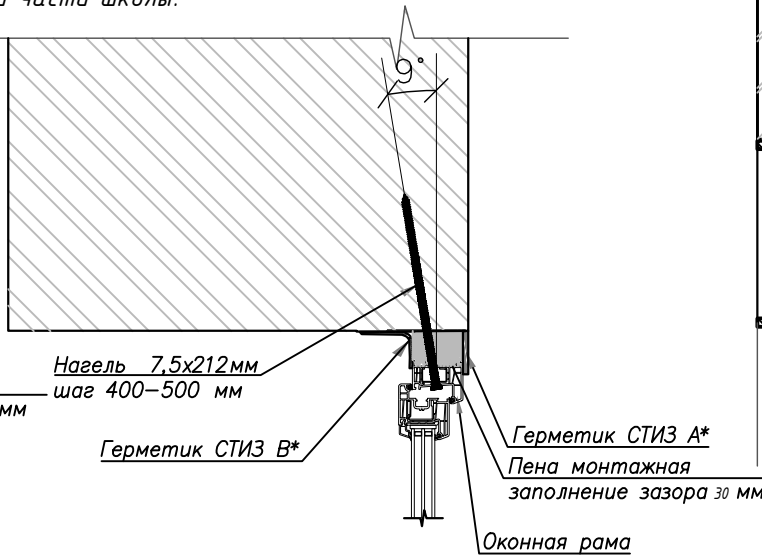


						ШК429		
						5-ая ул. Соколиной Горы, д.14		
Изм.	Кол.уч	Лист	N док.	Подпись	Дата	Монтажные узлы	Стадия	Лист/Листов
ГИП							РД	12/16
Проверил	Ткаченко Евгений						ООО "ШварцГрупп"	
Разраб.	Харитонова Ирина				18.08.2026			
Н.контр.								

Монтажные узлы вариант для основания бетон

Дата


Подпись

М.П.

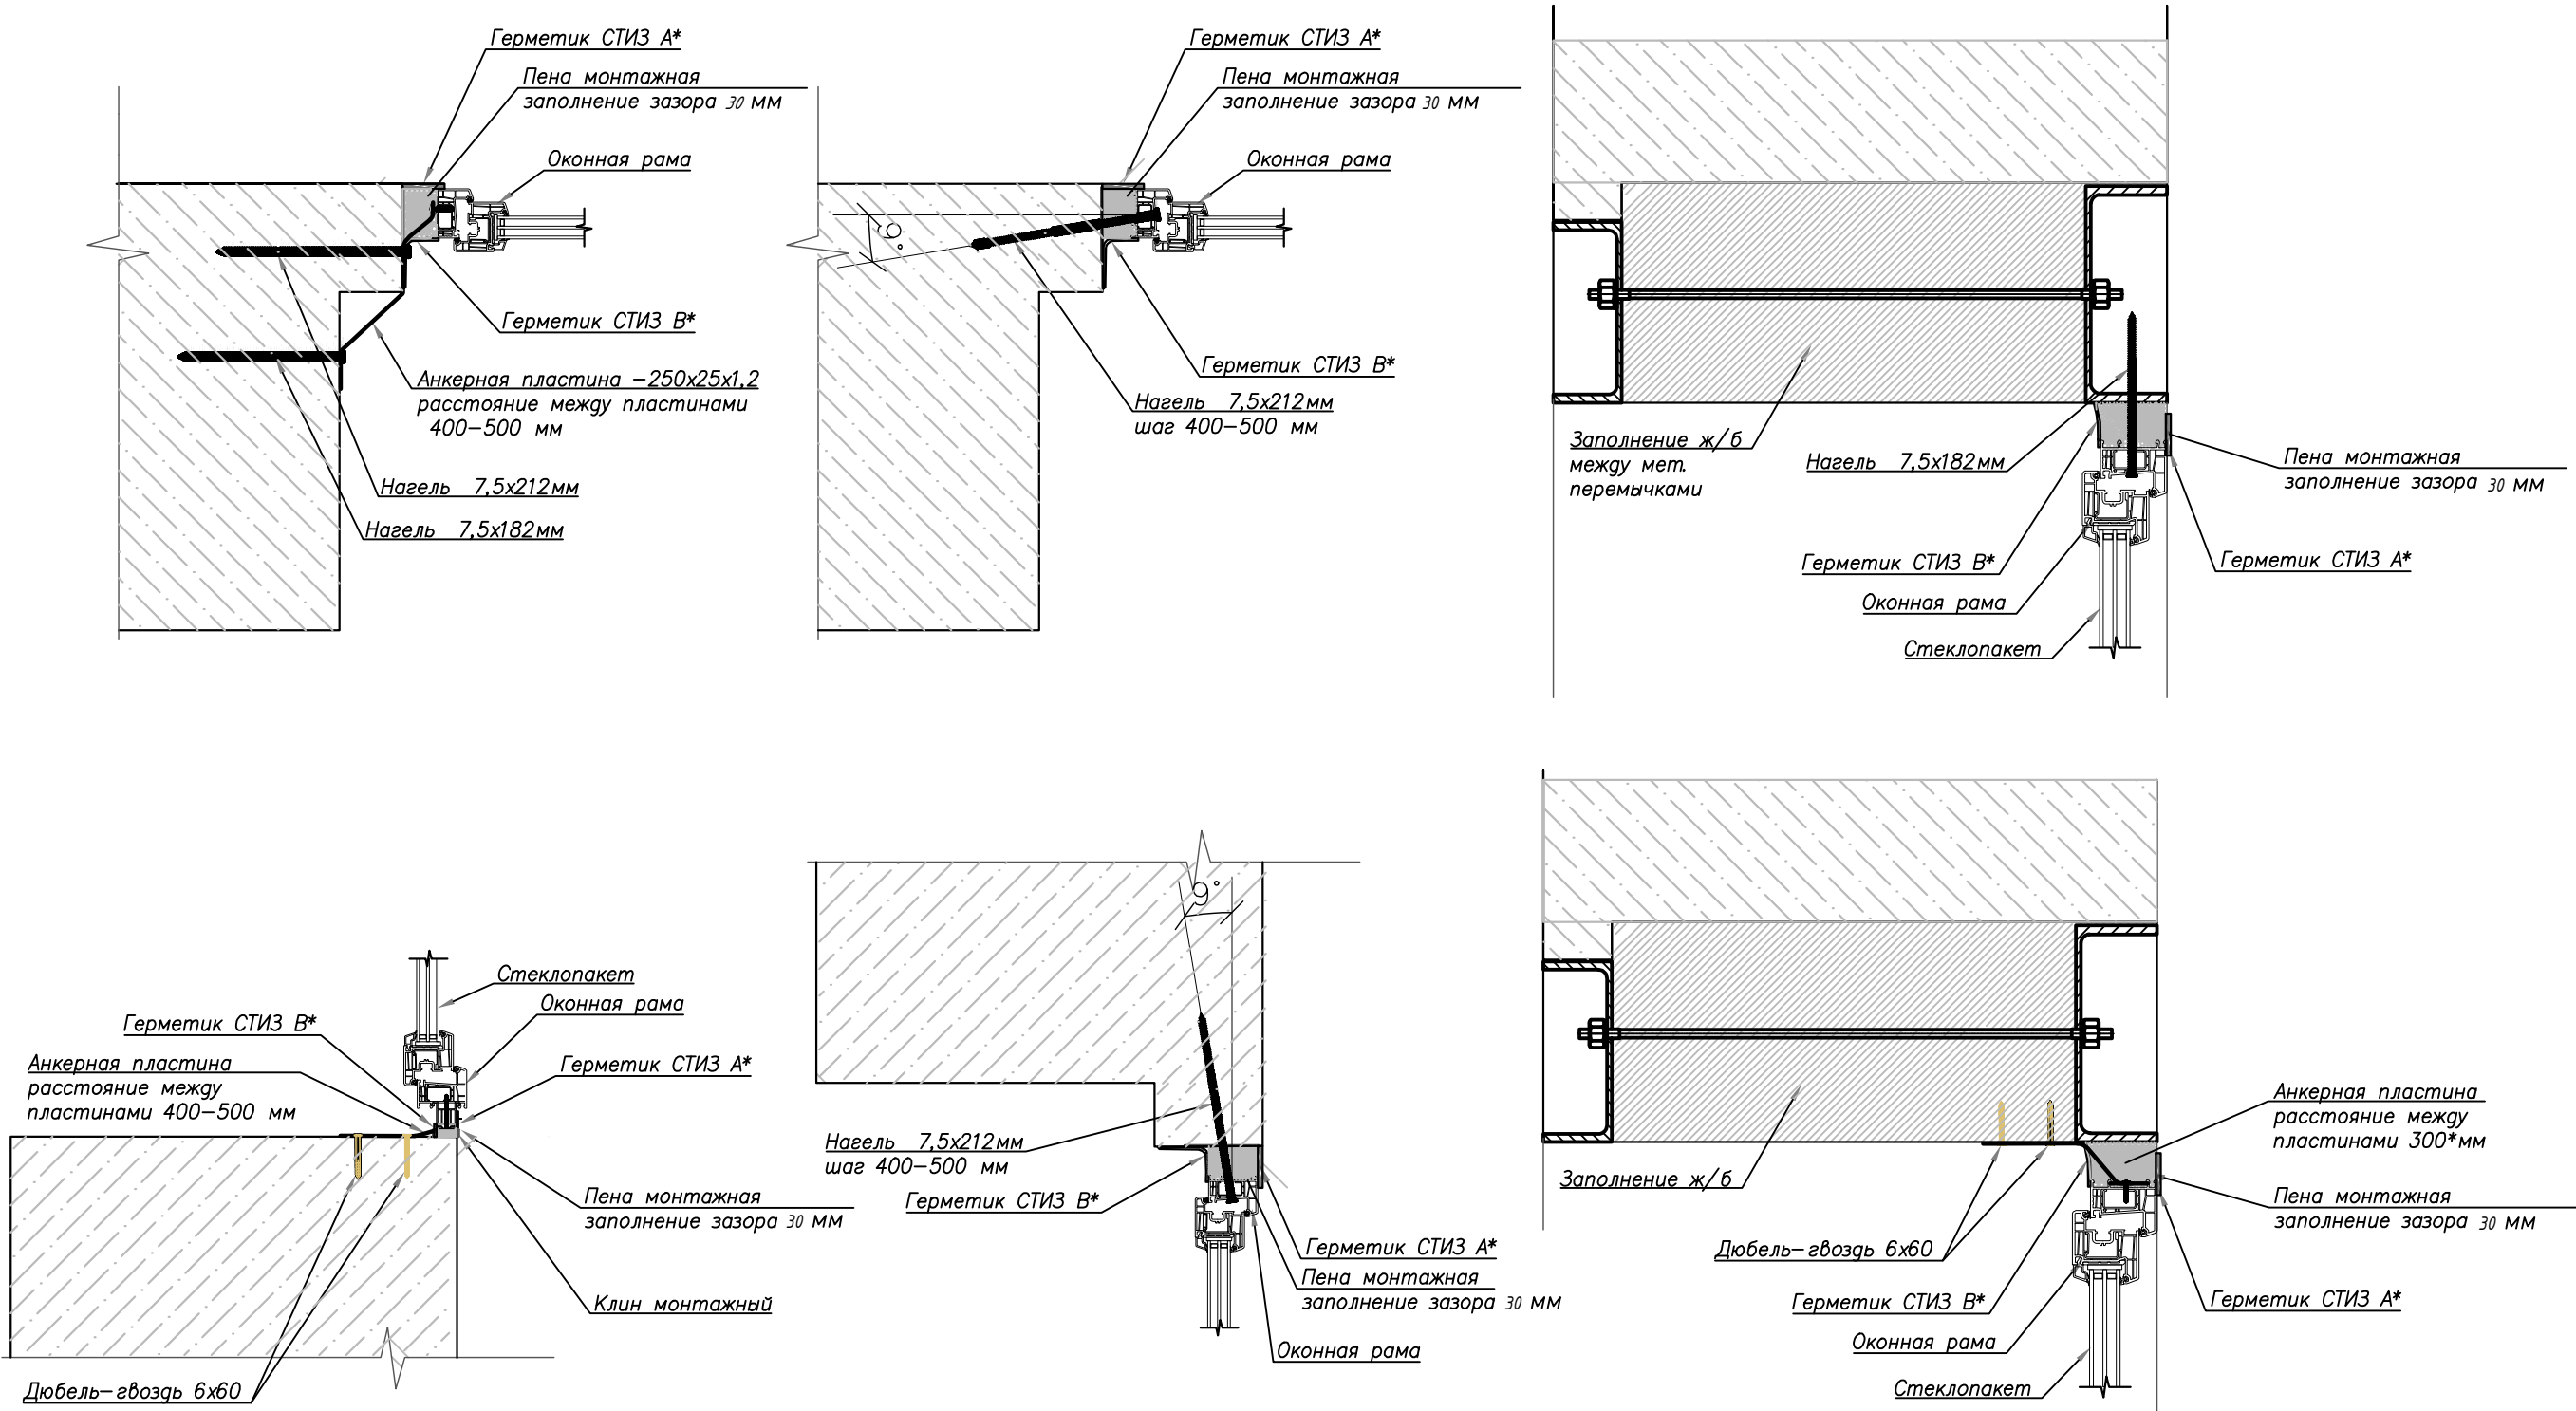


						ШК429		
						5-ая ул. Соколиной Горы, д.14		
Изм.	Кол.уч	Лист	N док.	Подпись	Дата	Монтажные узлы	Стадия	Лист/Листов
ГИП							РД	13/16
Проверил	Ткаченко Евгений						ООО "ШварцГрупп"	
Разраб.	Харитонова Ирина				18.08.2026			
Н.контр.								


Узел примыкания к вертикальному участку проема рамы огнестойкого оконного блока (вид сверху)

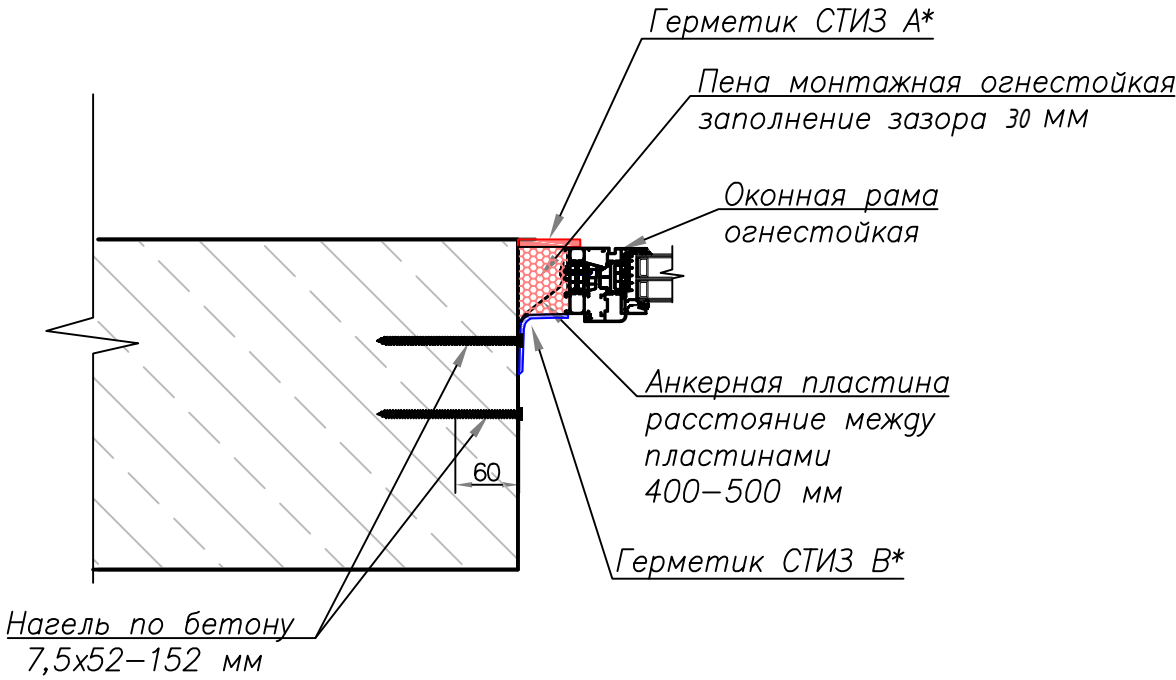

Узел примыкания к потолочному откосу проема рамы огнестойкого оконного блока

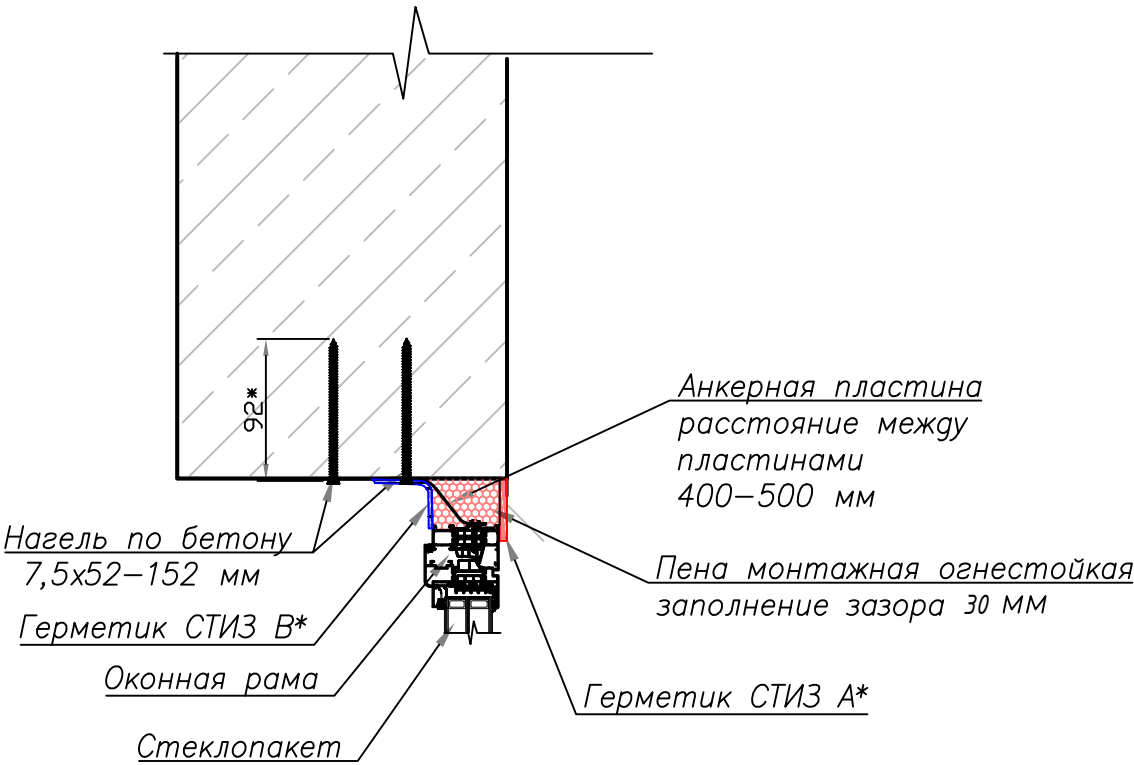


Узел примыкания к нижней части проема рамы огнестойкого оконного блока

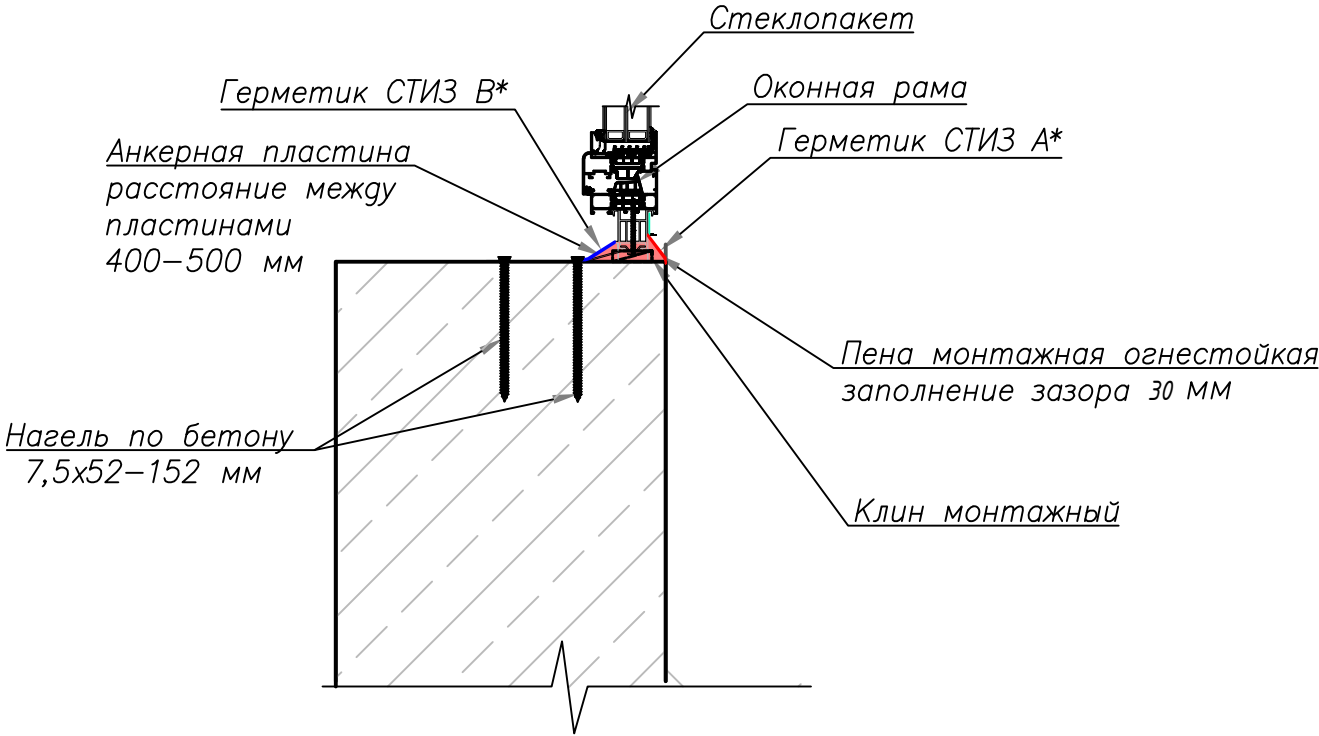


						ШК429		
						5-ая ул. Соколиной Горы, д.14		
Изм.	Кол.уч	Лист	N док.	Подпись	Дата	Монтажные узлы	Стадия	Лист/Листов
ГИП							РД	14/16
Проверил	Ткаченко Евгений						ООО "ШварцГрупп"	
Разраб.	Харитонова Ирина				18.08.2026			
Н.контр.								

Спецификация заполнения оконных проемов.


ОК-3/3 (1-эт)
ОК-3 (1-2-эт)

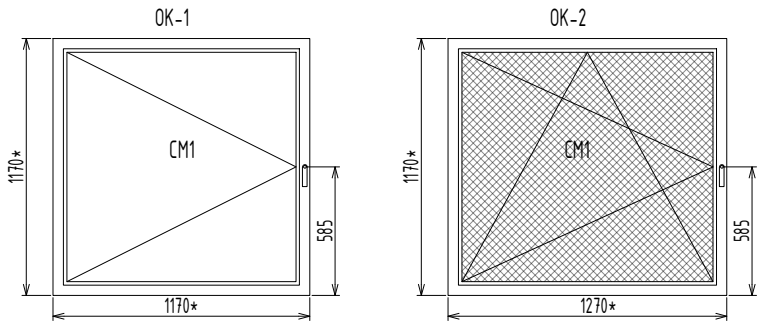


ОК-3 (3-4-эт)

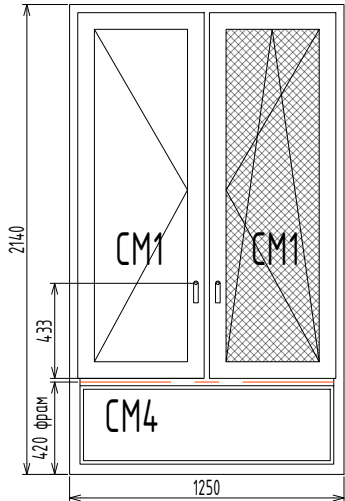


ОК-3/1 E30 (1-эт)

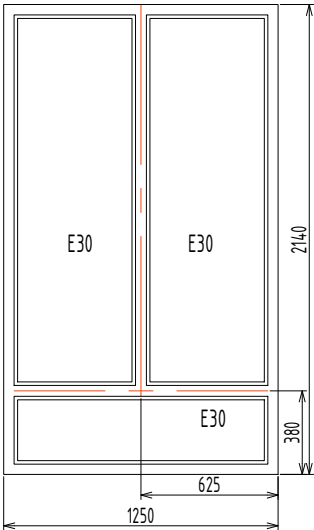


ОК-3/2 (1-2-эт)

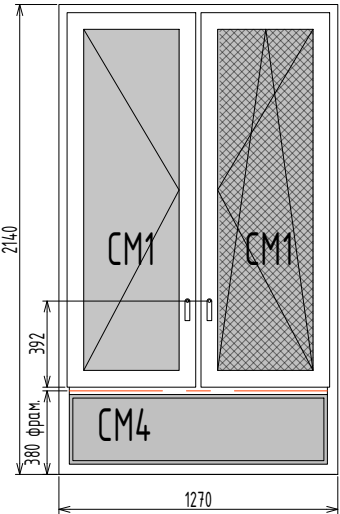


ОК-3/2 (3-4-эт)

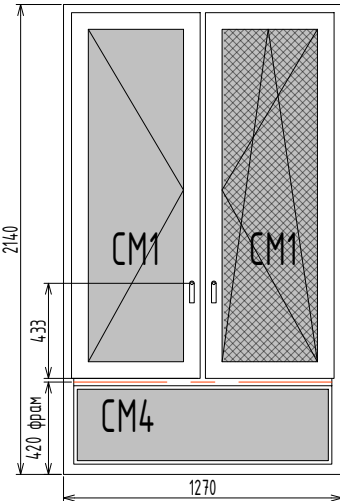


ОК-3/4 (1-2-эт)

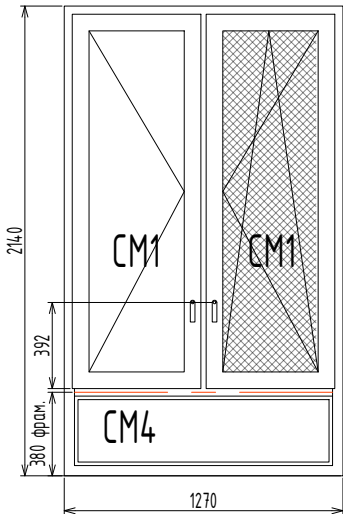


ОК-3/4 (3-4-эт)
+лестницы

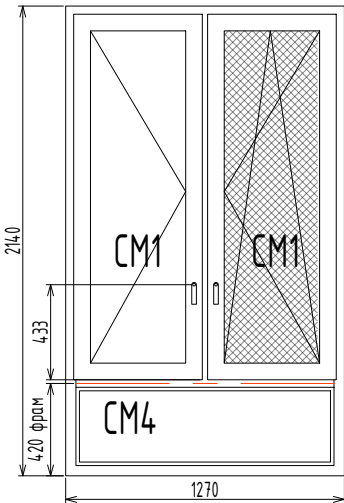


ОК-4/3 (1-2-эт)
ОК-4 (1-2-эт)

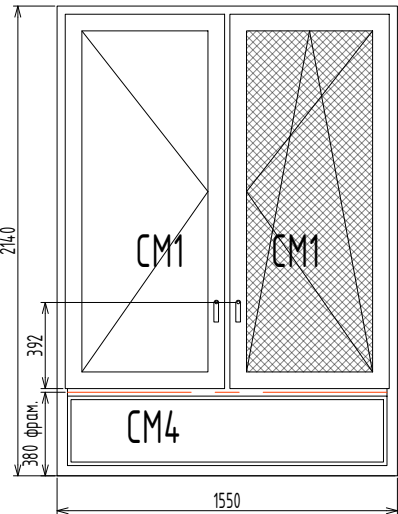


ОК-4/3 (3-4-эт)
ОК-4 (3-4-эт)

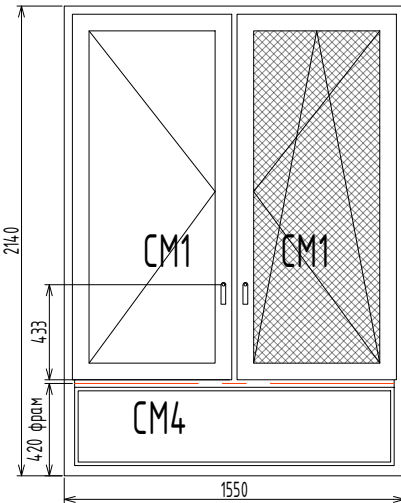

ОК-4/1 E30 (1-2-эт)

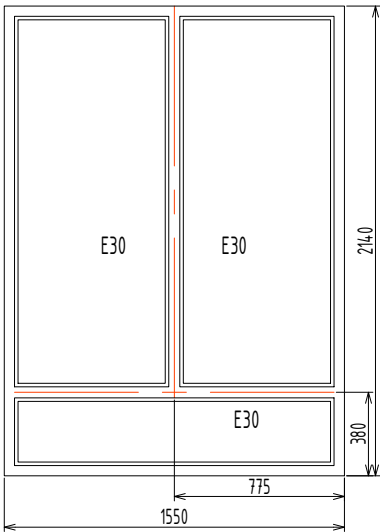


ОК-4/1 E30 (3-4-эт)

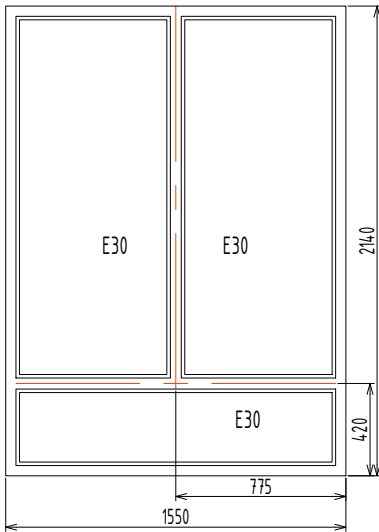

						ШК429		
						5-ая ул. Соколиной Горы, д.14		
Изм.	Кол.уч	Лист	№ док.	Подпись	Дата	Спецификация заполнения оконных проемов.	Стадия	Лист/Листов
ГИП	Проверил	Ткаченко Евгений					РД	15/16
Разраб.	Н.контр.	Харитонова Ирина			18.08.2026		ООО "ШварцГрупп"	

Спецификация заполнения оконных проемов.

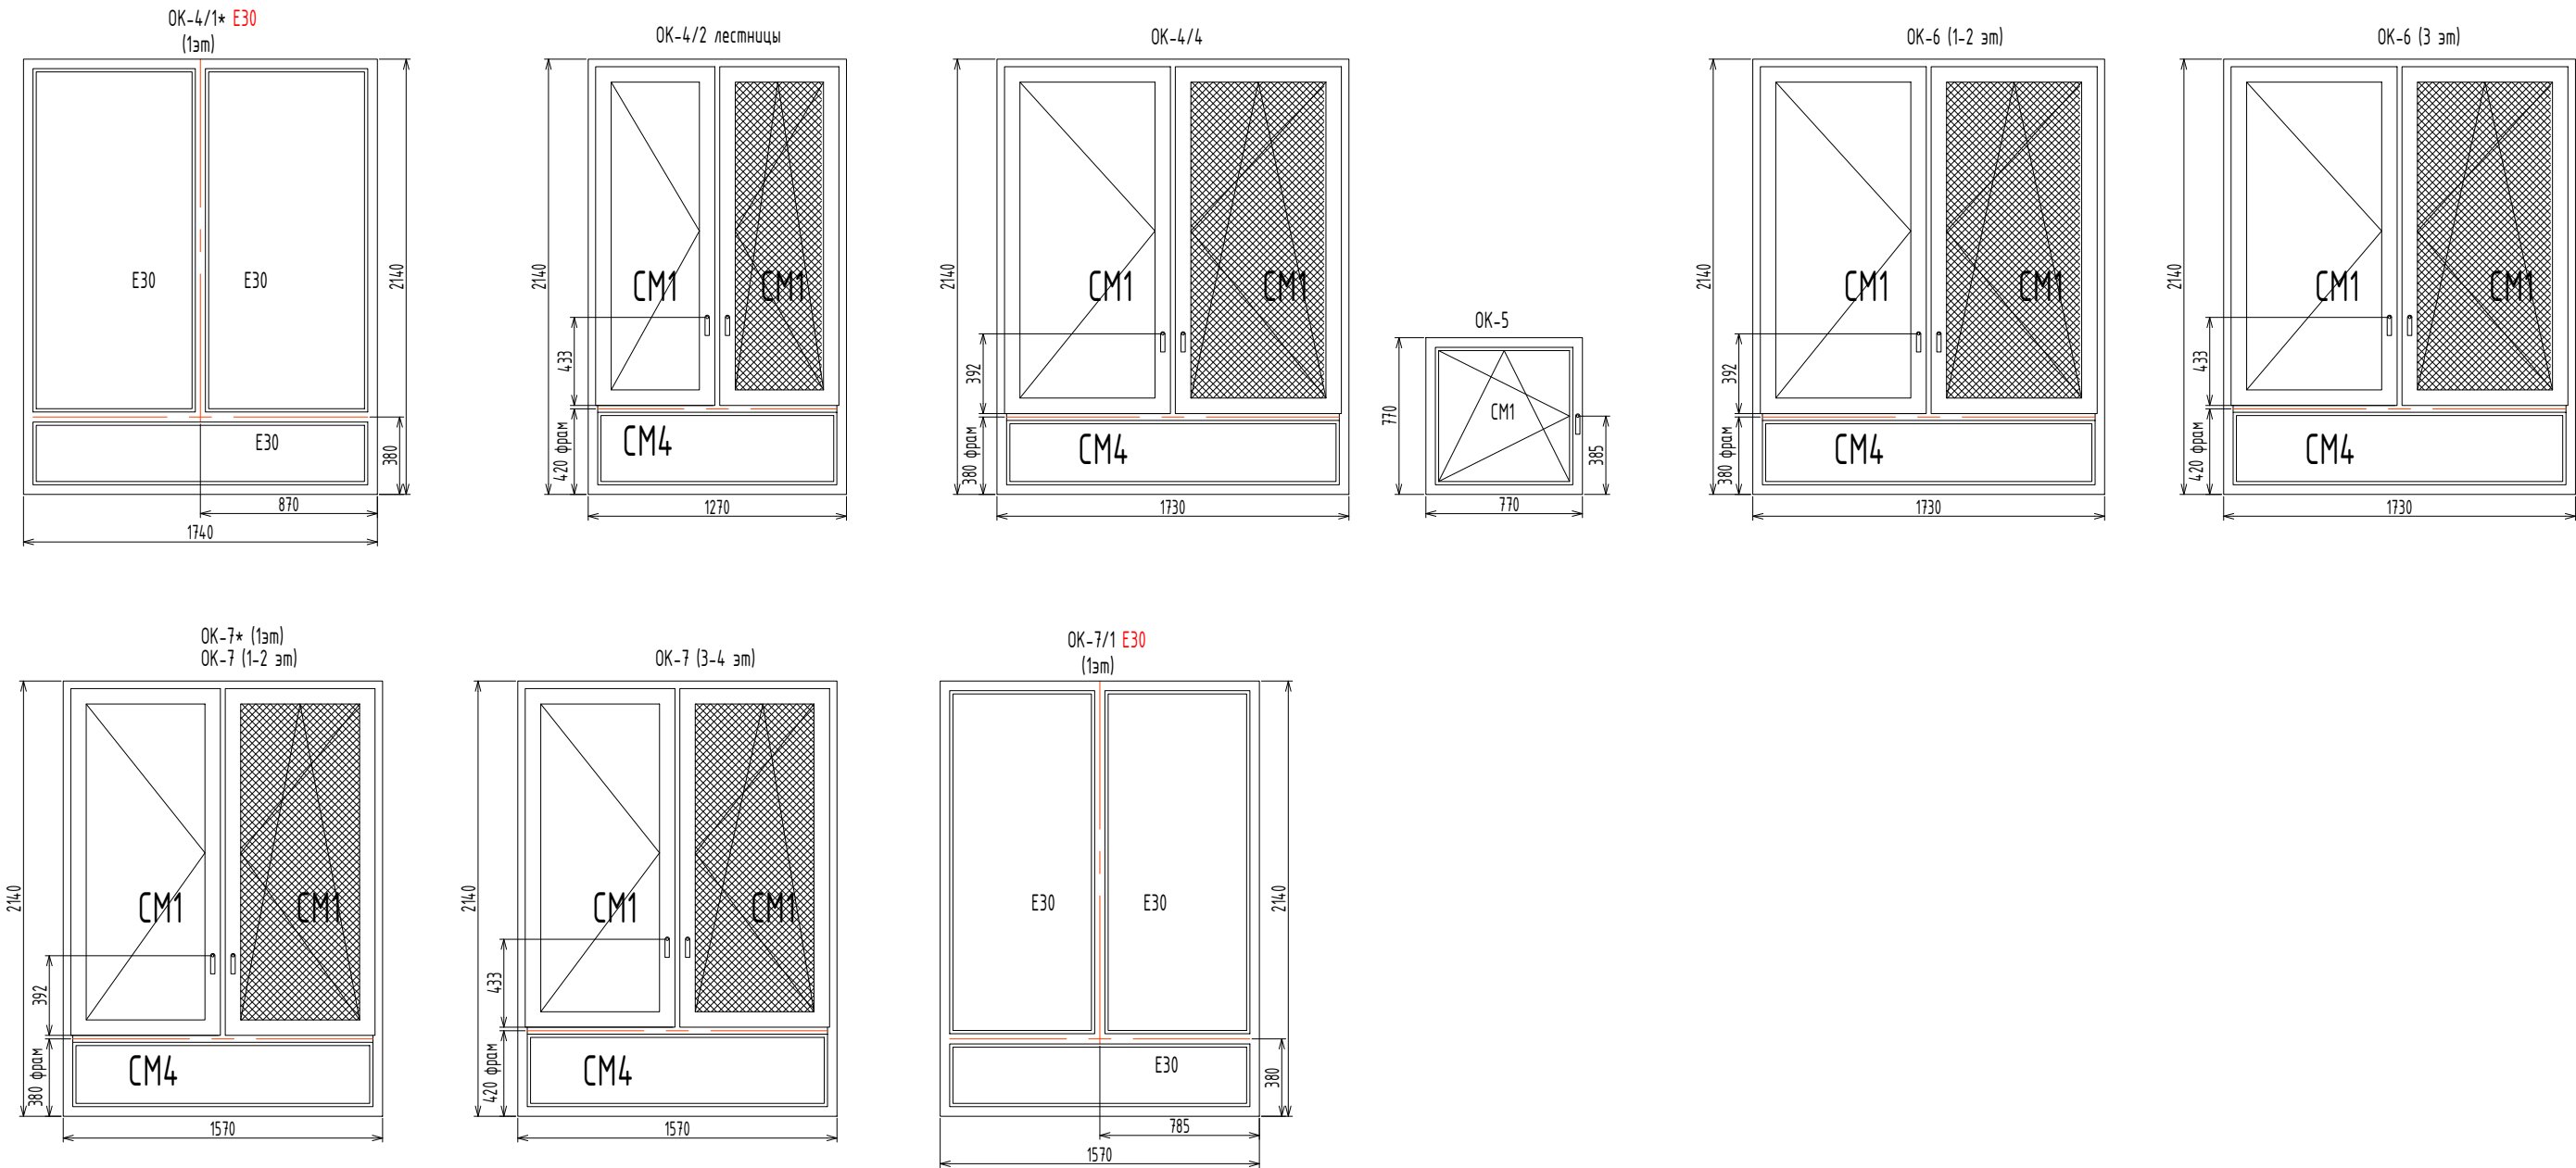

						ШК429		
						5-ая ул. Соколиной Горы, д.14		
Изм.	Кол.уч	Лист	N док.	Подпись	Дата	Спецификация заполнения оконных проемов.	Стадия	Лист/Листов
ГИП	Проверил	Ткаченко Евгений					РД	16/16
Разраб.	Харитонова Ирина				18.08.2026		ООО "ШварцГрупп"	
Н.контр.								