



Схема армирования входной группы в/о 7-14/А-В

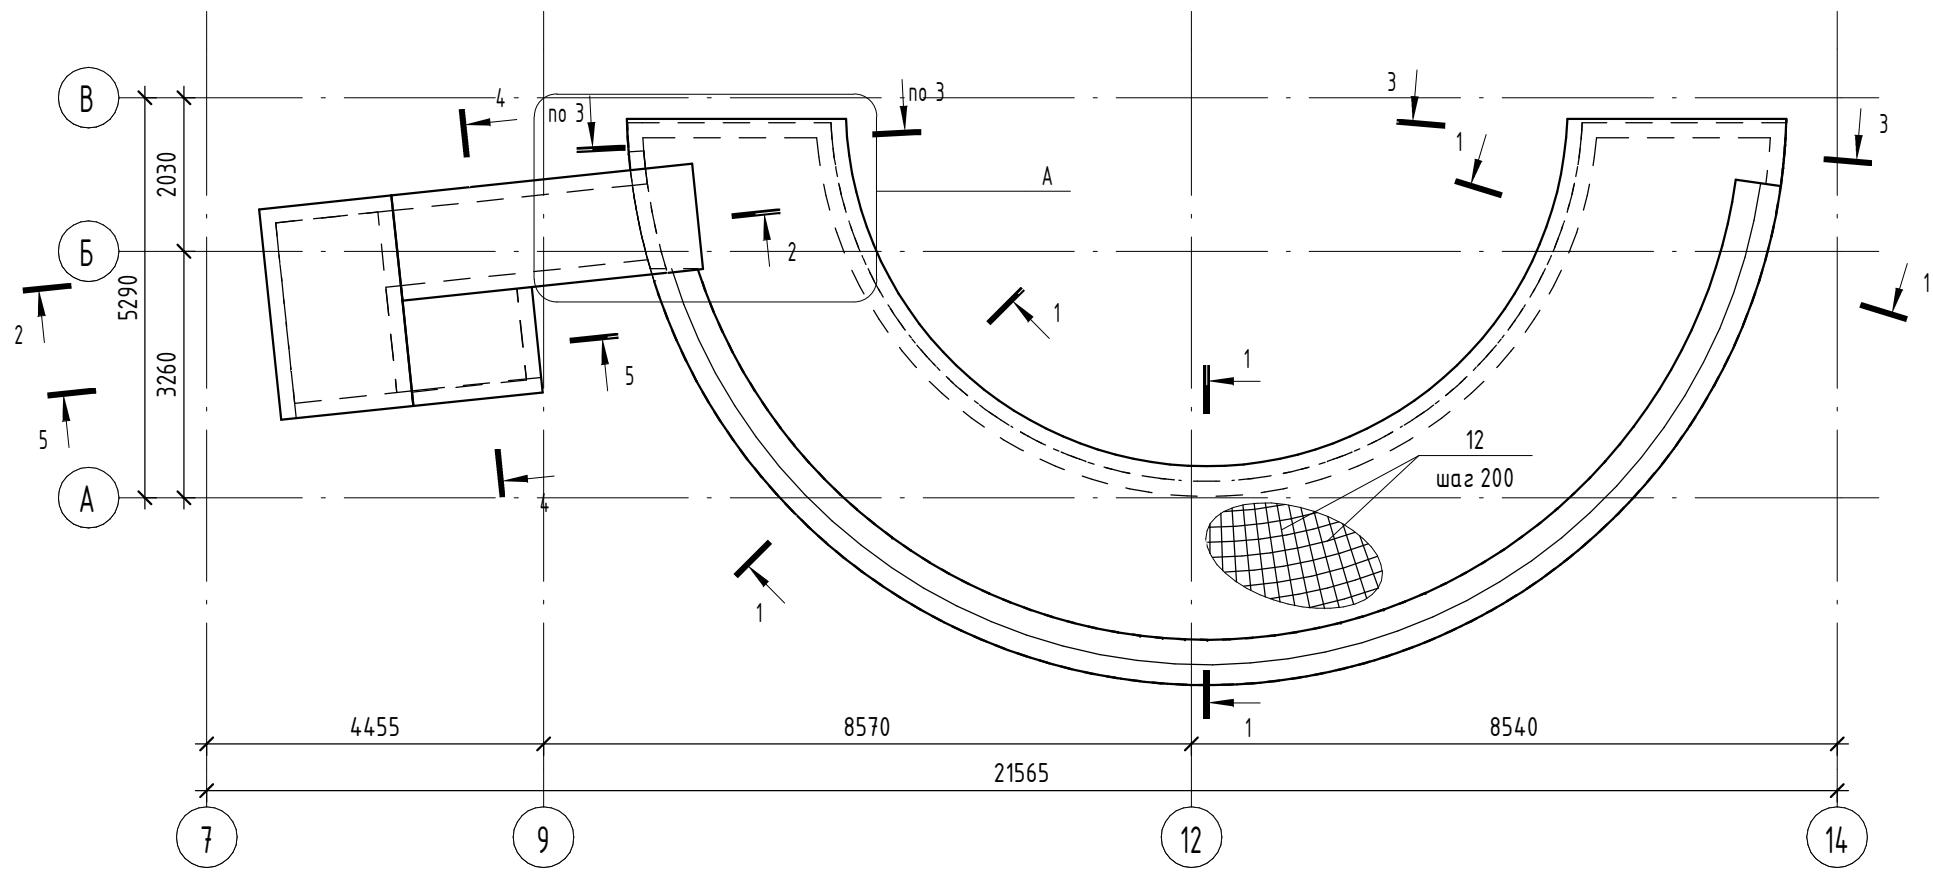

2-2

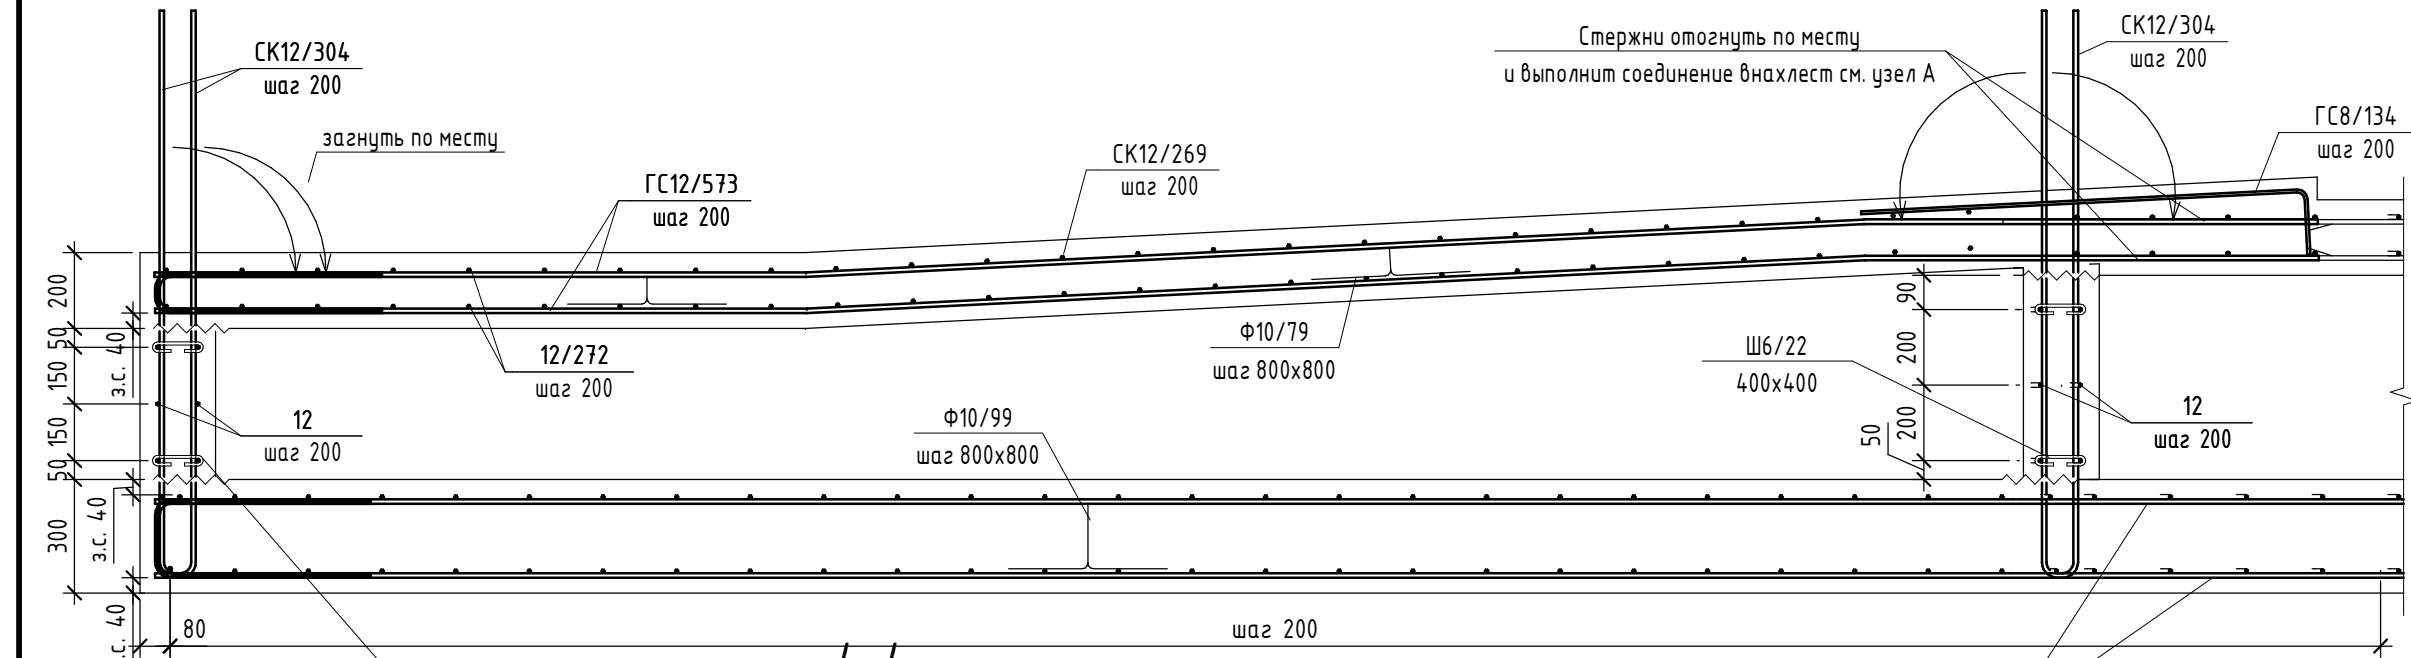

4-4

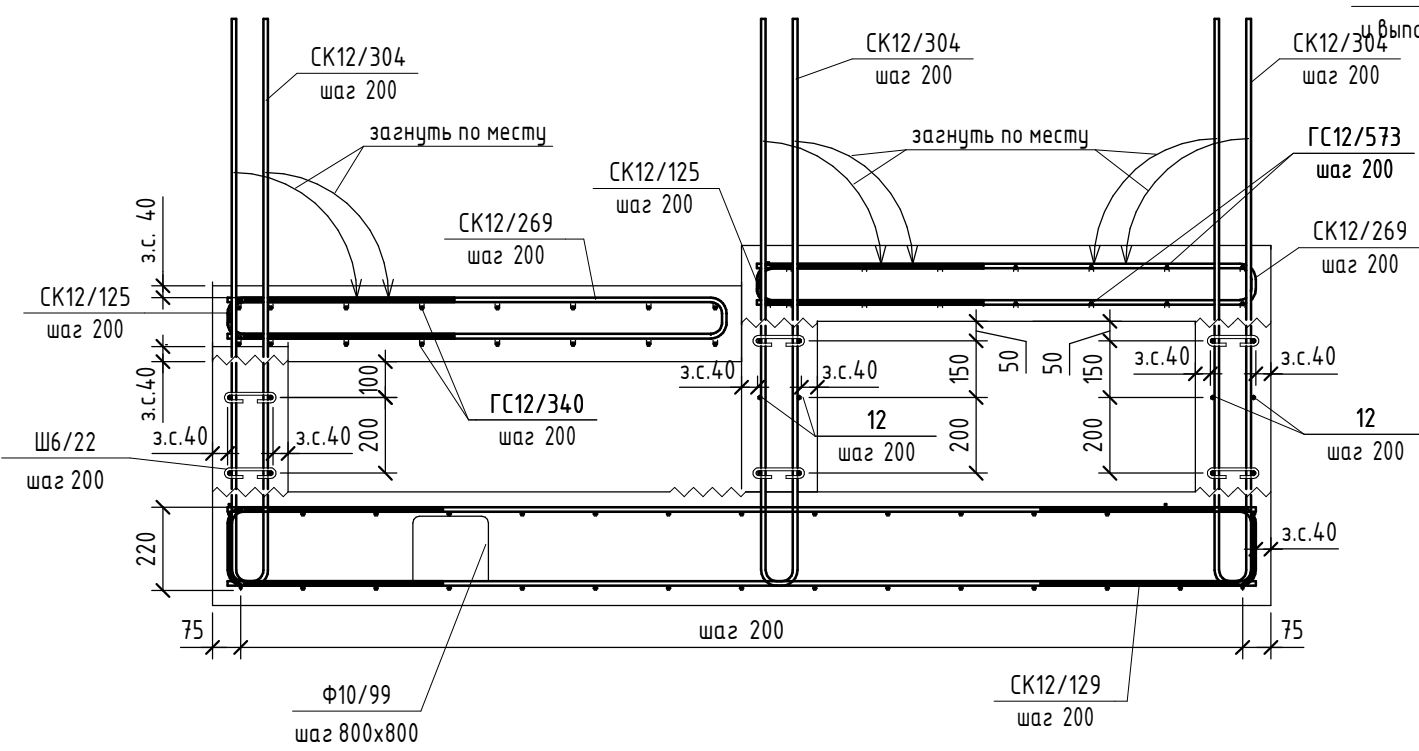


Схема расположения фиксаторов Ф1

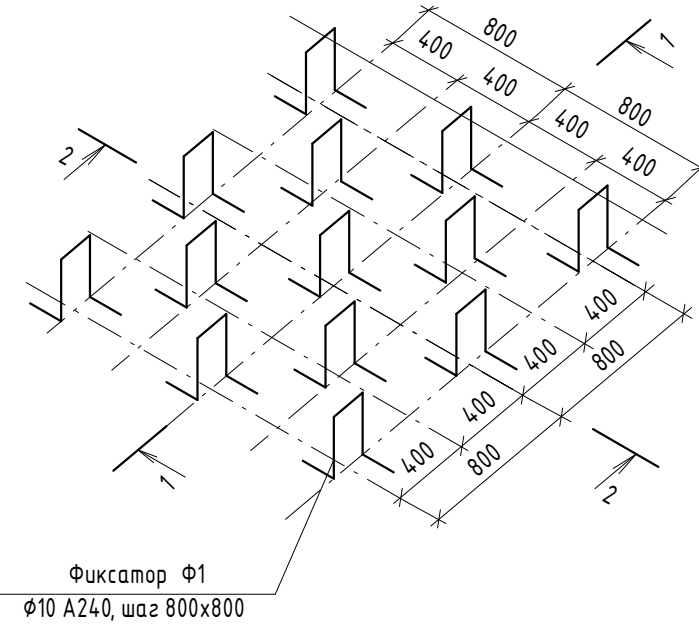


Схема расположения шпилек с шагом 400х400 в шахматном порядке



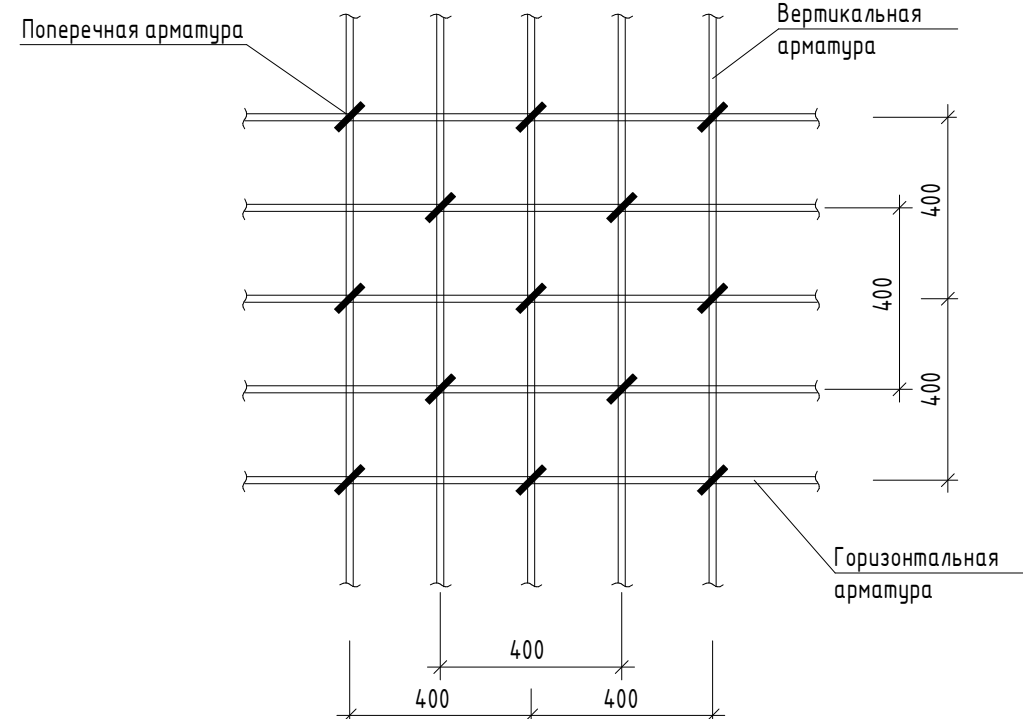


Схема стыка арматурных стержней А500С (перепуск стержней без сварки)

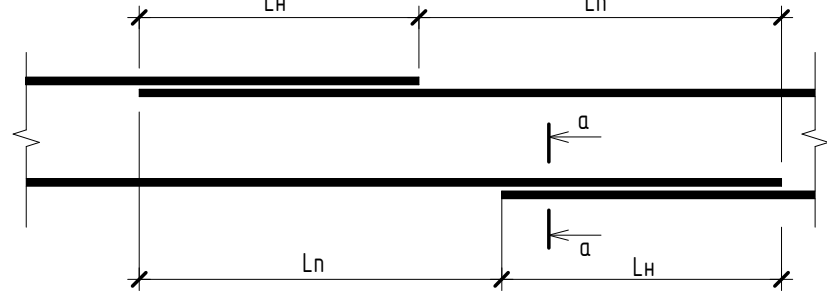


Диаметр, мм	Длина нахлеста Lн, мм	Смещение нахлеста Lп, мм
8	400	550
12	600	800


Типовой узел армирования торца фундаментной плиты

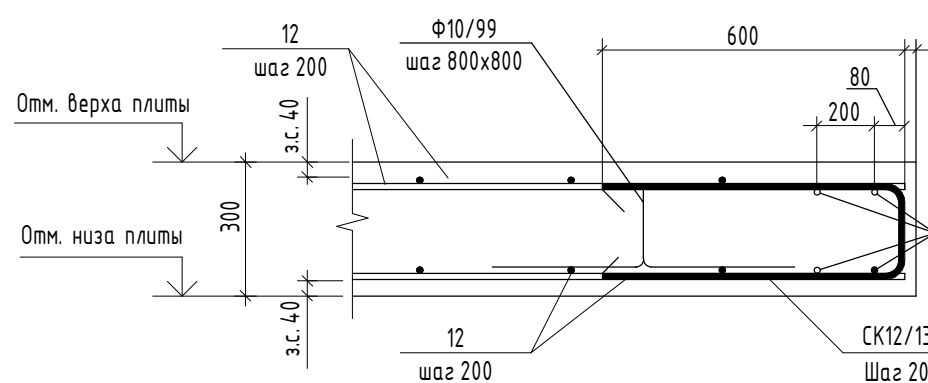


Узел Г-образного соединения стен

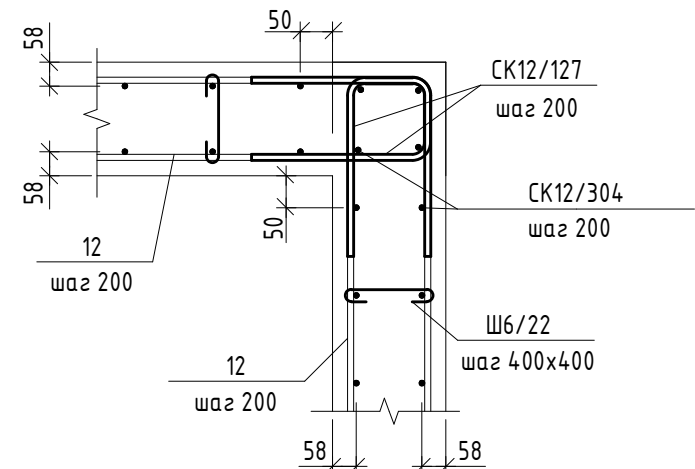


Типовой узел армирования торца плиты

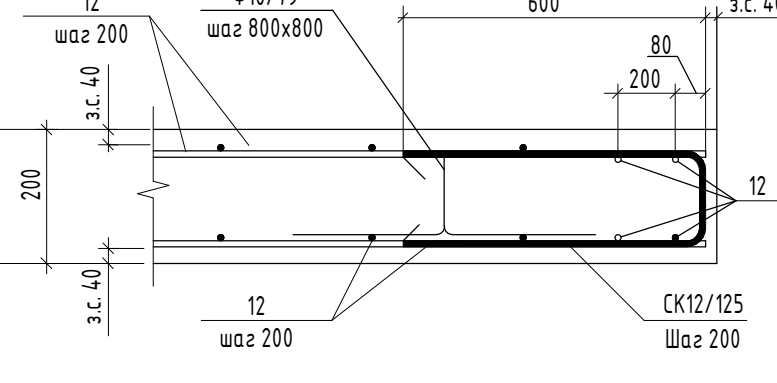


Узел Т-образного соединения стен

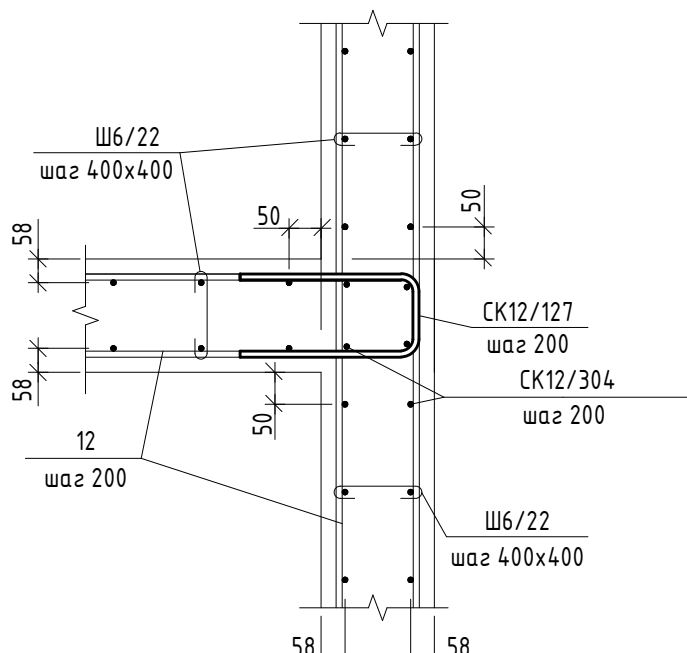


1-1

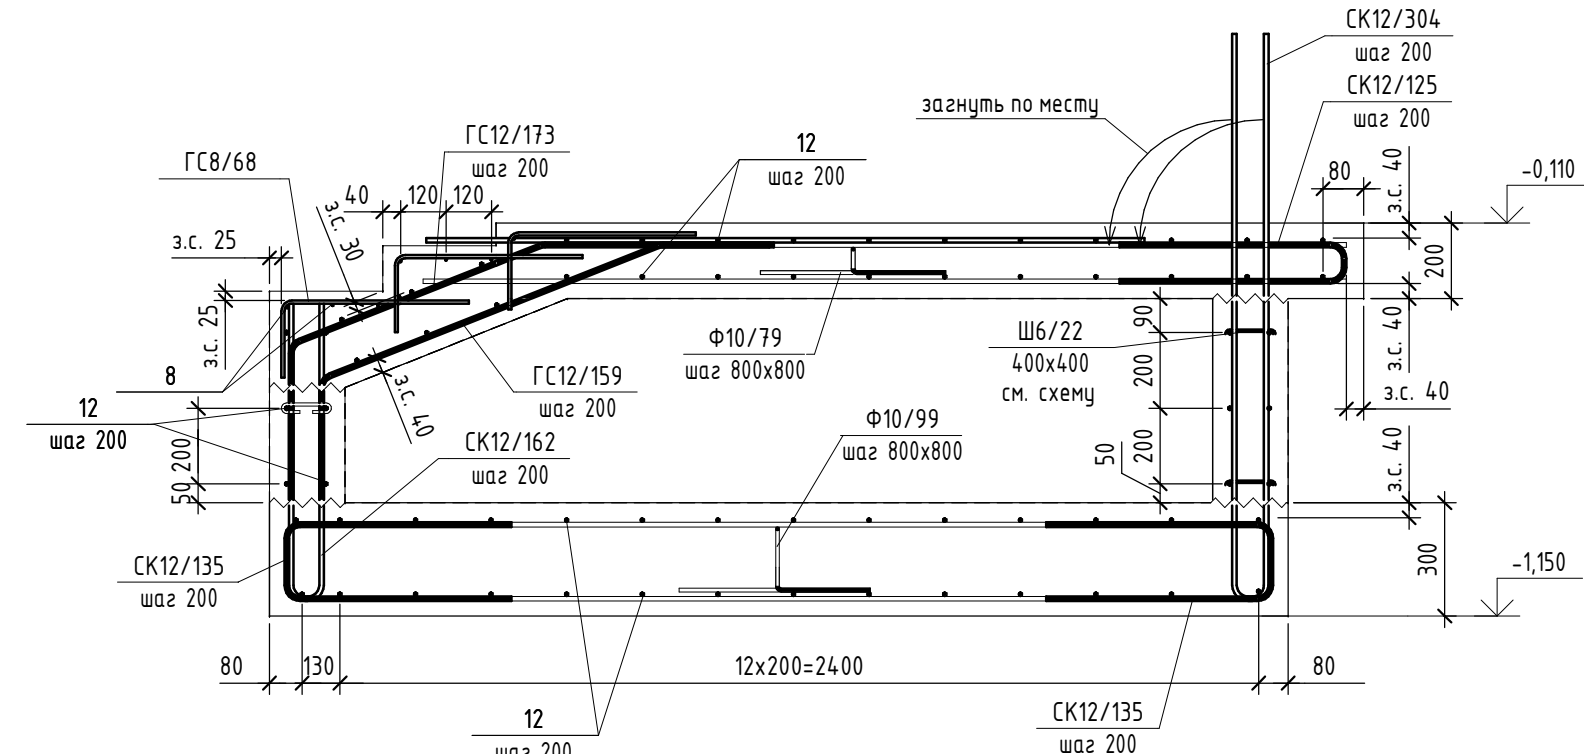

3-3

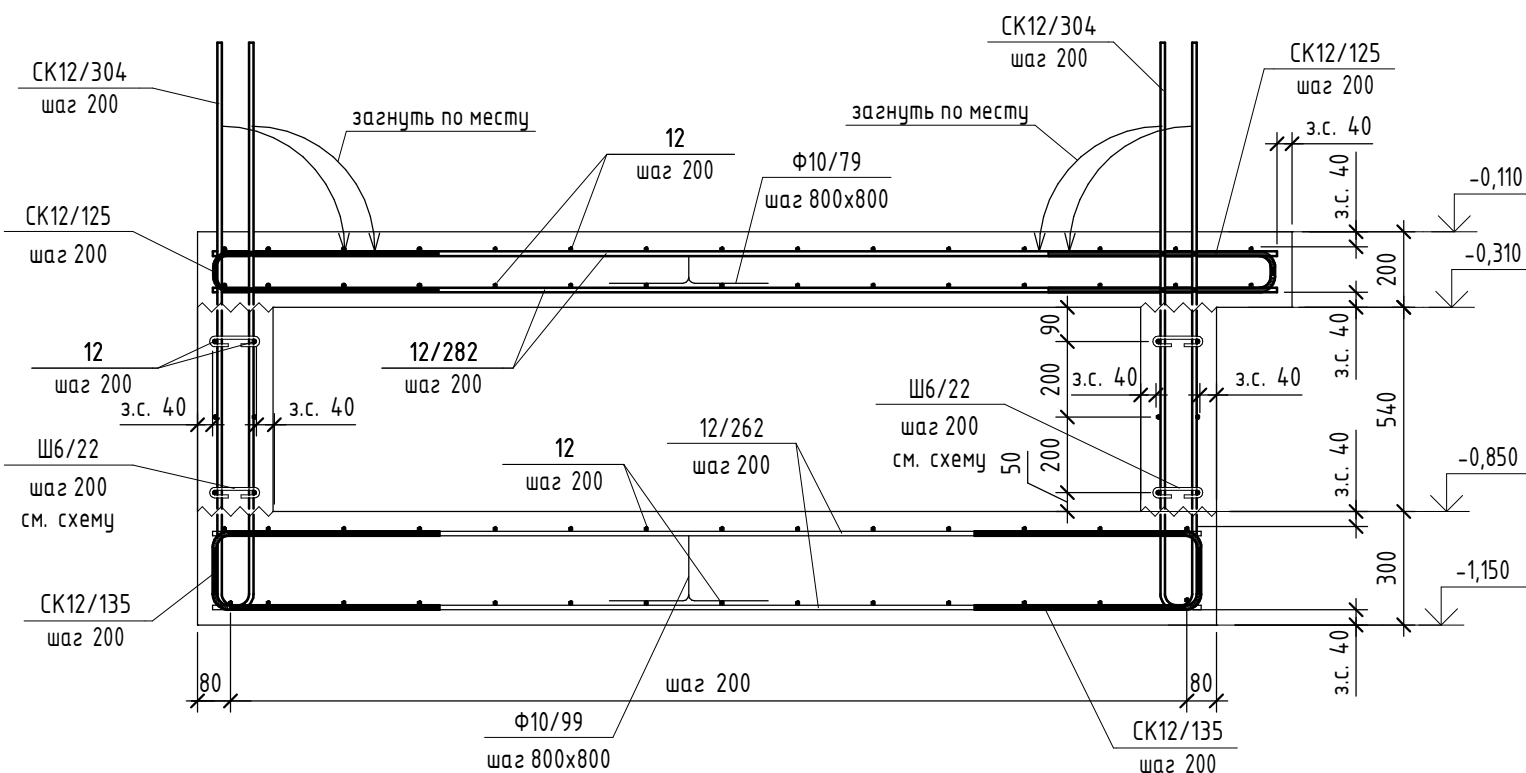

5-5

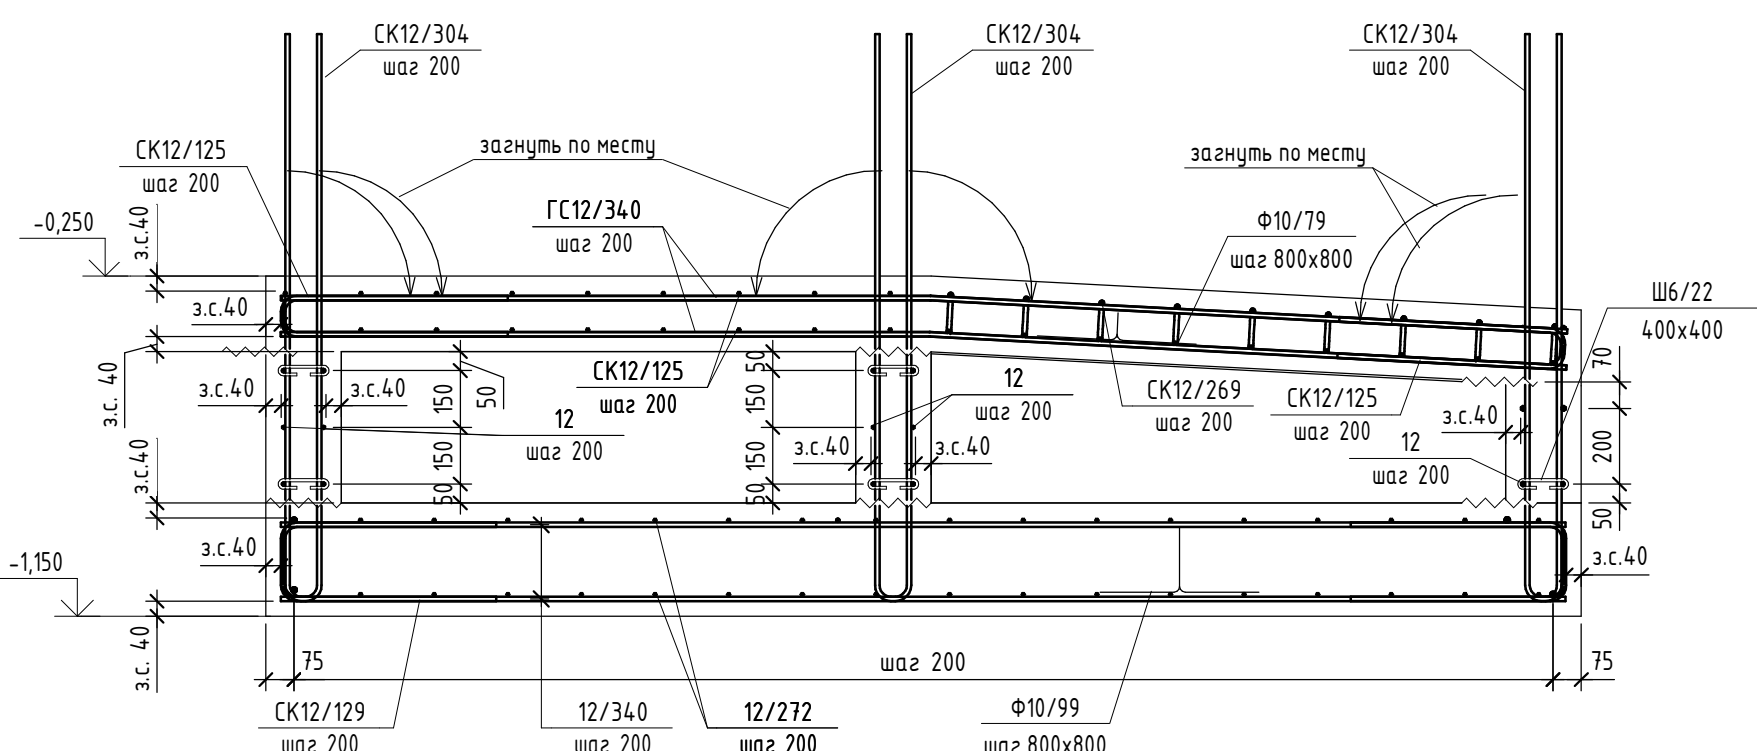


Ведомость деталей

Поз.	Эскиз
ГС8/134	
ГС8/68	
ГС12/573	
ГС12/173	
ГС12/159	
ГС12/569	
ГС12/340	
ГС12/340	
СК12/304	
СК12/269	
СК12/162	
СК12/135	
СК12/129	
СК12/127	
СК12/125	
Ш6/22	
Ф10/99	
Ф10/79	

Спецификация монолитной конструкции

Поз.	Обозначение	Наименование	Кол.	Масса ед, кг	Примечание
		Наименование конструкции			
		Детали			
8	ГОСТ 34028-2016	Ø8 А500С L, поз.м	183,4	0,395	72,45
12	ГОСТ 34028-2016	Ø12 А500С L, поз.м	1445,8	0,888	1283,85
12/606	ГОСТ 34028-2016	Ø12 А500С L= 6060	14	5,382	75,34
12/340	ГОСТ 34028-2016	Ø12 А500С L= 3400	16	3,02	48,32
12/282	ГОСТ 34028-2016	Ø12 А500С L= 2815	10	2,5	25,00
12/272	ГОСТ 34028-2016	Ø12 А500С L= 2720	54	2,416	130,46
12/262	ГОСТ 34028-2016	Ø12 А500С L= 2620	8	2,327	18,62
12/242	ГОСТ 34028-2016	Ø12 А500С L= 2420	8	2,149	17,20
12/200	ГОСТ 34028-2016	Ø12 А500С L= 2000	94	1,776	167,32
12/190	ГОСТ 34028-2016	Ø12 А500С L= 1900	98	1,688	165,62
12/132	ГОСТ 34028-2016	Ø12 А500С L= 1320	16	1,173	18,76
ГС8/134	ГОСТ 34028-2016	Ø8 А500С L= 1340	7	0,53	3,71
ГС8/68	ГОСТ 34028-2016	Ø8 А500С L= 680	3	0,269	0,81
ГС12/573	ГОСТ 34028-2016	Ø12 А500С L= 5725	15	5,084	76,26
ГС12/173	ГОСТ 34028-2016	Ø12 А500С L= 1725	98	1,532	149,94
ГС12/159	ГОСТ 34028-2016	Ø12 А500С L= 1585	98	1,408	138,18
ГС12/569	ГОСТ 34028-2016	Ø12 А500С L= 5685	1	5,049	5,05
ГС12/340	ГОСТ 34028-2016	Ø12 А500С L= 3400	2	3,02	6,04
ГС12/340	ГОСТ 34028-2016	Ø12 А500С L= 3400	14	3,02	42,28
СК12/304	ГОСТ 34028-2016	Ø12 А500С L= 3040	236	2,7	637,20
СК12/269	ГОСТ 34028-2016	Ø12 А500С L= 2695	25	2,394	59,85
СК12/162	ГОСТ 34028-2016	Ø12 А500С L= 1615	98	1,435	141,12
СК12/135	ГОСТ 34028-2016	Ø12 А500С L= 1355	237	1,204	284,50
СК12/129	ГОСТ 34028-2016	Ø12 А500С L= 1295	79	1,15	90,85
СК12/127	ГОСТ 34028-2016	Ø12 А500С L= 1265	51	1,124	57,12
СК12/125	ГОСТ 34028-2016	Ø12 А500С L= 1255	197	1,115	220,20
Ш6/22	ГОСТ 34028-2016	Ø6 А240 L= 220	379	0,049	18,57
Ф10/99	ГОСТ 34028-2016	Ø10 А240 L= 995	192	0,614	117,89
Ф10/79	ГОСТ 34028-2016	Ø10 А240 L= 795	129	0,491	63,34

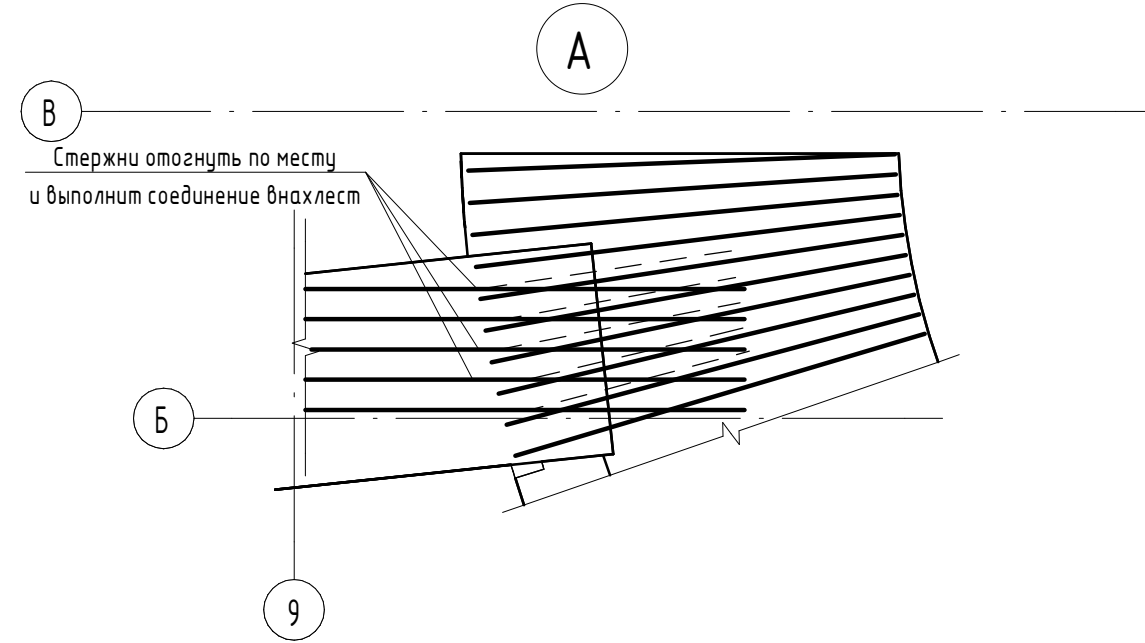

Условные обозначения:

з.с. - защитный слой
~~~~~ - Рабочий шаг бетонирования (РШБ)

- Общие данные см. лист 1
- Опубличные чертежи см. лист 39.
- Ведомость расхода стали см. лист 42.

|          |               |      |        |                                                                                       |       |  |  |  |   |   |        |
|----------|---------------|------|--------|---------------------------------------------------------------------------------------|-------|--|--|--|---|---|--------|
|          |               |      |        |                                                                                       |       |  |  |  | 16-25/Г-Р-КР1   |   |        |
|          |               |      |        |                                                                                       |       |  |  |  | Капитальный ремонт объекта "ГБОУ "Школа №429 "Сокольная гора",<br>расположенного по адресу: г.Москва, ул.Соколиной Горы 5-ая, д.14 |   |        |
| Изм.     | Колуч.        | Лист | № док. | Подпись                                                                               | Дата  |  |  |  | Стадия   | Лист                                                                                                | Листов |
| Разраб.  | Хабиров       |      |        |  | 07.26 |  |  |  | Конструктивные решения   | Р                                                                                                   | 40     |
| Проверил | Дидик         |      |        |  | 07.26 |  |  |  |   |   |        |
| Н.контр. | Губарева Е.В. |      |        |  | 07.26 |  |  |  | Армирование входной группы в/о 7-14/ А-В                                                                                           |  <b>АЗУРИТ</b> |        |
| ГИП      | Маркова       |      |        |  | 07.26 |  |  |  |   |   |        |