



Схема расположения фундаментной плиты входной группы в/о 17.1/Л.1 на отм. -1,990

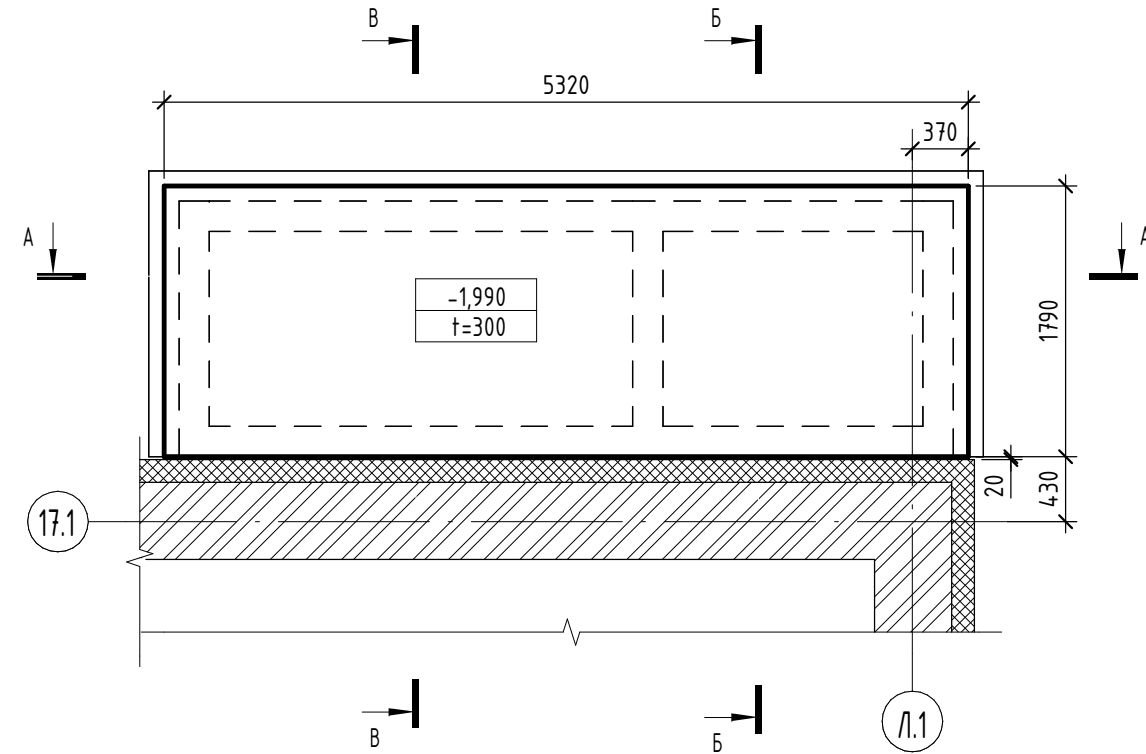

А-А
Опалубка

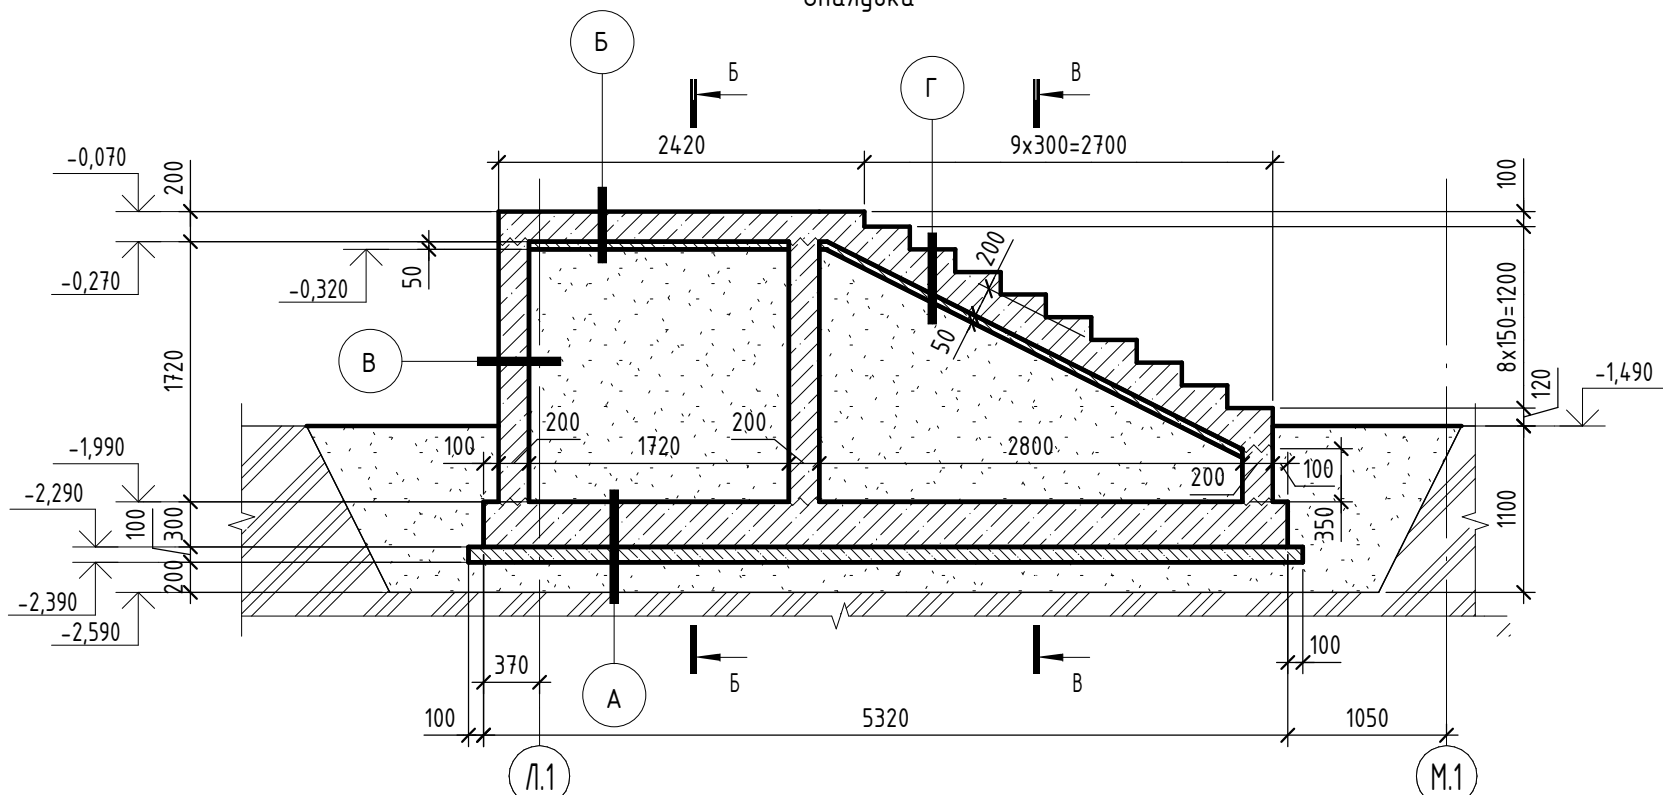

Б-Б
Опалубка


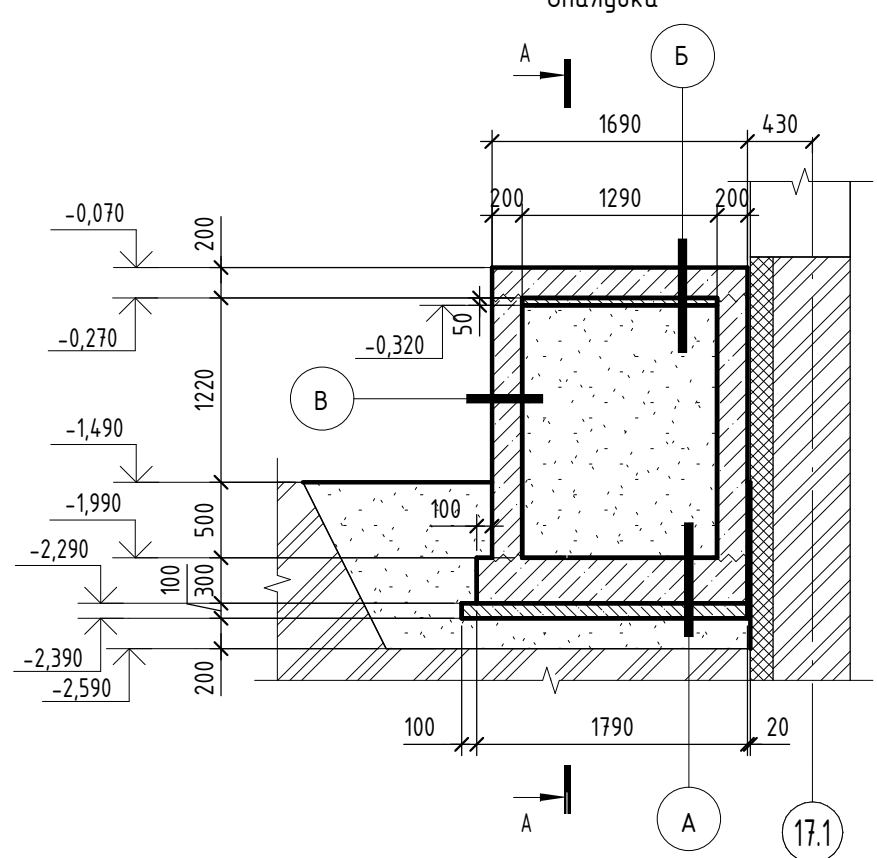


Схема расположения стен входной группы в/о 17.1/Л.1 на отм. -1,990

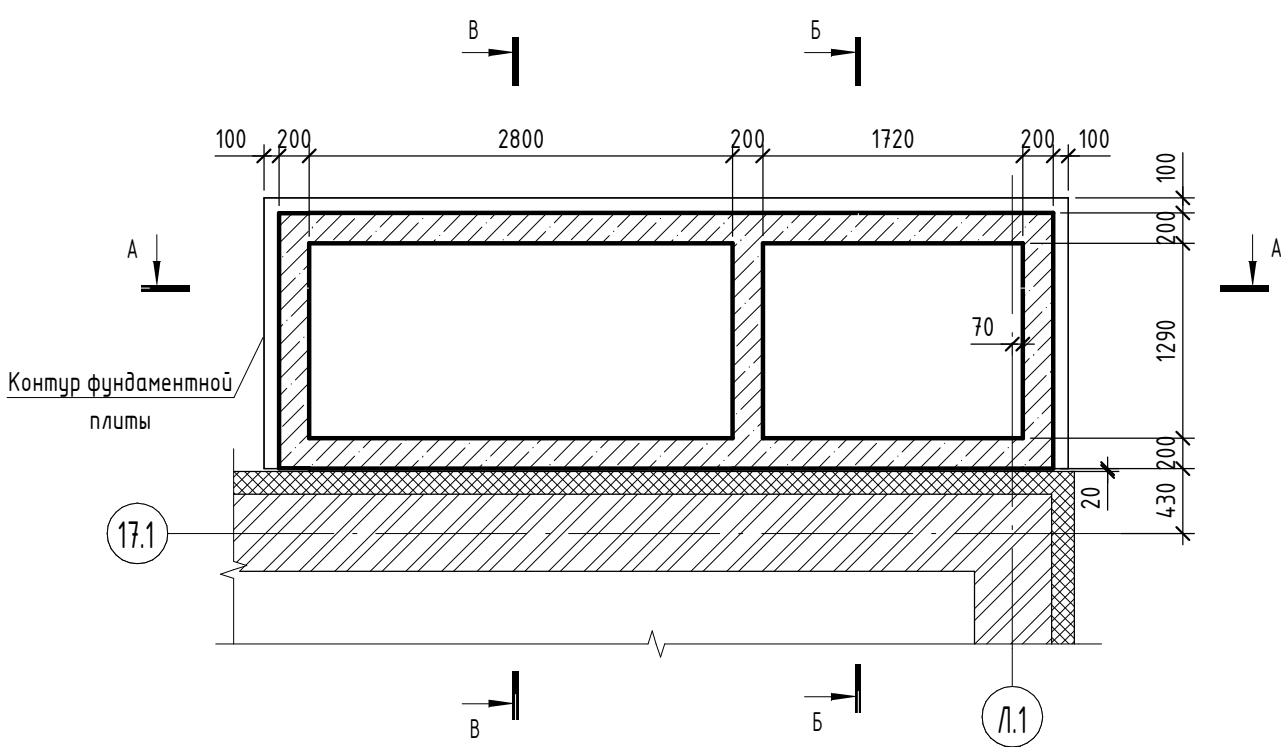

В-В
Опалубка


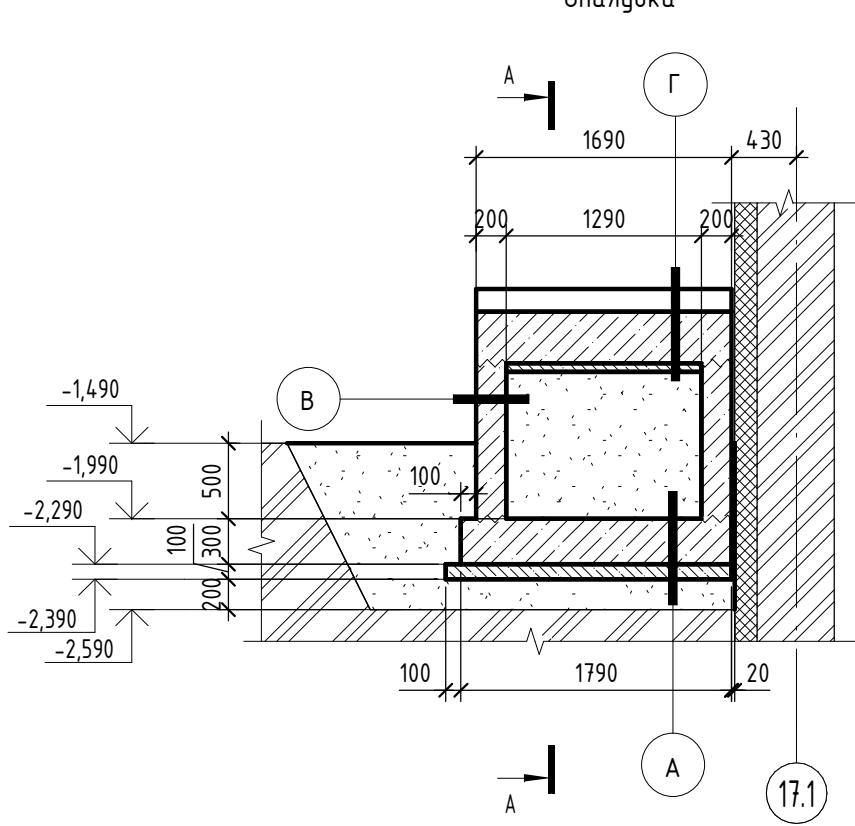


Схема расположения входной группы в/о 17.1/Л.1 на отм. -0,070

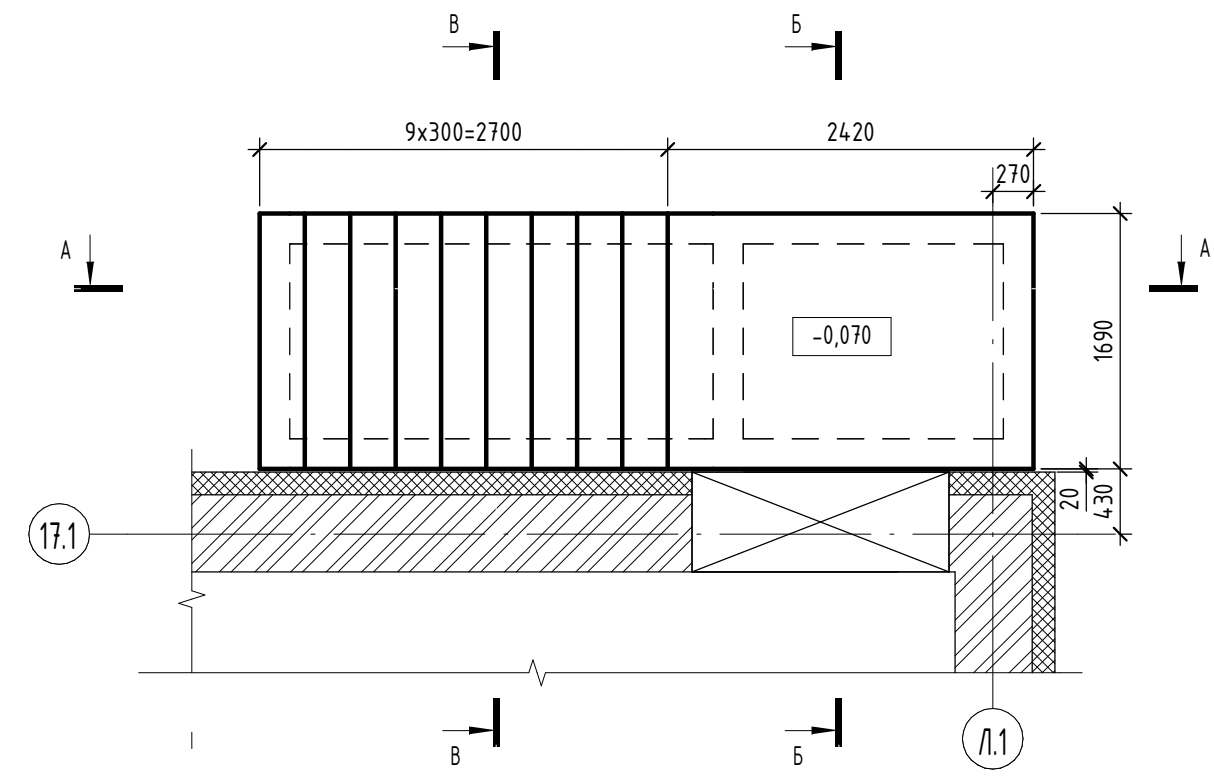

А	Монолитная плита (В25 W6 F150)	-300мм
	Гидроизоляция обмазочная	-2 слоя
	Бетонная подготовка В7,5	-100мм
	Песок средней крупности	
	утрамбованный послойно (Купл=0,95)	-200мм
	Пленка ПЭ 200мкм	-2 слоя
	Грунт основания	

Монолитная плита (В25 W6 F150)	-200мм
Бетонная подготовка В7,5	-50мм
Пленка ПЭ 200мкм	-2 слоя
Засыпка песком средней крупности	
утрамбованный послойно (Купл=0,95)	
Пленка ПЭ 200мкм	-2 слоя

Гидроизоляция обмазочная	-2 слоя
Монолитная стена (В25 W6 F150)	-200мм
Пленка ПЭ 200мкм	-2 слоя
Засыпка песком средней крупности	
утрамбованный послойно (Купл=0,95)	

Монолитная лестница (В25 W6 F150)	-200мм
Бетонная подготовка В7,5	-50мм
Пленка ПЭ 200мкм	-2 слоя
Засыпка песком средней крупности	
утрамбованный послойно (Купл=0,95)	
Пленка ПЭ 200мкм	-2 слоя

- Общие данные см. лист 1
- Армирование см. лист 3
- Все конструкции соприкасающиеся с грунтом гидроизолировать 2 слоями обмазочной гидроизоляции на битумной основе по 2 слоям битумного праймера.

Ведомость расхода материалов


Поз.	Обозначение	Наименование	Кол.	Масса ед, кг	Примечание
		Материалы			
	ГОСТ 30693-2000	Гидроизоляция обмазочная (Битумная мастика)			27,63 м ²
	ГОСТ 8736-2014	Песок средней крупности			20,34 м ³
	ГОСТ 10354-82	Пленка полиэтиленовая 200 мкм (2 слоя)			30,21 м ²

0,000=156,92

16-25/Г-Р-КР1					
Капитальный ремонт объекта "ГБОУ "Школа №429 "Соколиная гора", расположенного по адресу: г.Москва, ул.Соколиной Горы 5-ая, д.14					
Изм.	Кол.уч.	Лист	№ док.	Подпись	Дата
Разраб.	Шевченко	07.26			
Проверил	Дидык	07.26			
Конструктивные решения					Стадия
					Р
					Лист
					10
					Листов
Н.контр.	Губарева Е.В.	07.26			
ГИП	Маркова	07.26			
Схема расположения входной группы в/о 17.1/Л.1					



Схема армирования стен входной группы в/о 17.1/Л.1 на отм -1,990

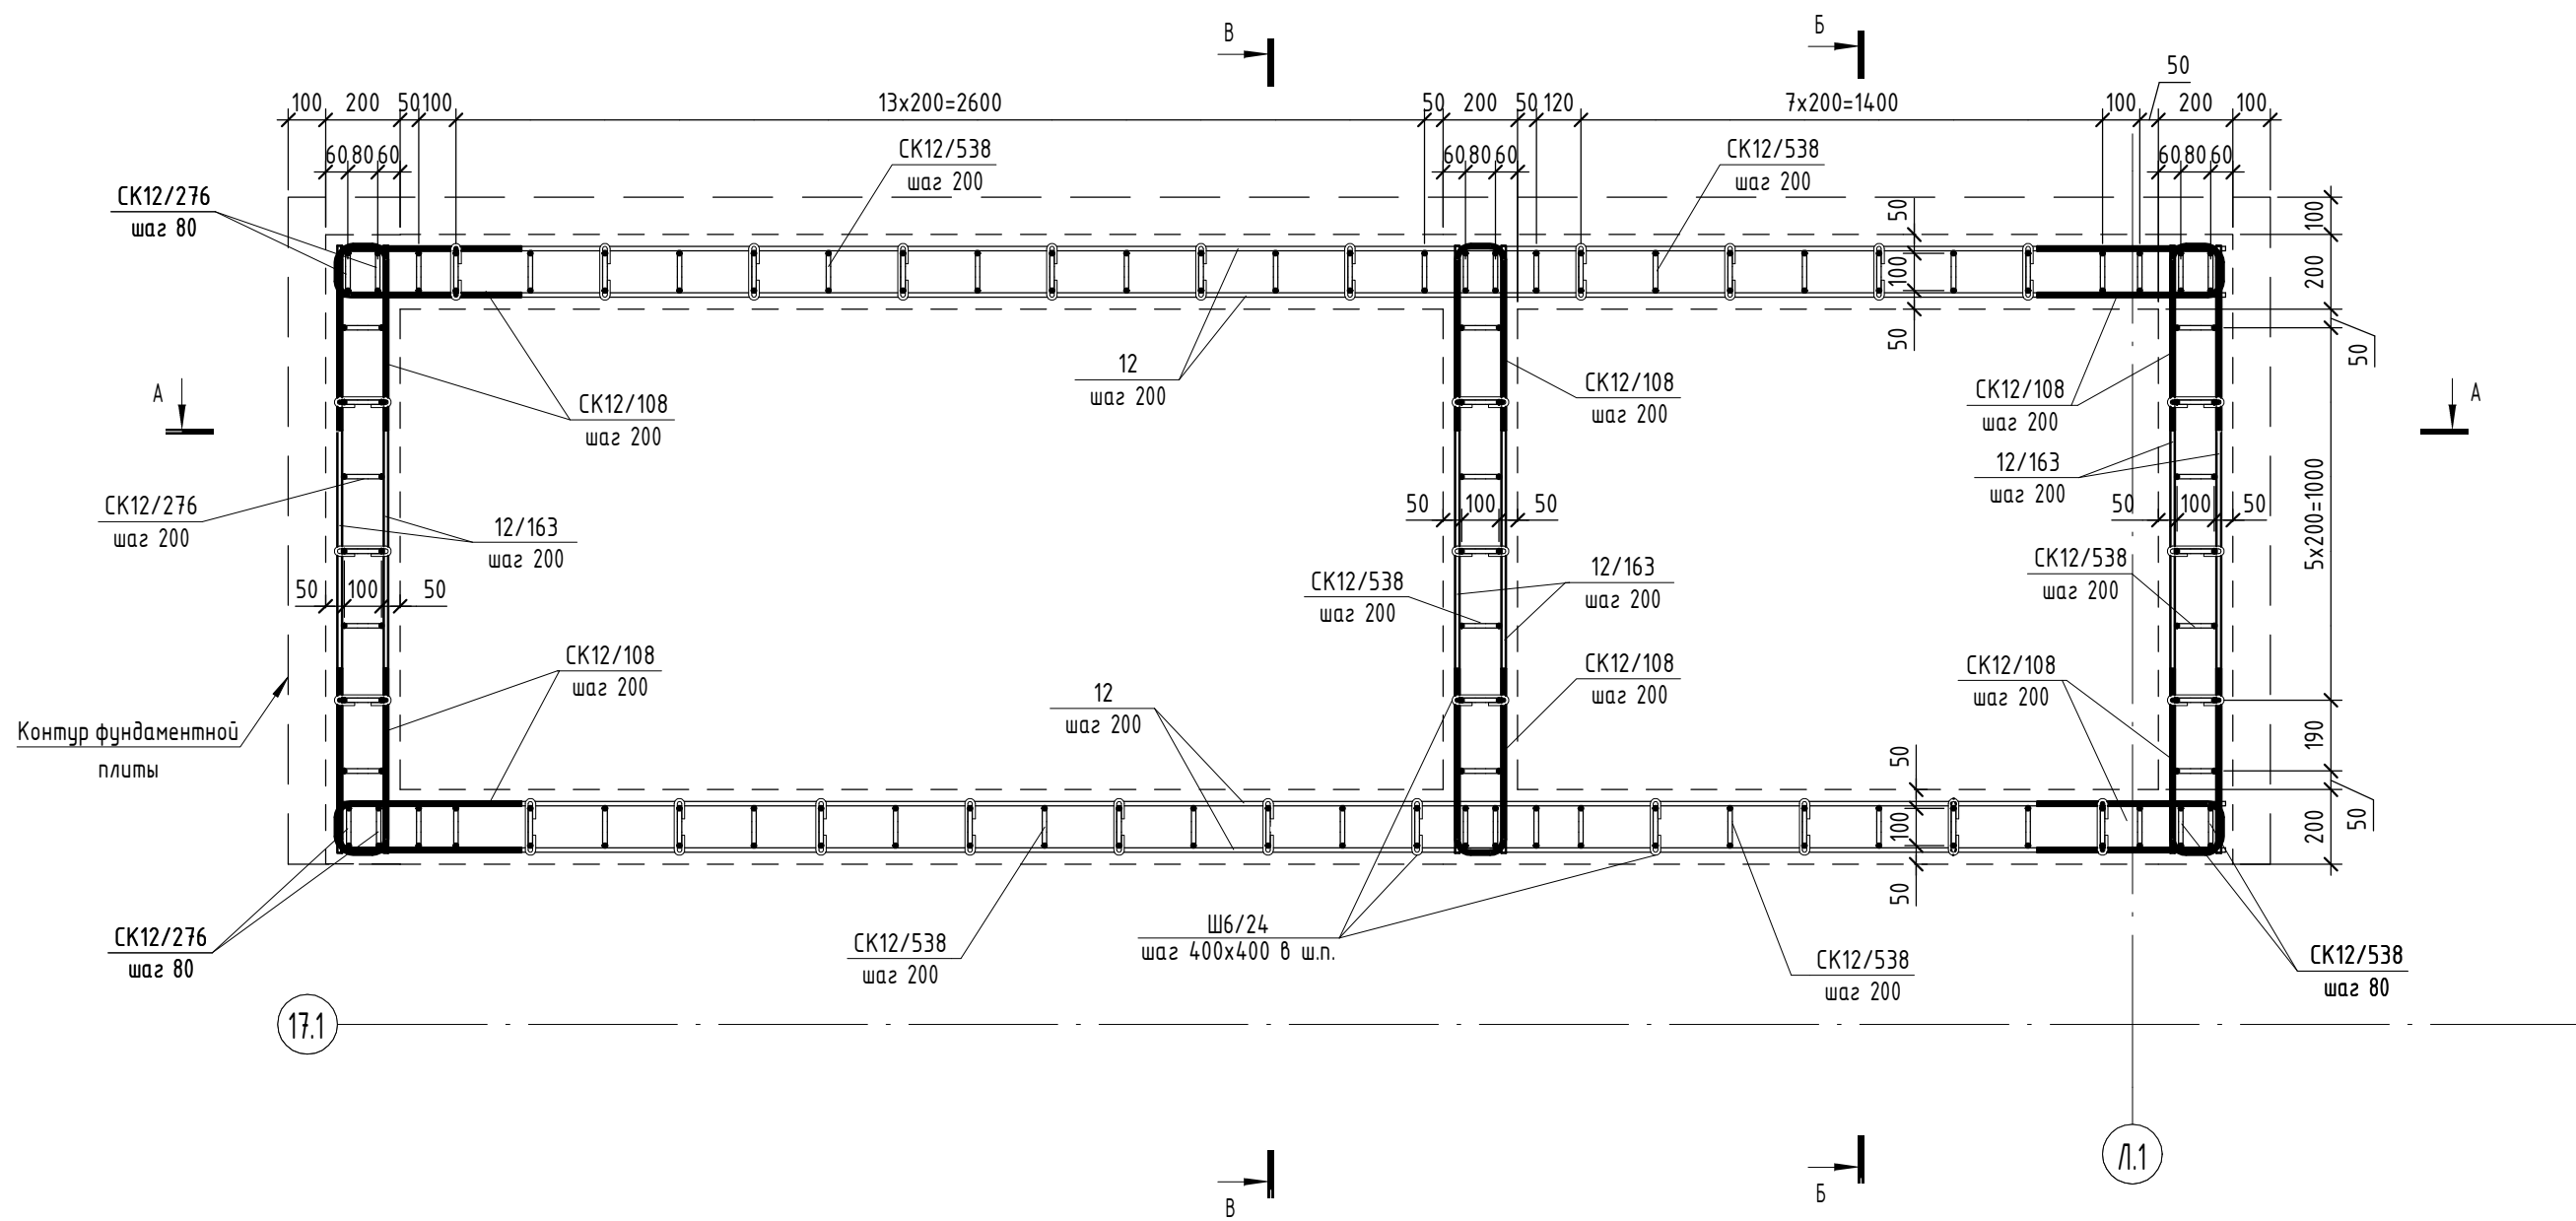

А-А
Армирование

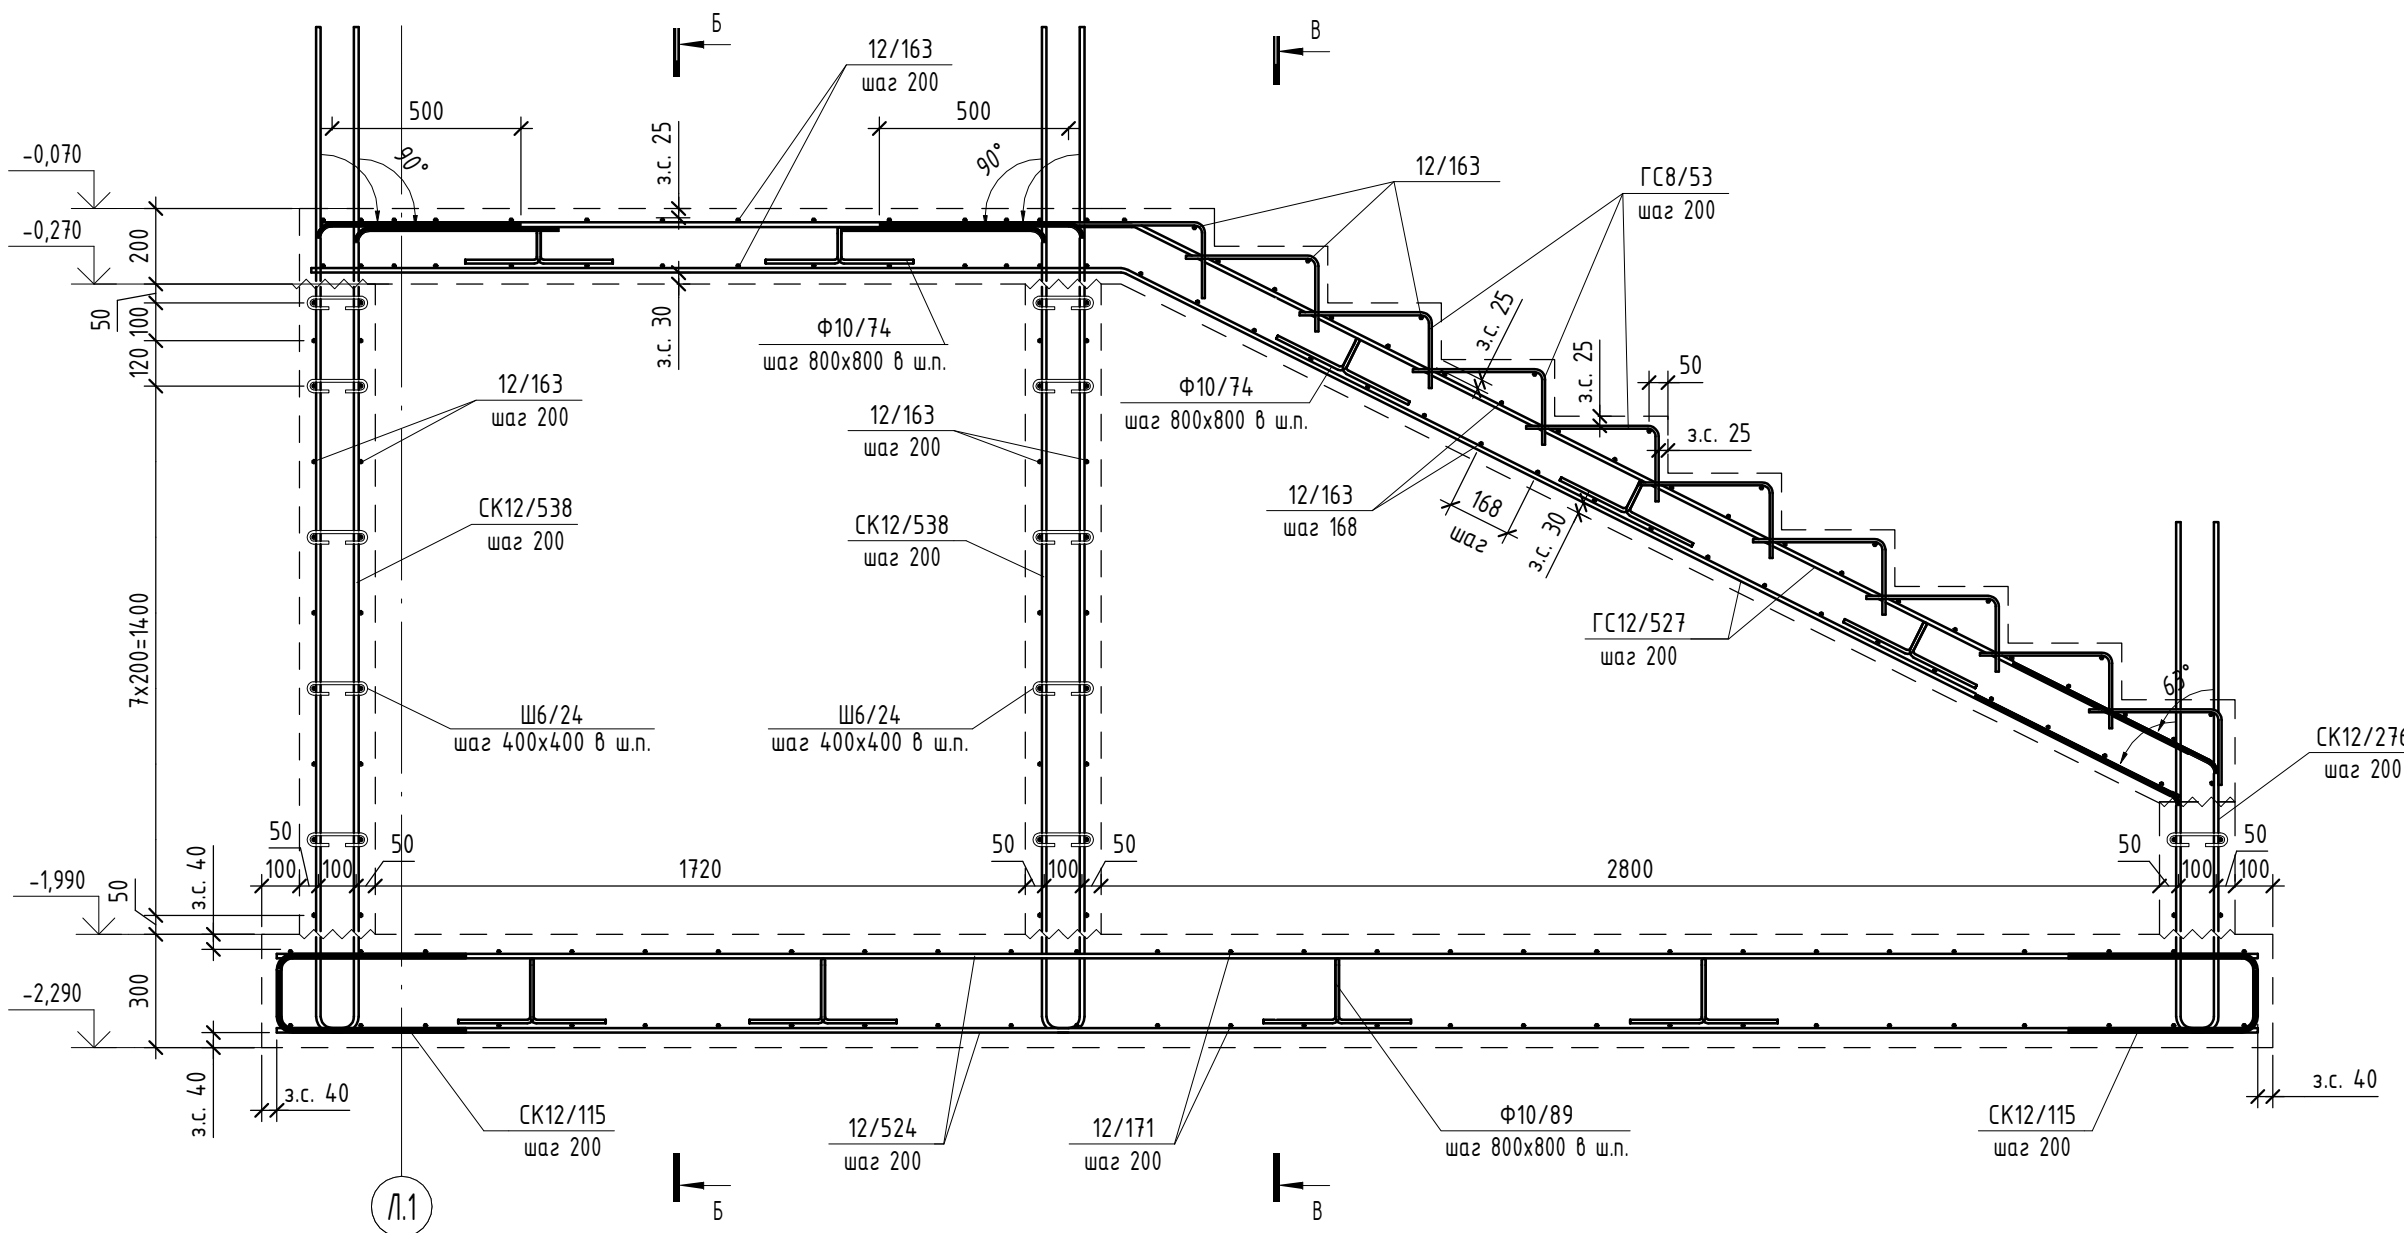


Схема расположения фиксаторов Ф10



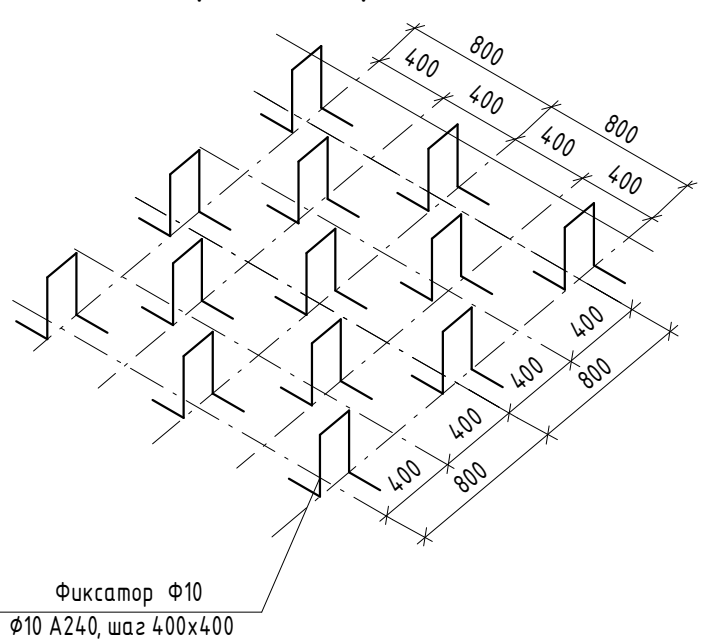


Схема расположения шпилек с шагом 400x400 в шахматном порядке

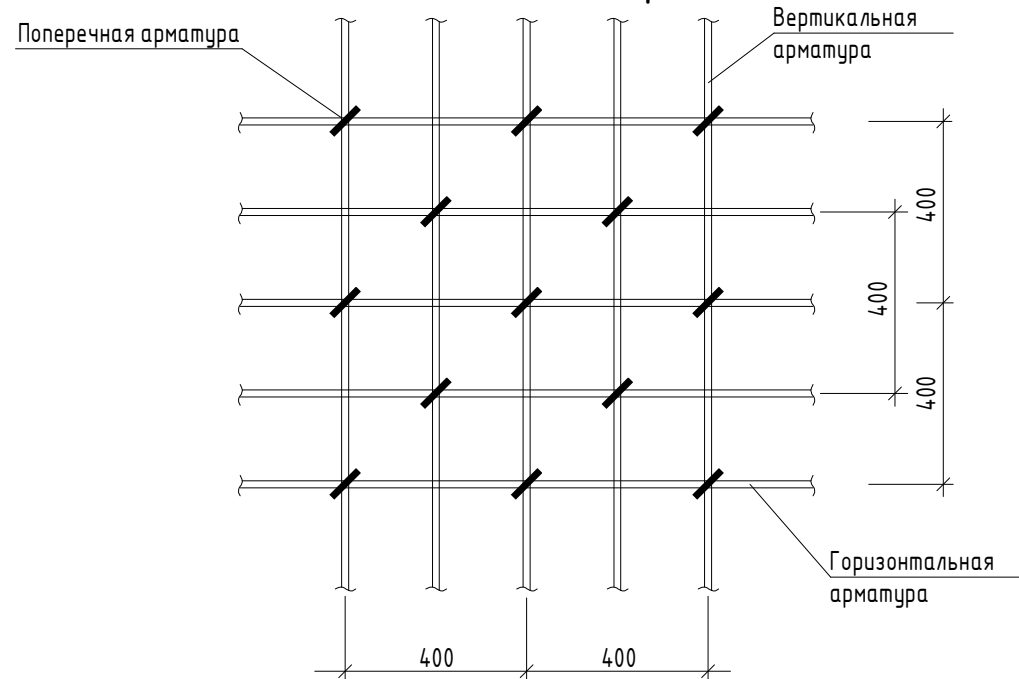


Б-Б

Армирование

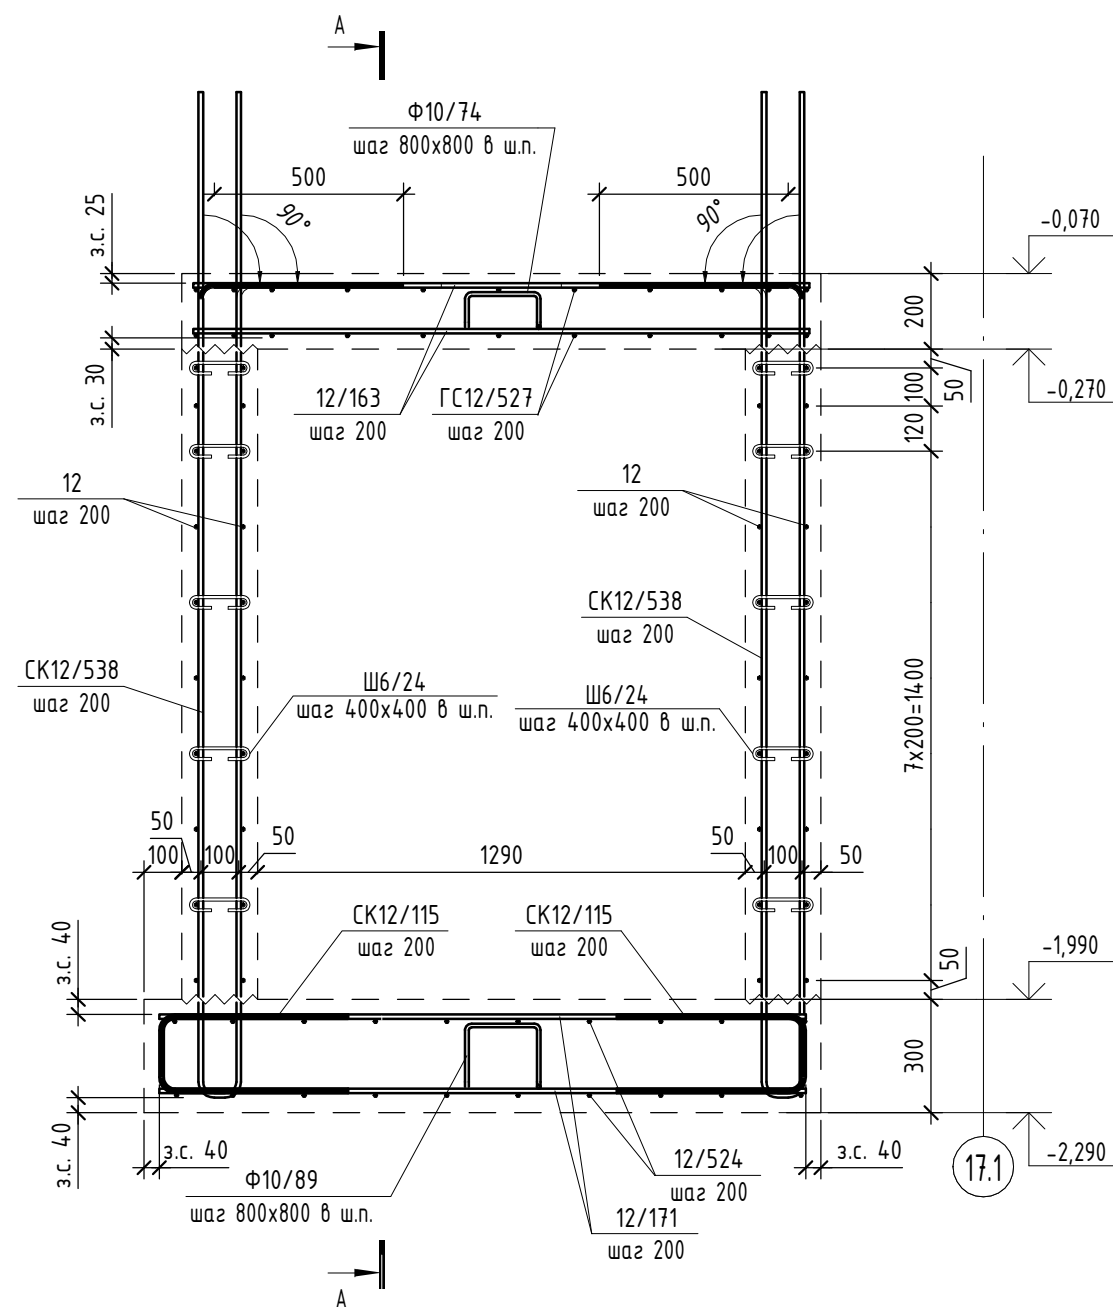

В-В

Армирование

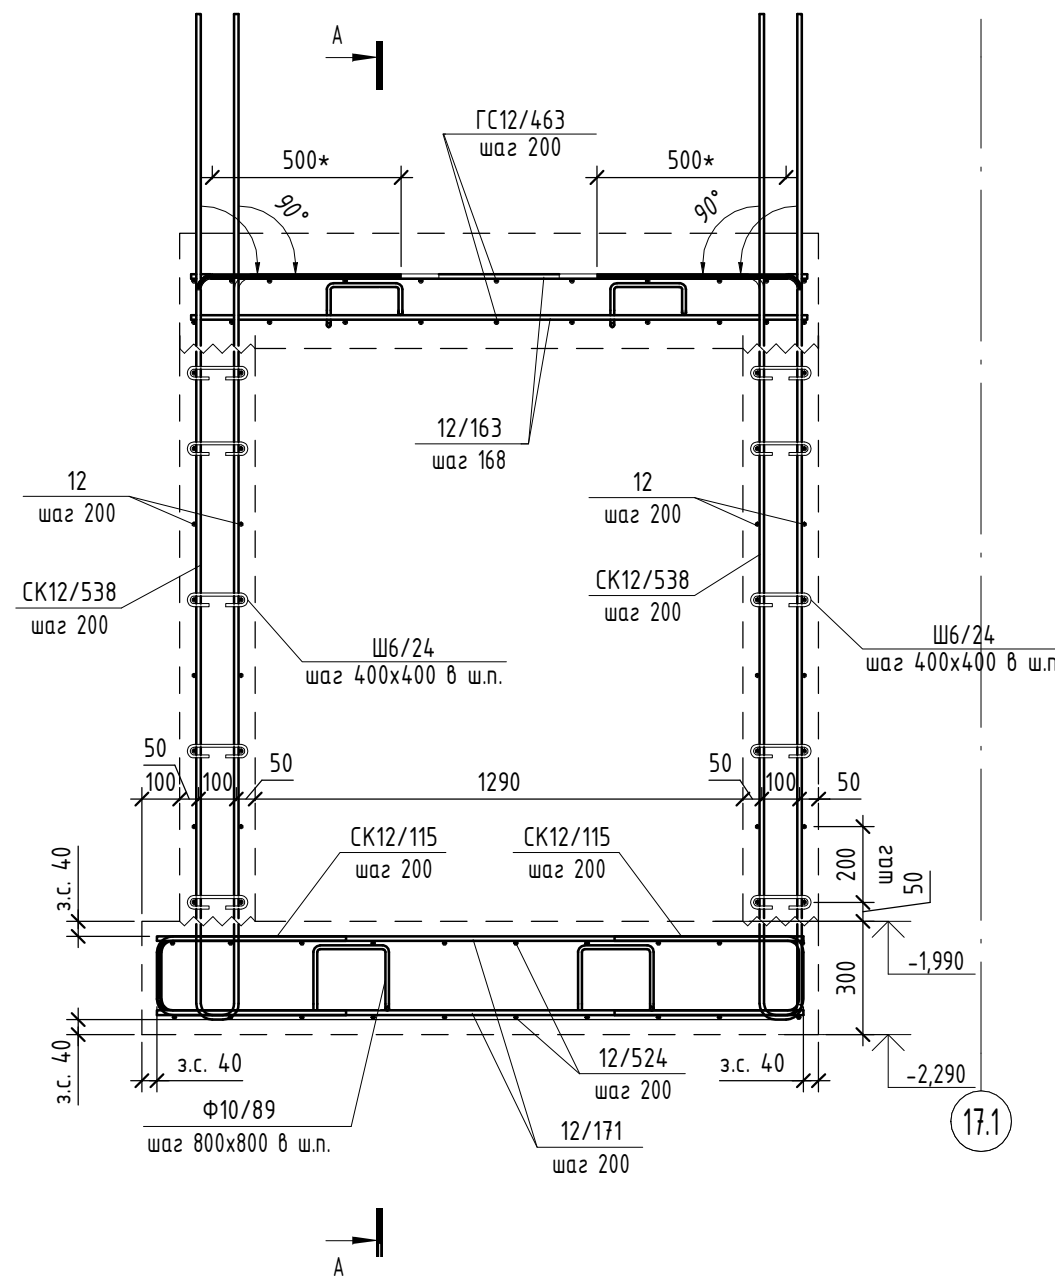

Ведомость расхода стали, кг

Марка конструкции	Изделия арматурные					
	Арматура класса					
	A240			A500C		
	Ø6	Ø10	Итого	Ø8	Ø12	Итого
Фундаментная плита	0	6,1	6,1	0	626,7	626,7
Стены	12,3	0	12,3	0	269,3	269,3
Площадка	0	2,3	2,3	0	40,6	40,6
Лестничные марши	0	3,7	3,7	18,9	173,9	192,8
Общий расход	12,3	12,1	24,3	18,9	1110,5	1129,4

Ведомость деталей

Поз.	Эскиз
ГС8/53	
ГС12/527	
СК12/538	
СК12/276	
СК12/115	

Ведомость деталей


Поз.	Эскиз
СК12/108	
Ш6/24	
Ф10/89	
Ф10/74	

Примечание:
1) Размеры скоб (СК) указаны по внутренним границам деталей.
2) Перед изготовлением гнутых элементов производителя работ выполнить пробный образец и сверить с фактическим армированием.

Спецификация элементов армирования входной группы


Поз.	Обозначение	Наименование	Кол.	Масса ед, кг	Примечание
		Наименование конструкции			
		Детали			
12	ГОСТ 34028-2016	Ø12 A500C L, поз.м	158	0,888	140,28
12/524	ГОСТ 34028-2016	Ø12 A500C L= 5240	20	4,654	93,06
12/171	ГОСТ 34028-2016	Ø12 A500C L= 1710	56	1,519	85,08
12/163	ГОСТ 34028-2016	Ø12 A500C L= 1630	121	1,448	175,26
ГС8/53	ГОСТ 34028-2016	Ø8 A500C L= 530	90	0,21	18,90
ГС12/527	ГОСТ 34028-2016	Ø12 A500C L= 5270	22	4,68	102,96
СК12/538	ГОСТ 34028-2016	Ø12 A500C L= 5375	72	4,773	343,66
СК12/276	ГОСТ 34028-2016	Ø12 A500C L= 2755	11	2,447	26,91
СК12/115	ГОСТ 34028-2016	Ø12 A500C L= 1155	76	1,026	77,98
СК12/108	ГОСТ 34028-2016	Ø12 A500C L= 1080	68	0,96	65,28
Ш6/24	ГОСТ 34028-2016	Ø6 A240 L= 240	227	0,054	12,26
Ф10/89	ГОСТ 34028-2016	Ø10 A240 L= 895	11	0,553	6,09
Ф10/74	ГОСТ 34028-2016	Ø10 A240 L= 745	13	0,46	5,98

Схема стыка арматурных стержней (перепуск стержней без сварки)

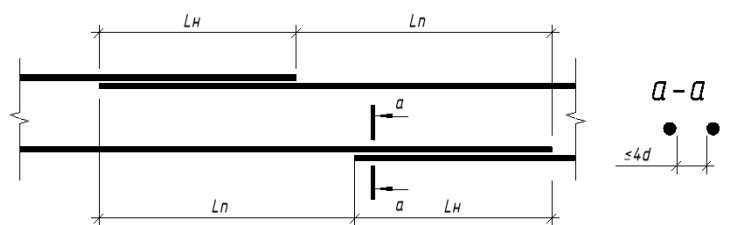

Тип арматуры	Длина нахлеста Ln	Длина анкеровки	Смещение нахлеста Ln, не менее
Ф12 A500C	595	500	800

Диаметр гибки арматуры

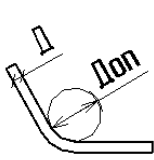

Диаметр стержня, мм	Минимальный диаметр оправки, мм
A240	
Ø6	15
Ø10	25
A500C	
Ø8	40
Ø12	60

- Общие данные см. лист 1
- Опубличные чертежи см. лист 2
- * - арматуру обрезать по месту

Условные обозначения:
з.с. - защитный слой бетона
~~~~~ - шаг бетонирования

|          |               |      |        |                      |       |   |   |      |        |  |
|----------|---------------|------|--------|----------------------|-------|---|---|------|--------|--|
|          |               |      |        |                      |       | 16-25/Г-Р-КР1   |   |      |        |  |
|          |               |      |        |                      |       | Капитальный ремонт объекта "ГБОУ "Школа №429 "Сокольная гора", расположенного по адресу: г.Москва, ул.Сокольной Горы 5-ая, в.14 |   |      |        |  |
| Изм.     | Кол.уч.       | Лист | № док. | Подпись              | Дата  | Конструктивные решения   | Стадия                                                                                              | Лист | Листов |  |
| Разраб.  | Шевченко      | 1    |        | <i>Шевченко</i>      | 07.26 |   | Р                                                                                                   | 11   |        |  |
| Проверил | Дидж          | 1    |        | <i>Дидж</i>          | 07.26 |   |   |      |        |  |
| Н.контр. | Губарева Е.В. | 1    |        | <i>Губарева Е.В.</i> | 07.26 | Схема армирования входной группы в/о 17.1/Л.1                                                                                   |  <b>АЗУРИТ</b> |      |        |  |
| ГИП      | Маркова       | 1    |        | <i>Маркова</i>       | 07.26 |   |   |      |        |  |