

Схема расположения форшахты в/о 9-А1



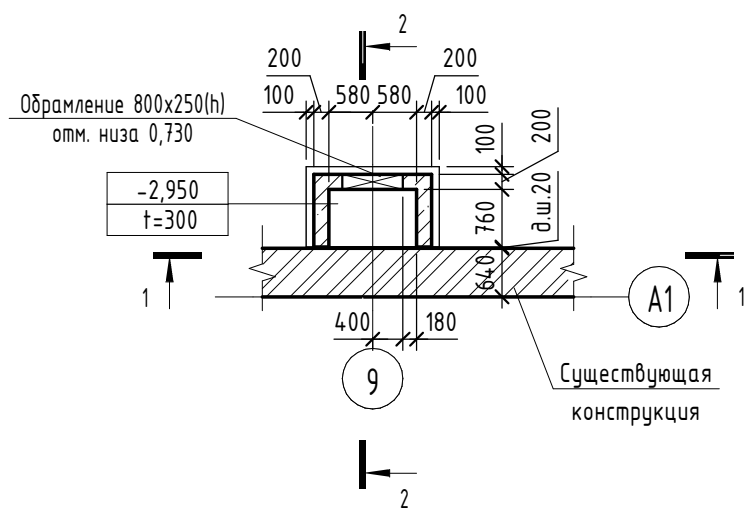



Схема расположения арматурных выпусков вундаментной плиты в/о 9-А1

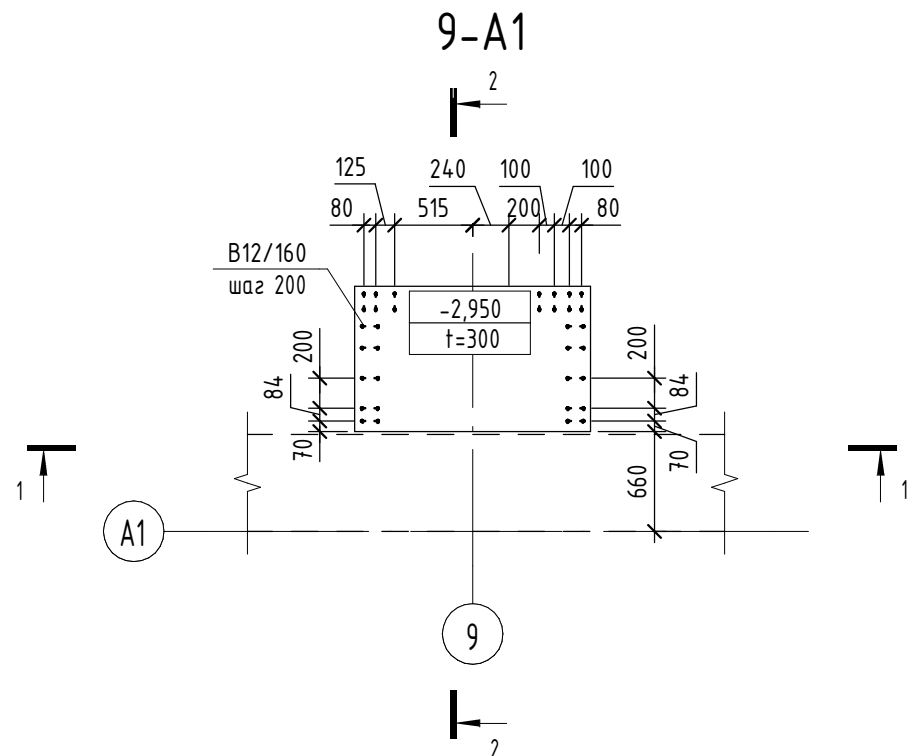

1-1 Армирование

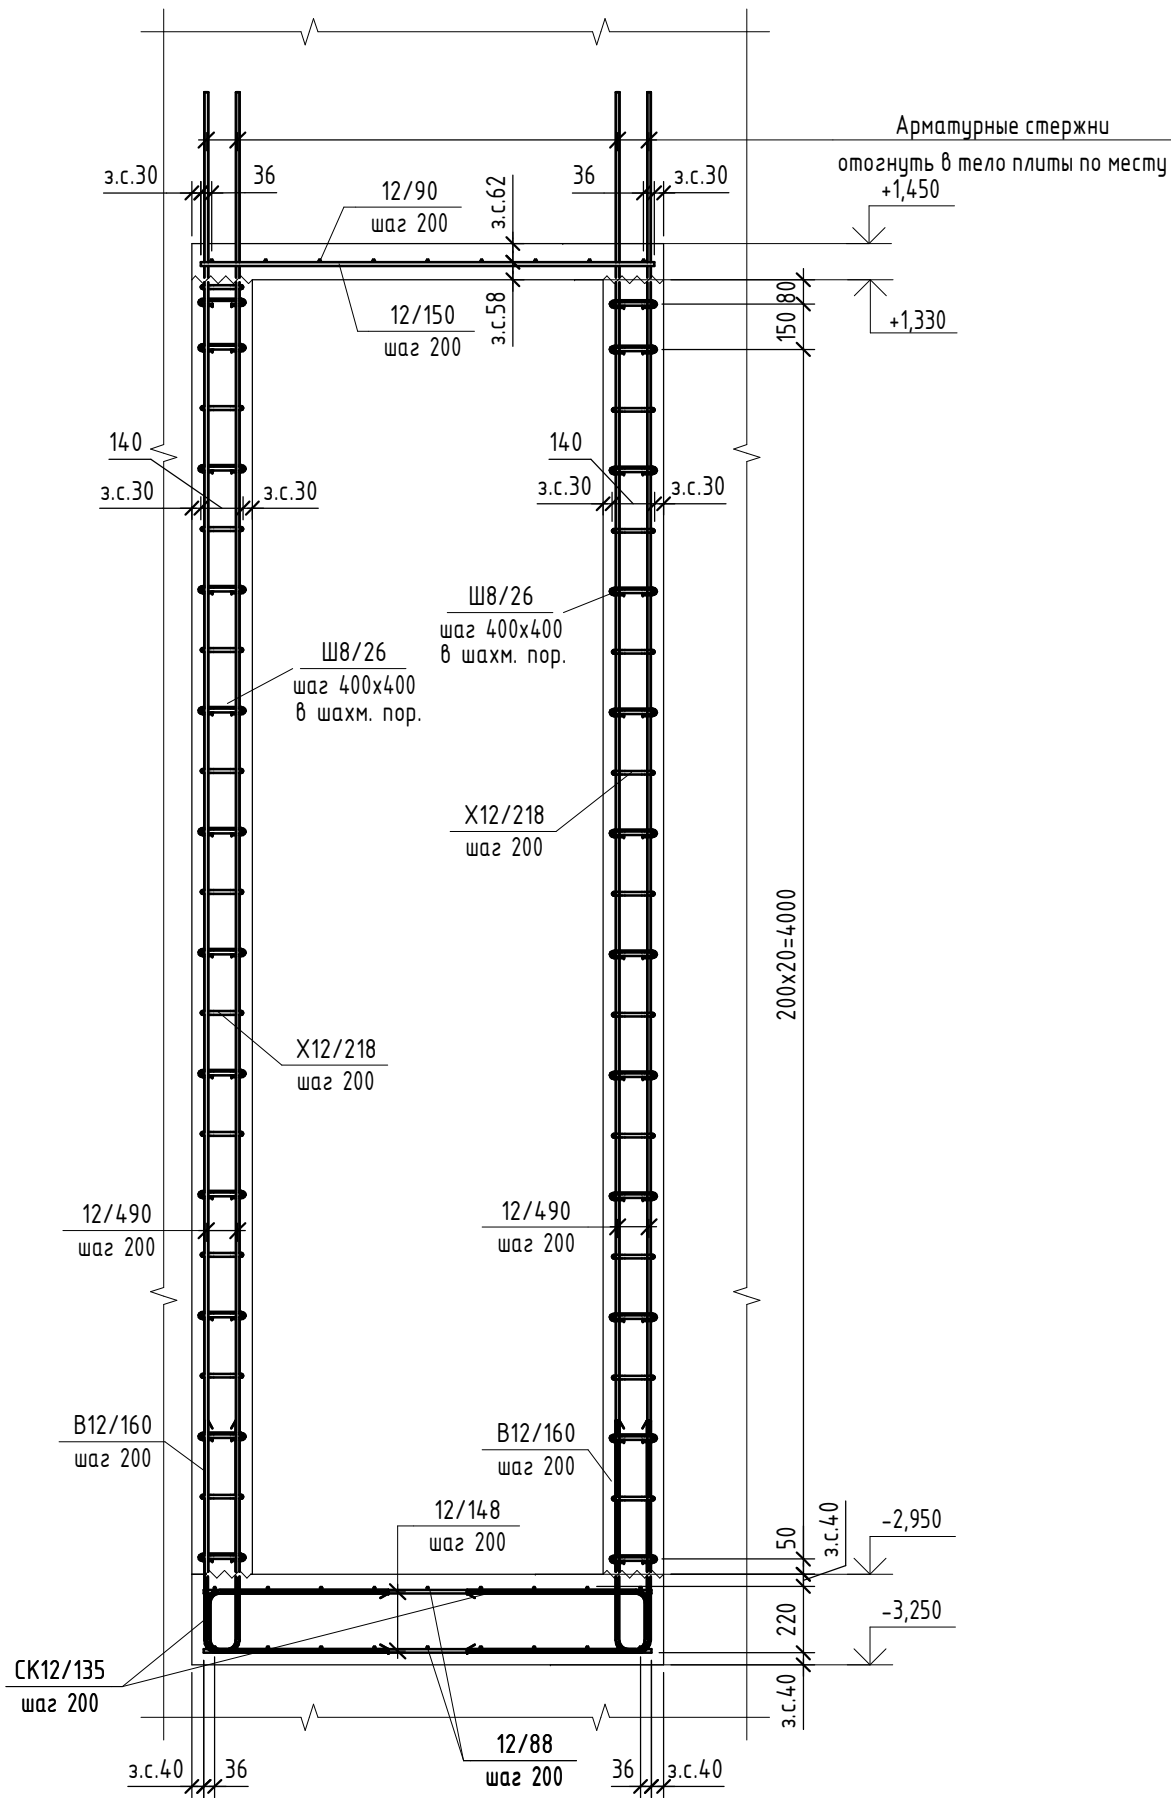

2-2 Армирование

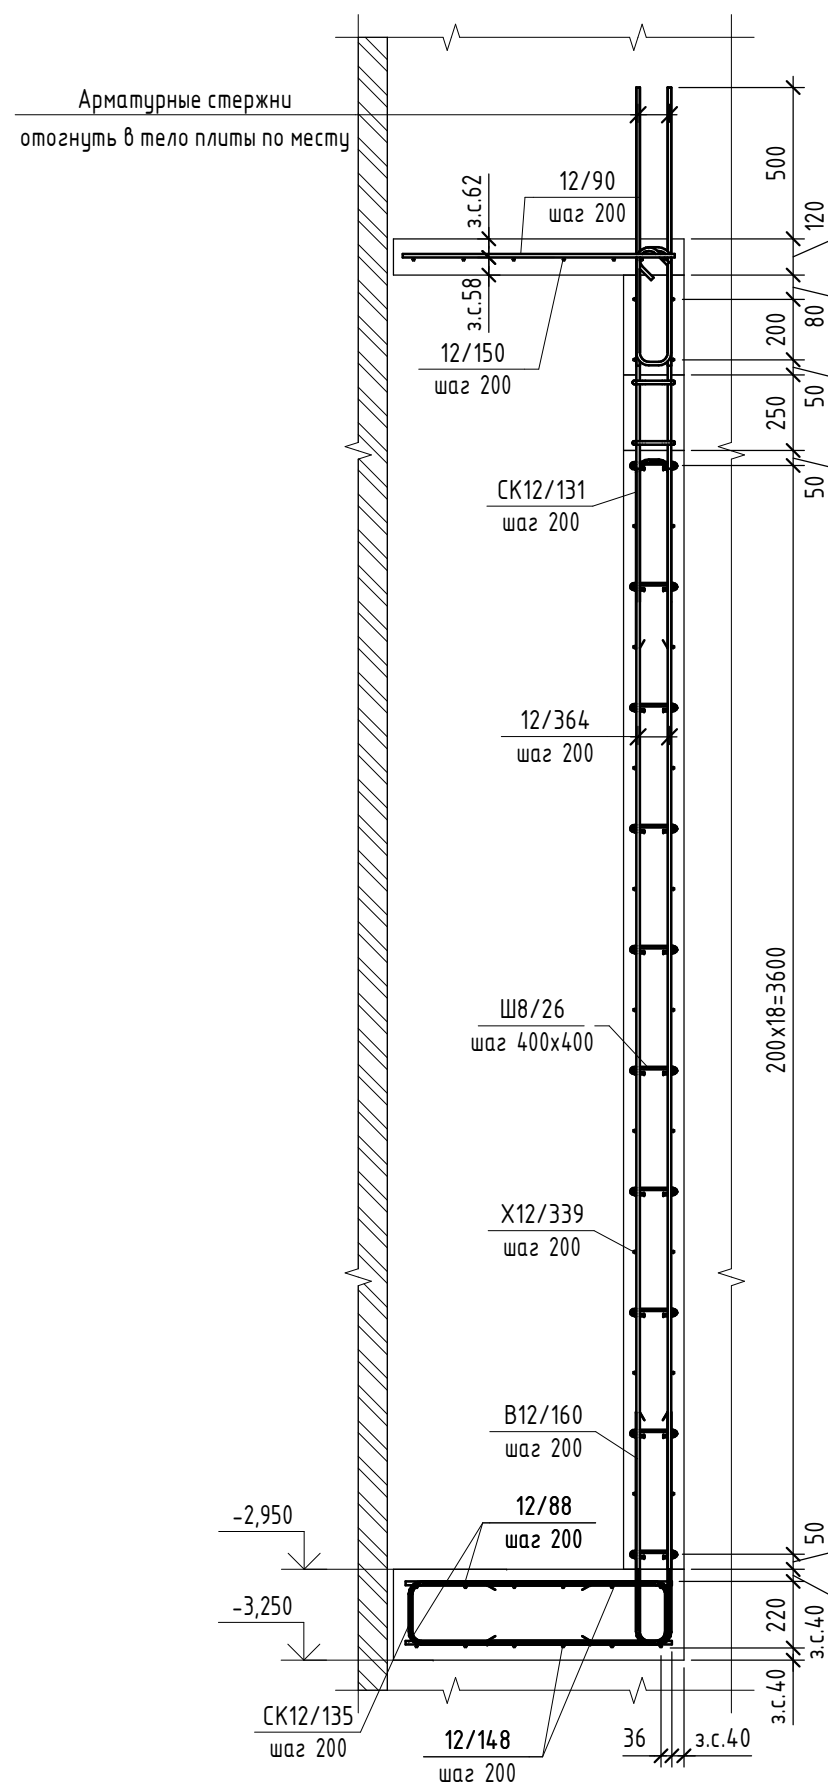

1-1 Опалубка

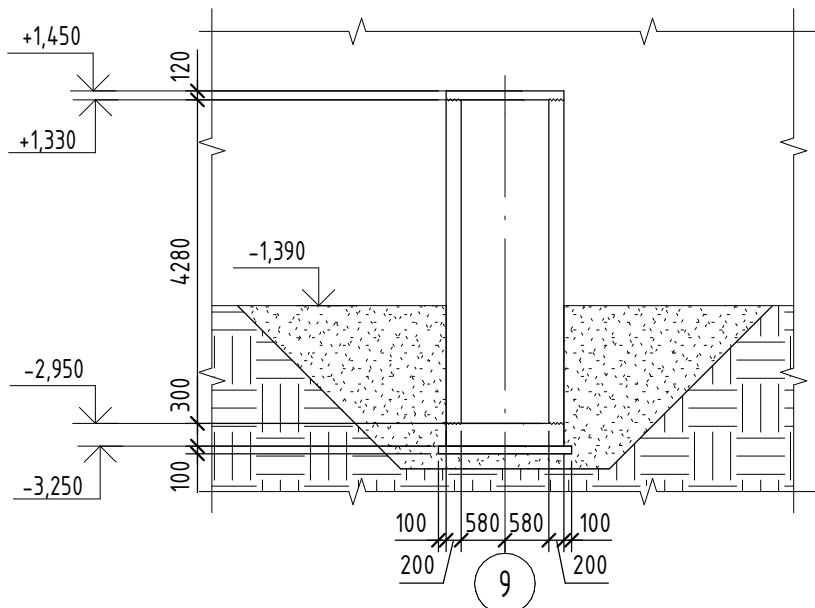


Схема обрамления отверстия в стене



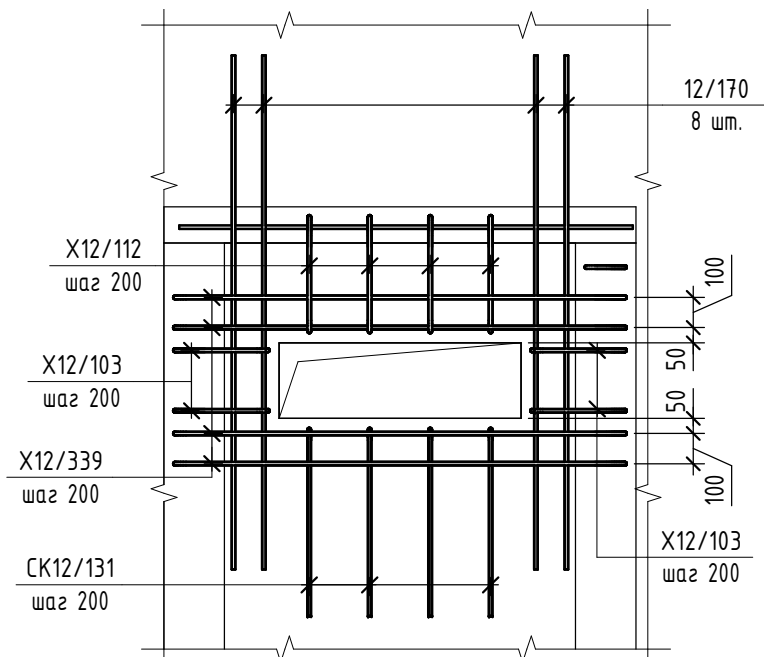



Схема расположения шпилек с шагом 400х400 в шахматном порядке

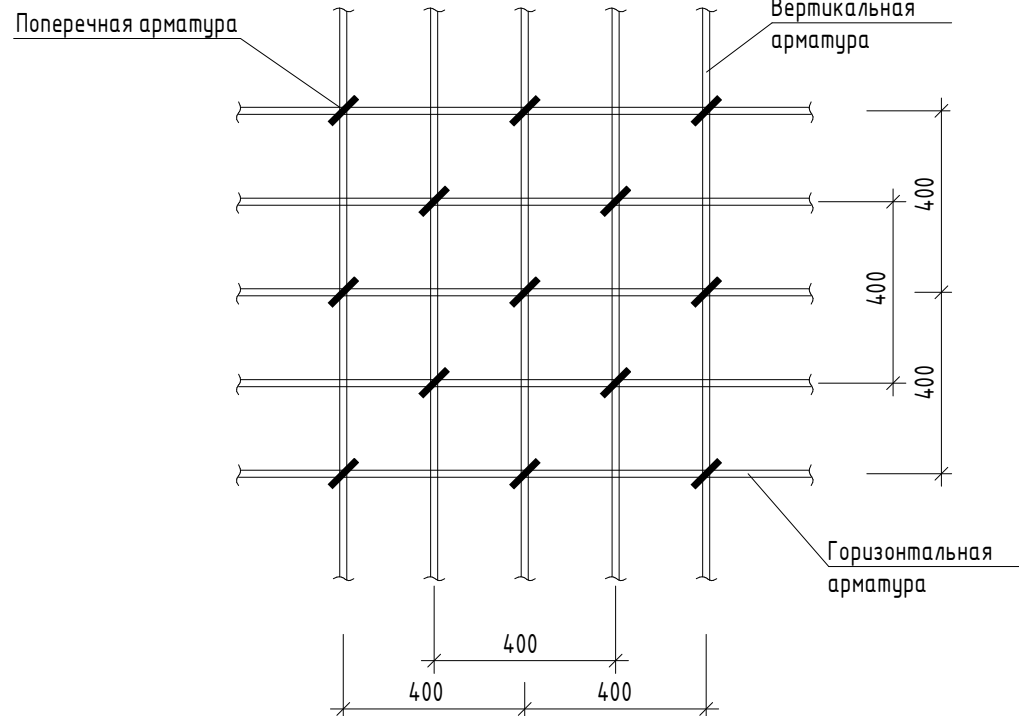

2-2 Опалубка

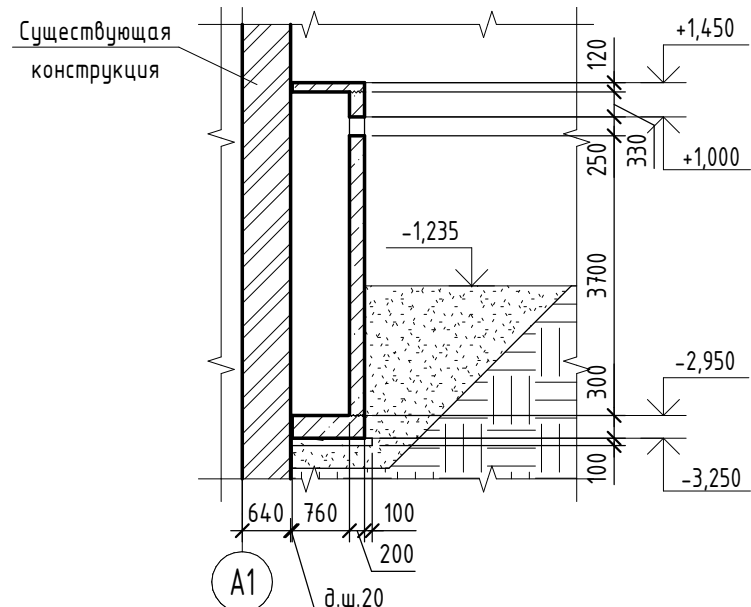

Типовой Г-образный узел расположения арматурных стержней

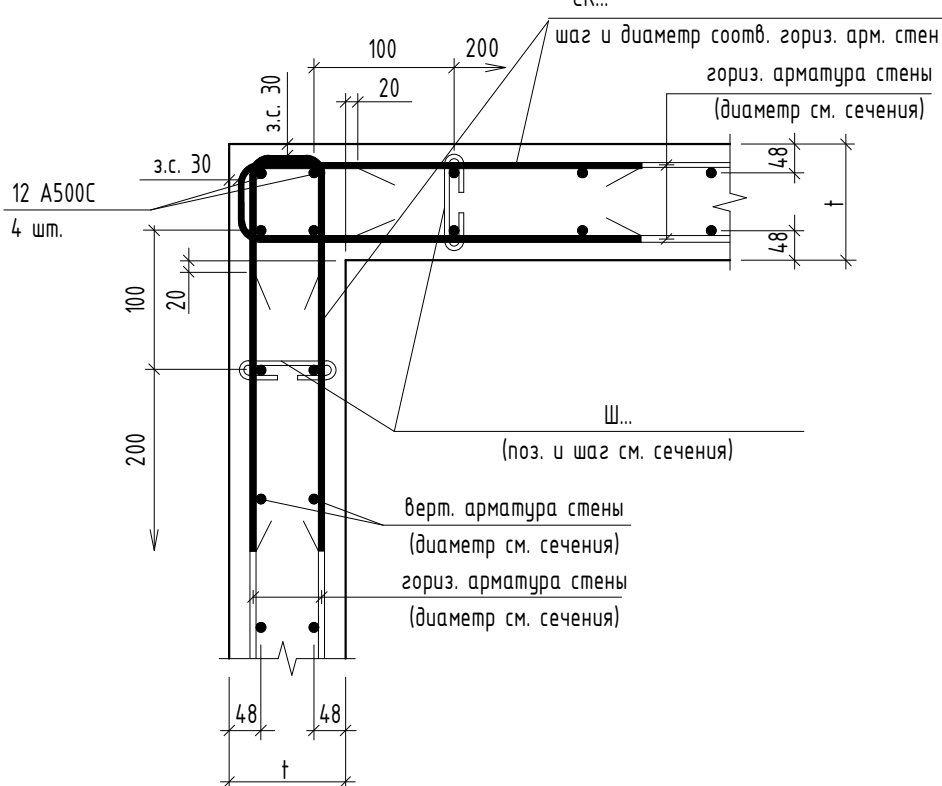

Типовой торцевой узел расположения арматурных стержней


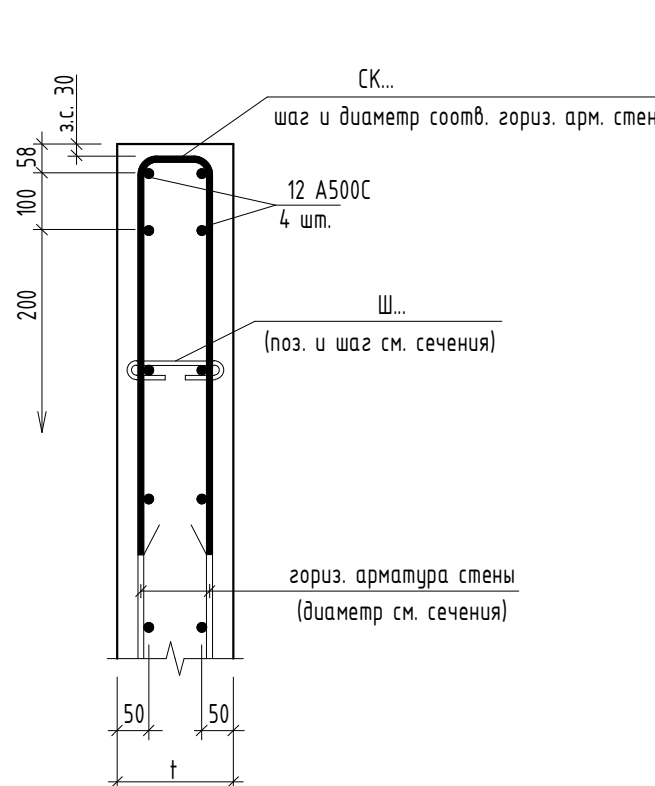



Схема стыка арматурных стержней (перепуск стержней без сварки)

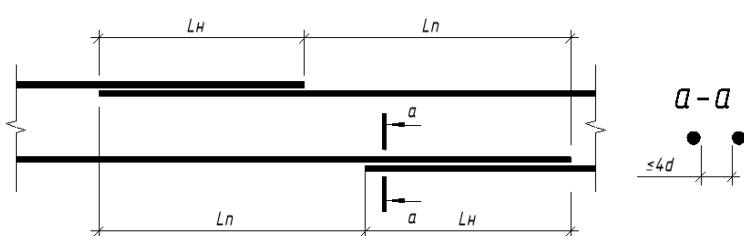

Тип арматуры	Длина нахлеста Lн	Длина анкеровки	Смещение нахлеста Lп, не менее	Позиция
Ф12 А500С	595	500	800	

Условные обозначения:
з.с. - защитный слой бетона
~~~~~ - шов бетонирования  
-0,070 - Отметка верха и  
+200 - толщина плиты перекрытия

Маркировка позиций арматуры

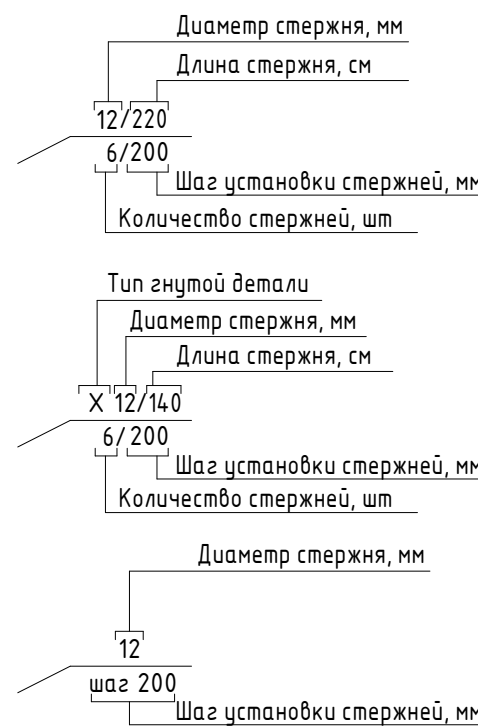

- Архитектурные планы и разрезы здания см. чертежи марки АР.
- Фактическое расположение существующих конструкций уточнять по месту.
- Общие указания см. лист 1.
- В основании фундаментов принят песок средней крупности с послойным уплотнением с коэффициентом уплотнения  $k=0.95$ .
- В случае обнаружения ниже подошвы проектируемого фундамента слабых грунтов, насыпи или грунтовых вод обратиться к проектной организации для принятия проектных решений.
- Для доковых поверхностей фундаментной плиты и стен соприкасающихся с грунтом, выполнить гидроизоляция 2 слоями горячего битума.
- Обратную засыпку пазух котлована выполнить песком средней крупности с послойным уплотнением с коэффициентом уплотнения  $k=0.95$ .
- Основное горизонтальное армирование фундаментной плиты выполняется отдельными стержнями Ф12А500С, крестообразные пере- сечения арматурных стержней вязать отожженной вязальной проволокой  $d10$  мм в соответствии с требованиями приложения Ж ГОСТ 10922-2012, п. Ж5. Для фиксации нижних рядов арматуры и обеспечения защитного слоя применять неизвлекаемые фиксаторы из бетона или пластика .