




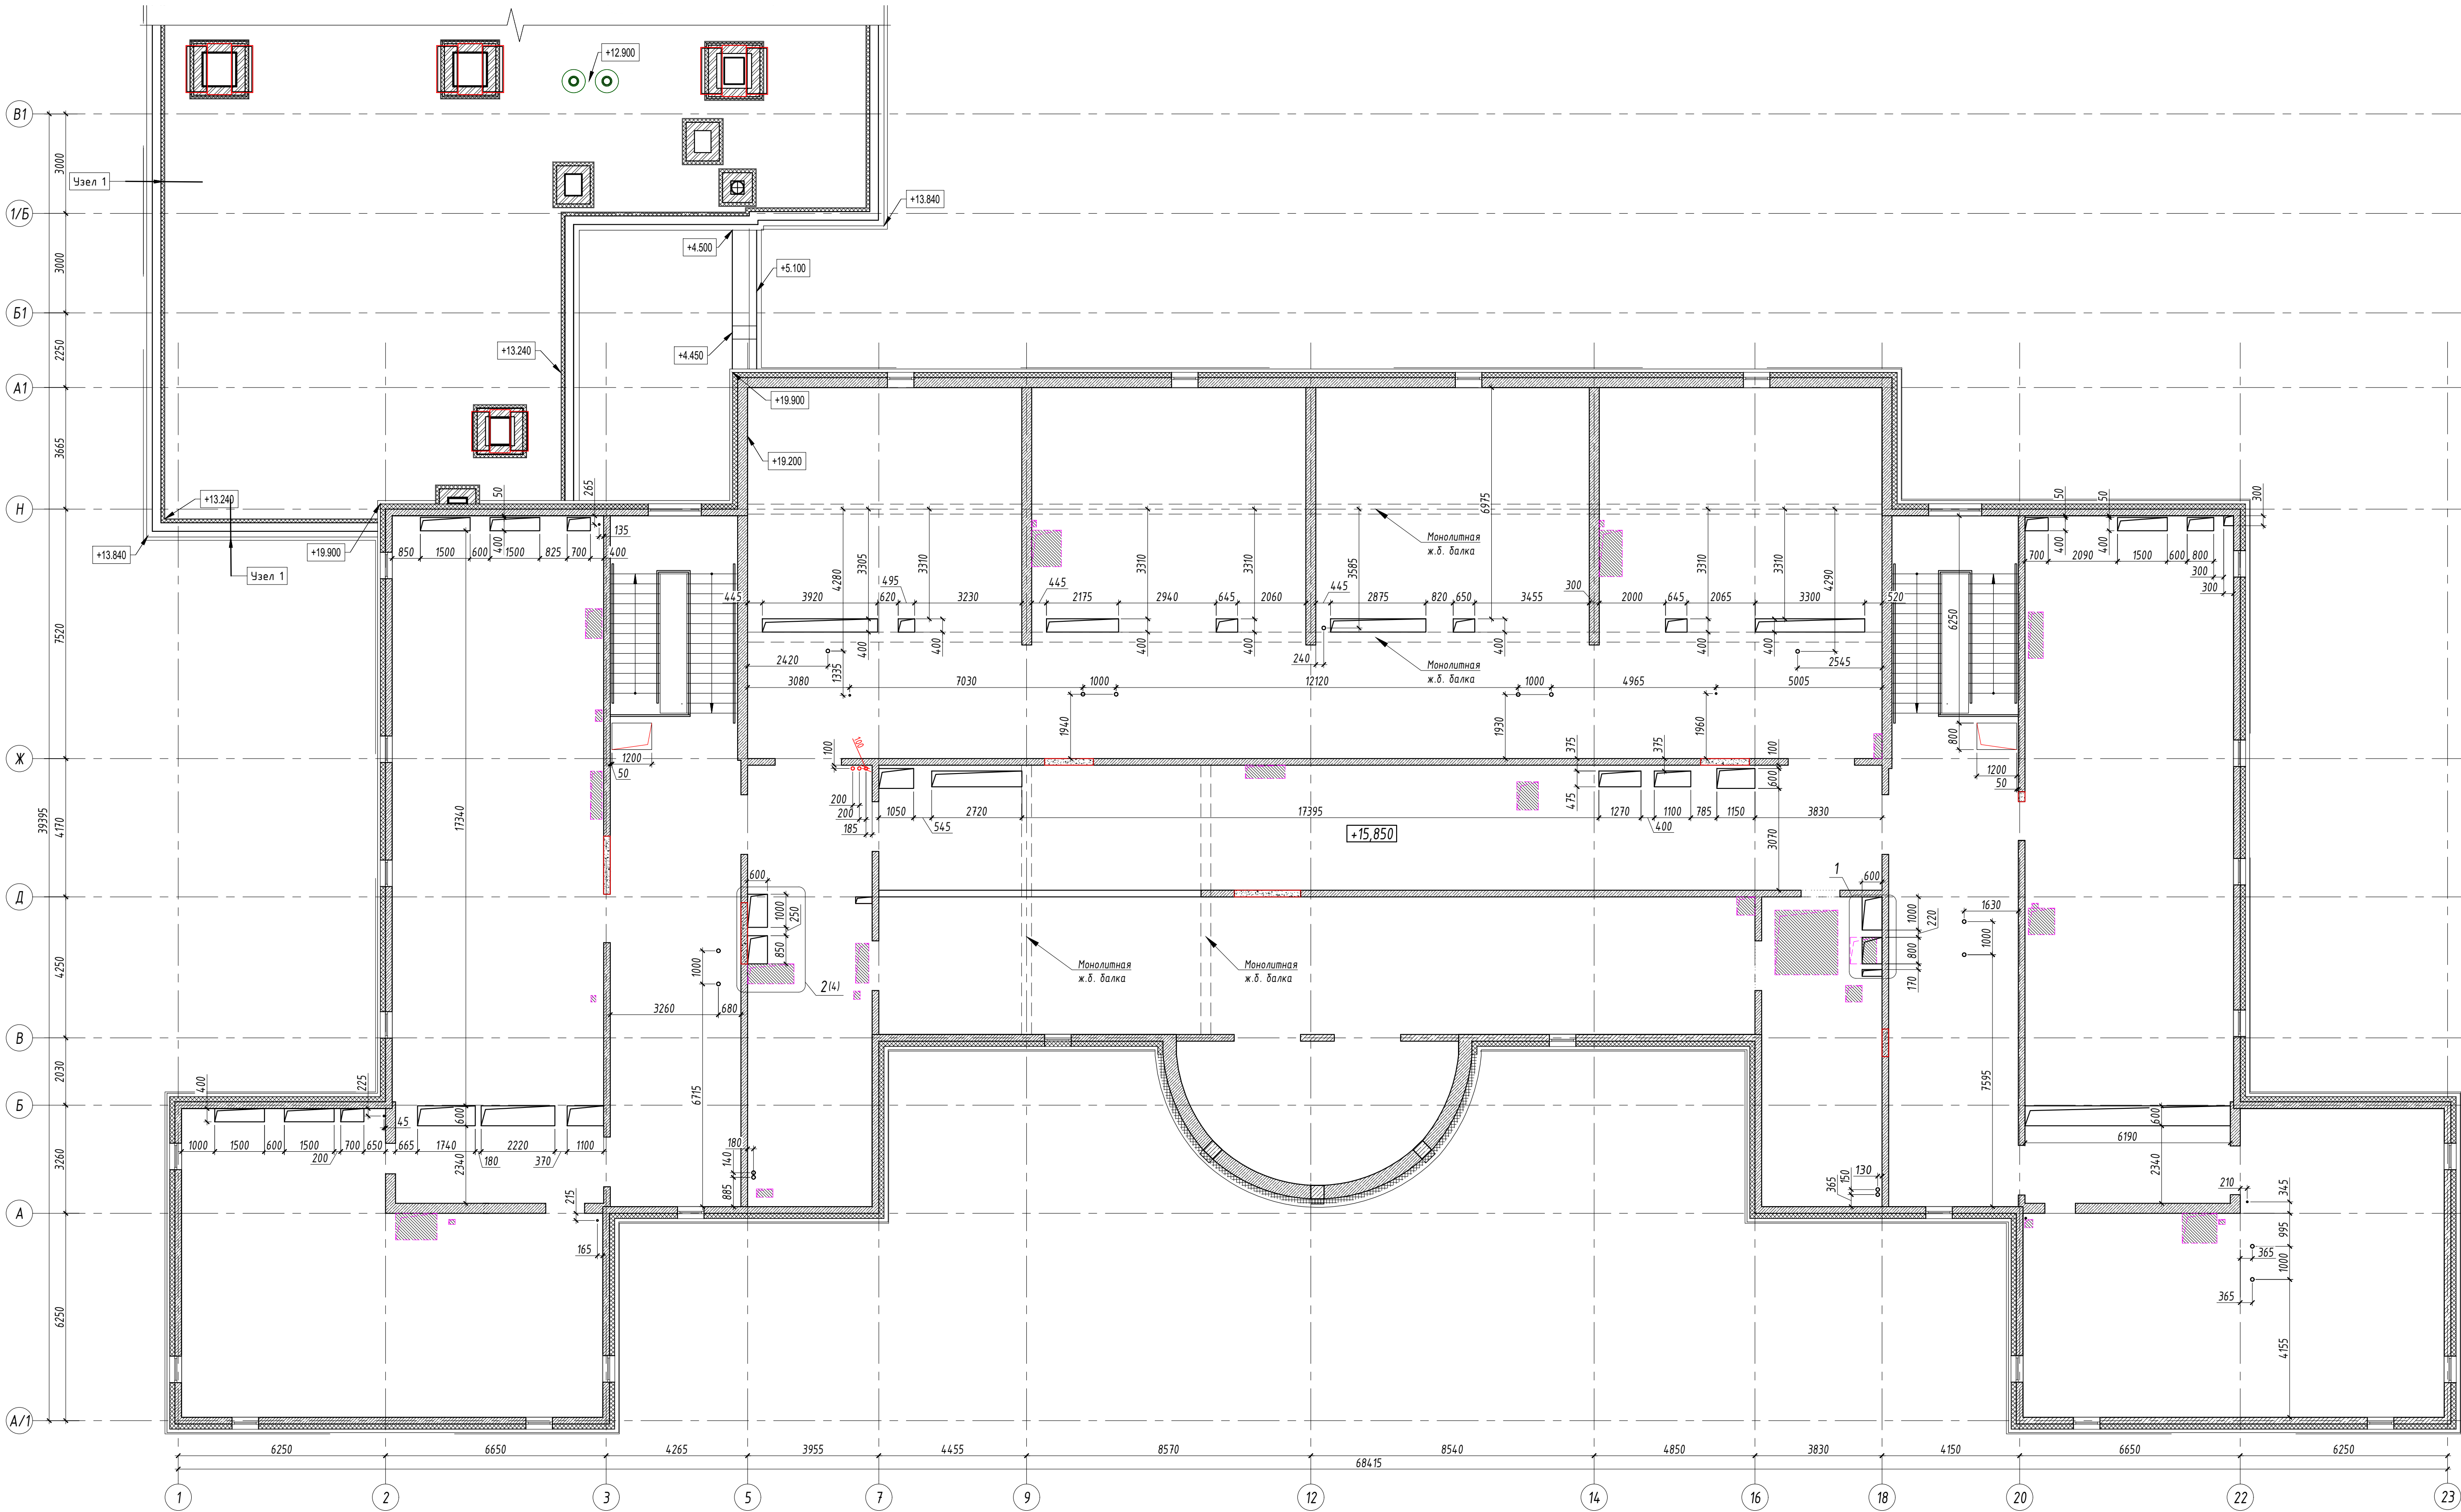


Фрагмент 1 в осях Д/18 на отм. +15,850

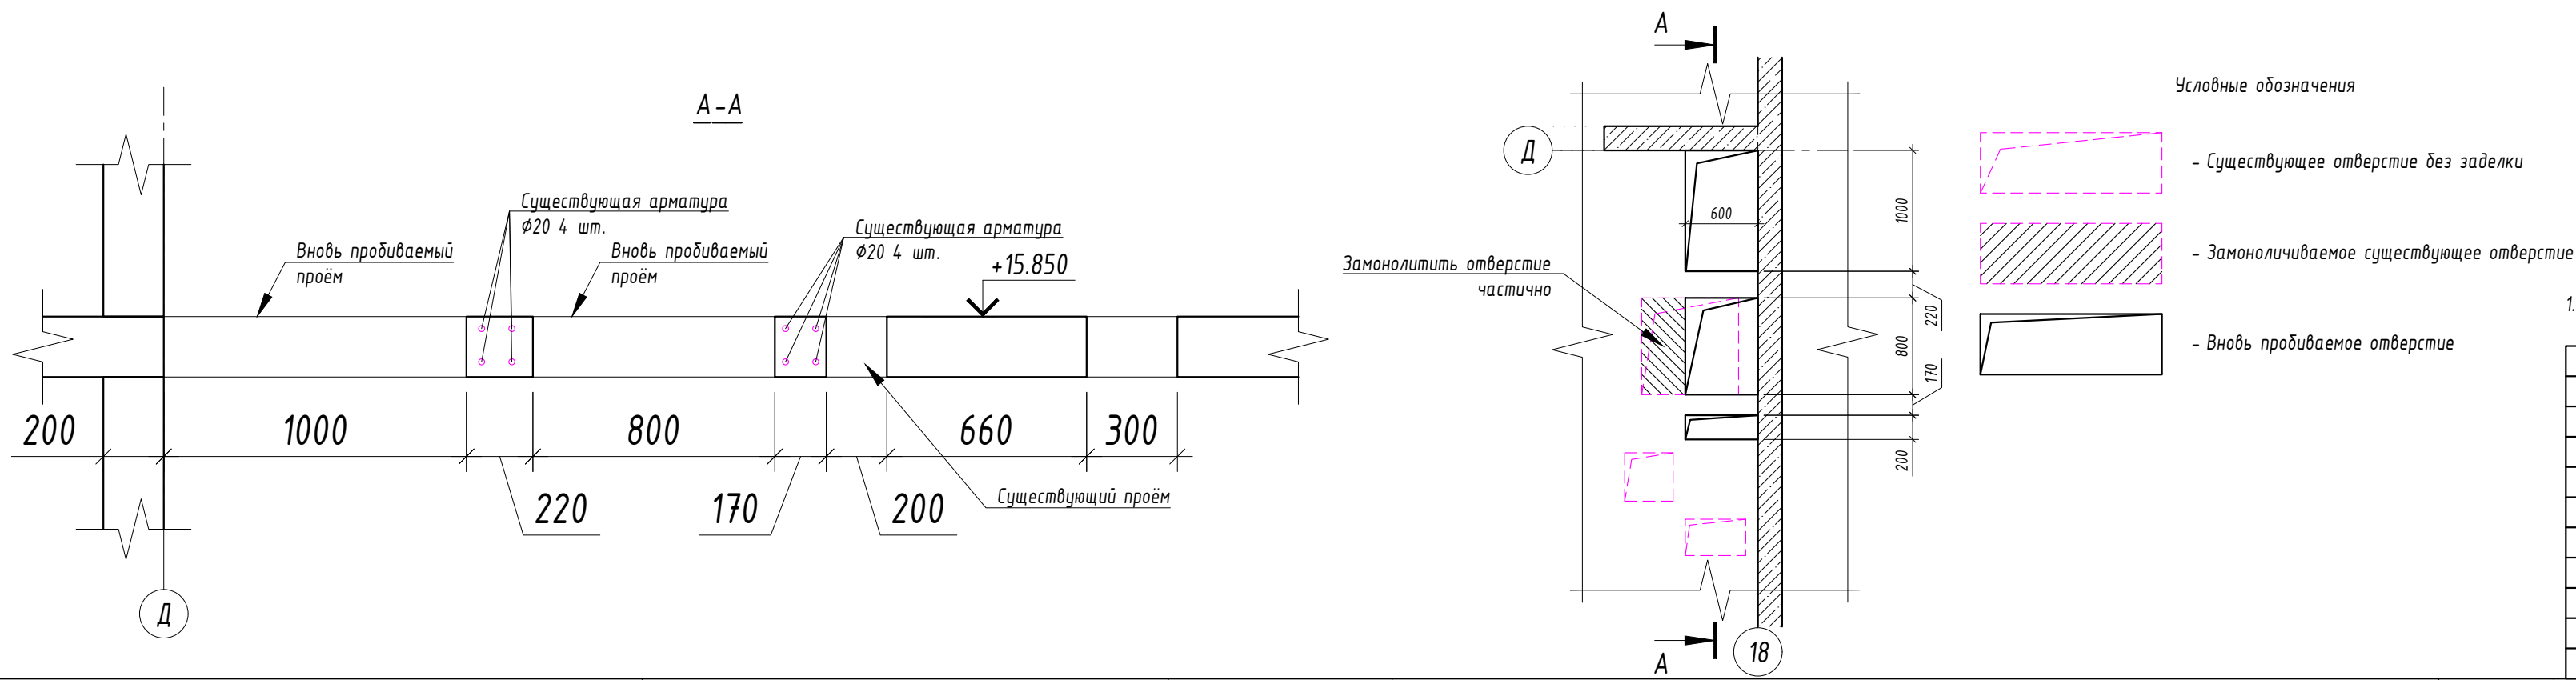

|           |           |      |        |         |            |   |        |      |
|-----------|-----------|------|--------|---------|------------|---|--------|------|
|           |           |      |        |         |            | 16-25/Г-Р-КР5   |        |      |
|           |           |      |        |         |            | Капитальный ремонт объекта "ГБОУ Школа №429 "Соколовая гора", расположенного по адресу: г. Москва, ул. Соколовой горы 5-я, д. 14. |        |      |
| Изм.      | Кол. изм. | Лист | № док. | Подпись | Дата       | Конструктивные решения   | Стадия | Лист |
| Разраб.   | Вариантов |      |        |         | 01.09.2026 |   | Р      | 2    |
| Проверил  | Прудников |      |        |         | 01.09.2026 |   |        |      |
|           |           |      |        |         |            | Схема расположения отверстий на отм. +15,850                                                                                      |        |      |
| Н. контр. | Гударева  |      |        |         | 01.09.2026 | АЗУРИТ   |        |      |
| ГИП       | Маркова   |      |        |         | 01.09.2026 |   |        |      |

|              |          |     |    |
|--------------|----------|-----|----|
| Составлено   | ВК       | ЗМ  | СС |
| Прош. и дата | Взм. и № | ГАП | ОВ |
| Имя и подп.  |          |     |    |

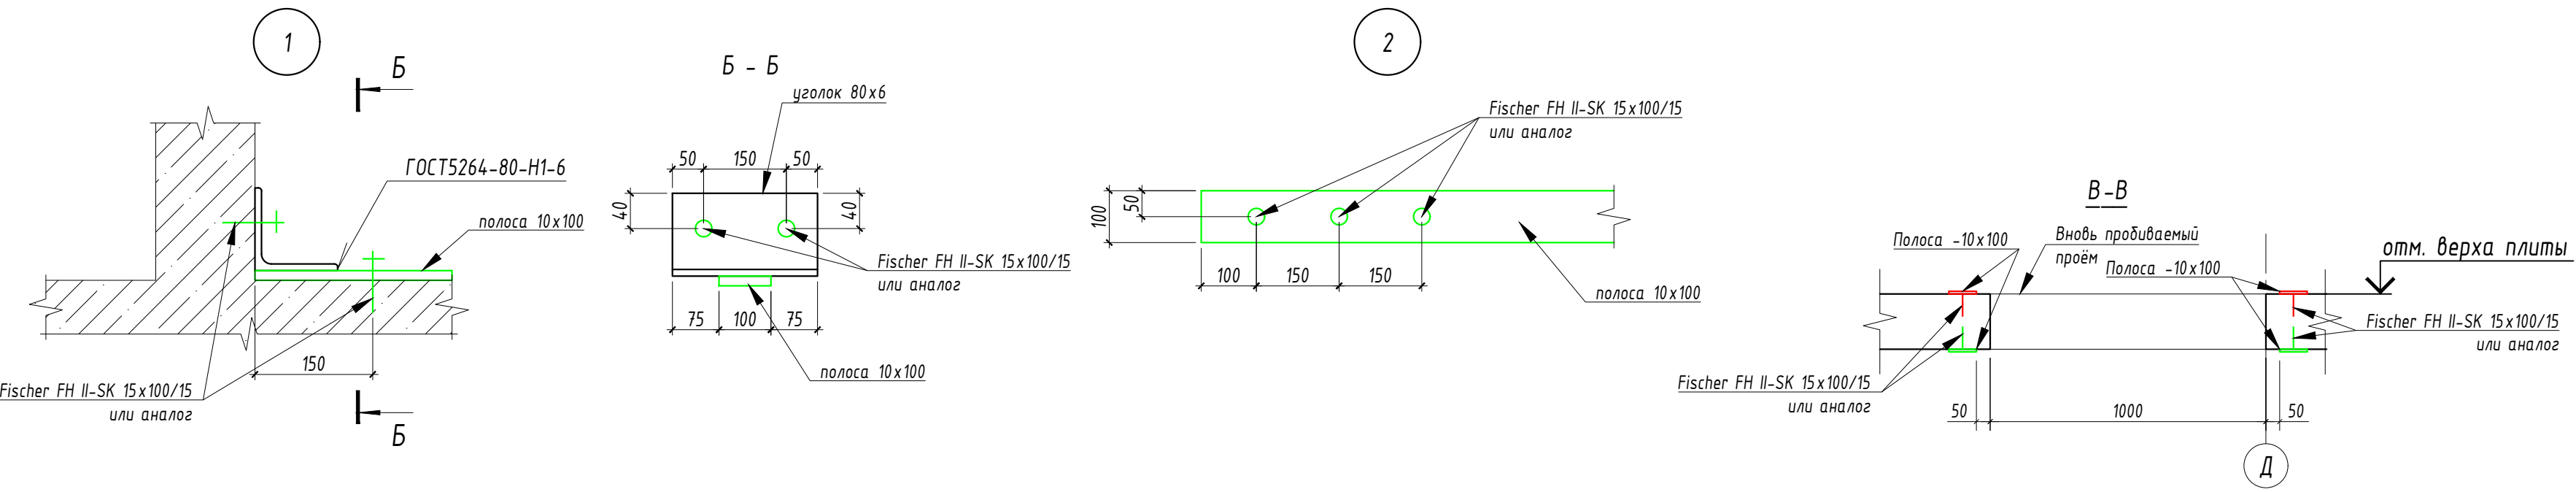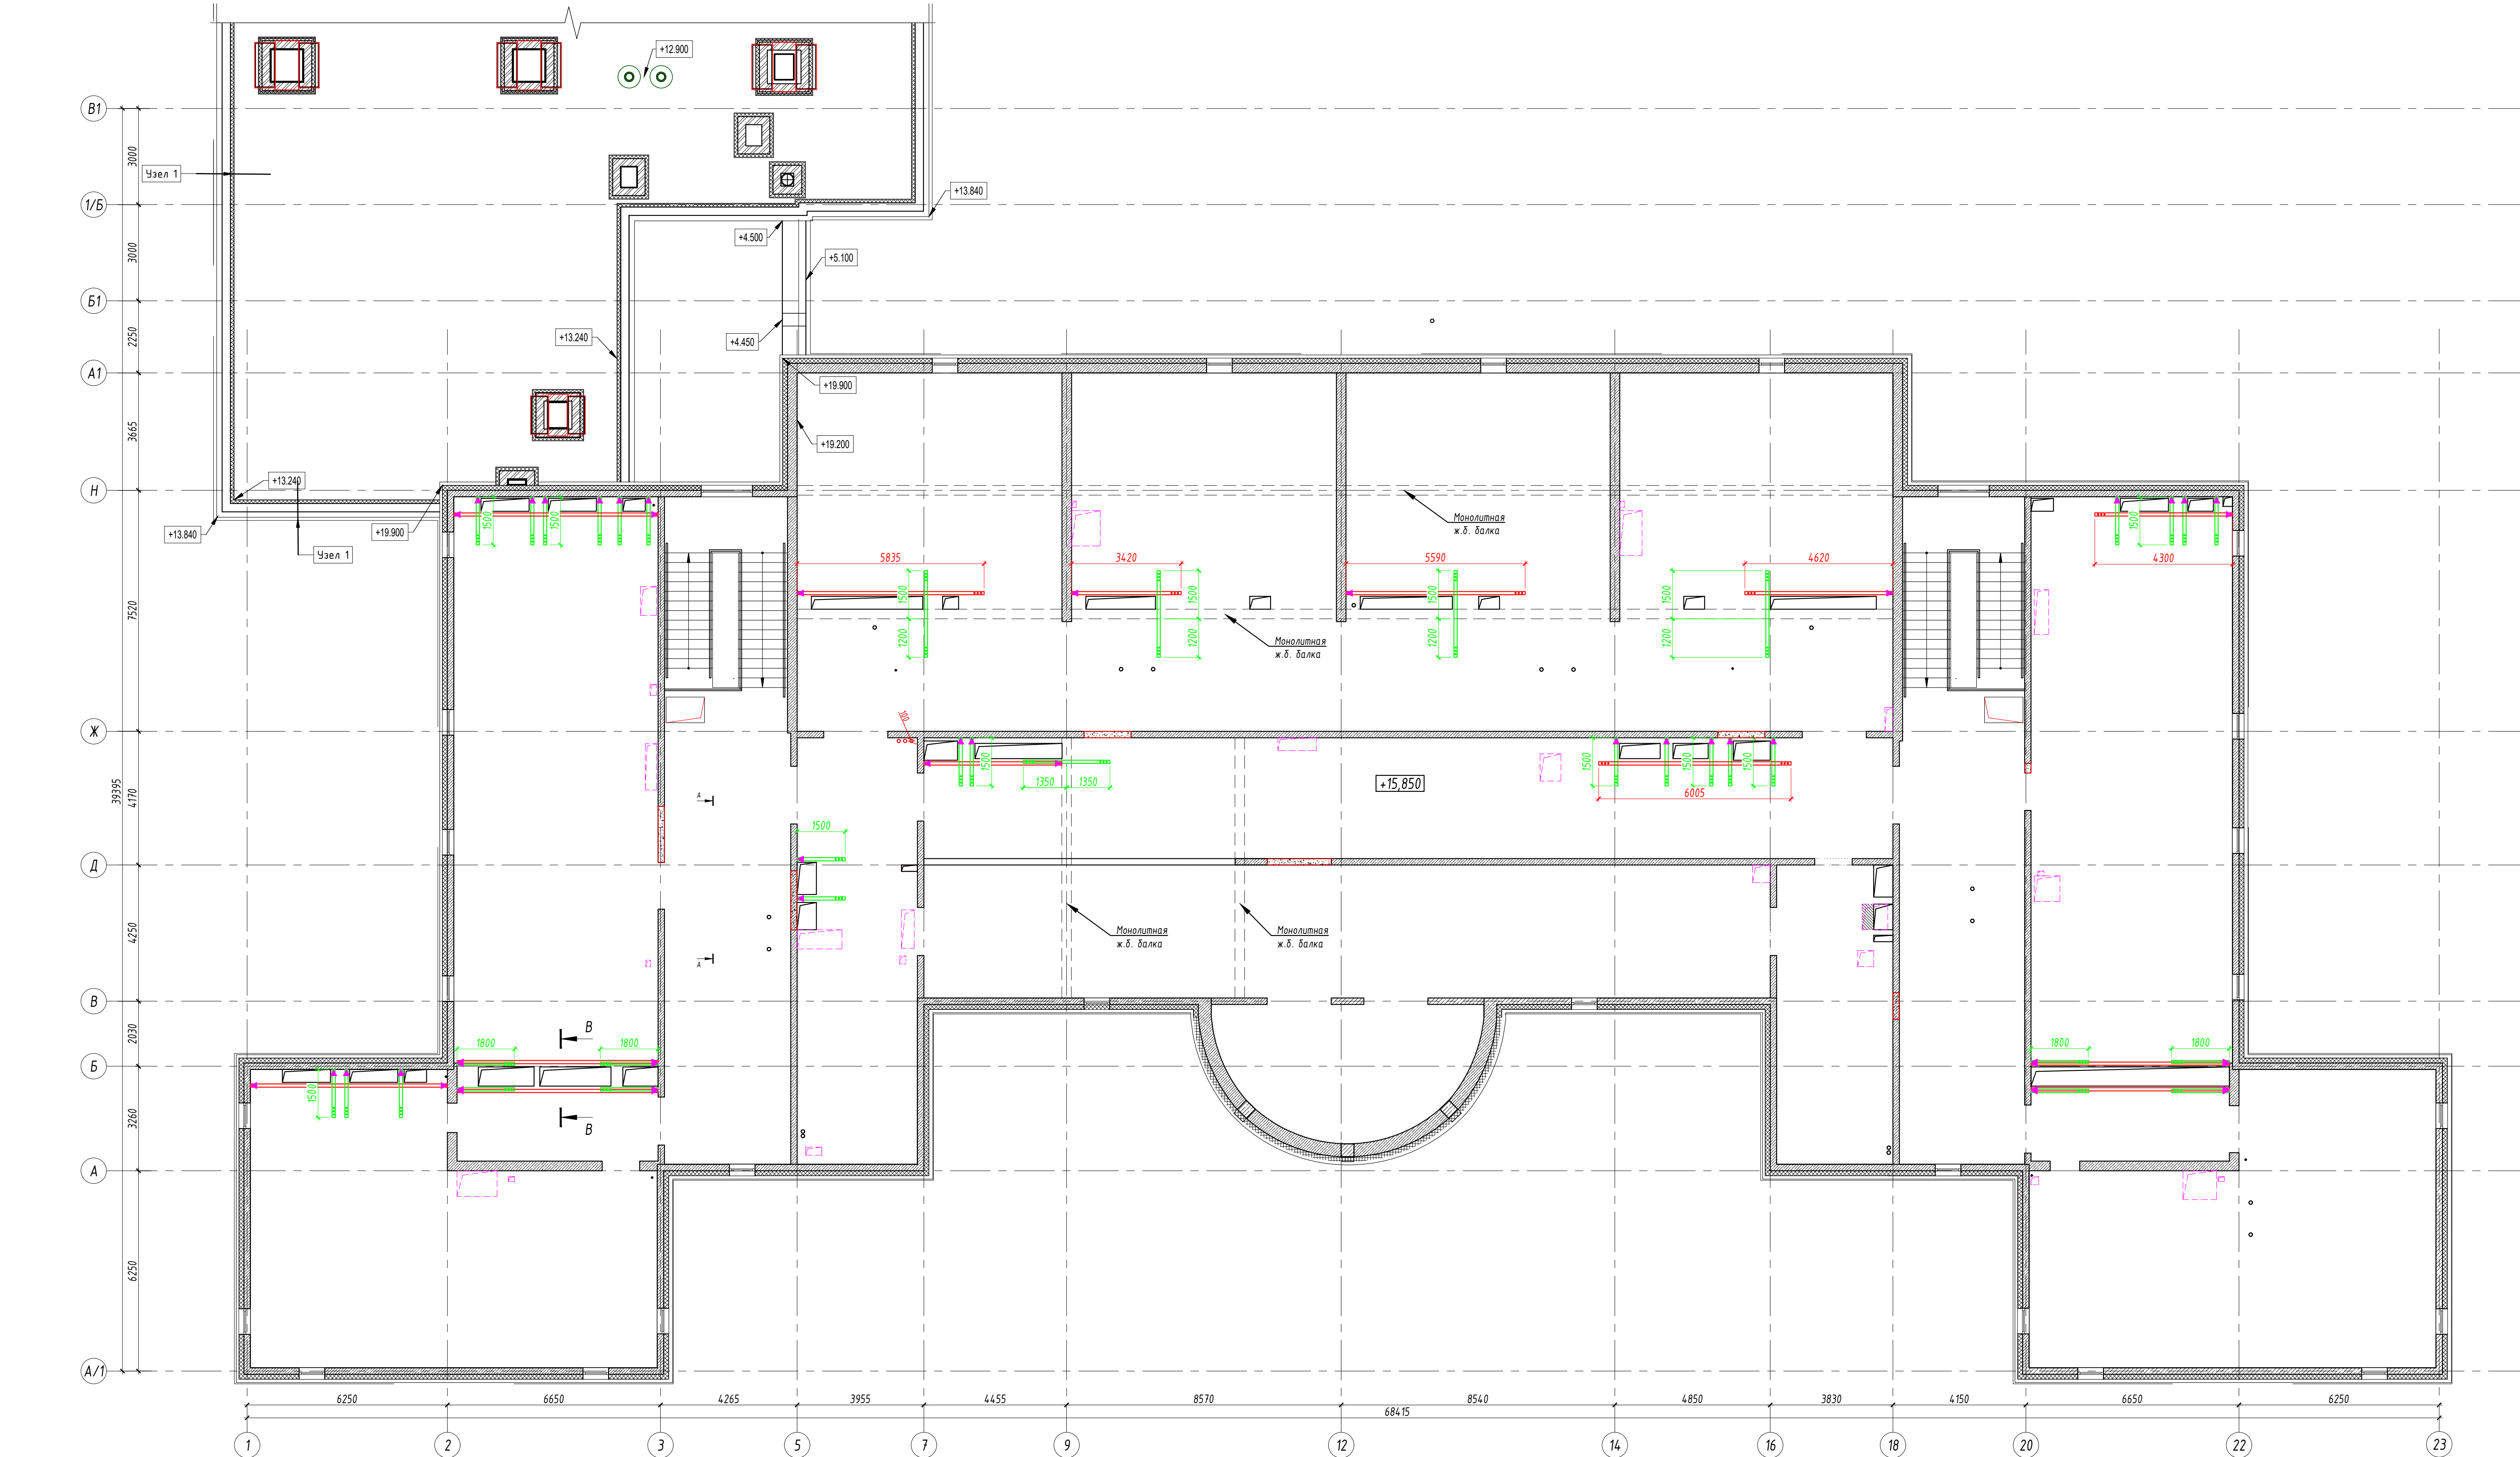

Порядок производства работ:

- Разрушить перекрытие, подлежащее усилению.
- В местах расположения элементов усиления произвести очистку перекрытия от мусора, наливой раствора, элементов пирога пола/потолка до основания монолитного железобетона. Для узла №1 так же произвести очистку участка стены.
- До устройства усиления и замоноличивания существующих проемов выполнить прорезание новых проемов в плите перекрытия, в соответствии со схемой на листе 2.
- Произвести нарезку элементов усиления, при необходимости произвести сварочные работы и выполнение отверстий под анкерные болты согласно узлам 1 и 2. При расположении полосы усиления между вертикальными монолитными конструкциями длину принимать на 40мм меньше фактической.
- Усиление полосой -10x100 выполнять с отступом в 50 мм от края проёма в соответствии с разрезом В-В.
- Фиксацию выполнять анкерами Fischer FH II-SK 15x100/15 или аналог.
- Открытые участки стальных элементов обрабатывать огнезащитным составом, обеспечивающим предел огнестойкости не менее R120. Площадь обработки 7,7 м².
- Спецификации элементов усиления см. лист 5.

Условные обозначения

- ▲ - крепление полосы усиления согласно узлу 1
- - полоса 10x100 по верхней поверхности плиты перекрытия
- - полоса 10x100 по нижней поверхности плиты перекрытия

|           |           |      |        |         |            |
|-----------|-----------|------|--------|---------|------------|
| Изм.      | Кол. изм. | Лист | № док. | Подпись | Дата       |
| Разраб.   | Варнашов  |      |        |         | 01.09.2026 |
| Проверил  | Прудников |      |        |         | 01.09.2026 |
| Н. контр. | Гударева  |      |        |         | 01.09.2026 |
| ГИП       | Маркова   |      |        |         | 01.09.2026 |

16-25/Г-Р-КР5

Капитальный ремонт объекта "ГБОУ Школа №429 "Соколиная гора", расположенного по адресу: г. Москва, ул. Соколиной горы 5-я, д. 14.

Конструктивные решения

Стадия: Р, Лист: 3, Листов: 14



Схема расположения усиления вновь пробиваемых отверстий на отм. +15,850

АЗУРИТ


ФОРМАТ А1

Фрагмент 2 в осях Д/5 на отм. +15,850

Принципиальная схема восстановления плиты в зоне существующего проёма 500 мм и менее


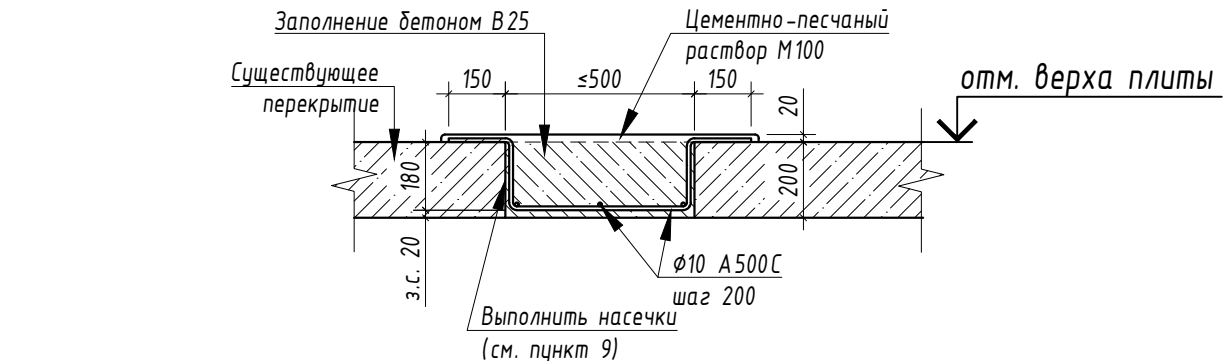
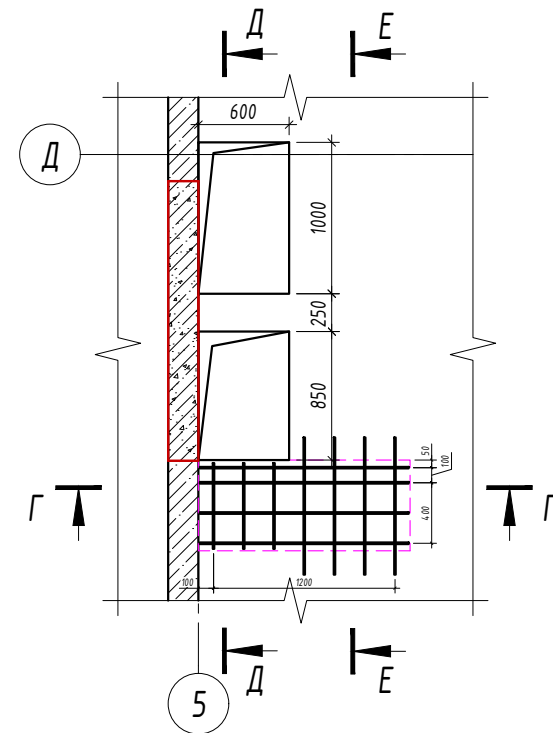


Принципиальная схема восстановления плиты в зоне существующего проёма более 500 мм

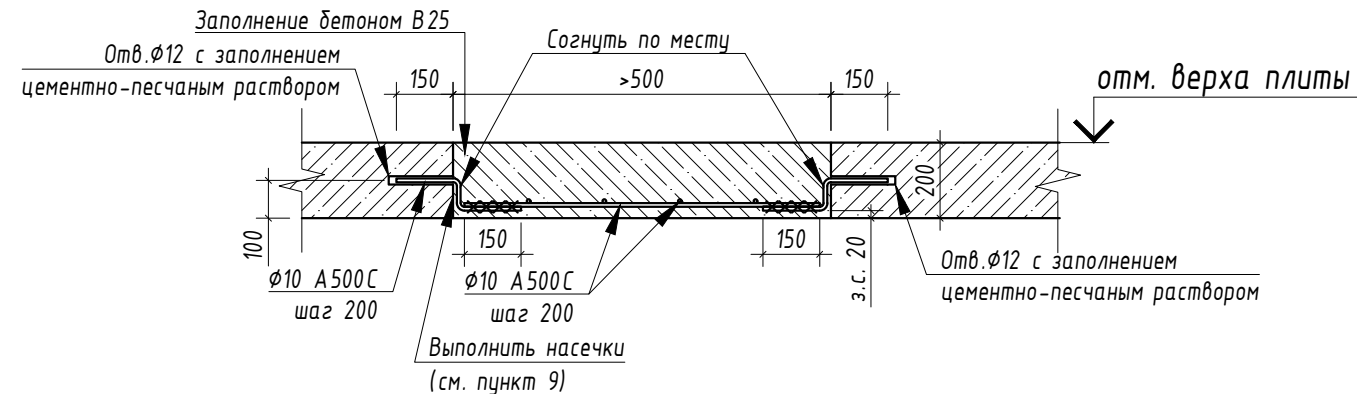

Порядок производства работ:

1. Работы по замоноличиванию существующих проёмов выполнять до устройства усиления вновь пробиваемых проёмов.
2. Произвести очистку перекрытия от мусора, напылов раствора, элементов пирога пола/потолка до основания монолитного железобетона.
3. Произвести нарезку элементов армирования, при необходимости произвести сварочные работы.
4. Выставить опалубку для заполнения проёма.
5. Выполнить монтаж элементов армирования в проектное положение.
6. Заполнить проём в соответствии с узлами на данном листе.
7. Спецификацию элементов усиления см. лист 5.
8. Фрагмент 2 замаркирован на листе 2.
9. Для улучшения сцепления заполняемого бетона выполнить насечки на поверхности существующего проёма.

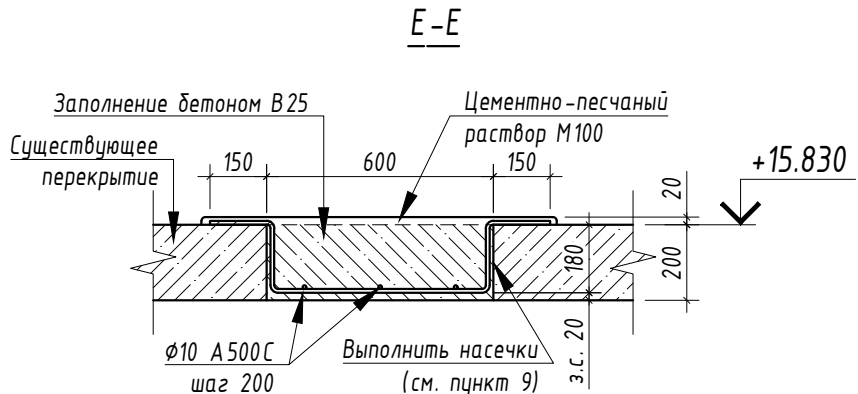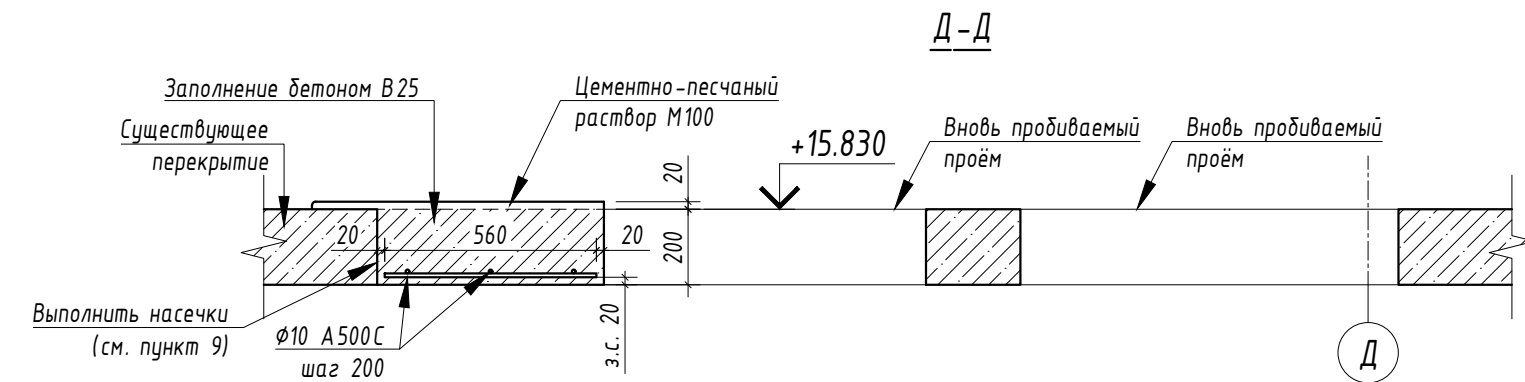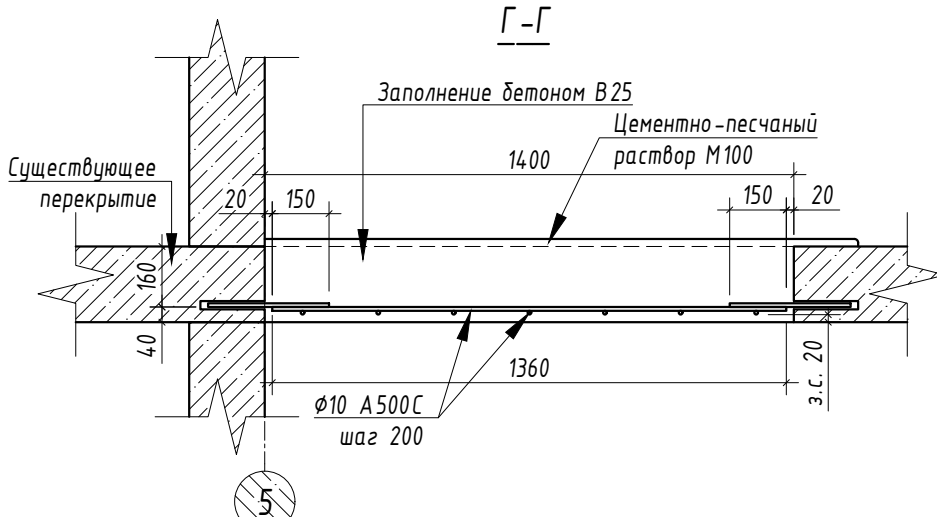

|           |        |           |       |         |            |   |   |      |        |
|-----------|--------|-----------|-------|---------|------------|---|---|------|--------|
|           |        |           |       |         |            | 16-25/Г-Р-КР5   |   |      |        |
|           |        |           |       |         |            | Капитальный ремонт объекта "ГБОУ Школа №429 "Соколиная гора",<br>расположенного по адресу: г. Москва, ул. Соколиной горы 5-я, д. 14. |   |      |        |
| Изм       | Кол.уч | Лист      | № док | Подпись | Дата       | Конструктивные решения   | Стадия                                                                                              | Лист | Листов |
| Разраб.   |        | Варнашов  |       |         | 01.09.2026 |   | Р                                                                                                   | 4    |        |
| Проверил  |        | Прудников |       |         | 01.09.2026 |   |   |      |        |
|           |        |           |       |         |            |   |   |      |        |
|           |        |           |       |         |            | Принципиальные узлы замоноличивания<br>проёмов                                                                                       |  <b>АЗУРИТ</b> |      |        |
| Н. контр. |        | Губарева  |       |         | 01.09.2026 |   |   |      |        |
| ГИП       |        | Маркова   |       |         | 01.09.2026 |   |   |      |        |

Спецификация элементов усиления проёмов на отм. +15,850

| Поз. | Обозначение             | Наименование                            | Кол.  | Масса<br>ед., кг | Примечание           |
|------|-------------------------|-----------------------------------------|-------|------------------|----------------------|
|      | ГОСТ 34028-2016         | Ø10 А500С L=м.п.                        | 205,7 | 0,616            | 126,7                |
|      | ГОСТ 103-2006           | -10х100 L=м.п.                          | 136,5 | 7,85             | 1071,5               |
|      | ГОСТ 8509-93            | Уголок 80х80х6 L=м.п.                   | 12,5  | 7,36             | 92                   |
|      | Анкерный болт втулочный | Fischer FH II-SK 15х100/15 (или аналог) |       |                  | 250 шт.              |
|      |                         | <u>Материалы</u>                        |       |                  |                      |
|      | ГОСТ 25029-2020         | Грунтовка ГФ-021 (за 1 раз)             |       |                  | 17,26 м <sup>2</sup> |
|      | ГОСТ 6465-2023          | Эмаль ПФ-115 (за 2 раза)                |       |                  | 34,52 м <sup>2</sup> |
|      | ГОСТ 26633-2015         | Бетон В25                               |       |                  | 2,75 м <sup>3</sup>  |
|      | ГОСТ 28013-98           | Цементно-песчаный раствор М100          |       |                  | 7,8 м <sup>3</sup>   |
|      |                         |                                         |       |                  |                      |
|      |                         |                                         |       |                  |                      |

[illegible]

16-25/Г-Р-КР5

Капитальный ремонт объекта "ГБОУ Школа №429 "Соколиная гора", расположенного по адресу: г. Москва, ул. Соколиной горы 5-я, д. 14.

## Конструктивные решения

Спецификация элементов усиления  
проёмов на отм. +15,850

