


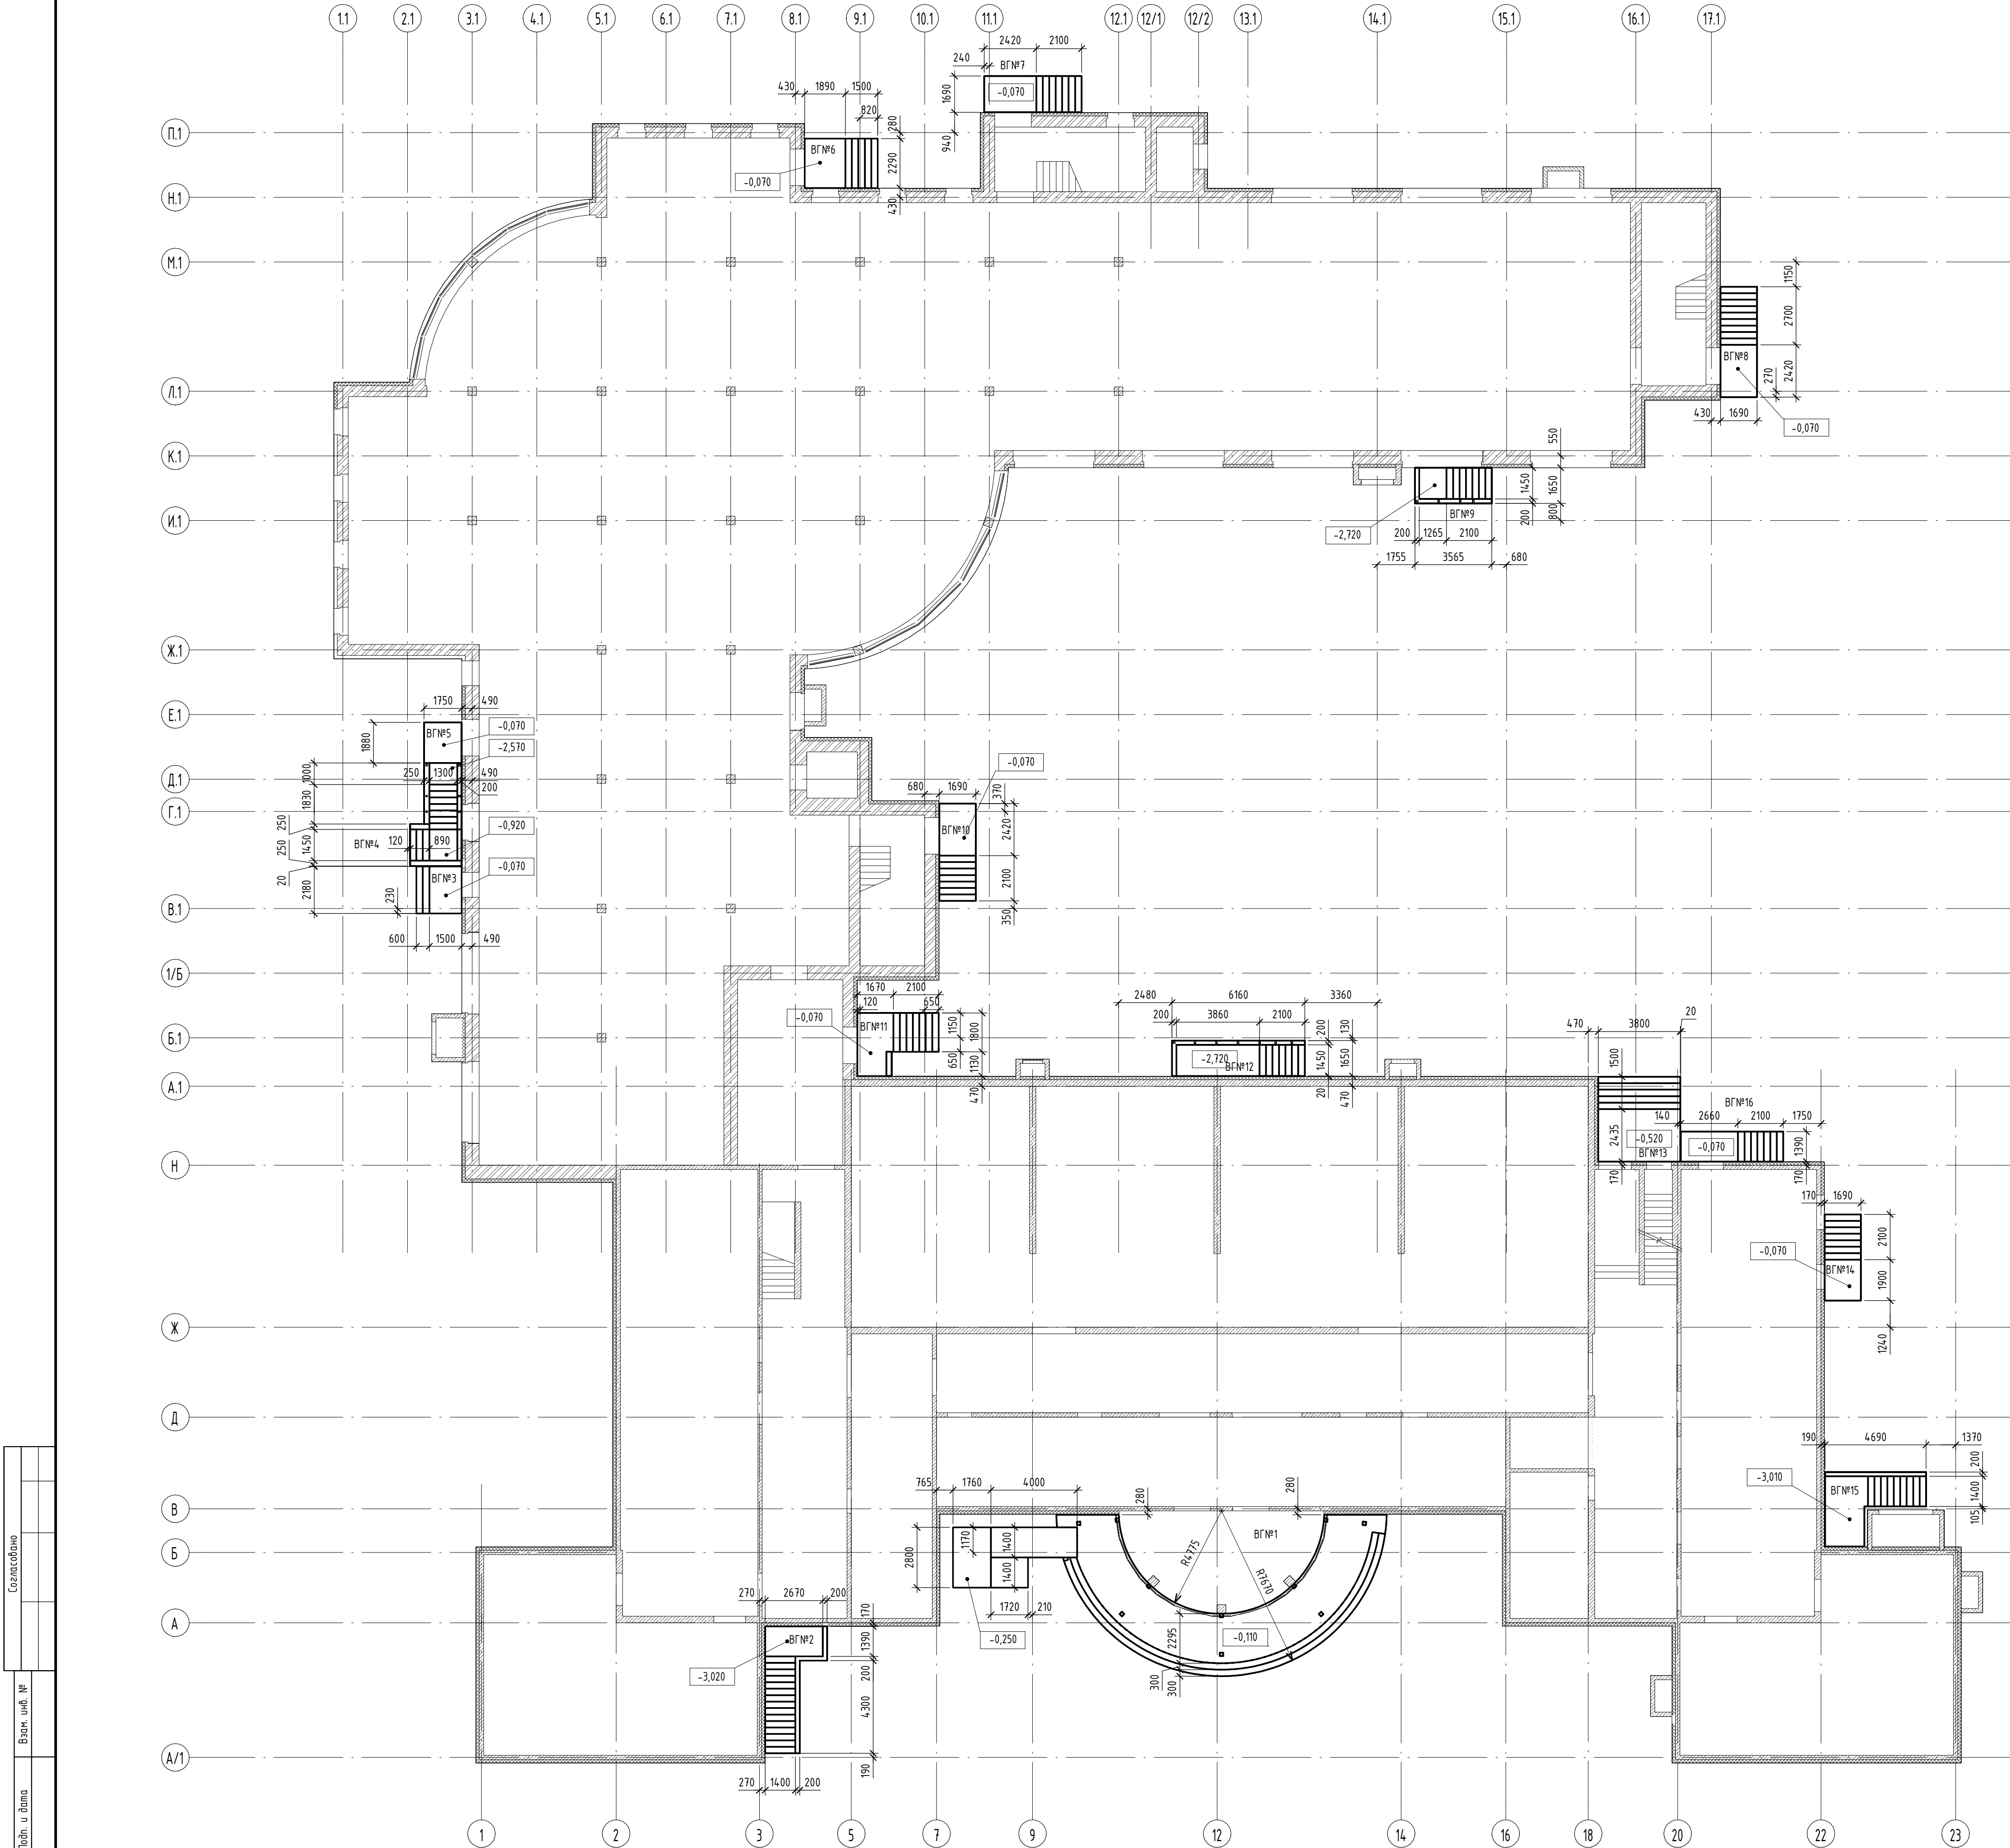

1. Общие данные см. лист 1
2. Схемы расположения, армирования входных групп и устройство навесов см. листы 3-46.