


Схема расположения фундаментной плиты входной группы в/о 20/Н на отм. -1,700

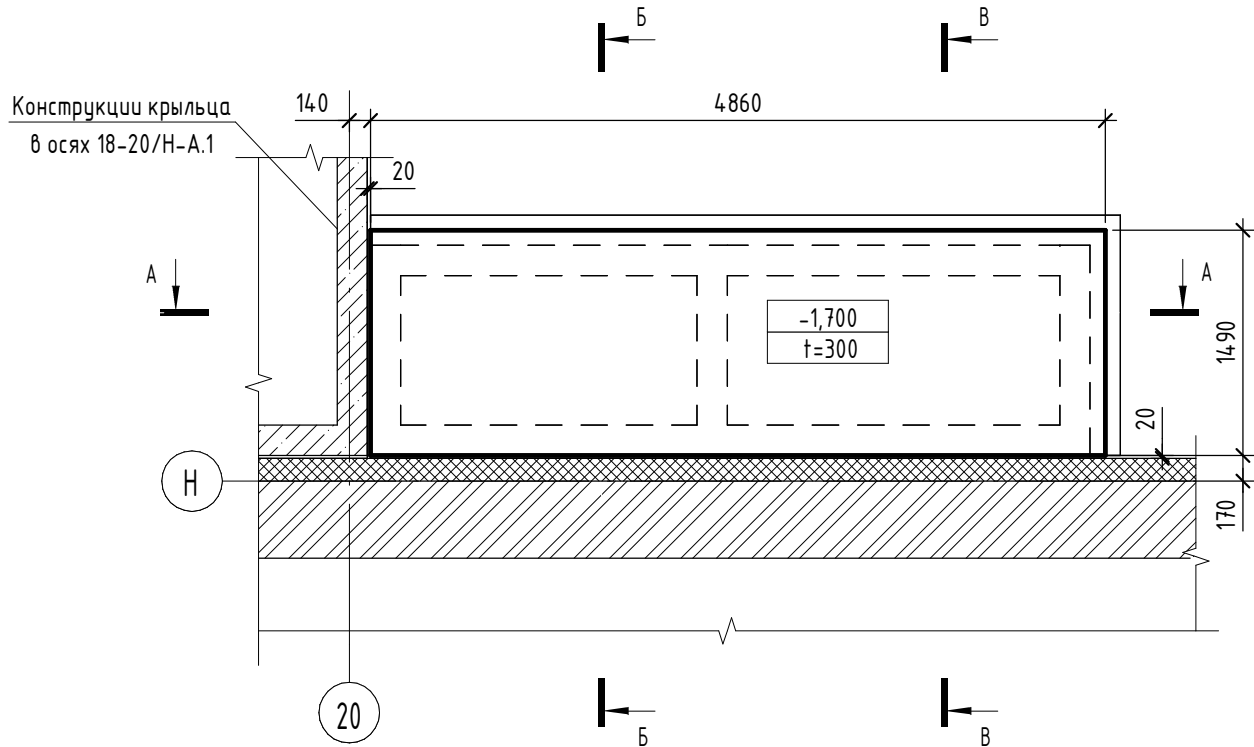

А-А
Опалубка

Схема расположения стен входной группы в/о 20/Н на отм. -1,700


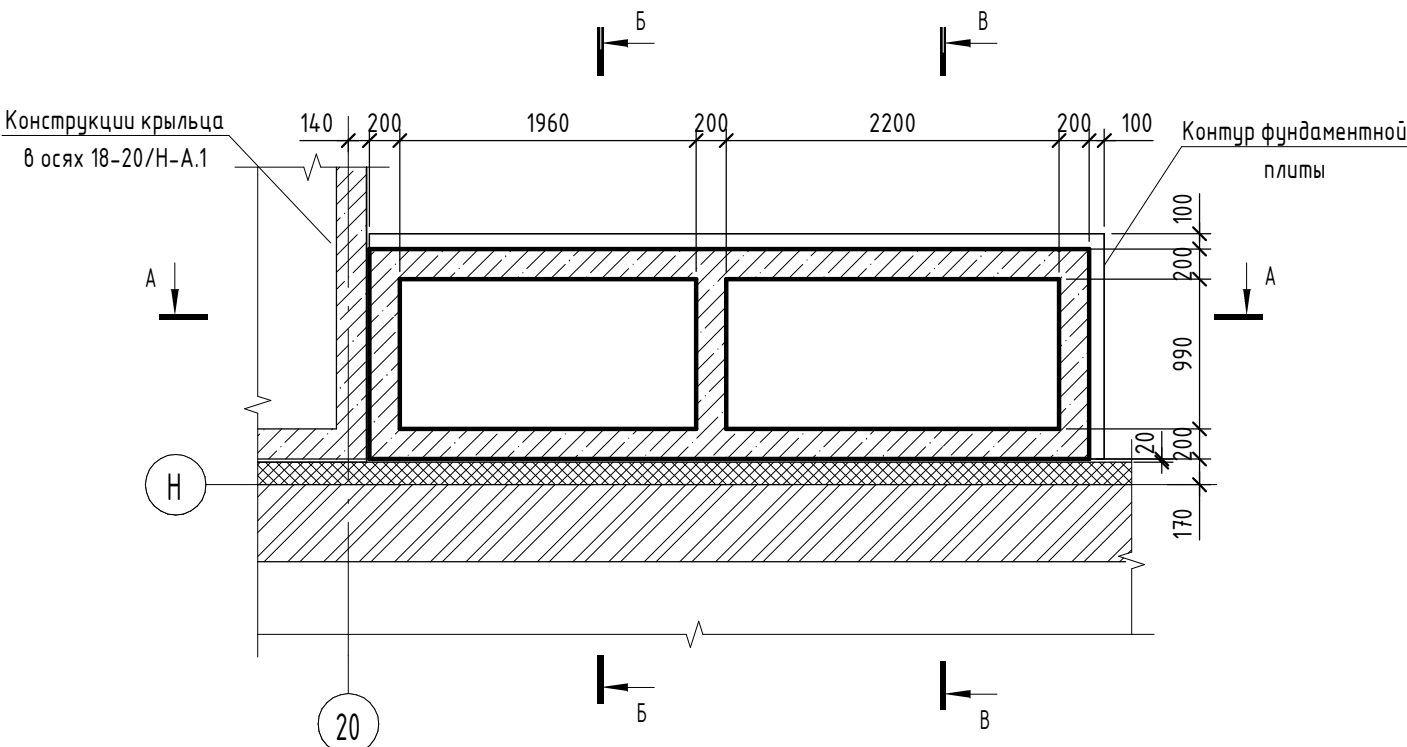


Схема расположения входной группы в/о 20/Н на отм. -0,070

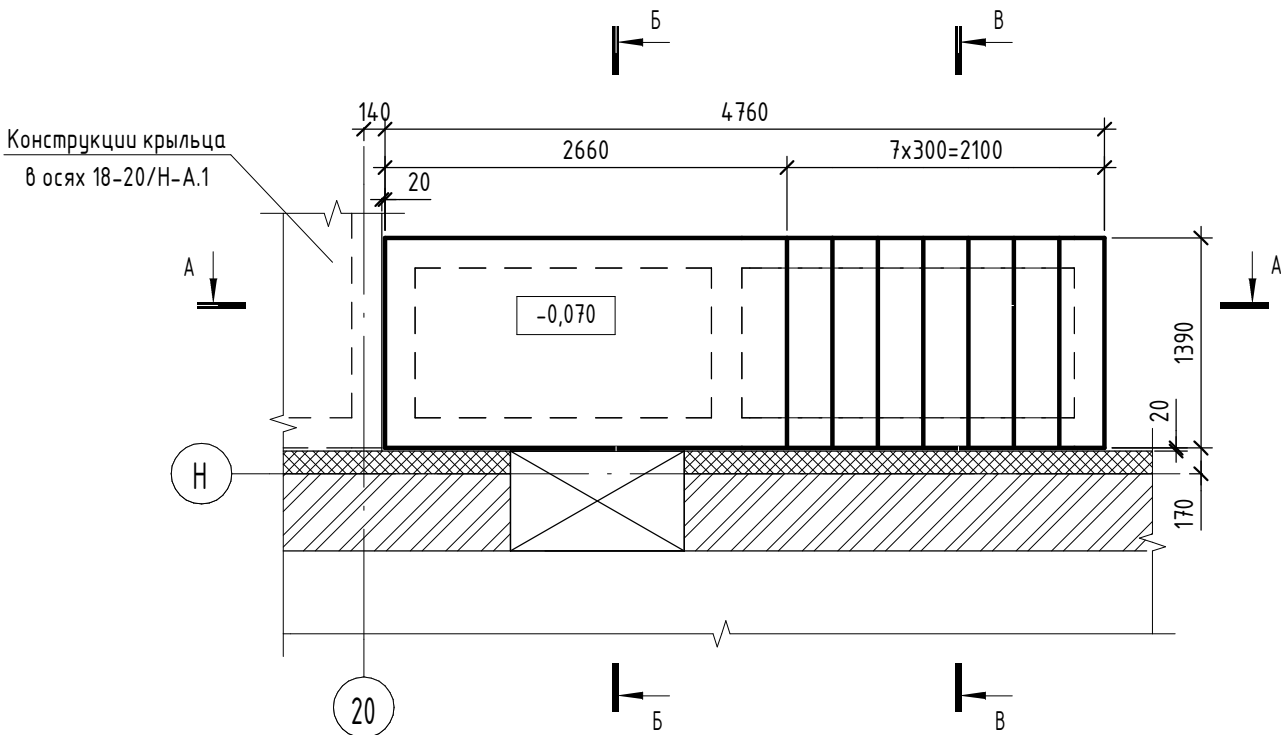

А

Монолитная плита (B25 W6 F150)	-300мм
Бетонная подготовка B7,5	-50мм
Пленка ПЭ 200мкм	-2 слоя
Гидроизоляция обмазочная	-2 слоя
Бетонная подготовка B7,5	-100мм
Песок средней крупности	утрамбованный послойно (Купл=0,95)
Пленка ПЭ 200мкм	-2 слоя
Грунт основания	

Монолитная плита (B25 W6 F150) -200мм

Бетонная подготовка B7,5	-50мм
Пленка ПЭ 200мкм	-2 слоя
Засыпка песком средней крупности	утрамбованный послойно (Купл=0,95)
Пленка ПЭ 200мкм	-2 слоя

Б

Монолитная лестница (B25 W6 F150) -200мм

Бетонная подготовка B7,5	-50мм
Пленка ПЭ 200мкм	-2 слоя
Засыпка песком средней крупности	утрамбованный послойно (Купл=0,95)
Пленка ПЭ 200мкм	-2 слоя

Г

Ведомость расхода бетона, м³

Конструкция	Бетон класса		
	ГОСТ 26633-2015		
	B7.5	B25 F150 W6	Итого
Фундаментная плита	0	2,17	2,17
Стены	0	2,81	2,81
Площадка	0	0,66	0,66
Лестничный марш	0	0,96	0,96
Бетонная подготовка	1,01	0	1,01
Всего	1,01	6,6	7,61

- Общие данные см. лист 1
- Армирование см. лист 16
- Все конструкции соприкасающиеся с грунтом гидроизолировать 2 слоями обмазочной гидроизоляции на битумной основе по 2 слоям битумного праймера.

Ведомость расхода материалов

Поз.	Обозначение	Наименование	Кол.	Масса ед, кг	Примечание
		Материалы			
	ГОСТ 30693-2000	Гидроизоляция обмазочная (Битумная мастика)			21,92 м²
	ГОСТ 8736-2014	Песок средней крупности			13,39 м³
	ГОСТ 10354-82	Пленка полиэтиленовая 200 мкм (2 слоя)			22,03 м²


0,000=156,92

16-25/Г-Р-КР1


Капитальный ремонт объекта "ГБОУ "Школа №429 "Соколиная гора", расположенного по адресу: г.Москва, ул.Соколиной Горы 5-ая, д.14

Изм.	Кол.уч.	Лист	№ док.	Подпись	Дата	Конструктивные решения	Стадия	Лист	Листов
Разраб.	Шевченко	07.26					Р	15	
Проверил	Дидык	07.26				Схема расположения входной группы в/о 20/Н			
Н.контр.	Губарева Е.В.	07.26							
ГИП	Маркова	07.26							

Схема армирования стен входной группы в/о 20/Н на отм -1,700

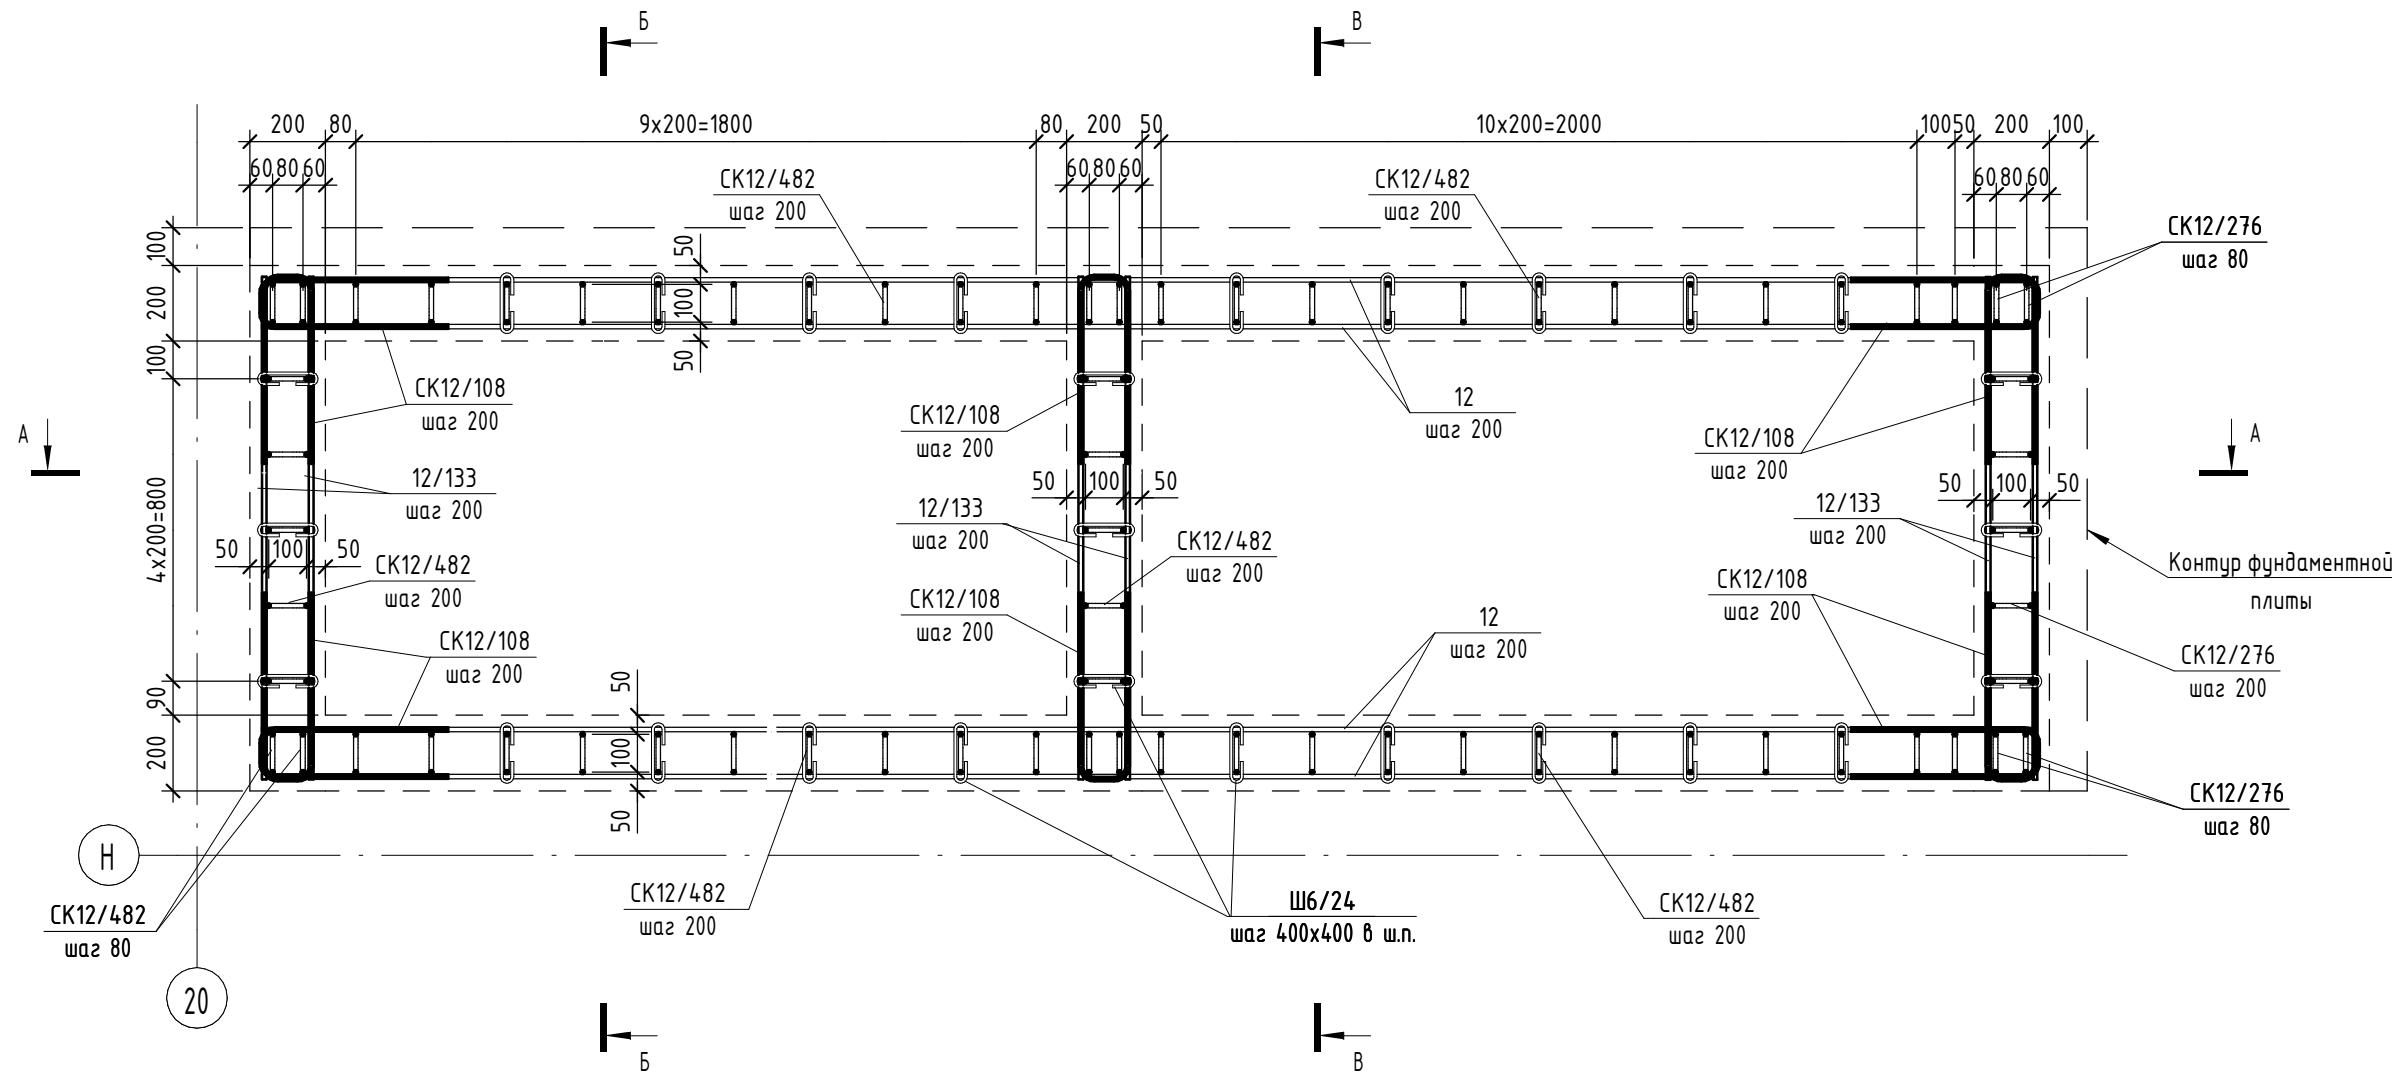


А-А
Армирование

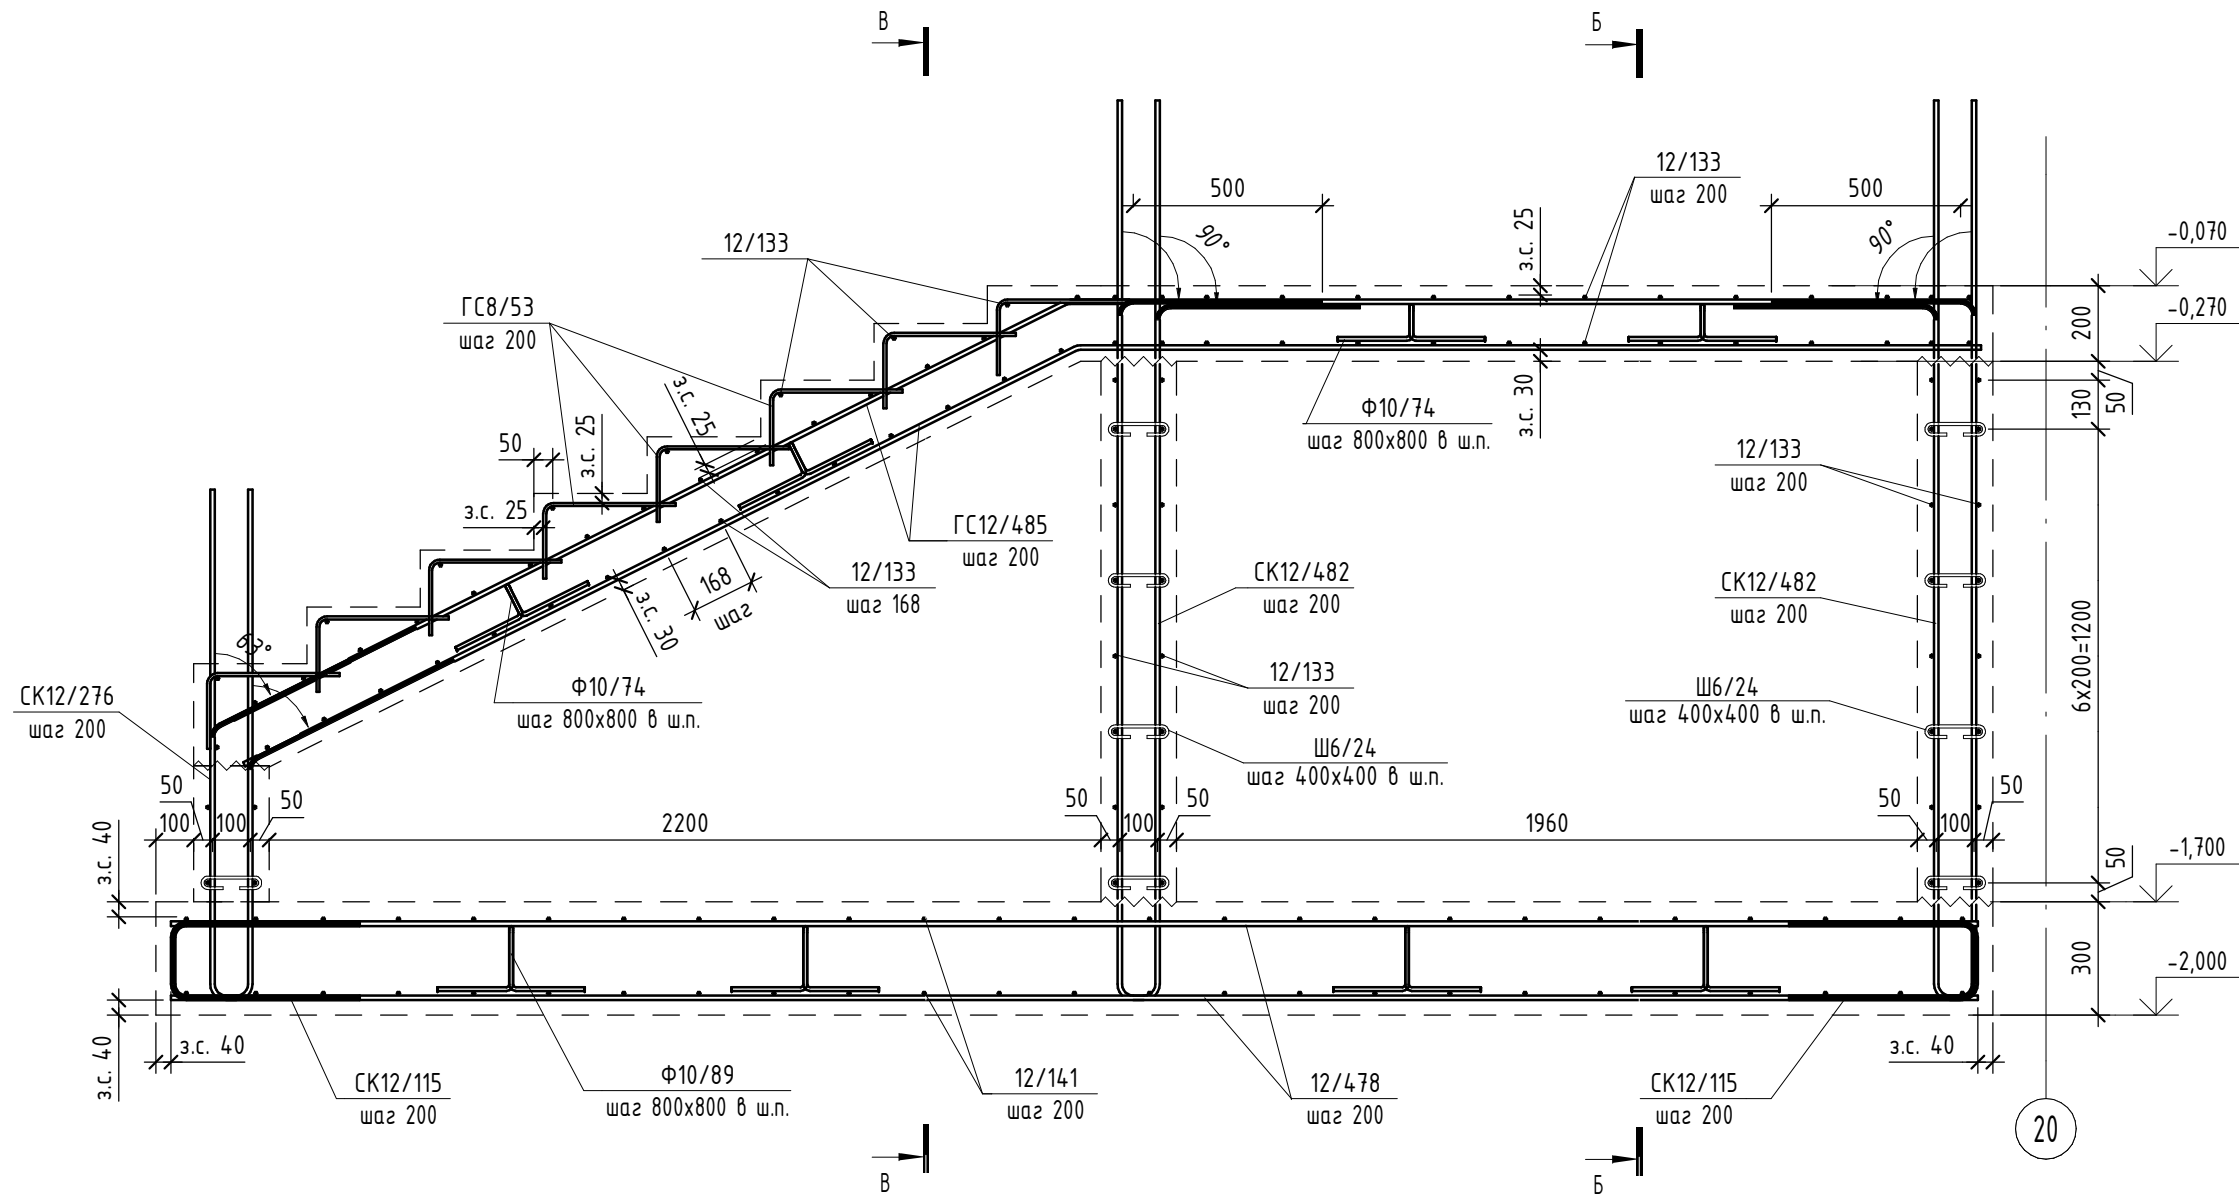


Б-Б

Армирование

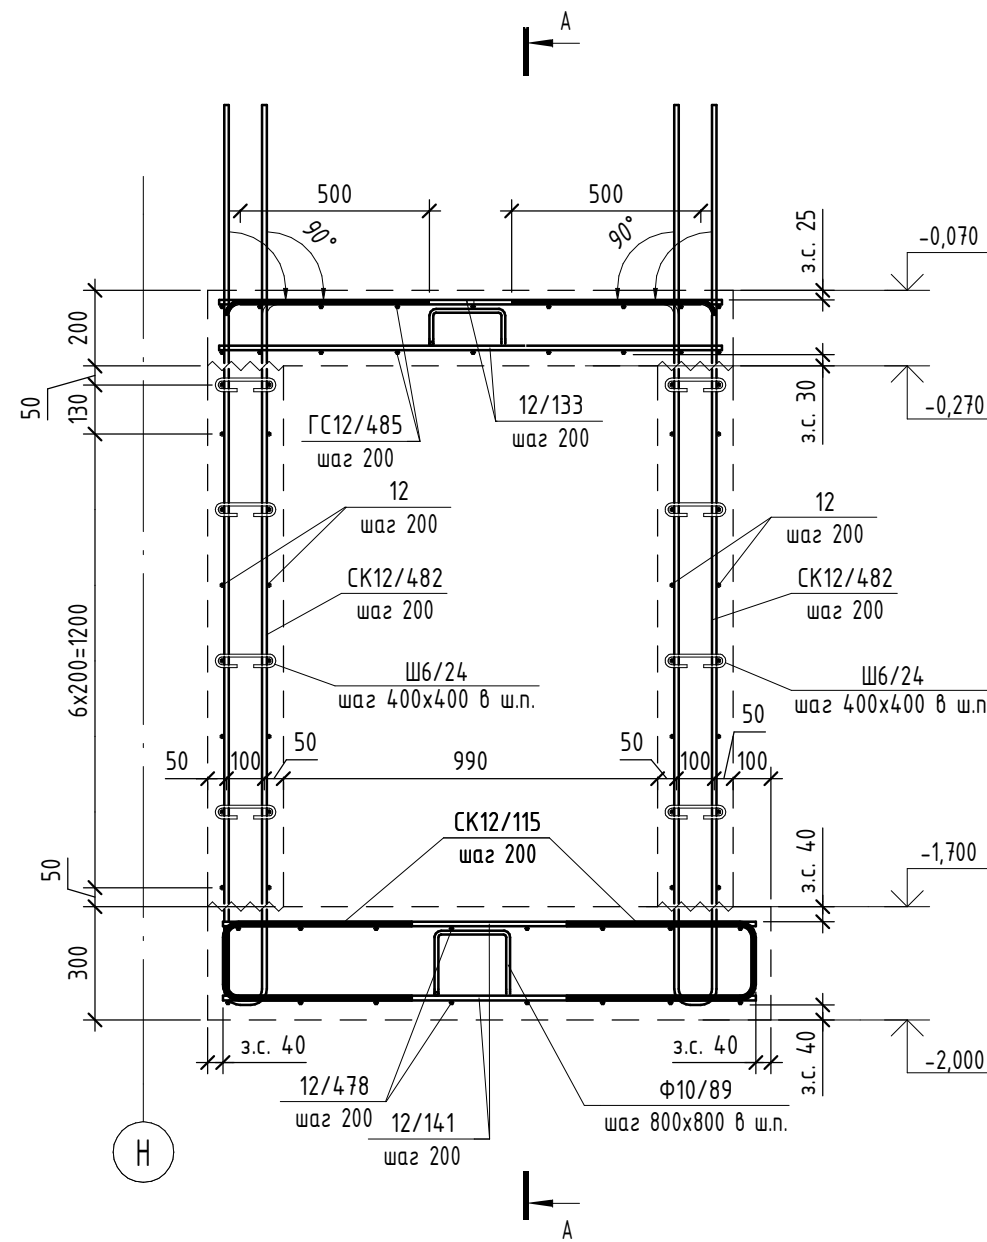

В-В

Армирование

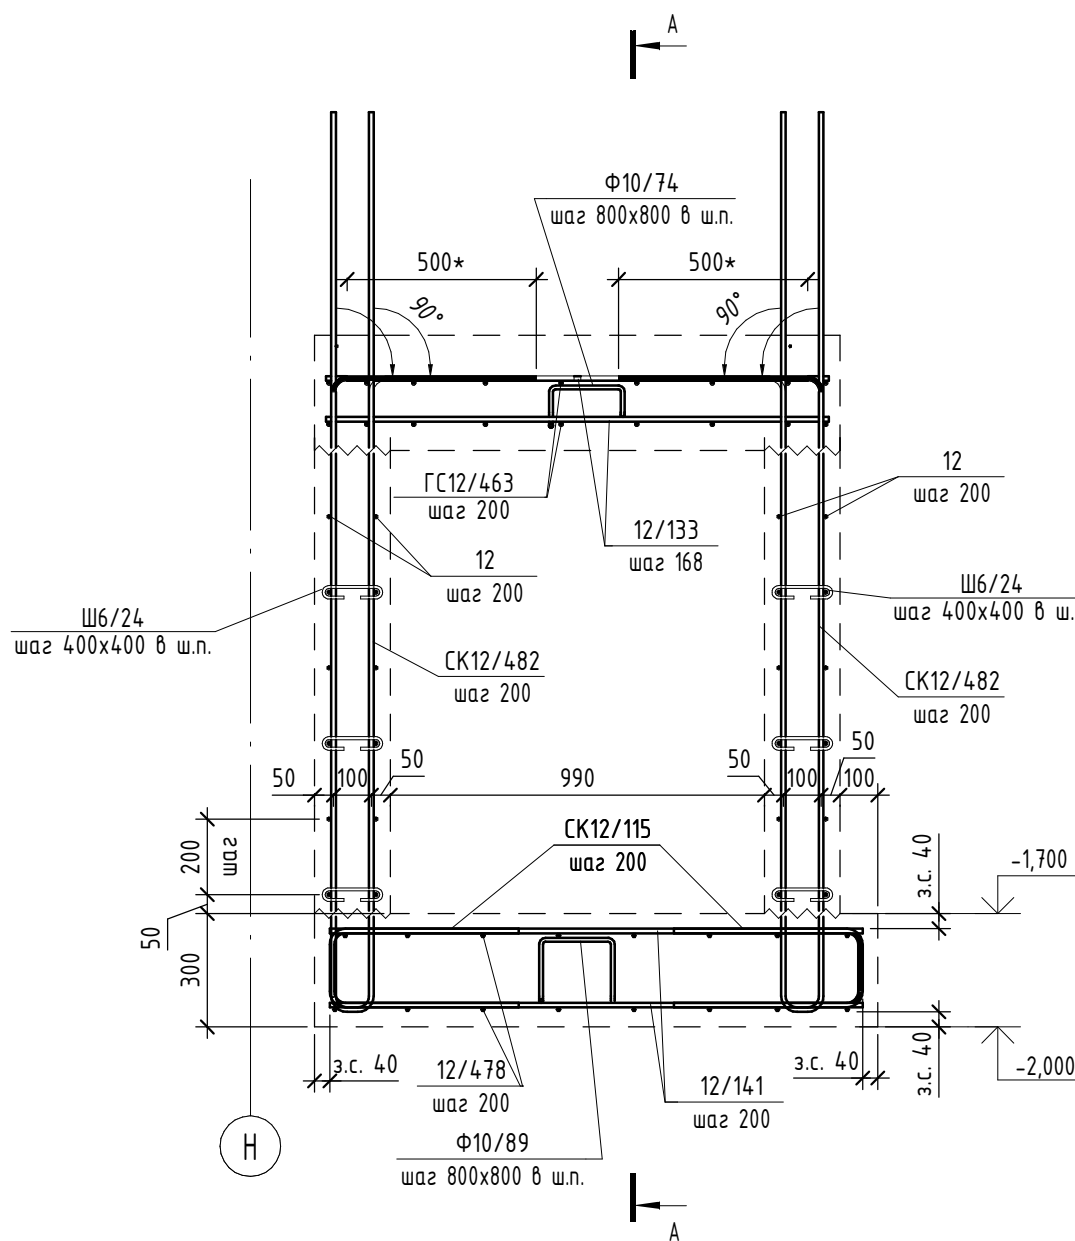

Ведомость деталей

Поз.	Эскиз
ГС8/53	
ГС12/485	
СК12/482	
СК12/276	
СК12/115	

Ведомость деталей

Поз.	Эскиз
СК12/108	
Ш6/24	
Ф10/89	
Ф10/74	

Примечание:
1) Размеры скруток (СК) указаны по внутренним границам деталей.
2) Перед изготовлением гнутых элементов производитель работ выполнить пробный образец и сверить с фактическим армированием.

Спецификация элементов армирования входной группы

Поз.	Обозначение	Наименование	Кол.	Масса ед. кг	Примечание
Наименование конструкции					
Детали					
12	ГОСТ 34028-2016	Ø12 А500С	L, поз.м	126,8	0,888 112,60
12/478	ГОСТ 34028-2016	Ø12 А500С	L= 4780	16	4,245 67,96
12/141	ГОСТ 34028-2016	Ø12 А500С	L= 1410	50	1,253 62,64
12/133	ГОСТ 34028-2016	Ø12 А500С	L= 1330	103	1,182 121,68
ГС8/53	ГОСТ 34028-2016	Ø8 А500С	L= 530	72	0,21 15,12
ГС12/485	ГОСТ 34028-2016	Ø12 А500С	L= 4855	18	4,312 77,60
СК12/482	ГОСТ 34028-2016	Ø12 А500С	L= 4815	62	4,276 265,13
СК12/276	ГОСТ 34028-2016	Ø12 А500С	L= 2755	9	2,447 22,02
СК12/115	ГОСТ 34028-2016	Ø12 А500С	L= 1155	66	1,026 67,72
СК12/108	ГОСТ 34028-2016	Ø12 А500С	L= 1080	56	0,96 53,76
Ш6/24	ГОСТ 34028-2016	Ø6 А240	L= 240	176	0,054 9,50
Ф10/89	ГОСТ 34028-2016	Ø10 А240	L= 895	4	0,553 2,21
Ф10/74	ГОСТ 34028-2016	Ø10 А240	L= 745	4	0,46 1,84

Диаметр гибки арматуры


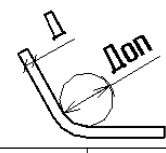


Схема стыка арматурных стержней
(перепуск стержней без сварки)

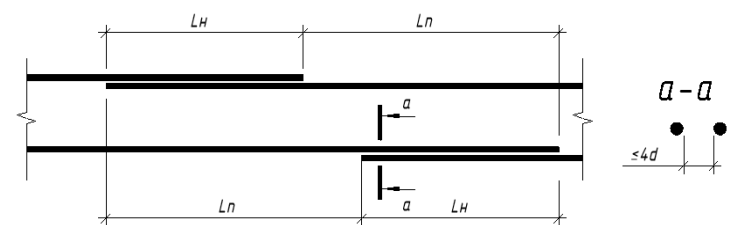

Тип арматуры	Длина нахлеста Ln	Длина анкеровки	Смещение нахлеста Ln, не менее
Ф12 А500С	595	500	800

Диаметр стержня, мм	Минимальный диаметр оправки, мм
А240	
Ø6	15
Ø10	25
А500С	
Ø8	40
Ø12	60

Схема расположения
фиксаторов Ф10


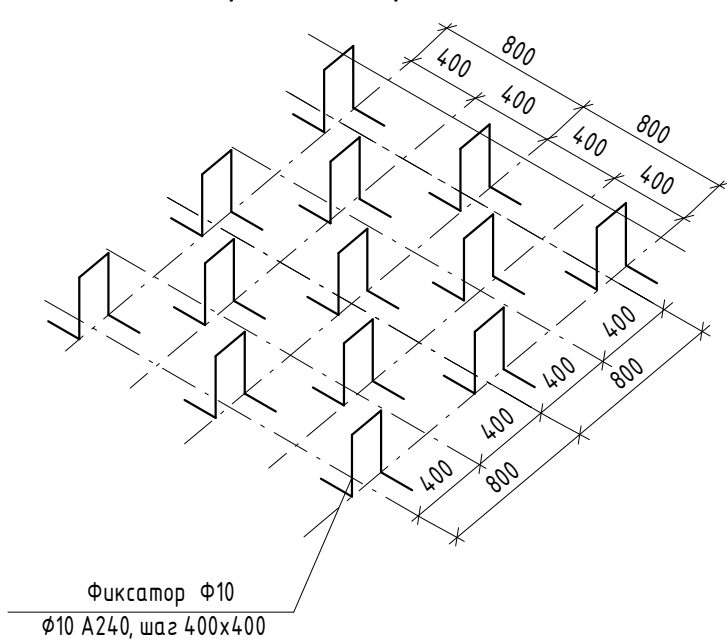


Схема расположения шпилек
с шагом 400х400
в шахматном порядке

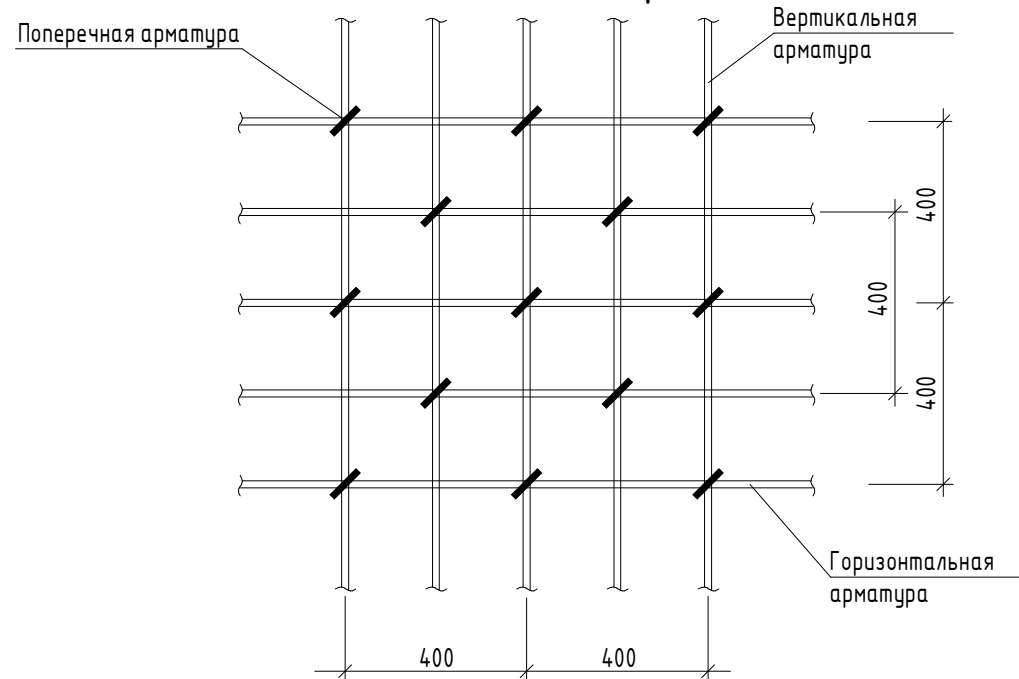

Ведомость расхода стали, кг

Марка конструкции	Изделия арматурные						Всего
	Арматура: класса						
	A240			A500C			
	ГОСТ 34028-2016			ГОСТ 34028-2016			
	Ø6	Ø10	Итого	Ø8	Ø12	Итого	
Фундаментная плита	0	2,2	2,2	0	485,5	485,5	487,7
Стены	9,5	0	9,5	0	208,9	208,9	218,4
Площадка	0	0,9	0,9	0	33,1	33,1	34
Лестничный марш	0	0,9	0,9	15,1	123,7	138,8	139,7
Общий расход	9,5	4,1	13,6	15,1	851,1	866,2	879,8

- Общие данные см. лист 1
- Опубличные чертежи см. лист 15
- * - арматуру обрезать по месту

Условные обозначения:
з.с. - защитный слой бетона
~~~~~ - шаг бетонирования

0,000=156,92

|          |               |       |        |         |      |   |        |      |
|----------|---------------|-------|--------|---------|------|---|--------|------|
|          |               |       |        |         |      | 16-25/Г-Р-КР1   |        |      |
|          |               |       |        |         |      | Капитальный ремонт объекта "ГБОУ "Школа №429 "Сокольная гора", расположенного по адресу: г.Москва, ул.Сокольной Горы 5-ая, в.14 |        |      |
| Изм.     | Кол.лч.       | Лист  | № док. | Подпись | Дата | Конструктивные решения   | Стадия | Лист |
| Разраб.  | Шевченко      | 07.26 |        |         |      |   | Р      | 16   |
| Проверил | Дидж          | 07.26 |        |         |      |   |        |      |
| Н.контр. | Губарева Е.В. | 07.26 |        |         |      | Схема армирования входной группы в/о 20/Н                                                                                       |        |      |
| ГИП      | Маркова       | 07.26 |        |         |      |   |        |      |